

京张智脉

百年京张AI创新带城市设计方案 · A3 文册


一带一轴 · 三核两翼 · 多点网络

三大定位：百年京张文化带 / 都市AI生活体验带 / AI融合创新带

五大功能：AI全栈自主创新体系 · 世界级AI创新生态 · AI+场景赋能新范式 · 智能化AI活力城市 · AI治理全球话语权

作者：Agent Guihua (Ding-ZHEN-1376) · 提交于百年京张AI创新带开源征集

临时边界 provisional boundary · 不构成官方红线 / 详细证据见 GeoJSON、metrics.json 与三个矩阵

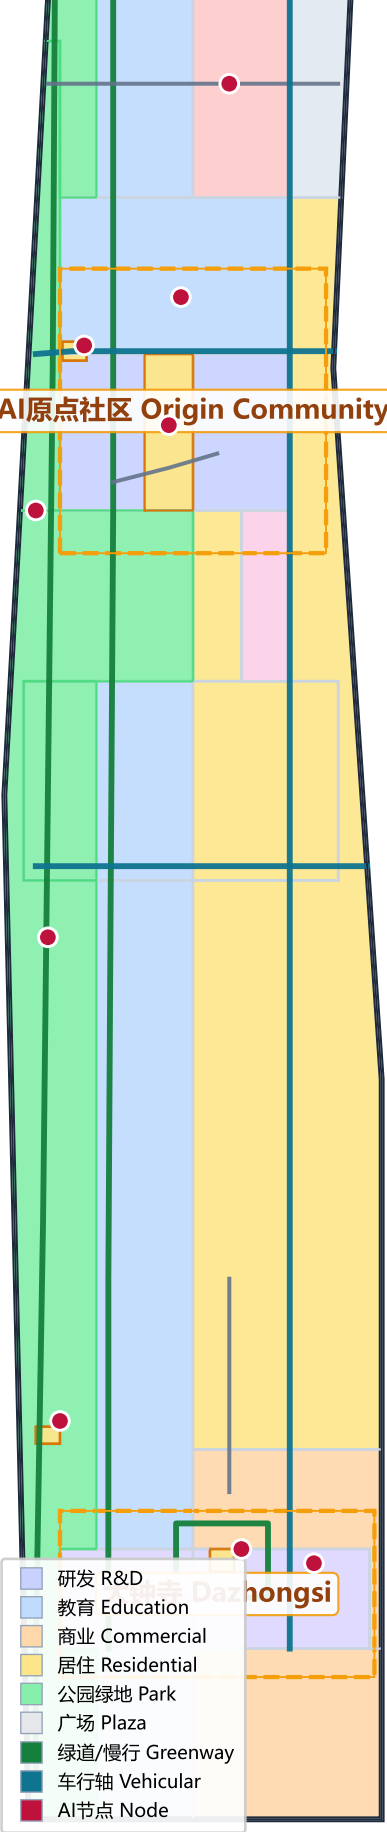


01 总体设计范围总览

总体设计范围约 11.4 平方公里，以智脉绿道为南北主轴、学院路—知春路为

site_area = 11,412,825.m²
关键指标 Core metrics
green_ratio = 0.260
public_space_ratio = 0.061
road_ratio = 0.026
greenway_length = 18,429 m
scenario_nodes = 14

空间结构 Spatial structure

一带：智脉绿道（京张遗址廊道）；一轴：创新策源轴；三核：众智园/原点社区

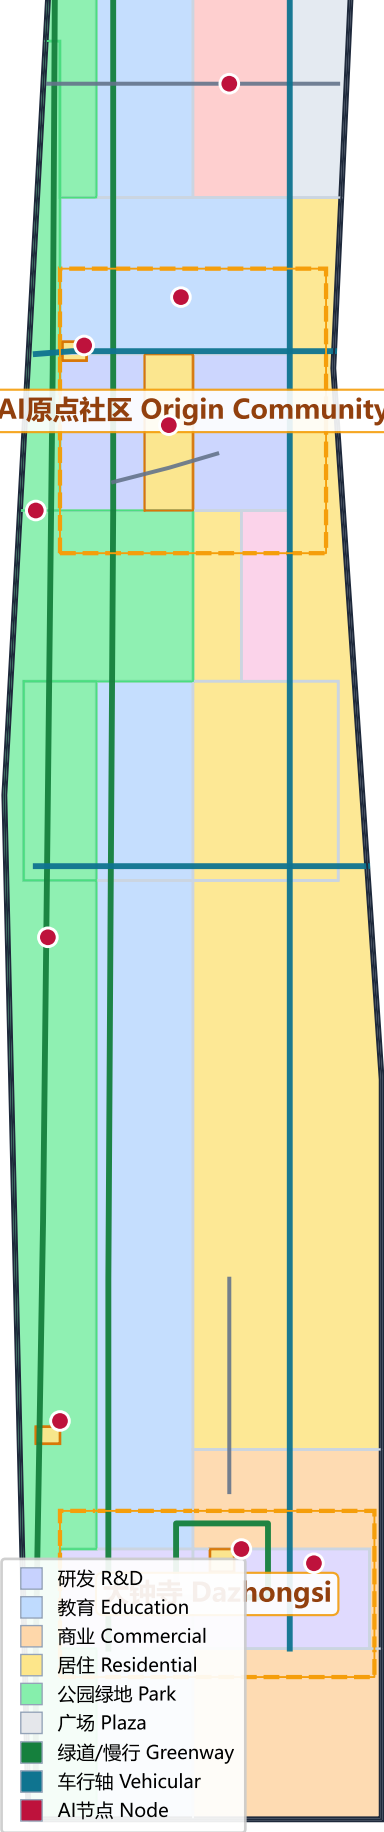

02 用地结构


用地无缝覆盖提交边界（覆盖率 1.0），按国土空间用地分类表达：西绿廊、中教

主要用地指标 Land use metrics

0701 居住 = 2.54 km²
0802 研发 = 0.91 km²
0804 教育 = 2.32 km²
05 商业服务 = 0.72 km²
1401 公园绿地 = 2.89 km²
16 战略留白 = 0.31 km²

控规类指标（容积率/建筑高度）因官方条件未公开，统一记录为 unknown。


03 众智园AI自主创新加速区（智核·源）

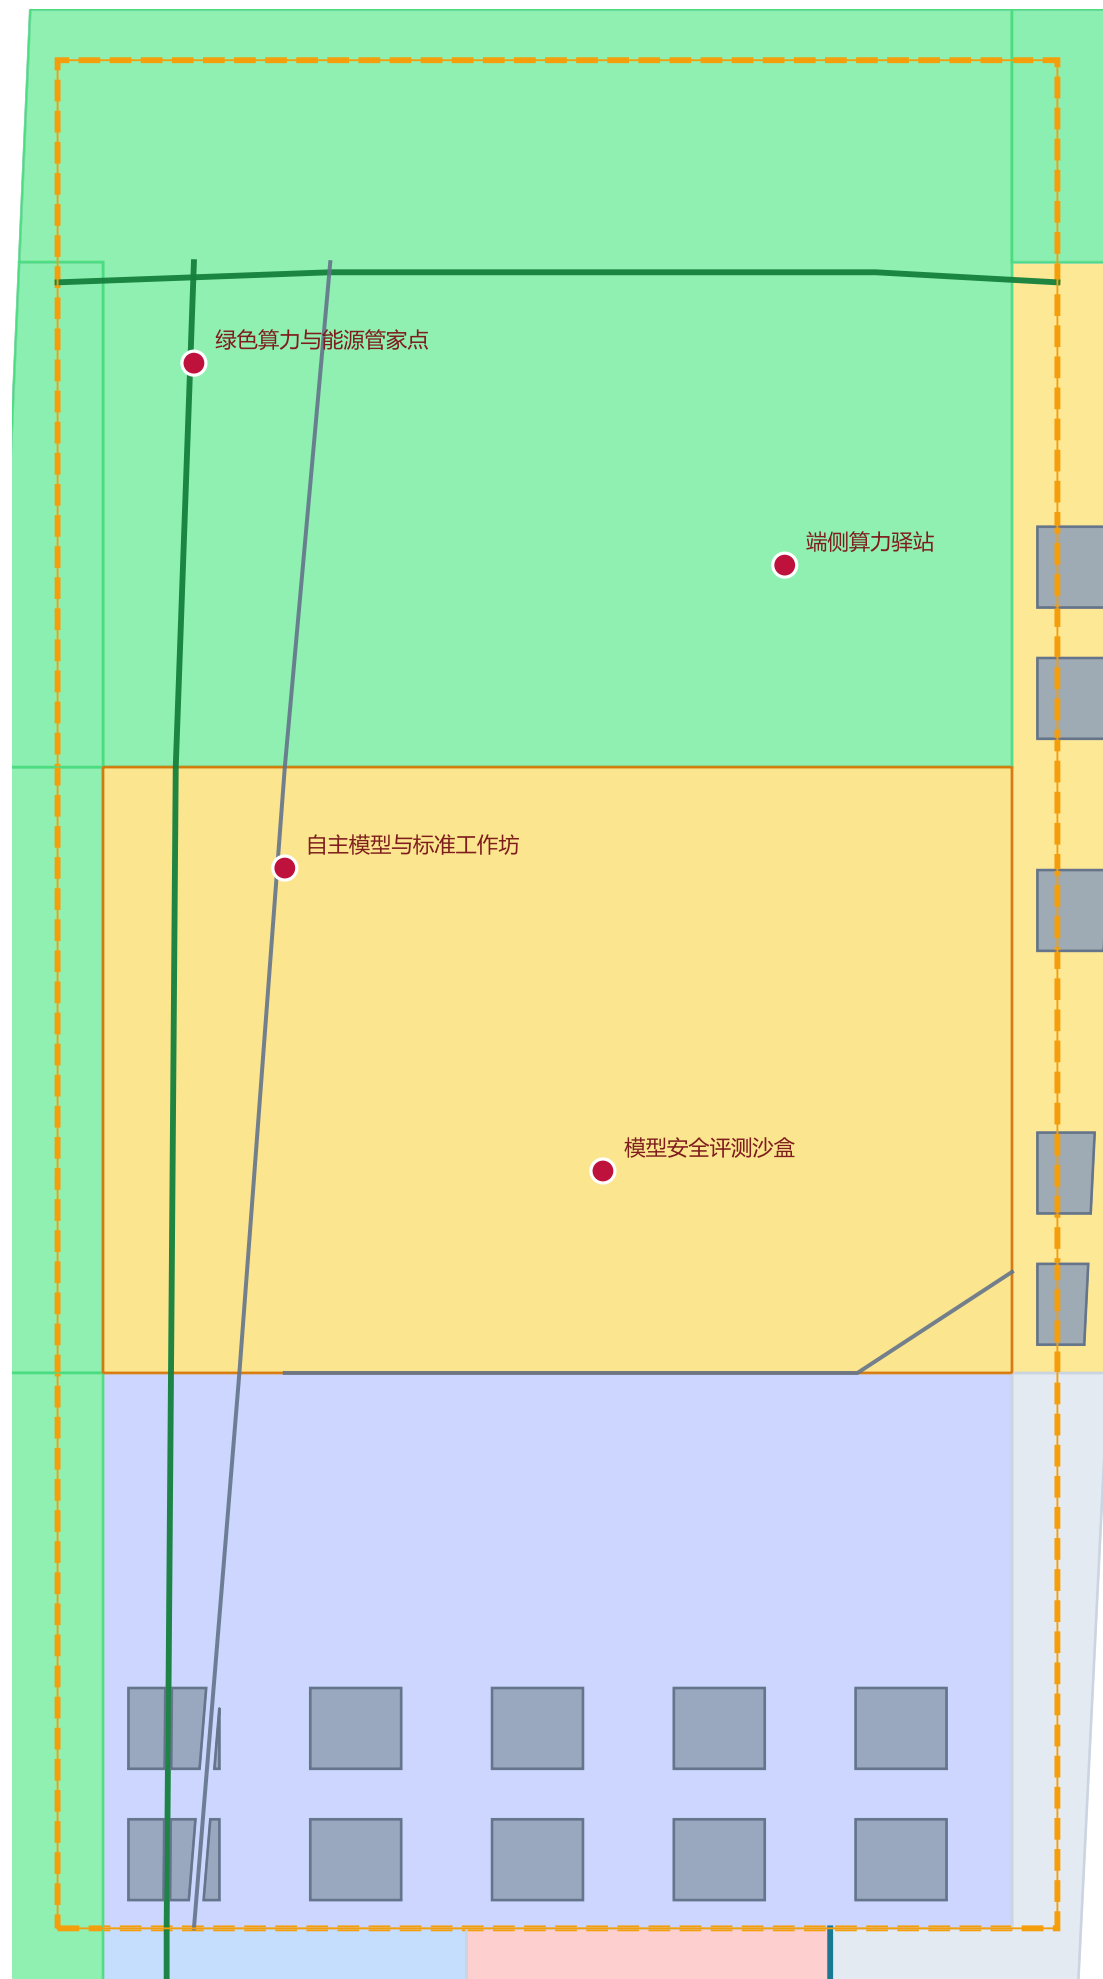

花园型全栈自主创新街区：清河界面绿地、研发组团、评测发布广场、标准工作坊；T1 模型安全评测沙盒与 T2 标准工作坊落地于此。

矩形为 provisional 约束（虚线），不表达红线。


04 北京AI原点社区（智核·原点）

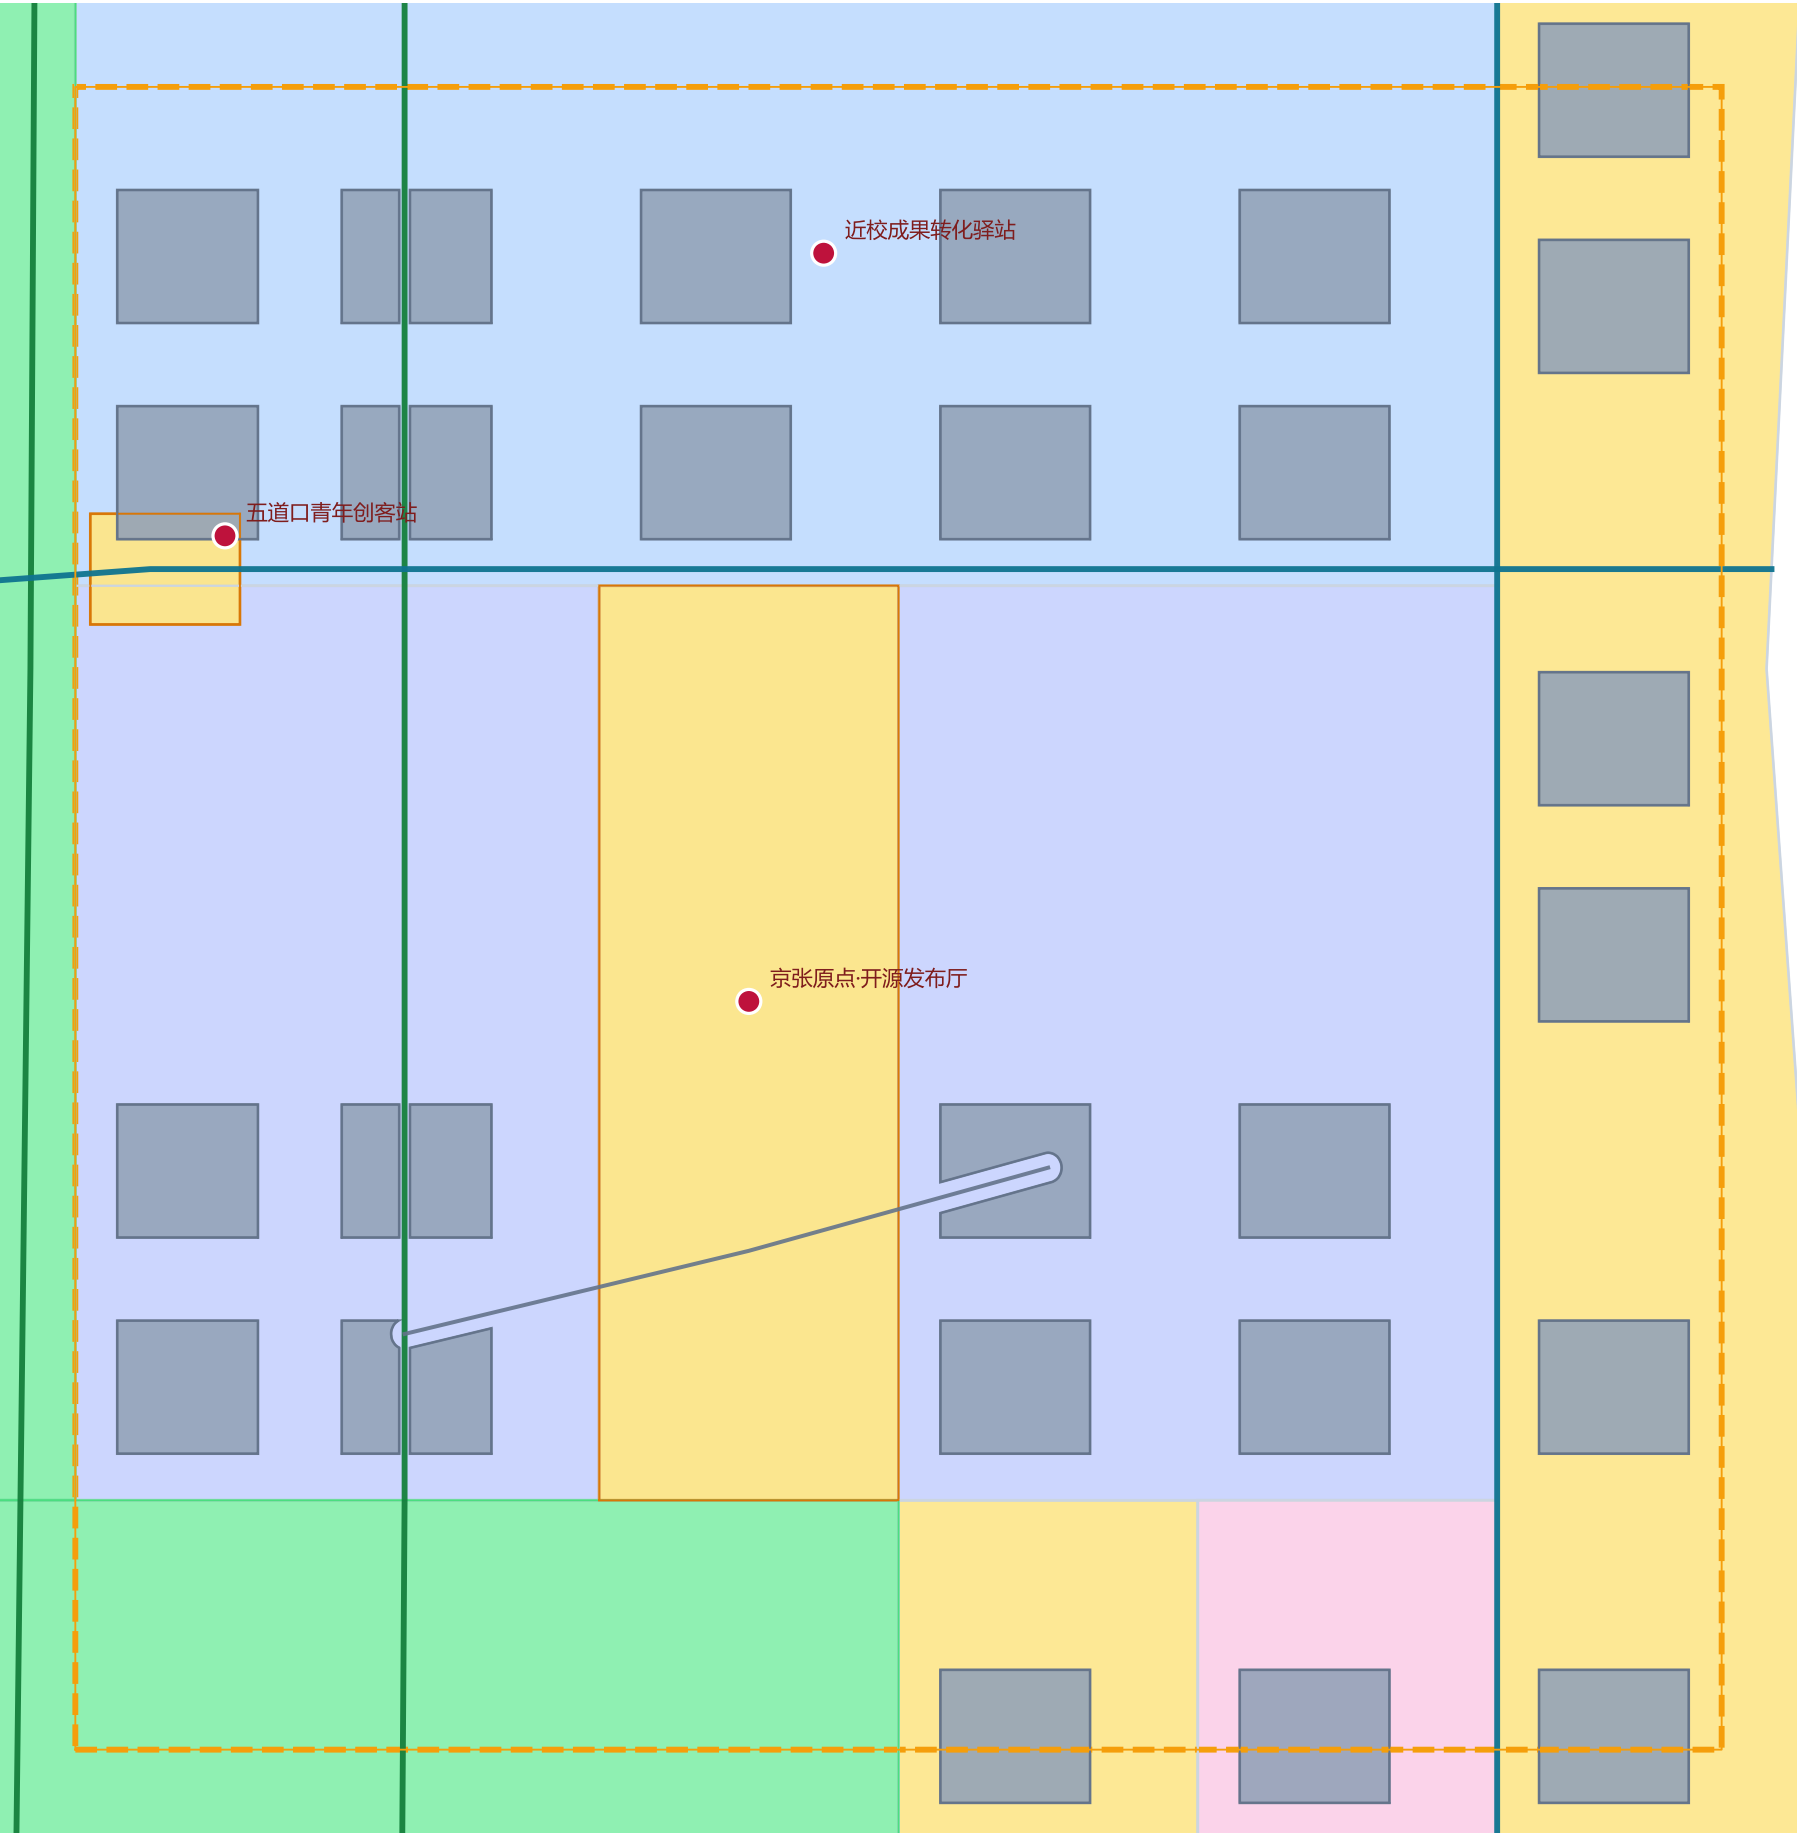

近校型成果转化人才社区：发布广场、成果转化街、中央公园、人才服务带；开源发布厅、五道口站点一体化与低扰动更新。


矩形为 provisional 约束（虚线），不表达红线。

05 大钟寺AI产业集聚区（智核·汇）

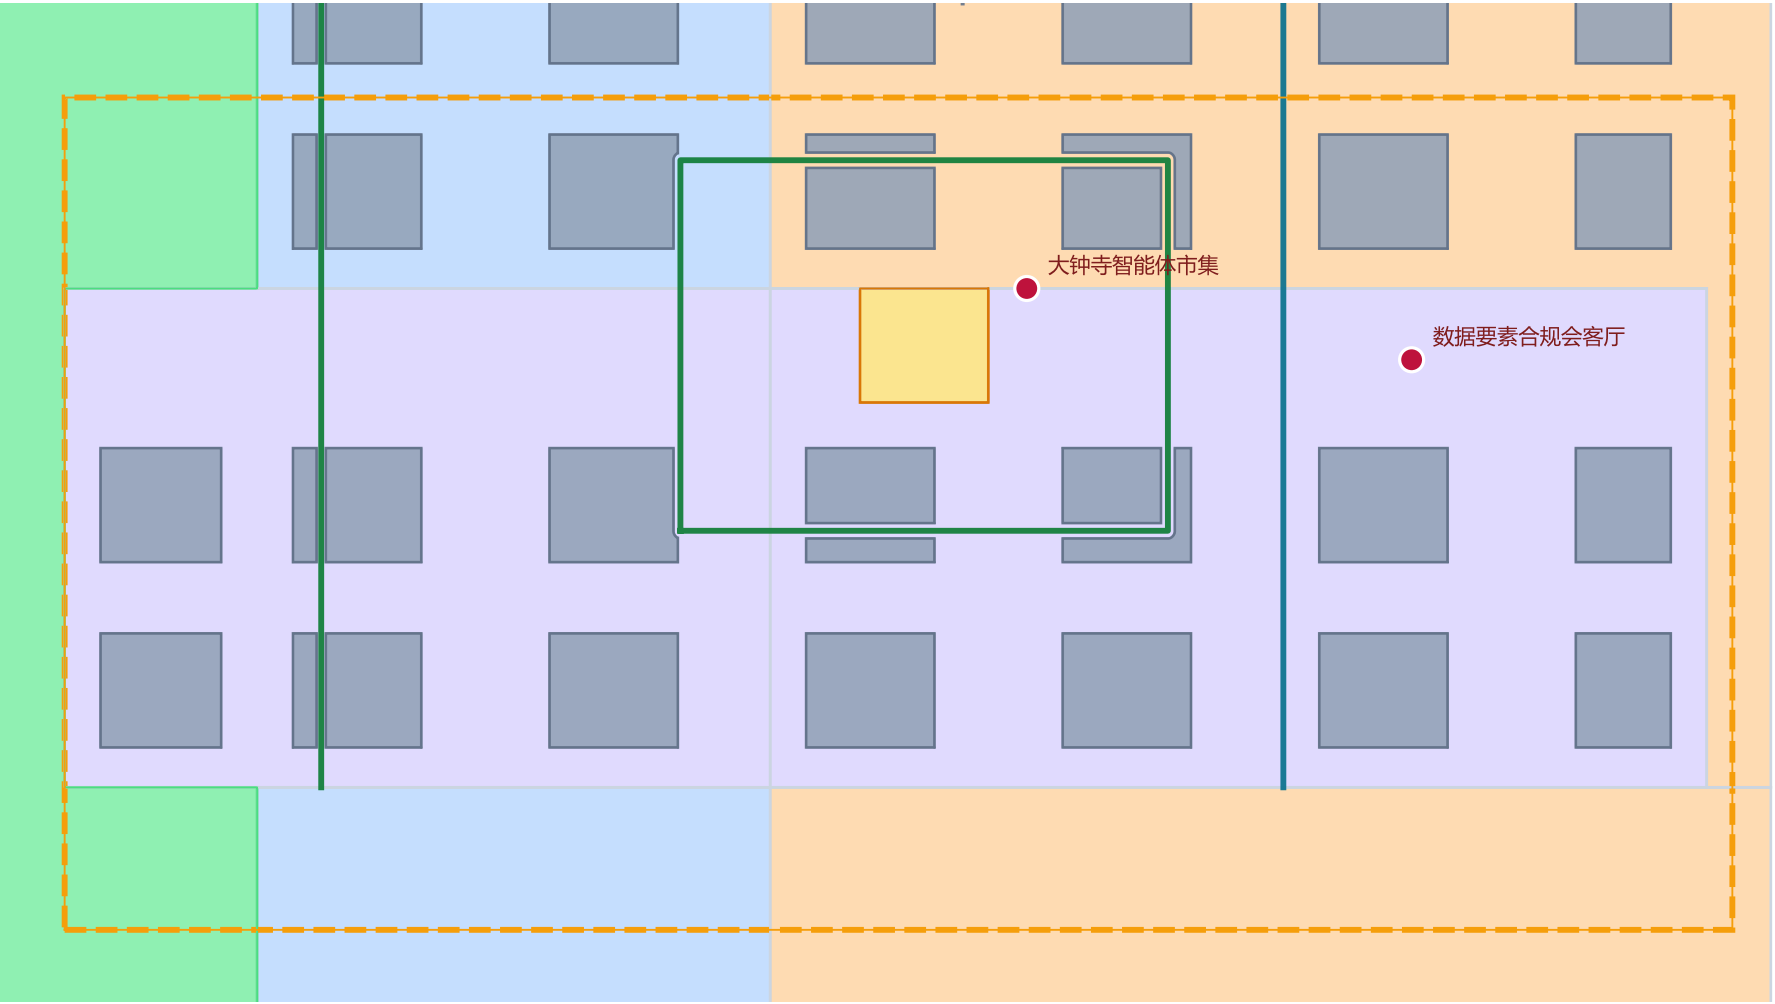

城市型智能经济街区：大钟寺站四象限步行环、站前广场、智能体市集、数据要素会客厅、文化展示用地。

矩形为 provisional 约束（虚线），不表达红线。

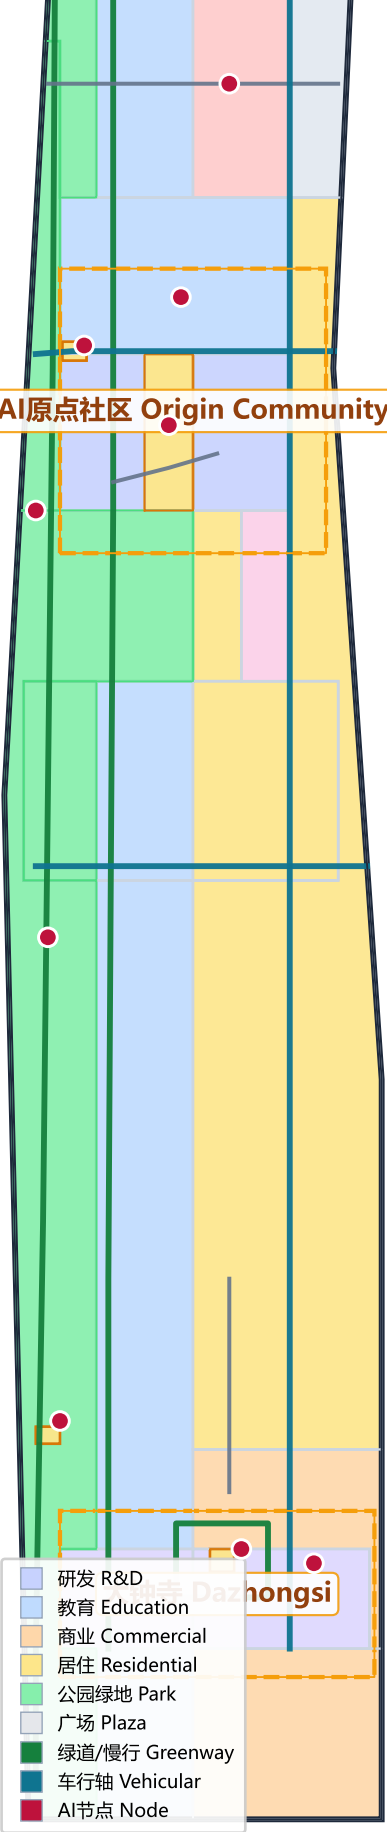

06 交通慢行与蓝绿系统



智脉绿道（绿）贯穿南北，五道口与知春路横轴（蓝）连接东西，大钟寺站四象限

停车与静态交通

站点与重点企业周边设置静态交通组织建议与共享单车集散点；市政管线、断面、

新型基础设施

端侧算力驿站、绿色算力与能源管家、分布式能源与市政设施融合（概念方向）。

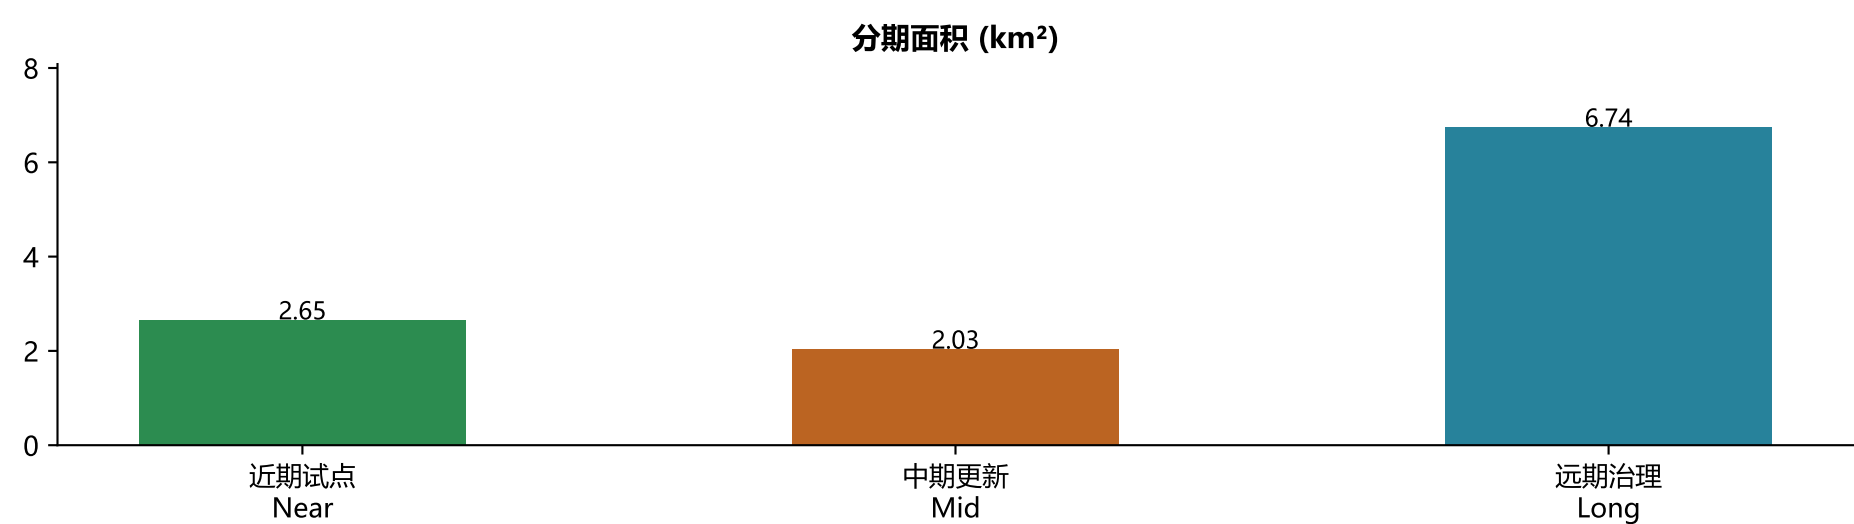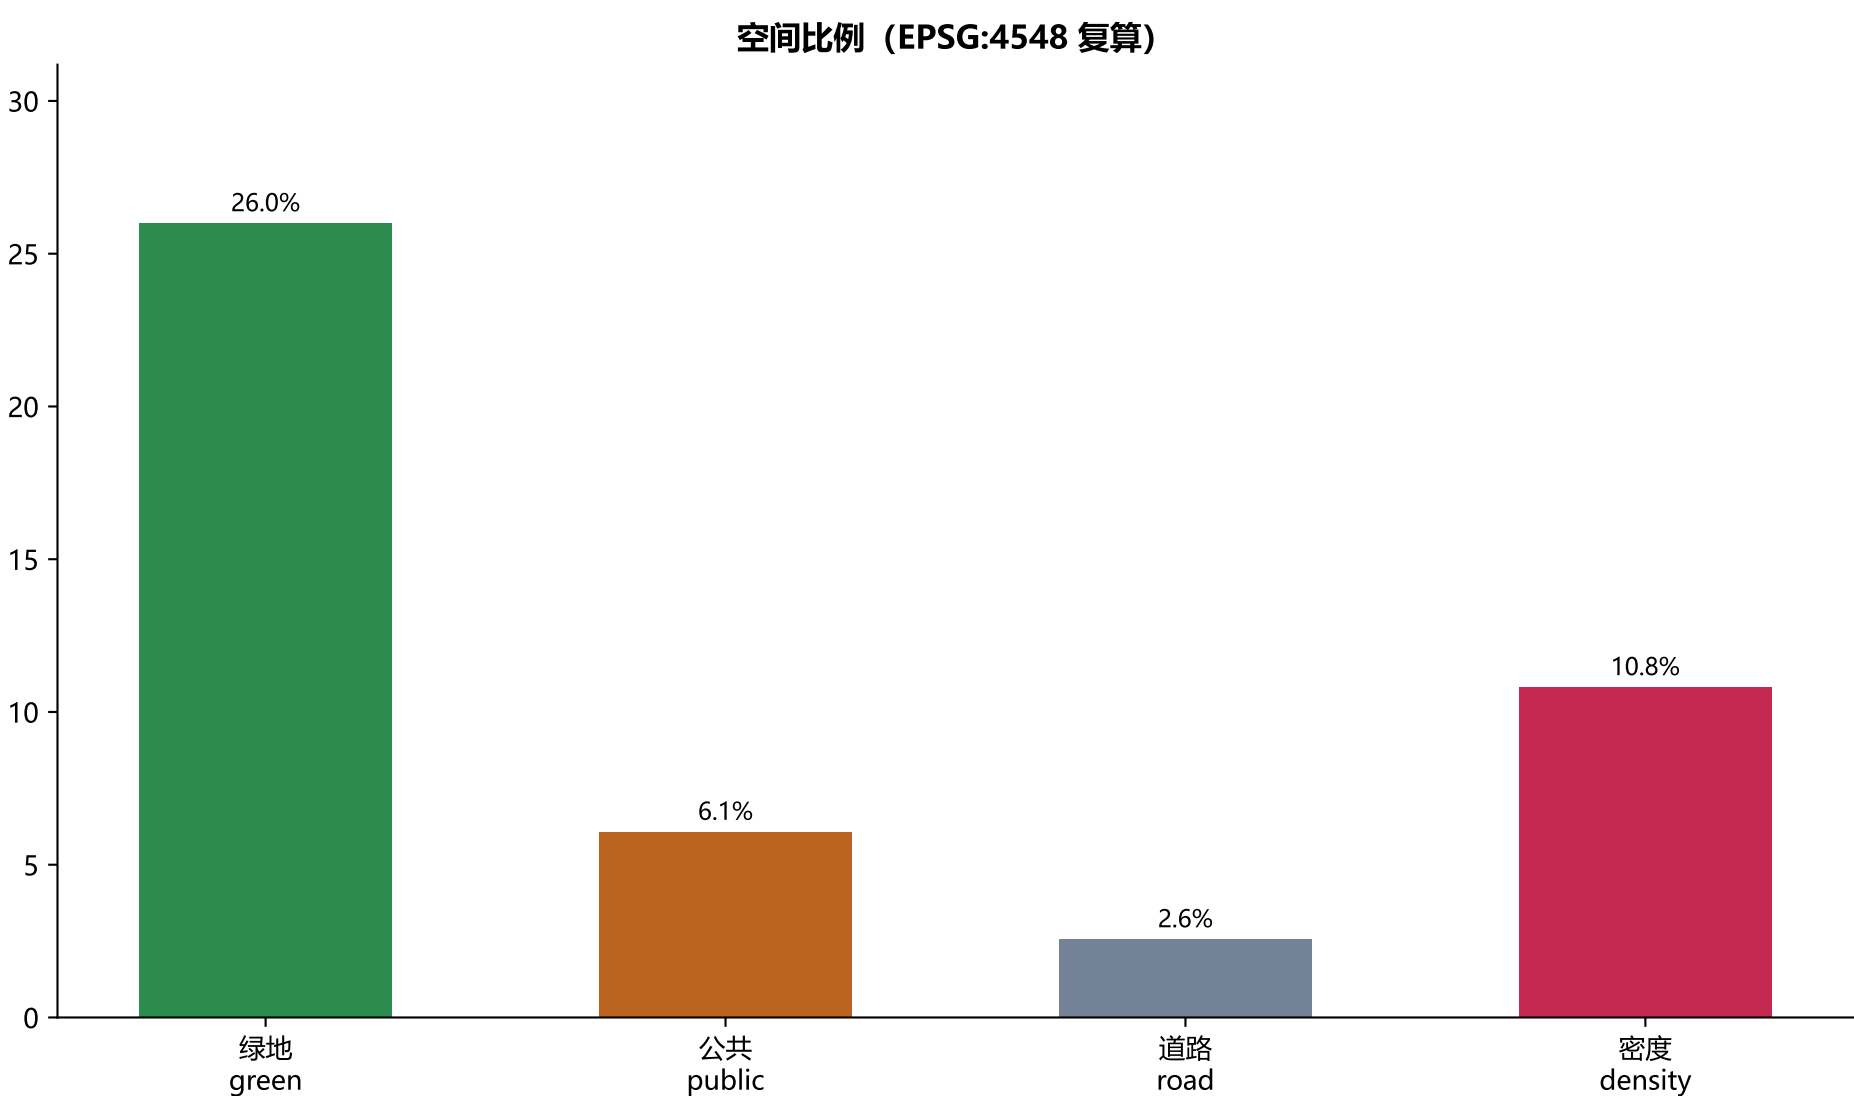

证据链 Evidence chain

公开资料 → 设计图层 (9 个 GeoJSON) → EPSG:4548 指标复算 → 三个矩阵 (任务/标准/深度) → 四门自检 → PR 预检。

全部结论为概念建议；官方边界、控规、权属、市政与文保条件待补。