
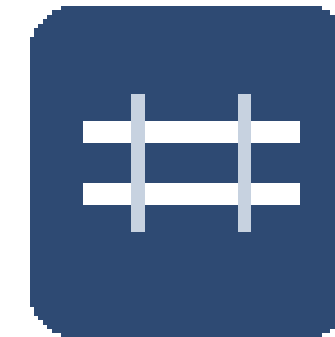


## 总体概念 · 一正线三站两翼

把百年京张铁路变成一条创新产线：动力段·源头站 → 编组段·转化站 → 到达段·到达站

PROVISIONAL 临时边界 · 非官方红线

## 总体设计范围总览（东西向示意放大）

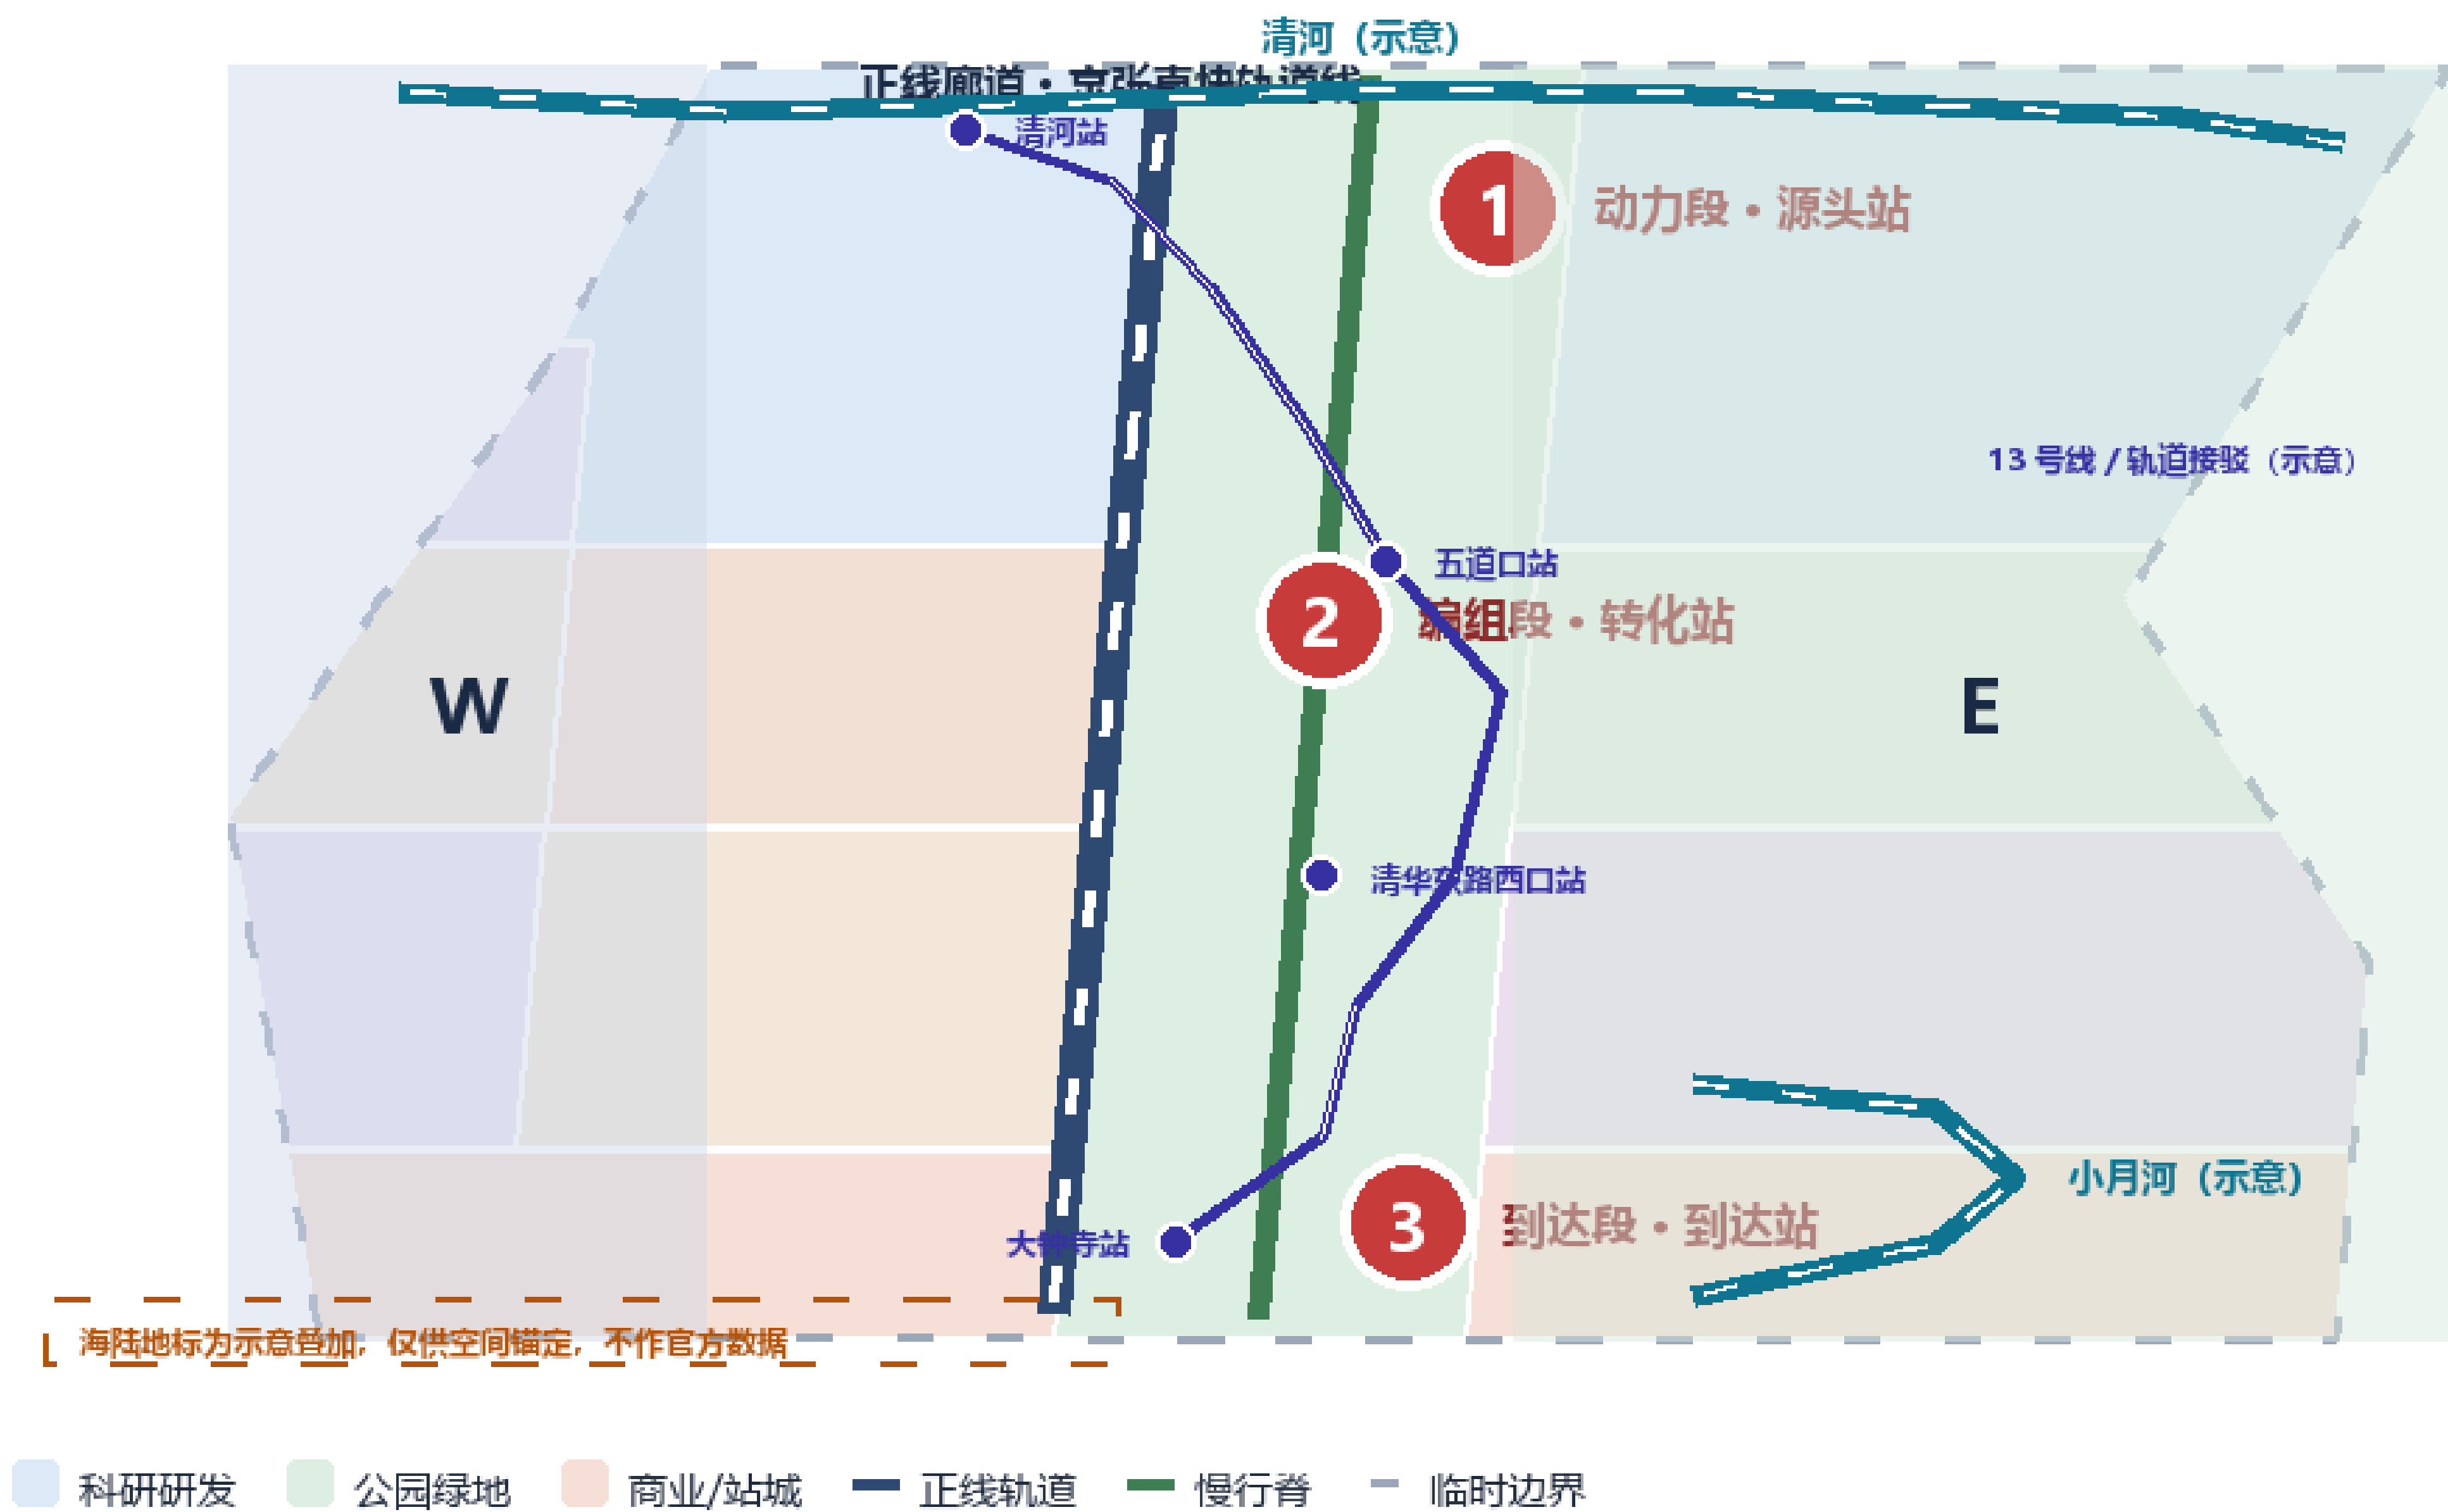

## JINGZHANG EXPRESS

百年京张AI创新带城市设计

—正线三站两翼 = 创新产线（研发→转化→市场）

官方层（公告命名） → 品牌层（方案命名）

众智园AI自主创新加速区

动力段·源头站

北京AI原点社区

编组段·转化站

大钟寺AI产业聚集区

到达段·到达站

## 两翼功能

W 中关村科技服务翼（西）·企业服务·孵化转化·人才服务

E 小月河场景赋能翼（东）·具身智能·机器人·医疗·影视场景试验

## 总体设计范围

11.41 km<sup>2</sup>公告 ≈11.40 km<sup>2</sup>

## 重点区域数

3 处

众智园·原点·大钟寺

## 绿地率

40.5%

绿地 462.2 ha

## 公共空间率

6.7%

公共空间 76.8 ha

数据来源：geometry/\*.geojson + metrics.json (EPSG:4548 复算) | 百年京张AI创新带城市设计

provisional 边界仅作约束示意

总体概念与空间结构总览（临时边界）—— 统筹 43.6 km<sup>2</sup> / 总体 11.4 km<sup>2</sup> / 重点区约 368.4 公顷

|                                             |                               |                           |                                     |
|---------------------------------------------|-------------------------------|---------------------------|-------------------------------------|
| 约 11.41 km <sup>2</sup>                     | 3 处                           | 40.5%                     | 6.7%                                |
| 总体设计范围复算面积 (11,412,825.386 m <sup>2</sup> ) | 重点区域 (metric: key_area_count) | 绿地率 (metric: green_ratio) | 公共空间比例 (metric: public_space_ratio) |

- 一正线：沿京张遗址公园贯通的创新产线主轴，文化、慢行与功能复合走廊
- 三站：众智园（源头）/ 原点社区（转化）/ 大钟寺（到达），对应创新链三环节
- 两翼：中关村科技服务翼（资本与知识产权）+ 小月河场景赋能翼（具身智能与场景验证）
- 创新产线隐喻：统筹层「产线往哪里开」→ 总体层「编组、路网、站城关系」→ 重点层「三站造什么、怎么落地」
- 三层边界均为概念建议，具体范围认定待正式控规与官方 CAD/GIS 数据确认

结构回溯：proposal.md §3.范围、§4.总体设计范围；几何 geometry/site\_boundary.geojson；指标 metrics.json。



## 用地结构·三站×三带矩阵与沿线用地分区

动力/编组/到达三段 × 西翼服务带/正线活力带/东翼场景带；色带按正线方向展布

## 三站 × 三带 矩阵（面积按复算占优用地）


|               | 1 西翼·中关村科技服务带                                                  | 2 正线·京张遗址公园活力带                                                   | 3 东翼·小月河场景赋能带                                                |
|---------------|----------------------------------------------------------------|------------------------------------------------------------------|--------------------------------------------------------------|
| 动力段·源头站（众智园）  | <b>0802 科研用地(研发)</b><br><b>3.2 ha</b><br>0.3%<br>+ 0701 1.7 ha | <b>0802 科研用地(研发)</b><br><b>88.0 ha</b><br>7.7%<br>+ 1401 67.9 ha | <b>0802 科研用地(研发)</b><br><b>122.8 ha</b><br>10.8%             |
| 编组段·转化站（原点社区） | <b>0702 社区服务设施</b><br><b>35.4 ha</b><br>3.1%<br>+ 0701 20.6 ha | <b>1401 公园绿地</b><br><b>99.3 ha</b><br>8.7%<br>+ 0803 64.4 ha     | <b>0804 教育用地</b><br><b>79.2 ha</b><br>6.9%<br>+ 0802 37.9 ha |
| 到达段·到达站（大钟寺）  | <b>05 商业服务业</b><br><b>28.7 ha</b><br>2.5%<br>+ 0701 27.9 ha    | <b>1401 公园绿地</b><br><b>81.7 ha</b><br>7.2%<br>+ 05 49.6 ha       | <b>0806 医疗卫生用地</b><br><b>82.8 ha</b><br>7.3%<br>+ 05 67.0 ha |

## 用地代码图例（面积自 metrics.json 复算）

- 05 商业服务业 145.3 ha (12.7%)
- 0701 城镇住宅(人才社区) 50.2 ha (4.4%)
- 0702 社区服务设施 115.9 ha (10.2%)
- 0802 科研用地(研发) 289.7 ha (25.4%)
- 0803 文化用地 73.2 ha (6.4%)
- 0804 教育用地 88.5 ha (7.8%)
- 0806 医疗卫生用地 129.5 ha (11.3%)
- 1401 公园绿地 249.0 ha (21.8%)

控规类指标（容积率/高度/密度/退线）无官方条件 → 待正式数据补齐

## 沿正线（北→南）的用地分区色带

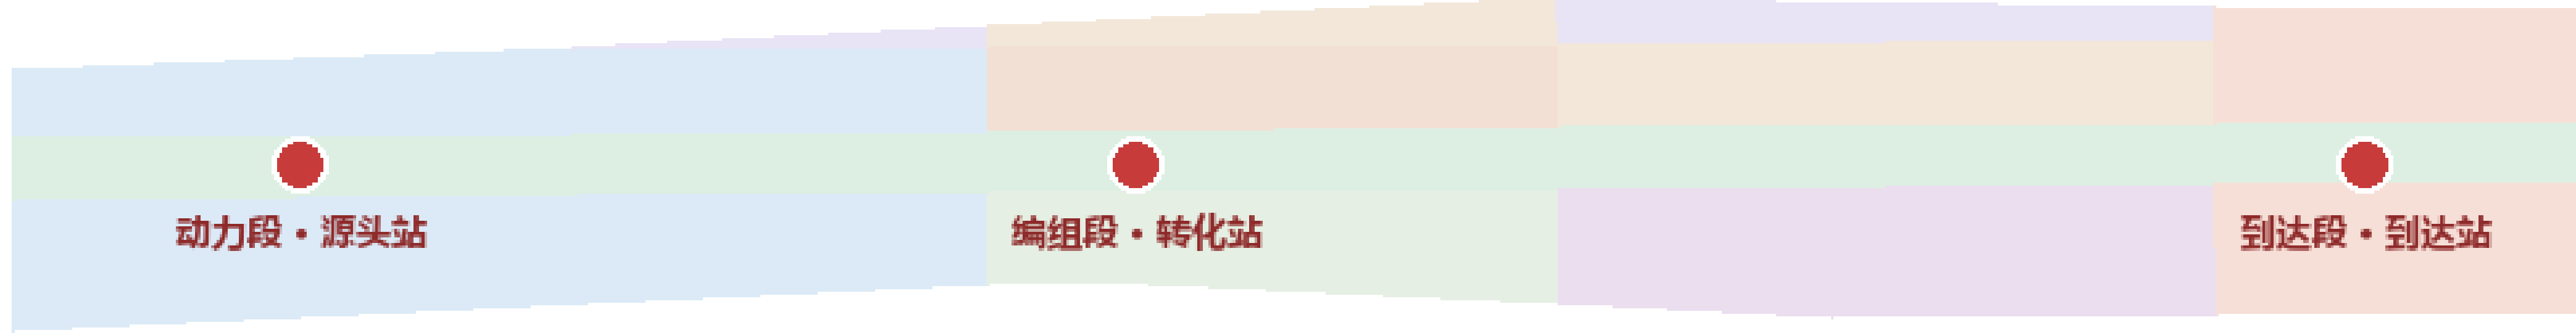

北 N → 南 S

数据来源：geometry/\*.geojson + metrics.json (EPSG:4548 复算) | 百年京张AI创新带城市设计

provisional 边界仅作约束示意

总体设计范围用地结构与空间关系（临时边界）

|                                              |                                        |                                              |                                                         |
|----------------------------------------------|----------------------------------------|----------------------------------------------|---------------------------------------------------------|
| <b>0802 • 25.4%</b><br>科研用地（众智园AI研发与机器人试验研发） | <b>1401 • 21.8%</b><br>公园绿地（京张遗址公园活力带） | <b>05 • 12.7%</b><br>商业服务业用地（大钟寺站城商业与AI原生消费） | <b>141.18 万 m²</b><br>建筑基底总面积 (1,411,751.75 m², 设计意象口径) |
|----------------------------------------------|----------------------------------------|----------------------------------------------|---------------------------------------------------------|

• 更新对象：低效空间与遗址公园两侧地区；识别逻辑遵循公告：更新潜力、功能业态、居住商贸均衡、AI企业聚集与AI产业空间规模

• 保留：遗址公园、文物文化节点、轨道与有价值既有建筑；改造：低效厂房/办公/社区空间适AI化；新建：创新平台、人才住房与链接枢纽

• 容积率、建筑高度、建筑密度、绿地率（官方口径）、退线状态均 unknown，待正式控规补齐后复算

• 拆改暂不给出具体地块结论，仅提供分类框架与深化检查项 (design\_depth\_matrix.json)

用地占比复算自 metrics.json (land\_use\_share\_\*)；图例 geometry/land\_use.geojson, geometry/buildings.geojson,




## 交通蓝绿·正线慢行脊·轨道接驳·蓝绿连续性

慢行脊 + 轨道接驳点 + 蓝绿连续性 + 断点修复 + AI场景节点

PROVISIONAL 临时边界·非官方红线

交通慢行与蓝绿空间系统（示意）

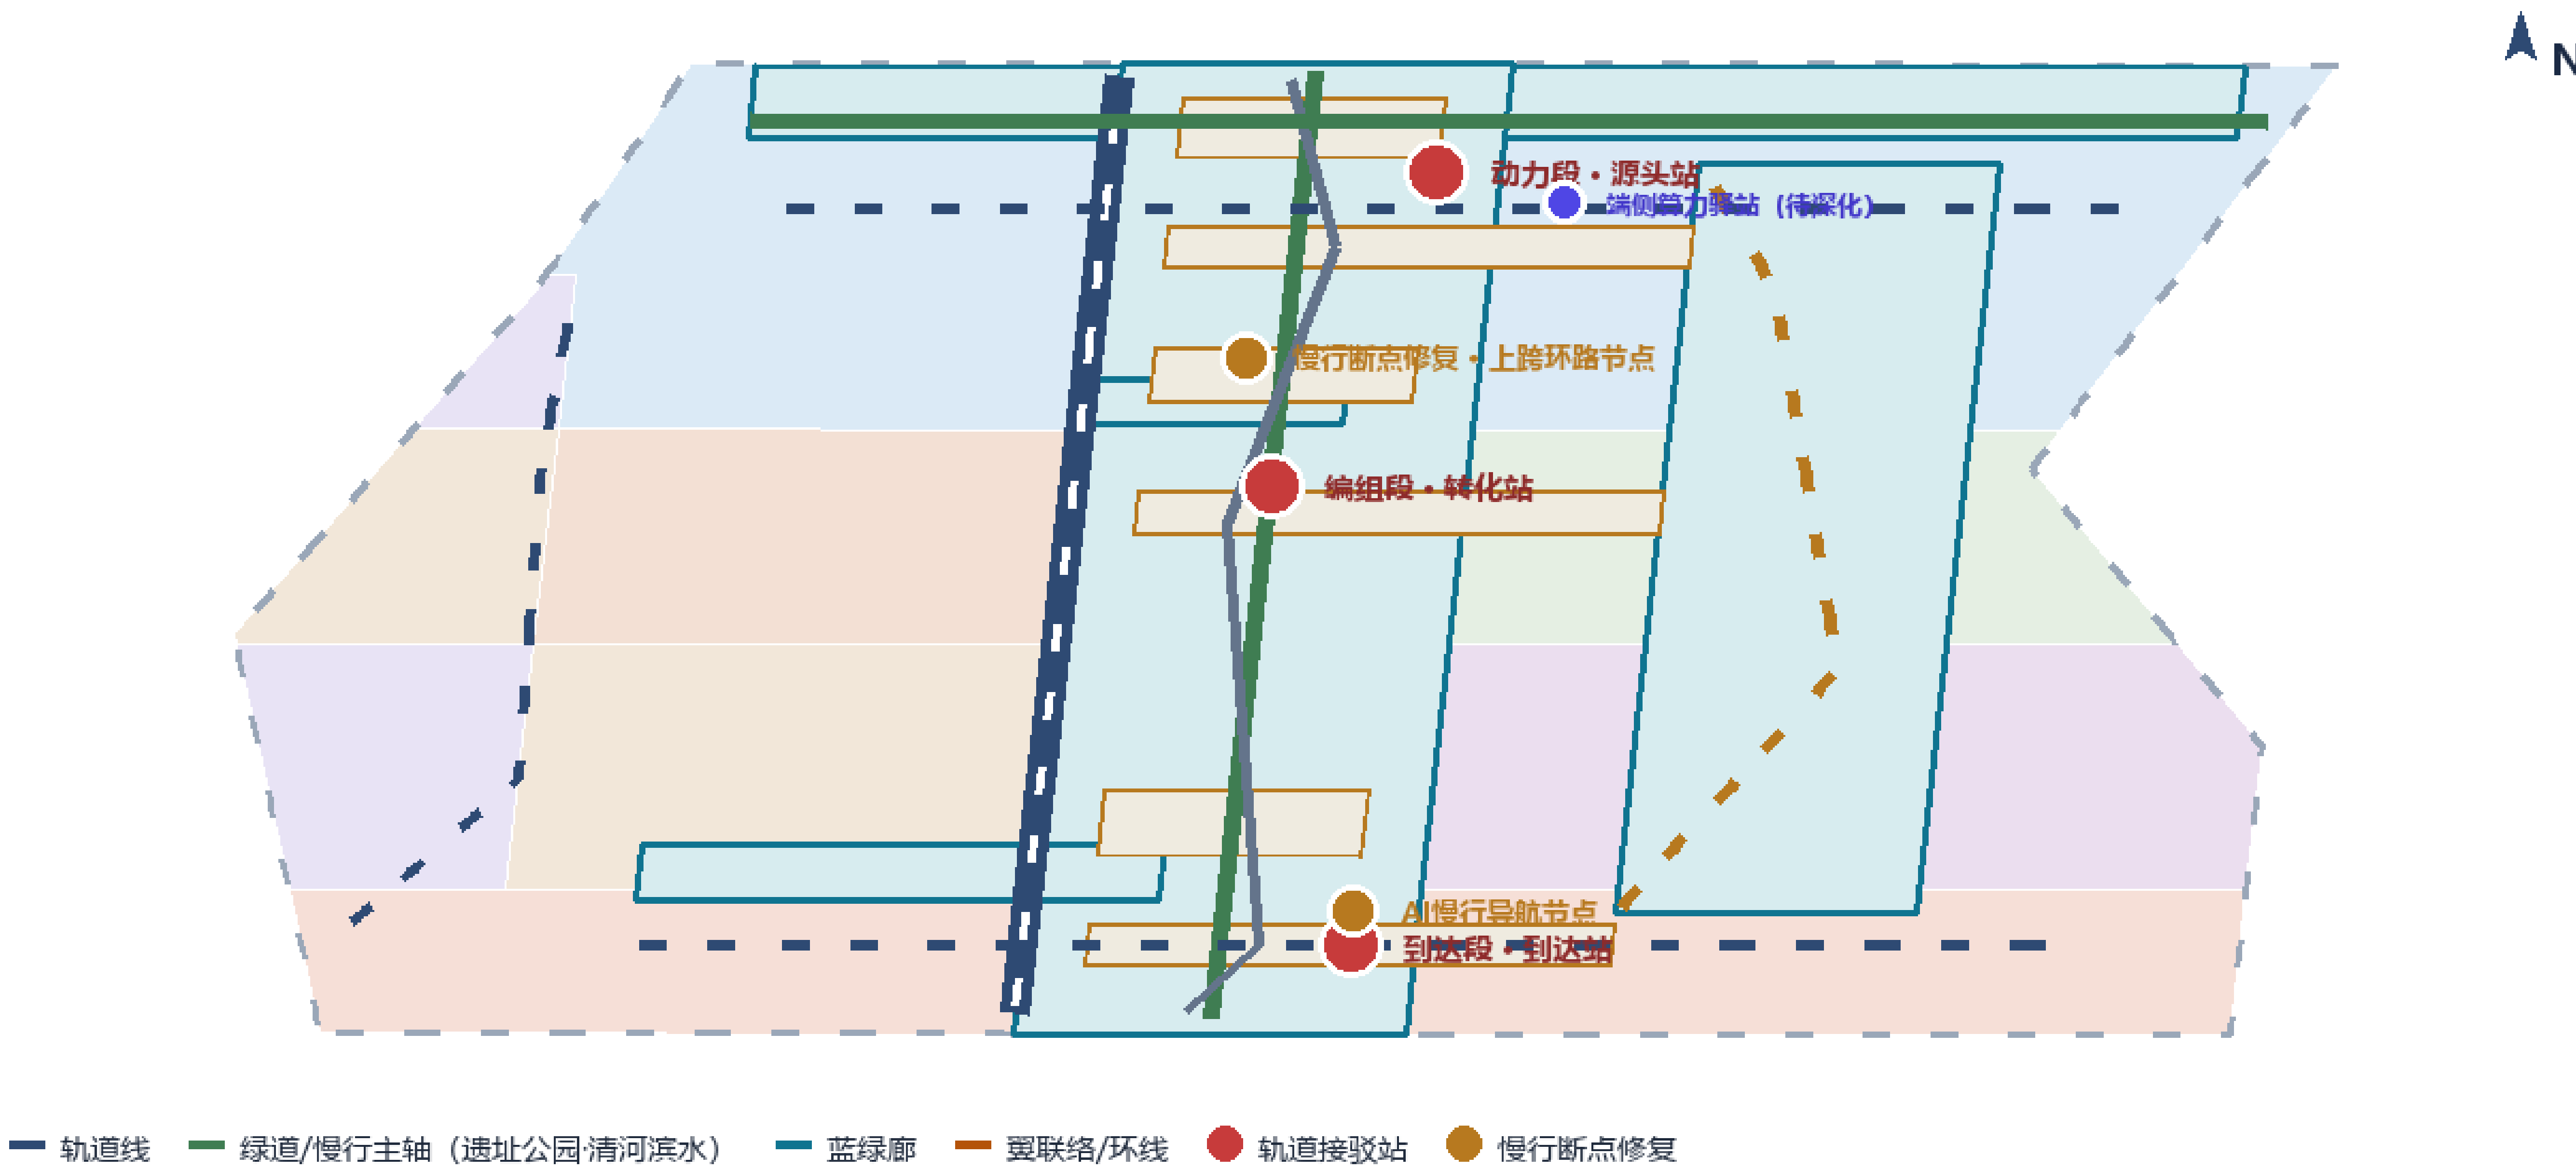

## KEY METRICS

道路中心线总长（概念网络）

44,977 m

概念道路网络

绿地率

40.5%

蓝绿连续性

公共空间率

6.7%

站前广场+慢行节点

京张直快轨道线（三站接驳）

遗址公园慢行主轴（绿道）·串联三站

开发者散步道

图内边界仅供生成/展示/复算，不作审批依据

数据来源：geometry/\*.geojson + metrics.json (EPSG:4548 复算) | 百年京张AI创新带城市设计

provisional 边界仅作约束示意

交通慢行与蓝绿公共空间复合系统（临时边界）

44,977.56 m

道路网络复算总长（44,977.56 米，概念网络口径）

3 站

轨道站点一体化：五道口 / 清华东路西口 / 大钟寺

1 轴 + 2 环

遗址公园慢行主轴 + 两翼慢行环线（含清河滨水步道）

待确认

道路红线、轨道线位、桥隧与市政管线

- 正线：遗址公园慢行主轴（ROAD-001/007）+ 三站接驳轨道线（ROAD-002）构成南北脊梁
- 轨道站点一体化：四象限步行连通、非机动车停放等静态交通组织
- 市政：AI产业服务设施、创新服务平台、分布式能源、碳捕捉力与传统三大设施融合
- 管线、能源、排水、防洪与消防工程资料缺失，全部列为正式深化前置条件

图源 geometry/roads.geojson (ROAD-001—008)；指标 metric\_road\_length.m；本图不含工程线位信息。




## 交通蓝绿 · 正线慢行脊 · 轨道接驳 · 蓝绿连续性

慢行脊 + 轨道接驳点 + 蓝绿连续性 + 断点修复 + AI场景节点

PROVISIONAL 临时边界 · 非官方红线

交通慢行与蓝绿空间系统（示意）

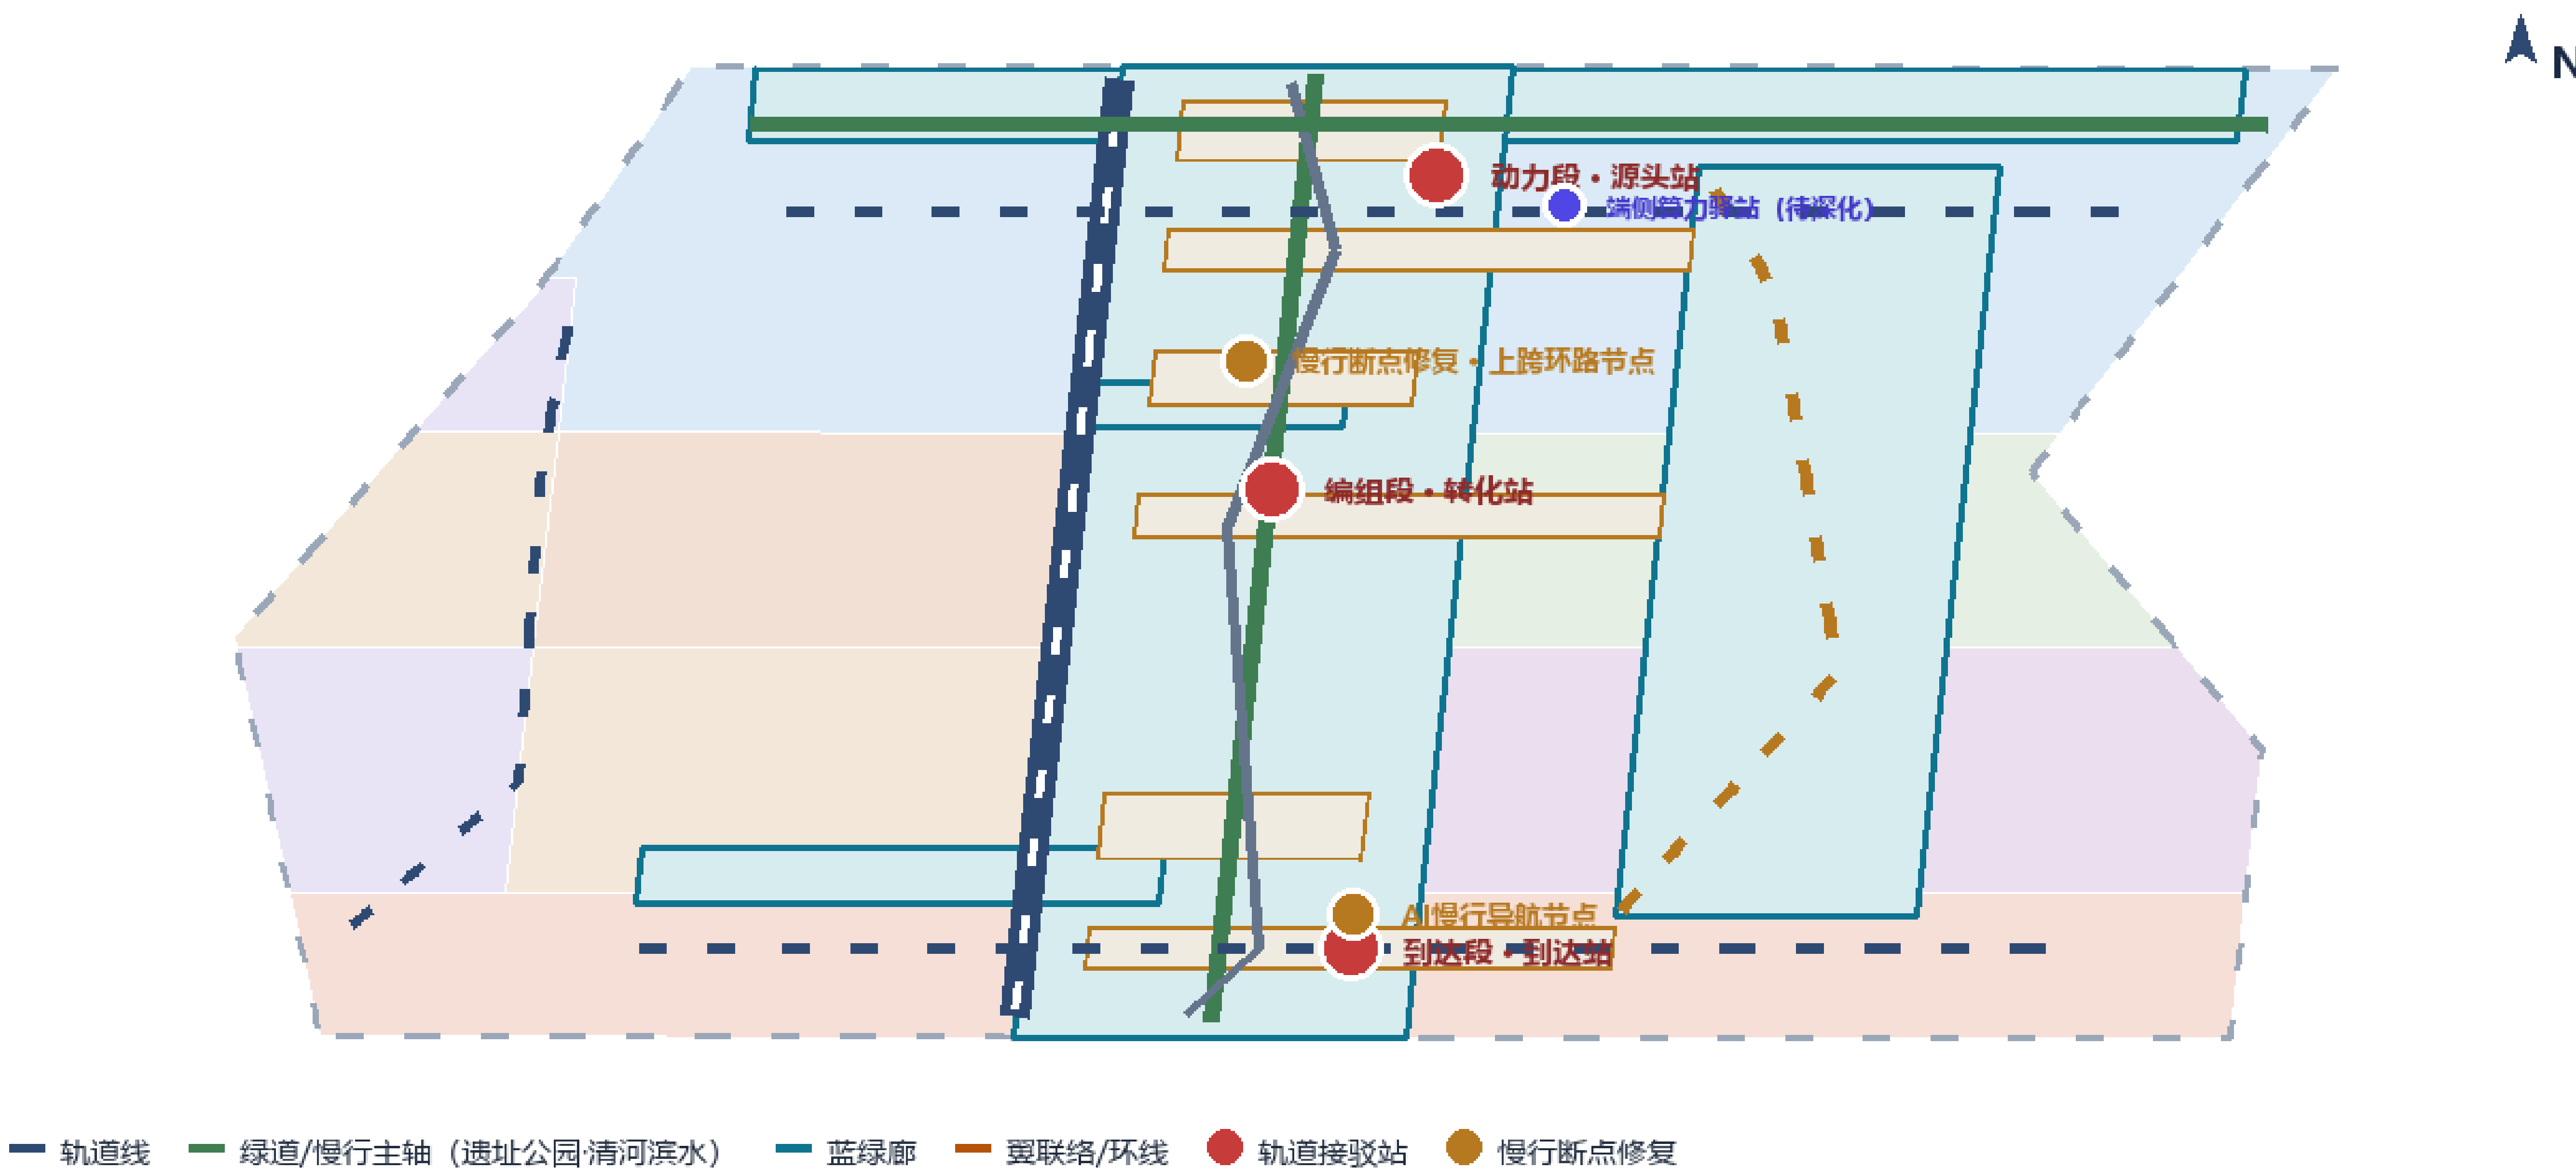

— 轨道线 — 绿道/慢行主轴（遗址公园·清河北水） — 蓝绿廊 — 翼联络/环线 — 轨道接驳站 — 慢行断点修复

## KEY METRICS

道路中心线总长（概念网络）

44,977 m

概念道路网络

绿地率

40.5%

蓝绿连续性

公共空间率

6.7%

站前广场+慢行节点

京张直快轨道线（三站接驳）

遗址公园慢行主轴（绿道）·串联三站

开发者散步道

图内边界仅供生成/展示/复算，不作审批依据

数据来源：geometry/\*.geojson + metrics.json (EPSG:4548 复算) | 百年京张AI创新带城市设计

provisional 边界仅作约束示意

交通慢行与蓝绿公共空间复合系统（临时边界）——蓝绿骨架示意

462.21 万 m²

绿道系统复算面积 (4,622,126.492 m²)

40.5%

绿地率 (metric: green\_ratio)

76.82 万 m²

公共空间复算面积 (768,238.604 m²)

6.7%

公共空间比例 (metric: public\_space\_ratio)

- 骨架：京张遗址公园活力带、传统清河、小月河与观礼、企业、社区出行，南北贯通东西连通的步道与骑行道体系
- AI 朝圣地标①：处发钟楼智能体贡献智慧（众智园源头站）
- AI 朝圣地标②：开源成果展示廊（原点社区开源广场）
- AI 朝圣地标③：开发者散步道（遗址公园慢行主轴，连接三站/节点）
- 风貌：京张铁路历史文化 + 中关村创新文化 + AI 创新文化；清河与小月河蓝线待官方确认

图源: geometry/green\_space.geojson, geometry/public\_space.geojson; 图例: metric: green\_ratio / public\_space\_ratio.



# 重点区域 · 三站差异：源头-转化-到达

定位 · 空间动作 · AI场景 · 实施风险（几何为 provisional 粗略范围）

PROVISIONAL 临时边界 · 非官方红线

## 三处重点区位置（临时粗略范围）



图内边界仅供生成/展示/复算，不作审批依据

### ① 众智园AI自主创新加速区

动力段 · 源头站 · 192.9 ha

定位：花园型全栈自主创新街区

空间：强化清河界面 · 产业展示 · 低碳创新交往 · 对外交通组织

AI场景：自主模型测试 · 标准制定工作坊 · 安全治理展示 · 低碳算力体验

风险：清河蓝线/防洪待确认 · 对外交通需复核

### ② 北京AI原点社区

编组段 · 转化站 · 104.3 ha

定位：近校型成果转化与人才社区

空间：校区-园区-街区慢行缝合 · 成果发布 · 人才服务 · 开源协作

AI场景：开源社区 · 成果发布 · 人才特区服务 · 近校孵化

风险：校区边界/权属待确认 · 拆改留待定

### ③ 大钟寺AI产业聚集区

到达段 · 到达站 · 72.0 ha

定位：城市型智能经济与国际交往街区

空间：大钟寺站一体化 · 四象限步行连通 · 商业服务 · 绿地复合利用

AI场景：智能体与智能终端展示 · 内容消费 · 数据要素 · 国际路演

风险：轨道站点/管线条件待确认 · 路口四象限实施复杂

数据来源：geometry/\*.geojson + metrics.json（EPSG:4548 复算） | 百年京张AI创新带城市设计

provisional 边界仅作约束示意

三处重点区域索引与设计定位（临时边界）

|                                             |                                         |                                        |                                  |
|---------------------------------------------|-----------------------------------------|----------------------------------------|----------------------------------|
| 192.92 ha<br>众智园AI自主创新加速区（1,529,201.877 m²） | 104.32 ha<br>北京AI原点社区（1,043,236.909 m²） | 72.05 ha<br>大钟寺AI产业聚集区（720,454.219 m²） | 369.3 ha<br>三处重点区域合计（约 368.4 公顷） |
|---------------------------------------------|-----------------------------------------|----------------------------------------|----------------------------------|

• 动力段 源头站（众智园）：花园型全栈自主创新街区，「南研北展、蓝绿环抱」；清河创新界面 + 研发组团 + 治理展示组团  
• 编组段 转化站（原点社区）：近校成果转化街 + 开源协作组团 + 人才居住组团（校区-园区-街区融合）  
• 到达段 到达站（大钟寺）：站城商业街区 + AI原生消费体验街区，四象限步行连通  
• 三处片区为临时粗略边界（PROV-KEY-001/002/003），官方 polygon 到位后按 A-BOUNDARY-002 复算  
图景 geometry/key\_areas.geojson；面积 metric/key\_area\_sqm；» 数值均与公件的图景范围内一致。



|                                      |                        |                                 |                                  |
|--------------------------------------|------------------------|---------------------------------|----------------------------------|
| 13                                   | 4 ★                    | 6 类                             | 1 闭环                             |
| AI 场景卡（AI+医疗/医疗/教育/法律/生活/交通/公共空间/商业） | 产业测试验证场景（卡01/05/07/11） | 用户画像：研究者/开发者/创业者/投资人/市民与老年/国际访客 | 场景开放 → 参与测试 → 成果沉淀 → 社区增长 → 招引转化 |

场景卡一览

- 每张卡给出空间位置、服务对象、数据、隐私边界、人工复核、运营主体与风险七要素
- 治理原则：数据最小化、公开来源、可解释、人工复核；不替代规划审批，不输出未授权个人画像
- 年度活动体系（概念）：开发者大会、开源成果发布日、AI场景开放周、国际路演

场景卡七要素全文见 proposal.md | AI 场景卡：全部为概念建议与测试验证性质，不构成已批准运营。

| 编号 | 场景名称           | 空间位置        | 验证 |
|----|----------------|-------------|----|
| 01 | ★模拟训练与评测开放测试场  | 众智园         | ★  |
| 02 | 安全治理沙盘         | 众智园         |    |
| 03 | 京张文化智能导览       | 遗址公园/文化带    |    |
| 04 | 企业服务智能体        | 原点社区/众智园    |    |
| 05 | ★开源合规与知识产权服务台  | 原点社区        | ★  |
| 06 | 公共安全运营人工复核     | 公共空间        |    |
| 07 | ★近校创新教育与AI素养课堂 | 原点社区        | ★  |
| 08 | AI健康服务导航       | 小月河翼        |    |
| 09 | 大钟寺AI原生消费与内容体验 | 到达站         |    |
| 10 | 数据要素会客厅        | 到达站         |    |
| 11 | ★小月河低速机器人配送    | 小月河翼        | ★  |
| 12 | AI生活服务样板街      | 社区/商业交汇处    |    |
| 13 | AI慢行与无障碍导航     | 遗址公园/轨道交通节点 |    |



# 指标证据链 · 复算关系 · 指标卡 · 待确认控规

PROVISIONAL 临时边界 · 非官方红线

所有 known 指标自 geometry 在 EPSG:4548 下复算；5 项控规指标待正式数据补齐

## 复算关系

geometry/\*.geojson

EPSG:4548 投影复算  
shapely 面积/长度

metrics.json  
39 known + 5 unknown

图件 · 正文 · HTML · 矩阵

## 总体设计范围面积

11.41 km<sup>2</sup>

公告 ≈11.40 km<sup>2</sup>

## 绿地率

40.5%

绿地 462.2 ha

## 公共空间率

6.7%

公共空间 76.8 ha

## 建筑基底面积（概念，low conf.）

1.41 km<sup>2</sup>

confidence=low · 概念

## 道路中心线总长（概念网络）

44,977 m

概念道路网络

## 重点区域面积（3处）

192.9 ha

动力段 · 源头站

104.3 ha

编组段 · 转化站

72.0 ha

到达段 · 到达站

## 分期实施面积

325.7 ha

P1 近期试点

314.8 ha

P2 中期更新

500.7 ha

P3 长期治理

## 用地结构占比（复算）

0802 科研用地(研发) 25.4%

1401 公园绿地 21.8%

05 商业服务业 12.7%

0806 医疗卫生用地 11.3%

## 待正式数据补齐 (status=unknown)

容积率 / 建筑高度 / 建筑密度 · 官方绿地率 / 退线

官方控规条件缺失: planning\_limits.json status=missing; 正式提交前不得以推测值冒充审定指标

floor\_area\_ratio

building\_height\_m

building\_density

green\_ratio\_official

setback\_m

→ value = null (待正式控规数据补齐)

数据来源: geometry/\*.geojson + metrics.json (EPSG:4548 复算) | 百年京张AI创新带城市设计

provisional 边界仅作约束示意

核心指标复算与证据链 (临时边界)

11,412,825.386 m<sup>2</sup>

总体设计范围面积 (metric: site\_area\_sqm)

44,977.56 m

道路长度 (metric: road\_length\_m)

1,411,751.75 m<sup>2</sup>

建筑基底面积 (metric: building\_footprint\_area\_sqm)

容差内

总体与三处重点区域面积均与公告的值一致 (A-AREA-TOLERANCE-001)

- 合规矩阵覆盖公告 1.3, 1.4, 1.5 (含 1.5.3.1/1.5.3.2/1.5.3.3) 与 agent-1-agent-6 全部必选任务
- 每象任务对应报告章节、图层、图则、图纸、HTML 页面、来源、假设与自检项 (compliance\_matrix.json)
- 容积率、高度、密度、官方绿地率、退线: unknown, 待正式控规补齐 (planning\_limits.json)
- 待补资料: 官方红线、重点区官方 polygon、道路红线、权属、市政管线、文保、蓝线、防洪与消防
- 本成果为 provisional boundary 概念成果, 替换 official polygon 后所有图层与指标整体复算

指标全部来源 metrics.json; 复算坐标系 EPSG:4548; 差值假设 A-AREA-TOLERANCE-001.