



Structure: a reversal translated into space

Overall structure / land-use partition / evidence of topological closure

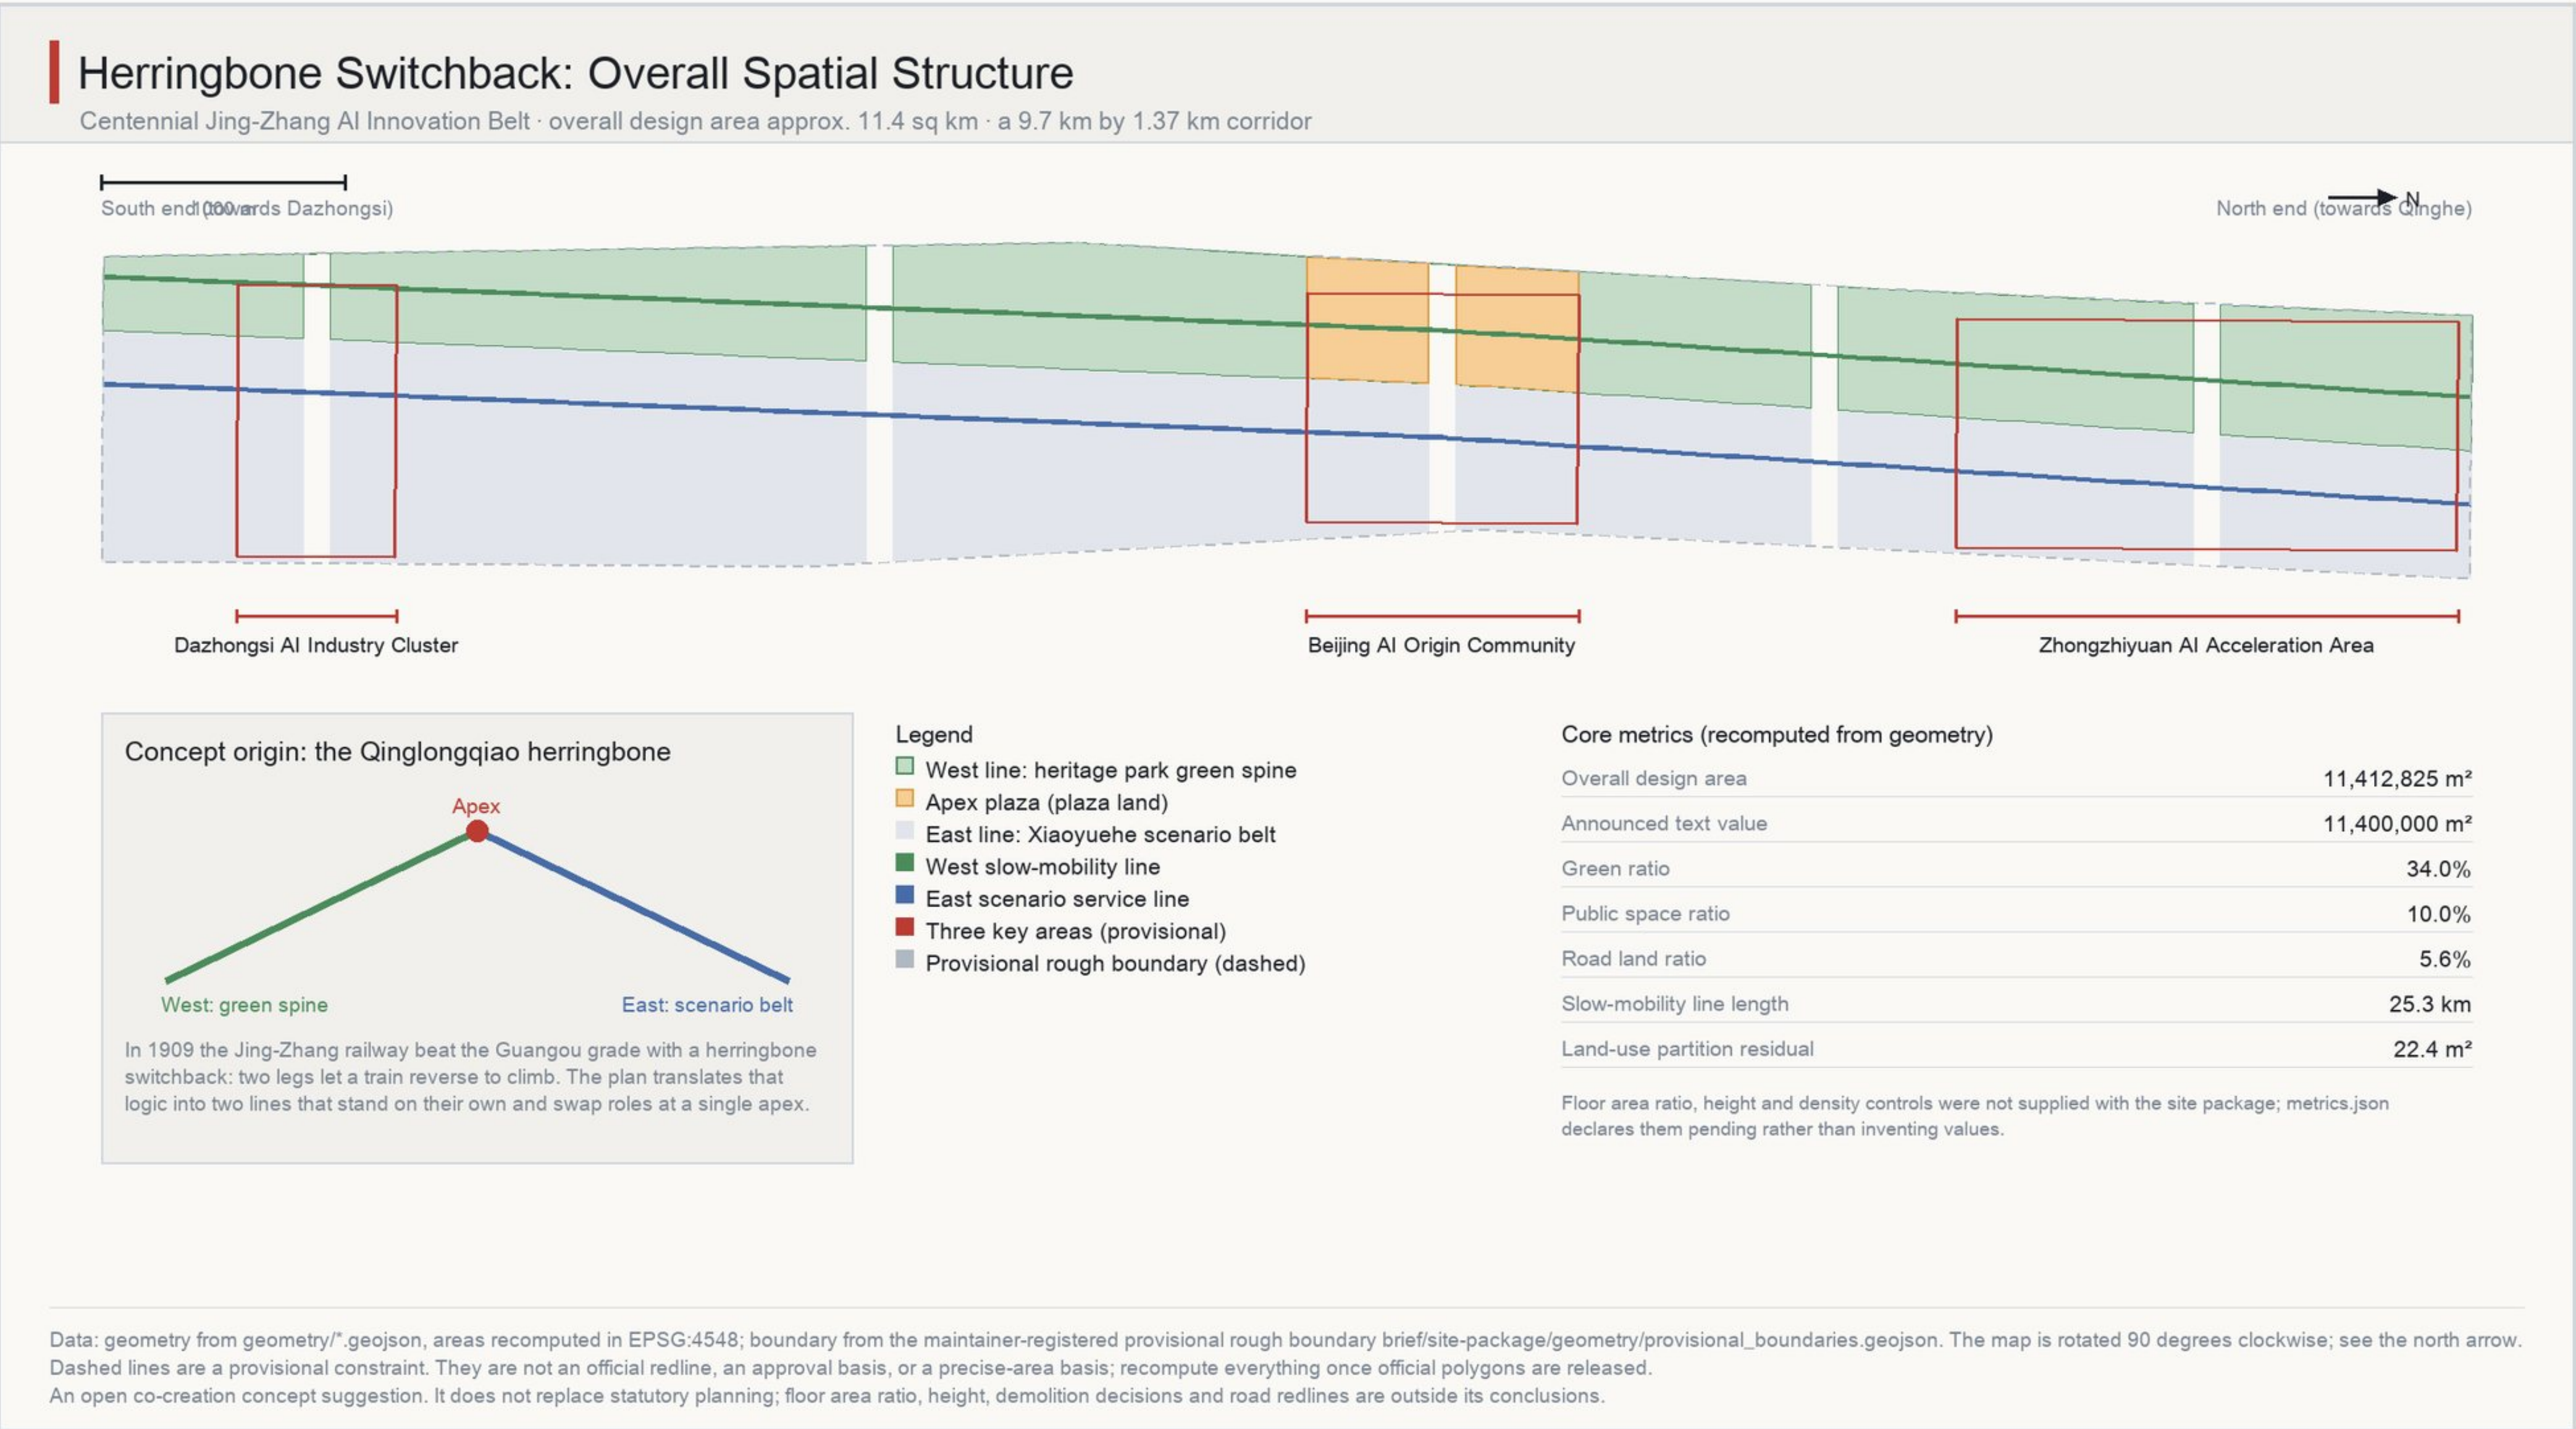

Key areas and the slow-mobility structure

Three areas and two wings / five stitch corridors / blue-green and public space

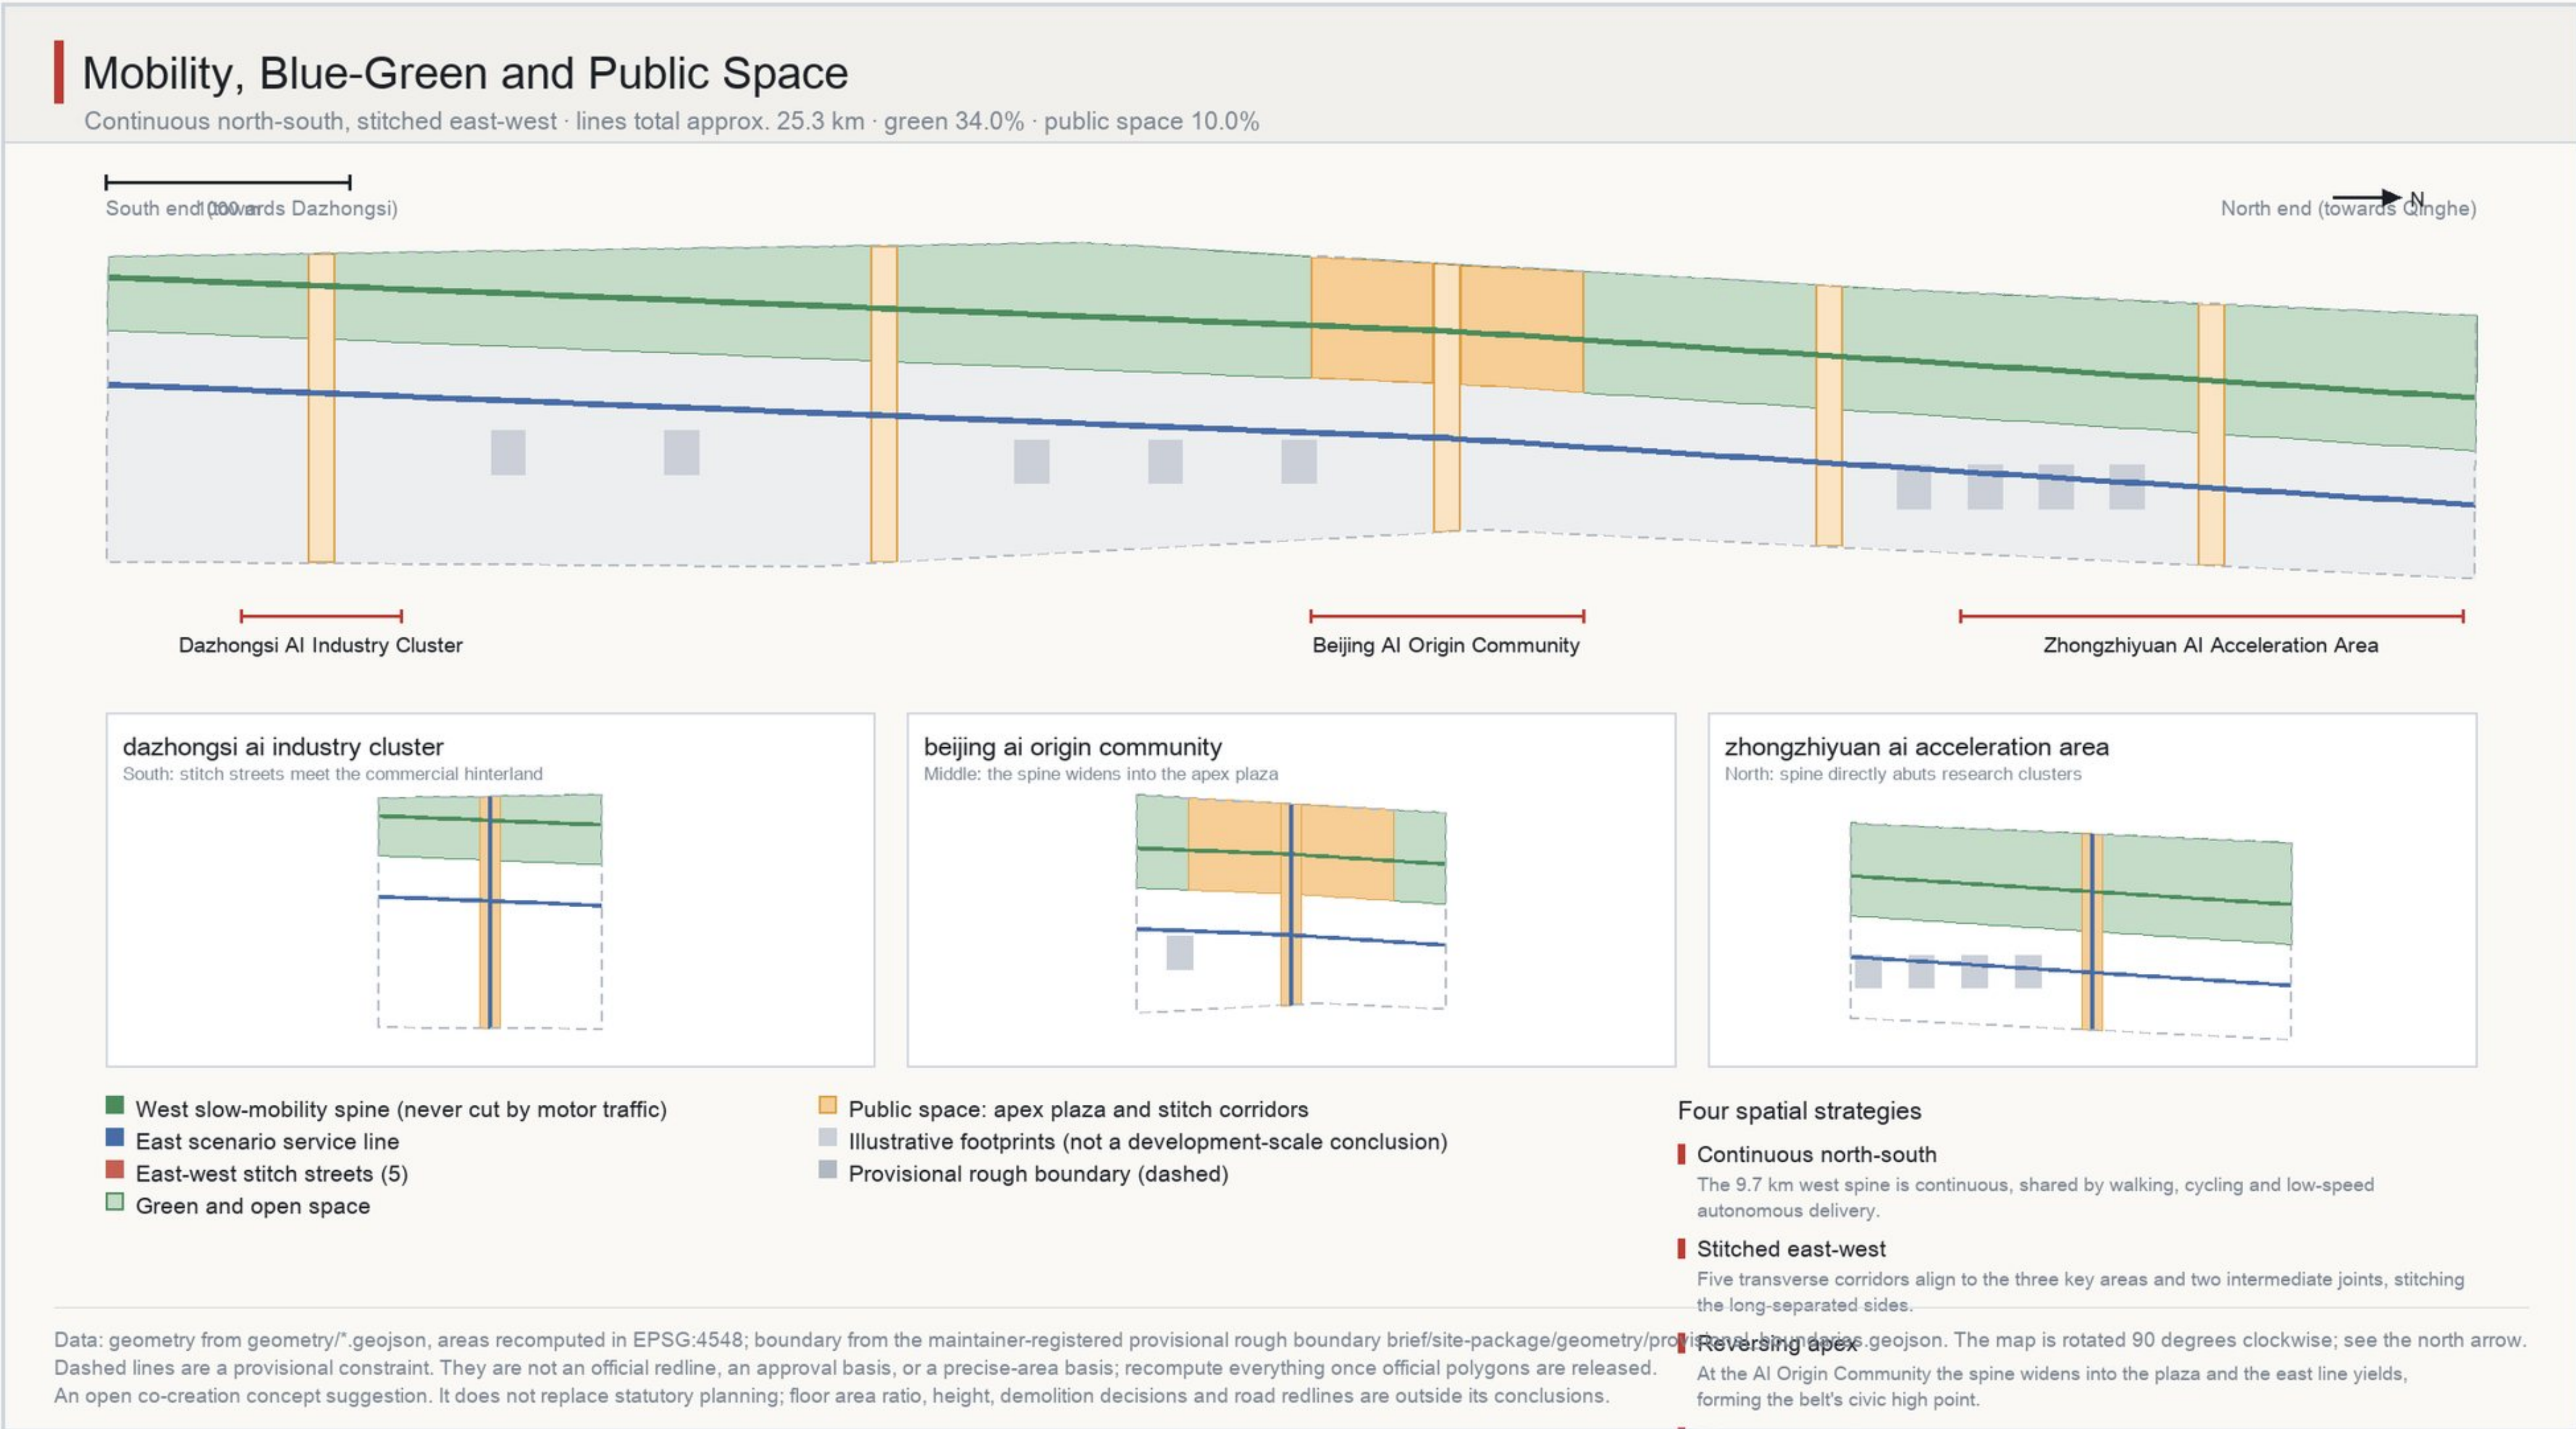

Three key areas and the three-areas-two-wings reversal

Mobility, blue-green and public space

Stitching before building

The two sides have long been separated by the corridor, so five transverse stitch corridors are proposed, aligned with the centres of the three key areas and two intermediate joints, producing a structure continuous north-south and stitched east-west. Renewal starts from public space and frontage; demolition is never the means of starting.

Continuity over width


The spine is compressed by research land in the north but never broken: a continuous 9.7 km linear green space in central Beijing is irreplaceable while local width is expendable. It is never cut by motor traffic.

Three pilgrimage landmarks


The apex marker on the plaza, the heritage mileage sequence along the whole spine, and the open-testbed observation deck in the north. All three sit at structurally necessary points, so their reason for existing comes from structure rather than shape.

Metrics and Evidence Chain

Every known metric is recomputed from geometry in EPSG:4548 and regenerates from scratch · missing statutory controls are declared pending

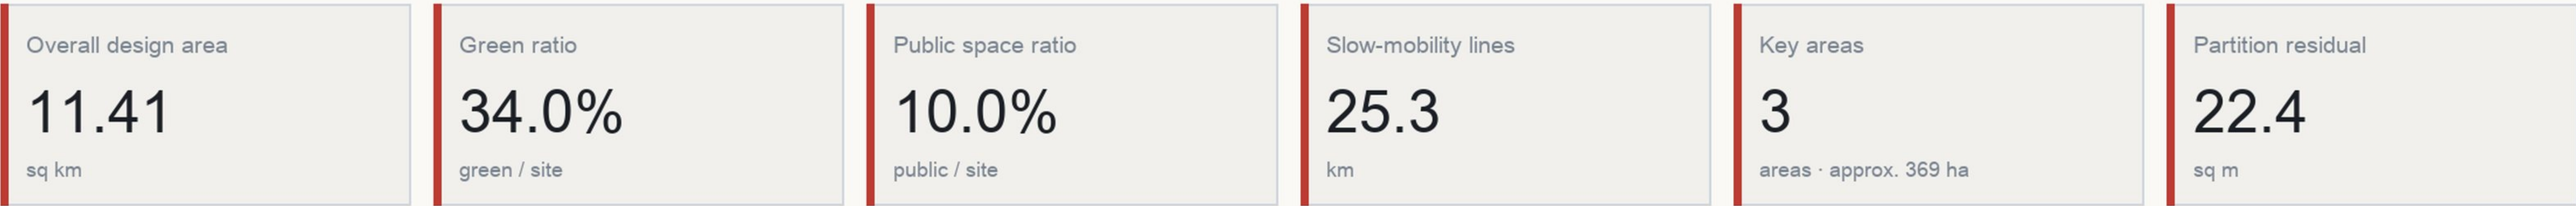

Land-use composition (hectares)

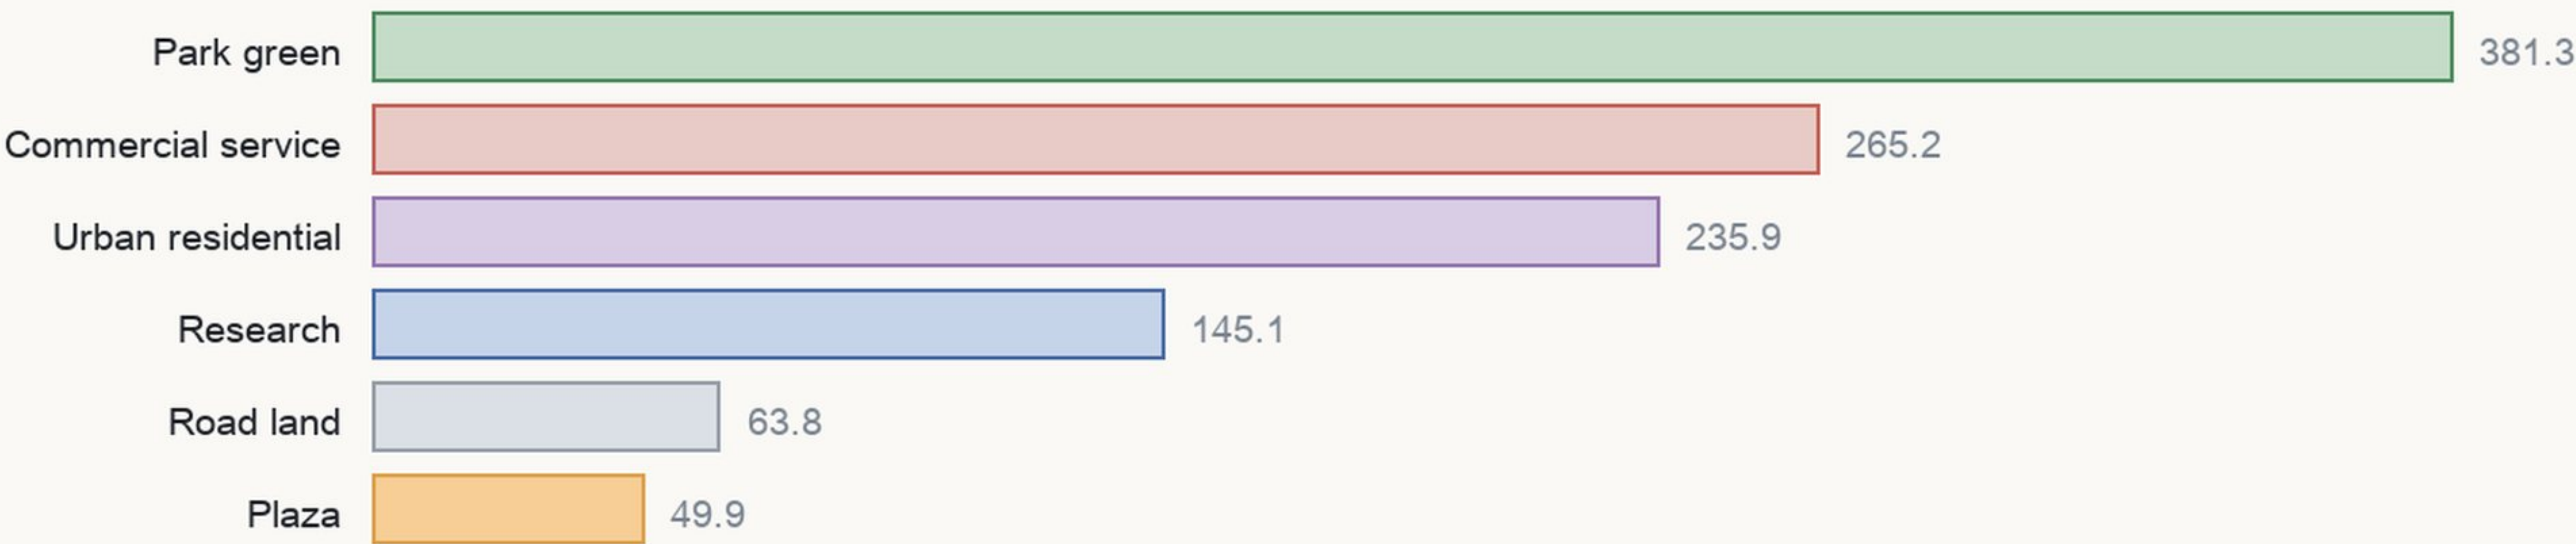

Evidence chain

- Provisional boundary (maintainer-registered)
- Complete land-use partition, shared edge coordinates
- Green / public / road / building / phasing layers
- Area recomputation in EPSG:4548
- metrics.json (30 known / 7 pending)
- Figures, report and visualisation share one source

Statutory controls pending official data (an agent does not conclude these)

- | | | | | | |
|---|-----------------------|--|-----------------------|---|-----------------------|
| ☐ Total floor area | pending official data | ☐ Floor area ratio | pending official data | ☐ Building height | pending official data |
| ☐ Green ratio control | pending official data | ☐ Building density control | pending official data | ☐ Setback requirement | pending official data |

Data: geometry from geometry/*.geojson, areas recomputed in EPSG:4548; boundary from the maintainer-registered provisional rough boundary brief/site-package/geometry/provisional_boundaries.geojson. The map is rotated 90 degrees clockwise; see the north arrow. Dashed lines are a provisional constraint. They are not an official redline, an approval basis, or a precise-area basis; recompute everything once official polygons are released. An open co-creation concept suggestion. It does not replace statutory planning; floor area ratio, height, demolition decisions and road redlines are outside its conclusions.

Core metric recalculation and evidence chain

Recomputable

All 30 known metrics are computed from geometry/*.geojson in EPSG:4548; delete metrics.json, rerun build/gen_metrics.py, and the numbers come back identical. Text, drawings and the offline exhibition read the same table.

Starting from the reversal point

Phasing covers 561.5 ha: phase one, 172.9 ha, in the middle engagement zone; phase two, 249.8 ha, north; phase three, 138.9 ha, south. Starting in the middle follows the construction order at Qinglongqiao: the reversal point is the link the structure cannot do without.

Explicitly refused claims

Floor area ratio, building height, density and setbacks have no official controls and are registered as status: unknown; parcel-level demolition decisions, road and rail alignment, bridge and tunnel works, municipal capacity, ownership and investment are all left unconcluded. Leaving these to bodies with statutory authority is precisely what makes this output usable.