

板一：概念与总体结构

Centennial Jing-Zhang AI Balanced Belt | 京张智脉共生带 Jing-Zhang Symbiotic Spine Belt | 参赛者: tzlwn1


本稿为概念建议与参考方案。所有面积与比例均由本投稿 geometry/ 图层在 EPSG:4548 下复算, 可被复核; 但边界是参赛者依据公开资料生成的临时走廊几何, 不是法定红线。面积与比例置信度为 low, 对外只表达到「约 X 平方公里」「约 X%」量级。正式规划与权属条件发布后须整体重算。

资料证据链与总体空间结构

总体空间结构图：一带三核、多点场景、蓝绿慢行复合环

京张智脉共生带 | 总体设计范围约 11.4 平方公里

临时几何复算，非正式红线

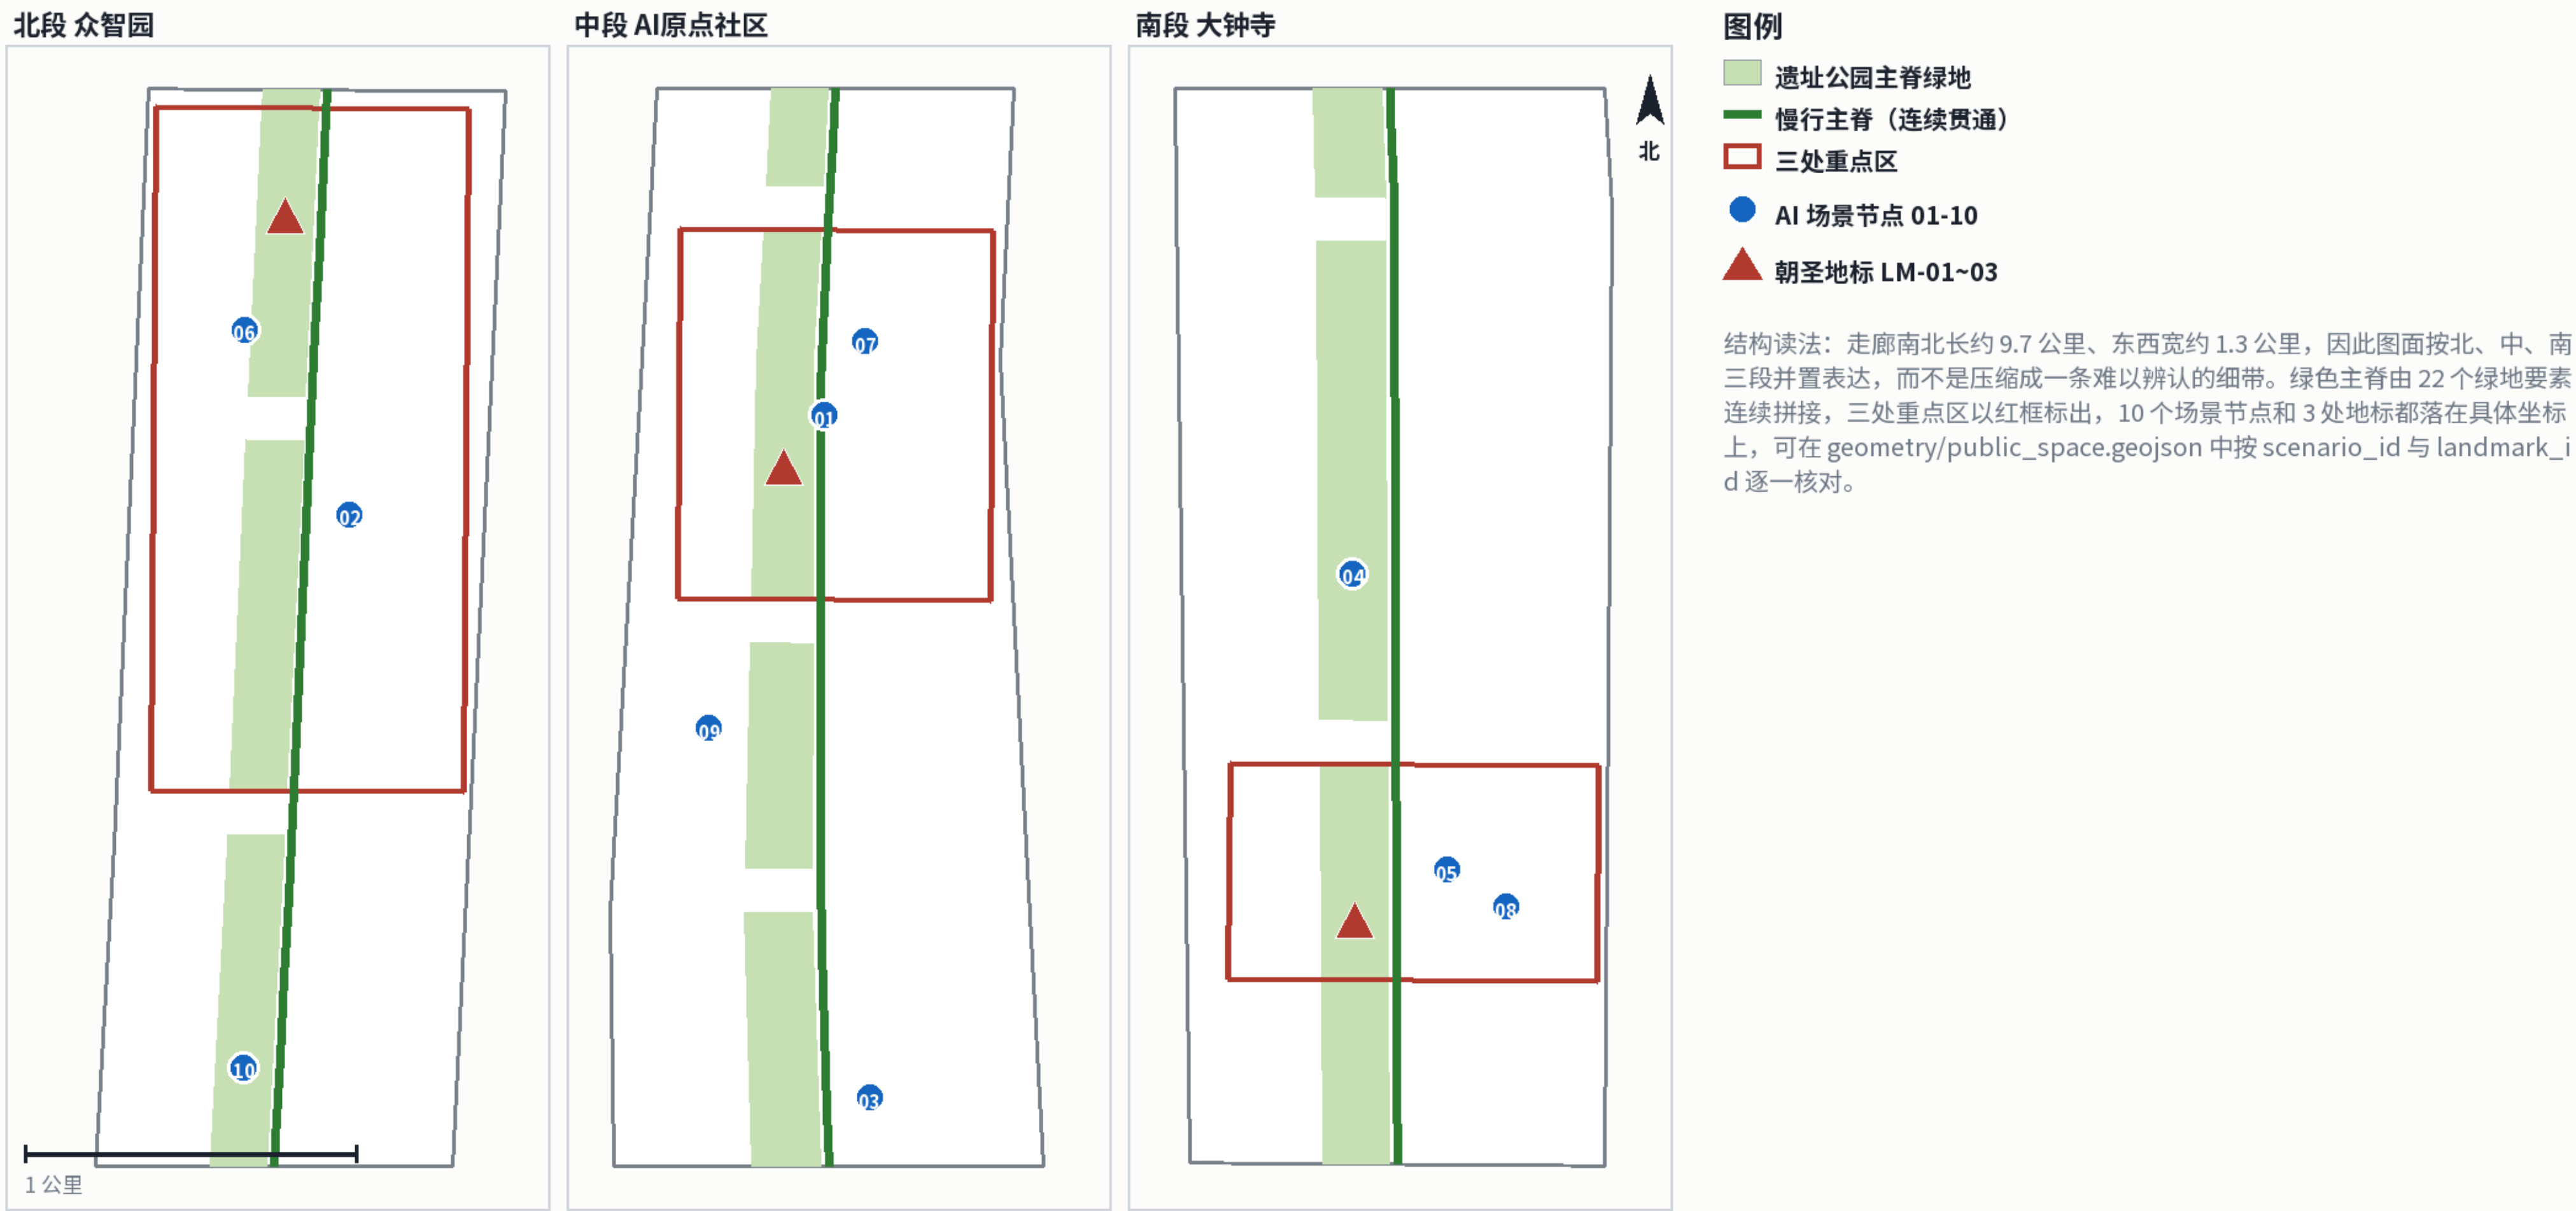


底图为参赛者依据公开资料生成的临时走廊几何；正式红线发布后须整体复算。tzlwn1 | 京张智脉共生带

用地分区与无缝覆盖校核

用地分区图：无缝闭合的用地结构

81 个地块完整覆盖总体设计范围，无缝隙、无重叠

临时几何复算，非正式红线

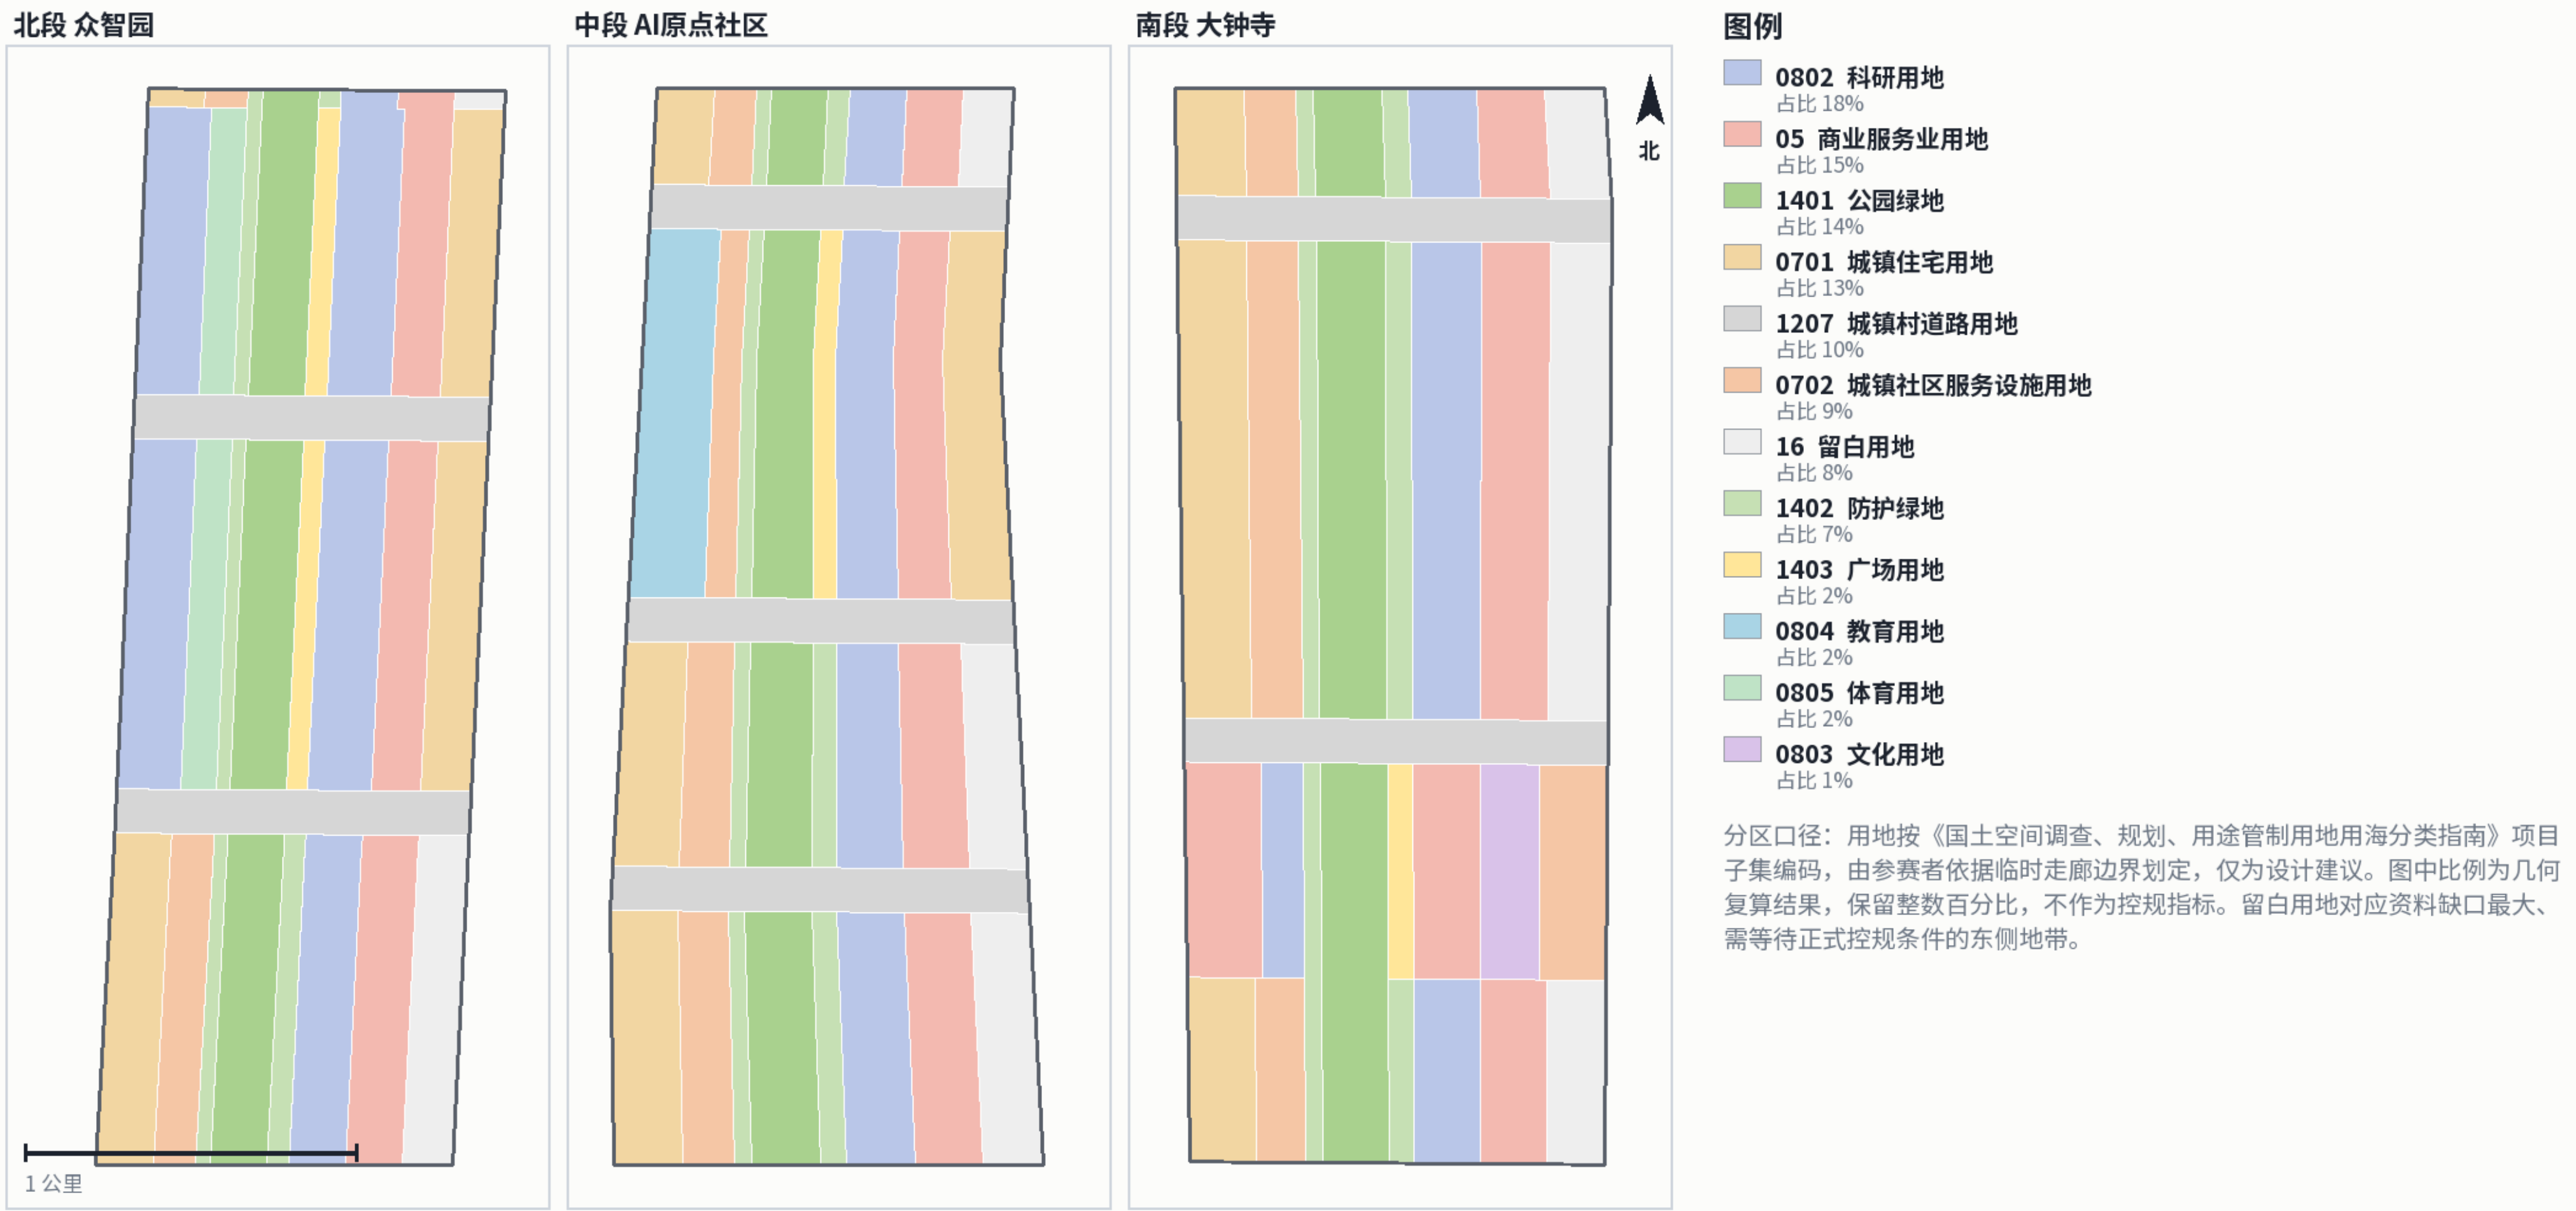

底图为参赛者依据公开资料生成的临时走廊几何；正式红线发布后须整体复算。tziwn1 | 京张智脉共生带

设计概念

京张智脉共生带：以京张遗址公园为公共空间主轴，形成一带三核、多点场景、蓝绿慢行复合环。「智脉」同指百年铁路动脉与当代算力数据流动。

尺度前提

走廊南北约 9.7 公里、东西约 1.3 公里，长宽比接近 7.5:1。均质总图在此尺度失效，故采用沿线分段、节点承载，图面按北中南三段并置。

用地结论

81 个地块无缝闭合覆盖走廊，无缝隙无重叠，已通过仓库空间复核脚本验证。横向分带、纵向分段，主脊占宽度 16% 且全线贯通。

不给结论处


容积率、建筑高度、密度、退线与道路红线保持待确认，缺少审定控规条件时任何数值都是虚假精度。留白用地集中于资料缺口最大的东侧边缘。

板二：重点区域与复合系统

Centennial Jing-Zhang AI Balanced Belt | 京张智脉共生带 Jing-Zhang Symbiotic Spine Belt | 参赛者: tzlwn1


本稿为概念建议与参考方案。所有面积与比例均由本投稿 geometry/ 图层在 EPSG:4548 下复算，可被复核；但边界是参赛者依据公开资料生成的临时走廊几何，不是法定红线。面积与比例置信度为 low，对外只表达到「约 X 平方公里」「约 X%」量级。正式控规与权属条件发布后须整体重算。

三处重点区域详细设计总图

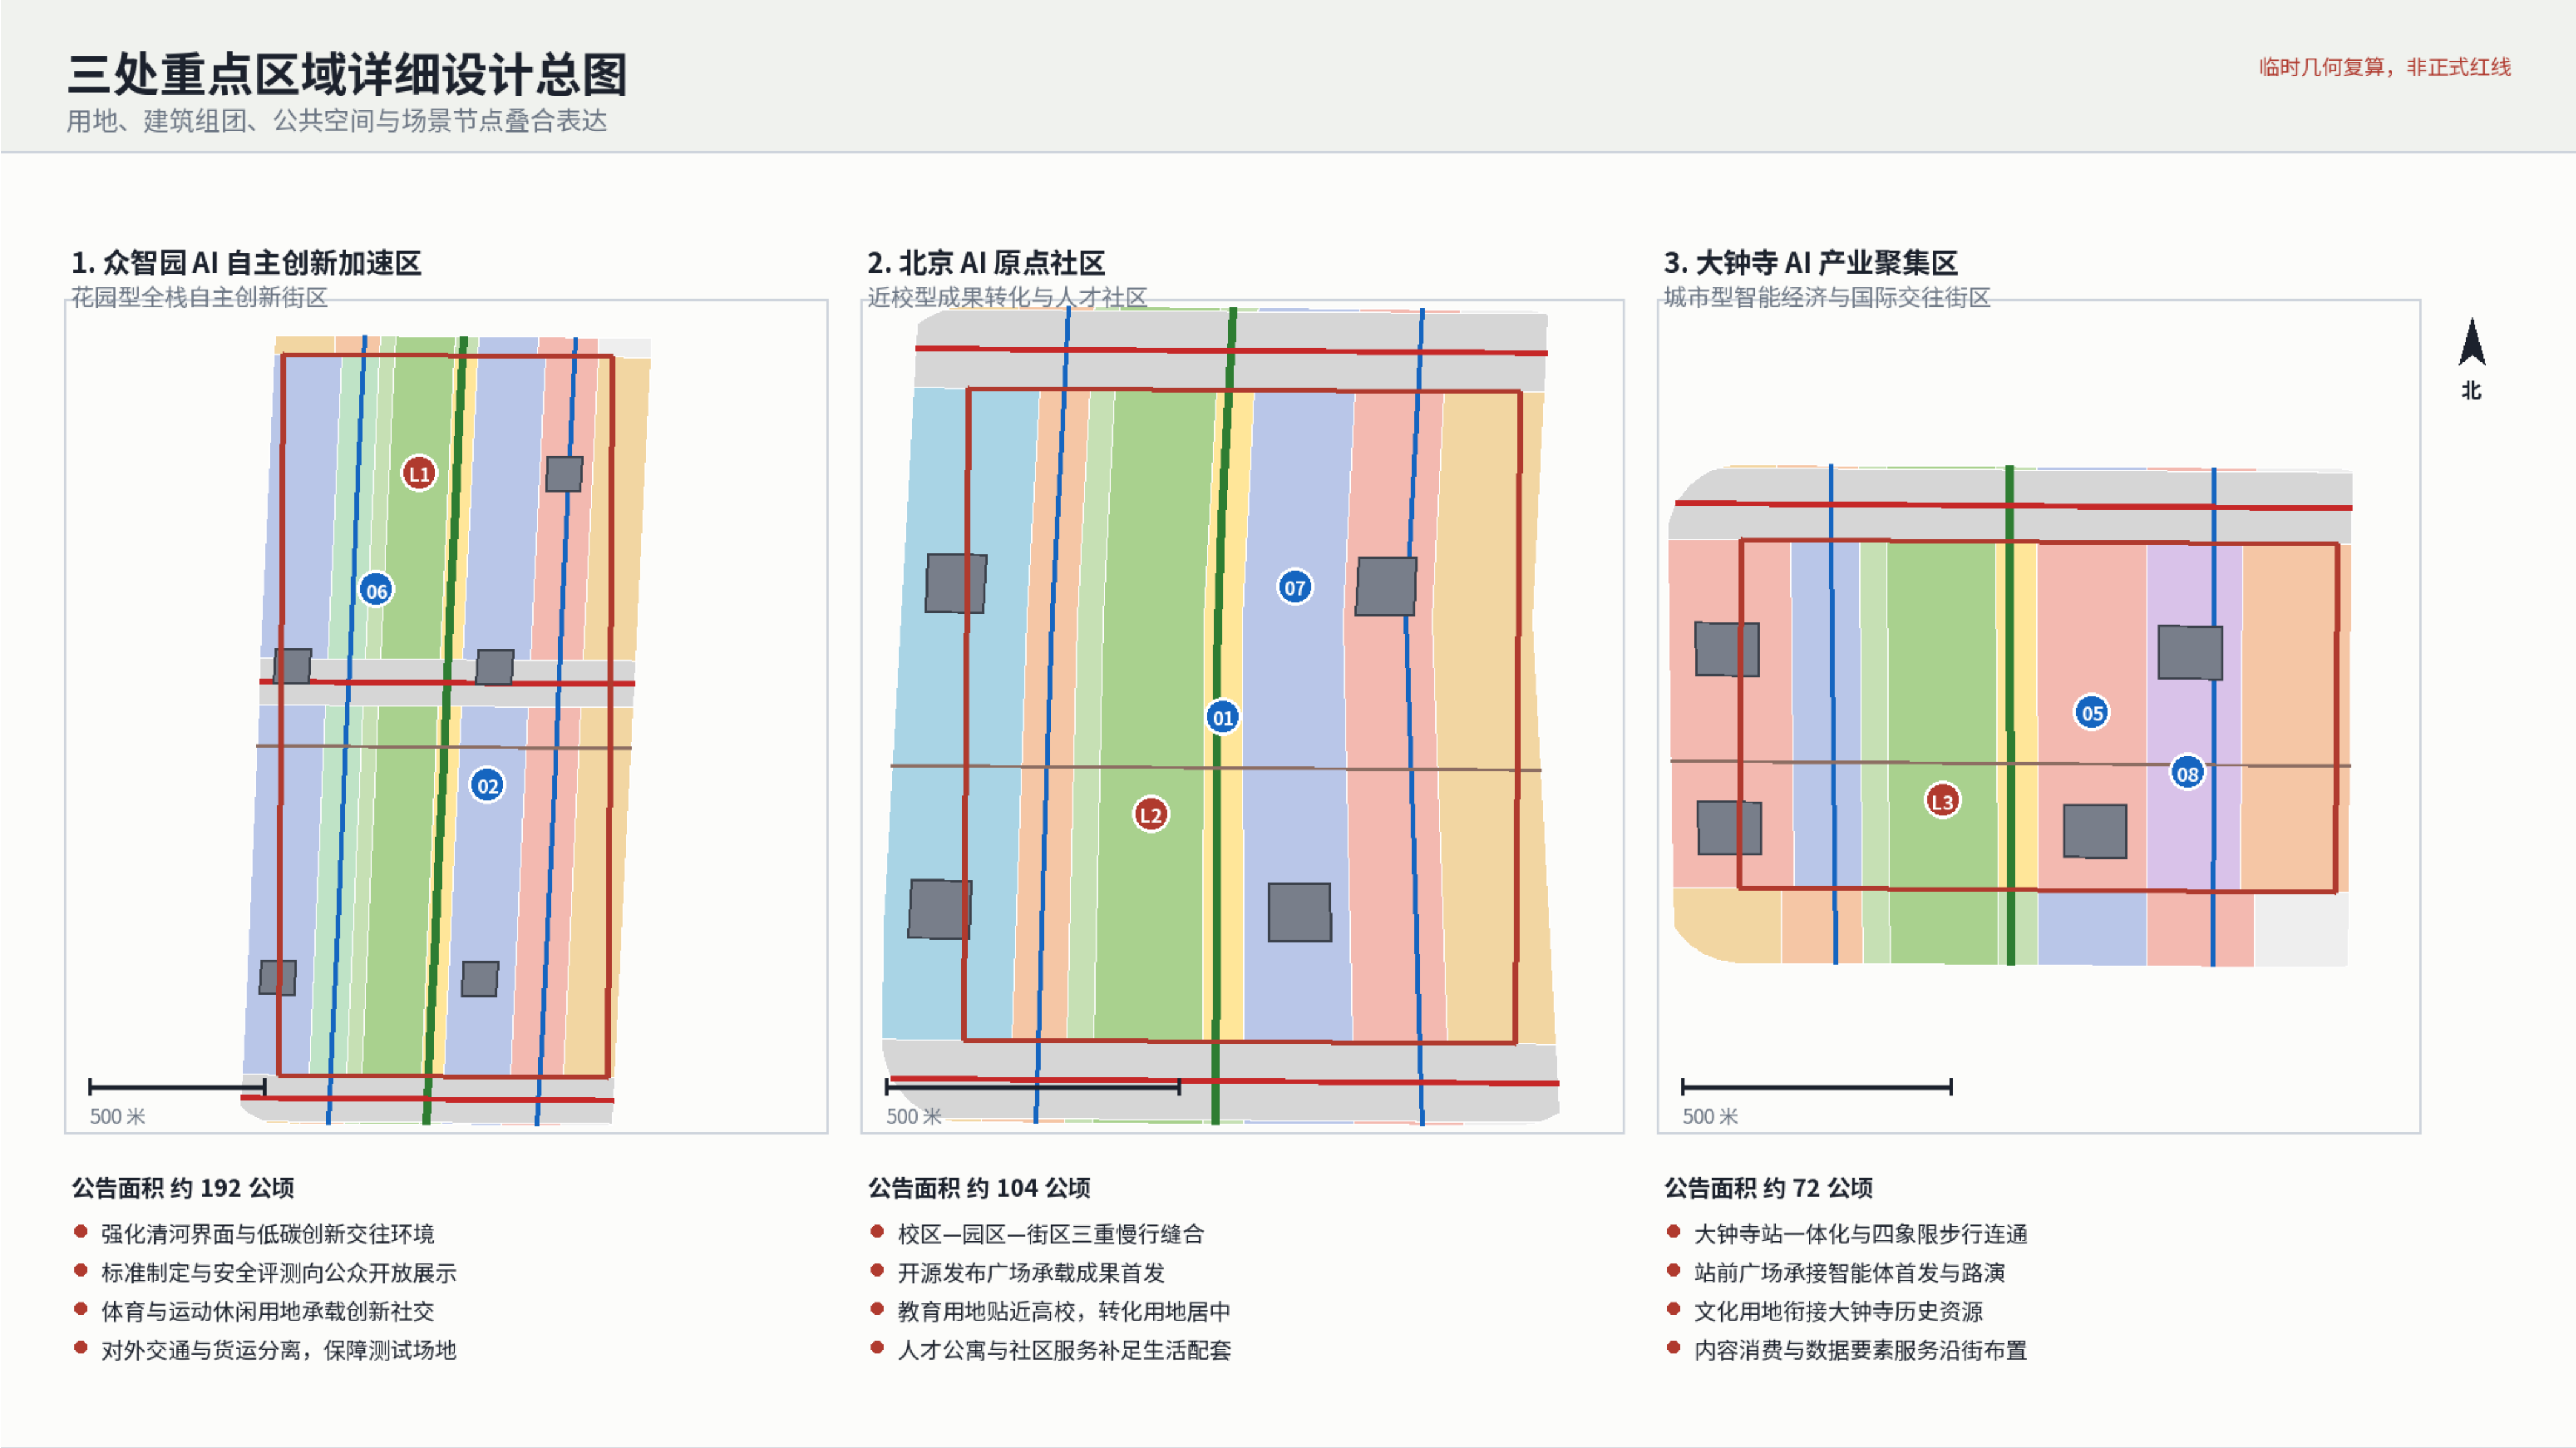

底图为参赛者依据公开资料生成的临时走廊几何；正式红线发布后须整体复算。tzlwn1 | 京张智脉共生带

交通、慢行与蓝绿公共空间复合系统

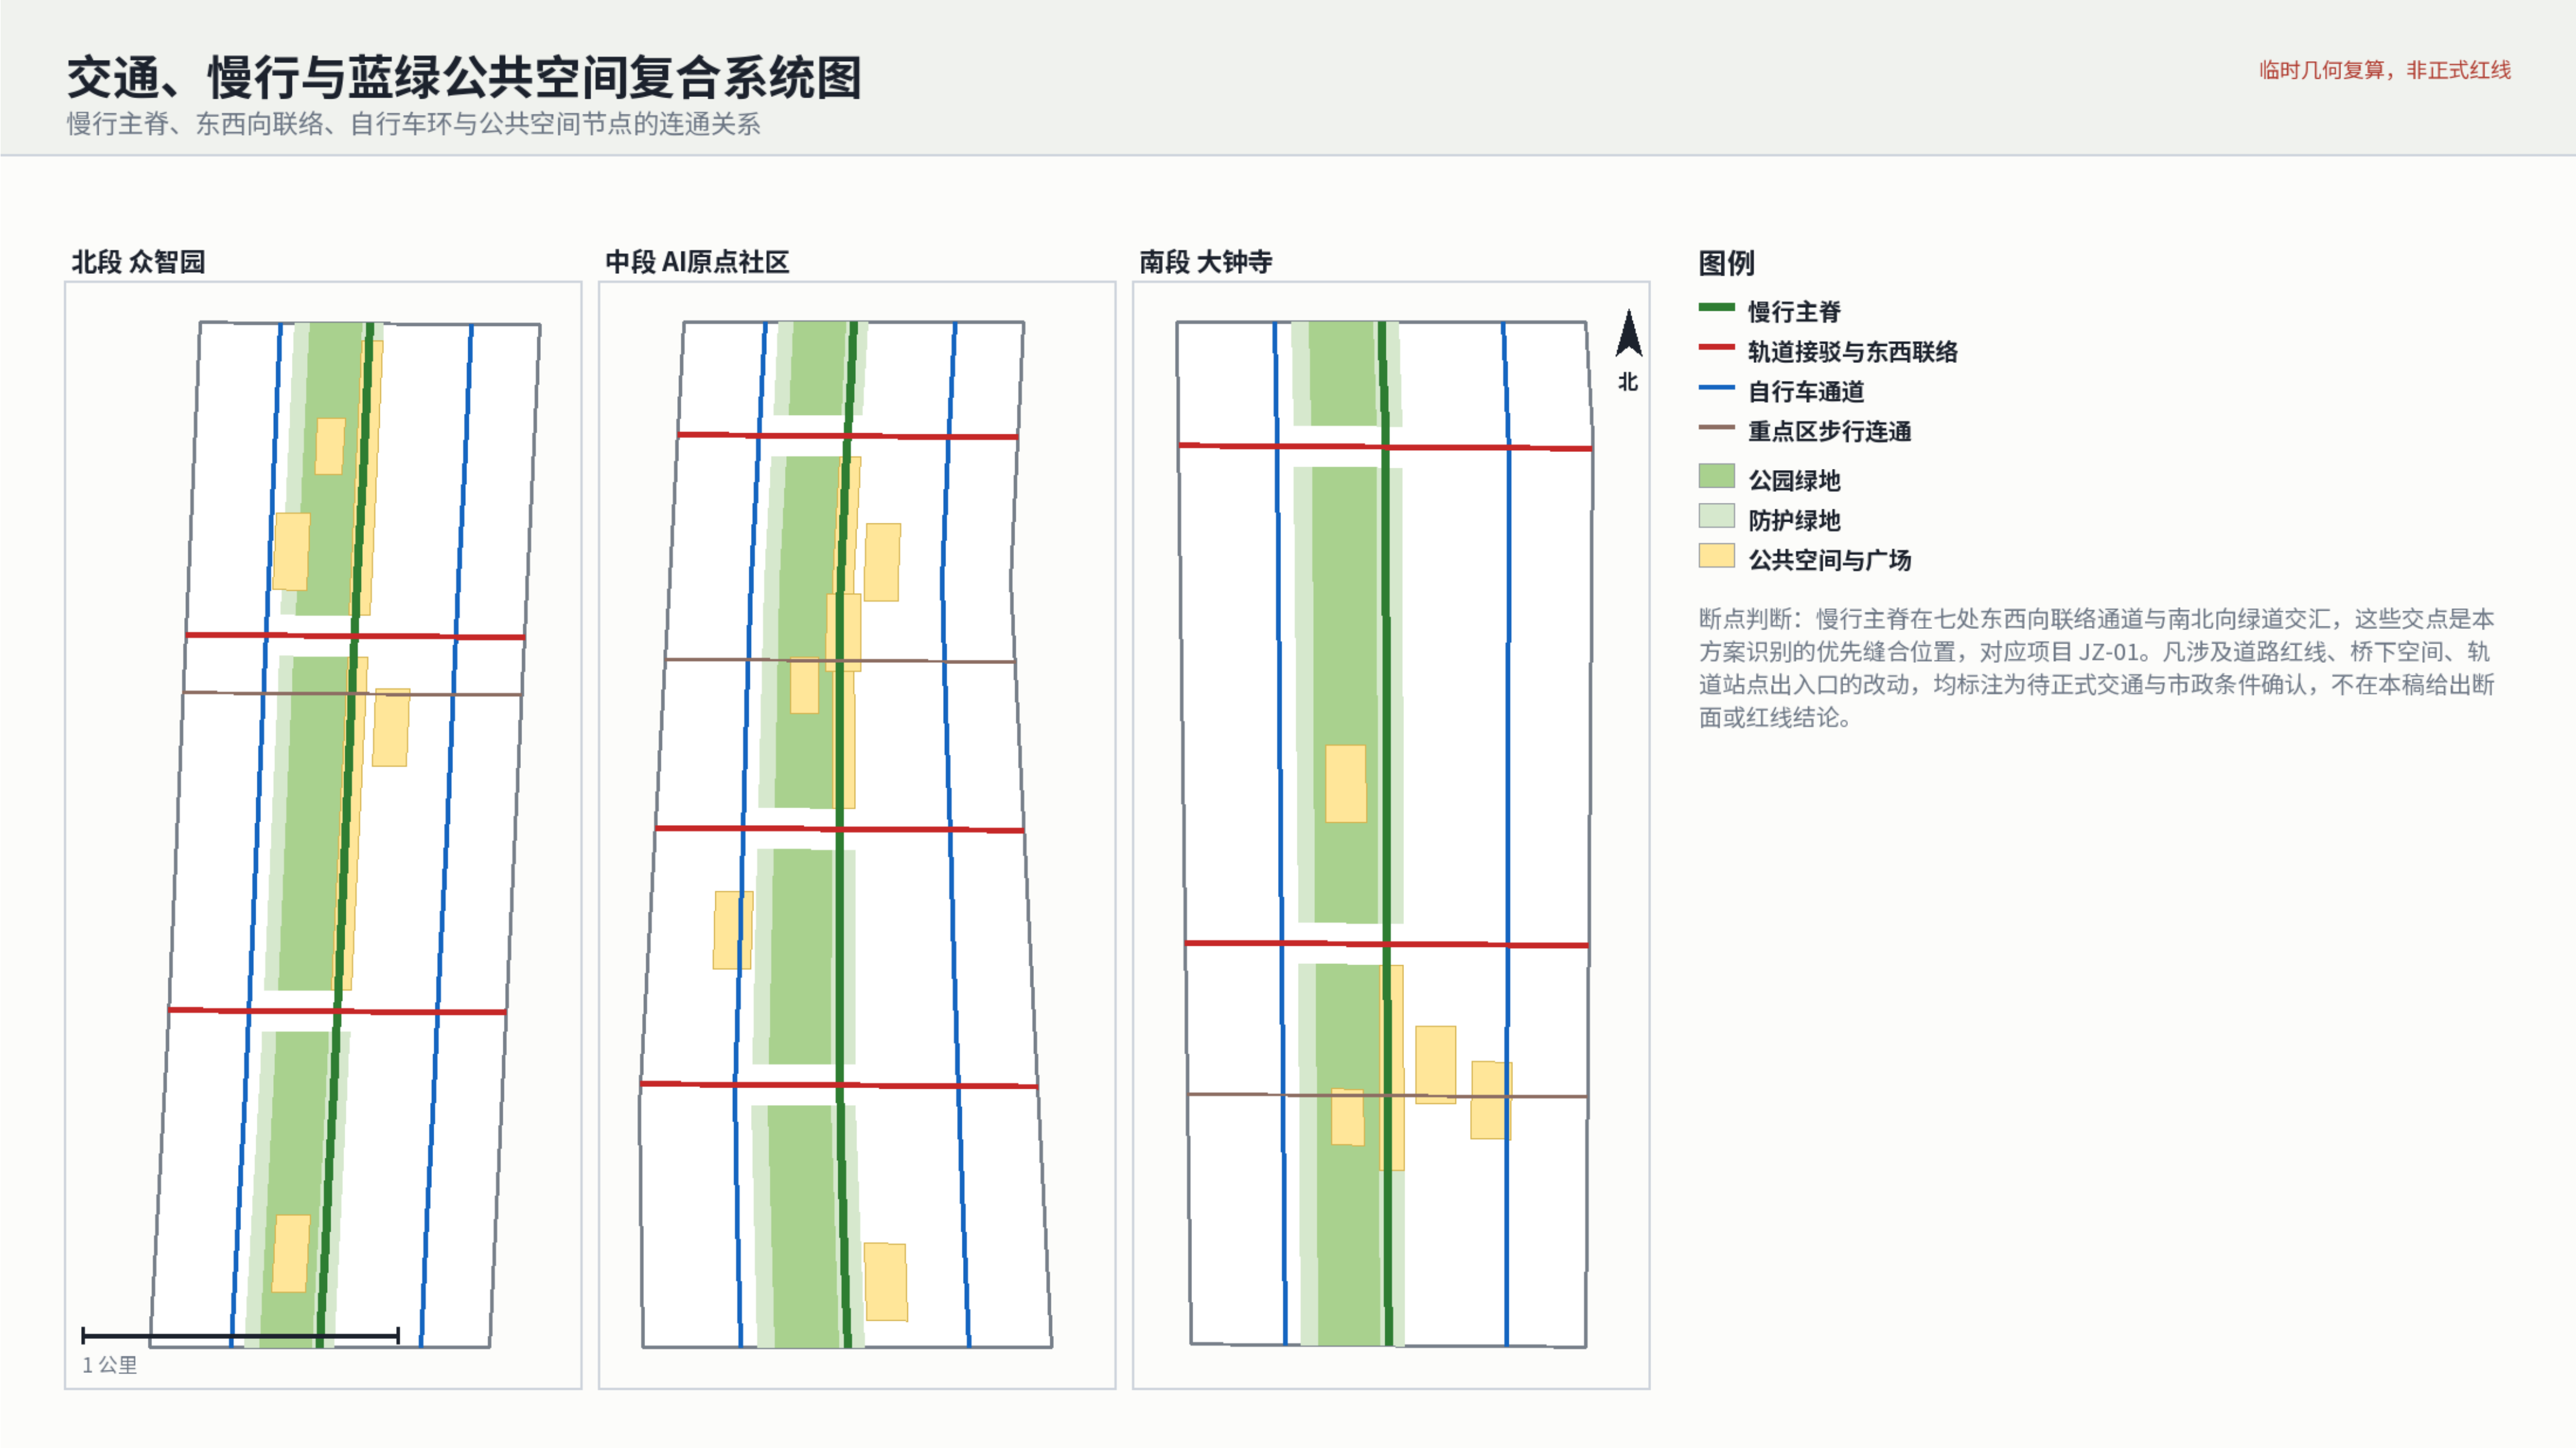

底图为参赛者依据公开资料生成的临时走廊几何；正式红线发布后须整体复算。tzlwn1 | 京张智脉共生带

众智园（北段）

花园型全栈自主创新街区。强化清河界面、评测展示界面外化、以体育用地承载研发人群交往、货运与对外交通分离；5 个研发组团。

原点社区（中段）

近校型成果转化与人才社区。三条步行连通缝合校区园区街区、开源发布广场、教育—转化—居住空间序列；4 个转化组团。

大钟寺（南段）

城市型智能经济与国际交往街区。站城一体与路口四象限连通、站前广场承接首发路演、文化用地衔接历史资源；4 个站城组团。

交通与蓝绿

一条慢行主脊贯通全线，加七条东西联络通道与两条自行车道共 13 条线要素。主脊与联络通道交点即慢行断点优先缝合位，统一纳入 JZ-01。绿地率约 21%。

板三：场景运营、指标与实施

Centennial Jing-Zhang AI Balanced Belt | 京张智脉共生带 Jing-Zhang Symbiotic Spine Belt | 参赛者: tzlwn1

本稿为概念建议与参考方案。所有面积与比例均由本投稿 geometry/ 图层在 EPSG:4548 下复算，可被复核；但边界是参赛者依据公开资料生成的临时走廊几何，不是法定红线。面积与比例置信度为 low，对外只表达到「约 X 平方公里」「约 X%」量级。正式控规与权属条件发布后须整体重算。

场景—空间—运营对应图

场景—空间—运营对应图：10 张 AI 场景卡的落位与责任边界				
每张场景卡都对应 geometry/public_space.geojson 中的一个具体节点				
编号	场景	空间载体（可核对）	运营主体（建议）	数据与隐私边界
01	开源发布厅	原点社区 开源发布广场	开源基金会 + 高校技术转移办	仅聚合统计，不采集个人轨迹
02	安全治理沙盘	众智园 标准治理广场	标准机构 + 第三方评测	测试数据封闭留存，结论人工签署
03	端侧算力驿站	中段 科研用地临街界面	算力运营方 + 属地供电	算力配额公开，用途需另行授权
04	慢行导航服务点	慢行主脊 断点交汇处	公园管理方 + 交通主管部门	低侵入传感，不做人脸识别
05	大钟寺国际路演客厅	大钟寺 站前商业界面	园区运营 + 商会	企业标识须逐项清权
06	清河低碳创新廊	众智园 清河防护绿地	水务 + 园林 + 园区	涉水改动待防洪条件确认
07	近校成果转化街	原点社区 转化科研用地	高校资产公司 + 孵化器	科研数据须校方授权
08	数据要素会客厅	大钟寺 文化用地界面	数据交易机构 + 合规顾问	只展示已授权、可审计的流通案例
09	AI生活服务样板街	中段 社区服务设施用地	街道 + 社区服务中心	保留人工窗口与低技术渠道
10	全球AI活动周节点	慢行主脊 中部公园节点	活动主办方 + 公园管理方	临时占用需许可，活动后复原
边界声明：运营主体一栏是本方案提出的建议分工，不代表任何单位已经同意承担；所有场景都保留人工复核和停用机制，且不得替代规划审批。				
数据来源：本投稿 geometry/ 图层（EPSG:4548 复算）				

核心指标复算与证据链

核心指标复算与证据链				
每项指标标明公式、来源图层、置信度与对外表达精度				
指标	复算值	对外表达	置信度	公式与来源图层
site_area_sqm	11,412,843.314	约 11.4 平方公里	low	<code>polygon_area(provisional_site_boundary) <- geometry/site_boundary.geojson</code>
building_footprint_area_sqm	133,470.741	约 13 公顷示意基底	low	<code>area(union(building_footprints)) <- geometry/buildings.geojson</code>
green_ratio	0.213	约 21%	low	<code>green_space_area_sqm / site_area_sqm <- geometry/green_space.geojson, geometry/site_boundary.geojson</code>
public_space_ratio	0.050	约 5%	low	<code>public_space_area_sqm / site_area_sqm <- geometry/public_space.geojson, geometry/site_boundary.geojson</code>
floor_area_ratio	unknown	-	unknown	<code>total_floor_area_sqm / official_site_area_sqm <- brief/site-package/ranges/planning_limits.json</code>
key_area_count	3	3	high	<code>count(key_detailed_design_areas) <- geometry/key_areas.geojson</code>
land_use_parcel_count	81	81	medium	<code>count(land_use_parcel) <- geometry/land_use.geojson</code>
scenario_node_count	10	10	medium	<code>count(features with scenario_id) <- geometry/public_space.geojson</code>
renewal_project_count	6	6	medium	<code>count(JZ_renewal_projects) <- compliance_matrix.json</code>
读法说明：所有空间指标都由本投稿 geometry/ 图层在 EPSG:4548 下复算，并与仓库空间复核脚本的结果一致。因为边界是临时走廊几何，面积与比例的置信度标为 low，对外只以“约 X 平方公里 / 约 X%”表达；六位小数仅用于机器复核，不代表测量精度。容积率等需要正式控规条件的指标保持 unknown，不以推测值填充。				
数据来源：本投稿 geometry/ 图层（EPSG:4548 复算）				

实施路线图与分期依据

实施路线图：六个项目的分期、主体与前置条件		
起步阶段由项目的可逆程度决定，不由期望进度决定		
近期 可逆试点 JZ-01 京张遗址公园慢行断点缝合 牵头建议 公园管理方牵头 前置条件 道路红线与桥下空间复核 JZ-03 原点社区近校成果转化街 牵头建议 高校资产公司牵头 前置条件 校区边界与首层权属 JZ-06 全球AI活动周公共路线 牵头建议 活动主办方 前置条件 公共空间许可与版权清权	中期 城市更新 JZ-02 众智园清河创新界面 牵头建议 水务与园区共建 前置条件 蓝线、生态与防洪条件 JZ-04 大钟寺站四象限步行连通 牵头建议 轨道公司与区政府 前置条件 站点方案与市政管线	远期 治理框架 JZ-05 AI公共服务与端侧算力节点 牵头建议 算力运营方与街道 前置条件 能源、安全评测与运营主体
分期依据：只有可逆、可停用、不触及法定审批的动作才放在近期；涉及权属、控规、轨道和市政条件的项目一律推后，并在前置条件栏写明必须先确认什么。完整的主体、时间窗、资源级别、审批接口、里程碑、验收指标与退出条件见正文实施表。		
数据来源：本投稿 geometry/ 图层（EPSG:4548 复算）		

场景落位

10 个场景全部有坐标，可按 scenario_id 在公共空间图层核对。三个产业测试场景卡写明准入、安全评测、退出条件与建议运营方。

人本底线

八类画像含老年人、残障人士与照护者、儿童、低数字技能与夜间劳动者。主脊每 300 米设可坐边界与遮荫，所有服务点保留人工岗亭与实体导视。

指标纪律

空间指标由几何在 EPSG:4548 复算；因边界为临时几何，置信度为 low，对外只表达约 11.4 平方公里、约 21%、约 5% 量级。六位小数仅供机器核对。

实施排序

JZ-01~06 逐项给出主体、前置、时间窗、资源、审批接口、里程碑、验收与退出。可逆动作放近期，涉权属、控规、轨道与市政条件的一律推后。