


JZ-1909 AI Belt

Overall proposal — One Rail, Two Rivers, Three Stations • Six Axes, Multiple Nodes

Overview map · land-use structure and design elements (north points right)

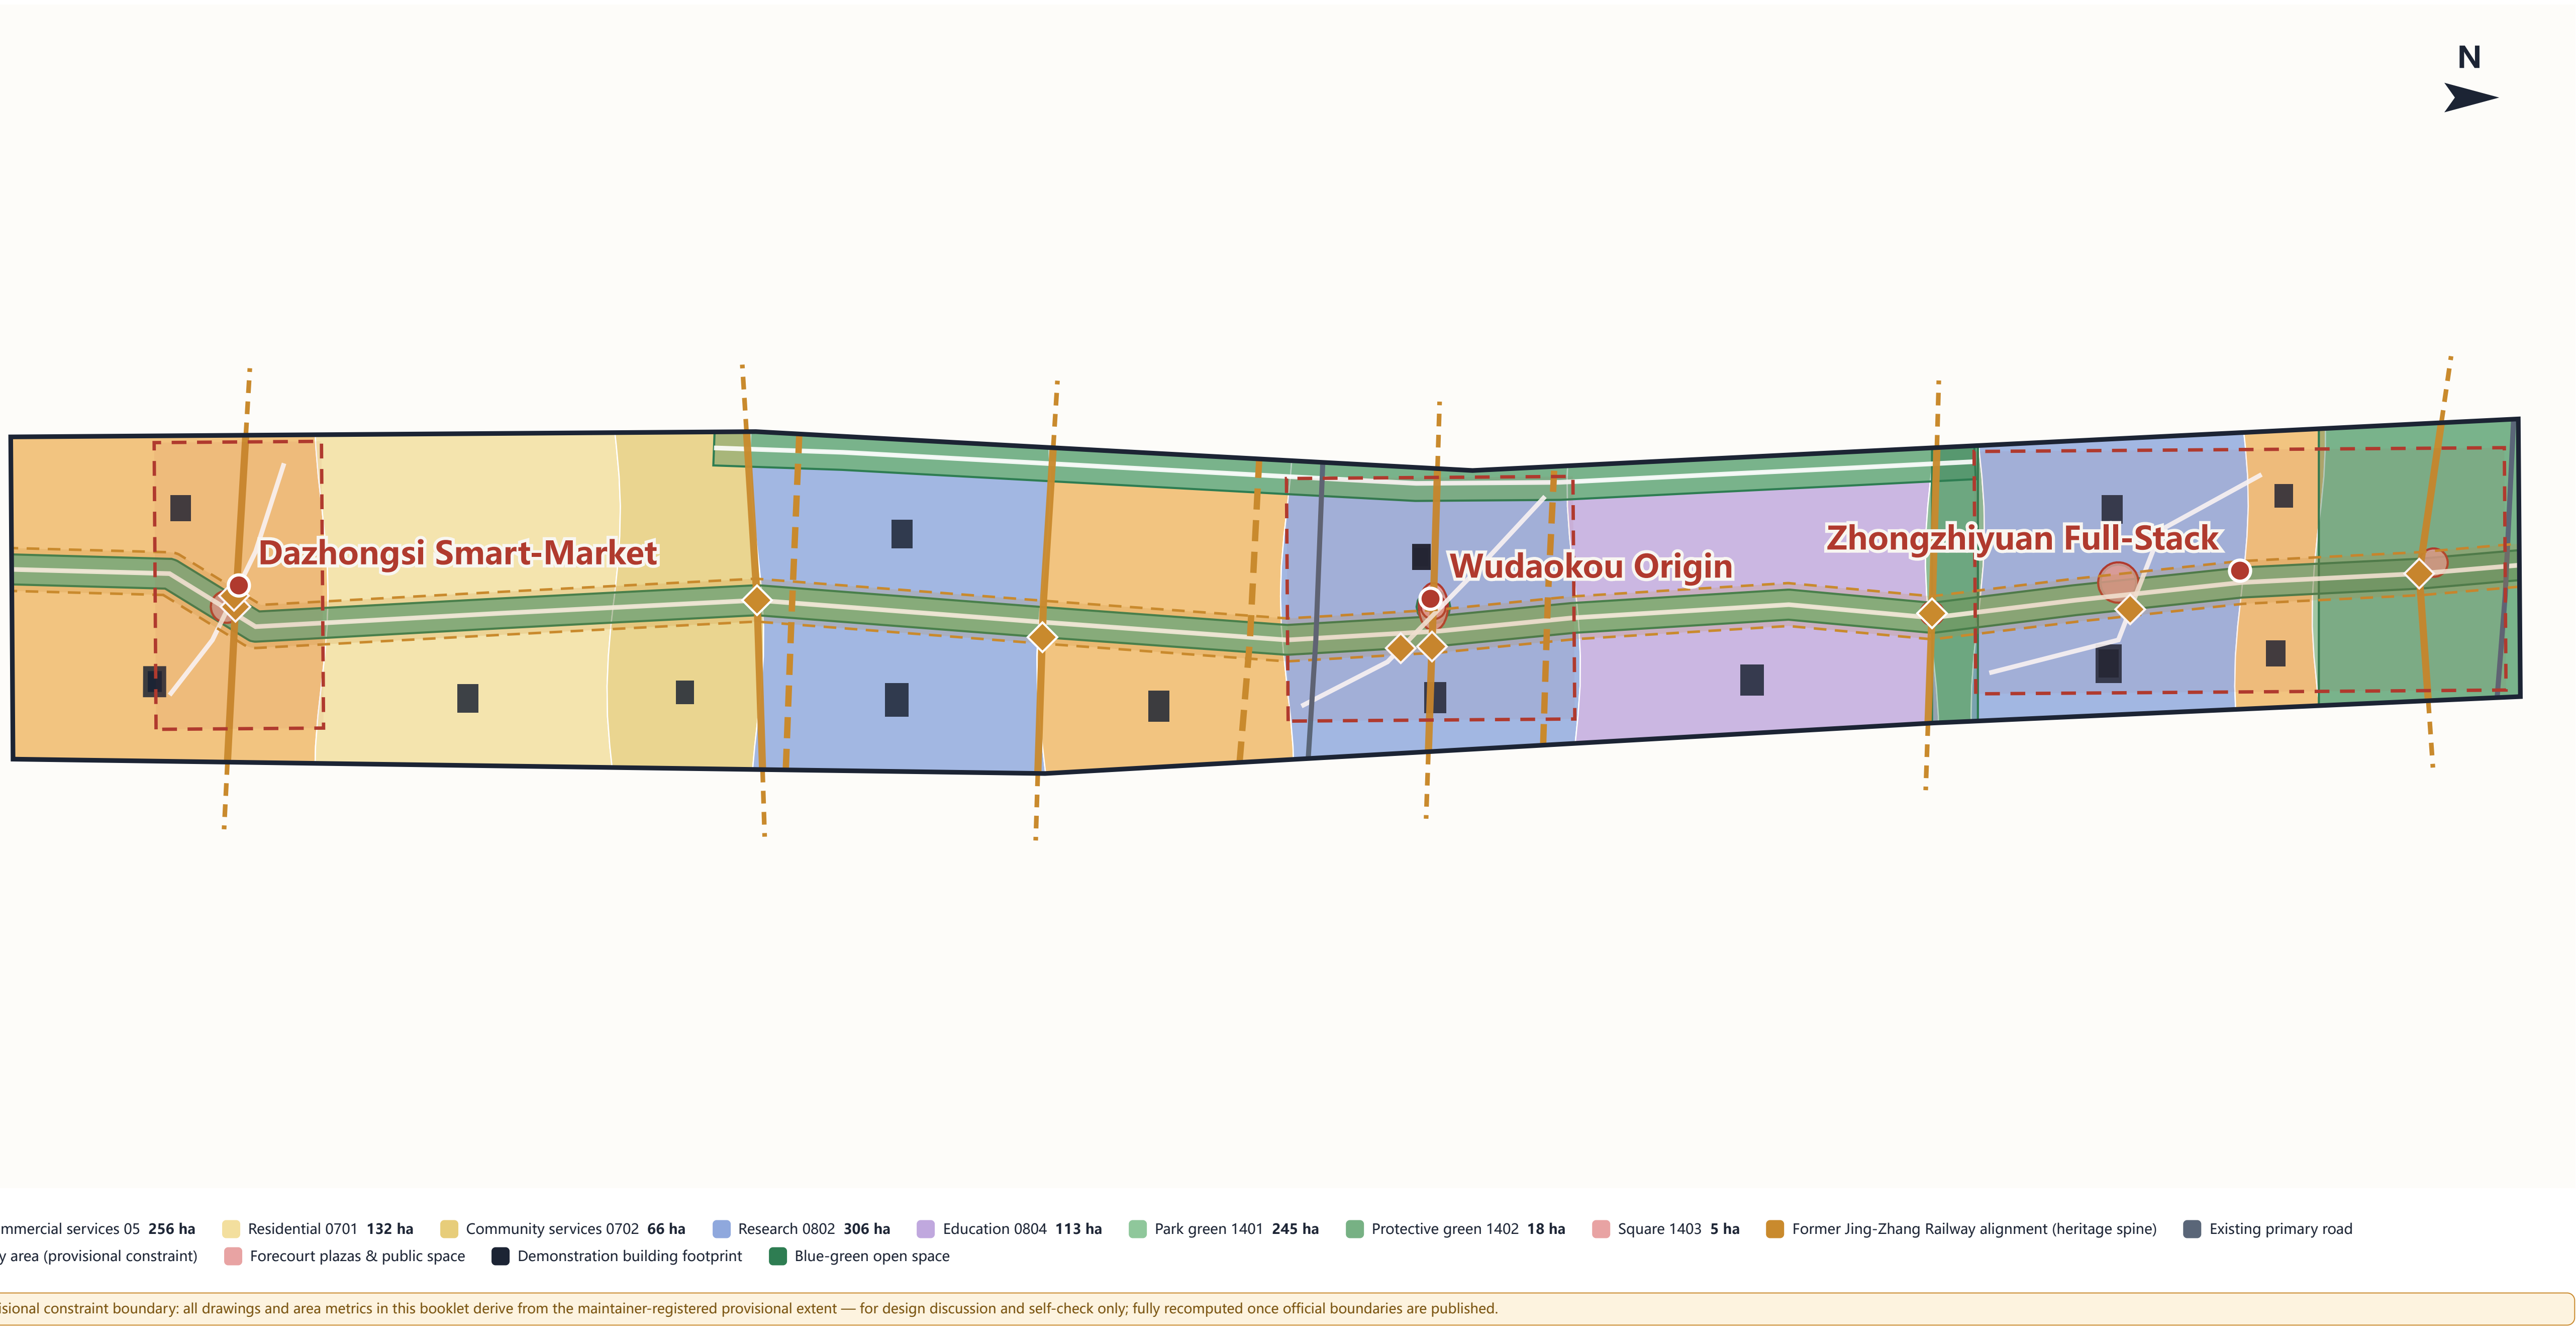

One Rail

Jing-Zhang heritage slow-mobility spine: a ≈9.8 km, ≈116 m-wide heritage park ridge along the 1909 alignment, combining walking, cultural display and AI scenarios (core segment of the plan's 'belt').

Two Rivers

Qinghe riverside living room (≈83.4 ha waterfront at the north) × Xiaoyue River scenario-connection corridor (in-site segment ≈62 m inside the east edge; the river channel itself runs outside the site) — linking the plan's 'three belts'.

Three Stations

Dazhongsì AI Market, Wudaokou AI Origin and Zhongzhiyuan Full-Stack as relay switch points (AI Market and AI Origin carry the plan's 'two centers'); the Two Wings (Zhongguancun tech-services westward, Xiaoyue scenario eastward) diverge at Wudaokou and converge at Zhongzhiyuan — the two strokes of 人.

Six Axes • Nodes

Six east-west stitch axes (Dazhongsì / Xueyuan Rd / Zhichun Rd / Wudaokou / Ring-5 / Qinghe) answer the plan's 'N-S continuity, E-W connection'; 9 switch plazas at 18 corridor crossings of 9 transverse lines, one point per line, match the plan's 'multiple nodes'.

Key metrics

≈ 1,141.3 ha

Overall design area

Announcement ≈ 11.4 sqkm; provisional recompute matches

23.5%

Green ratio (recomputed)

green_space layer union / submitted area; calibers reconciled in the proposal

≈ 9.8 km

Heritage rail slow-mobility spine

Links three stations and all cultural nodes

63

Land-use parcels

Planar partition from shared cut lines; seamless full coverage

19

Demonstration renewal buildings

8 new - 9 converted - 2 retained; demolition pending survey

3 / ≈ 368.4 ha

Key areas

Zhongzhiyuan - AI Origin - Dazhongsì (provisional)

Phasing

Phase 1

≈ 748.9 ha

Three-station opening districts and spine demonstration segment

Phase 2

≈ 167.6 ha

Origin Community depth and Qinghe waterfront; Zhongzhiyuan concept pilot starts

Phase 3

≈ 224.7 ha

Zhongzhiyuan full-stack district and two-river living rooms completed

JZ-1909 AI Belt

Evidence & operations — verifiable, auditable, iterable

AI+ scenario system			
No.	Scenario	Carrier	Summary
01	AI slow-mobility navigation	Entire heritage spine	Explainable wayfinding and low-intrusion sensing identify walking breaks and crowding; output remains human-reviewable
02	Enterprise-service Copilot	Service posts at three stations	Policy retrieval, space matching and application guidance with sources and confidence attached
03	Public-safety and event-operations review	Forecourt plazas	Aggregate-only crowd and event-risk alerts; decisions remain human
04	Low-speed robot delivery test	Origin Community local streets	Route-limited, speed-limited, reversible delivery pilot with tiered data opening
05	AI cultural guide	1909 memory route	Multilingual narration of Jing-Zhang Railway and Zhongguancun innovation history, fact-checked
06	AI health-service navigation	Community service nodes	Connects nearby health resources without diagnostic conclusions; medical and other listed public-service venues keep on-site guidance and human-operated channels, with traditional and smart services running in parallel per State Council Document 2020 No.45 as policy background (its phased goals have expired; referenced for scenario design only)
07	Safety-governance sandbox (test)	Zhongzhiyuan laboratory	Visit-able, bookable and auditable node for standards, trusted evaluation and red-team testing
08	Edge-compute posts (test)	Public service points at three stations	New-infrastructure prototype fusing distributed compute and low-carbon energy, for professional deepening
09	Open-source release hall	Origin Station plaza	Achievement release, code-contribution display and small roadshows
10	Low-carbon operations monitoring (test)	Qinghe riverside living room	Stormwater, energy and carbon monitoring with public metric definitions
11	Data-element reception hall	Dazhongsi' district	A compliant, authorized and auditable urban interface for data circulation
12	1909 global AI week route	Belt-wide public spaces	Annual operations mix of developer festival, scenario open days and pilgrimage route

Recomputed metrics	
Submitted area	1,141.3 ha
Blue-green open space	267.9 ha
Blue-green share	23.5%
Public space area	6.3 ha
Public space share	0.6%
Demonstration footprint	13.0 ha
Demonstration footprint share (design)	1.1%
Road centerline length	25,471 m
Heritage spine length	9,800 m
Phase 1 area	748.9 ha
Phase 2 area	167.6 ha
Phase 3 area	224.7 ha
Key area count	3
Land-use parcels	63
Data gaps (pending official data): Floor area ratio · Building height limit · Statutory coverage · Statutory green ratio · Setback control — Pending official data	


Task coverage & professional matrices	
Announcement tasks 17/17 covered	
Agent tasks 6/6 covered	
Formal design depth 15/15 complete	
9 professional standards answered (incl. 3 new non-mandatory)	

Source tiers	
SITE-PACKAGE — 任务书、枚举、设计空间、限值、模式与临时边界等场地包材料。	
SOURCE-REGISTRY — 区分 formal 可用、背景、临时与待审资料的登记册。	
PROCESSED-FACT-PACK — 范围、任务、资料用途与缺资料清单的导航层，非新权威来源。	
BOUNDARY-SOURCE — 提交总体设计范围（临时约束），仅用于生成、展示与临时自恰。	
KEY-AREA-SOURCE — 三处重点区域范围（临时约束），仅用于生成、展示与临时自恰。	
OFFICIAL-ANNOUNCEMENT — 公告 1.3/1.4/1.5 的任务、范围、面积、语言与成果归属主控制据。	
AGENT-TASKBOOK — 十条共创原则、六项智能体任务、场景/品牌/运营要求与边界条款。	
GLOBAL-CASE-BACKGROUND — 全球创新生态案例为背景研究（匠莊造、伦敦国王十字、Kista、Kendall Square、深圳南山、杭州城西、慕尼黑 Werksviertel），仅作参考参照，不作为正式证据。	
KG-DRAFT-2024 — 《北京海淀区京张铁路遗址公园沿线（人工智能创新街区重点地区）HD00-1601等街区控制性详细规划（街区层面）（2022-2035年）（草案）》公示图则（北京市规划和自然资源委员会海淀分局，2024-12-20 公示）：空间结构“一带一轴、两心多点”，三大目标定位，规模控制（常住约36.4万人、城乡建设用地约1648.1公顷、建筑规模约2369.3万平方米）、九类主导功能分区、配套设施（公共服务298处等）、整体景观结构“三带六轴、多廊多中心”、交通体系（道路网密度约8.0公里/平方公里、绿色出行80%）等结构性衔接依据。	
KG-APPROVAL-2026 — 北京日报报道（2026-08-12）：市规划自然资源委于 2026-08-11 批复《北京海淀区京张铁路遗址公园沿线（人工智能创新街区重点地区）HD00—1601等街区控制性详细规划（街区层面）（2024年—2035年）》；范围东至新街口外大街、西至中关村大街、北至成府路、南至西直门外大街，共 9 个街区约 1668.2 公顷；以绿色公共空间建设引领区域城市更新，发展大模型、智能体、具身智能等新业态，构建生活圈与创新圈融合的一刻钟社区服务圈。	
HD-YUANDIAN-2026 — 北京市海淀区人民政府官网《北京AI原点社区，全球AI人才创新创业的“第一站”》：北京AI原点社区约 3 平方公里（以东开大厦为中心），立足“创新策源、创业首选”特色定位，目标打造“全球AI人才创新创业第一站”，东升产业空间集聚 AI 领域企业 300 多家、占比超七成（2025 年 AI 相关专利商标超 2000 项）、1 公里半径内聚集 30 多所高校和科研机构、超 1000 位 AI 科学家、1.3 万名开发者、10 万名相关专业学子；康桥学堂（免费工位、全生命周期创业服务）、大模型生态服务站（“找政策、找资金、找算力、找人才、找伙伴、找智力、找空间、找场景”八大核心问题一站式解决）、“15分钟活力生活圈”（4000 余套人才公寓、海淀未来学校等）；社区已纳入北京市首批人工智能创新街区，北京市打造以海淀为核心的“一核多点”布局。本案五道口-原点站空间承接与功能适配呼应依据。	
AMAP-POI-2026 — 高德开放平台周边检索 API（2026-08-13 检索，按范围图外包矩形 lng 116.300–116.380 / lat 39.925–39.998，GCJ02→WGS84 转换）：地铁站 28、高等院校 50、公园广场 68、综合医院 32、购物中心 37，用于总体空间结构规划图（spatial-structure）的设施分布校核叠加；底图为高德地图 webrd 瓦片（z15）。	

Overall Spatial Structure Plan | One Rail, Two Rivers, Three Stations • Six Axes (Ama

Amap geographic base × submitted GeoJSON structure × Amap POI facility check — aligned with the regulatory plan's 'belt-axis-centers-nodes' and carrying Beijing AI Or

Overall design area 11.4 sqkm (provisional): rail as trunk • three-station relay • six-axis stitch • node network

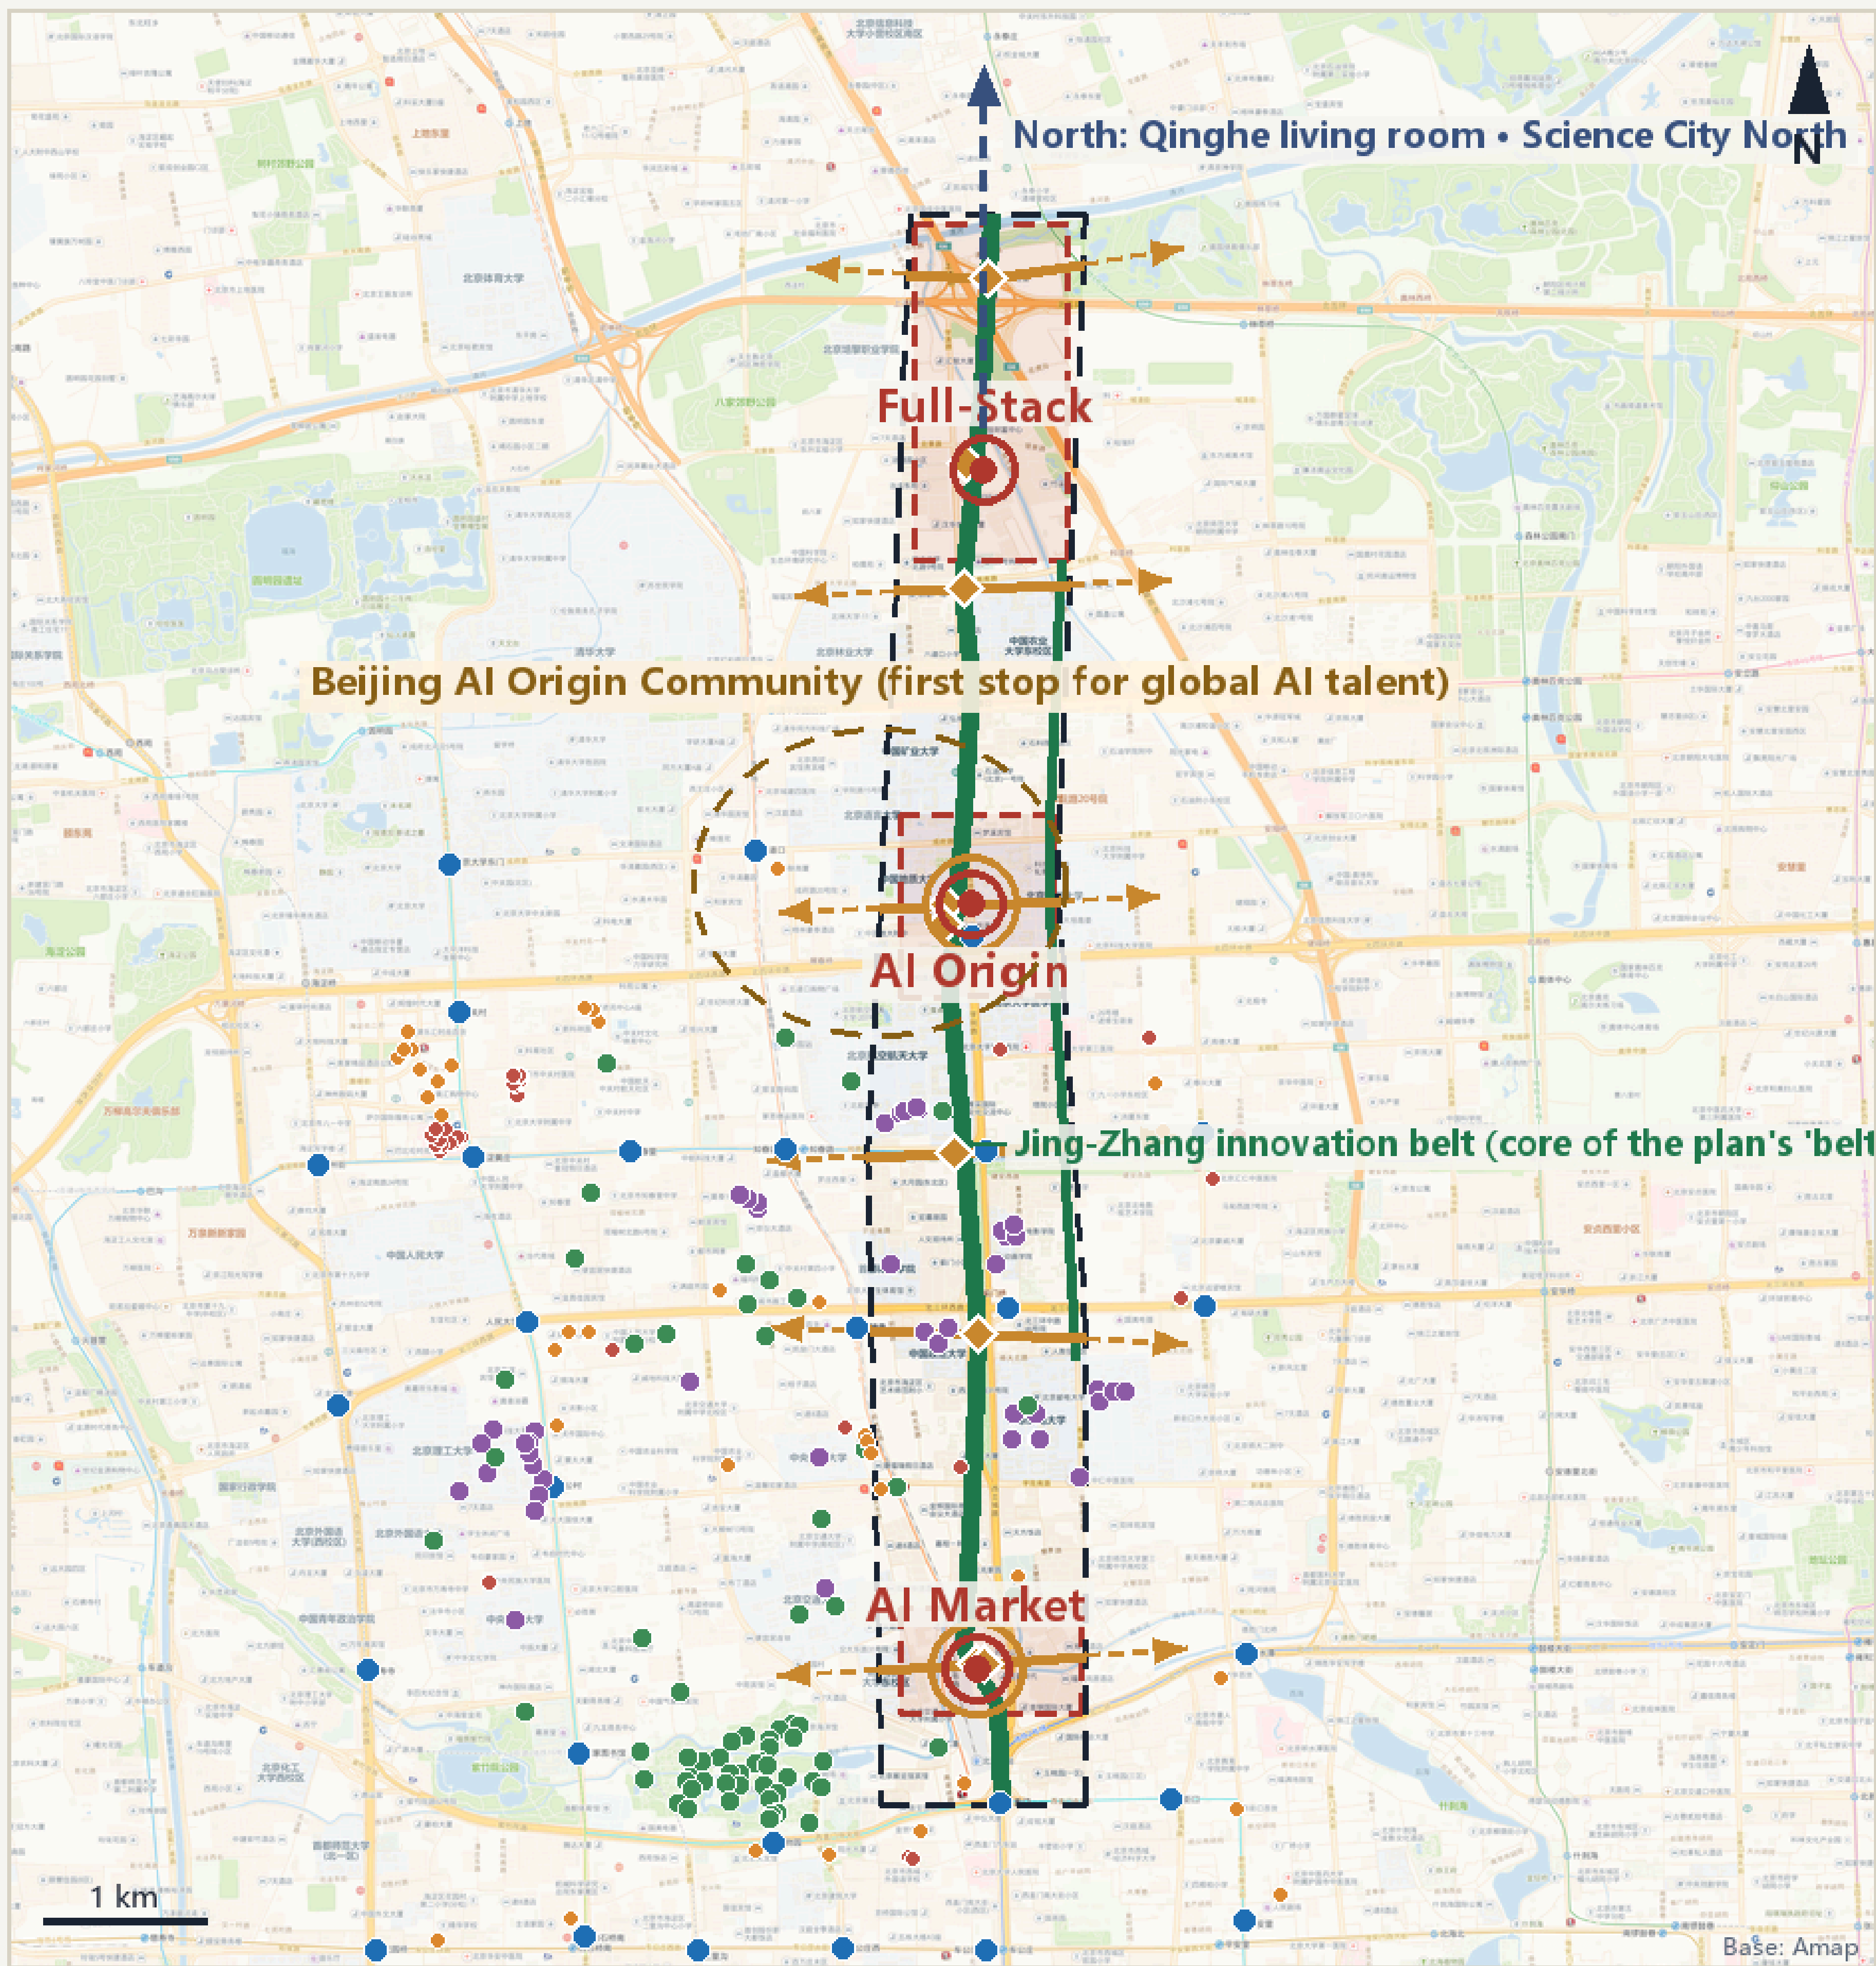

Base: Amap webdr tiles (z15, GCJ02 Mercator, 2026-08); POI: Amap around-search within the regulatory-plan box (152m radius); structure overlaid via EPSG:4548→WG

STRUCTURE / key points

- One rail: ≈9.8 km heritage spine — spatial skeleton of the plan-belt's core segment (Jing-Zhang innovation-and-exchange belt)
- Two rivers: Qinghe living room × Xiaoyue corridor (linking the 'three belts')
- Three stations: AI Market · AI Origin · Full-Stack relay points — carrying the 'two centers'; AI Origin matches Beijing AI Origin Community
- Six axes: east-west stitch axes answering 'N-S continuity, E-W connection'
- Multiple nodes: 9 switch plazas matching the plan's node system

ALIGNMENT / regulatory plan & AI Origin Community

- Plan: one belt, one axis, two centers, nodes
 - one rail, three stations, six axes, nodes (aligned since v1.5)
- Beijing AI Origin Community: 'innovation source, first choice'
 - carried by Wudaokou AI Origin — spatial anchor of the 'first stop' for global AI talent
- Campus-park-block fusion • 15-min lively living circle
 - the AI Origin 'campus—park—block' slow-mobility stitch is its spatial landing
- Foundation-model ecosystem station: eight-factor services
 - echoed by the Origin Hall + open-source collaboration center programming
- Beijing's first AI innovation blocks: 'one core, multiple nodes'
 - this proposal's 'one rail, three stations, node network' plugs in

POI CHECK / facilities (Amap)

- metro stations 28
- universities 50
- parks & squares 68
- hospitals 32
- shopping malls 37

Station-level facilities match the 15-minute service-circle structure: metro stations spread evenly along the corridor and axes; the university cluster underpins the Wudaokou campus-park-block stitch.

LEGEND

- overall design area (provisional)
- key areas (provisional)
- heritage spine (one rail)
- E-W stitch axes (six)
- switch plazas (8 nodes)
- three stations