


BOARD 1 · OVERALL DESIGN STRUCTURE

总体设计结构

Overall design structure — one line, three stations, two switches


令牌闭塞的今用：一条连续运行、按令牌分段预约的城市AI开放测试主线，在三处重点片区断开为站点，由两处道岔把东西两侧接入主线。线是产品，站是接口。

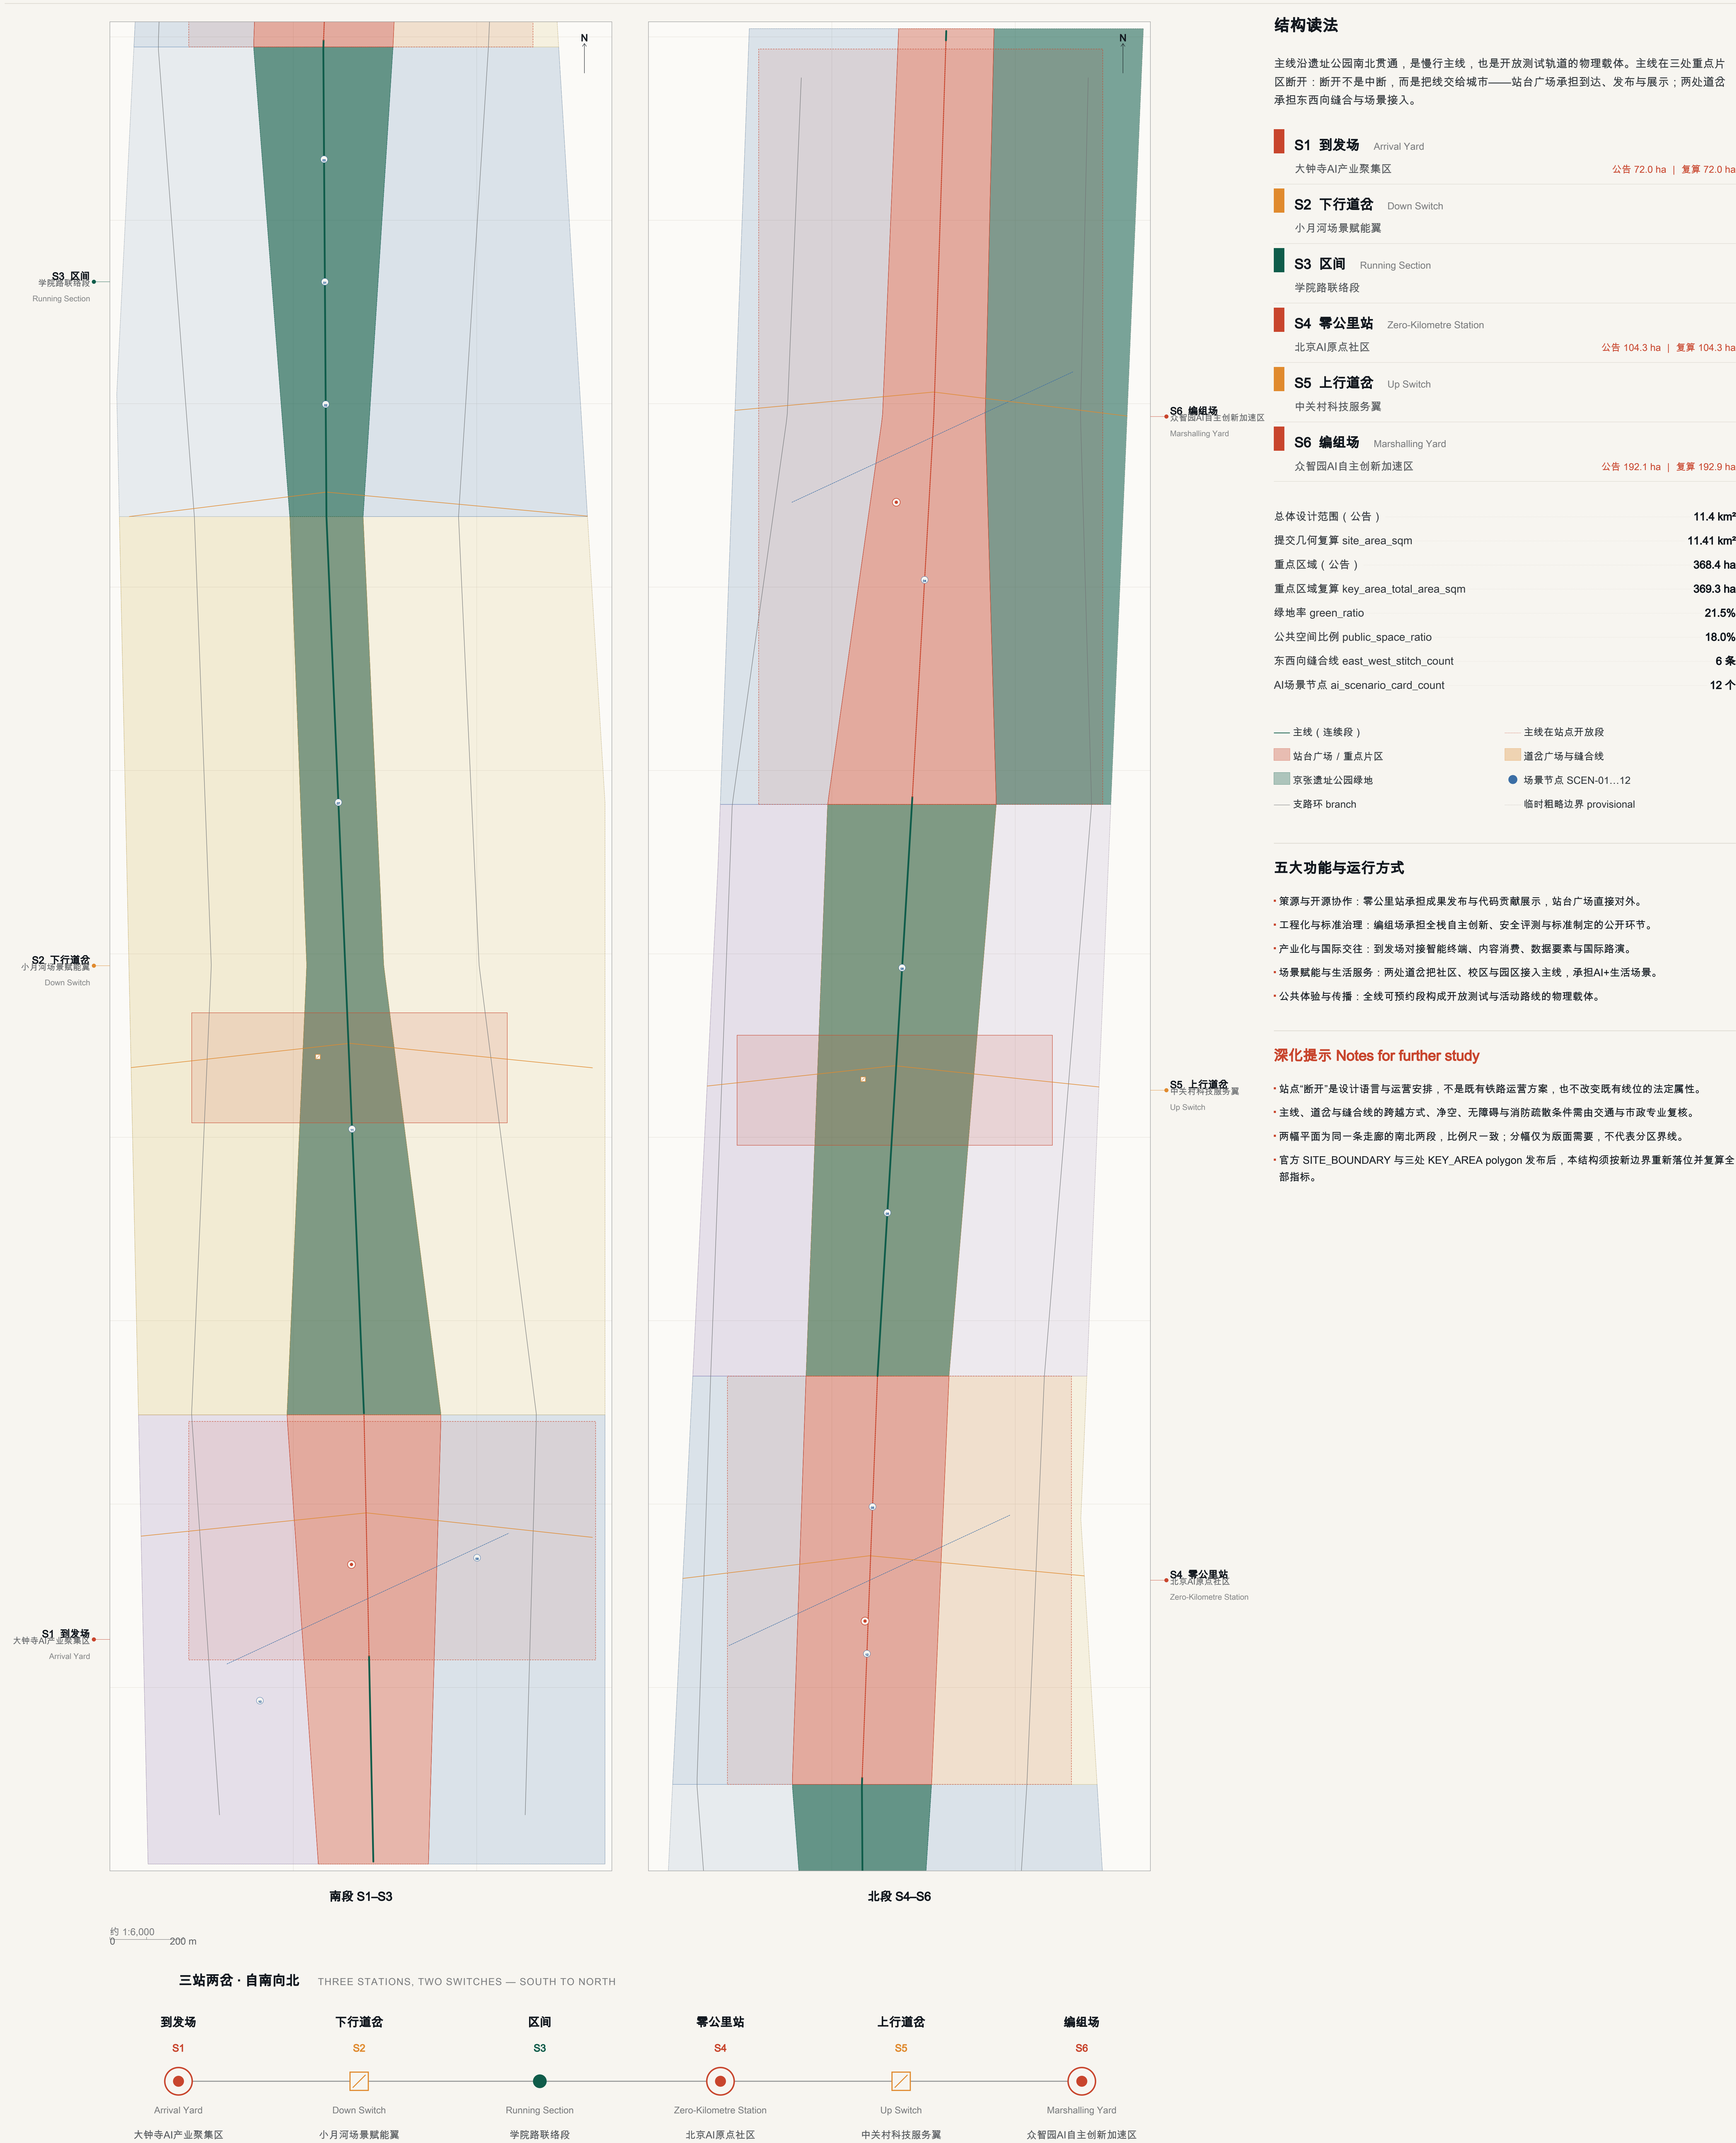

用地布局与城市更新

Land use & urban renewal


用地采用国土空间用途管制分类公开指引子集表达，完整覆盖提交边界；建筑基底为更新抓手的概念示意。容积率、建筑高度与建筑密度待正式控规条件确认。

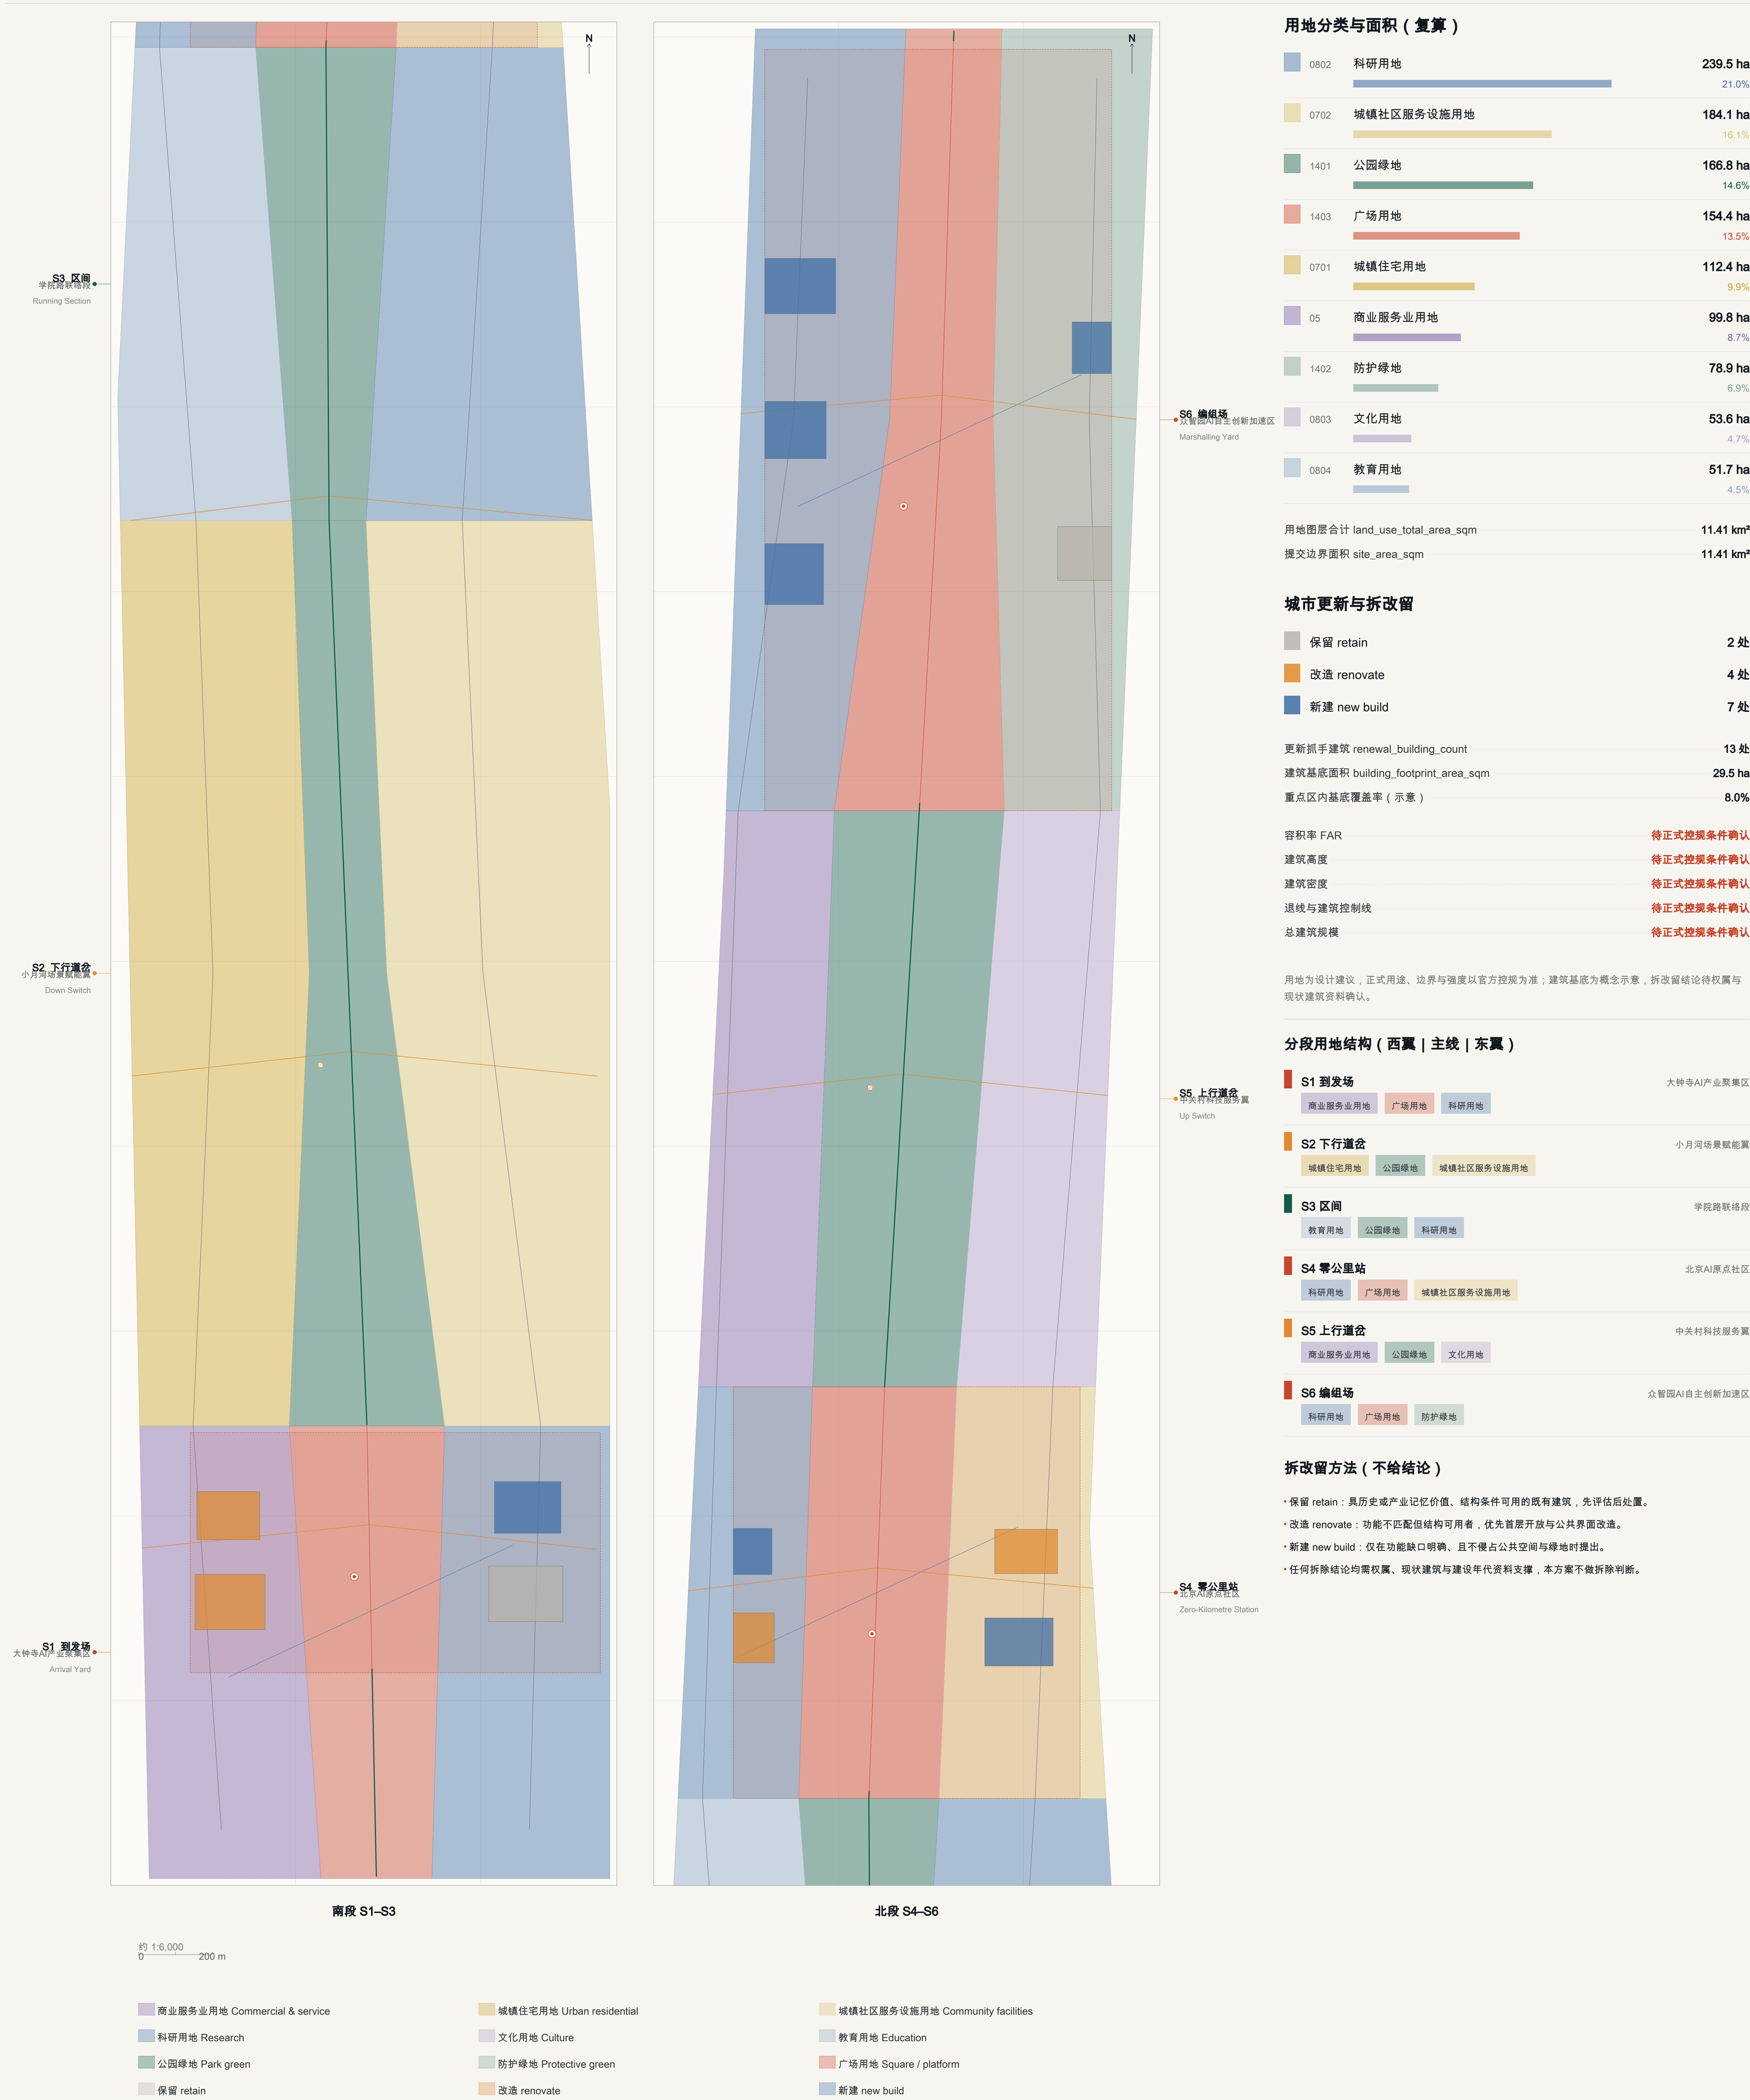

交通、轨道、慢行与市政支撑

Mobility, rail, slow traffic & municipal support

以连续慢行主线、六条东西向缝合线与三条轨道接驳建议线组织廊道两侧的可达性；道路红线宽度、横断面与道路面积未公开，本板不给出任何道路面积或红线数值。

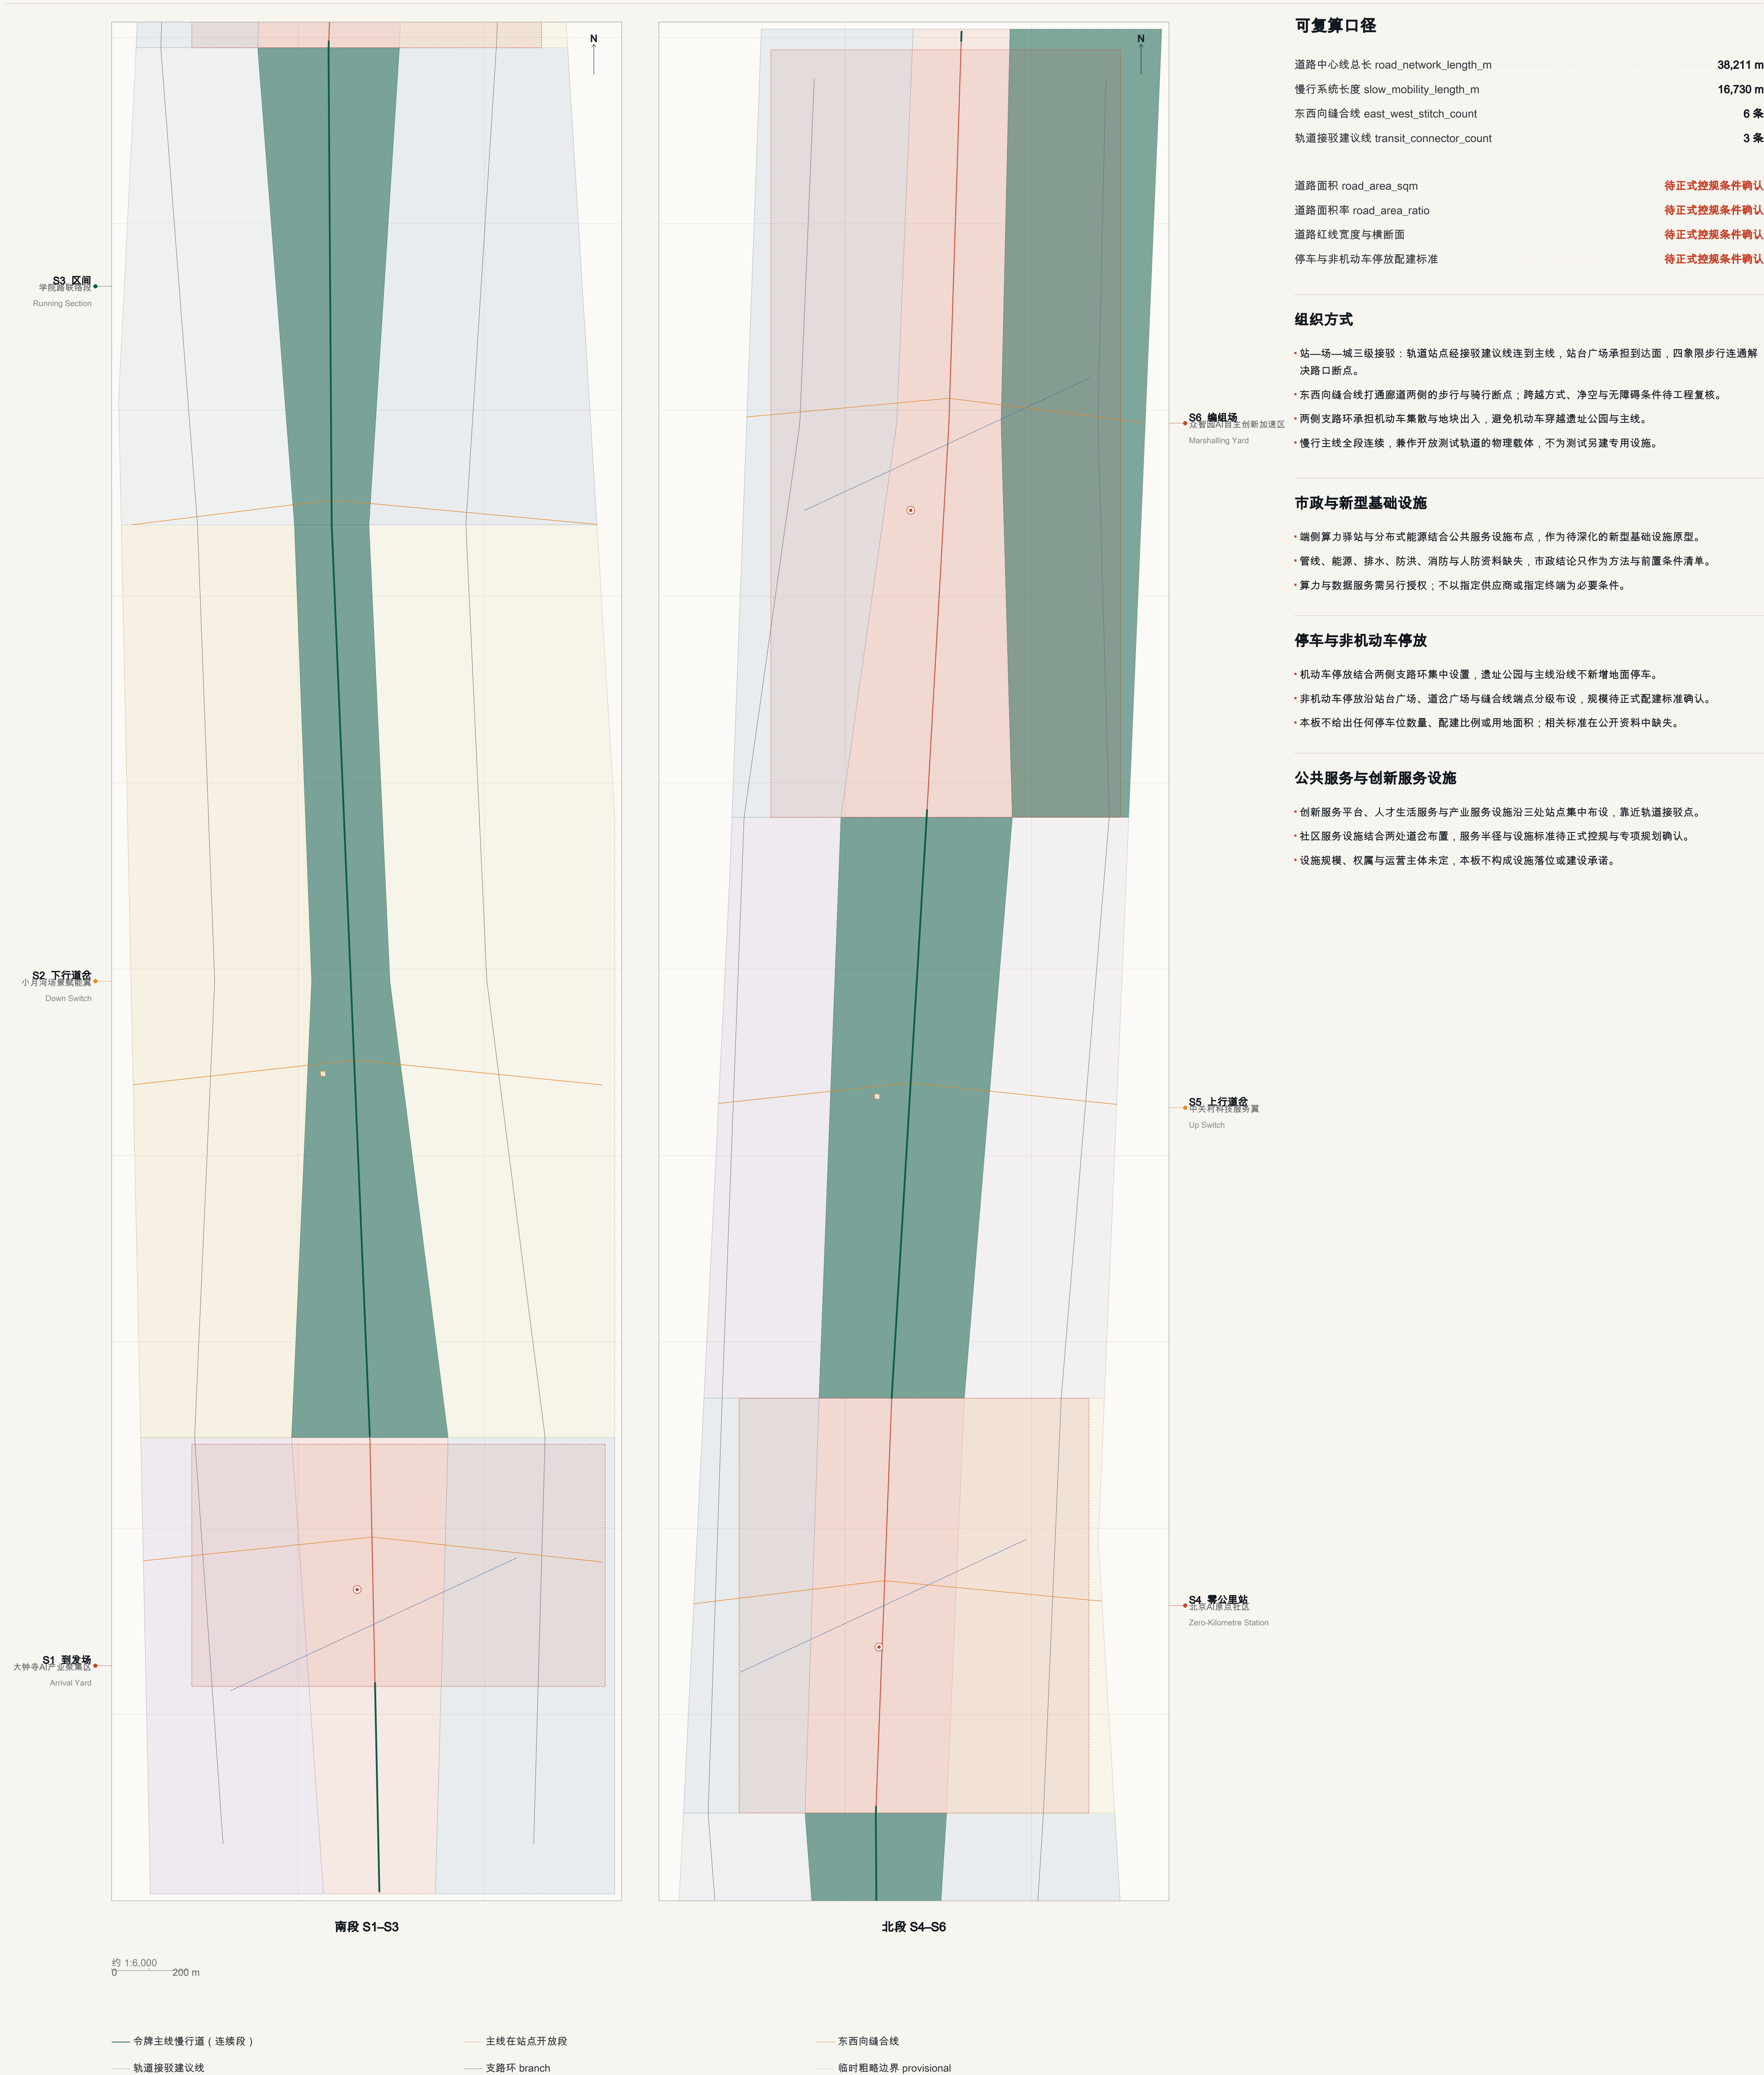

遗址公园连续绿地既是生态基底，也是开放测试与公共活动的载体；站台广场与道岔广场构成南北到达面与东西向公共客厅。



BOARD 5 · THREE KEY AREAS IN DETAIL

三大重点片区详细设计


Three key areas in detail — concept proposal

三处重点片区自北向南依次为编组场（众智园）、零公里站（北京AI原点社区）与到发场（大钟寺）；各片区均为概念建议，容积率、建筑高度与建筑密度待正式控规条件确认。

编组场 众智园AI自主创新加速区

花园型全栈自主创新街区

Marshalling Yard

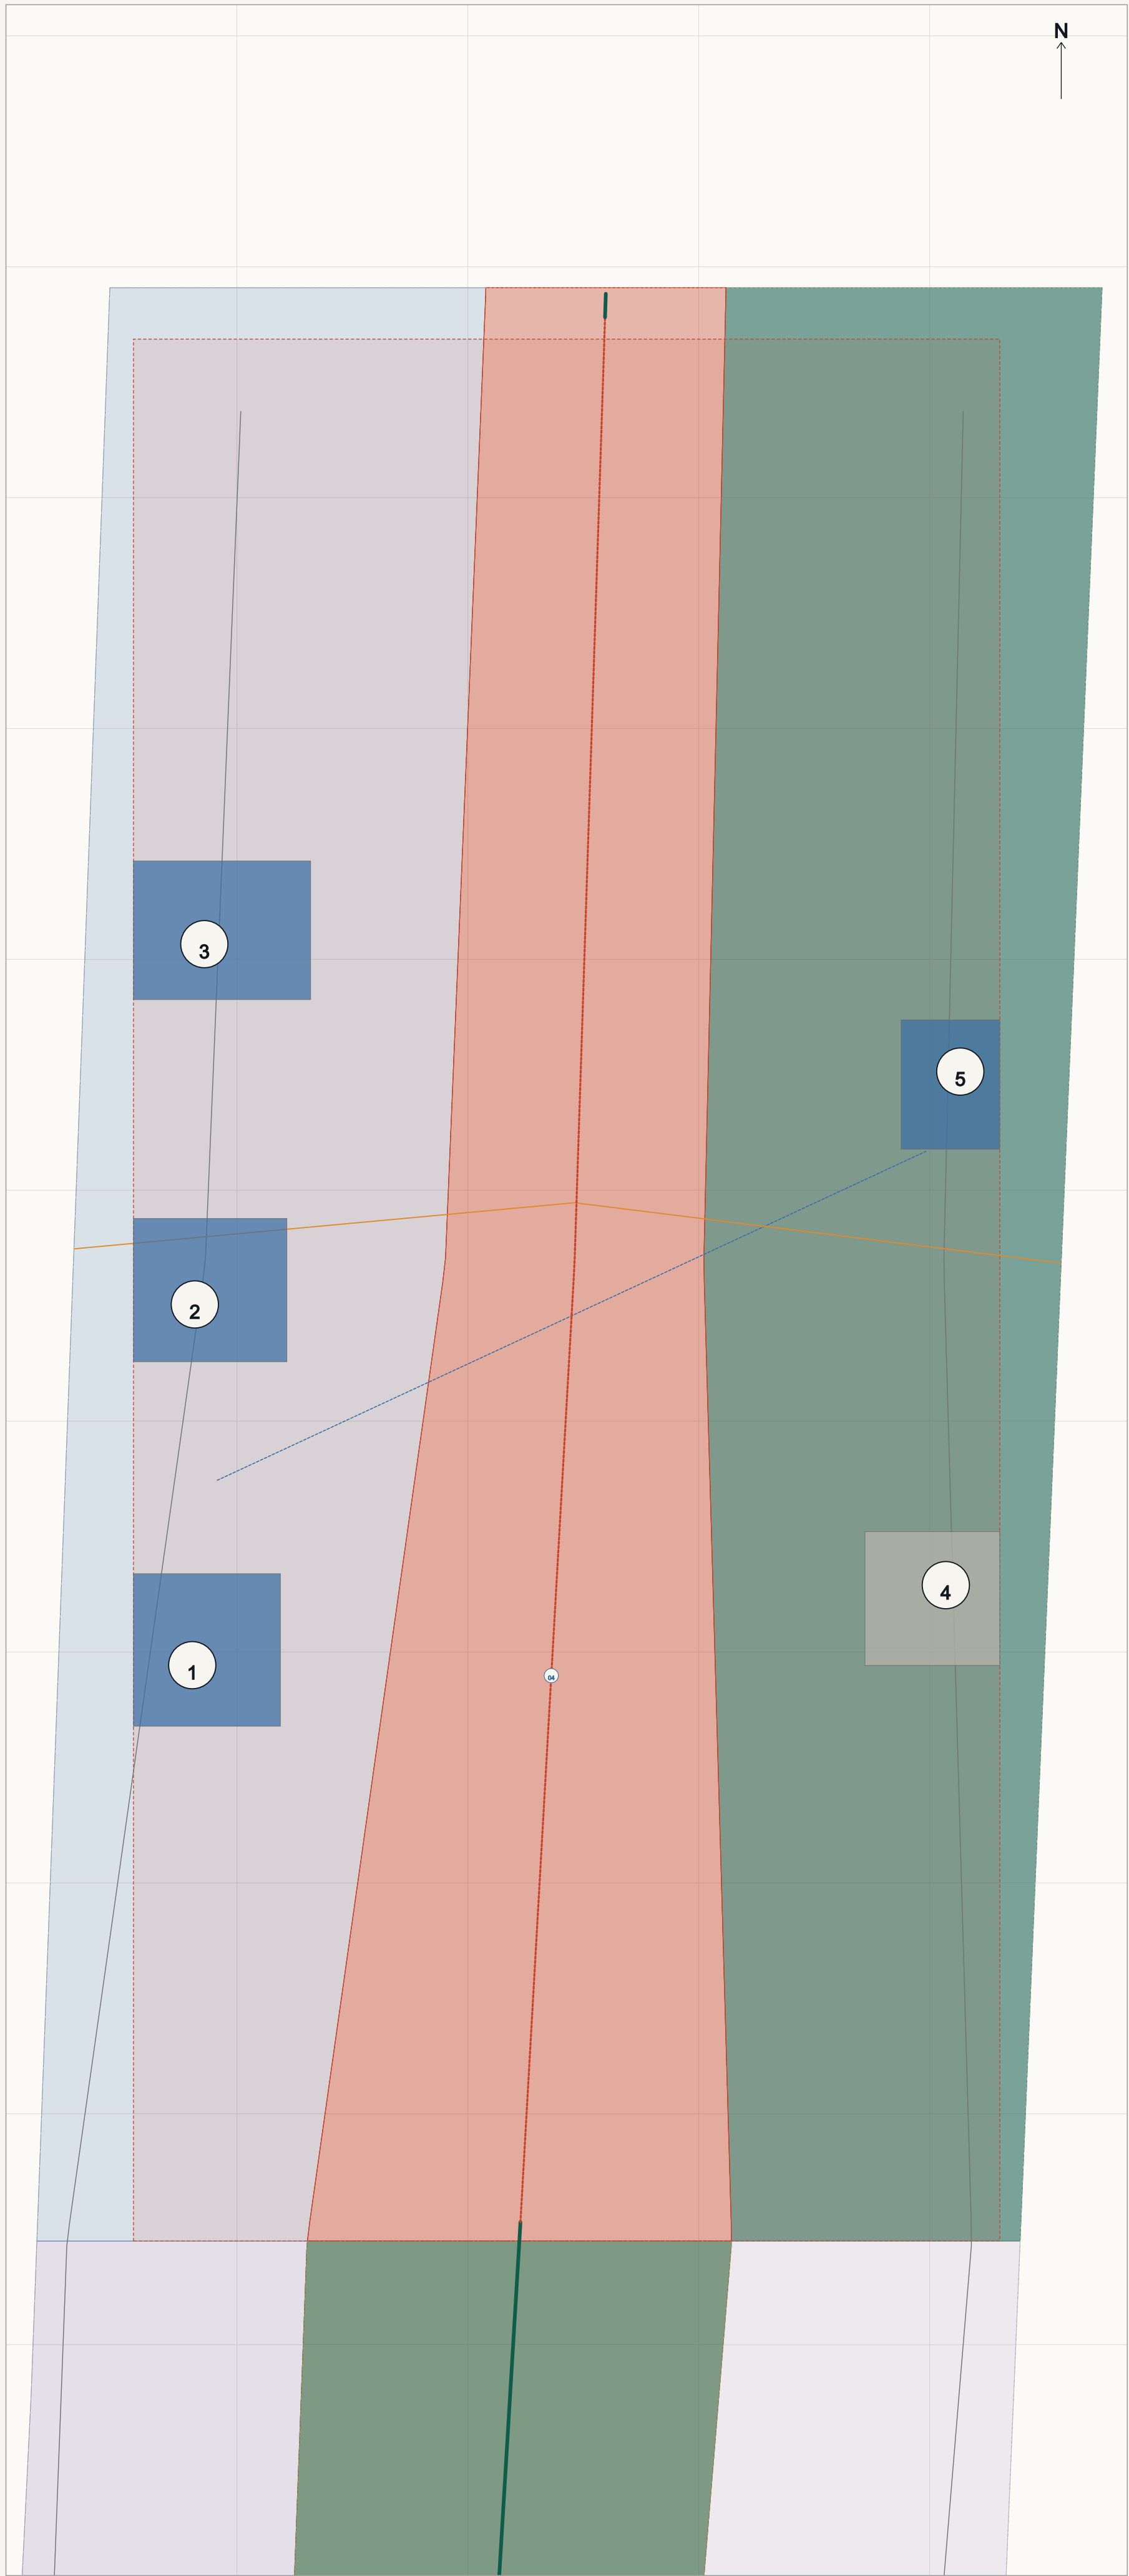

约 1:5,000
0 200 m

公告面积 announced	192.1 ha
提交几何复算 recomputed	192.9 ha
更新抓手 handles	5 处

更新抓手清单

- 1

全栈自主创新研发组团

new_build
- 2

安全治理与评测实验室

new_build
- 3

标准与治理服务楼

new_build
- 4

现状保留产业建筑

retain
- 5

自主创新展示馆

new_build

空间动作（概念建议）


- 强化清河界面与北端防护绿带，把生态缓冲同时用作开放测试与展示的绿色基底。
- 以标准制定、安全评测与全栈自主创新研发组团构成产业核心，配自主创新展示馆对外开放。
- 站台广场承担自主创新开放展示与标准治理公众面；北段跨线解决北五环界面的步行断点。
- 对外交通依赖轨道连接建议线 with 支路环；站位与红线以正式轨道与控规资料为准。

容积率 FAR	pending
建筑高度	pending
建筑密度	pending
建筑规模	pending

零公里站 北京AI原点社区

近校型成果转化与人才社区

Zero-Kilometre Station

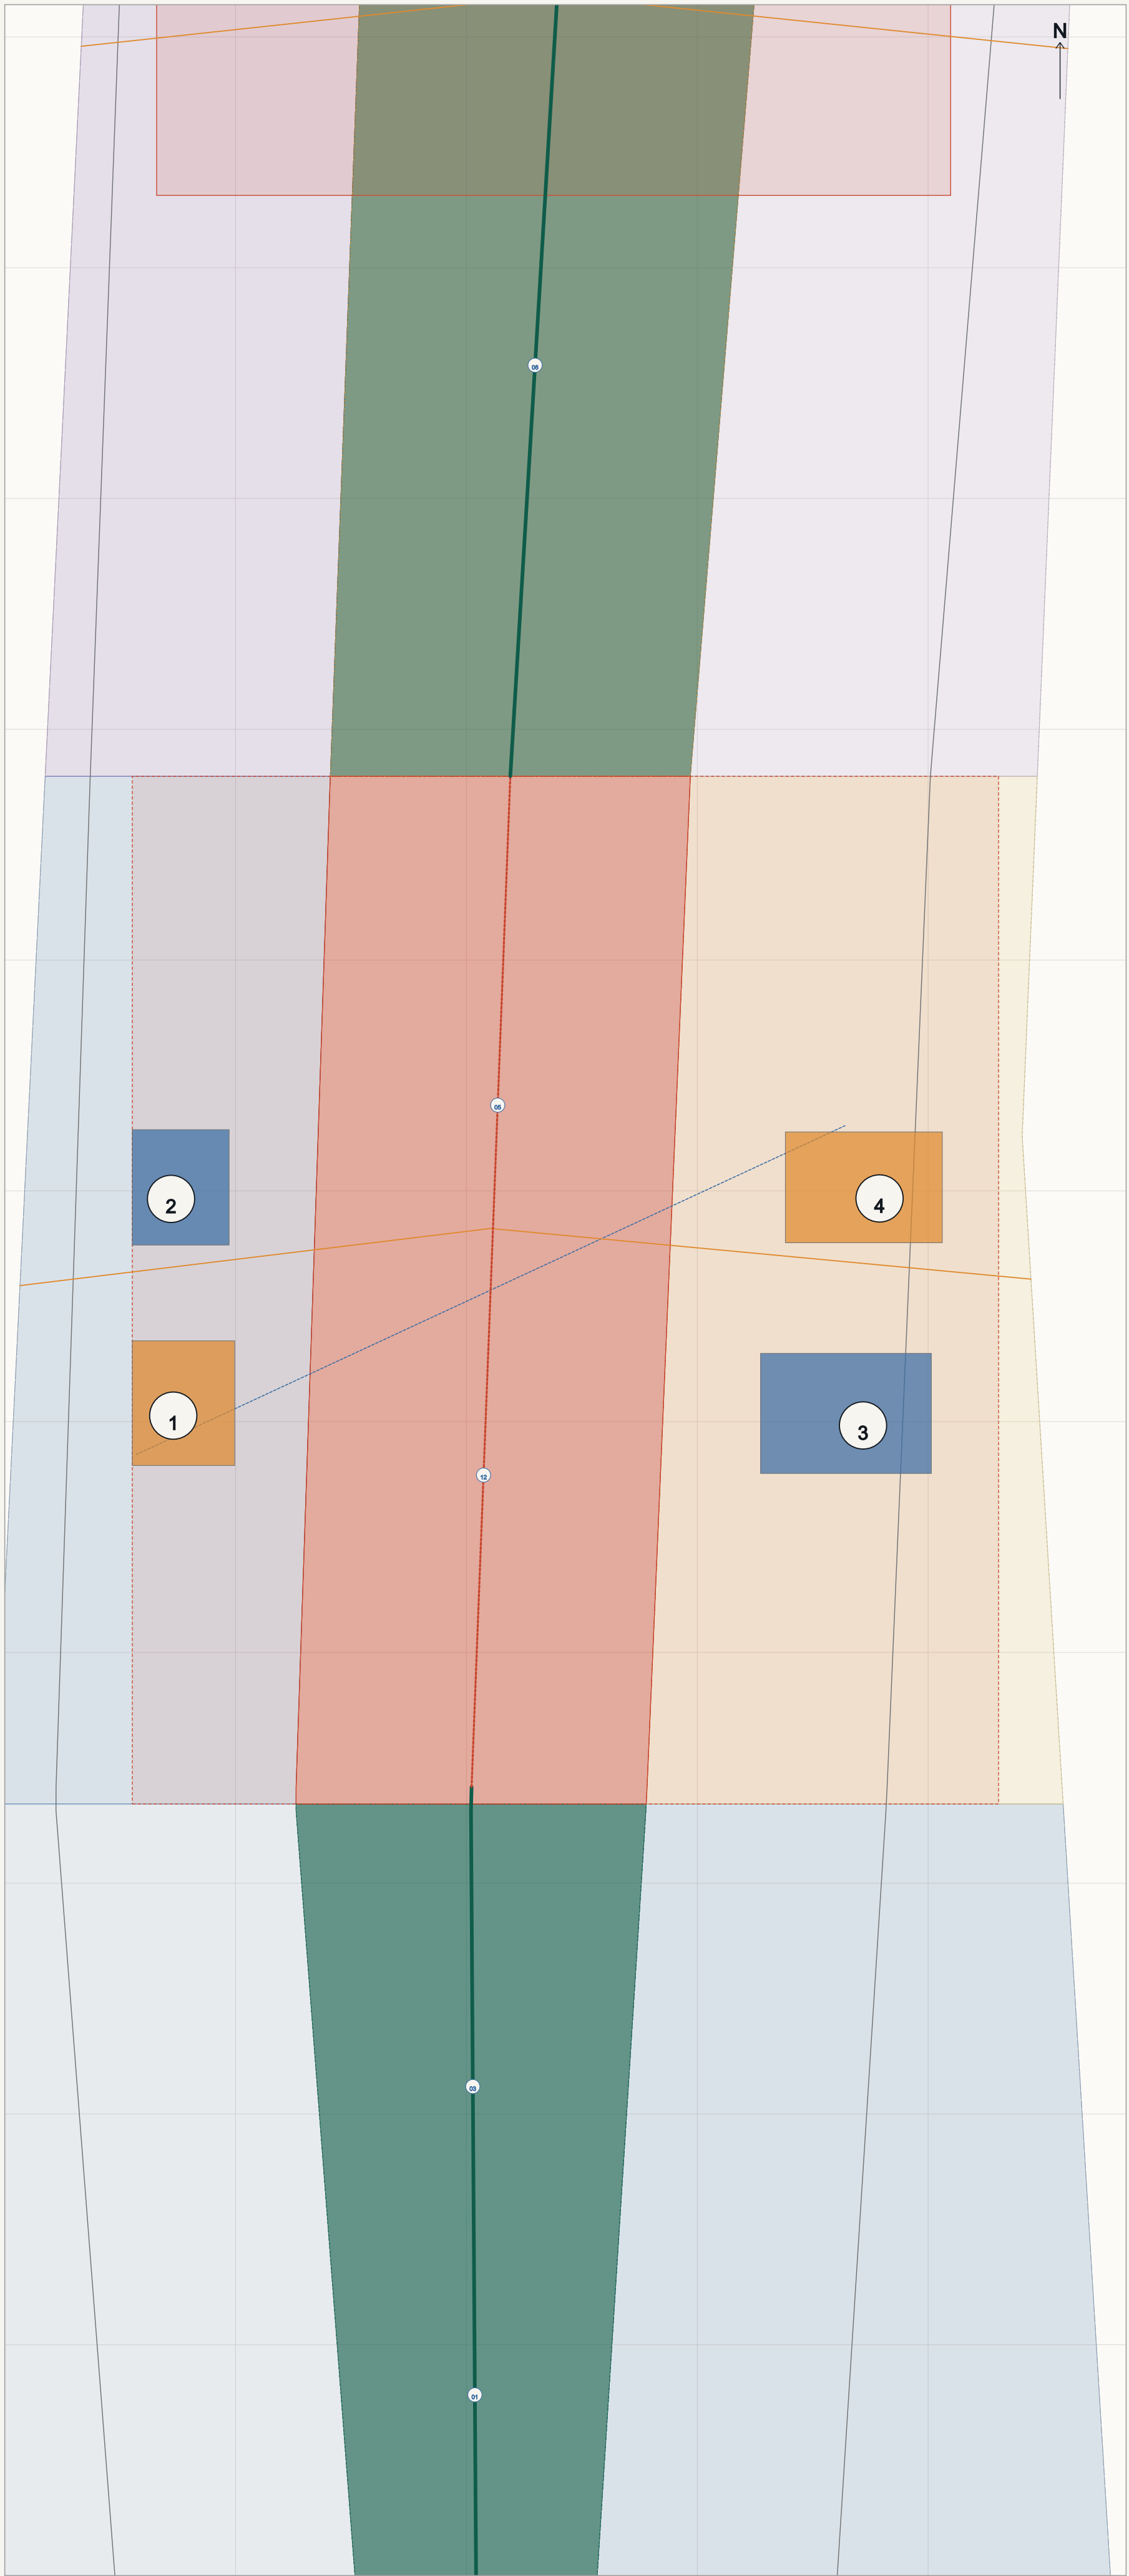

约 1:5,000
0 200 m

公告面积 announced	104.3 ha
提交几何复算 recomputed	104.3 ha
更新抓手 handles	4 处

更新抓手清单

- 1

近校成果转化孵化器

renovate
- 2

开源协作实验室

new_build
- 3

人才公寓组团

new_build
- 4

原点社区服务中心

renovate

空间动作（概念建议）


- 零公里碑与开源发布厅构成主场：成果发布、代码贡献展示与小型路演在站台广场直接对外。
- 近校成果转化孵化器、开源协作实验室紧邻高校界面，用东西向缝合线把校区、园区与街区连成慢行网络。
- 补足人才公寓组团与原点社区服务中心，回应人才特区的居住、生活与社交需求。
- 折改留分类仅为概念示意；权属、现状建筑与建设年代资料缺失，结论待正式资料确认。

容积率 FAR	pending
建筑高度	pending
建筑密度	pending
建筑规模	pending

到发场 大钟寺AI产业聚集区

城市型智能经济与国际交往街区

Arrival Yard

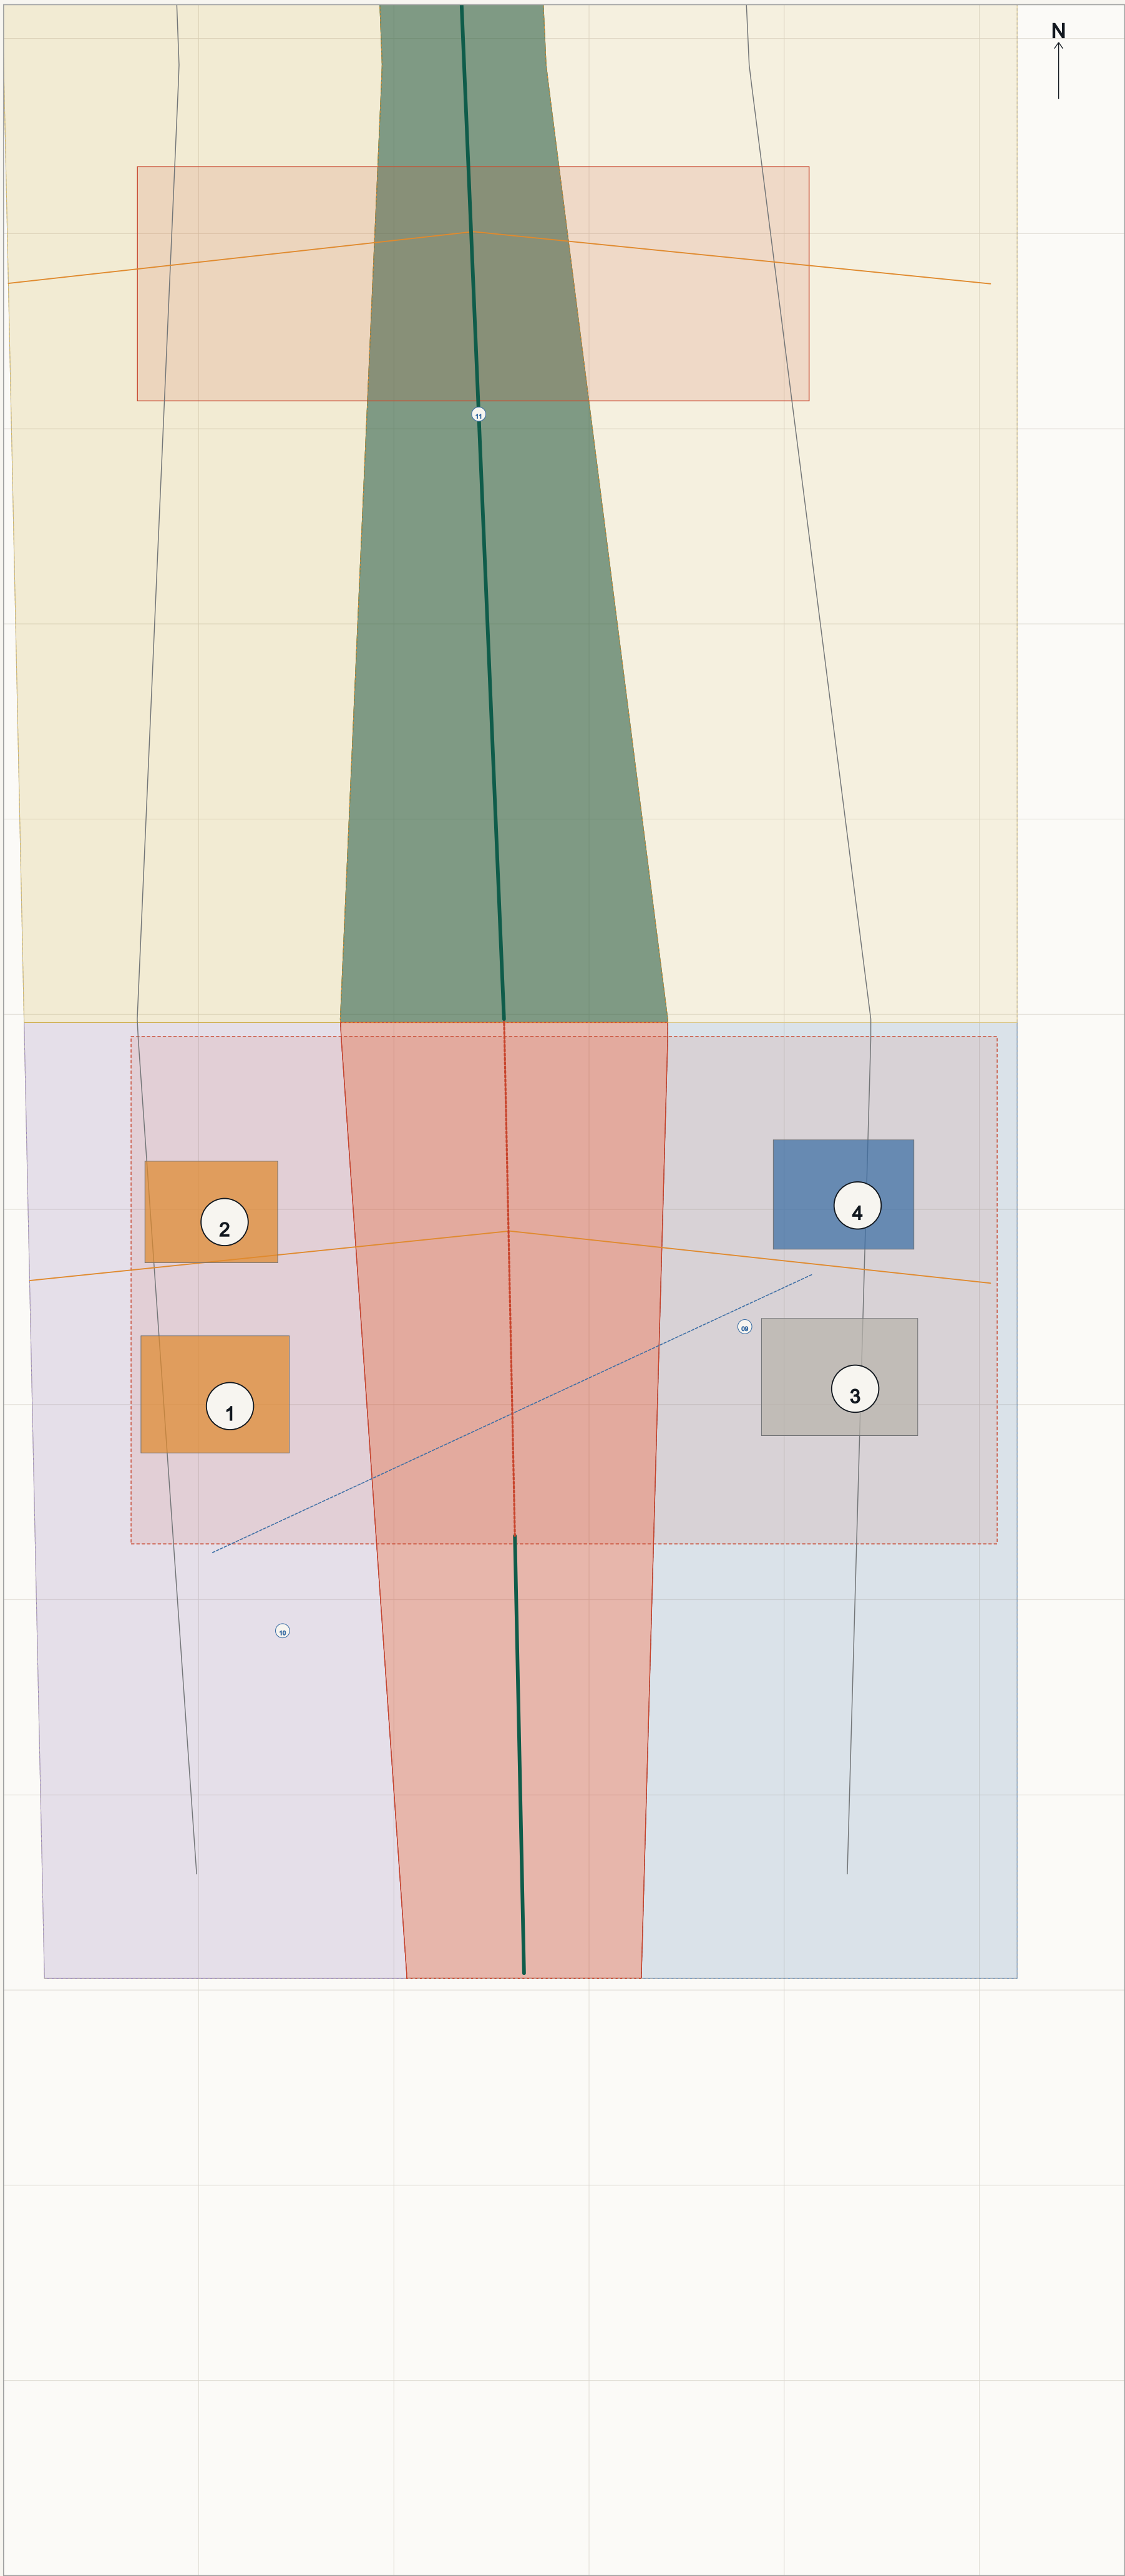

约 1:6,000
0 200 m

公告面积 announced	72.0 ha
提交几何复算 recomputed	72.0 ha
更新抓手 handles	4 处

更新抓手清单

- 1

到发场智能原生消费街区

renovate
- 2

国际路演客厅

renovate
- 3

智能终端企业总部组团

retain
- 4

数据要素会客厅

new_build

空间动作（概念建议）

- 以大钟寺站一体化与四象限步行连遇为骨架，把站点客流直接引入站台广场与主链南端。
- 智能终端企业总部组团、数据要素会客厅与国际路演客厅构成城市型产业界面。
- 智能原生消费街区承接商业服务业用地，把AI+生活服务落到可运营的小尺度街区。
- 规划绿地与广场复合利用，作为到达展示面；具体交叉口组织需交通专业复核。

容积率 FAR	pending
建筑高度	pending
建筑密度	pending
建筑规模	pending

- 保留 retain

改造 renovate
- 公园绿地

场景节点

- 新建 new build
- 临时粗略边界 provisional

- 站台 / 广场用地
- 主链连续段

底图为临时粗略边界（provisional），不得作为官方红线或精确面积依据。
本图全部空间提案为概念建议 / 参考方案，可供专业团队深化研究；不构成法定规划、政府批准、实施确认或投资承诺。
容积率、建筑高度、建筑密度、道路红线与道路面积：待正式控规条件确认（pending）。


AI场景、实施与运营

AI scenarios, implementation & operation

全线划为六段可预约段，承载12个AI场景节点；场景带具名运营方、明示数据边界与不可自动化取消的人工复核点。场景为概念建议，未获批准运营。

可预约段与场景节点

Bookable segments & scenario nodes

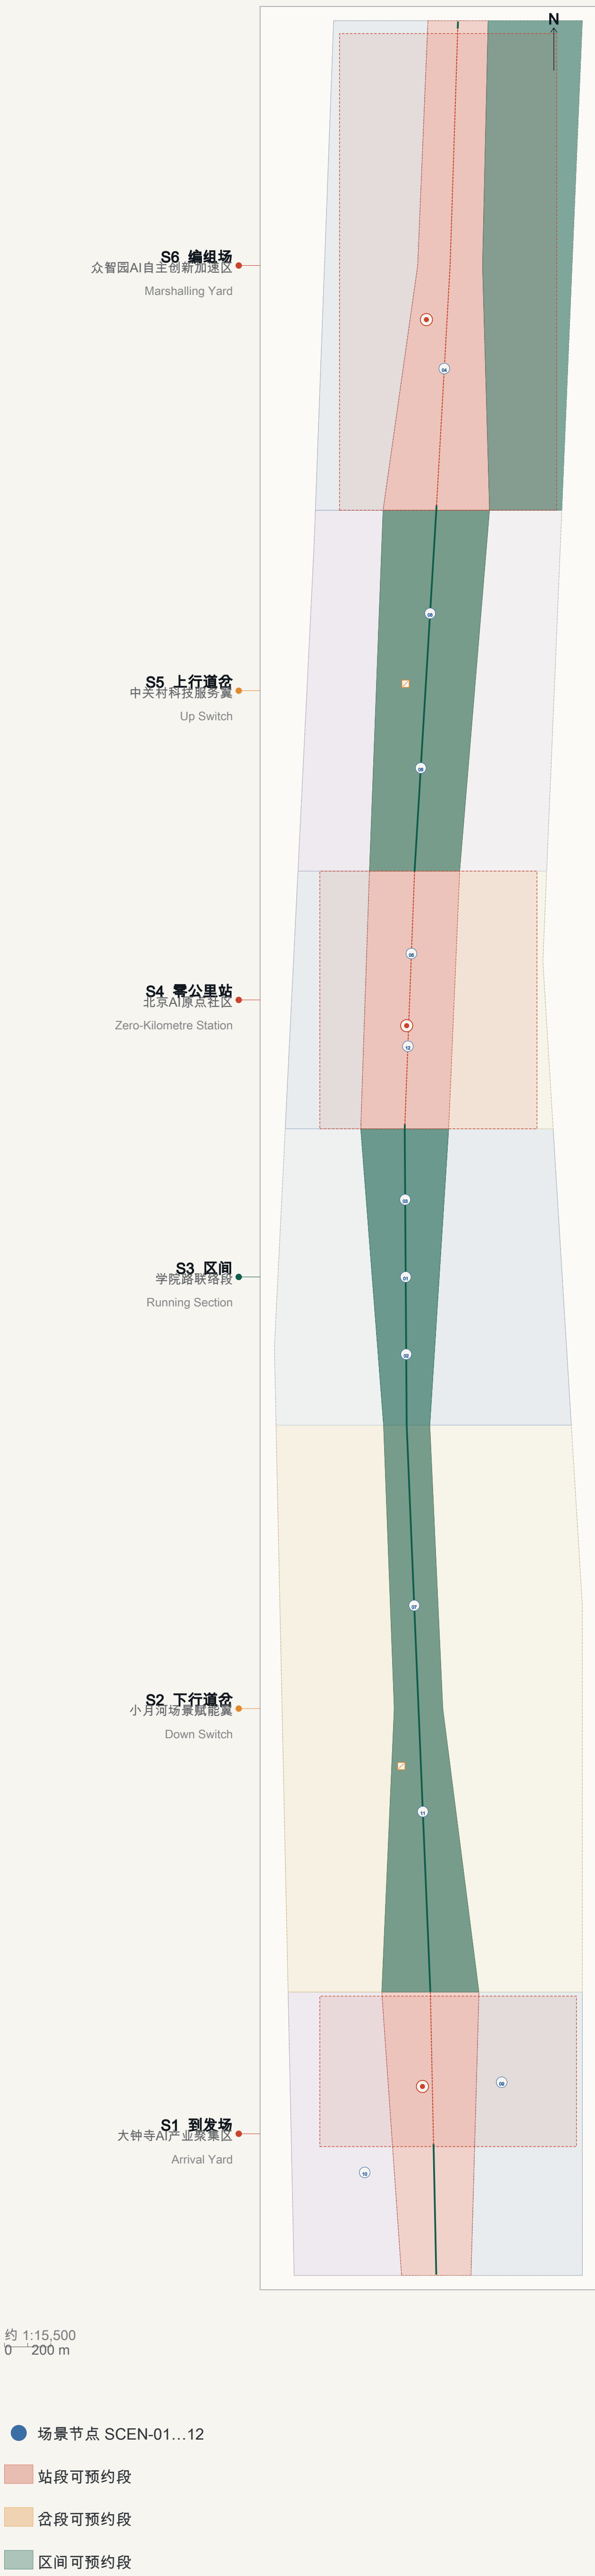

运行协议

预订—布设—按公开规则运行限定窗口—归还普通公共使用；具名运营方、明示数据边界、不可自动化取消的人工复核点。

AI场景卡 12 张

AI scenario cards (constraints.geojson · SCENARIO_NODE)

01	可预约轨道段	S3
Bookable track segment		
人工复核必需		
仅使用公开或已授权数据；不做个体画像；不以指定供应商为必要条件；场景为概念建议，未获批准运营。		
02	低速机器人配送验证	S3
Low-speed robot delivery validation		
产业测试验证场景 人工复核必需		
仅使用公开或已授权数据；不做个体画像；不以指定供应商为必要条件；场景为概念建议，未获批准运营。		
03	自主慢行体验评估	S3
Autonomous slow-mobility assessment		
产业测试验证场景 人工复核必需		
仅使用公开或已授权数据；不做个体画像；不以指定供应商为必要条件；场景为概念建议，未获批准运营。		
04	模型安全红队沙盒	S6
Model safety red-team sandbox		
产业测试验证场景 人工复核必需		
仅使用公开或已授权数据；不做个体画像；不以指定供应商为必要条件；场景为概念建议，未获批准运营。		
05	开源发布厅	S4
Open-source release hall		
人工复核必需		
仅使用公开或已授权数据；不做个体画像；不以指定供应商为必要条件；场景为概念建议，未获批准运营。		
06	沿线AI文化导览	S5
AI cultural guide along the line		
人工复核必需		
仅使用公开或已授权数据；不做个体画像；不以指定供应商为必要条件；场景为概念建议，未获批准运营。		
07	AI+医疗健康服务导航点	S2
AI+ health service navigation point		
人工复核必需		
仅使用公开或已授权数据；不做个体画像；不以指定供应商为必要条件；场景为概念建议，未获批准运营。		
08	企业服务Copilot窗口	S5
Enterprise service copilot counter		
人工复核必需		
仅使用公开或已授权数据；不做个体画像；不以指定供应商为必要条件；场景为概念建议，未获批准运营。		
09	数据要素会客厅	S1
Data-element service house		
人工复核必需		
仅使用公开或已授权数据；不做个体画像；不以指定供应商为必要条件；场景为概念建议，未获批准运营。		
10	智能原生消费街区	S1
Intelligent-native retail street		
人工复核必需		
仅使用公开或已授权数据；不做个体画像；不以指定供应商为必要条件；场景为概念建议，未获批准运营。		
11	公共安全与活动运营复核	S2
Public safety and event operations review		
人工复核必需		
仅使用公开或已授权数据；不做个体画像；不以指定供应商为必要条件；场景为概念建议，未获批准运营。		
12	全球AI活动周步行路线起点	S4
Global AI Week route start		
人工复核必需		
仅使用公开或已授权数据；不做个体画像；不以指定供应商为必要条件；场景为概念建议，未获批准运营。		

用户画像与空间响应

开源开发者	需求：发布、协作、测试、社区声誉
边界：不采集个人行为轨迹；活动数据仅做聚合统计	
初创团队	需求：低成本办公、算力入口、产品试验场
边界：算力与数据服务需另行授权	
头部企业访客	需求：展示、商务、国际接待、招聘
边界：企业标识与案例须清权	
周边居民	需求：通勤、休闲、社区服务、低扰动更新
边界：不得居民画像用于商业推荐	
高校师生	需求：成果转化、跨校协作、日常慢行
边界：校园数据与科研成果需授权	

分期实施与运营

Phasing & operation



BOARD 7 · METRICS RECOMPUTATION & COMPLIANCE RESPONSE

指标复算与合规响应

Metrics recomputation & compliance response

全部 known 指标均由提交 GeoJSON 在 EPSG:4548 下复算；容积率、建筑高度、建筑密度、道路红线与道路面积在公开资料中缺失，一律登记为 unknown。

指标复算表 metrics.json

指标	置信度	值
site_area_sqm	high	11.41 km²
land_use_total_area_sqm	high	11.41 km²
land_use_area_commercial_services_05_sqm	medium	99.8 ha
land_use_area_urban_residential_0701_sqm	medium	112.4 ha
land_use_area_community_facilities_0702_sqm	medium	184.1 ha
land_use_area_research_0802_sqm	medium	239.5 ha
land_use_area_culture_0803_sqm	medium	53.6 ha
land_use_area_education_0804_sqm	medium	51.7 ha
land_use_area_park_green_1401_sqm	medium	166.8 ha
land_use_area_protective_green_1402_sqm	medium	78.9 ha
land_use_area_square_1403_sqm	medium	154.4 ha
green_space_area_sqm	medium	245.7 ha
green_ratio	medium	21.53%
public_space_area_sqm	medium	206.0 ha
public_space_ratio	medium	18.05%
building_footprint_area_sqm	low	29.5 ha
building_footprint_ratio_key_areas	low	7.99%
key_area_count	high	3
key_area_total_area_sqm	medium	369.3 ha
key_area_beijing_ai_origin_community_sqm	medium	104.3 ha
key_area_dazhongsi_ai_industry_cluster_sqm	medium	72.0 ha
key_area_zhongzhiyuan_ai_acceleration_area_sqm	medium	192.9 ha
phasing_area_phase_1_sqm	medium	276.6 ha
phasing_area_phase_2_sqm	medium	482.0 ha
phasing_area_phase_3_sqm	medium	382.6 ha
road_network_length_m	medium	38,211 m
slow_mobility_length_m	medium	16,730 m
east_west_stitch_count	medium	6
transit_connector_count	medium	3
renewal_building_count	low	13
ai_scenario_card_count	high	12
pilgrimage_landmark_count	high	4
unknown (11) · 待正式控规条件确认		
total_floor_area_sqm	scenario_admission_turnaround_days	
floor_area_ratio	step_free_continuity_breaks	
building_height_m	non_digital_equivalence_ratio	
road_area_sqm	objection_resolution_days	
road_area_ratio	public_space_return_compliance_ratio	
booked_window_utilisation_ratio		

协议复演与治理覆盖 (simulation.json 离线合成)

simulation_task_count	80	tool_schema_pass_rate	100%
simulation_negative_branch_count	55	audit_completeness	100%
token_protocol_rule_count	10	scenario_data_boundary_count	12
simulation_success_rate	100%	scenario_human_review_count	12

面积一致性校核

用地图层合计 - 提交边界面积	12.0 sqm (0.0001%)
重点区复算 - 公告面积	+8,893.0 sqm (+0.24%)
提交边界复算 - 公告面积	+12,825 sqm

自检 self_check.json

- DETERMINISTIC_VALIDATION · pass · blocking

deterministic_validation: PASS
- SPATIAL_REVIEW · pass · blocking

spatial_review: PASS
- VISUAL_PACKAGING · pass · blocking

visual_review: PASS
- PROFESSIONAL_EVIDENCE · pass · blocking

professional_review: PASS

合规矩阵 compliance_matrix.json

任务号	任务名称	图层	指标	图纸	来源
1.3.1	构建世界级AI创新生态体系	2	2	2	2
1.3.2	建设适配AI新质生产力的新型城市形态	2	2	1	2
1.3.3	打造全球AI创新人才向往的高品质城区	2	3	1	2
1.4.1	统筹研究范围	1	1	1	2
1.4.2	总体设计范围	2	2	2	2
1.4.3	重点区域范围	1	5	1	2
1.5.1.1	统筹研究范围：AI创新生态体系	2	2	1	2
1.5.1.2	统筹研究范围：适配人工智能的未来城市形态	2	2	2	2
1.5.2.1	总体设计范围：产业目标与功能布局	2	3	1	2
1.5.2.2	总体设计范围：城市更新总体框架	3	3	2	2
1.5.2.3	总体设计范围：交通轨道市政配套设施	2	4	1	2
1.5.2.4	总体设计范围：京张遗址公园活力带	3	4	1	2
1.5.2.5	总体设计范围：城市风貌	2	2	2	2
1.5.3.required	重点区域详细设计必选项	4	2	2	2
1.5.3.1	众智园AI自主创新加速区	3	2	1	2
1.5.3.2	北京AI原点社区	3	3	1	2
1.5.3.3	大钟寺AI产业聚集区	3	2	1	2
agent.1	一带总体概念与功能统筹方案设计	3	2	2	2
agent.2	AI全栈自主创新体系与世界级AI创新生态设计	3	2	1	2
agent.3	AI+场景赋能新范式与智能化AI活力城市设计	3	3	2	2
agent.4	AI公共空间、智能原生新业态与朝圣地标设计	3	4	1	2
agent.5	百年京张文化、中关村文化与AI新文化融合叙事设计	2	2	1	2
agent.6	一带全球AI创新活动体系与长期运营设计	3	4	1	2

标准与成果深度响应

PROJECT-OFFICIAL-ANNOUNCEMENT 项目任务书	addressed	PROJECT-AGENT-OPEN-CALL-TASKBOOK 智能体开源征集	addressed
MOHURD-URBAN-DESIGN-MEASURES 城市设计	addressed	MOHURD-CONTROL-DETAILED-PLANNING 控规深度	addressed
MNR-LAND-USE-CLASSIFICATION-GUIDE 用地分类	addressed	MOHURD-ARCH-DESIGN-DEPTH-2016 建筑深度	addressed

成果深度 design_depth_matrix.json (15 项)

现状诊断与问题清单	complete	三层范围工作框架	complete
总体空间结构	complete	用地布局	complete
开发强度或待确认控规条件	complete	建筑高度、体量与风貌	complete
拆改留分类方法	complete	交通、轨道、慢行与停车	complete
市政与新型基础设施	complete	蓝绿与公共空间系统	complete
三处重点区域详细设计	complete	更新项目清单	complete
分期实施	complete	指标体系与面积复算	complete
风险与缺资料清单	complete		

口径与红线

- 第一类可复算空间指标已全部复算并写入 metrics.json；第二类管控指标登记为 unknown 并给出原因；第三类绩效指标进入 assumptions 与后续观测。
- 提交边界为仓库临时粗略边界 (official_boundary=false)，不得作为官方红线或精确面积依据；官方 polygon 发布后须整体重算，不能只替换单个文件。
- 本方案不声称官方批准、审定控规、最终土地权属、最终建设规模或保证实施。