


REN-Track · Overall Concept

Centennial Jing-Zhang AI Innovation Belt — overall concept

One belt · three areas · two wings · REN loop | Overall structure: belt · key areas · wings · REN collaboration loop

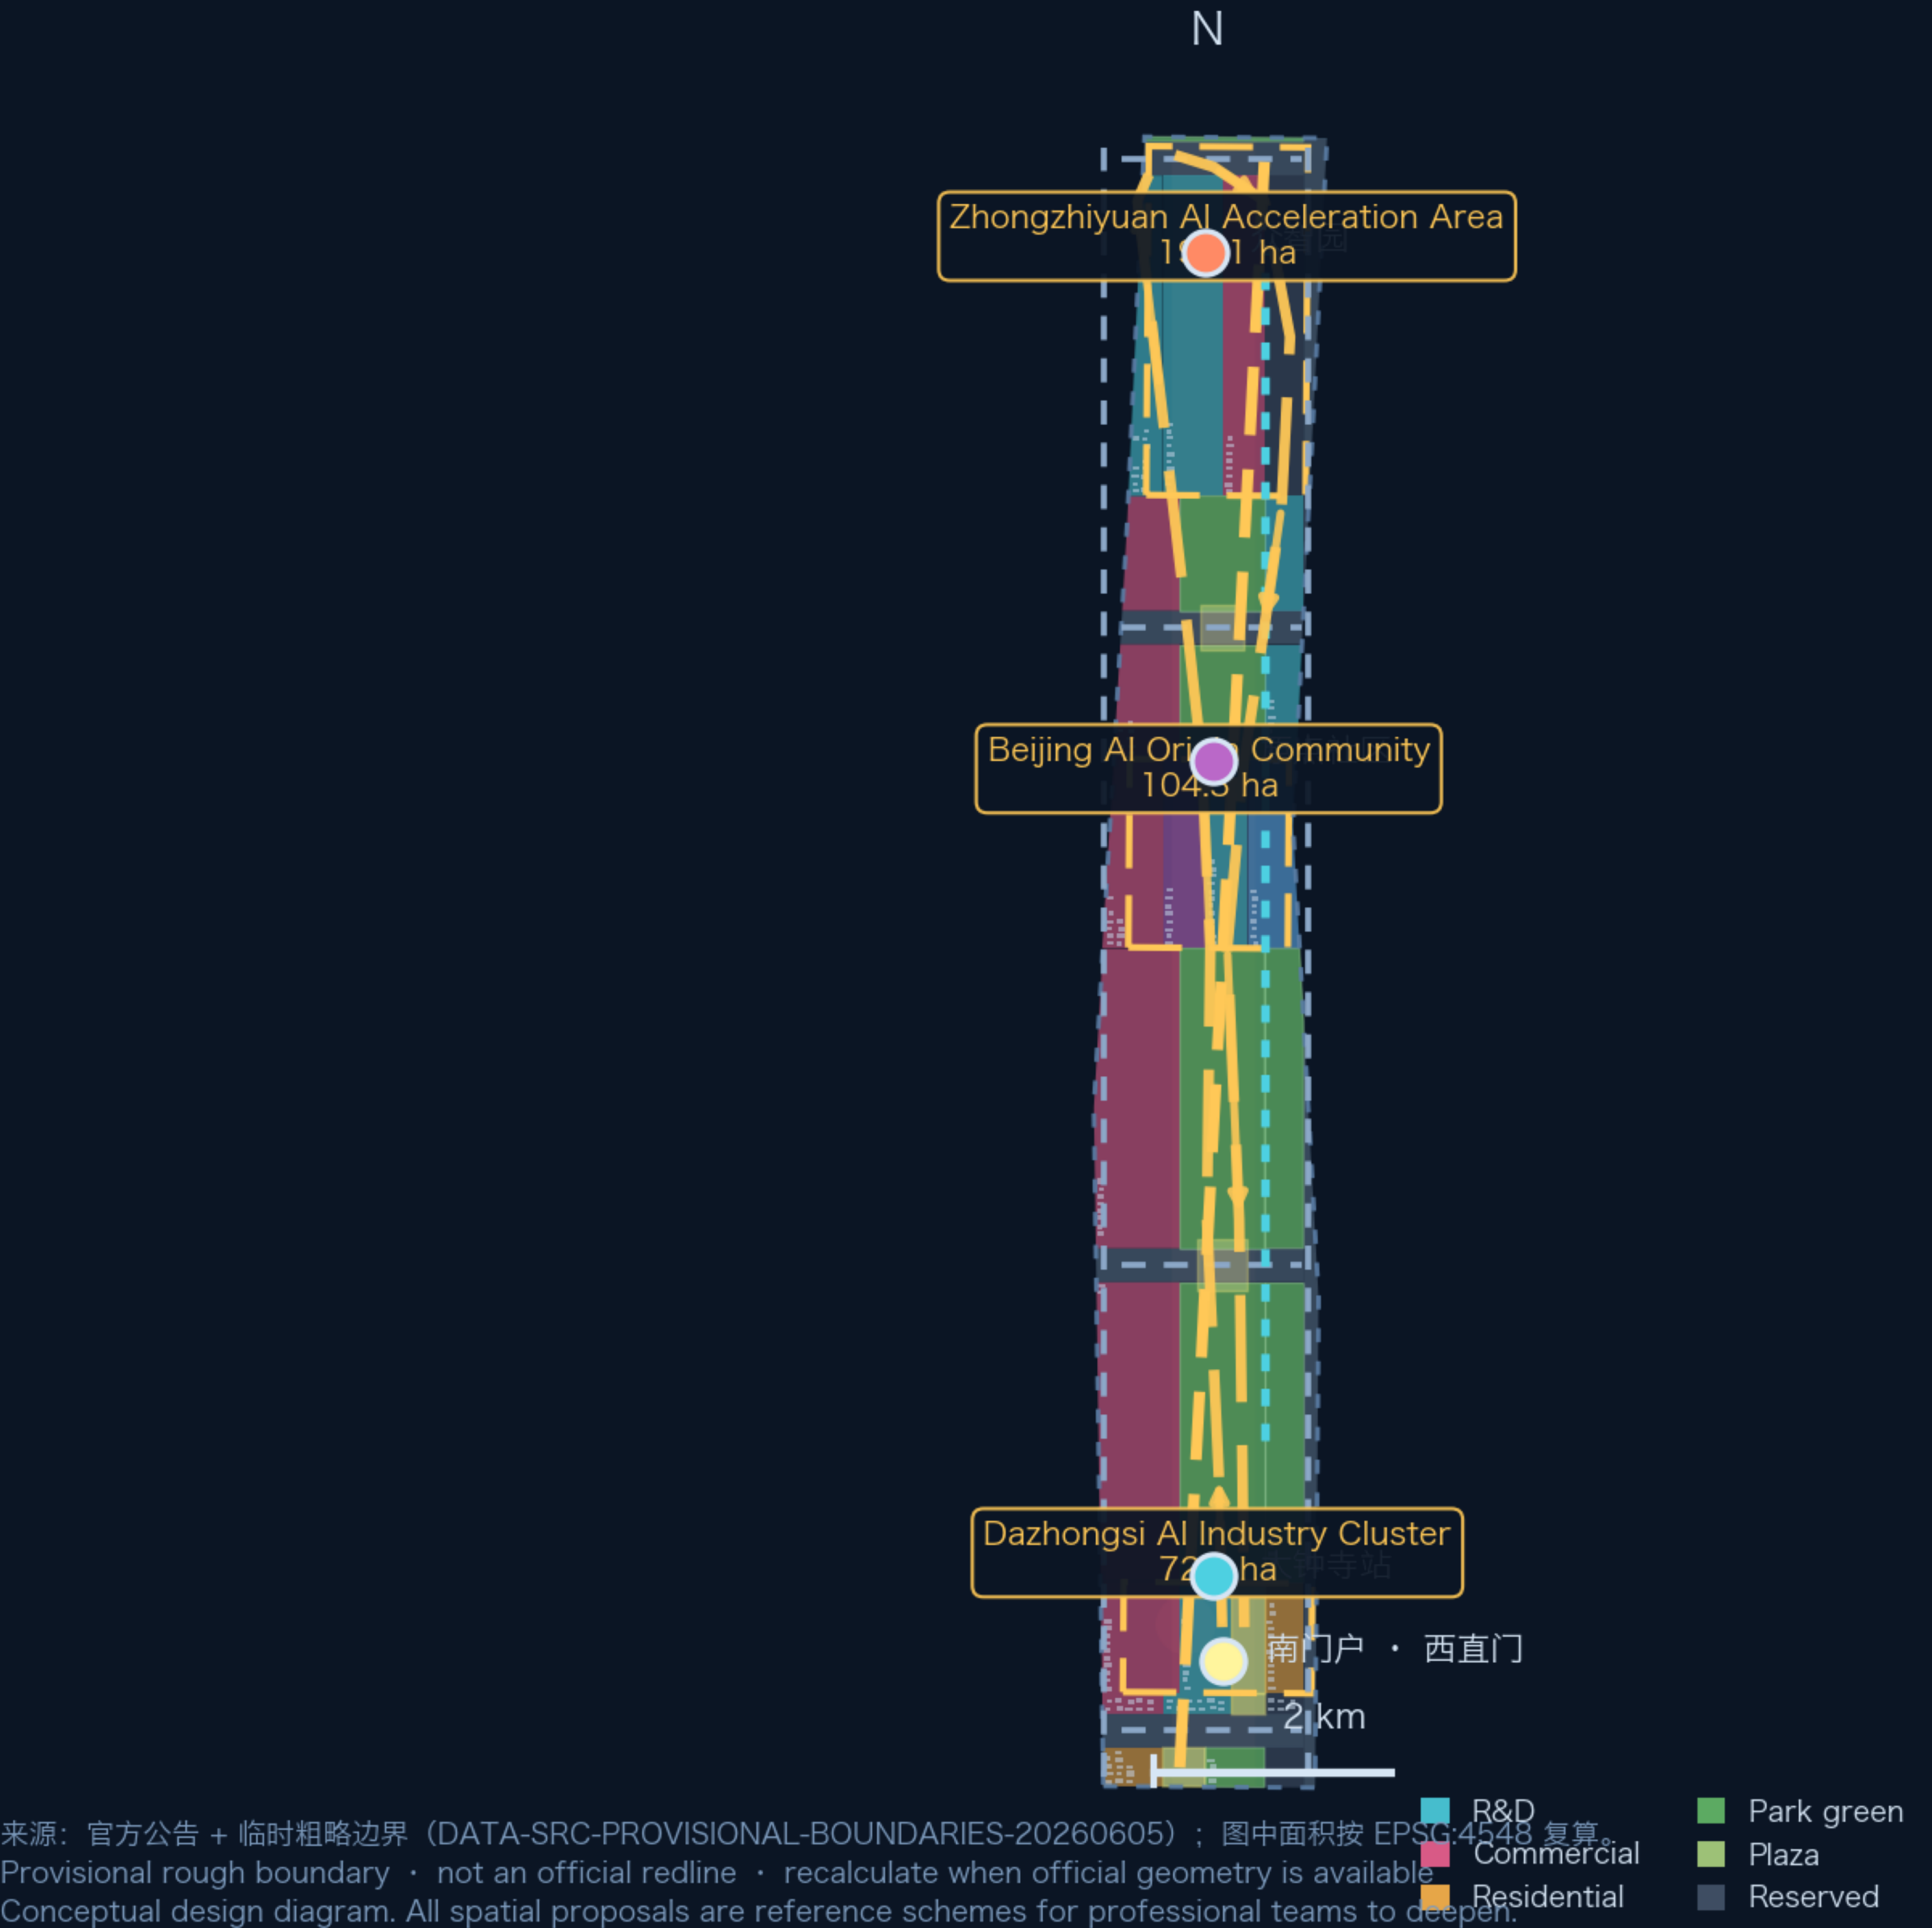

REN loop · three areas, two wings

The heritage zigzag (人) line of the Jing-Zhang Railway inspires a collaboration loop linking Dazhongsi - Origin Community - Zhongzhiyuan with the ZGC tech-service and Xiaoyuehe scenario wings.

Three positionings


Centennial Jing-Zhang cultural belt
Urban AI-life experience belt
AI-integration innovation belt

Five functions

Full-stack autonomous AI innovation
World-class AI ecosystem · AI+ scenario paradigm
Smart vibrant AI city · Global AI governance voice

Scope cascade

Research 43.6 km²
Overall design 11.4 km²
Key areas 368.4 ha

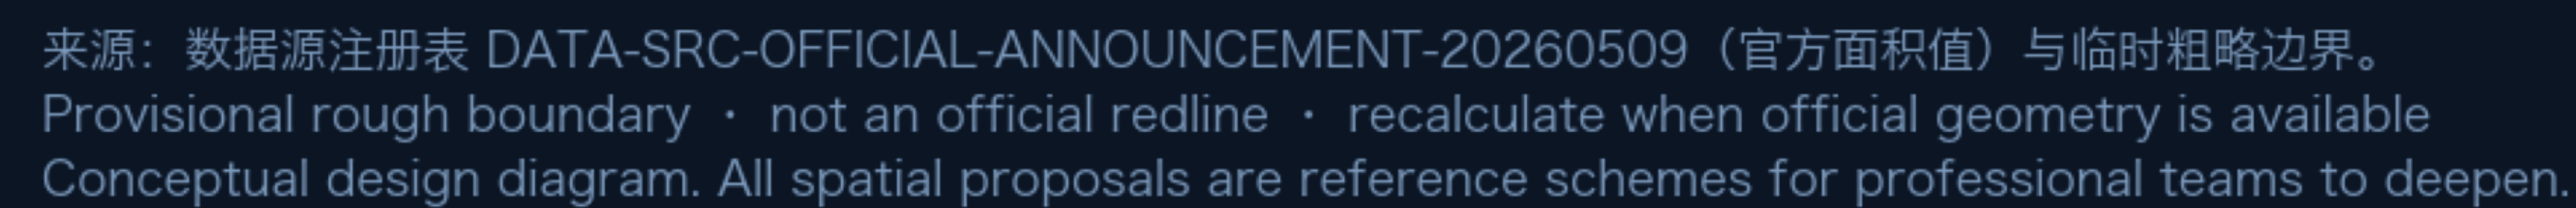


Land Use Type	Percentage
R&D	15.6%
Commercial	29.4%
Residential	2.0%
Cultural	2.4%
Education	2.8%
Park green	29.4%
Plaza	1.9%
Road	12.0%
Reserved	4.5%
(Unlabeled)	0.0%

Key areas
368.4 ha

Mobility, Rail and Blue-Green Network

Roads · rail intermodal · slow-mobility spine · green-blue network

Continuous slow spine · station integration · blue-green continuity | AI+ mobility and continuous blue-green public space

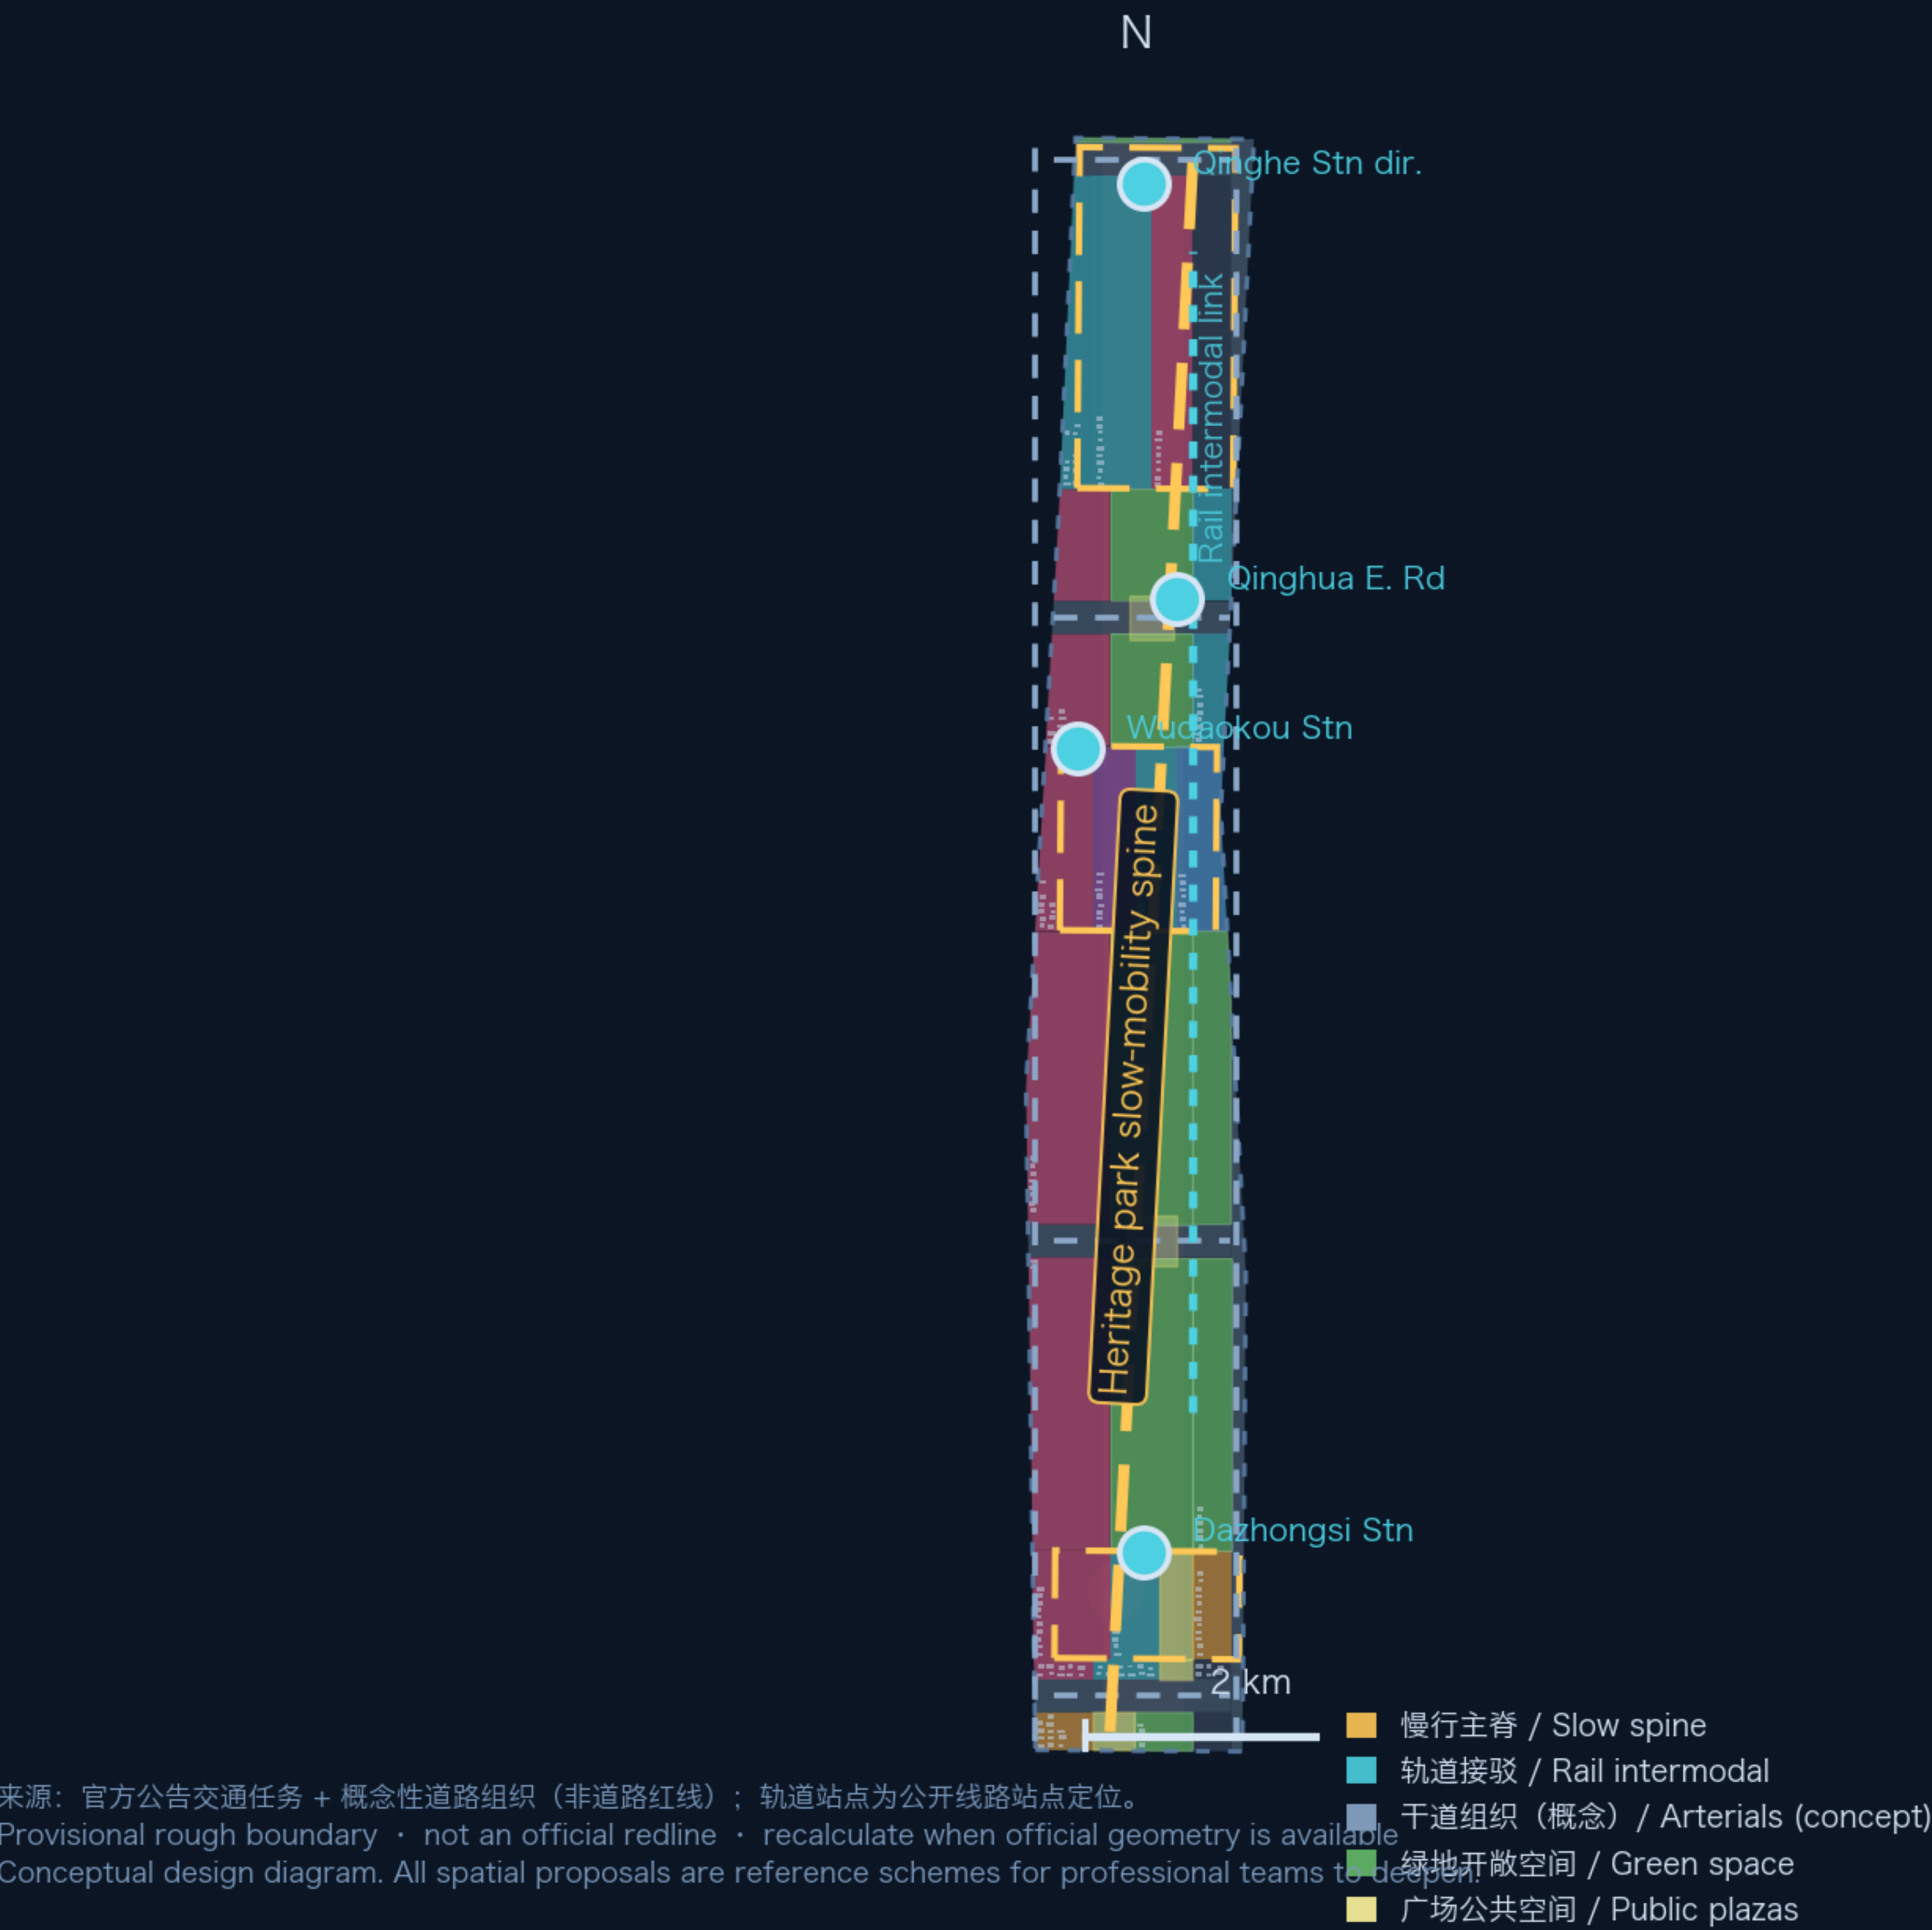

Slow-mobility continuity

The heritage park belt forms the slow spine linking the three key areas; gap-mending plus over/under-pass concepts are directional, pending engineering study.

Station integration

TOD concepts around Dazhongsi, Wudaokou, Qinghua E. Rd; four-quadrant walking connectivity and bike parking at the Dazhongsi station plaza.

Blue-green network

Qinghe - Xiaoyuehe - heritage park form a continuous blue-green skeleton serving AI scenarios: testing, display, exchange.


New infrastructure

Conceptual integration of edge compute, distributed energy with conventional municipal facilities as AI service layout.

Mobility, Rail and Blue-Green Network

Roads · rail intermodal · slow-mobility spine · green-blue network

Continuous slow spine · station integration · blue-green continuity | AI+ mobility and continuous blue-green public space

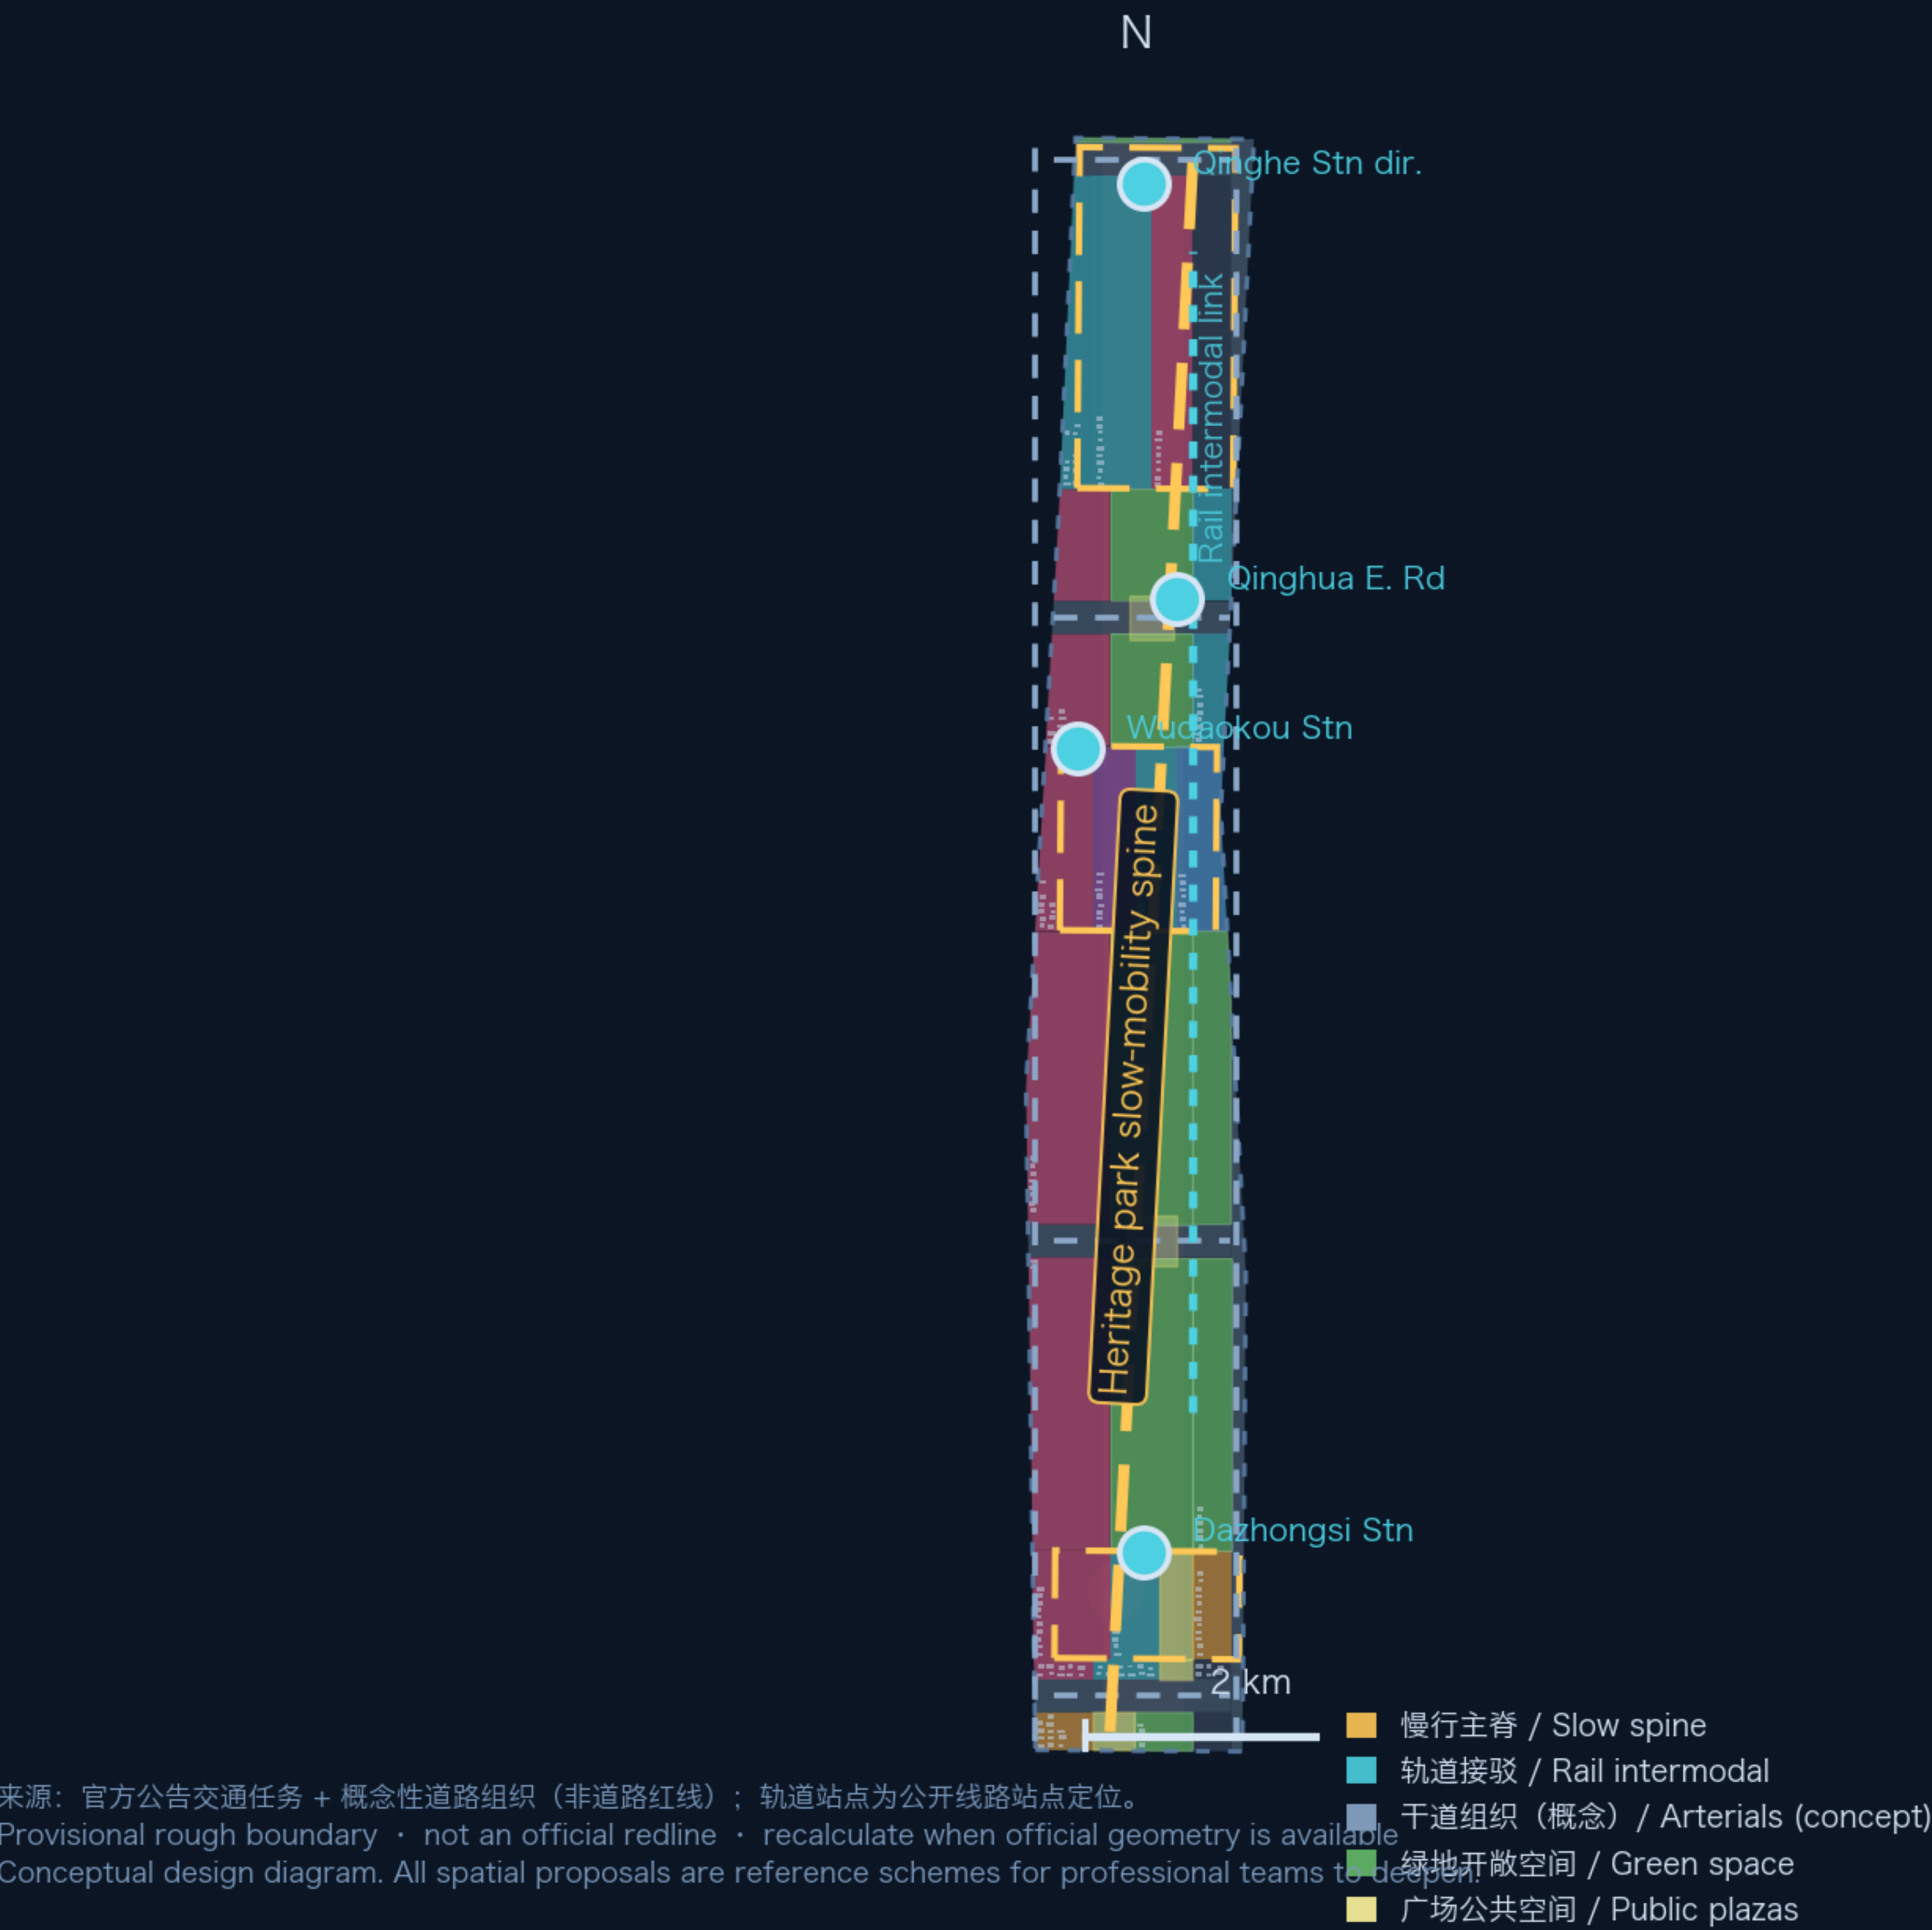

Slow-mobility continuity

The heritage park belt forms the slow spine linking the three key areas; gap-mending plus over/under-pass concepts are directional, pending engineering study.

Station integration

TOD concepts around Dazhongsi, Wudaokou, Qinghua E. Rd; four-quadrant walking connectivity and bike parking at the Dazhongsi station plaza.

Blue-green network

Qinghe - Xiaoyuehe - heritage park form a continuous blue-green skeleton serving AI scenarios: testing, display, exchange.

New infrastructure

Conceptual integration of edge compute, distributed energy with conventional municipal facilities as AI service layout.

Detailed Design of the Three Key Areas

Zhongzhiyuan · AI Origin Community · Dazhongsi

Fine-grained design · retain-renovate-demolish · AI scenarios | Three key areas at planning-implementation depth

Garden-type AI innovation block · national AI cluster
Full-stack autonomous innovation · standards & safety
National AI platform · Qinghe culture · 5th Ring linkage
Scenarios: full-stack pilot line · compute orchestration hall
Risk: external access relies on 5th Ring; official boundary pending




Zhongzhiyuan AI Acceleration Area · 192.1 ha

Campus-adjacent AI innovation block · talent zone
Incubation & commercialization · open-source · events
Wudaokou/Qinghua East Rd station TOD · low-impact renewal
Scenarios: AI origin museum · open-source community lounge
Risk: campus-park-block integration, multiple operators

Beijing AI Origin Community · 104.3 ha

Urban AI innovation block · intelligent economy
Agents / smart devices / content consumption · data assets
Station 4-quadrant connectivity · green compound use
Scenarios: smart retail street · data-asset pilot zone
Risk: station-city integration with heritage; controls pending

Dazhongsi AI Industry Cluster · 72.0 ha

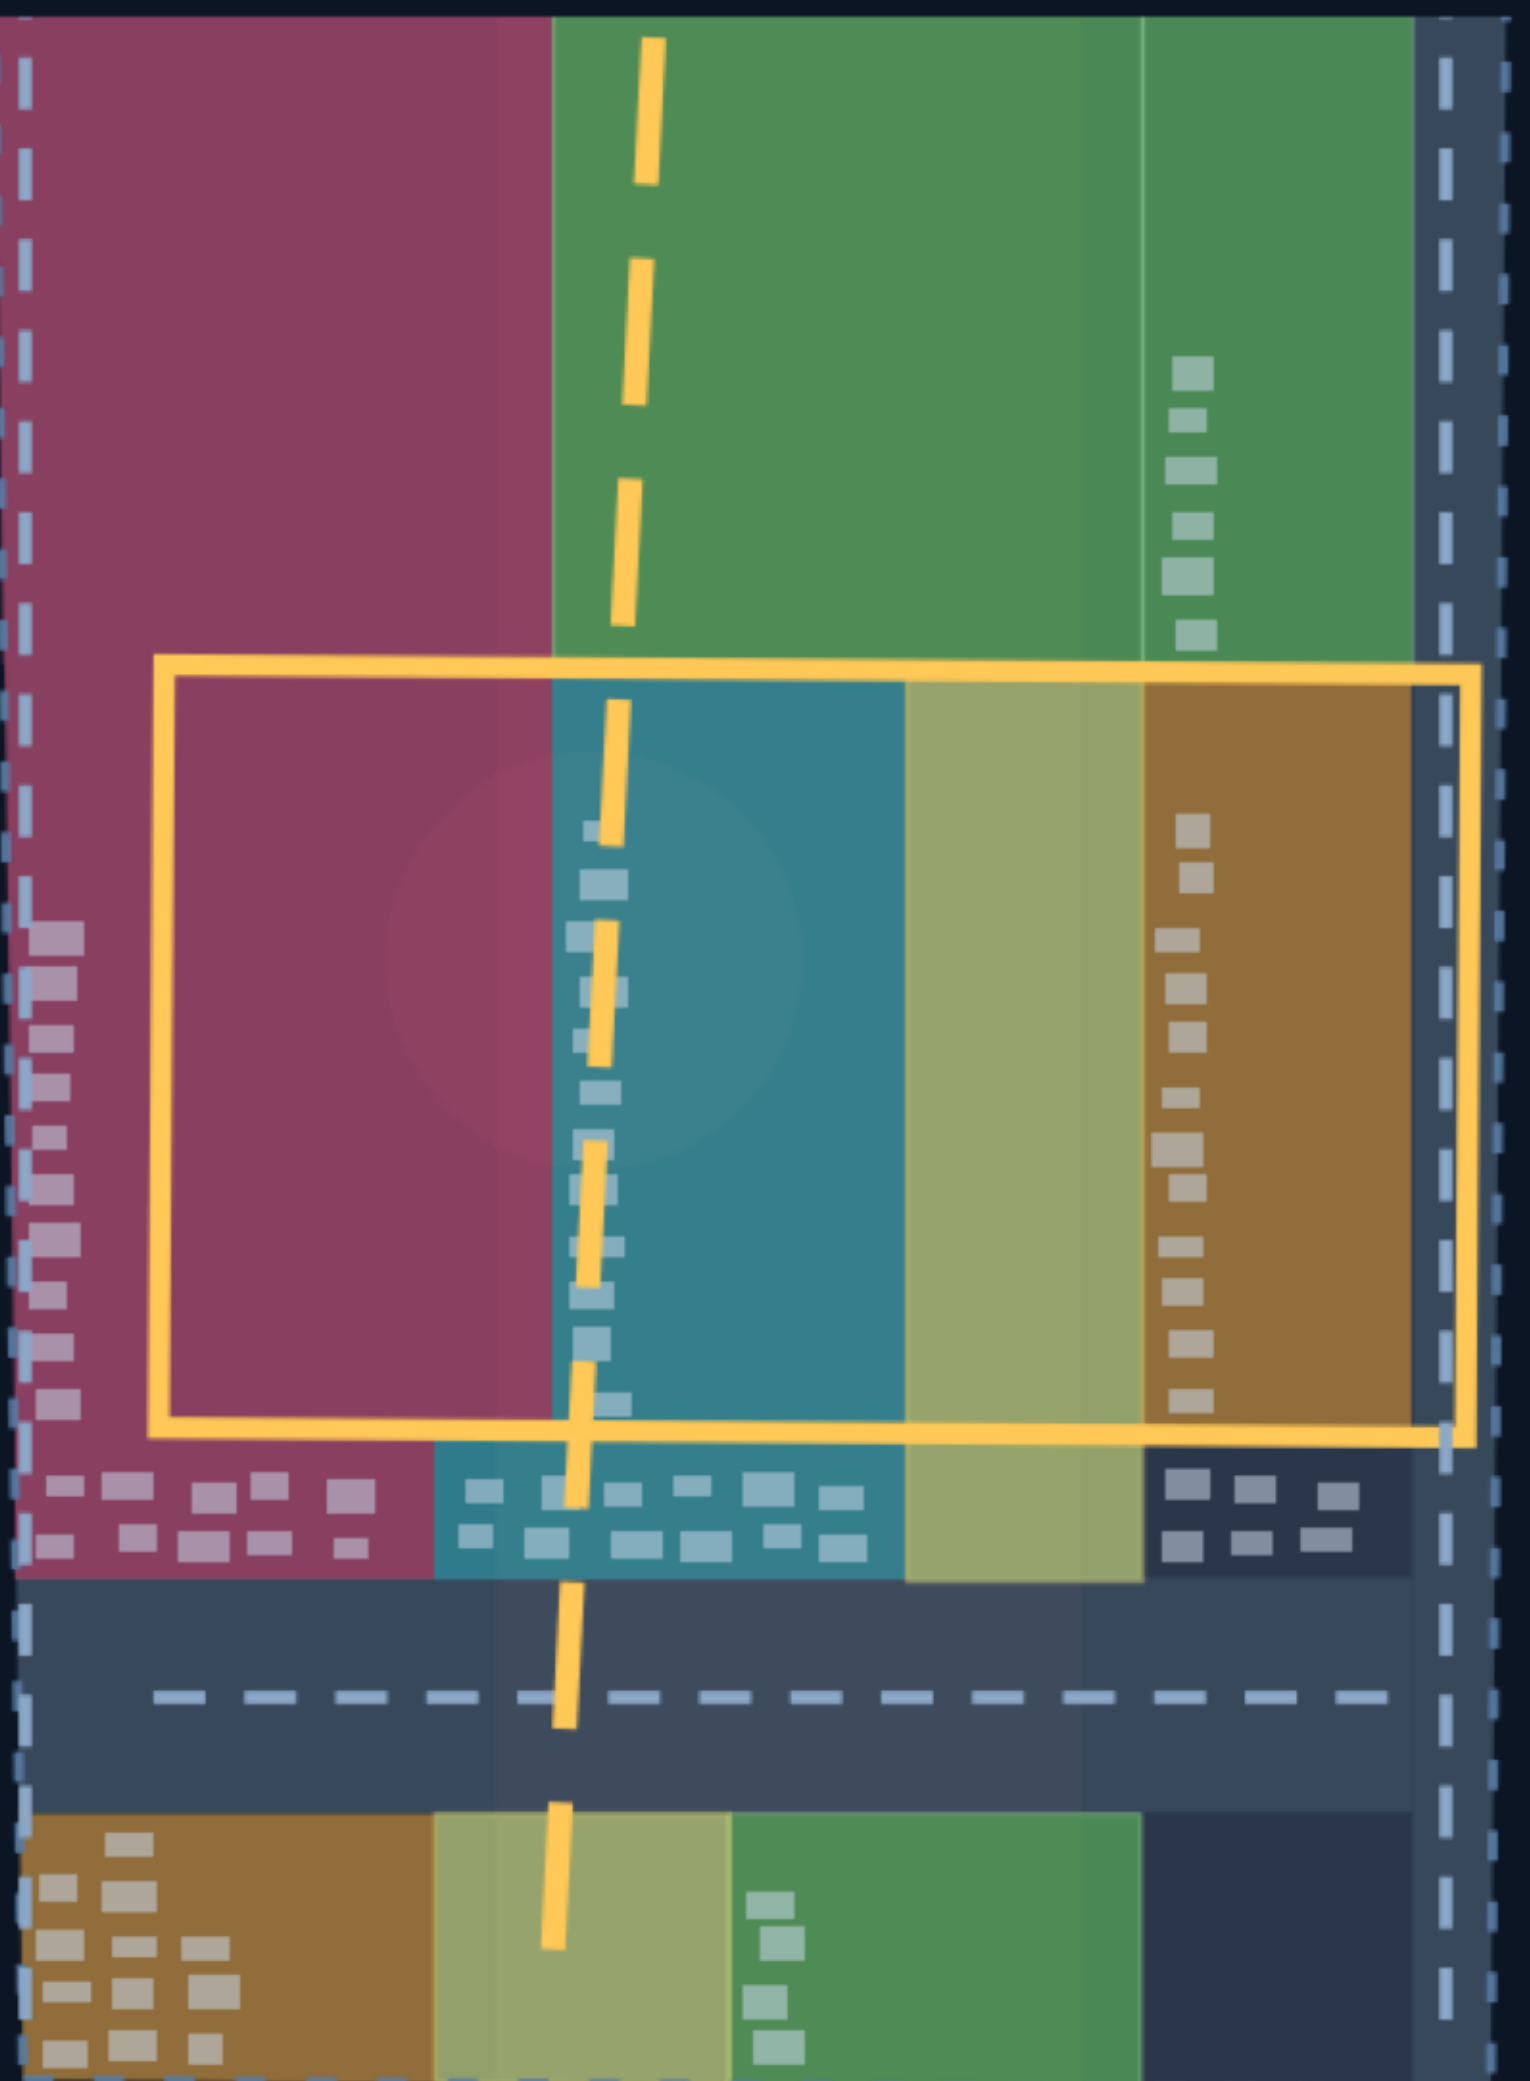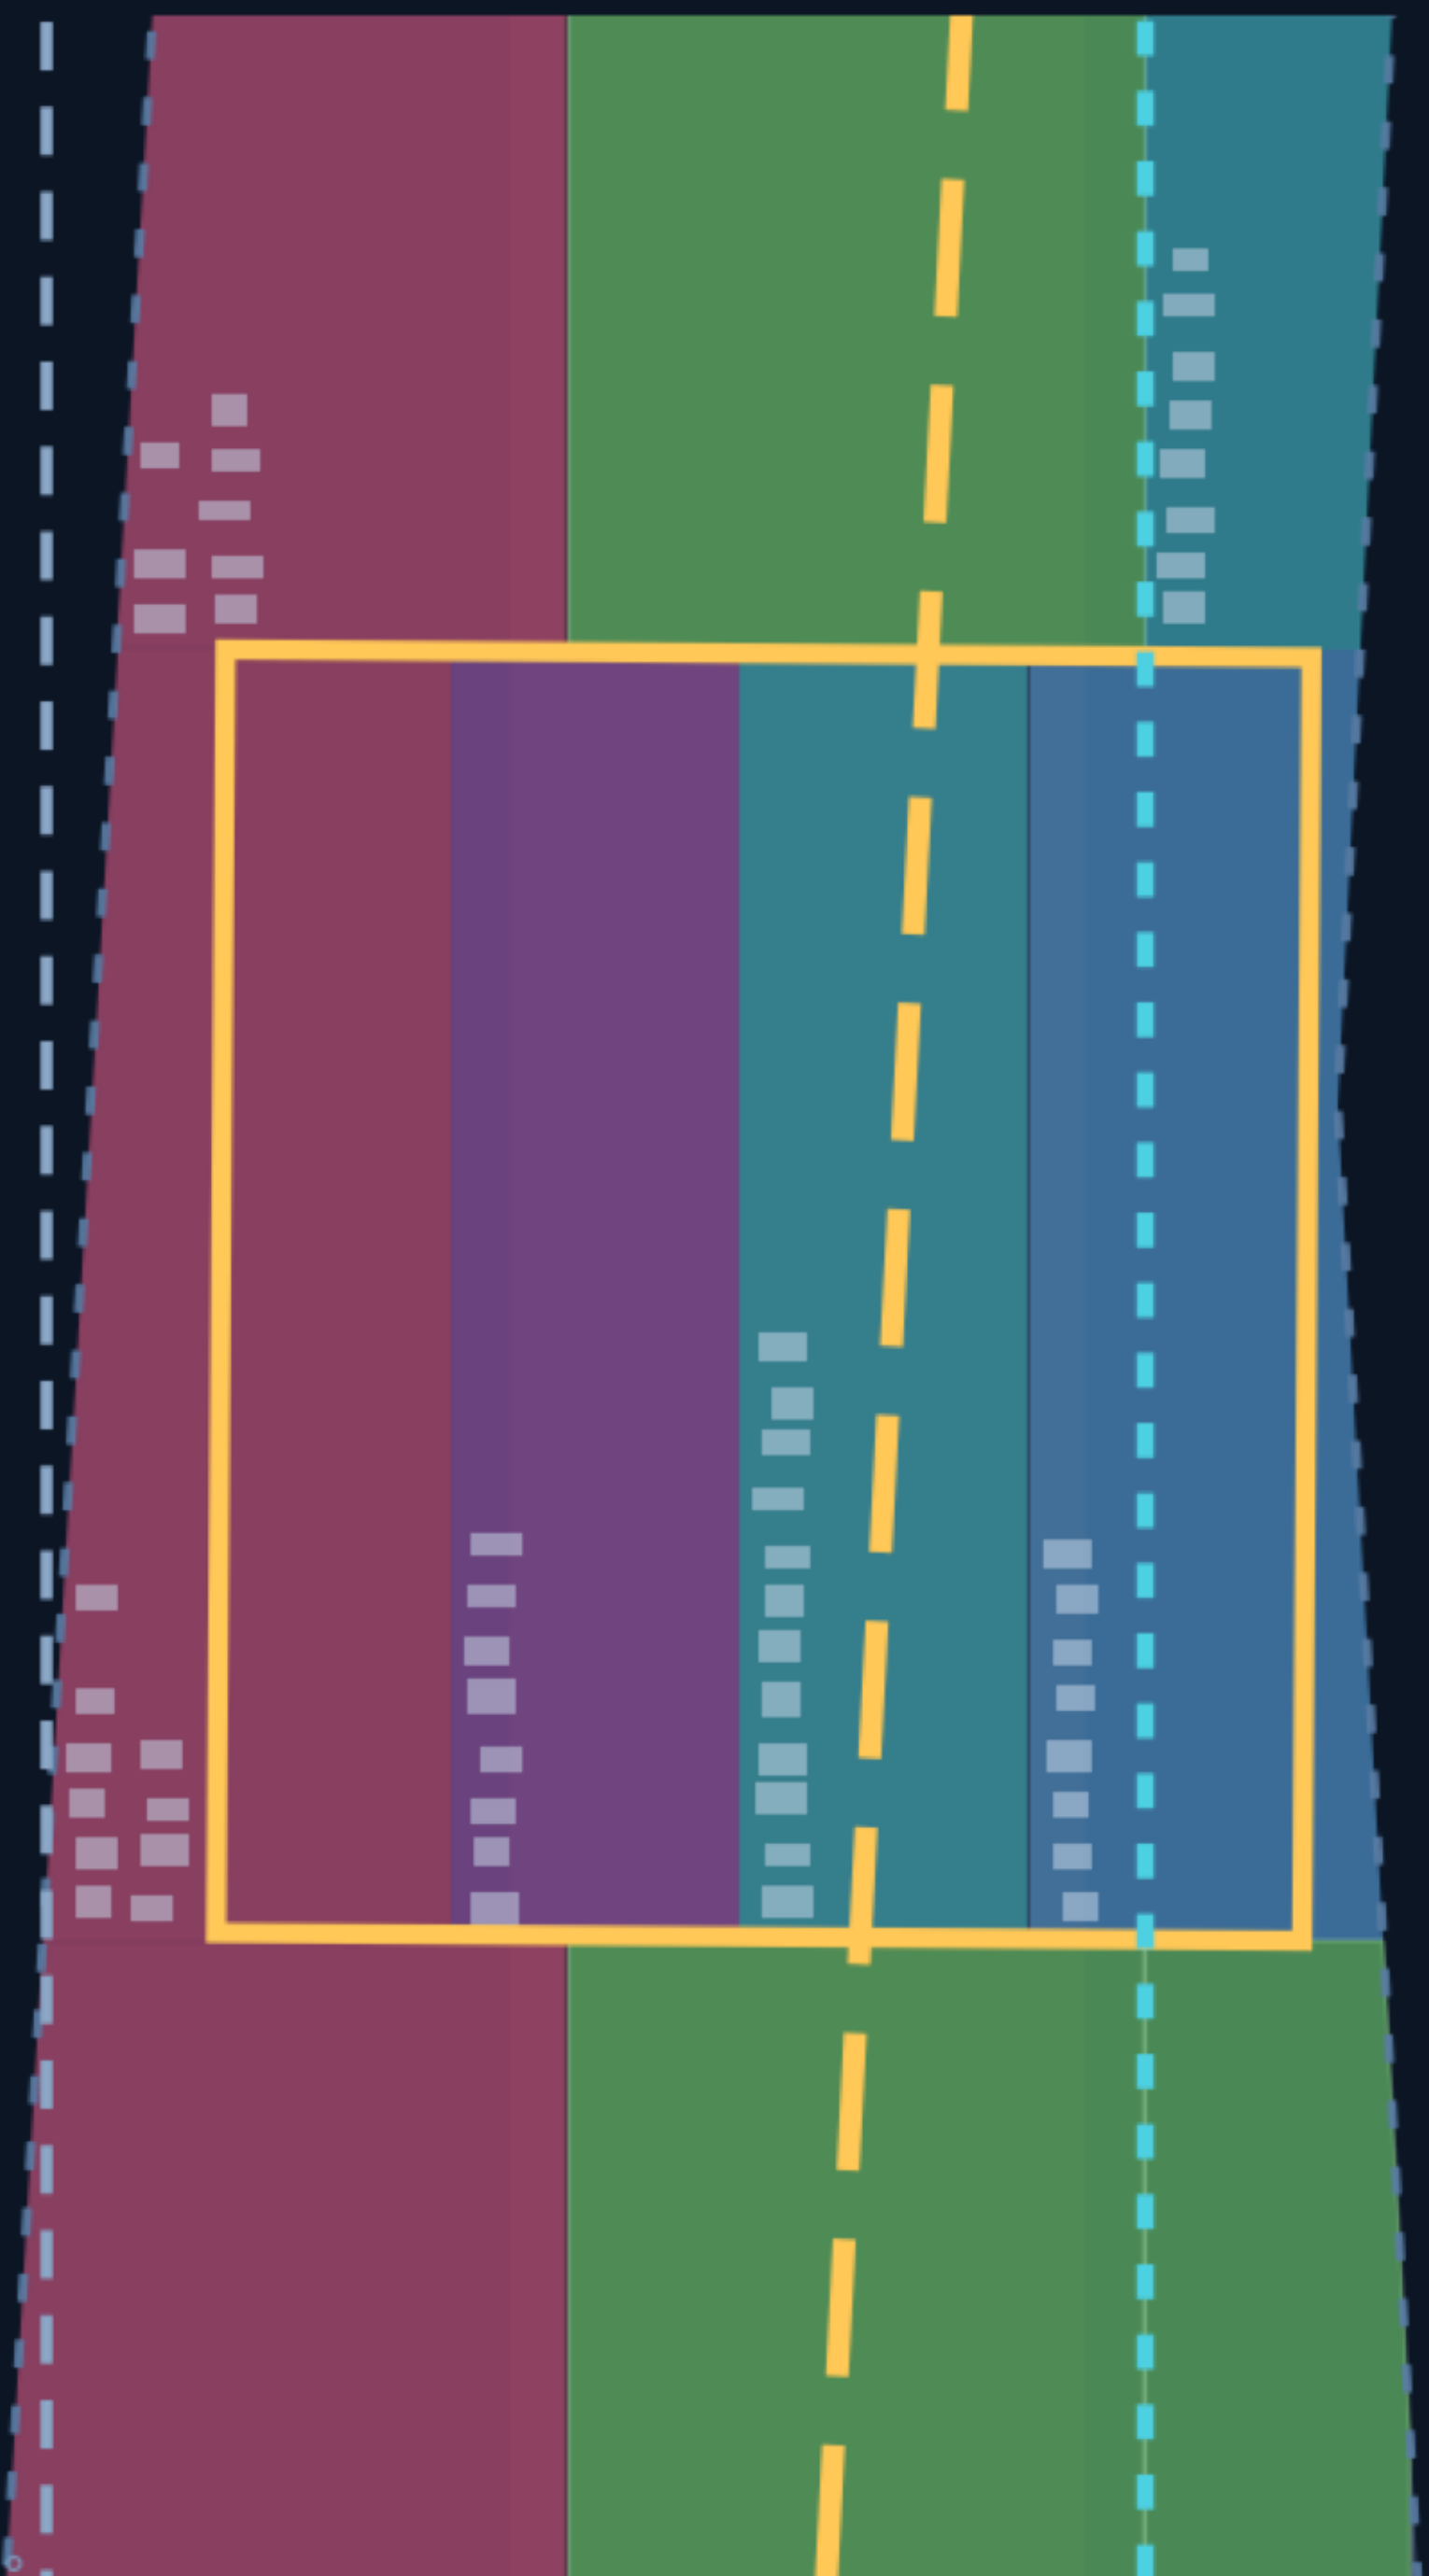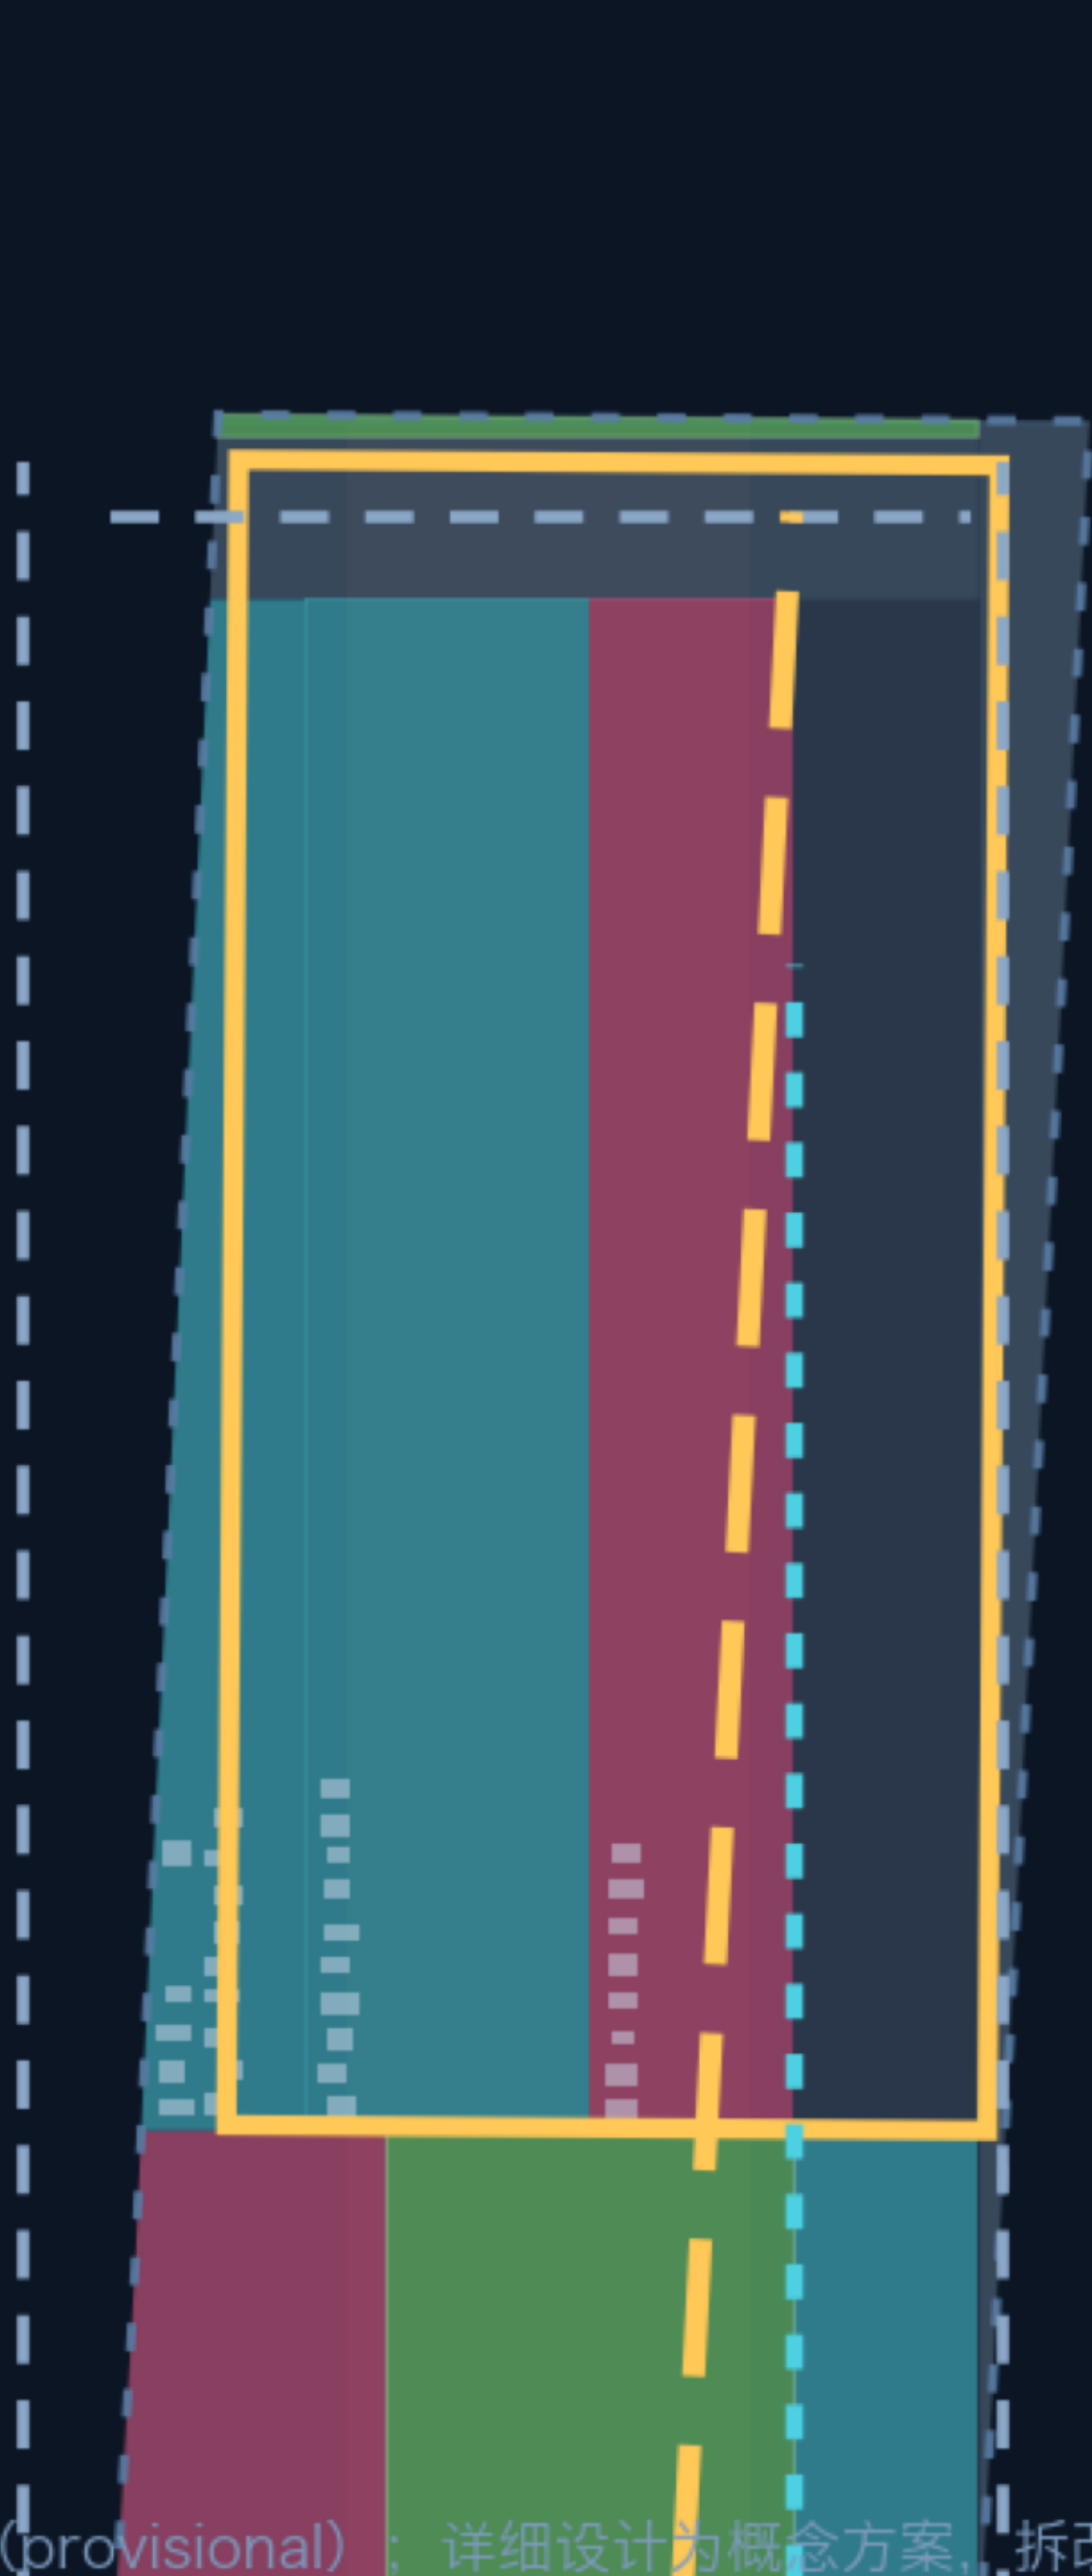

来源：临时粗略重点区范围（provisional）；详细设计的概念方案，拆改留为方向性建议，待官方边界与控规条件补齐后深化。
Provisional rough boundary · not an official redline · recalculate when official geometry is available
Conceptual design diagram. All spatial proposals are reference schemes for professional teams to deepen.

Metrics Recalculation and Evidence Chain

Geometry-derived metrics · statuses · data gaps

Area recalculation in EPSG:4548 · known / pending metrics | All displayed values recomputed from submission geometry

Site area 已复算 11.41 km² Polygon area in EPSG:4548	Green ratio 已复算 29.4 % Green space / site area	Public space ratio 已复算 3.2 % Plazas / site area	Building footprint 已复算 16.5 ha 180 conceptual blocks · density 1.4%
Road centerlines 已复算 39.9 km Conceptual network, not redlines	Key areas 已复算 3 areas Total 369.3 ha (provisional)	Phasing 已复算 Near 468 / Mid 422 / Far 252 ha P1 2026-28 · P2 2028-31 · P3 2031-35	FAR / building scale 待补 Pending official data Official FAR and total building scale not public; not fabricated

GeoJSON layers ▶	EPSG:4548 projection ▶	Area/length recompute ▶	metrics.json ▶	Figures/HTML/drawings ▶	Self-check PASS ▶	Human professional review
------------------	------------------------	-------------------------	----------------	-------------------------	-------------------	---------------------------

Self-check state (rerun locally before submission)

Deterministic validation PASS	Spatial review PASS	Visual packaging PASS	Professional evidence PASS	Bilingual contract PASS
----------------------------------	------------------------	--------------------------	-------------------------------	----------------------------

来源：全部数值由本方案 geometry/*.geojson 在 EPSG:4548 下复算；官方公告面积值见 data/source_registry.json。
Provisional rough boundary · not an official redline · recalculate when official geometry is available
Pending: official redline · official key-area polygons · FAR/height/density controls · road redlines · existing building survey · heritage protection lines
Conceptual design diagram. All spatial proposals are reference schemes for professional teams to deepen.

Metrics Recalculation and Evidence Chain

Geometry-derived metrics · statuses · data gaps

Area recalculation in EPSG:4548 · known / pending metrics | All displayed values recomputed from submission geometry

Site area 已复算 11.41 km² Polygon area in EPSG:4548	Green ratio 已复算 29.4 % Green space / site area	Public space ratio 已复算 3.2 % Plazas / site area	Building footprint 已复算 16.5 ha 180 conceptual blocks · density 1.4%
Road centerlines 已复算 39.9 km Conceptual network, not redlines	Key areas 已复算 3 areas Total 369.3 ha (provisional)	Phasing 已复算 Near 468 / Mid 422 / Far 252 ha P1 2026-28 · P2 2028-31 · P3 2031-35	FAR / building scale 待补 Pending official data Official FAR and total building scale not public; not fabricated

GeoJSON layers ▶	EPSG:4548 projection ▶	Area/length recompute ▶	metrics.json ▶	Figures/HTML/drawings ▶	Self-check PASS ▶	Human professional review
------------------	------------------------	-------------------------	----------------	-------------------------	-------------------	---------------------------

Self-check state (rerun locally before submission)

Deterministic validation PASS	Spatial review PASS	Visual packaging PASS	Professional evidence PASS	Bilingual contract PASS
----------------------------------	------------------------	--------------------------	-------------------------------	----------------------------

来源：全部数值由本方案 geometry/*.geojson 在 EPSG:4548 下复算；官方公告面积值见 data/source_registry.json。
Provisional rough boundary · not an official redline · recalculate when official geometry is available
Pending: official redline · official key-area polygons · FAR/height/density controls · road redlines · existing building survey · heritage protection lines
Conceptual design diagram. All spatial proposals are reference schemes for professional teams to deepen.