



Fig.01 | The Variations at a glance: above the bright line, below the dark line, the smart line between

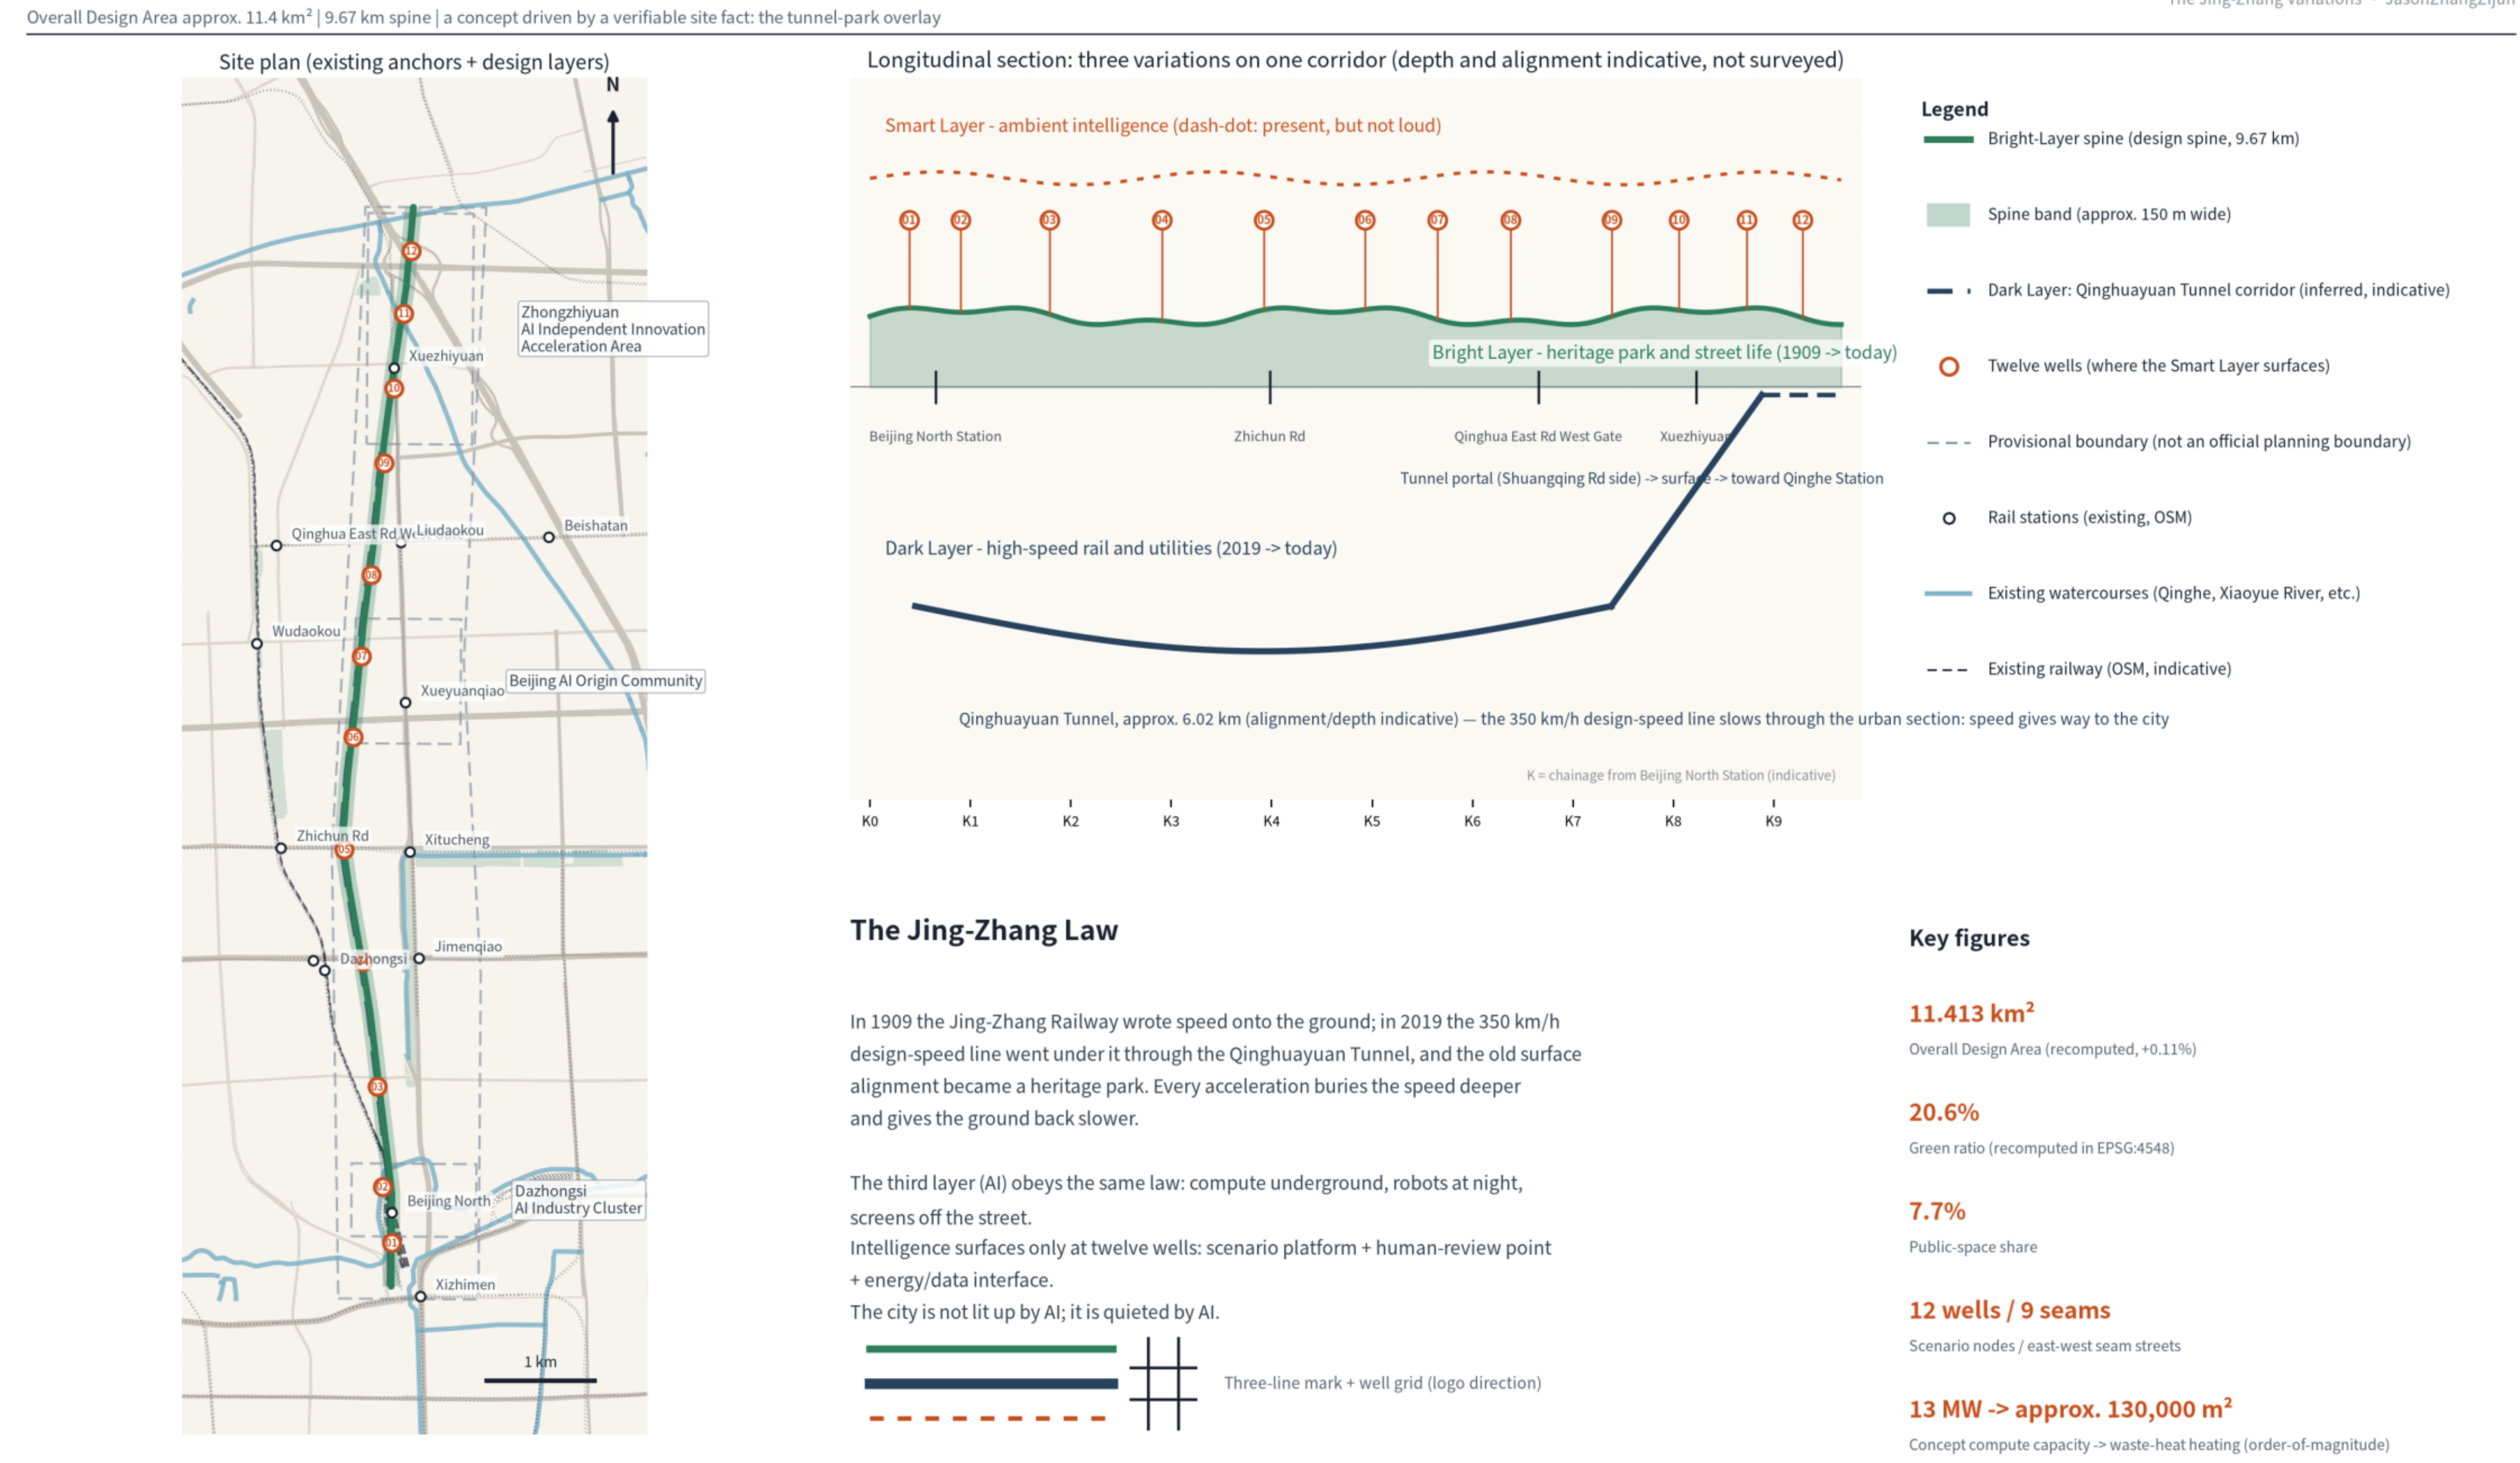


The provisional boundary (official_boundary=false, provisional_rough) is drawn only as a low-contrast dashed constraint and is not an official planning boundary; all areas are recomputed in EPSG:4548. Existing base-map features (c) OpenStreetMap contributors (ODBL), shown for context only. This drawing is a conceptual recommendation for professional teams to develop further.

Fig.02 | Land-use structure: the spine runs north-south, five movements divide it east-west

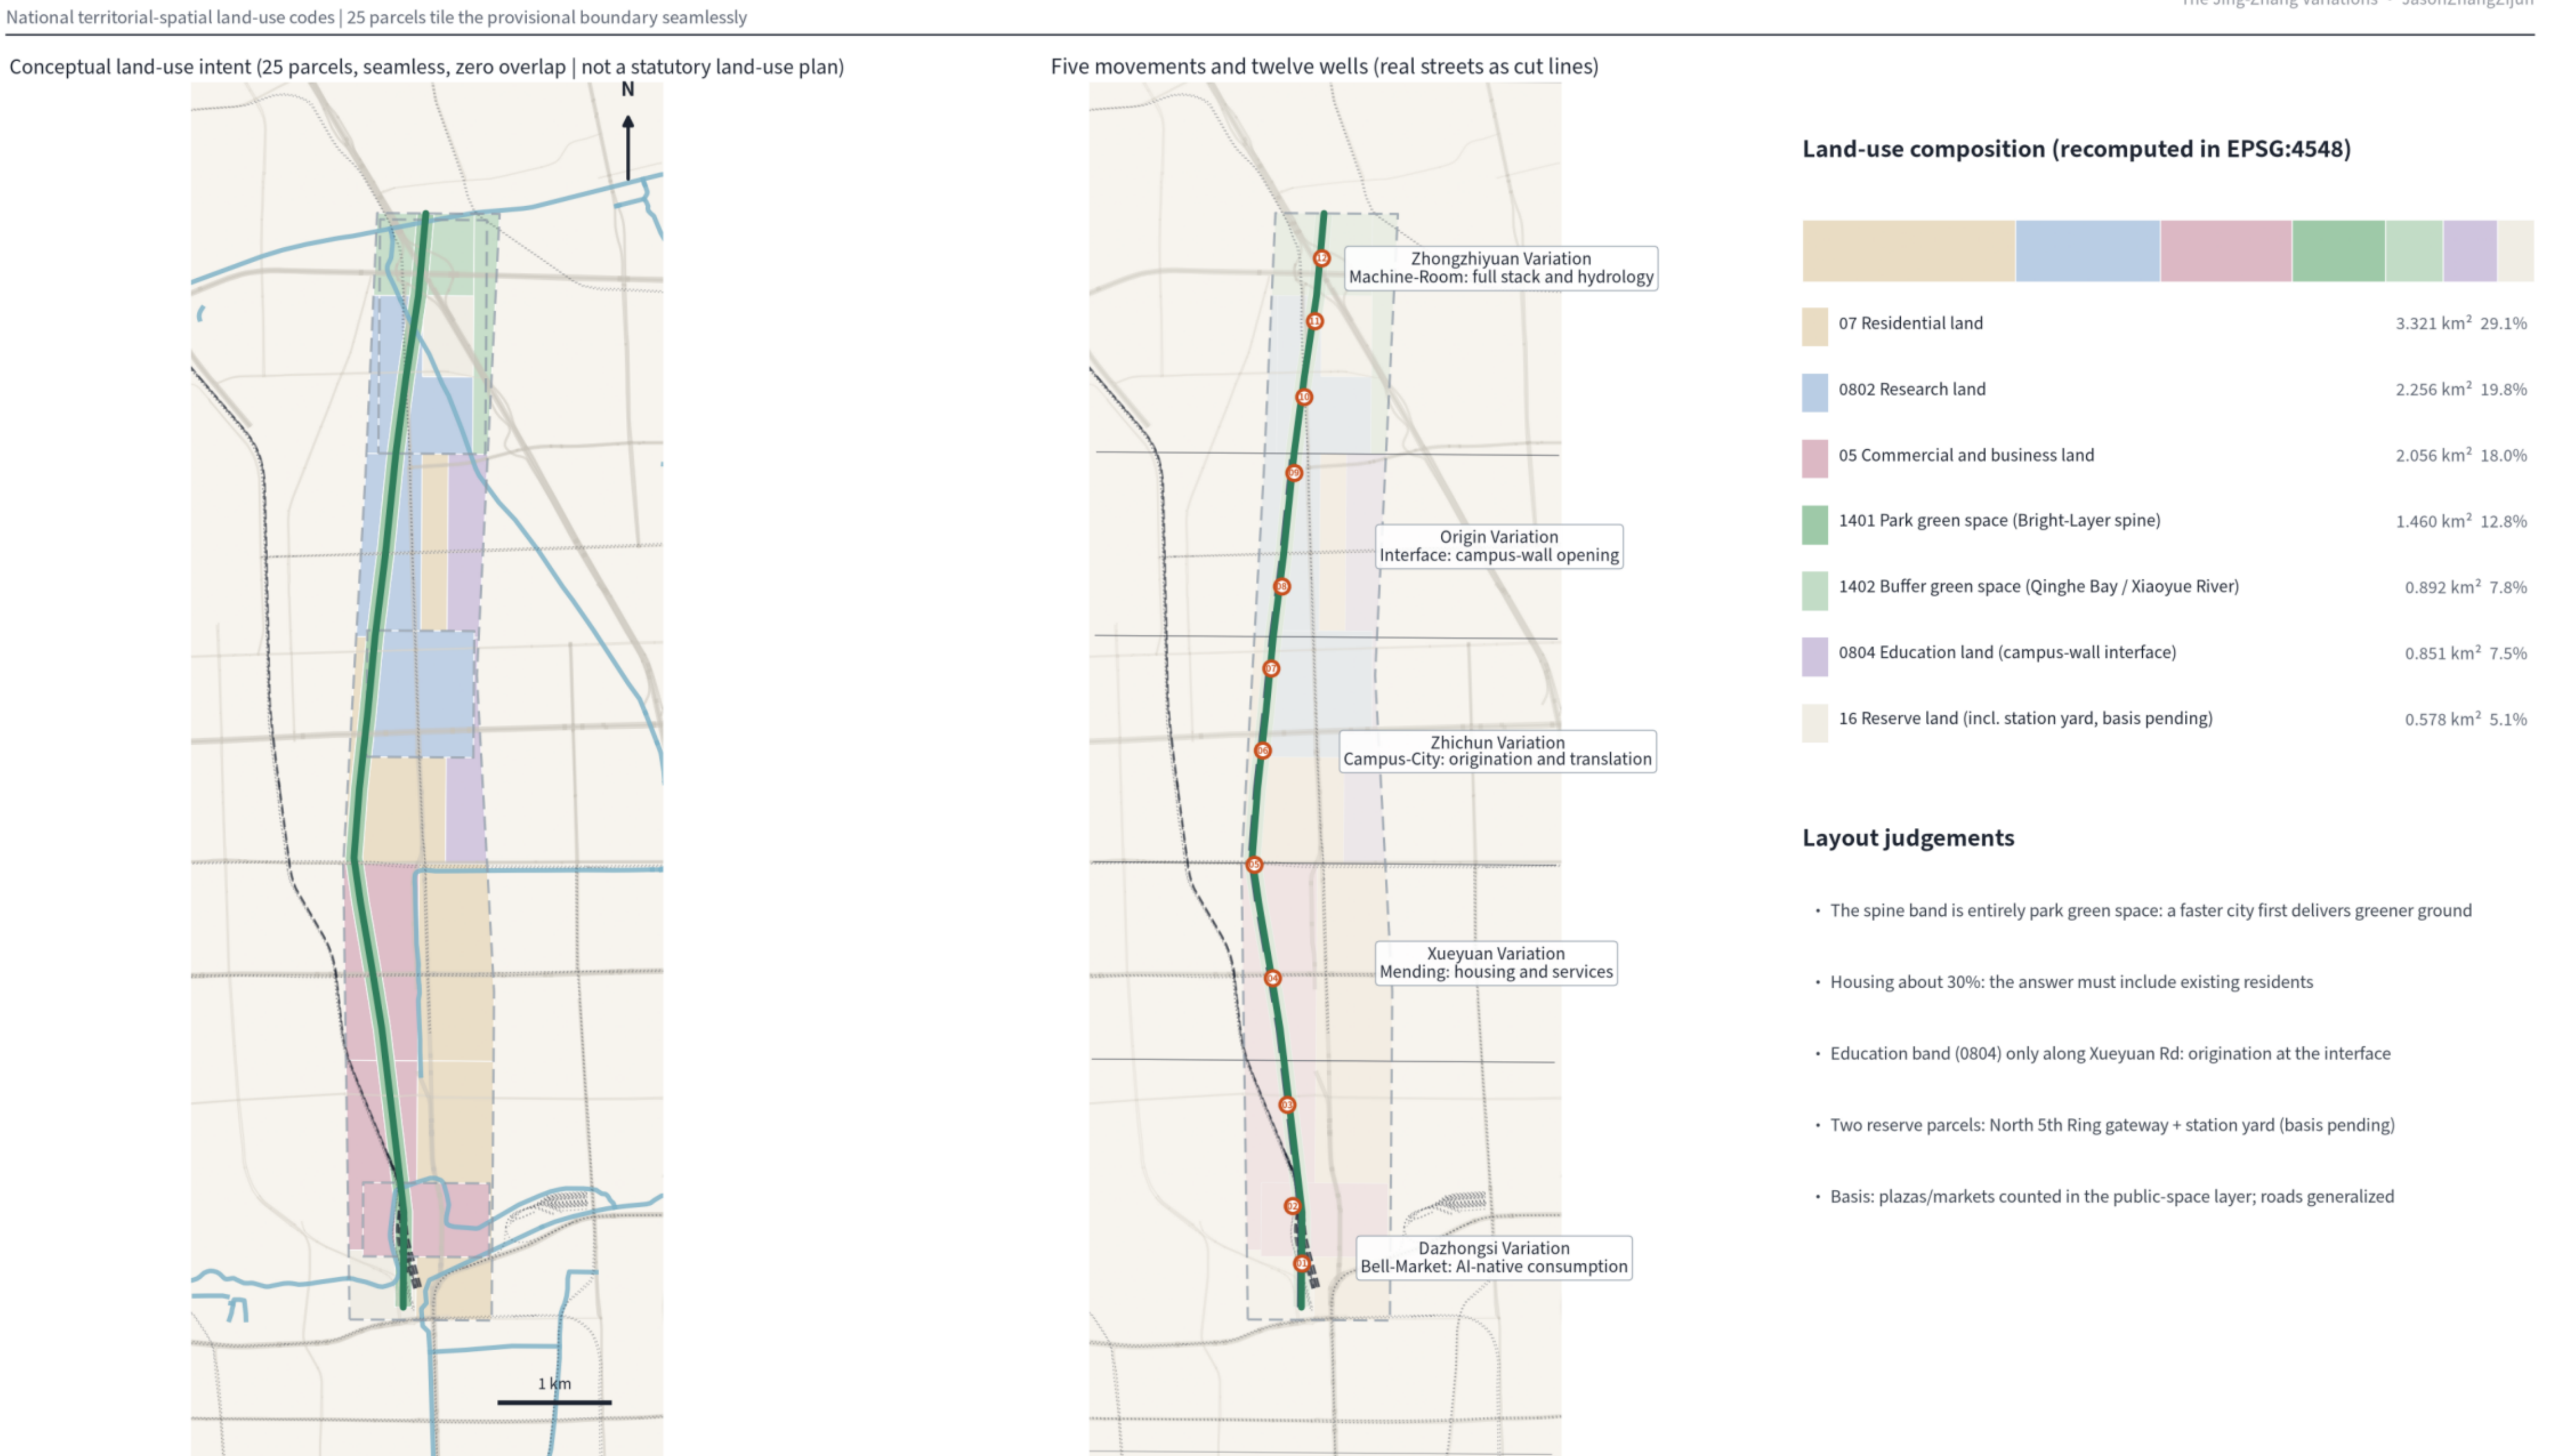


The provisional boundary (official_boundary=false, provisional_rough) is drawn only as a low-contrast dashed constraint and is not an official planning boundary; all areas are recomputed in EPSG:4548. Existing base-map features (c) OpenStreetMap contributors (ODBL), shown for context only. This drawing is a conceptual recommendation for professional teams to develop further.

Fig.03 | Three key areas: Bell-Market, Campus-City, Machine-Room

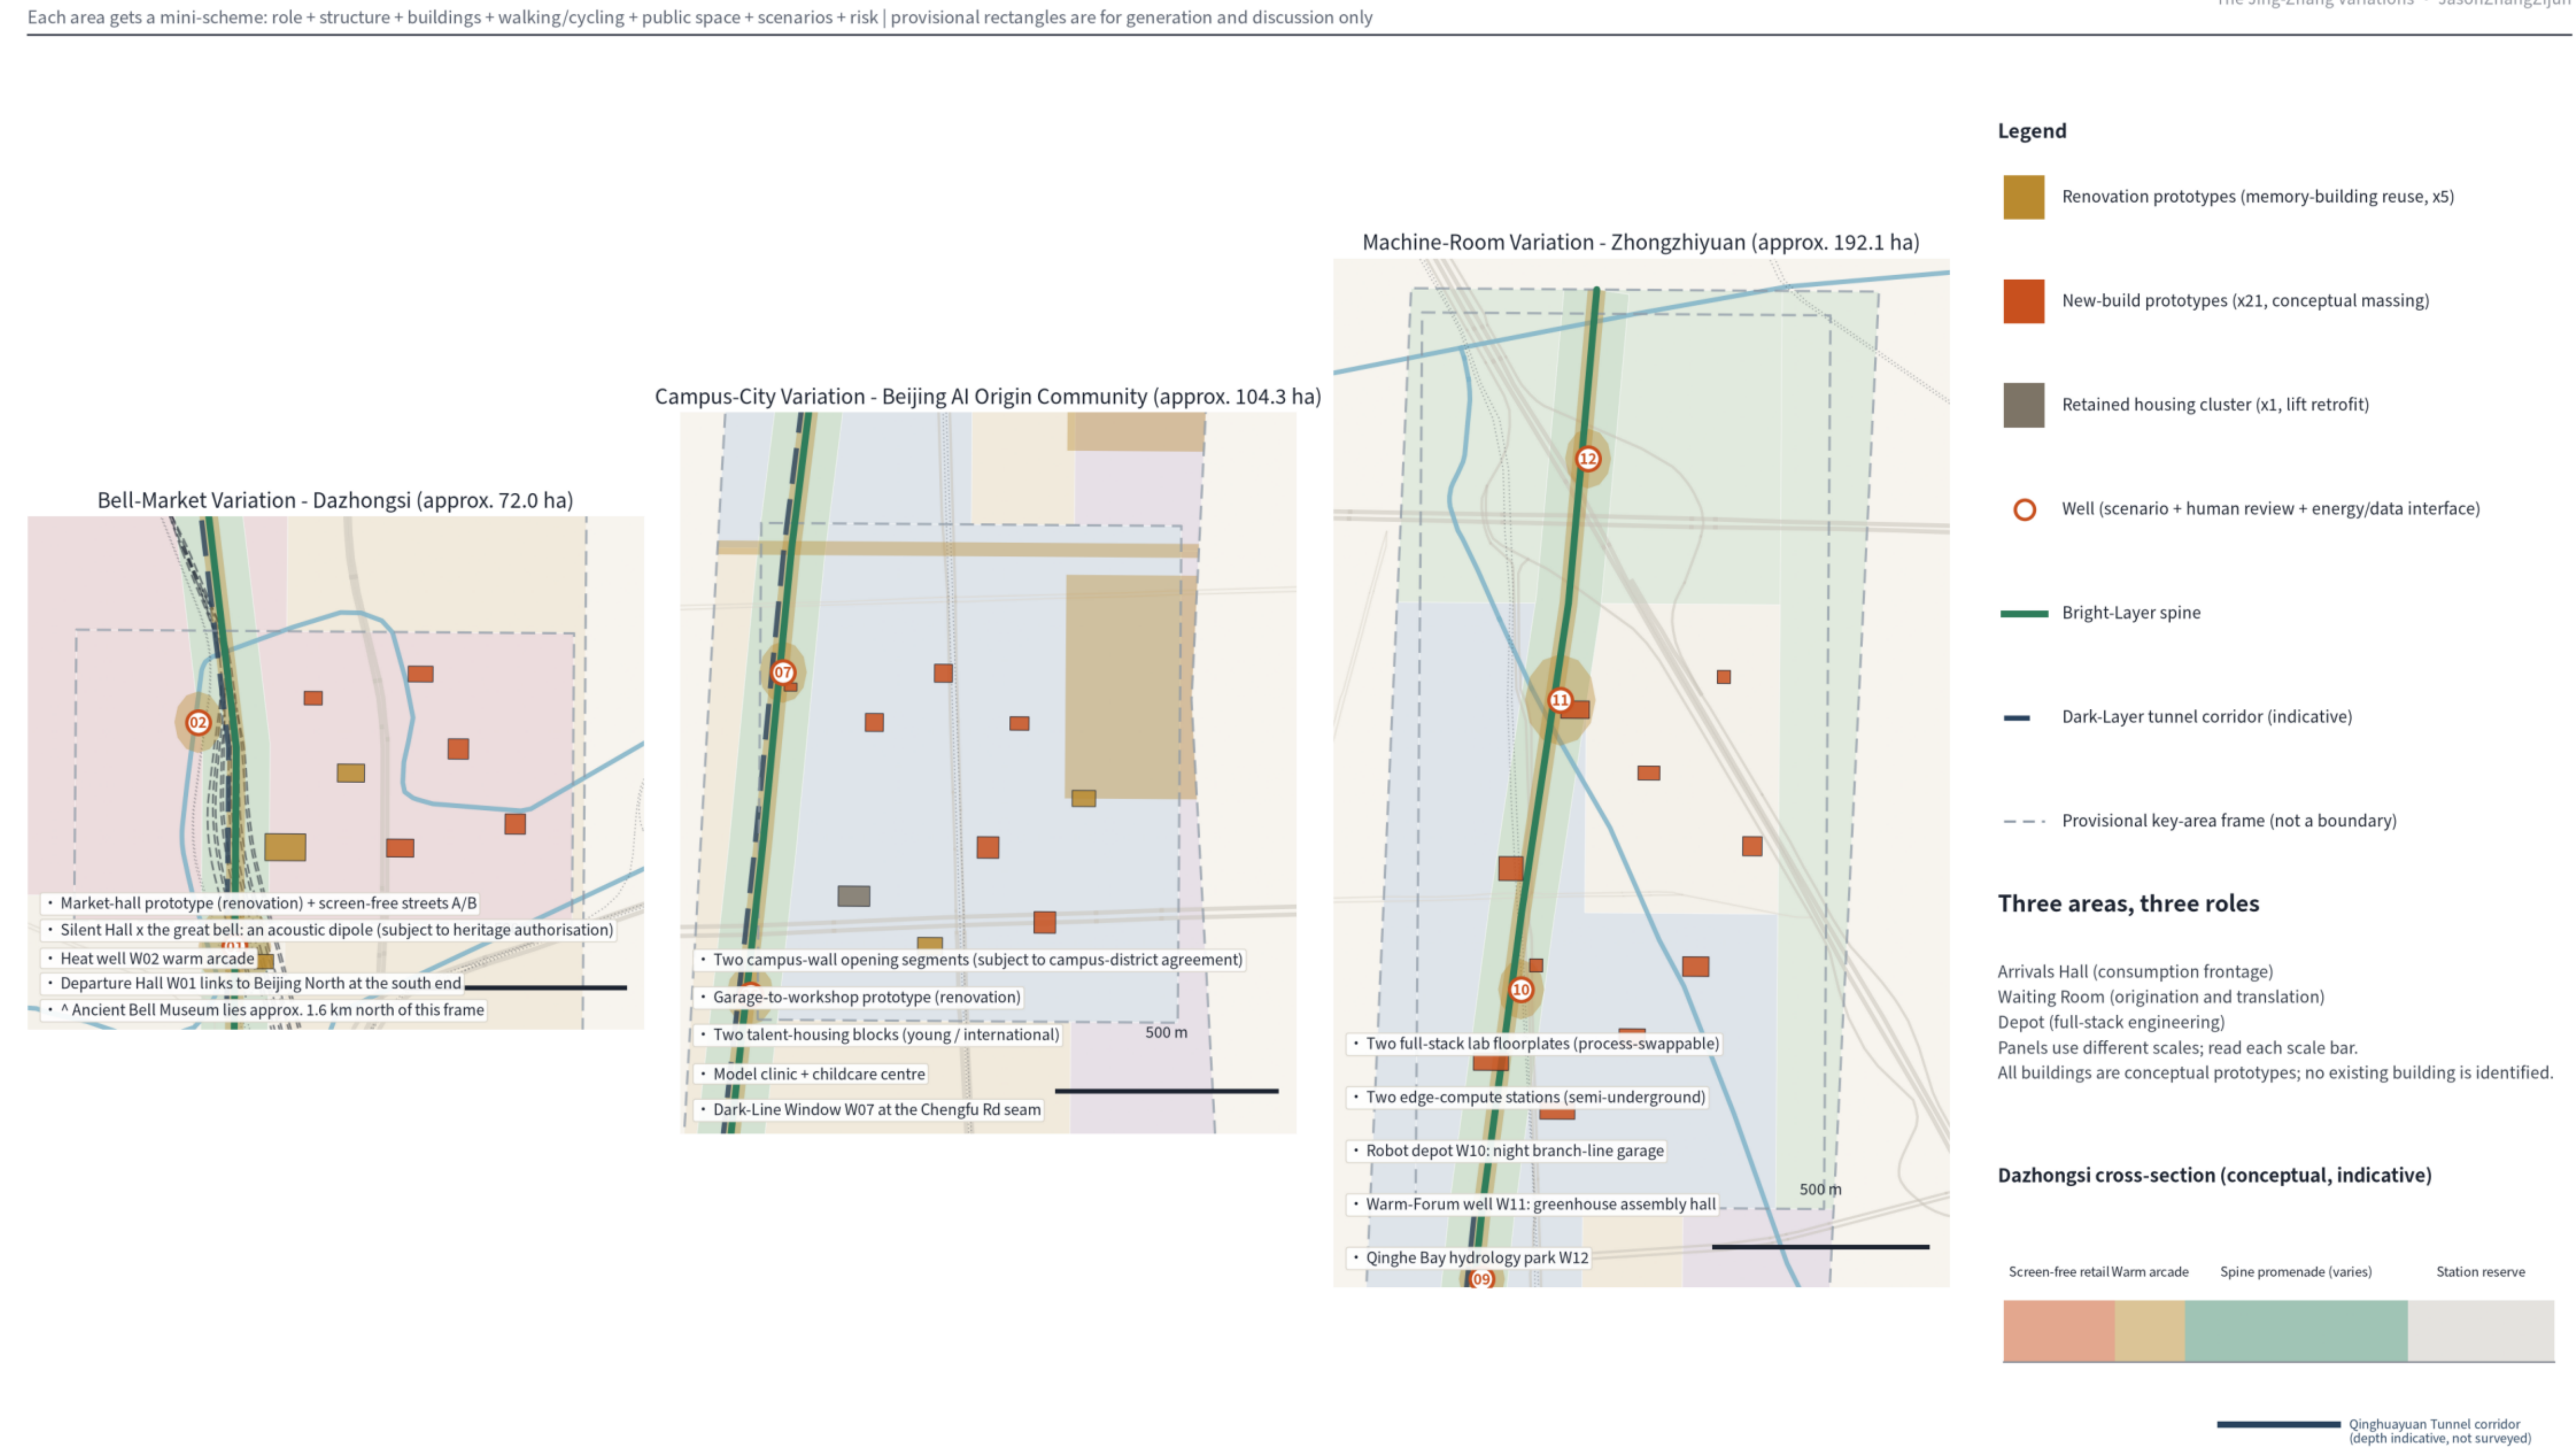

The provisional boundary (official_boundary=false, provisional_rough) is drawn only as a low-contrast dashed constraint and is not an official planning boundary; all areas are recomputed in EPSG:4548. Existing base-map features (c) OpenStreetMap contributors (ODBL), shown for context only. This drawing is a conceptual recommendation for professional teams to develop further.

Fig.04 | Mobility and blue-green systems: bury the fast, give the slow back to the ground

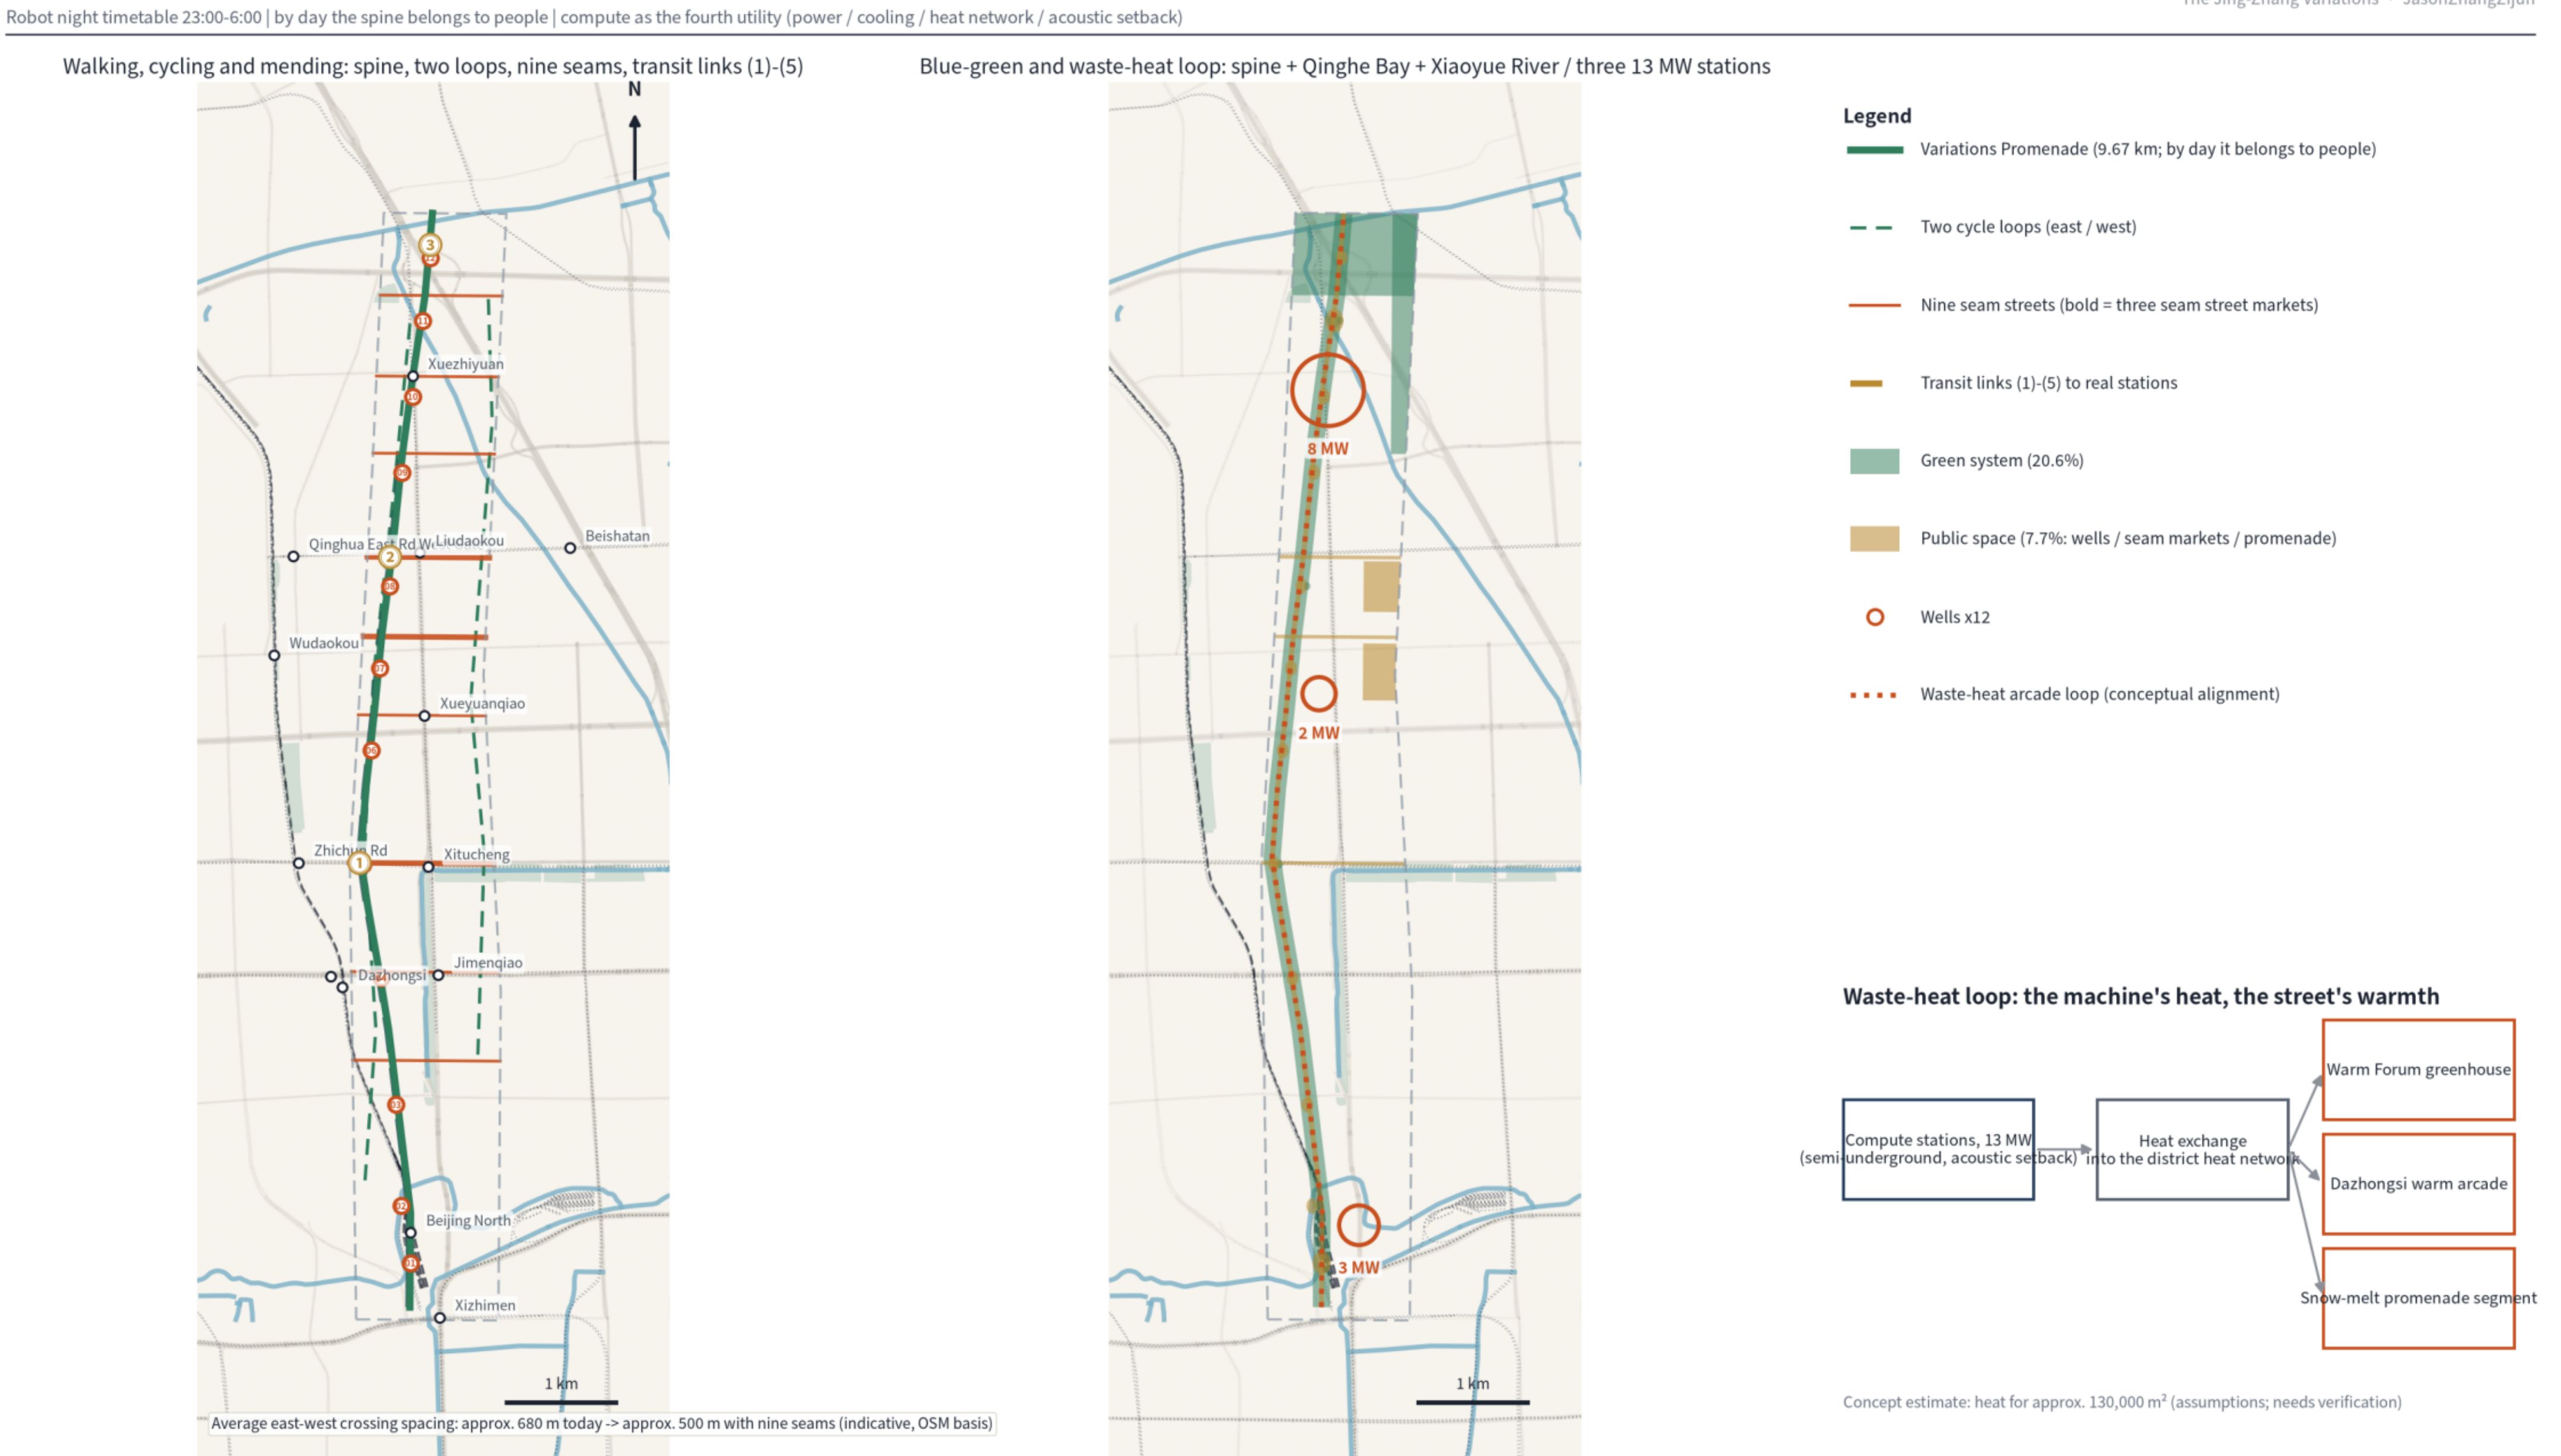


The provisional boundary (official_boundary=false, provisional_rough) is drawn only as a low-contrast dashed constraint and is not an official planning boundary; all areas are recomputed in EPSG:4548. Existing base-map features (c) OpenStreetMap contributors (ODBL), shown for context only. This drawing is a conceptual recommendation for professional teams to develop further.


Fig.05 | From evidence to synergy: regional division of labour, twelve wells, conversion pipeline

Training in Zhangjiakou, inference and scenarios in the belt | every figure recomputable | every unknown justified

Regional synergy along the Jing-Zhang axis

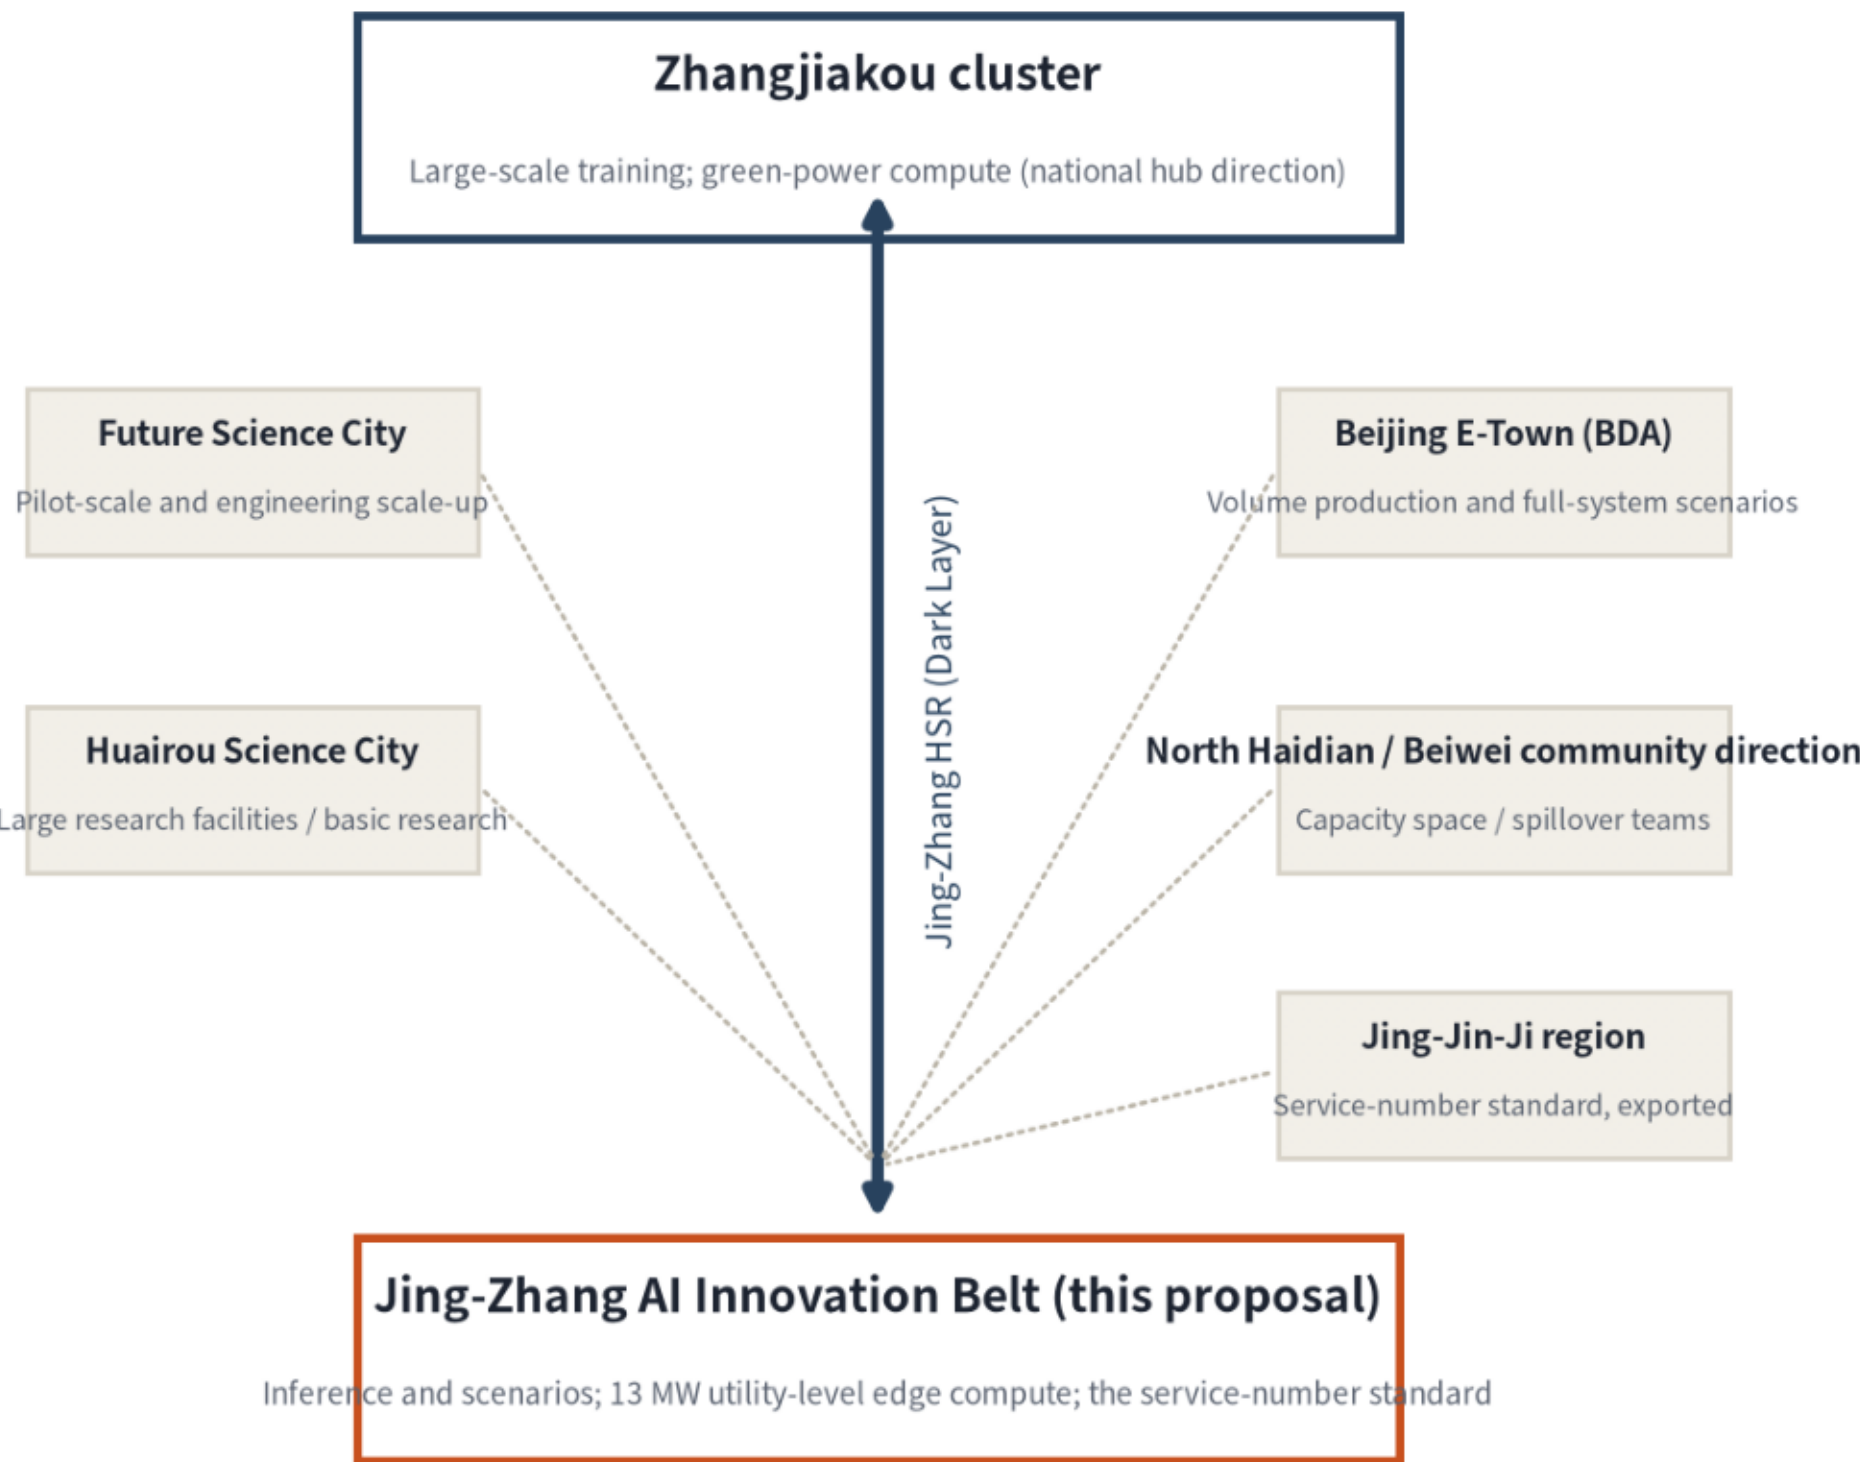

Twelve wells, pilgrimage route, conversion pipeline

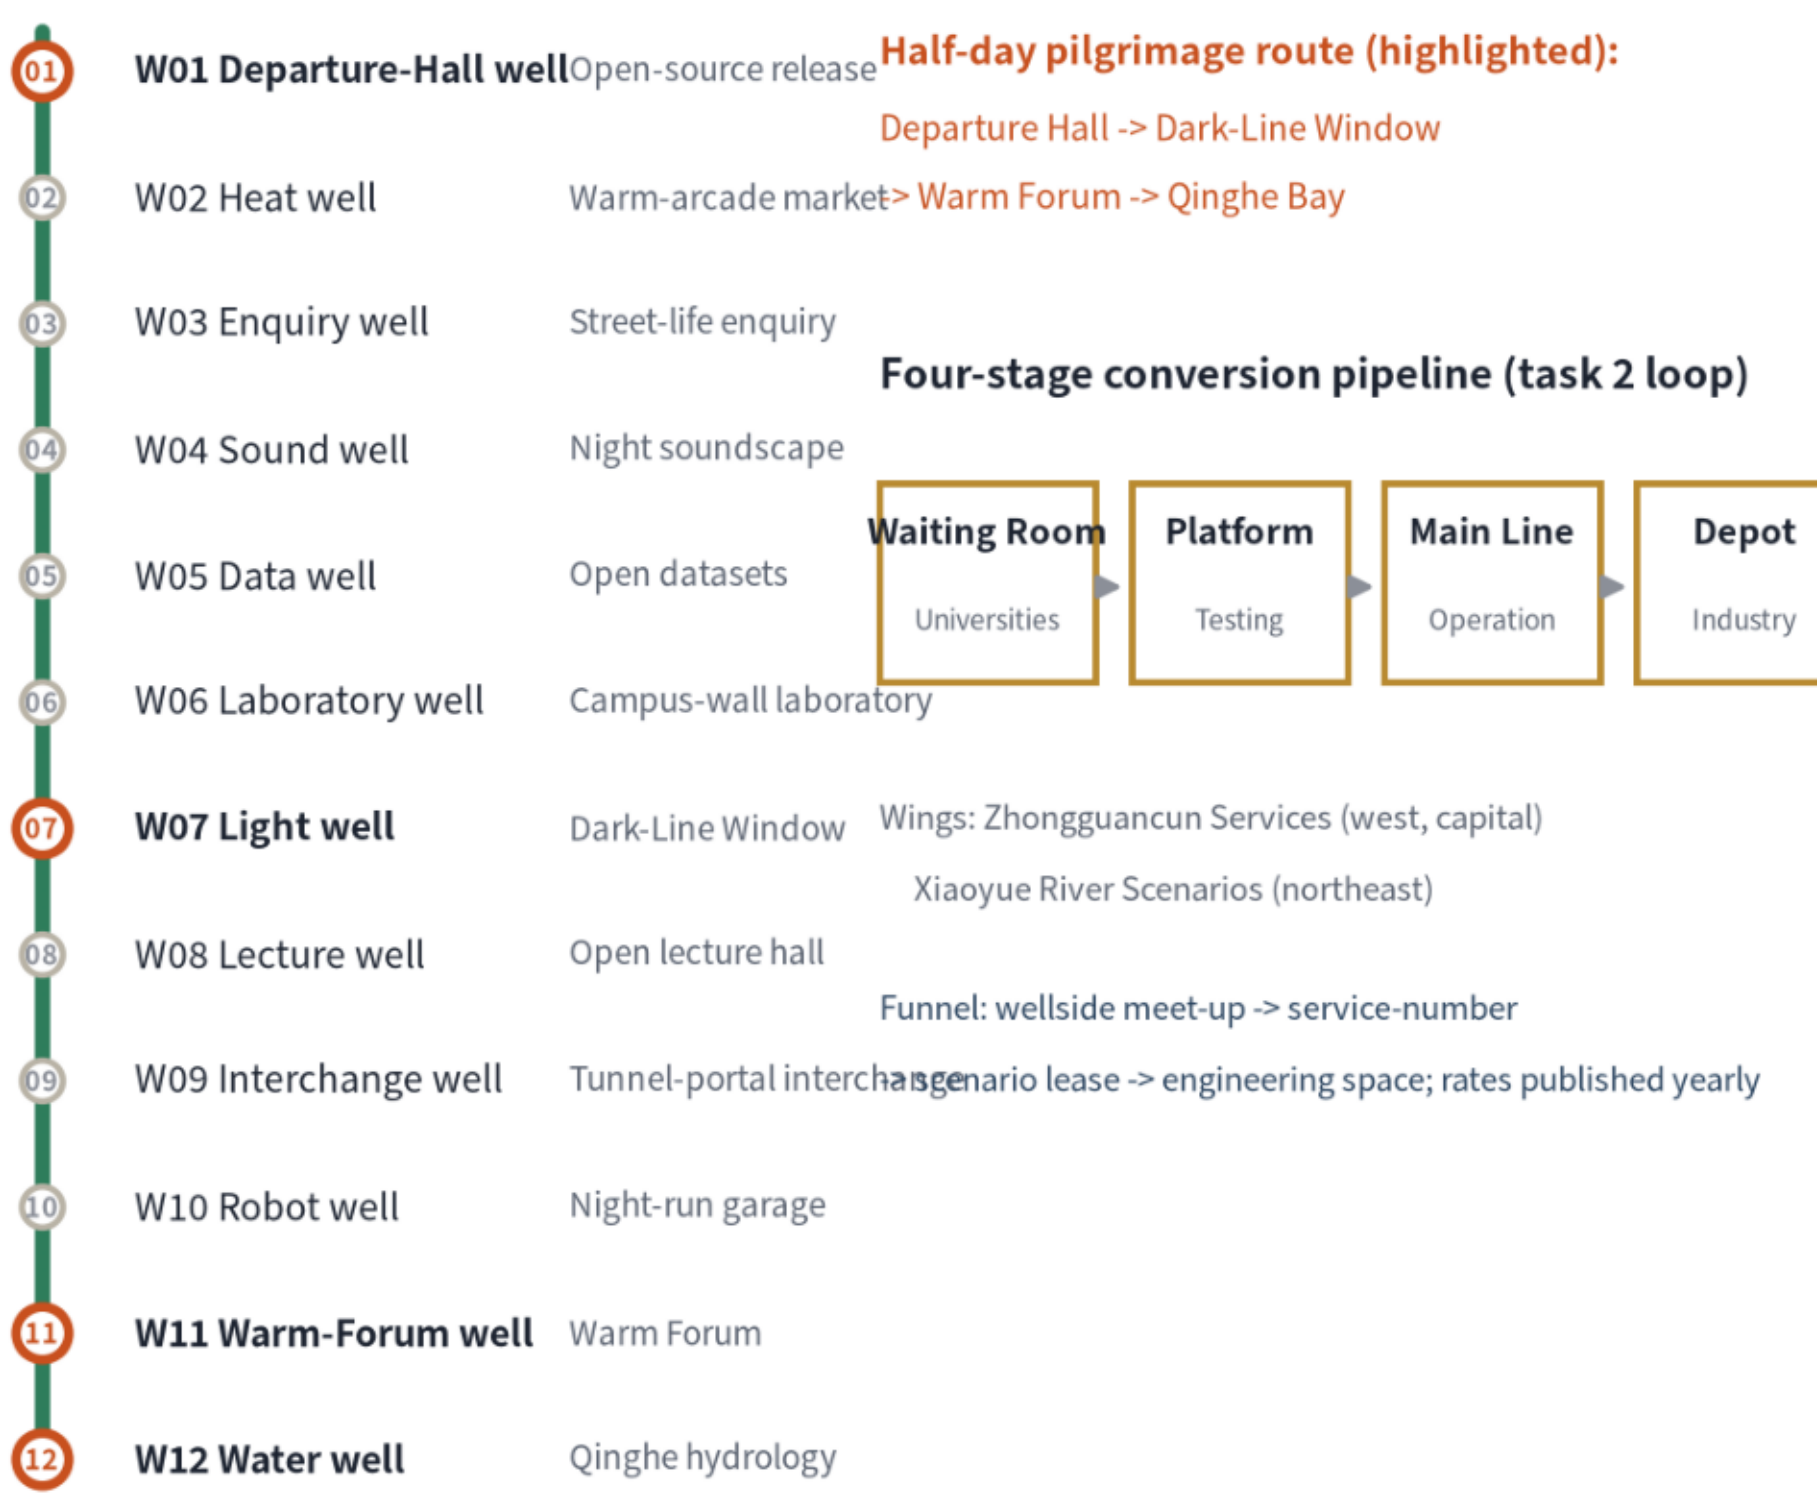

Key metrics (recomputed from geometry; formulas in metrics.json)

11.413 km² Overall Design Area recomputed (+0.11% vs. announcement)
20.6% / 7.7% Green ratio / public-space share
9,672 m 9 seams 12 wells Spine seams wells
13 MW -> approx. 130,000 m² Edge compute -> waste-heat heating (order-of-magnitude)
27 prototypes / approx. 334,000 m² Building prototypes / conceptual floor area
Conceptual split 1 / 5 / 21 Retain / renovate / new-build (not an existing-building survey)

Registered urban experiment (falsifiable)

Measure the baseline before works start; re-measure and publish yearly; shortfalls go into the annual report.

H1 Seam street markets -> east-west walking crossings increase

H2 Screen-free segments -> longer dwell time than the control high street

H3 Warm arcade -> longer winter use of the spine

Control segment: existing Zhichun Road frontage

Gate-based phasing (no year commitments)

Demonstration (campus agreement + funding) -> Loop (heat concession)

-> Mending (official boundary released + tunnel verification); below the gate, work pauses.

Honest unknowns: refusing manufactured certainty

Floor Area Ratio — official regulatory conditions not public

Building height — height controls (aviation / landscape / heritage) not public

Demolish-Renovate-Retain — conceptual prototypes only; no existing building is identified

Tunnel alignment and boundaries — inferred; no substitute for the statutory rail protection zone

When official data lands: all layers, metrics, drawings recomputed

Every known figure is recomputable from the geometry layers; formulas in metrics.json.

Evidence chain and task coverage

geometry: 9 layers	17 announcement tasks covered
metrics: 17 known values	agent.1–6 ✓
three matrices: 23 / 6 / 15 fully covered	5 mandatory standards addressed
proposal + five figures (readable tags)	15 design-depth items complete
four-part self-check PASS	14 cards / 7 personas / 3 tests
	3 counter-type landmarks

Three counter-type landmarks

Departure Hall

The flip-dot board announces service numbers, not trains; an honorary service number departs every year.

Dark-Line Window

A 350 km/h design-speed line slows and passes quietly beneath the city.

Warm Forum

The warmth of the debate is provided by the warmth of the machines.

International message

"A century after its first train, this corridor buried its fastest one to build its calmest park. Now it does the same with AI."