

板 01 | 总体设计结构



人字线 The Chevron Line: 一脊贯通 · 五处人字缝合 · 三核锚定 · 两翼外接

概念建议 / 参考方案，可供专业团队深化研究；不构成法定规划或政府审定结论

人字线 · The Chevron Line | 总体概念结构

一脊贯通 · 五处人字缝合 · 三核锚定 · 两翼外接 | 百年京张AI创新带（总体设计范围 11.4 km²）概念建议

概念建议 / 参考方案，可供专业团队深化研究；不构成法定规划或政府审定结论

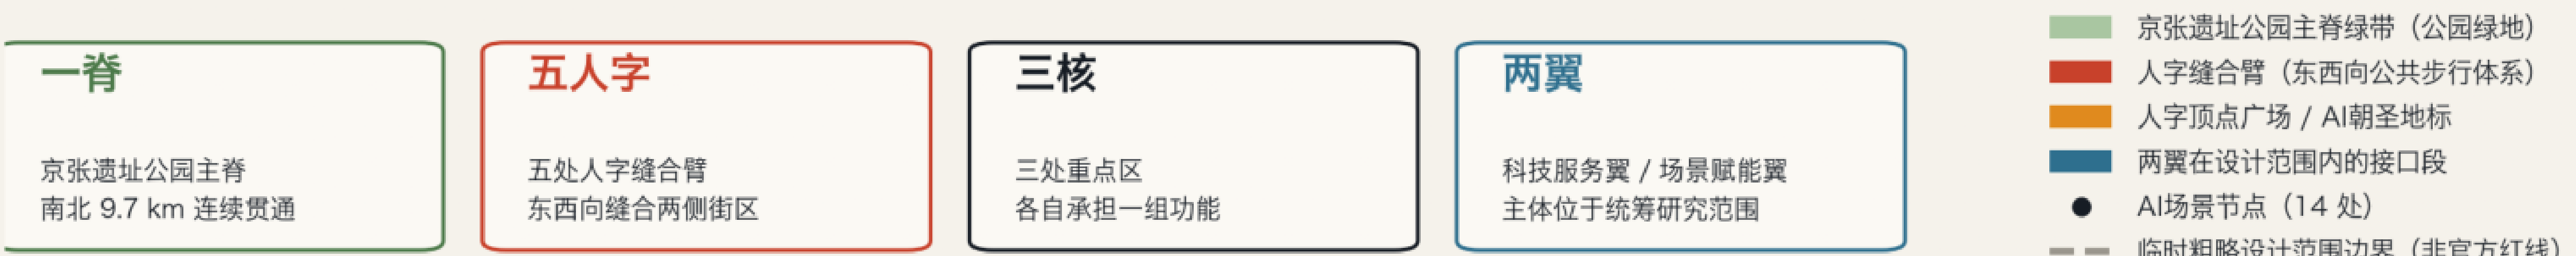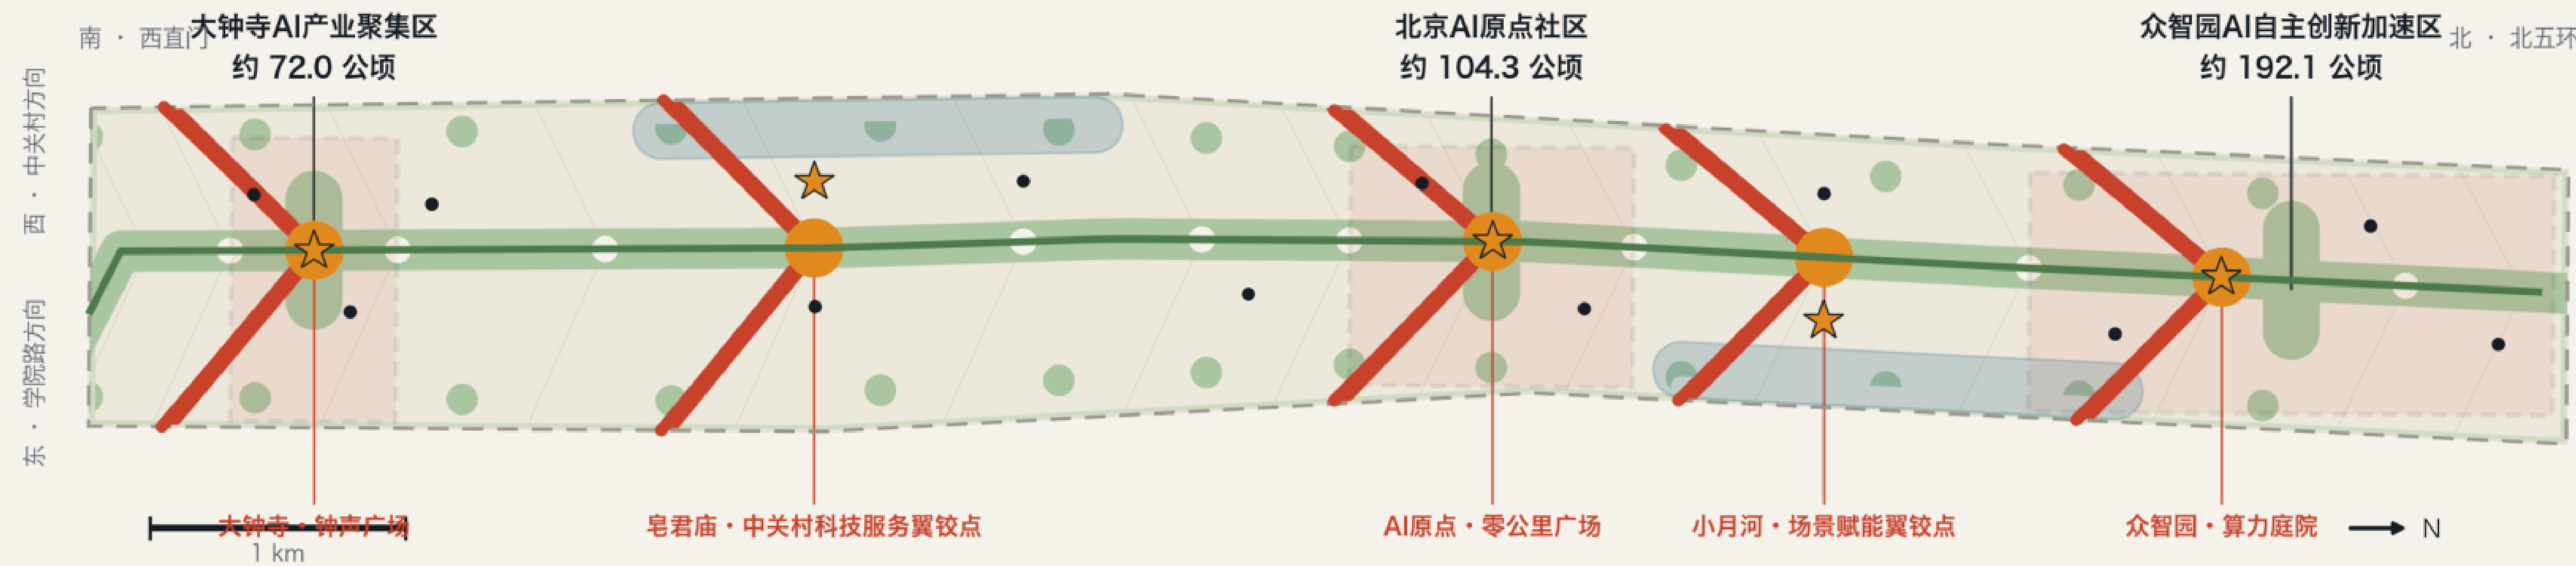

边界说明：底图边界来自仓库 `brief/site-package/geometry/provisional_boundaries.geojson` 的临时粗略范围（虚线弱化表达），非官方红线，不作为精确面积或审批依据；官方 `polygon` 发布后全部图层与指标重算。

数据来源：本图由本投稿 `geometry/*.geojson` 与 `metrics.json` 在 EPSG:4548 下派生绘制，不使用商业地图底图、新闻示意图或外部瓦片。

概念

“人”字来自 1909 年京张铁路青龙桥段以人字形展线

解决坡度的工程史实——承认限制，然后绕过去；

也来自本方案的立场：所有智能体与场景最终都要

回到人的日常与尊严。展线位于关沟段而非本范围内，

此处作为文化母题引用。

为什么用人字而不是横向连接

一 斜向臂更长，把更多街区纳入 400 米步行圈；

二 顶点自然形成向心公共空间，无需另辟大广场；

三 五个顶点沿主脊排列，形成可识别、可命名、

可运营的节奏，而不是均质的连续绿带。

核心指标

主脊慢行 9.75 km

人字缝合步道 8.37 km

设计范围 11.41 km²（临时边界）

绿地率 19.0%

公共空间率 9.0%

用地地块单元 48 个

AI 场景节点 14 处

朝圣与荣誉节点 5 处

三大定位的空间承载

百年京张文化带——主脊与里程碑体系；

都市 AI 生活体验带——顶点广场与场景节点；

AI 融合创新带——三核与两翼。

协同回路

众智园产出技术 → 原点社区形成团队与生态 →

大钟寺与全线场景验证并被市民使用 →

两翼把要素与需求换进来 → 再回到众智园。

命名体系与副题

线一段一站一里程碑一场 五级命名，起点 KO 零公里碑。

副题：两条腿，一次爬坡。Two legs, one climb.

Logo 方向：两条轨线在顶点相交、向北收敛，


顶点位置沿主脊移动即得到各段子标识。

用地分区对设计范围完全覆盖、相邻不重叠；更新框架为骨架—界面—节点—留白


用地结构与三层范围传导

从 43.6 km² 统筹研究、到 11.4 km² 总体设计、再到 368.4 ha 重点区的功能落位 | 用地分区对设计范围完全覆盖、相邻不重叠


概念建议：用地类别依据《国土空间调查、规划、用途管制用地用海分类指南》项目子集，不构成控规调整结论

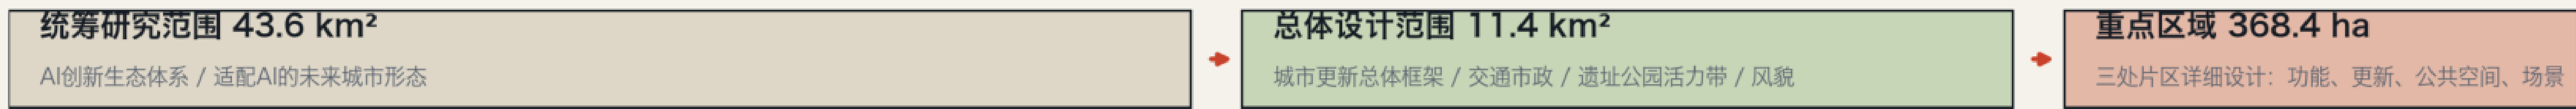

传导规则：上层决定产业与形态判断，中层决定更新与设施承载，下层验证地块、建筑、公共空间与场景可实施性；三层结论互相回引 compliance_matrix.json。

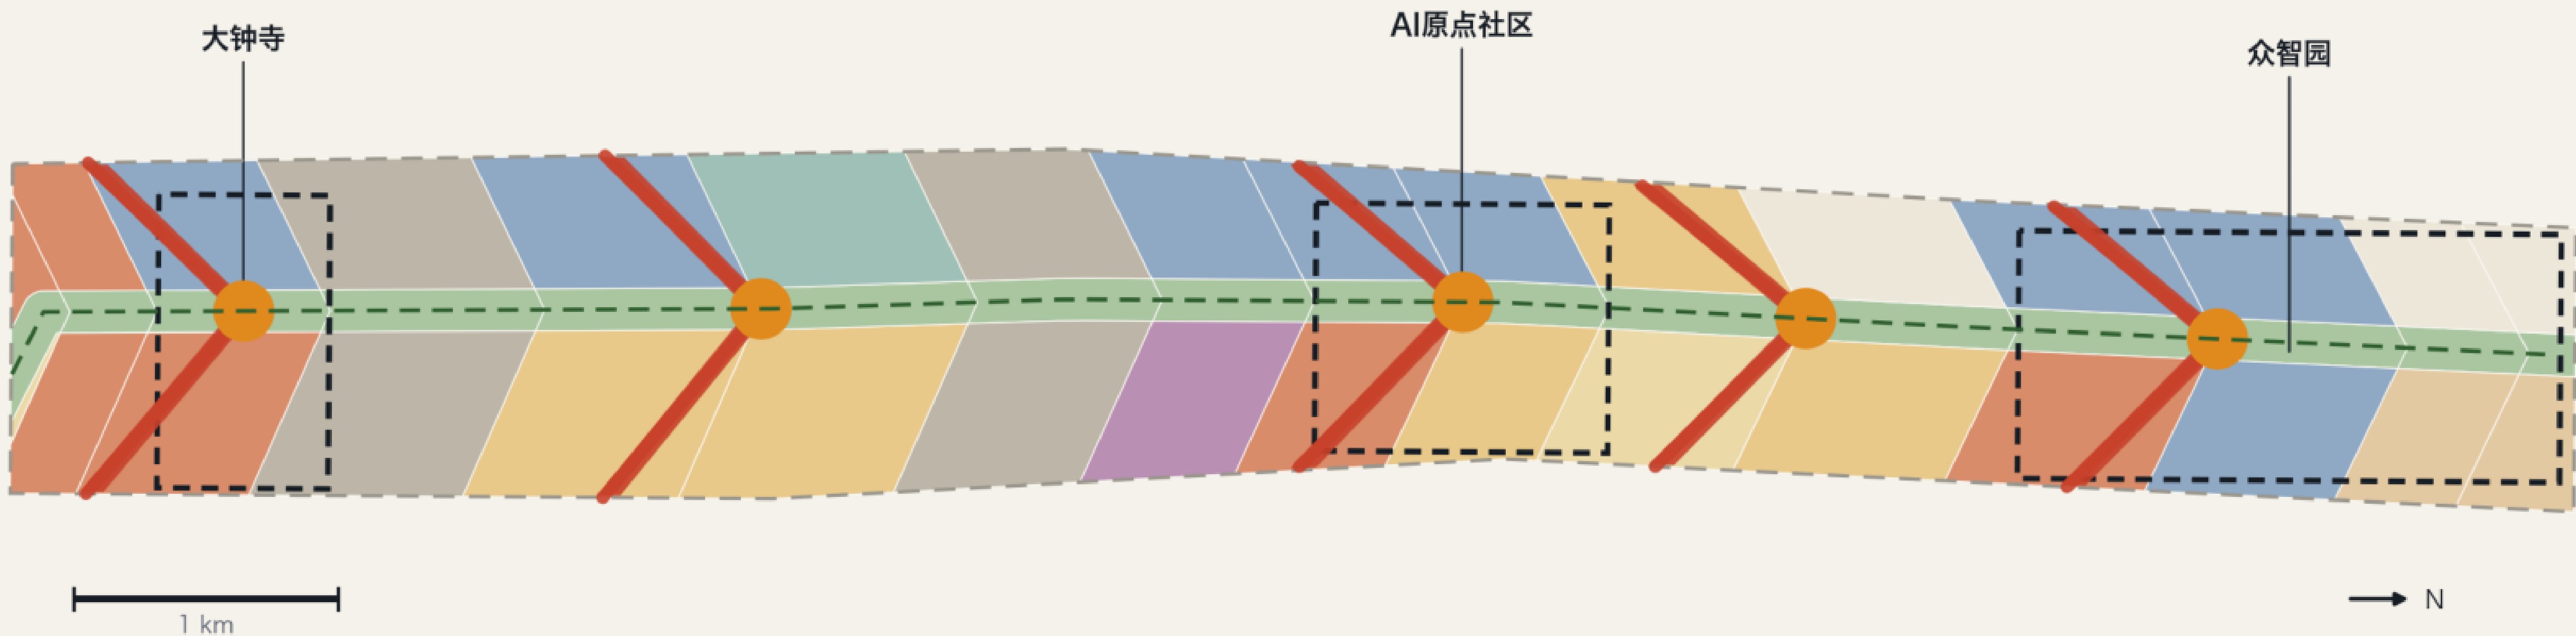

用地构成（按面积占比，复算自 geometry/land_use.geojson）

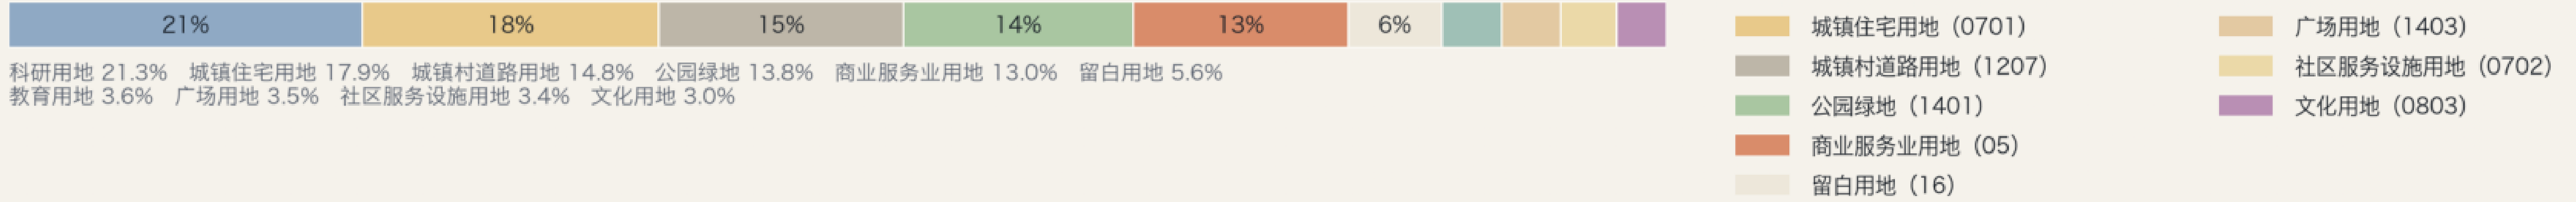

拓扑复算：覆盖缺口 0.0 m²、相邻重叠 0.0 m²，用地分区完全覆盖提交范围且互不重叠（48 个地块单元）。

边界说明：底图边界来自仓库 brief/site-package/geometry/provisional_boundaries.geojson 的临时粗略范围（虚线弱化表达），非官方红线，不作为精确面积或审批依据；官方 polygon 发布后全部图层与指标重算。

更新框架：骨架—界面—节点—留白

骨架：主脊与五组缝合臂，先行贯通；

界面：走廊两侧建筑由背面转为正面；

节点：站点、顶点广场与场景节点承担日常使用；

留白：为未成熟技术与业态预留，占 5.6%。

用地纪律

48 个用地单元由五组人字缝合线与主脊边线对设计

范围做无缝切分：覆盖缺口 0.0 m²、相邻重叠 0.0 m²。

用地代码取自官方分类指南的仓库项目子集。

非完整官方代码表，正式编制前须导入完整代码表。

代码	用地类别	块	ha	占比
0802	科研用地	8	243.5	21.3%
0701	城镇住宅用地	5	203.7	17.9%
1207	城镇村道路用地	4	168.6	14.8%
1401	公园绿地	16	157.9	13.8%
05	商业服务业用地	6	148.6	13.0%
16	留白用地	3	64.0	5.6%
0804	教育用地	1	41.5	3.6%
1403	广场用地	2	40.3	3.5%
0702	社区服务设施用地	2	39.1	3.4%
0803	文化用地	1	34.1	3.0%

拆改留（概念分类建议）

保留 6 组 | 提升改造 22 组 | 新建织补 22 组。

不提出任何具体地块的拆除建议：现状质量、权属

与居民意愿数据均不可得。

强度与高度

floor_area_ratio 与 building_height_m 保持 unknown:

两个口径必须分清

公开资料包中控规条件状态均为 missing。

用地口径的公园绿地占 13.8%；

绿地图层口径的绿地率为 19.0%。

差异来自防护绿地、口袋公园与放大绿核落在

其他用地单元内；两者都不等于法定绿地率指标。

板 03 | 交通、轨道、慢行与市政支撑


主脊慢行 1 条、人字缝合步道 5 条、站点接驳 13 条、自行车联络 13 条、支路联络 2 条

线位为概念示意，不构成道路红线、道路线形、轨道线位、桥隧工程或交通组织结论


慢行接驳、蓝绿公共空间与AI场景网络

主脊慢行 9.75 km | 人字缝合步道 8.37 km | 站点接驳 13 处 | AI场景节点 14 处 | 朝圣与荣誉节点 5 处

概念建议：线位、断面与节点均为参考方案，不构成道路红线、轨道线位或工程可行性结论

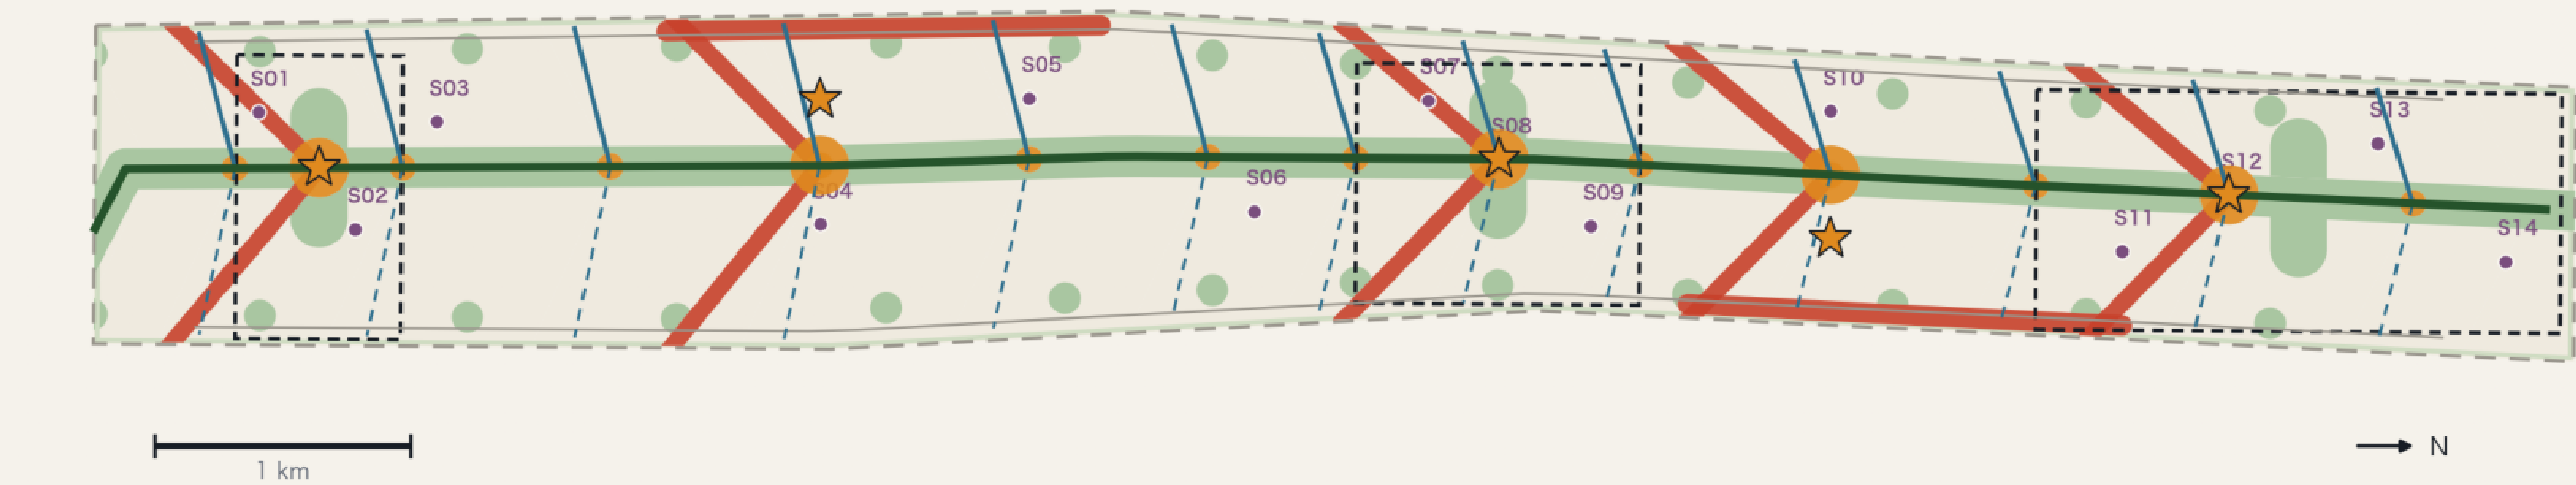

典型横断面关系示意（西—东，非工程断面）

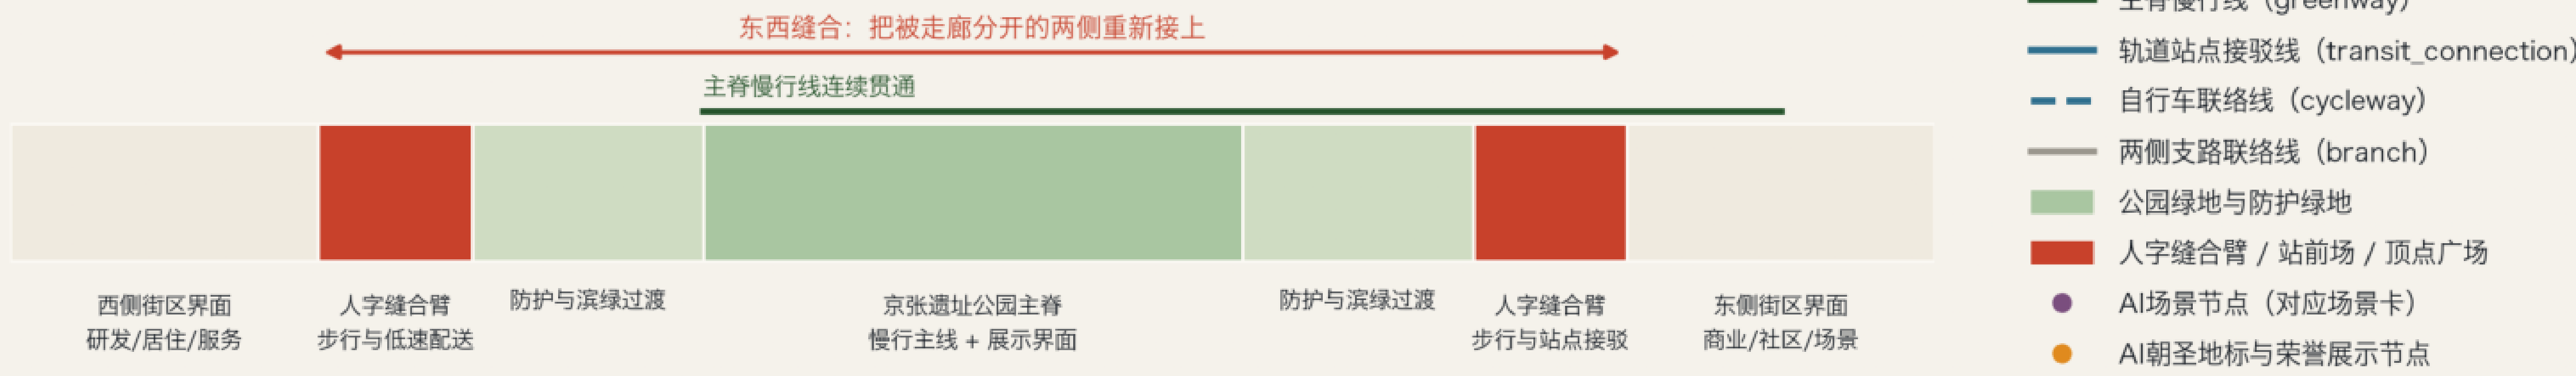

边界说明：底图边界来自仓库 brief/site-package/geometry/provisional_boundaries.geojson 的临时粗略范围（虚线弱化表达），非官方红线，不作为精确面积或审批依据；官方 polygon 发布后全部图层与指标重算。
数据来源：本图由本投稿 geometry/*.geojson 与 metrics.json 在 EPSG:4548 下派生绘制，不使用商业地图底图、新闻示意图或外部瓦片。

横断面关系（示意，非工程断面）

西侧街区界面—人字缝合臂—防护与滨绿过渡—

京张遗址公园主脊（慢行主线 + 展示界面）—

防护与滨绿过渡—人字缝合臂—东侧街区界面。

为什么把配送放在缝合臂

缝合臂承担日常过街与低速配送通道两个功能；

把配送机器人放在缝合臂而不是主脊，

是为了避免慢行主线被功能性交通占据。

站点接驳

13 处站点接驳线连接站前场、缝合臂与场景节点；

轨道站点出入口位置与工程可行性须由专业团队

依据官方资料确定。

市政与新型基础设施（只提原则）

算力与数据设施优先布置在众智园并预留扩展；

感知设施沿缝合臂与站前场布置，默认采集环境类

而非个人人类数据；充换电与低速配送支持设施结合

站前场与支路联络线设置；留白用地作为尚未明确

的市政与新基建需求的空间储备。

容量测算列为待补资料，不做结论。

公共服务设施

以社区服务设施用地与教育用地为载体，重点补足

步行 10 分钟内的社区服务、老年服务与青年友好

设施；具体配置标准需在取得人口口径数据后由

专业团队核定。



板 04 | 京张遗址公园活力带与蓝绿公共空间

主脊绿带 + 放大绿核 + 界面防护绿地 + 缝合臂两端口袋公园

人字线 · The Chevron Line | 总体概念结构

一脊贯通 · 五处人字缝合 · 三核锚定 · 两翼外接 | 百年京张AI创新带（总体设计范围 11.4 km²）概念建议

概念建议 / 参考方案，可供专业团队深化研究；不构成法定规划或政府审定结论

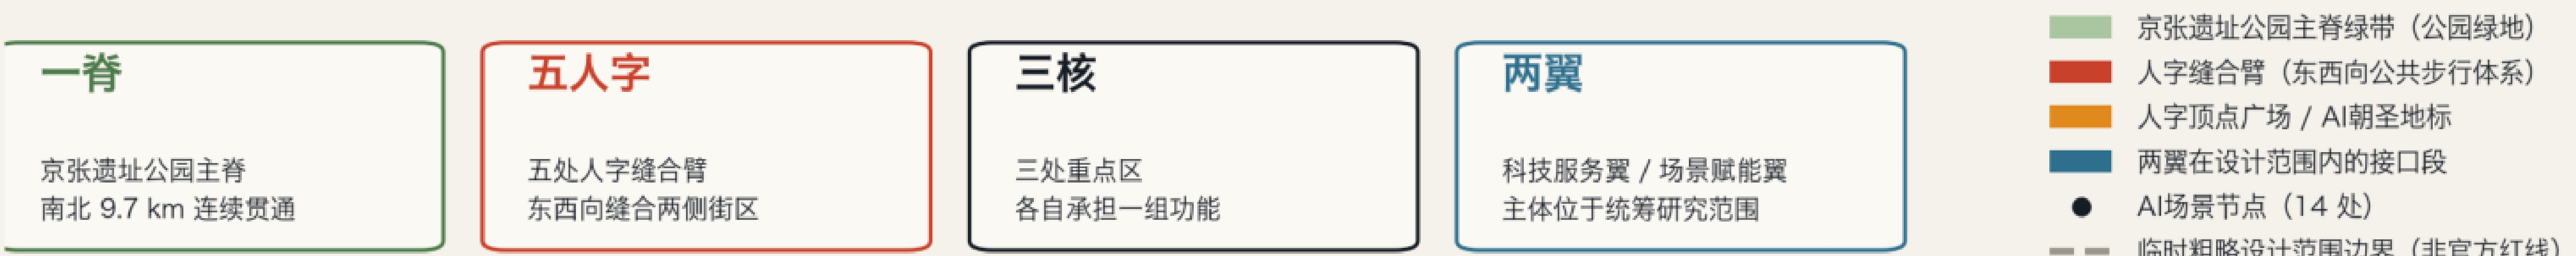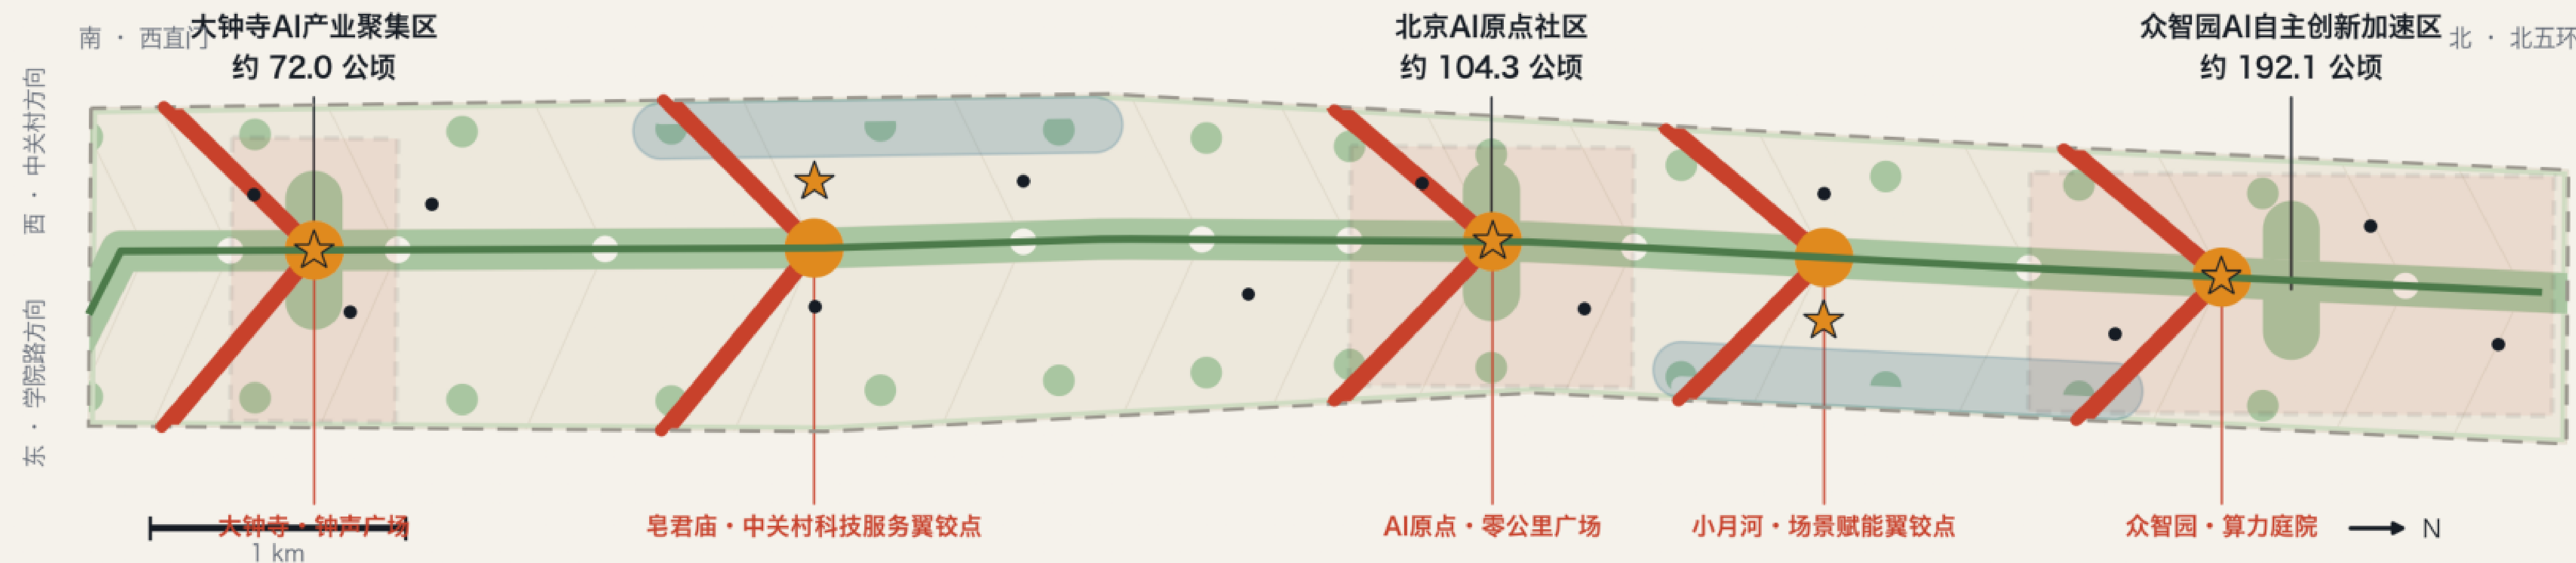

边界说明：底图边界来自仓库 brief/site-package/geometry/provisional_boundaries.geojson 的临时粗略范围（虚线弱化表达），非官方红线，不作为精确面积或审批依据；官方 polygon 发布后全部图层与指标重算。
数据来源：本图由本投稿 geometry/*.geojson 与 metrics.json 在 EPSG:4548 下派生绘制，不使用商业地图底图、新闻示意图或外部瓦片。

蓝绿系统四层

主脊绿带——沿遗址公园连续贯通的公园绿地；

放大绿核——三处重点区内的放大公园空间；

界面防护绿地——缓冲快速路、主干路与铁路影响；

口袋公园——设在每组缝合臂两端的停留点。

风貌三条原则（不给数值）

界面转正——底层设置面向公园的开口；

体量分级——顶点广场周边保持低体量与开敞；

材料克制——铁轨氧化铁红、遗址公园绿、里程碑铜金。

高度、退线与强度须待官方控规条件补齐后确定。

复算结果

绿地面积 217 ha | 绿地率 19.0%

公共空间面积 103 ha | 公共空间率 9.0%

广场与铺装已从绿地扣除，两图层互斥。

三处 AI 朝圣地标

零公里碑 The Zero Kilometre（AI 原点人字顶点）

人字塔 The Chevron Tower（众智园算力庭院）

回声钟廊 The Echo Colonnade（大钟寺缝合臂）

两处荣誉展示节点

里程碑林 Milestone Grove | 开源门 The Open Gate

公共空间组件库

里程碑构件、可坐边界、遮荫单元、夜间照明段、

临时展位、低速配送停靠位——让缝合臂可以分期、

分段、由不同主体建设而仍然是一套东西。

AI 公共空间三条原则

可观察——把算力、感知与调度做出公共界面；

可参与——至少一部分内容由开发者与市民贡献并可更新；

可退出——任何智能设施都有明确的关闭方式

与人工替代方案。

板 05 | 三处重点区域详细设计

设计原则是不重复定位：三处各承担一组功能

片区范围为临时粗略边界，图中地块、建筑与节点均为可深化的参考方案


三处重点区域：定位差异、空间抓手与资料条件

自北向南 众智园AI自主创新加速区 192.1 ha | 北京AI原点社区 104.3 ha | 大钟寺AI产业聚集区 72.0 ha

概念建议：片区范围为临时粗略边界，图中地块、建筑与节点均为可深化的参考方案

众智园AI自主创新加速区

公告面积 192.1 公顷 | 临时边界复算 192.9 公顷

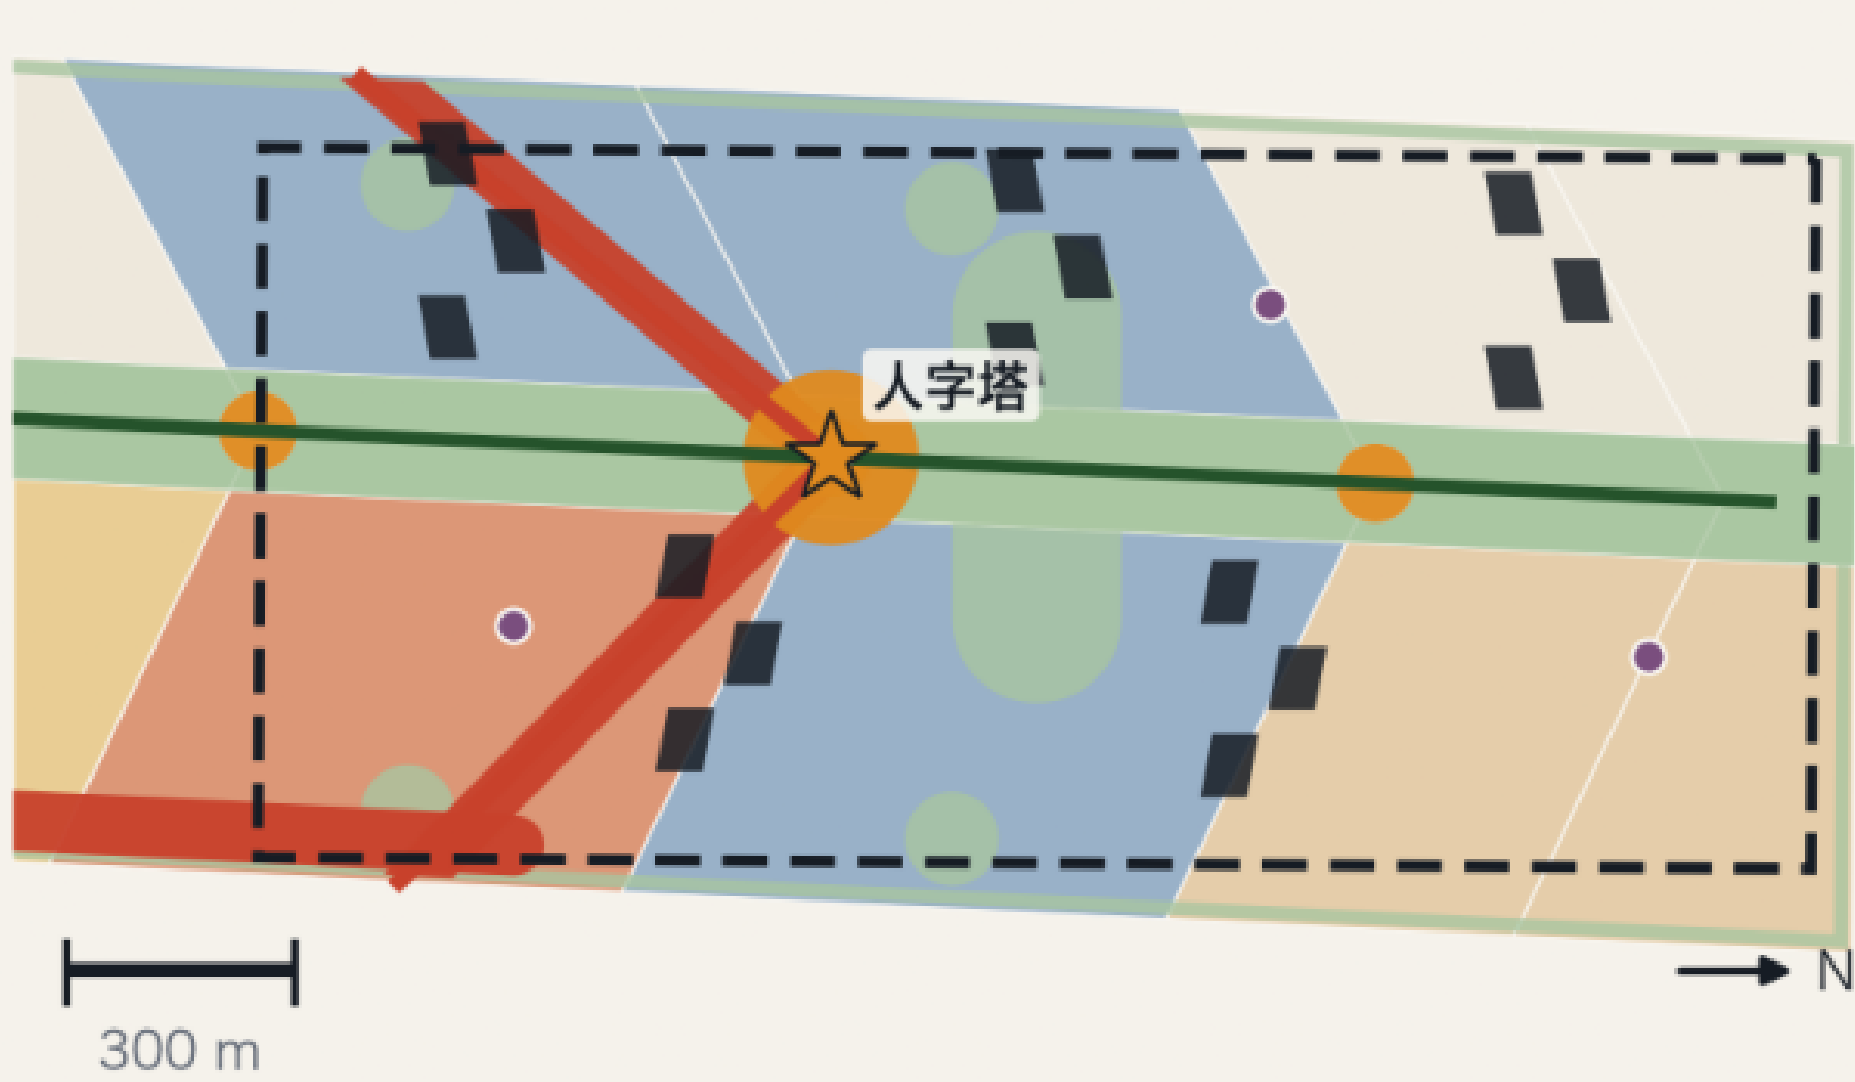

AI全栈自主创新体系 · AI治理全球话语权

抓手 算力庭院公共可视化 + 中试与测试验证场


空间 北五环门户接驳枢纽 + 众智园中枢人字广场

更新 以现状产业办公保留为主，空隙织补中试与实验室

风险 算力与市政容量、测试场安全边界须专业复核

北京AI原点社区

公告面积 104.3 公顷 | 临时边界复算 104.3 公顷

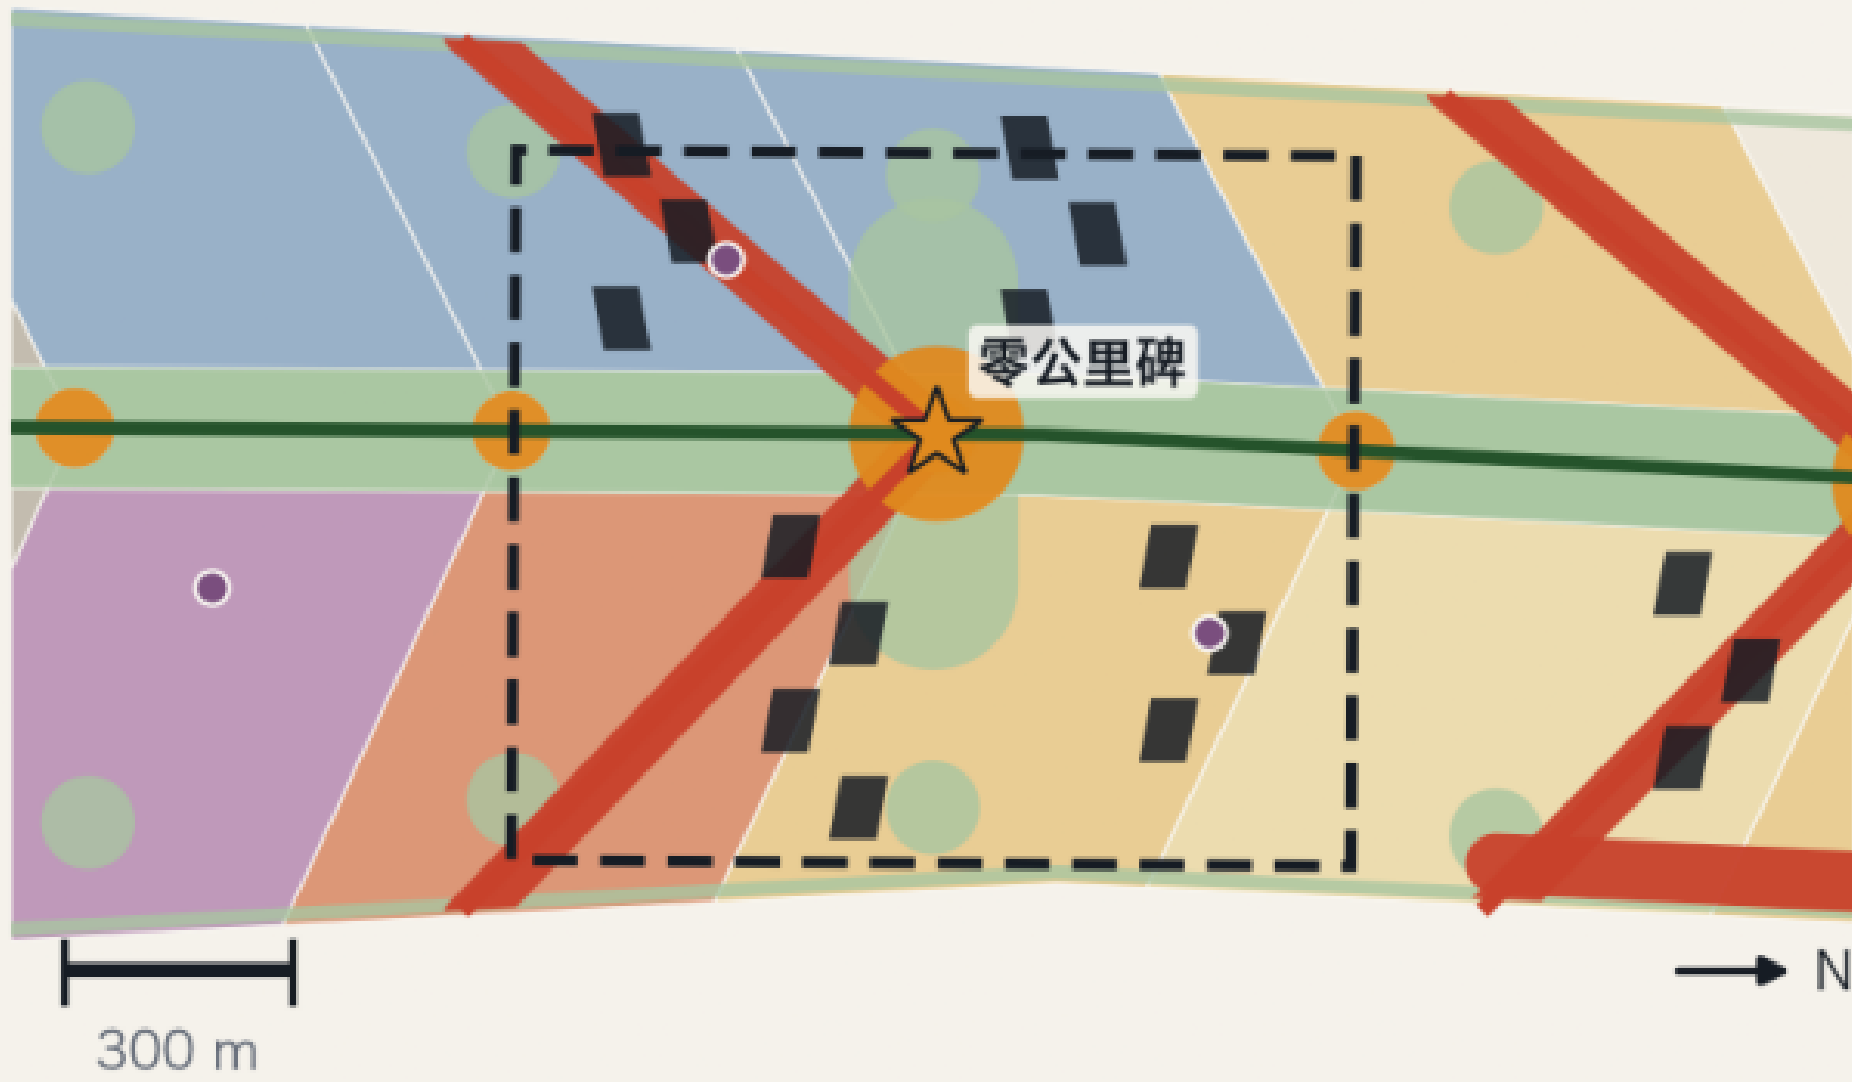

世界级AI创新生态 · 开发者日常

抓手 零公里AI朝圣广场 + 开发者社区客厅


空间 三条人字缝合臂把高校、企业与社区接入主脊

更新 孵化加速与人才公寓织补，社区服务提升改造

风险 人才居住与公共服务配比缺官方口径数据

大钟寺AI产业聚集区

公告面积 72.0 公顷 | 临时边界复算 72.0 公顷

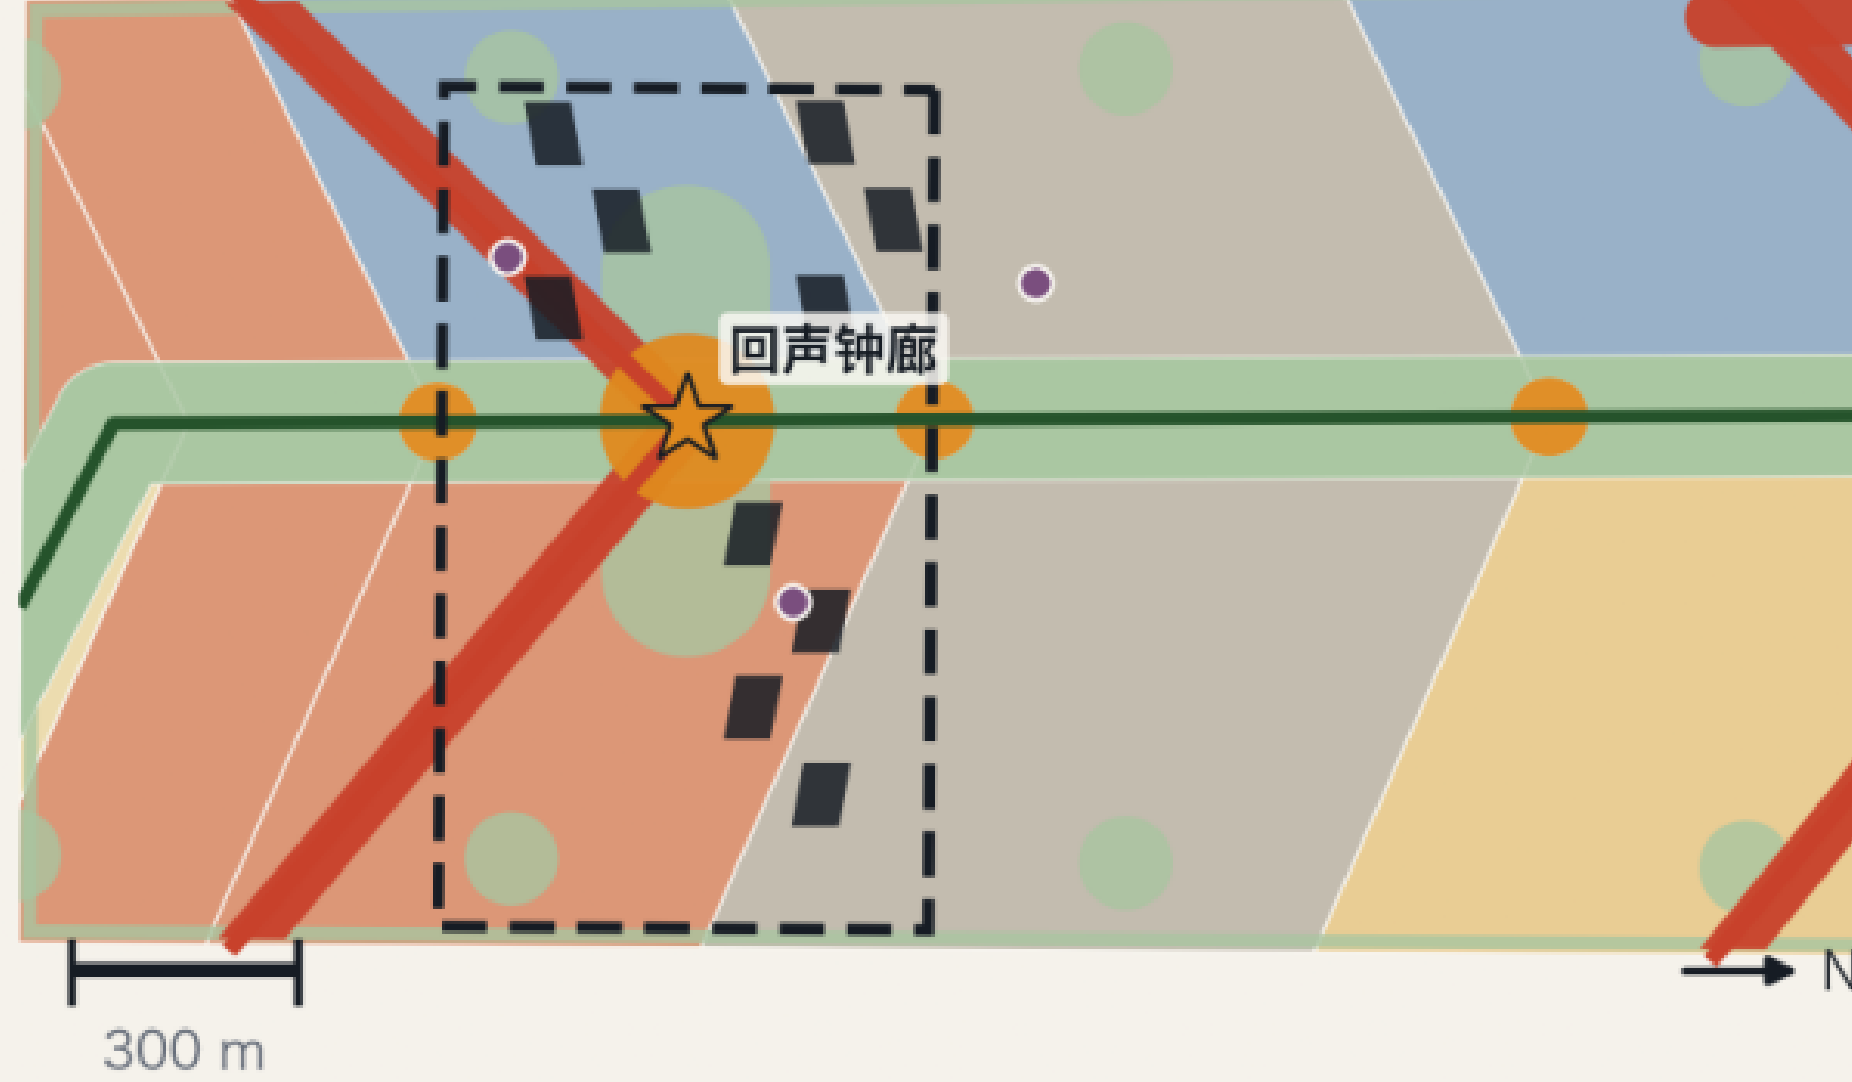

智能原生新业态 · 城市消费与商务

抓手 智能原生消费街区 + 商务楼宇AI服务中枢

空间 回声钟廊与钟声广场缝合东西两侧街区

更新 以存量商业与商务提升改造为主，文化织补

风险 文保与轨道站域控制条件缺资料，须官方确认

■ 更新项目建筑基底示意（保留/提升/织补） ■ 人字缝合臂与缝合步道

■ 顶点广场 / 站前场 / AI朝圣地标

■ 公园绿地

● AI场景节点

边界说明：底图边界来自仓库 brief/site-package/geometry/provisional_boundaries.geojson 的临时粗略范围（虚线弱化表达），非官方红线，不作为精确面积或审批依据；官方 polygon 发布后全部图层与指标重算。

数据来源：本图由本投稿 geometry/*.geojson 与 metrics.json 在 EPSG:4548 下派生绘制，不使用商业地图底图、新闻示意图或外部瓦片。

众智园 192.1 ha

AI 全栈自主创新体系 · AI 治理全球话语权

抓手：算力庭院公共可视化 + 中试与测试验证场

前置：算力与市政容量、测试场安全边界须专业复核

AI 原点社区 104.3 ha

世界级 AI 创新生态 · 开发者日常

抓手：零公里 AI 朝圣广场 + 开发者社区客厅

前置：人才居住与公共服务配比缺官方口径数据

大钟寺 72.0 ha

智能原生新业态 · 城市消费与商务

抓手：智能原生消费街区 + 商务楼宇 AI 服务中枢

前置：文保与轨道站域控制条件缺资料，须官方确认

共同纪律

三处片区的描述停留在结构关系与空间动作层面，

不出现地块级的边界、权属或拆除结论。

板 06 | AI 场景与实施运营

14 张场景卡（含 3 个产业测试验证场景） · 16 组更新项目 · 3 期实施建议 · 年度活动体系

编号	场景名称	类型	人工复核与退出
S01	智能原生消费街区	体验	商户与街区运营方双人复核
S02	商务楼宇AI服务中枢	服务	服务窗口保留人工坐席
S03	站城一体AI接驳	测试验证	交通管理部门复核，异常恢复常规组织
S04	科技服务翼企业服务窗口	服务	服务人员终审，AI 只做草拟
S05	北四环慢行安全复核点	治理	每周人工复核清单，结论公开
S06	小月河滨水感知与健康步道	体验	用户可随时关闭，默认不采集
S07	原点开发者社区客厅	服务	社区运营人工审核内容
S08	零公里AI朝圣广场	体验	活动方现场人工值守
S09	社区AI健康与养老导航	服务	全部建议须医护人员确认
S10	场景赋能翼低速配送走廊	测试验证	远程人工接管 + 物理限速
S11	众智园中试与测试验证场	测试验证	测试许可 + 安全员 + 熔断
S12	算力底座公共可视化	治理	运维方审核发布内容
S13	校城融合AI教育实验场	体验	校方与家长双重同意
S14	北五环门户活动与安全运营复核	治理	活动安全方案人工审定

分期建议

- 一期（约 4.99 km²）三处重点区与主脊贯通、
样板缝合臂与场景开放机制；
- 二期（约 4.44 km²）两翼接口平台、站点接驳与
场景节点加密；
- 三期（约 1.66 km²）留白用地、长期活动体系与
品牌资产沉淀。

开发者社区与场景开放机制

- 场景需求池 → 公开揭榜 → 测试许可（边界、期限、
安全方案与退出条件）→ 人工复核 → 落地清单。
- 清单制与退出制：目录、准入条件与复核记录公开；
设评估周期，未达预期即退出并释放空间。

组别	项目	类型	前置条件
大钟寺	智能原生消费界面改造	提升改造	文保与轨道站域控制条件确认
大钟寺	商务楼宇 AI 服务中枢	提升改造	业主自愿参与机制
大钟寺	钟声文化展示织补	新建织补	文保专项复核
大钟寺	回声钟廊与钟声广场	公共空间	权属与既有通道条件
原点社区	孵化加速载体织补	新建织补	现状建筑与权属数据
原点社区	人才公寓织补	新建织补	人口与配套口径数据
原点社区	现状 AI 研发族保留	保留	无
原点社区	社区服务提升	提升改造	居民意愿调查
原点社区	零公里广场与开发者客厅	公共空间	运营主体确定
众智园	中试实验室织补	新建织补	市政与算力容量复核
众智园	全栈研发族	新建织补	控规条件确认
众智园	现状产业办公保留	保留	无
众智园	校城融合设施提升	提升改造	校方参与机制
众智园	北五环门户接驳枢纽	新建织补	交通与轨道专项
科技服务翼	接口平台与企业服务窗口	公共空间	翼主体范围协调
场景赋能翼	接口平台与低速配送走廊	公共空间	测试许可与安全方案

年度活动体系与转化路径

- 3 月开源春会 | 6 月人字线城市 AI 马拉松 |
- 9 月京张 AI 周与朝圣日 | 12 月里程碑日；
- 每月场景开放日、每周零公里夜话。
- 开发者 → 团队 → 注册主体 → 长期入驻；
- 不构成招商、资金、政策或落户承诺。

板 07 | 指标复核与合规响应

全部面积与比例在 EPSG:4548 下由提交 GeoJSON 复算；23 项必答任务全部映射

指标复算、证据链与任务覆盖

所有面积与比例在 EPSG:4548 下由提交的 GeoJSON 复算 | 缺资料项一律标记为 unknown，不做推算

证据层级：GeoJSON / JSON 为权威数据，图纸与 HTML 为解释层，二者不得冲突

设计范围面积 11.41 km² 临时边界，公告约 11.4 km²	绿地率（复算） 19.0% 绿地面积 ÷ 范围面积	公共空间率（复算） 9.0% 已扣除与绿地重叠
主脊慢行长度 9.75 km road_class=greenway	人字缝合步道 8.37 km road_class=pedestrian	用地地块单元 48 个 完全覆盖、互不重叠
建筑基底示意 26.0 ha 体量研究，非现状普查	AI场景节点 14 处 对应场景卡 S01 - S14	朝圣与荣誉节点 5 处 3 处地标 + 2 处荣誉节点

证据链：从公开来源到可复核结论



任何无法从结构化数据复算的面积、比例、规模或数量，不写入正式结论。

标记为 unknown 的资料缺口（不做推算）

- 容积率 floor_area_ratio: 缺已批准控规条件
- 建筑高度 building_height_m: 缺高度 / 航空 / 文保限高
- 常住人口 resident_population: 缺与范围一致的口径
- 官方红线与三处重点区精确 polygon: 待资格预审文件包

数据来源：本图由本投稿 geometry/*.geojson 与 metrics.json 在 EPSG:4548 下派生绘制，不使用商业地图底图、新闻示意图或外部瓦片。

任务覆盖（compliance_matrix.json）

公告 1.3 设计目标

1.3.1	1.3.2	1.3.3
-------	-------	-------

公告 1.4 范围层次

1.4.1	1.4.2	1.4.3
-------	-------	-------

公告 1.5 设计内容

1.5.1.1	1.5.1.2	1.5.2.1
1.5.2.2	1.5.2.3	1.5.2.4
1.5.2.5	1.5.3.required	1.5.3.1
1.5.3.2	1.5.3.3	

面向智能体任务书

agent.1	agent.2	agent.3
agent.4	agent.5	agent.6

全部 23 项必答任务均映射到章节、图层、指标、图纸与 HTML 段落。

自检项	结果	级别
BOUNDARY_TRUST	pass	major
KEY_AREAS_TRUST	pass	major
LAND_USE_TOPOLOGY	pass	major
LAYER_INSIDE_SITE	pass	major
METRIC_RECALC	pass	major
VISUAL_STATIC	pass	info
VISUAL_METRIC_CONSISTENCY	pass	major
TASK_COVERAGE	pass	major
PROFESSIONAL_EVIDENCE	pass	major
CLAIM_BOUNDARY	pass	blocking
COPYRIGHT_CLEARANCE	pass	blocking
OFFICIAL_GEOMETRY_AVAILABLE	unknown	major

待补资料（标记 unknown，不做推算）

容积率 floor_area_ratio | 建筑高度 building_height_m

常住人口 resident_population

官方红线与三处重点区精确 polygon

证据链

sources.json → geometry/*.geojson → metrics.json →

风险与人工复核

三张 matrix.json → proposal.md / self_check.json

数据隐私 | 空间争议 | 政策不确定性 | 实施复杂度 |

技术成熟度 | 运维成本 | 公平与包容性——

七个维度逐条给出缓解措施与人工复核路径。

详见 proposal.md 第十二节。