

零号里程碑 ZERO MILESTONE


京张AI原点带城市设计 · 展板 B1 · 总体概念与三层范围

京张铁路的 0 公里起点在北京北站（原西直门站）——中国人自主修建的第一条干线铁路的「第 0 公里」；程序员的世界从 0 开始计数，AI 建立在 0 和 1 之上。本方案把创新带组织成一条零索引轴（Zero-Indexed Axis）：从南端 Km 0.0 到北端 Km 6.0，每个节点用「铁路公里标 + 计算机索引号」双重编号，让百年铁路的里程碑语言成为 AI 时代的公共寻址语言。

空间结构：一轴七节点 · 三带两翼；三处重点区 = 接口段（大钟寺 Km 1.0）· 原点段（五道口 Km 3.0）· 加速段（众智园 Km 5.0）



五段创新链 FIVE-STAGE INNOVATION CHAIN

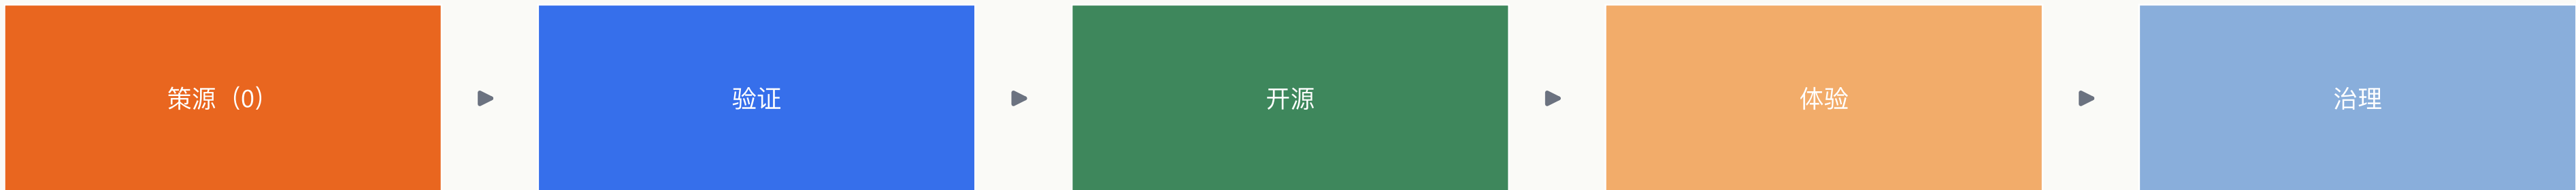

零成本要素翼（中关村科技服务翼）· 零门槛场景翼（小月河场景翼）

年度活动品牌：零时 Zero Hour —— 零点发布 · 开源共创周 · 受控测试季 · 成果发布周 · 治理评议周


三层范围 THREE-LEVEL SCOPE

统筹研究范围 Coordinated Research Area	AI 产业生态与未来城市形态如何组织；建立「策源（0）—验证—开源—体验—治理」创新接力链，形成三区两翼协同回路与全球 AI 创新活动体系。
约 43.6 km ² ~43.6 km ²	
总体设计范围 Overall Design Area	产业空间、城市更新、交通市政与风貌如何落图；一轴七节点、两翼三带，节点按 Km 0.0-Km 6.0 编号，用地、建筑、道路、绿地、公共空间与分期图层共同表达。
约 11.4 km ² ~11.4 km ²	
重点区域范围 Key Areas	三处片区如何达到详细设计深度；三座节点：接口段 / 原点段 / 加速段，每区给出定位、空间动作、AI 场景与实施依赖。
约 368.4 公顷 ~368.4 ha	
五问门槛 FIVE-QUESTION GATE	每个 AI 场景进入前必须回答：为谁服务 · 使用什么数据 · 谁来复核 · 失败如何退出 · 公共收益如何留下。


边界与重点区当前均为 provisional（临时粗略）：site 复算 11,412,825.386 m²（仅包内一致性）；临时大钟寺 polygon 质心距真实大钟寺站约 2.26 km（Issue #1029）；official 边界发布后整包重算。

展板 B2 · 用地与建筑容量

60 个共享边界用地单元完整覆盖临时 site（覆盖率 100%，无缝隙、无重叠）· 189 个概念建筑基底验证空间容量

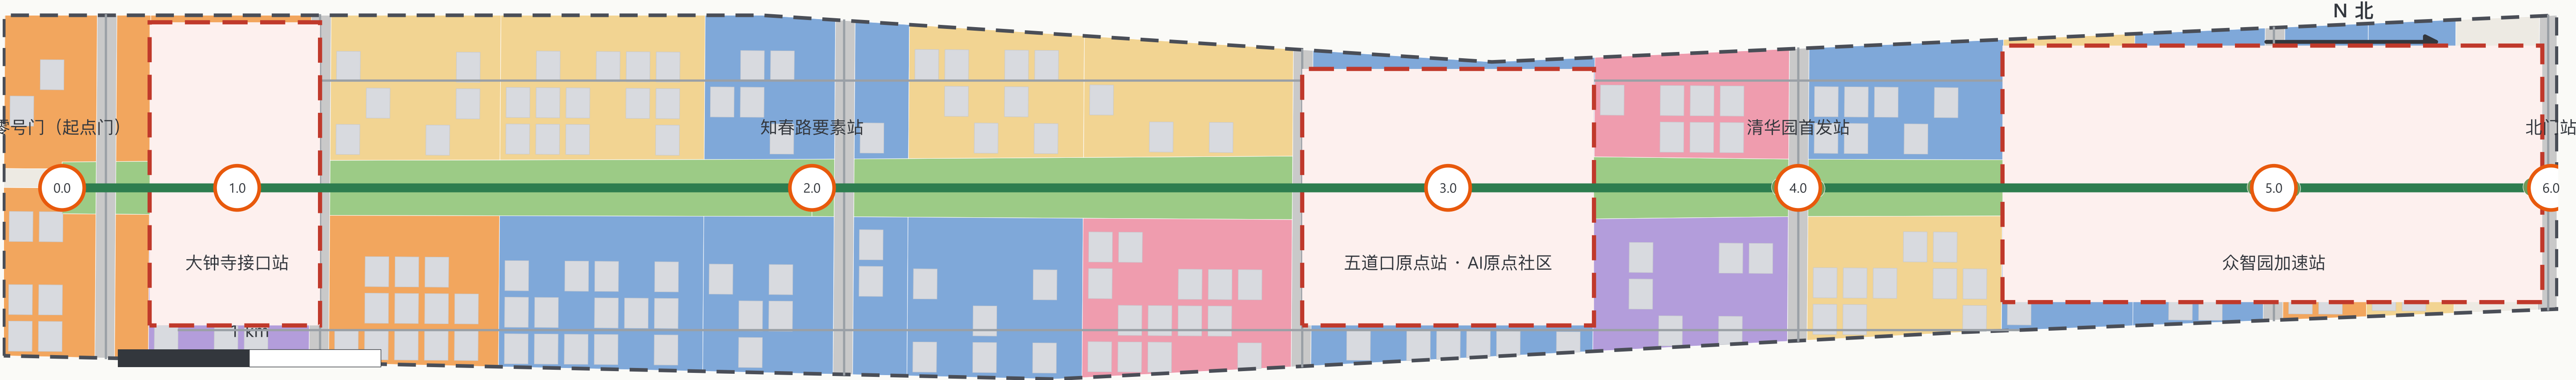

用地结构（公顷与占比）

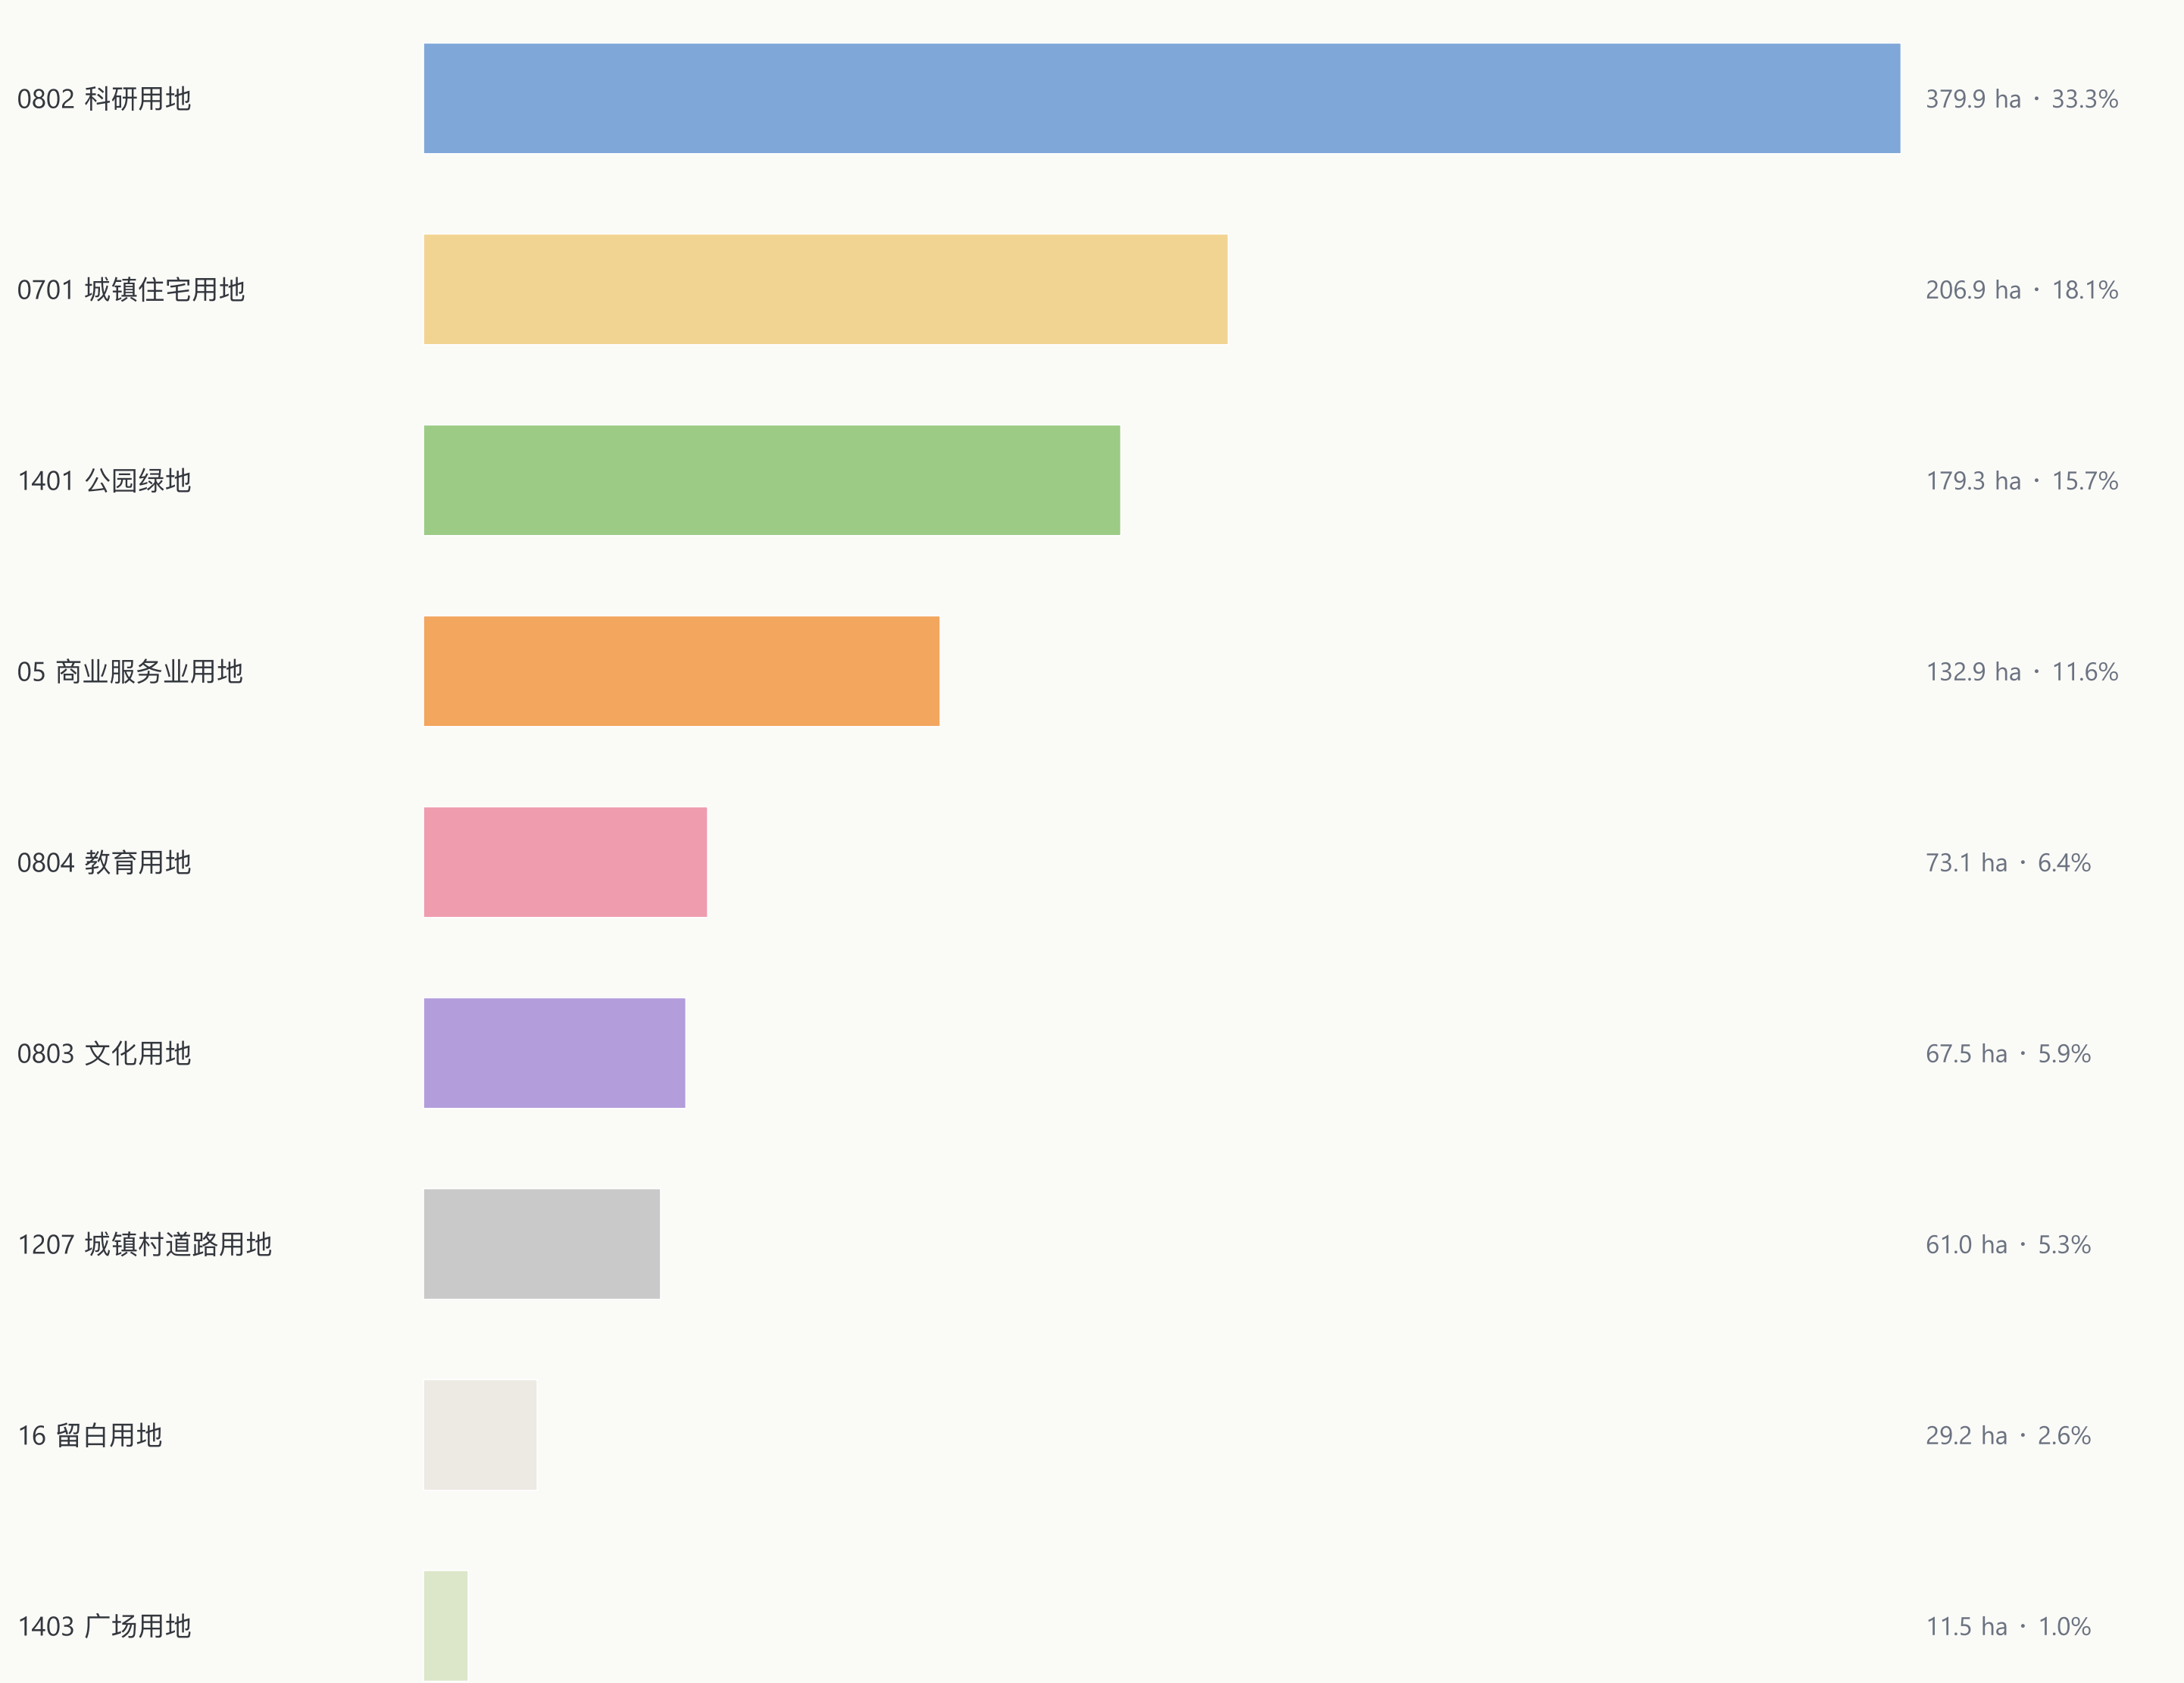

建筑容量 BUILDING CAPACITY

189

概念建筑单元

1,860,807.668 m²

建筑基底总面积

16.3045%

建筑密度（基底 / 场地）

管控指标（unknown）：容积率、建筑高度、退线——缺官方控规条件，原因已登记；建筑基底只用于验证空间容量与产业空间供给逻辑，不表示现实建筑。


索引格网：产业按状态供给 INDEX GRID

0802 科研	验证与策源载体 · 长期稳定供给
05 商业	体验与消费界面 · 绿灯稳定开放
0701 居住	生活承载 · 无 AI 等价格路径保底
0804 教育	策源与人才 · 校-园-城缝合
1401 绿地	零索引轴公共界面 · 全时开放
16 留白	状态待定的弹性载体 · 不预置功能

融合规则：黄灯限期供给（到期评估、扩绿或转红） · 绿灯稳定供给（不因运营方更替中断） · 红灯可收回再配置（退役即拆除，载体回到可再分配状态）。

展板 B3 · 三大重点区域


三处重点区 = 零索引轴的三个段位：接口段（大钟寺 Km 1.0）· 原点段（五道口 Km 3.0）· 加速段（众智园 Km 5.0）；共用「五问门槛」。

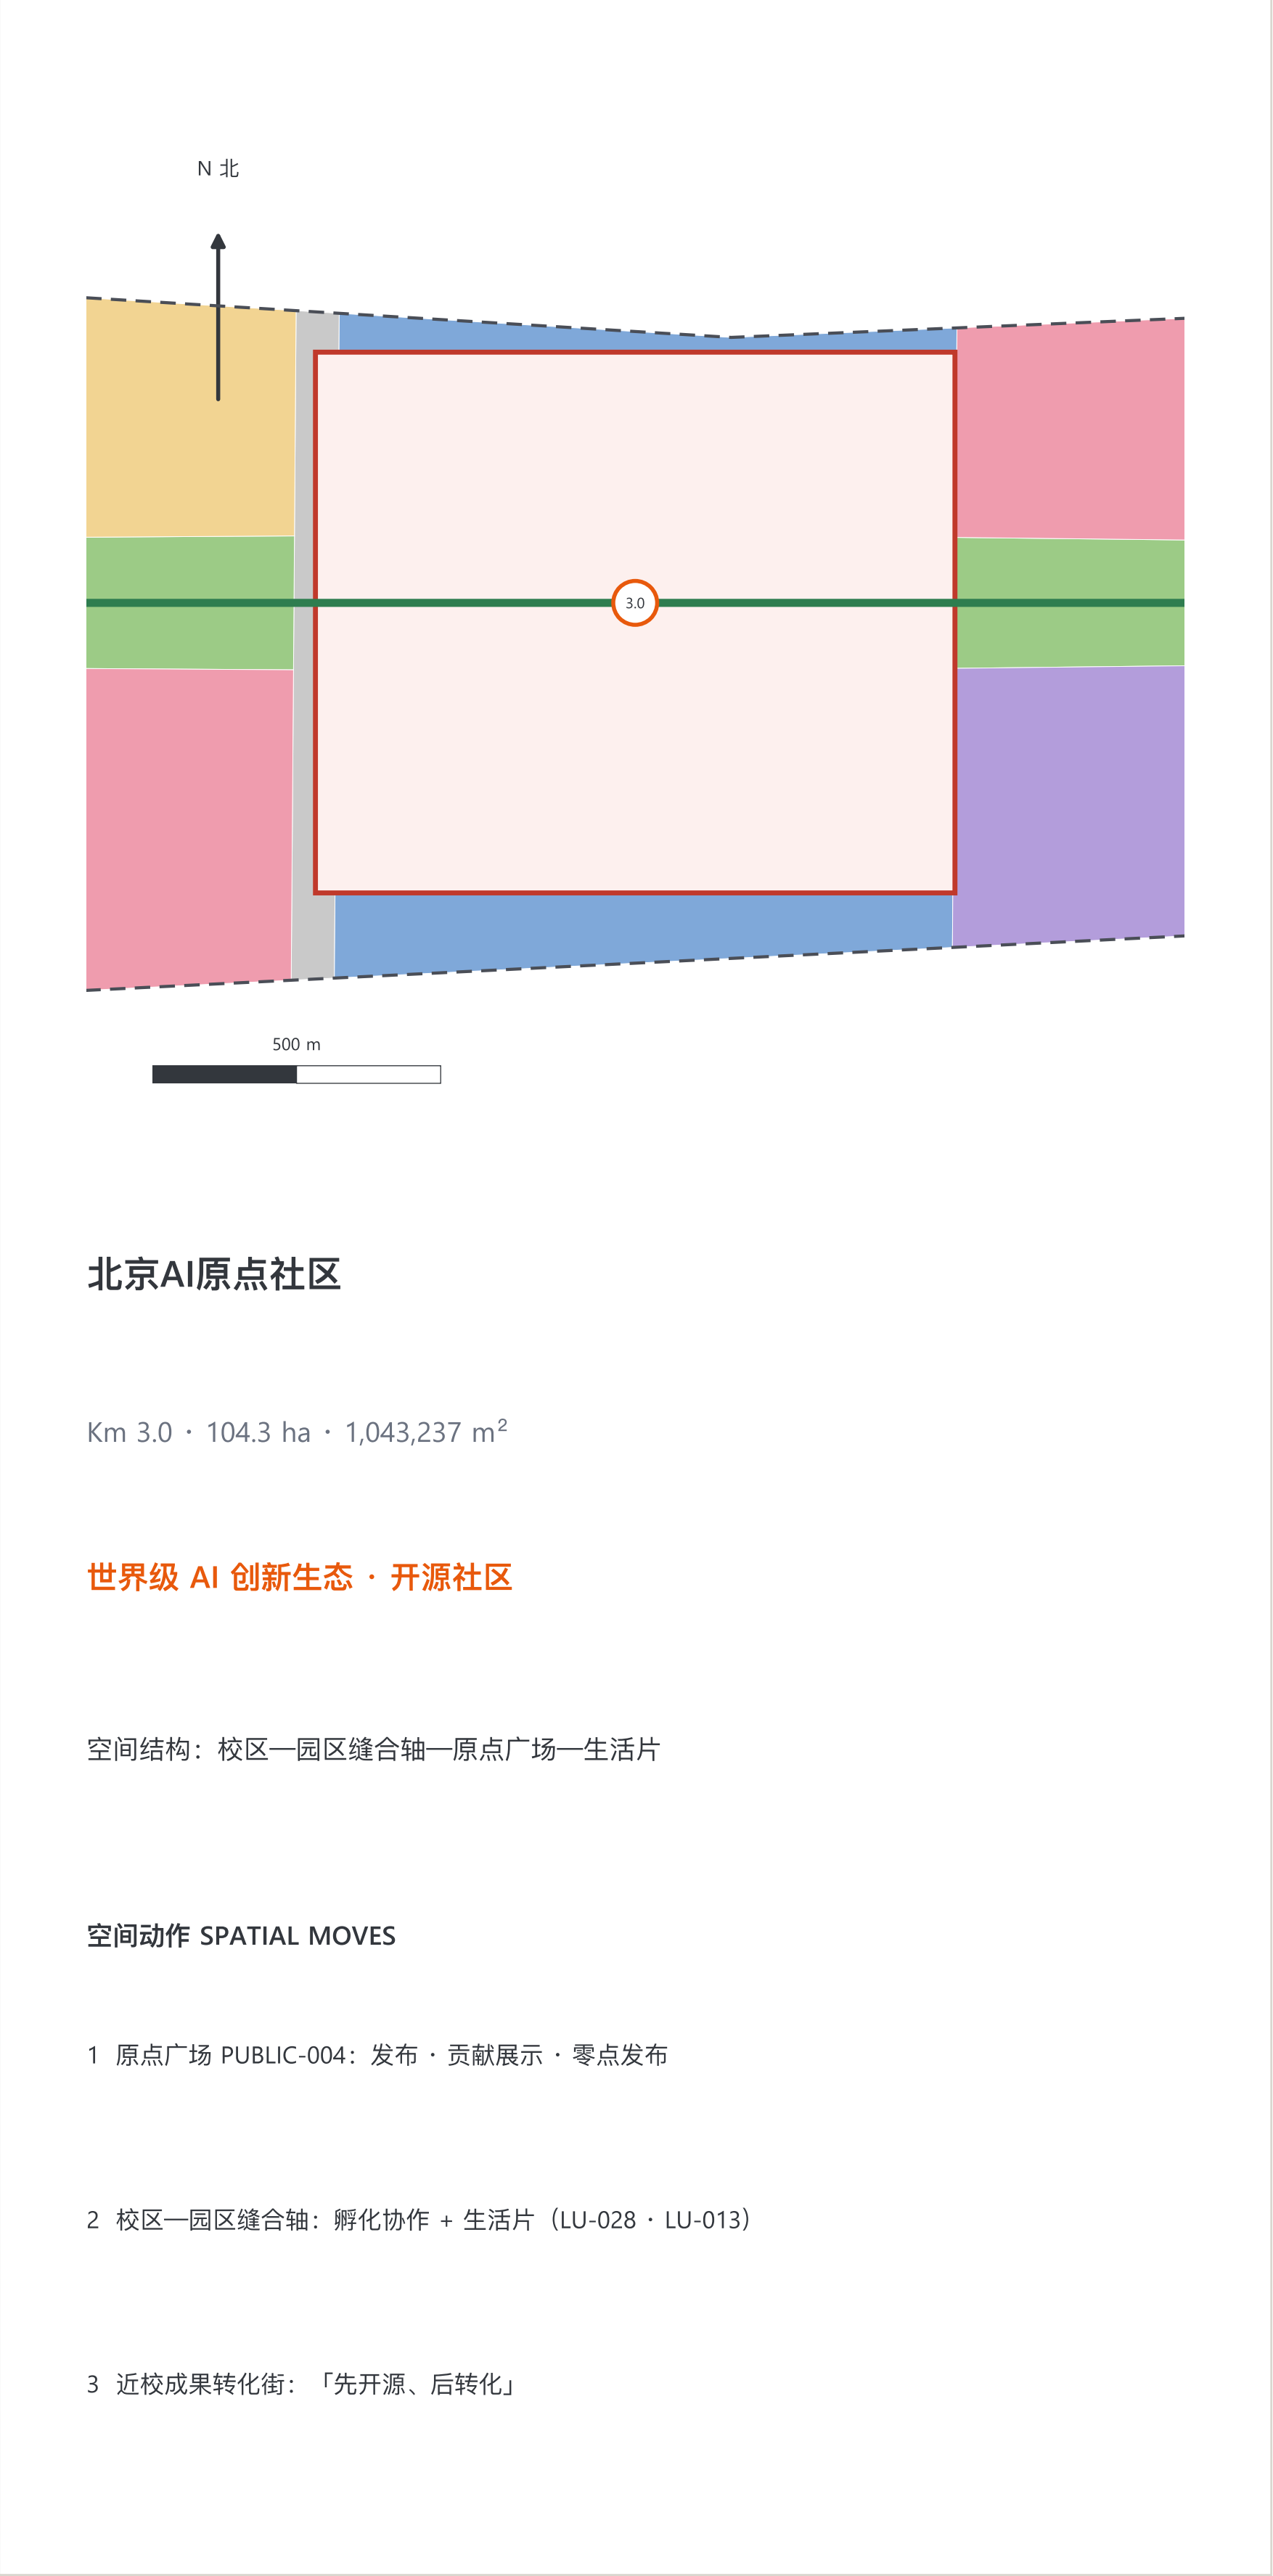

三处重点区的临时 polygon 包内复算面积：众智圆 1,929,201.877 m² · AI 原点 1,043,236.909 m² · 大钟寺 720,454.219 m²，合计 3,692,893.005 m²，与公告约 192.1 / 104.3 / 72.0 公顷量级一致；official polygon 到位后以官方边界重算。

展板 B4 · 蓝绿交通与实施指标

零索引轴绿带为骨架：东西缝合、南北连通；节点 10 分钟服务圈；道路均为方向性策略，红线待官方资料。

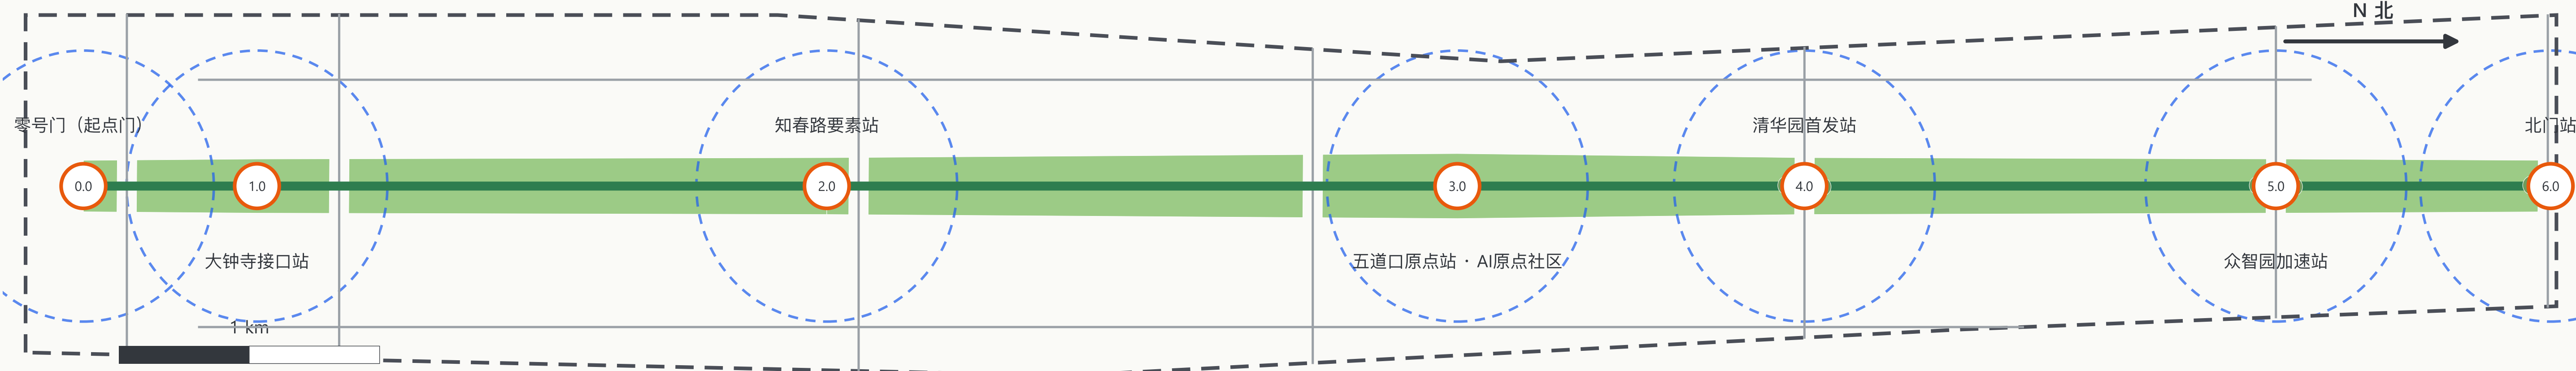

32,780.221 m	9,471.589 m	15.7112%	1.0070%
道路长度	绿道长度	绿地率	公共空间率
2,890,732.911 m ²	4,745,599.743 m ²	1,515,886.865 m ²	12 · 3
近期 (Km 3-4 核心段)	中期 (大钟寺-知春路段)	远期 (南北门户段)	AI 场景 · 测试验证
5 · 4 · 7	3,692,893.005 m ²	11,412,825.386 m ²	189 · 16.30%
画像 / 地标 / 案例	重点区合计	场地面积	概念建筑 · 密度

更新项目清单 (8 项) 与分期

编号	项目名称	类型	分期
ZM-01	零索引导视与公里标系统	公共空间 / 品牌	近期
ZM-02	原点-清华园核心段缝合 (Km 3-4)	城市更新 / 慢行	近期
ZM-03	众智园清河低碳创新界面	蓝绿空间 / 产业展示	近期
ZM-04	大钟寺站四象限步行连通	轨道一体化 / 慢行	中期
ZM-05	知春路数据要素会客厅	产业服务 / 更新	中期
ZM-06	七座节点广场实施	公共空间 / 品牌	中期
ZM-07	里程碑林与贡献墙	荣誉体系 / 公共艺术	近期
ZM-08	无 AI 等价服务点网络	公共服务 / 新基建	近期

近期 · 原点-清华园核心段 (Km 3-4)
2,890,733 m²
6%

中期 · 大钟寺-知春路段
4,745,600 m²
51.9%

远期 · 南北门户段
1,515,887 m²
16.6%

实施方法：限期试点—年度评估—扩大或回退；绿灯开放并接受申诉，黄灯限期测评与人工复核，红灯到期整改或退役（设备可拆除、数据可回滚）。

证据链 EVIDENCE CHAIN · EPSG:4548 可复算



全部空间指标由包内几何按 EPSG:4548 复算至同一位小数；三矩阵与自检结果作为 formal 证据；管控指标（容积率 / 高度 / 退线）待官方控规，保持 unknown。