


Board 1 · Overall Design Structure

One Spine, Three Needles, Four Stitch Galleries, Two Wings · JINGZHANG STITCH BELT

Taking the heritage park left by the buried Jingzhang Railway as the city's seam, stitching actions restore east-west connections, connect the north-south green ridge, and organize transit transfer.

Overall Concept · One Spine, Three Needles, Four Stitch Galleries, Two Wings

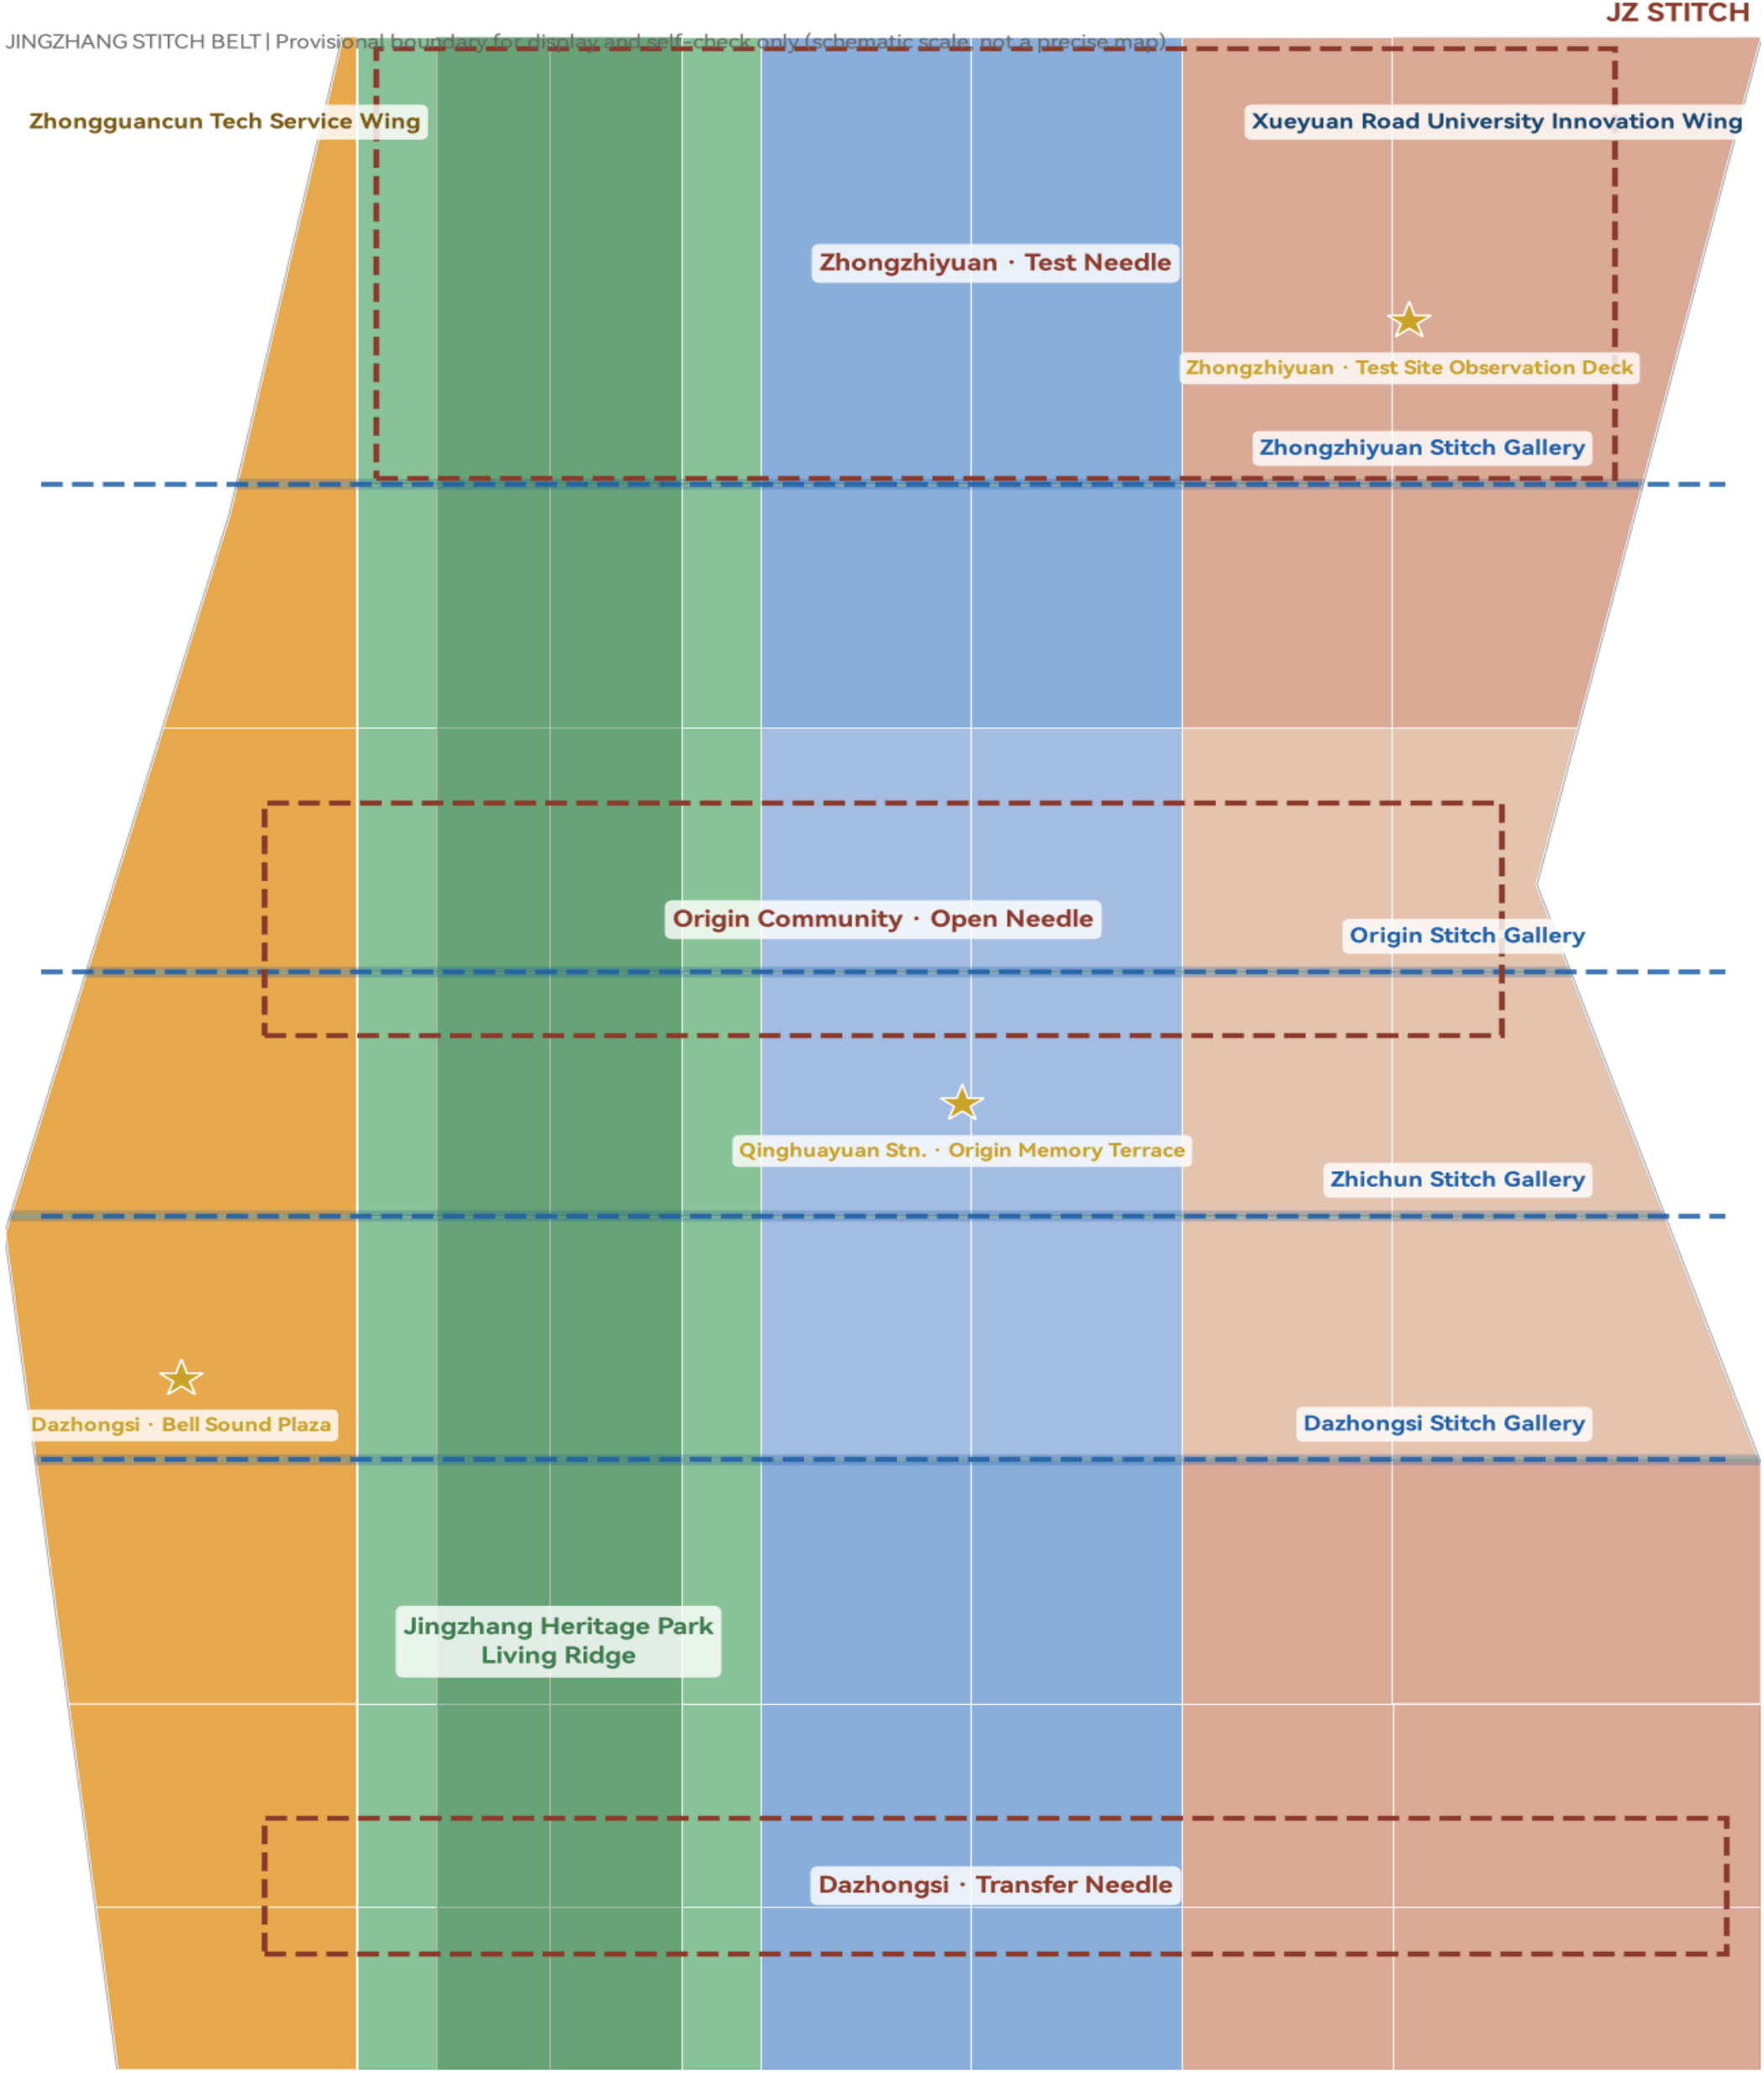


Provisional rough boundary is for display and self-check only; recalculate after official polygons are released. All conclusions are authoritative in GeoJSON/metrics.

Board 2 · Land Use and Urban Renewal

72 land-use cells covering the full site · Retain first, mend as the main method, renew as the supplement

Green space along stitch lines, industry along the university interface, community adjacent to innovation services; building clusters are conceptual illustrations.

Land-Use Zoning and Spatial Structure

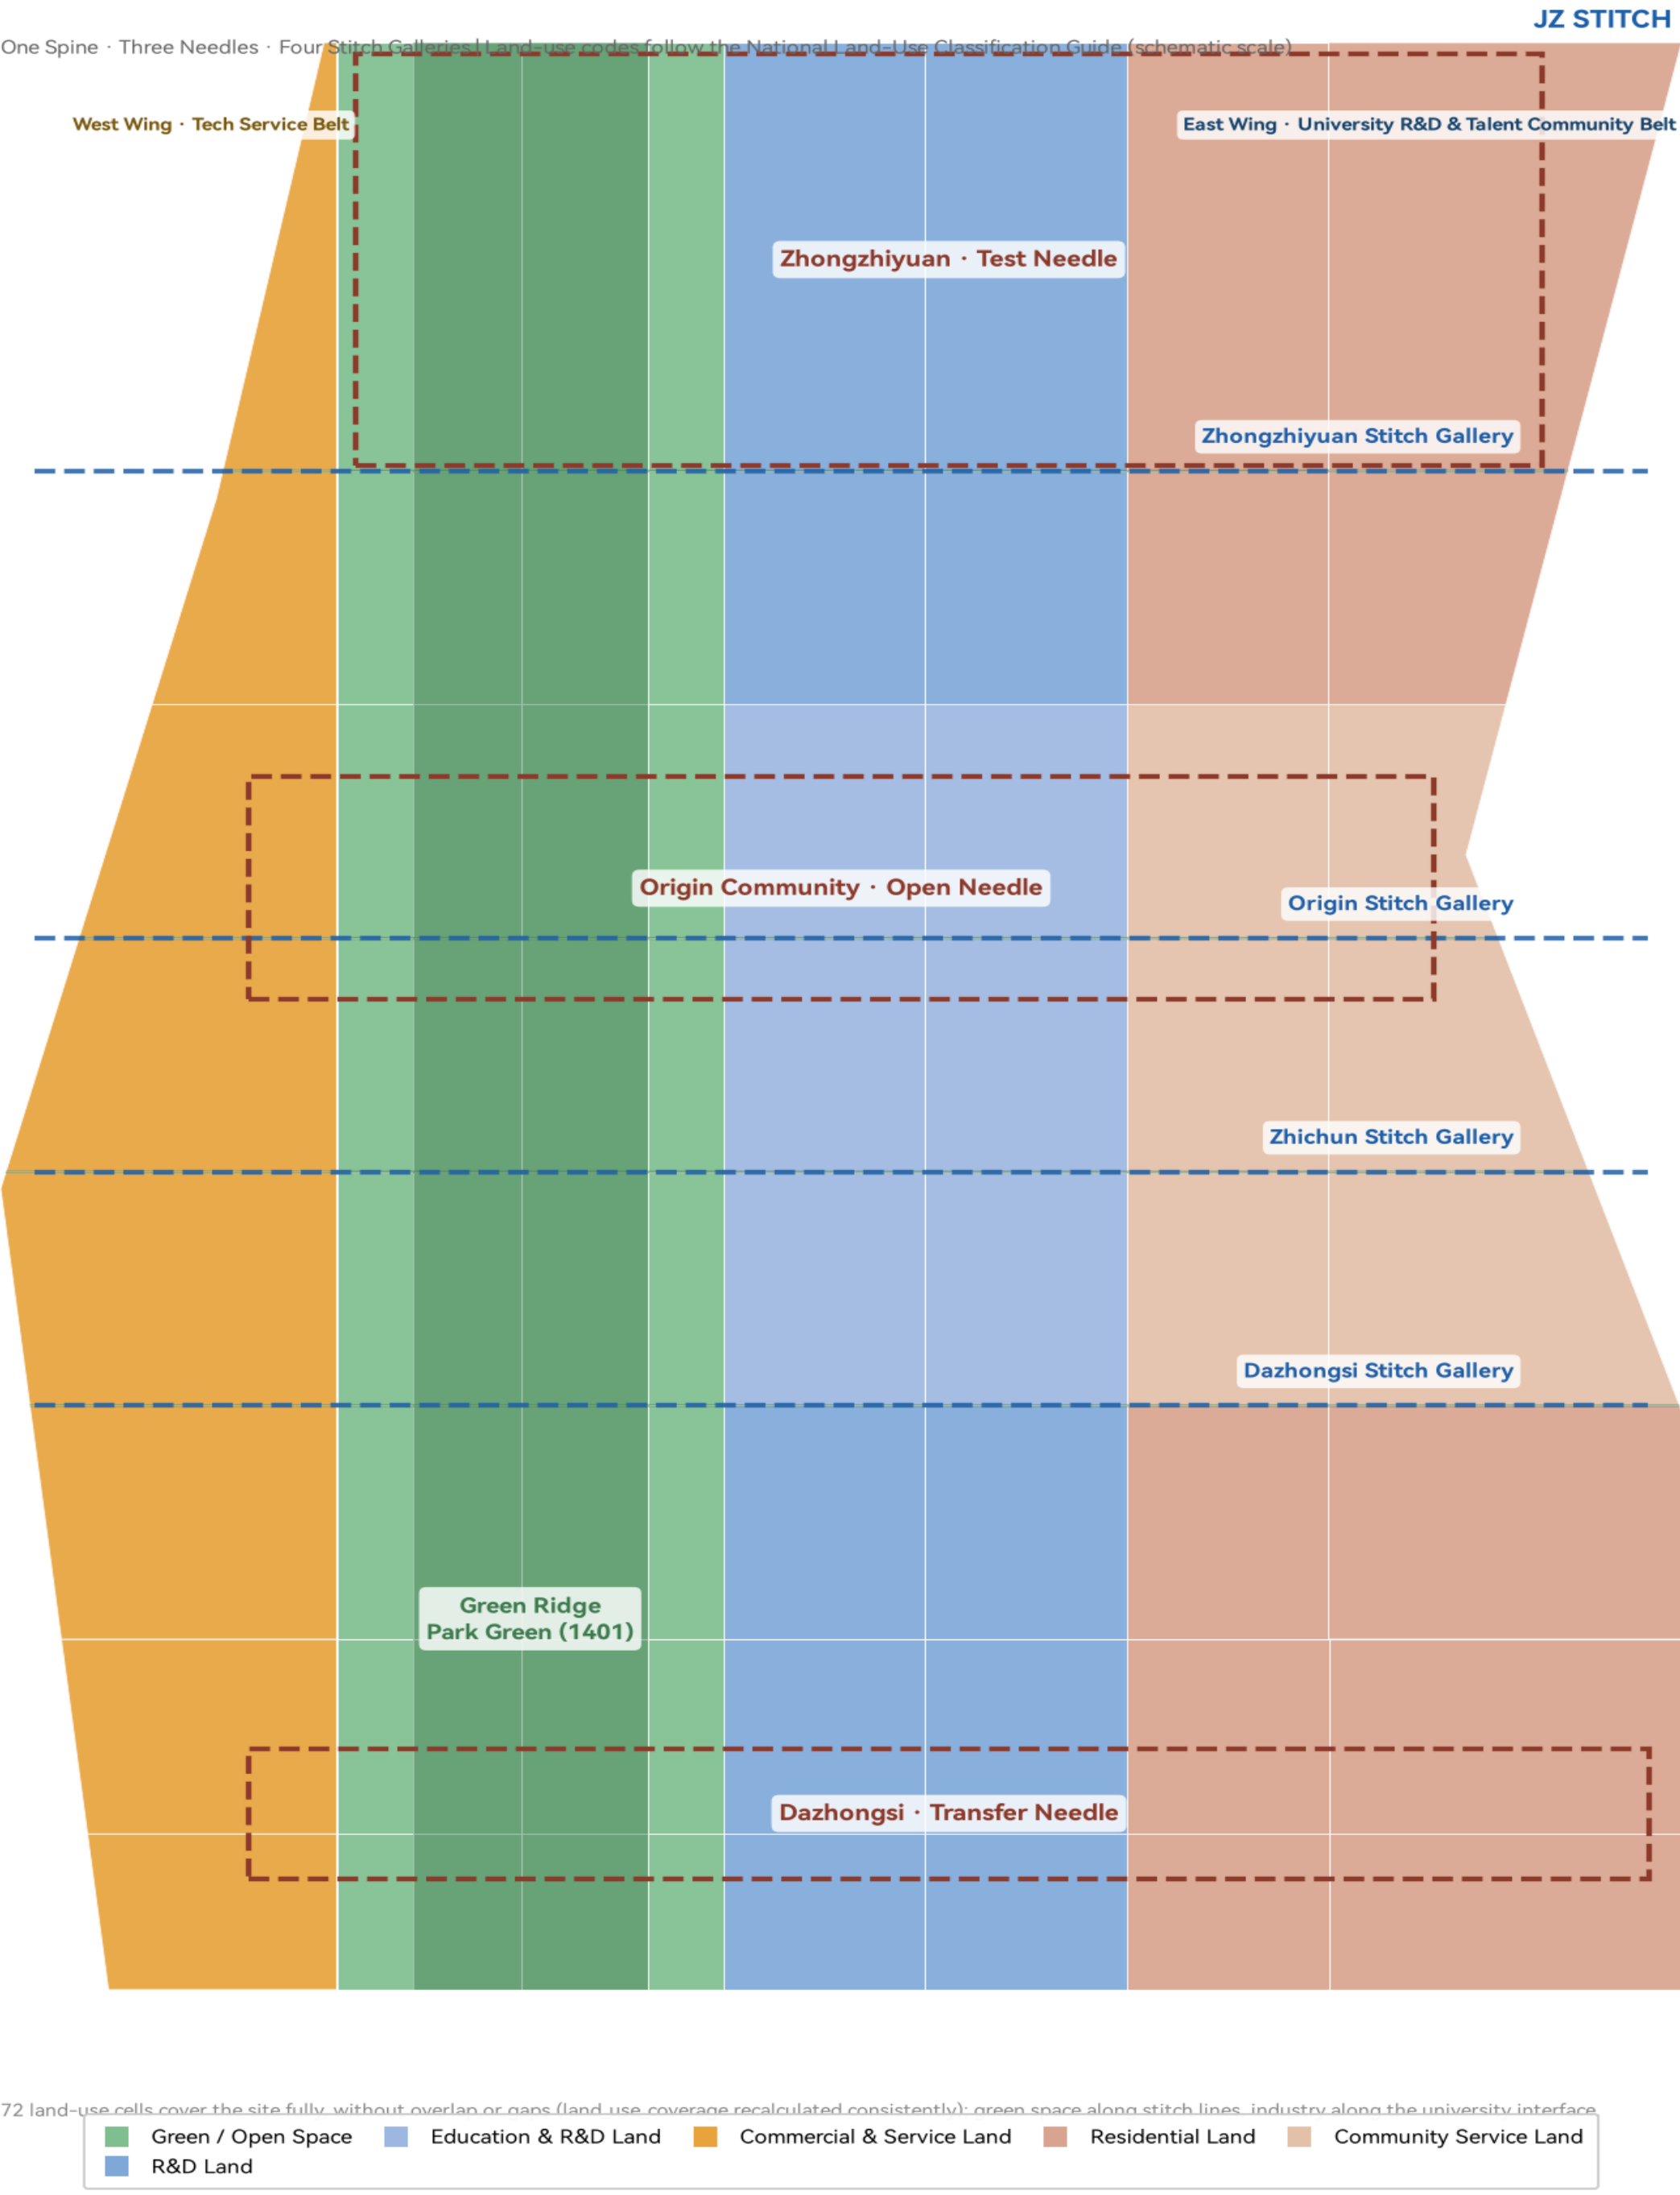


Provisional rough boundary is for display and self-check only; recalculate after official polygons are released. All conclusions are authoritative in GeoJSON/metrics.

Board 3 · Transport, Transit, and Blue-Green Public Space

Stitch-first traffic organization · Trunk-branch-leaf blue-green network

Cross-section reallocation of four stitch galleries; three-level transit station—stitch gallery—green ridge connection; 12 AI scenario cards anchored to real nodes.

Transport & Slow Mobility · Blue-Green Public Space · AI Scenario System

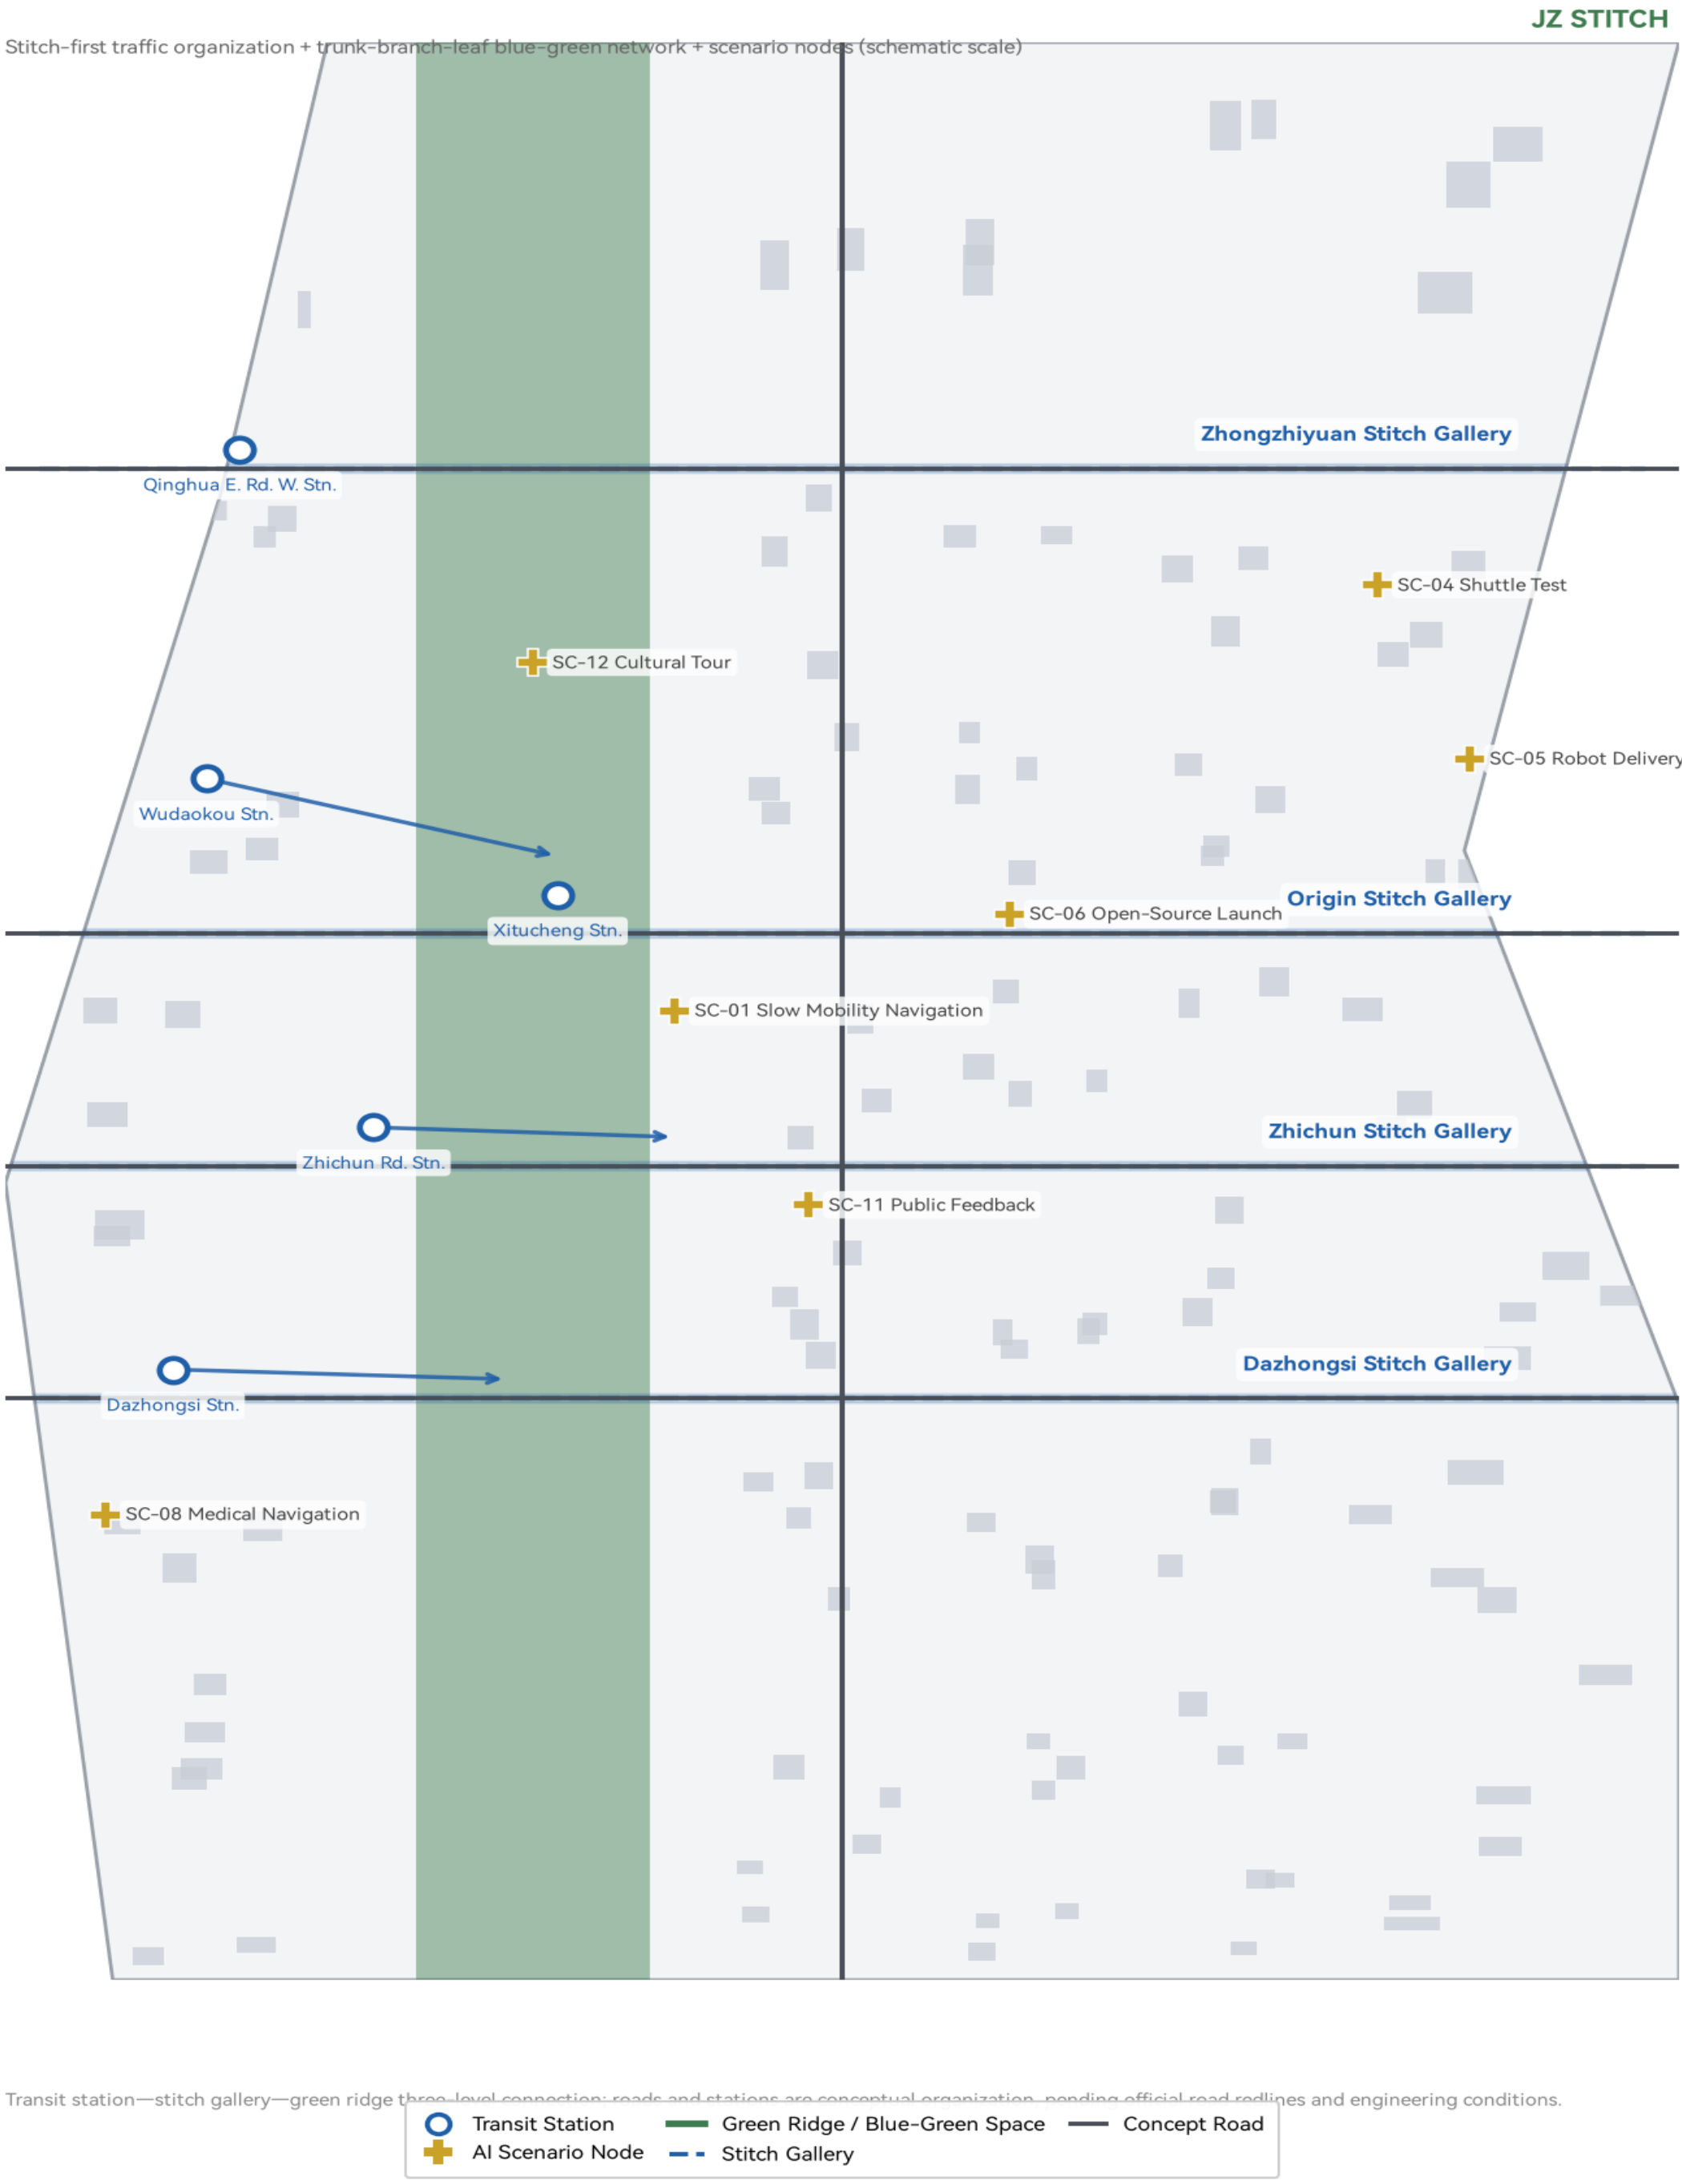


Board 4 · Key-Area Detailed Design

Test Needle / Open Needle / Transfer Needle

Differentiated positioning, spatial structure, scenarios, and implementation dependencies of three key areas; key areas are provisional rough polygons.

Three Key Areas · Detailed Design Index

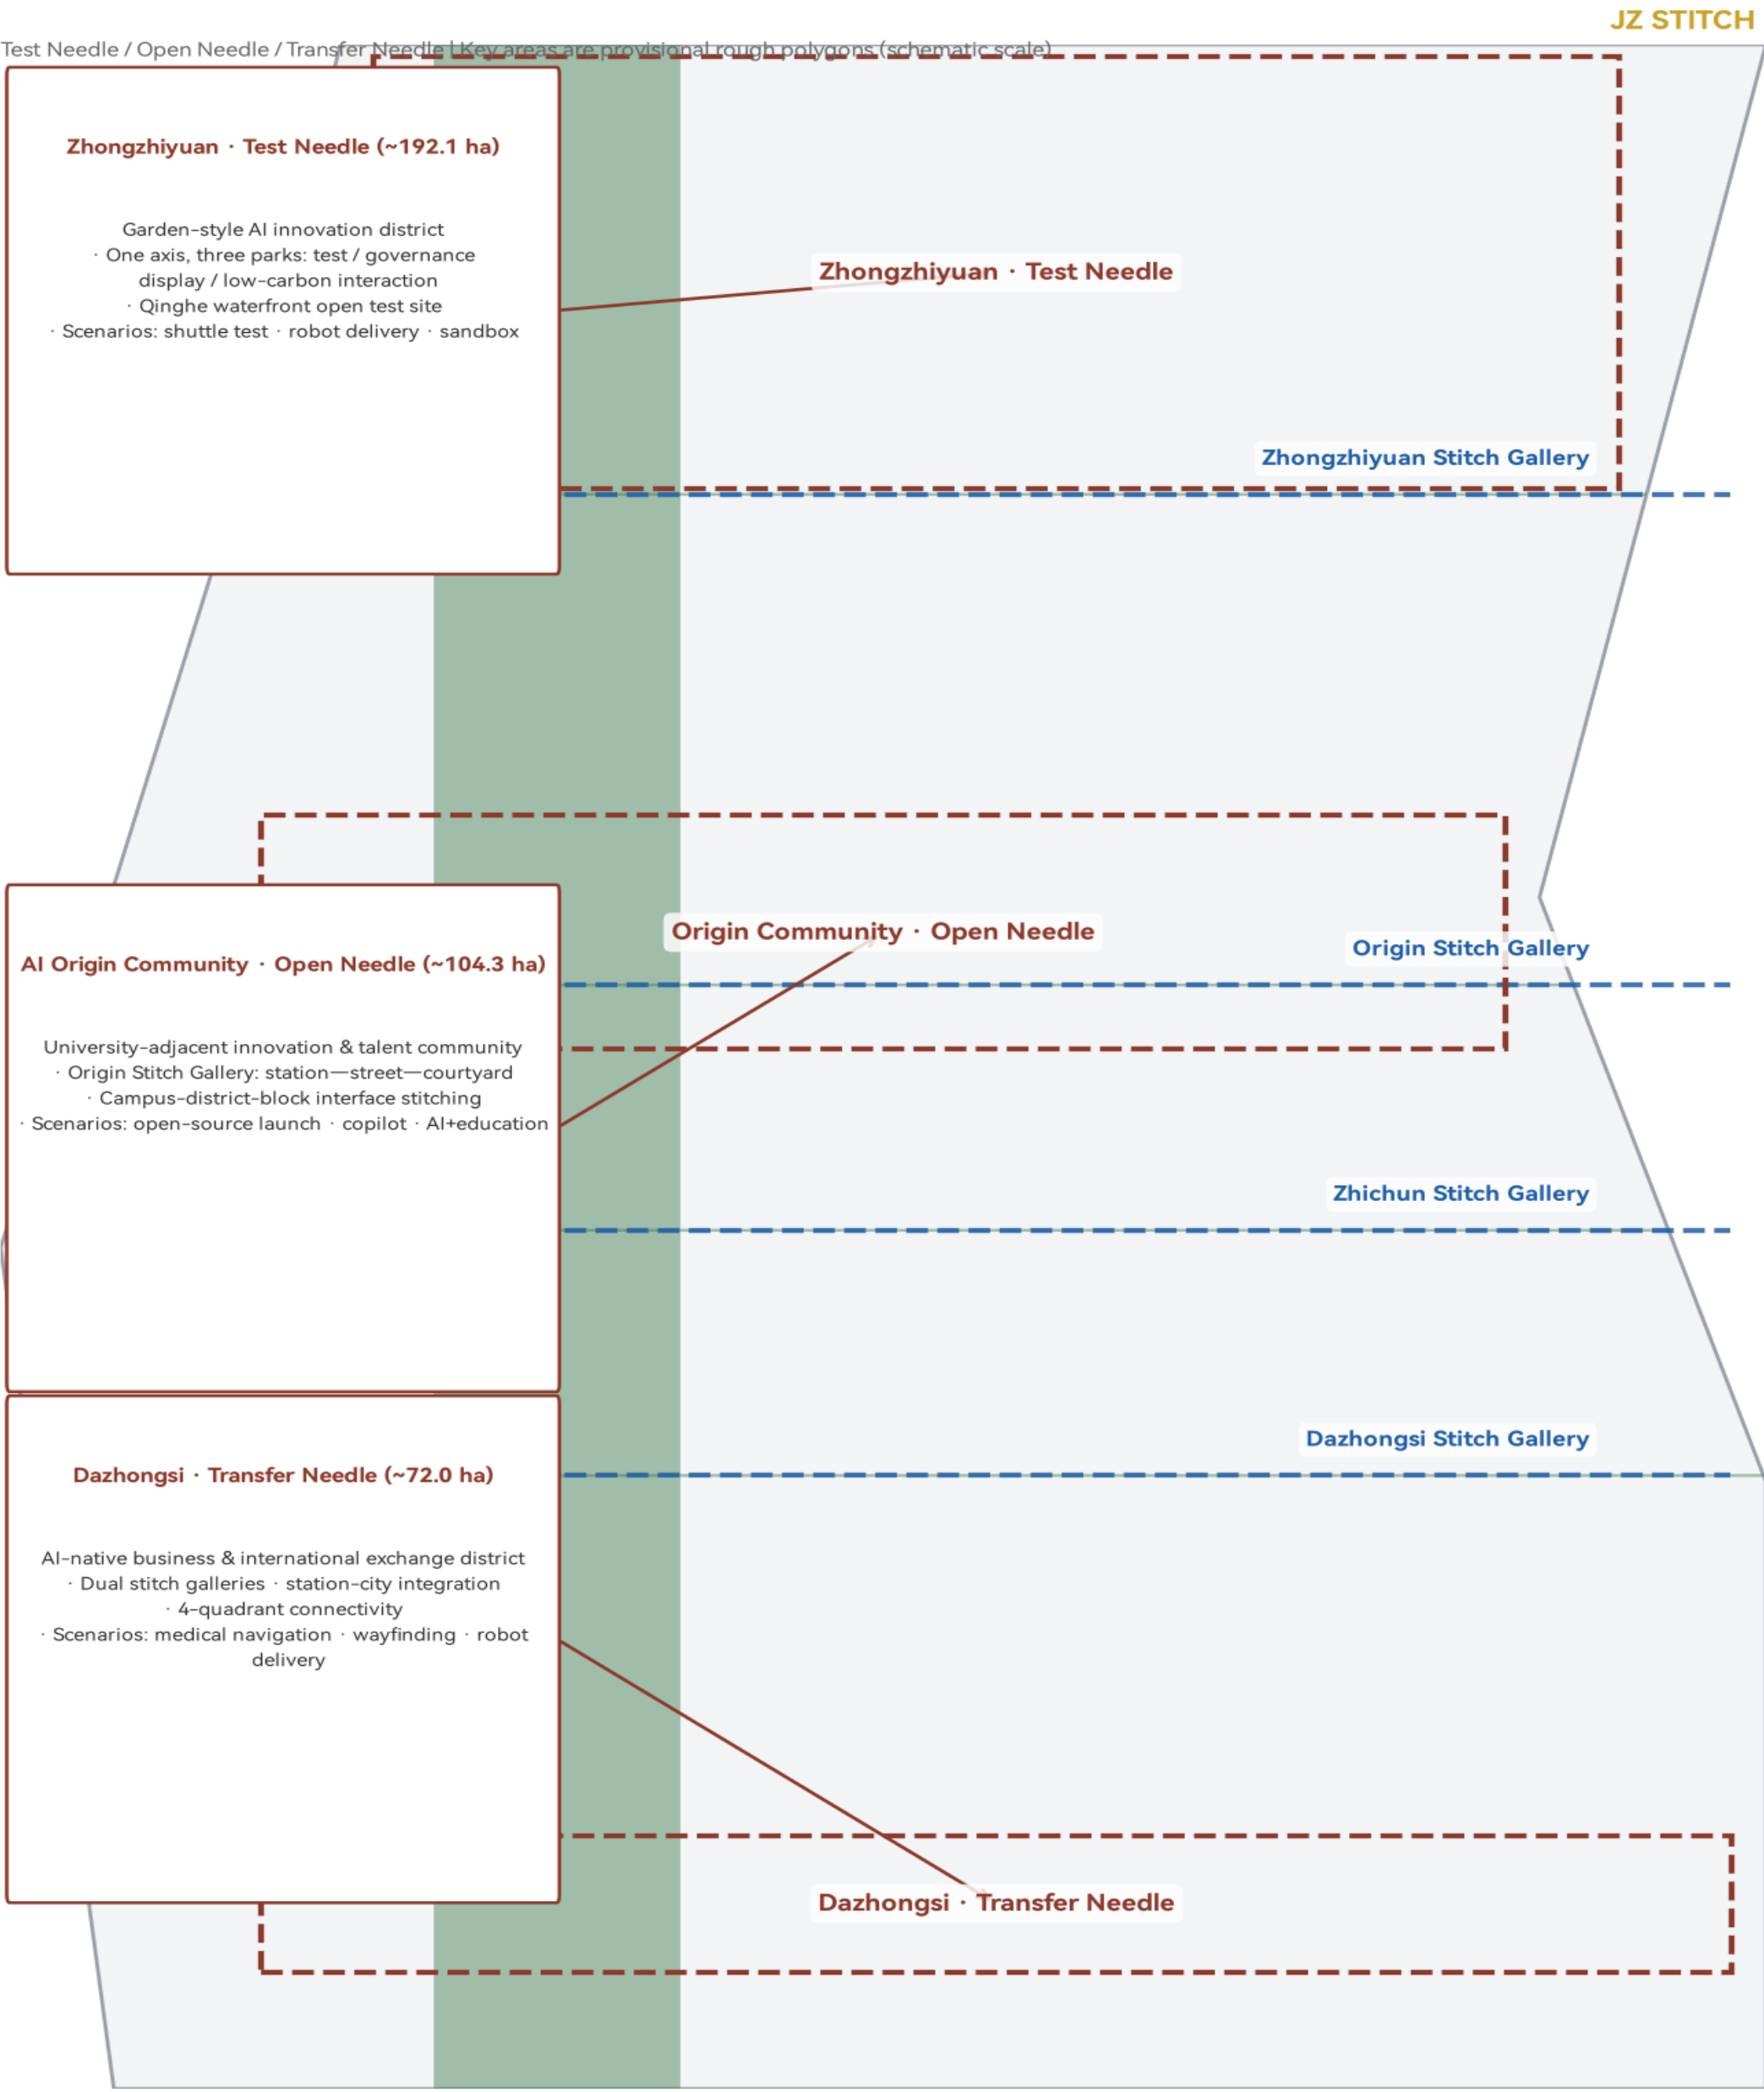

All three-area designs are directional conceptual recommendations; recalculate after official polygons are provided. Dependencies: road redlines / ownership / regulatory plans / station integration

Key Area (provisional) Stitch Gallery Green Ridge

Provisional rough boundary is for display and self-check only; recalculate after official polygons are released. All conclusions are authoritative in GeoJSON/metrics.

Overall Design Area [site_area_sqm] 11,412,825 m² Formula: polygon_area(site.boundary) Source: geometry/site.boundary.geojson	Land-Use Coverage [land_use_coverage_sqm] 11,412,848 m² Formula: sum(land_use) Source: geometry/land_use.geojson
Green Ratio [green_ratio] 16.5% Formula: green/site Source: geometry/green_space.geojson	Public Space Ratio [public_space_ratio] 1.7% Formula: public/site Source: geometry/public_space.geojson
Stitch Gallery Count [stitch_corridor_count] 4 Formula: count(PUB) Source: geometry/public_space.geojson	Key Area Count [key_area_count] 3 Formula: count(KEY_AREA) Source: geometry/key_areas.geojson
Concept Building Footprint [building_footprint_area_sqm] 361,487 m² Formula: sum(buildings) Source: geometry/buildings.geojson	Floor Area Ratio [floor_area_ratio] Pending Formula: Official regulatory conditions missing Source: planning/limits.json

Evidence chain: GeoJSON layers → EPSG:4548 projection recalculation → metrics.json → drawings/HTML presentation; all areas under the provisional boundary are for display and self-check only, not official precise areas; full recalculation after official polygons are released.

Provisional rough boundary is for display and self-check only; recalculate after official polygons are released. All conclusions are authoritative in GeoJSON/metrics.