

一环双轨


前行轨=遗址公园文化慢行轴;回传轨=科创服务环;在原点站交汇成「人」字。

人字形回路 · 总体概念

前行轨(遗址公园文化慢行轴)+ 回传轨(科创服务环)在原点站交汇成「人」字;三站十二口组织 11.4 km² 总体设计范围

京张·人字回路

百年京张AI创新带

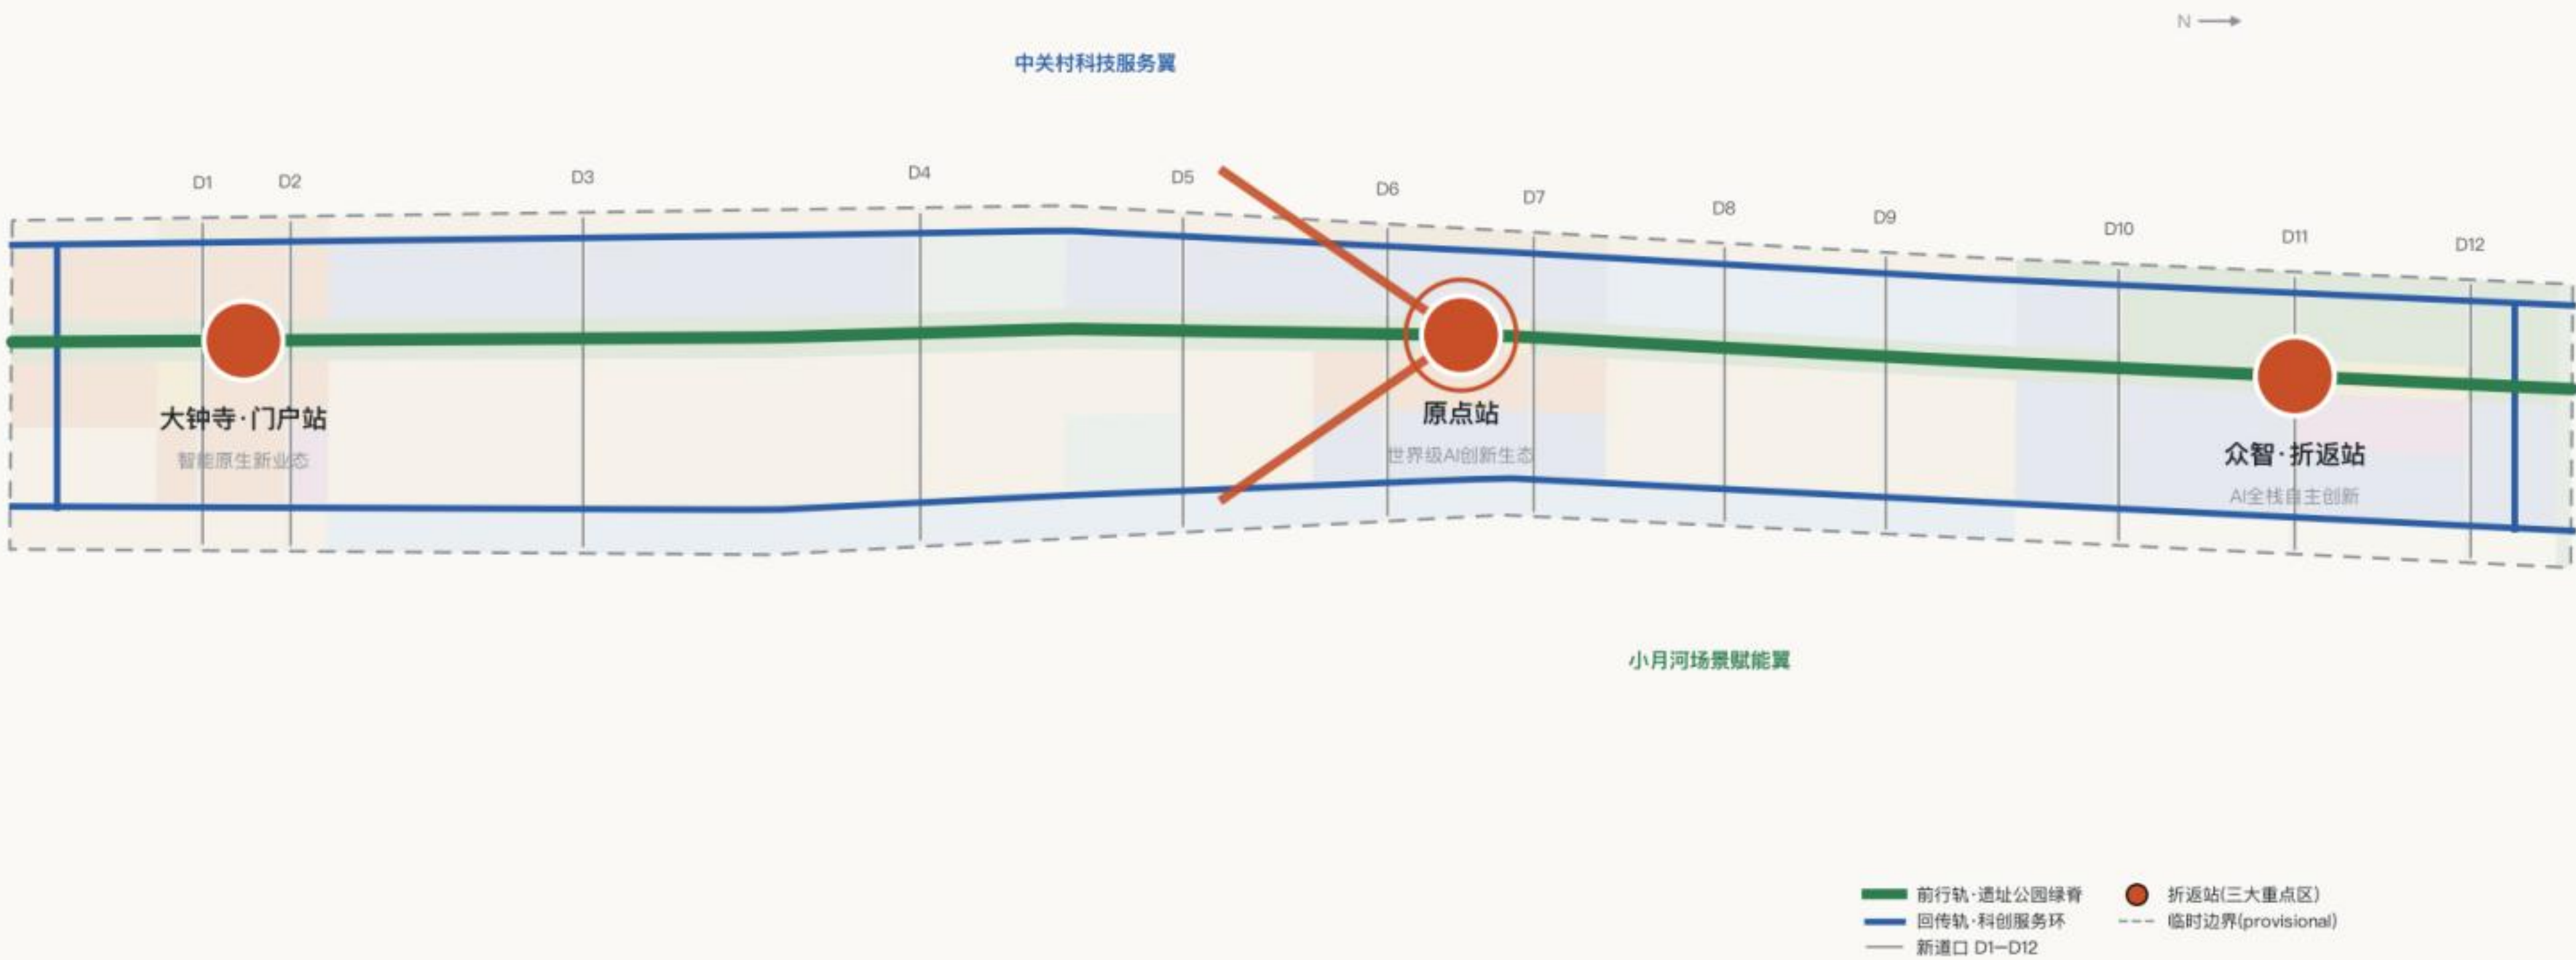

三站十二口

大钟寺·门户站 / 原点站 / 众智·折返站;12处新道口以600—900m间距缝合东西。

三大定位映射

文化带=前行轨;生活体验带=道口与场;融合创新带=回路整体。

概念转译

1908

青龙桥人字形折返-前行—换向—再前行

2026

反向传播:前向推理—误差折返—更新

城市

场景产生数据(前行),反馈更新空间与政策(折返)

边界状态:临时粗糙边界(provisional),由公告文字四至与面积拟合,不表达官方红线;官方数据发布后整链重算。数据来源:公告 + 仓库场地资料包;图面由包内 GeoJSON/metrics 程序化派生。

无缝分割


280个单元共享切分线、零重叠;绿脊与道口先锁定公共骨架。

三层范围传导 × 用地结构

用地分区为临时边界的无缝完整分割(280 个单元,共享切分线,零重叠);绿脊与道口先锁定公共骨架,建设用地在骨架间织补

京张·人字回路

百年京张AI创新带

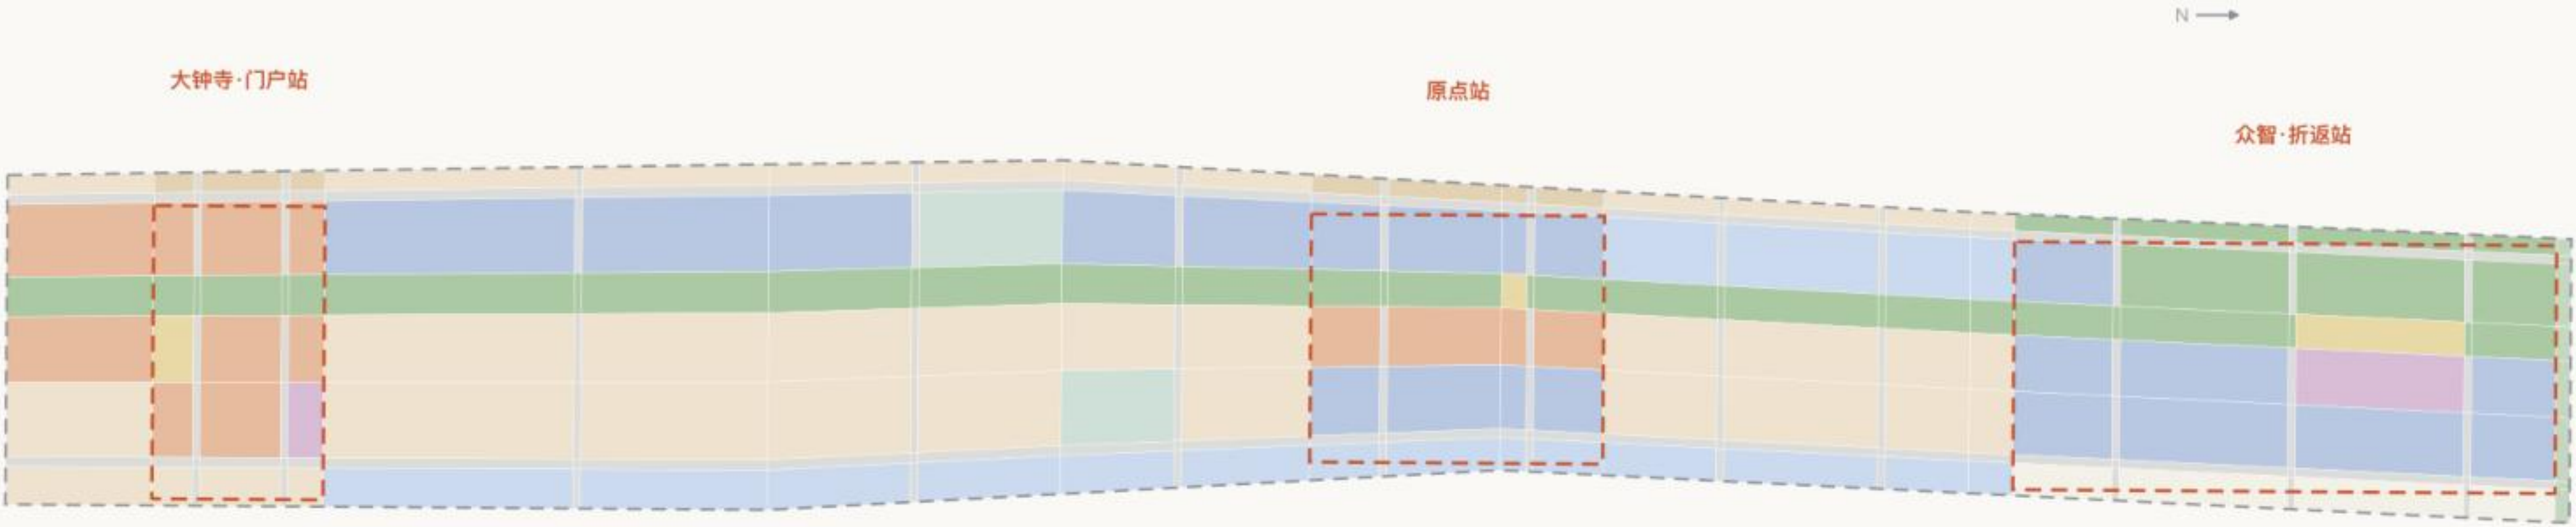

用地平衡

居住28.7% / 科研19.6% / 绿地16.0% / 教育10.6% / 道路8.6% / 商业8.2%。

保留优先

保留文保、社区与高校;更新低效楼宇与断裂界面;拆除最少且待现状调查确认。



横向渗透


最稀缺的不是道路容量而是过带渗透率;12道口重构微循环。

交通慢行 × 蓝绿公共空间复合系统

绿脊慢行道 9.7 km 贯通;12 处道口以 600—900 m 间距缝合东西;慢行网络总长约 23.6 km;既有轨道站锚定三站(概念示意)

京张·人字回路

百年京张AI创新带

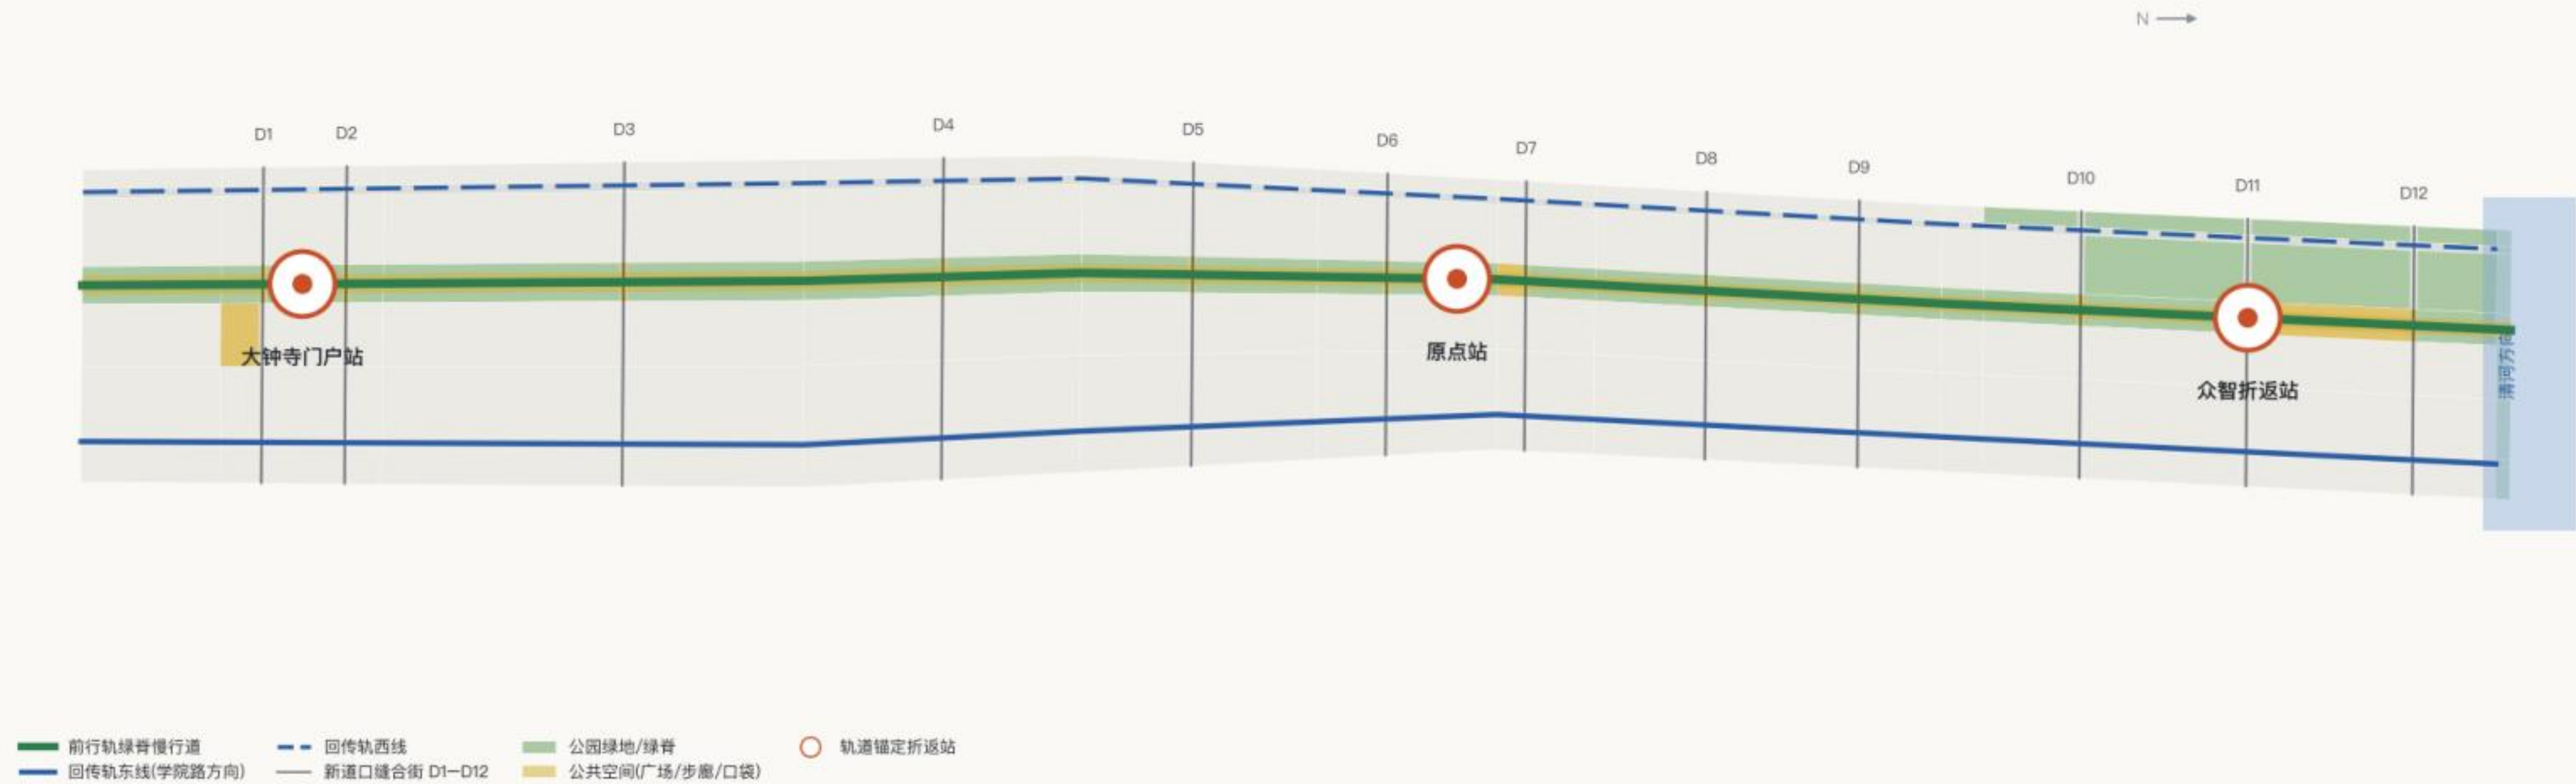

轨道锚定

三站锚定既有轨道站;不做线位工程判断。

AI基础设施

道口边缘算力+区域智算+匿名感知网+能碳折返(算力余热回收)。

AI 场景节点(部分)

S01 道口守望(12处) S04 众智试验场★ S05 清河感知水岸★ S06 大神寺智能市集★ S07 模型医院 S10 能碳折返

★ 产业测试验证场景,所有场景均设隐私边界与人工复核路径

边界状态-临时粗糙边界(provisional),由公告文字四至与面积拟合,不表达官方红线;官方数据发布后整链重算。数据来源:公告 + 仓库场地资料包;图面由包内 GeoJSON/metrics 程序化派生。

一脊一河一带


绿脊贯通9.7km;清河感知水岸;北五环防护绿带;绿地率16.0%。

交通慢行 × 蓝绿公共空间复合系统

绿脊慢行道 9.7 km 贯通;12 处道口以 600—900 m 间距缝合东西;慢行网络总长约 23.6 km;既有轨道站锚定三站(概念示意)

京张·人字回路

百年京张AI创新带

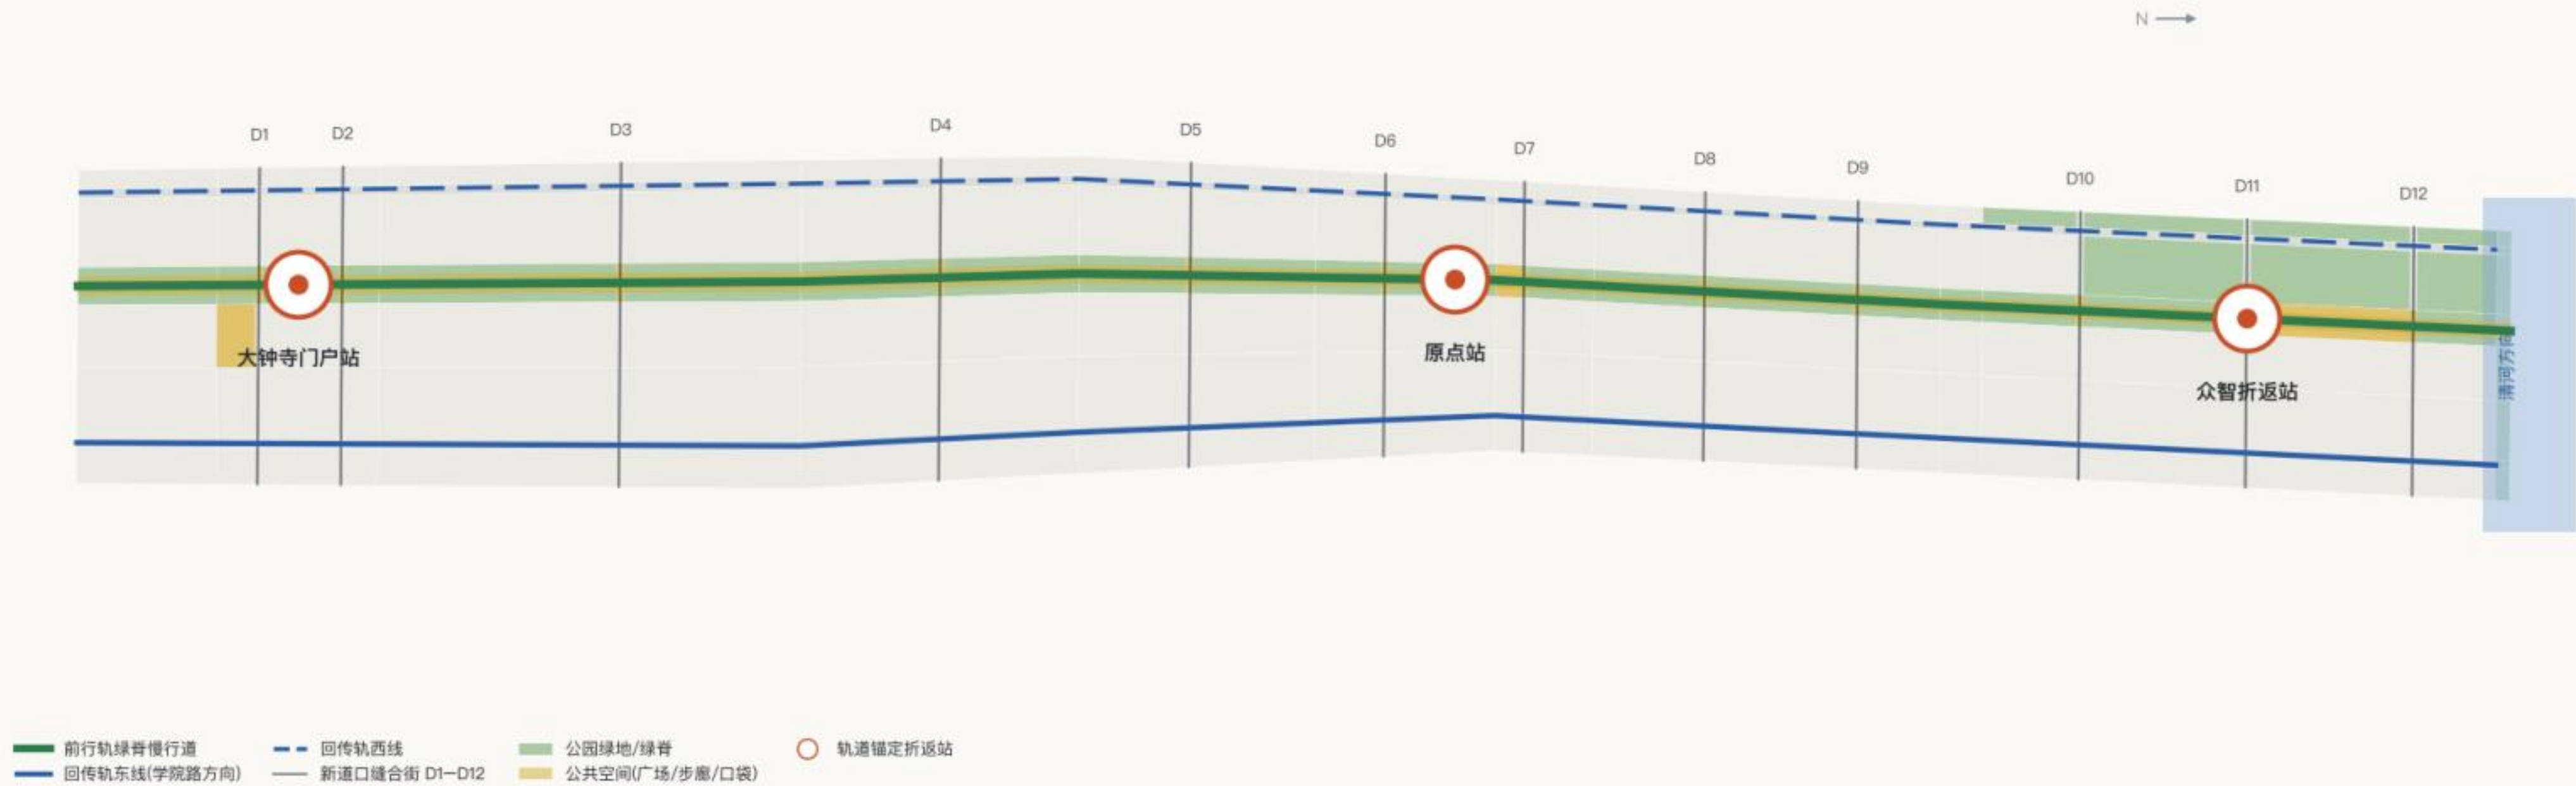

朝圣地标

人字碑 / 折返剧场 / 大钟算林 / 道口博物馆;贡献者里程碑+年度人字奖。

风貌基调

工程理性+校园绿荫,转红暖灰呼应站房记忆;标识双语+机器可读。

AI 场景节点(部分)

S01 道口守望(12处) S04 众智试验场★ S05 清河感知水岸★ S06 大钟寺智能市集★ S07 模型医院 S10 能碳折返


★ 产业测试验证场景,所有场景均设隐私边界与人工复核路径

边界状态-临时粗糙边界(provisional),由公告文字四至与面积拟合,不表达官方红线;官方数据发布后整链重算。数据来源:公告 + 仓库场地资料包;图面由包内 GeoJSON/metrics 程序化派生。



三站详细设计索引

自南向北:大钟寺·门户站(72.0 ha)— 原点站(104.3 ha)— 众智·折返站(192.9 ha);详细设计达到规划综合实施方案深度(概念建议)

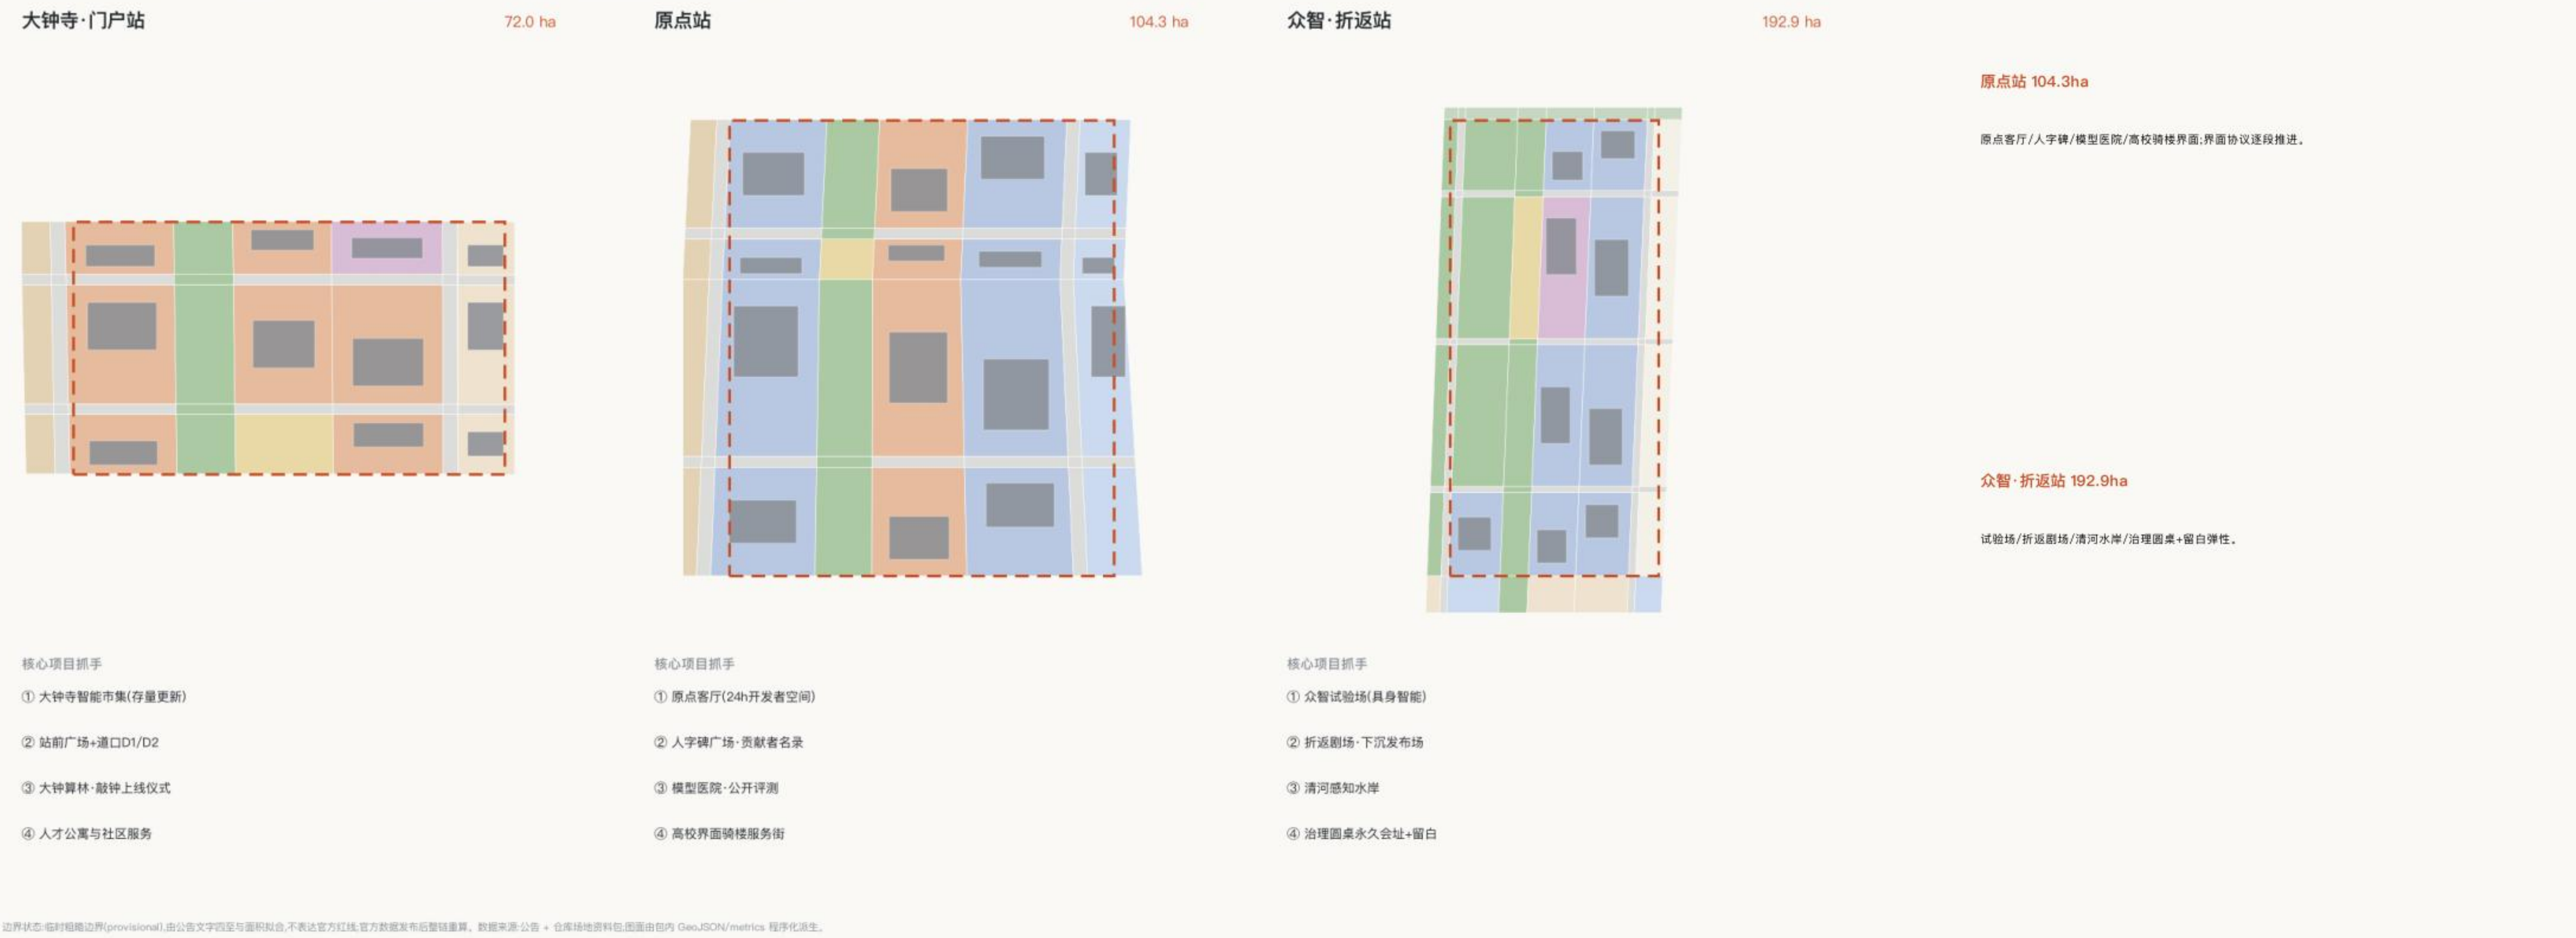

12张场景卡


3张产业测试验证(试验场/水岸/市集);全部设隐私边界与人工复核;绿黄红三态。

人字形回路 · 总体概念

前行轨(遗址公园文化慢行轴)+ 回传轨(科创服务环)在原点站交汇成「人」字;三站十二口组织 11.4 km² 总体设计范围

京张·人字回路

百年京张AI创新带

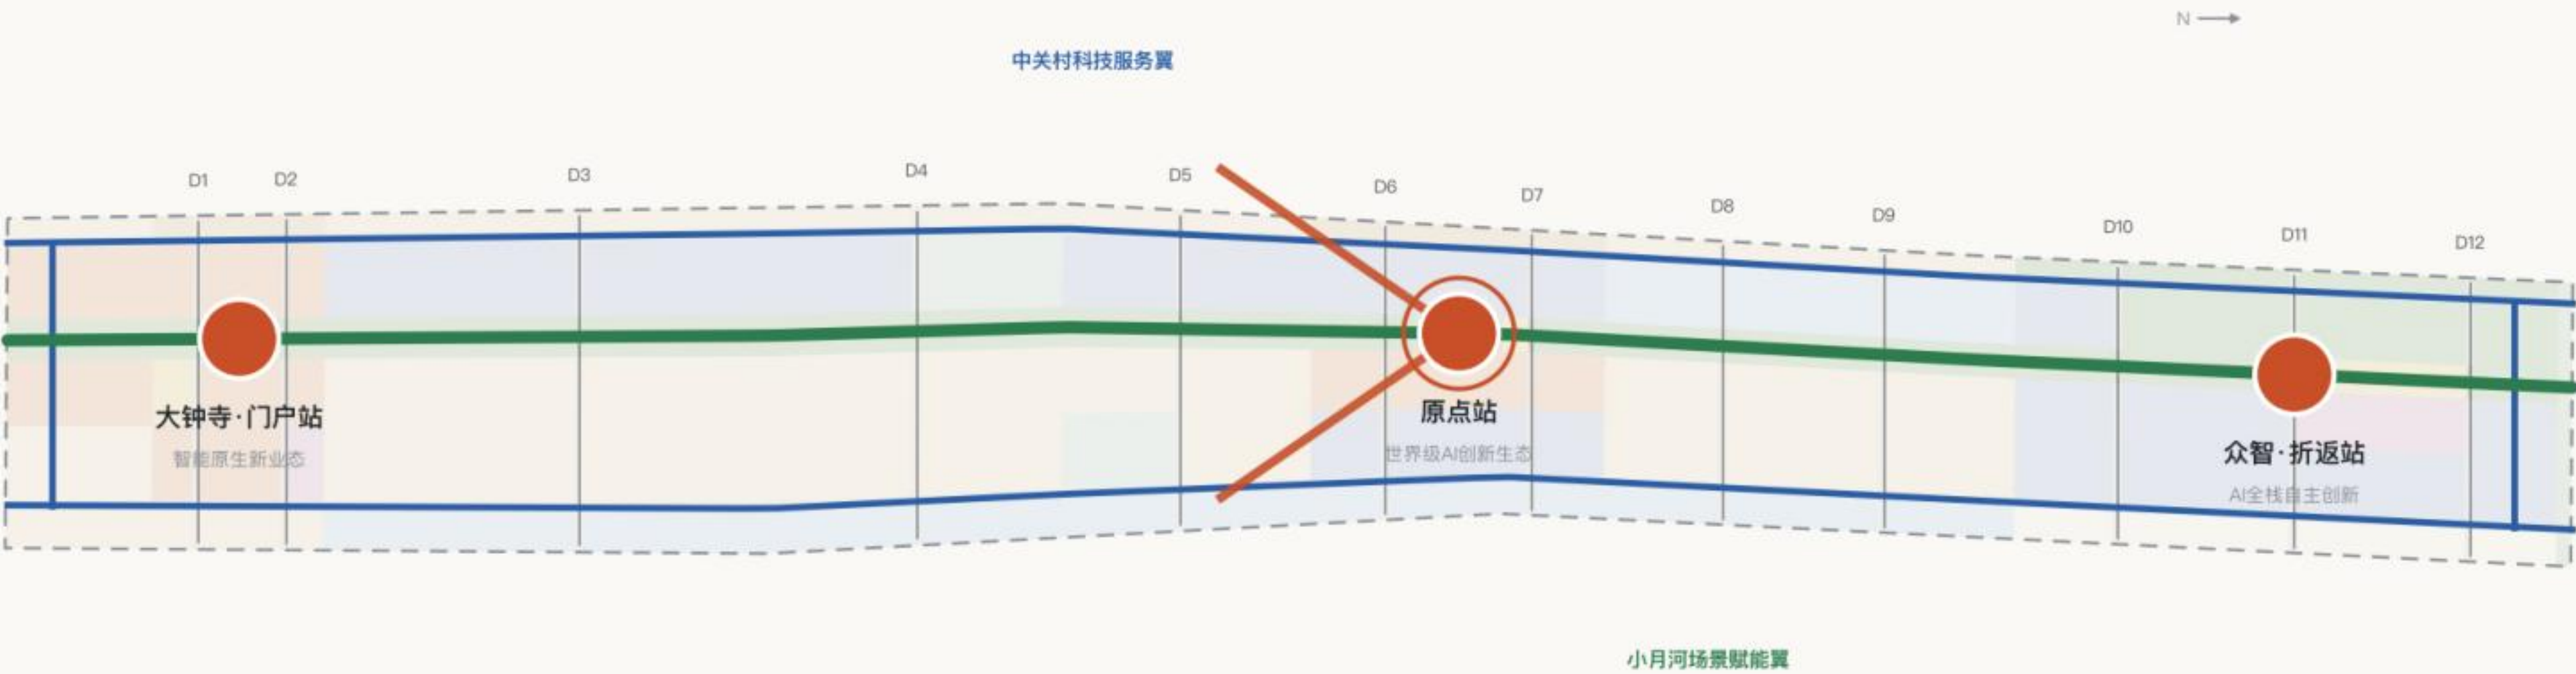

年度活动体系

京张折返周/红队公演/道口市集/铁轨黑客松/治理圆桌。

12项更新项目

三期实施:启动折返(26-28)→缝合成环(28-31)→全环运营(31-35)。

概念转译

1908

青龙桥人字形折返:前行—换向—再前行

2026

反向传播:前向推理—误差折返—更新

城市

场景产生数据(前行),反馈更新空间与政策(折返)

边界状态:临时粗糙边界(provisional),由公告文字四至与面积拟合,不表达官方红线;官方数据发布后整链重算。数据来源:公告 + 仓库场地资料包;图面由包内 GeoJSON/metrics 程序化派生。

- 前行轨:遗址公园绿脊
- 回传轨:科创服务环
- 新道口 D1-D12
- 折返站(三大重点区)
- 临时边界(provisional)

可复算指标

全部指标由GeoJSON在EPSG:4548复算;HTML展示与metrics.json逐位一致。

指标复算与证据链

全部指标由包内 GeoJSON 在 EPSG:4548 下复算;官方控规条件缺口显式登记为待补齐;自检链条:确定性校验 → 空间审查 → 可视化一致性 → 专业证据

京张·人字回路

百年京张AI创新带

任务覆盖

公告17项+agent 6项=23/23;5项强制标准;15项设计深度全部complete。

待补数据

官方红线/控规/道路红线/现状底数/文保线;登记为unknown,不作法定主张。



待正式数据补齐(登记为 unknown,不作法定主张)

官方红线与重点区多边形，控规容积率/高度/密度/绿地率，道路红线，现状建筑与权属底数，文保控制线，市政管线

边界状态:临时粗糙边界(provisional),由公告文字四至与面积拟合,不表达官方红线;官方数据发布后整链重算。数据来源:公告 + 仓库场地资料包;图面由包内 GeoJSON/metrics 程序化派生。