


新纪元，以人为名

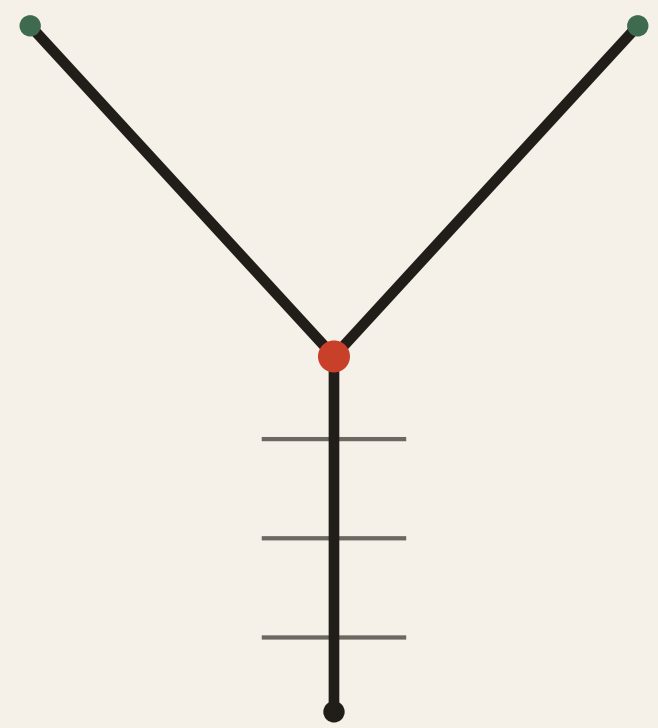

1909 年詹天佑画下“人”字——这座城市的 initial commit；
智能爆发的纪元，仍以“人”为名。一撇中国，一捺世界，互相支撑。

器

人字轨 = git branch
百年工程图例与代码同构

道

The Y stands for Human
AI 治理话语权的空间宣言

世

一撇一捺互相支撑
为全球开发者留一面刻名墙

历

Y-Era 纪年 Y0=1909
公元×Y 历双纪年体系

三芯详细设计索引

众智园 · 原点社区 · 大钟寺 —— 定位、示范项目与公共空间组织（概念建议）

众智园AI自主创新加速区

192.1 ha · 花园型 · 全栈自主创新街区

北京AI原点社区


104.3 ha · 近校型 · 创新生态街区

大钟寺AI产业集聚区

72.0 ha · 城市型 · 智能原生产态街区

总体结构 · 一轨两撇三芯

人字纪 · 京张AI创新带 总体设计范围空间结构（概念建议）

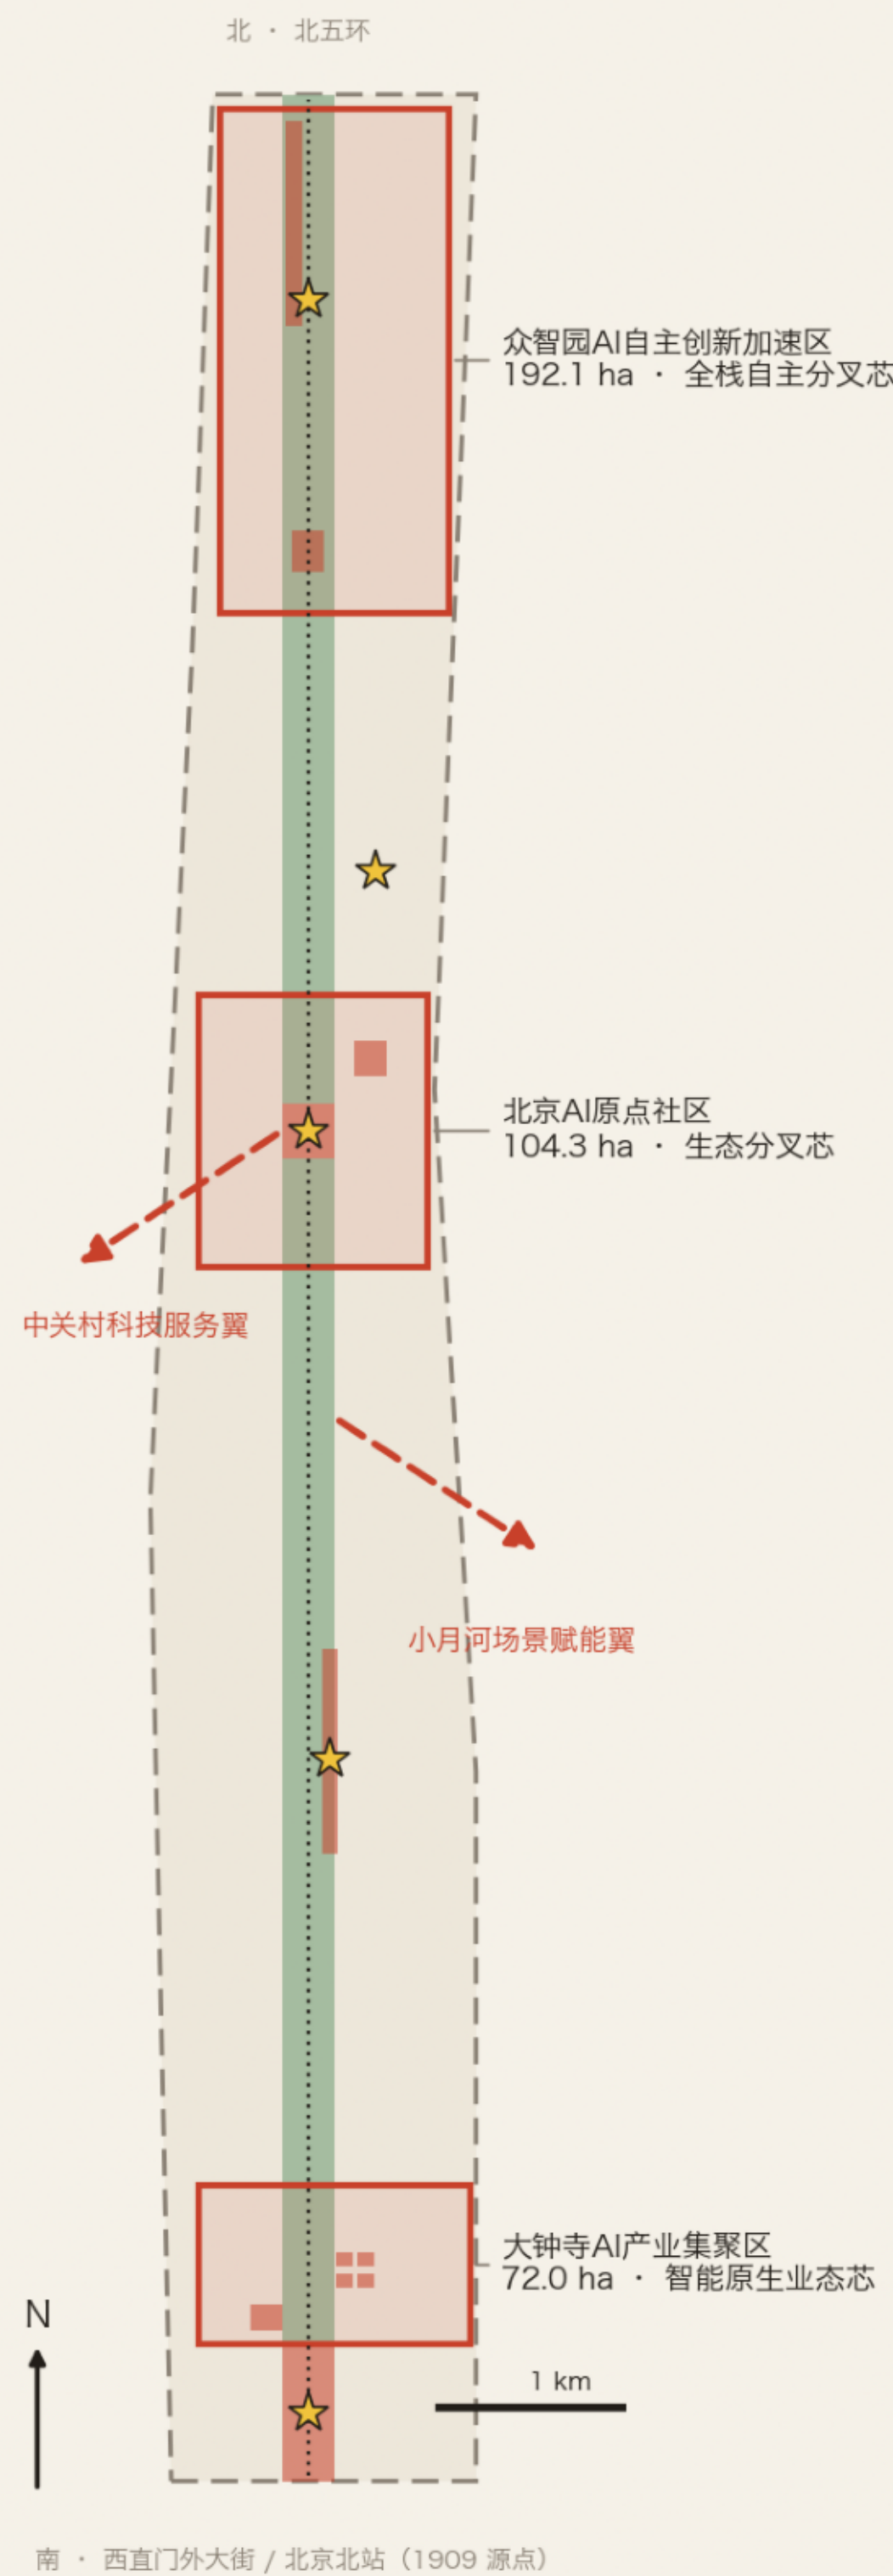

一轨两撇三芯 · 空间结构

一轨 京张遗址公园活力带主脊，南起源点广场（1909），北抵清河绿谷，全栈贯通绿道与开源展示系统。

两撇 中关村科技服务翼（西）与小月河场景赋能翼（东），一撇一捺互相支撑，构成“人”字协同回路。

三芯 众智园（全栈自主）、原点社区（创新生态）、大钟寺（智能原生产态）三个分叉芯，对应三大重点详细设计区。

AI 朝圣地标（★）

- ① 人字碑 · 全球贡献者荣誉墙
- ② 青龙桥对话馆（清华园站旁）
- ③ 分叉广场 Fork Plaza
- ④ Commit纪念带 · 开源展示廊
- ⑤ 源点广场 · 0km标

三级范围嵌套




- 总体设计范围（provisional）
- 重点详细设计区（provisional）
- 遗址公园活力带主脊
- AI 公共空间 / 广场
- 京张旧线走廊示意
- ★ AI 朝圣地标

边界为 provisional 粗略替代范围（依据公告文字四至与约面积推定），不代表官方红线；官方边界公布后所有面积与图面需重算。

用地布局 · 拓扑完整分区

25 个用地单元完整剖分总体设计范围（无缝无叠 · 概念建议）

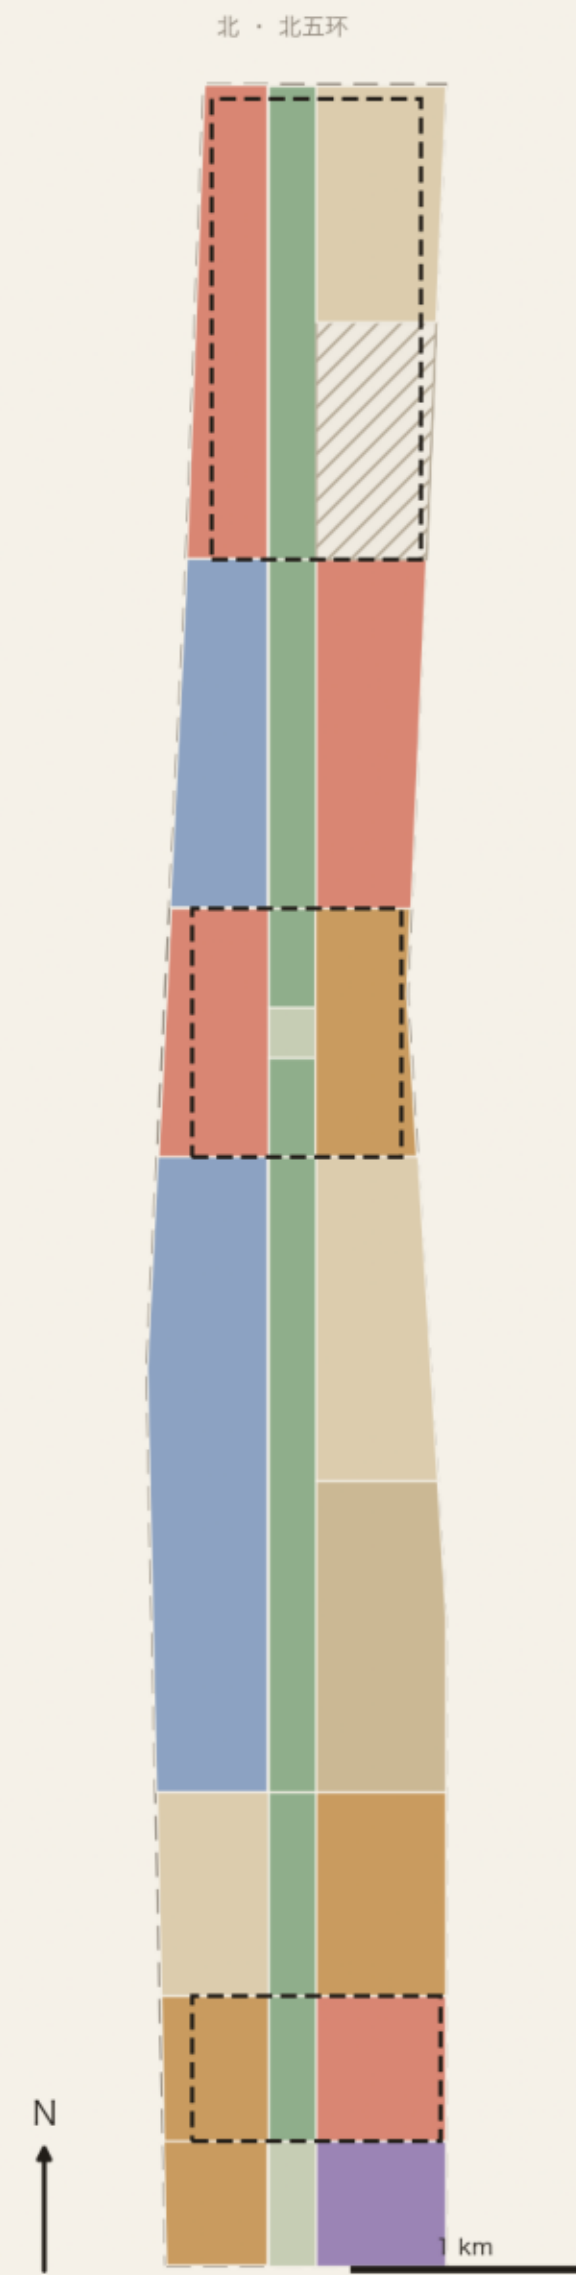

边界为 provisional 粗略替代范围（依据公告文字四至与约面积推定），不代表官方红线；官方边界公布后所有面积与图面需重算。用地分类采用国土空间用地用海分类。

用地构成（EPSG:4548 复算）

207.5 ha · 18.2%	公园绿地+广场
228.3 ha · 20.0%	科研用地
156.2 ha · 13.7%	商业服务业
254.6 ha · 22.3%	居住+社区服务
208.2 ha · 18.2%	教育用地
32.3 ha · 2.8%	文化用地
54.2 ha · 4.8%	战略留白

布局逻辑

· 主脊连续：1401 公园绿地贯穿七段，绿地率 16.7%，对应遗址公园活力带南北贯通要求。

· 科研两端强：0802 科研用地集中于众智园（全栈自主）与原点社区（成果转化）两芯。

· 居住内嵌：0701/0702 居住与社区服务嵌入走廊中段与东翼，就近平衡三芯就业。

· 消费在钟：05 商业服务业集中于大钟寺智能原生消费区与五道口创新消费节点。


· 文化锚南端：0803 文化用地落位南端原点门户，承载人字纪展示馆与对话分馆。

· 留白可进化：众智园东南 16 留白用地，为 AI 产业不可预知的空间需求预留弹性。

0802 科研	0803 文化
05 商业服务业	1401 公园绿地
0701 城镇住宅	1403 广场
0702 社区服务	16 留白
0804 教育	重点区 (provisional)

交通慢行 × 蓝绿公共空间

南北贯通 · 东西缝合 · 站城一体（概念建议）

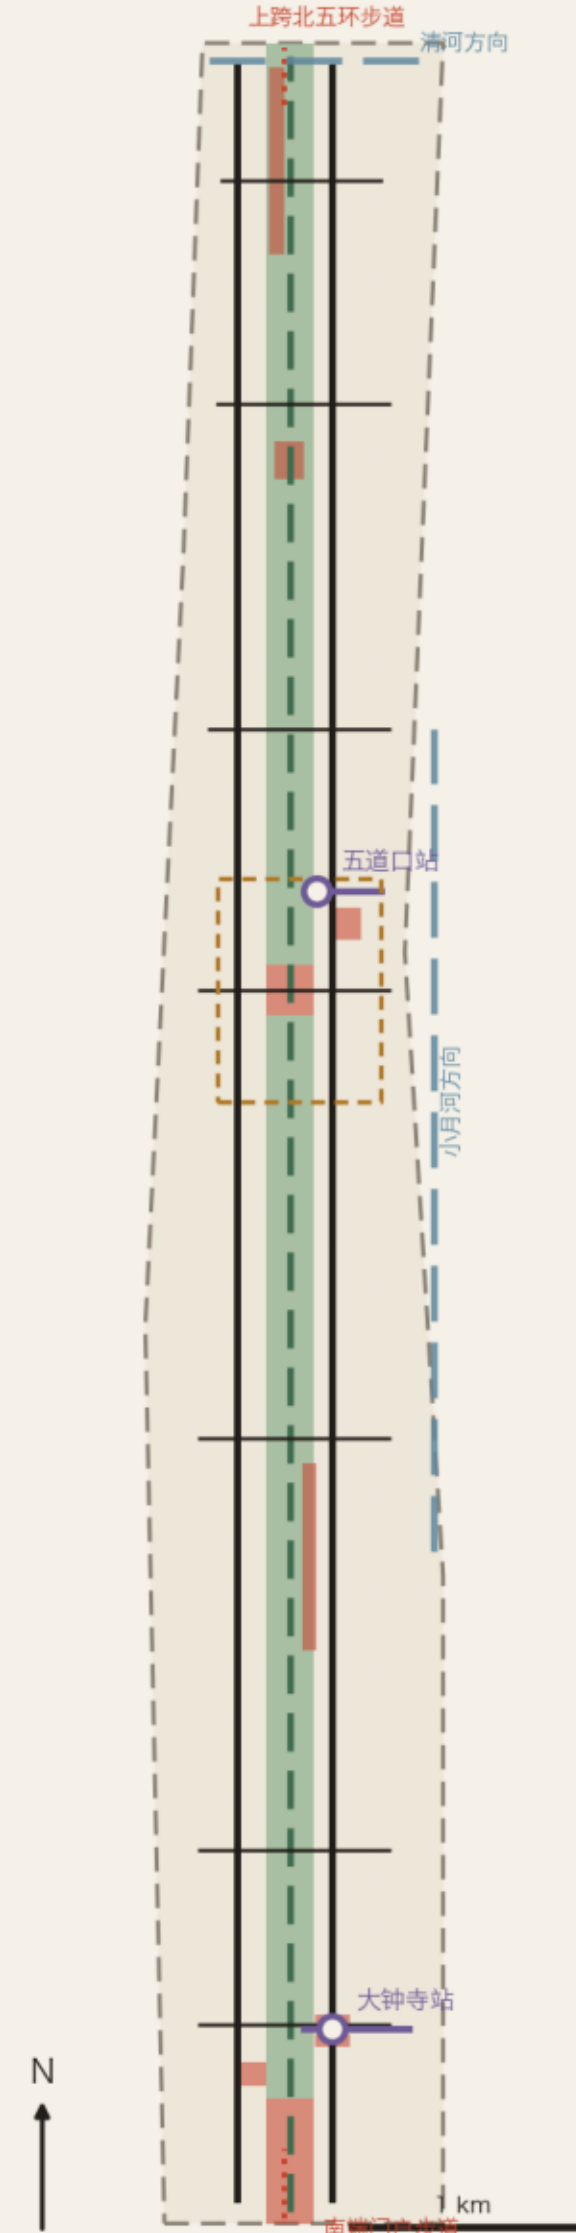

边界为 provisional 粗略替代范围（依据公告文字四至与约面积推定），不代表官方红线；官方边界公布后所有面积与图面需重算。

交通与蓝绿系统策略

南北贯通 绿道主脊全线 9.7km 贯通，两条南北次干路分担机动车流，把公园主脊让给慢行。

东西缝合 7 条东西支路 + 上环五环/西直门外步道，缝合铁路走廊两侧断点，回应慢行断点课题。

站城一体 五道口、大钟寺两站建设绿道 + 站前广场/四象限连通空间、轨道站点一体化组织。

骑行成环 原点社区骑行环串联校区—园区—广场，支撑近校创新街区。

蓝绿开放 北端衔接清河、东翼呼应小月河，绿地率 16.7%、公共空间率 3.1%（复算值）。

- 南北次干路（概念）
- 东西支路（概念）
- 遗址公园绿道主脊
- 骑行环
- 步行缝合绿道
- 轨道交通缝合
- 蓝绿联系方向（京冀）
- 公园绿地
- 广场 / 公共空间


待确认数据

- 道路红线 / 断面 / 轨道站点边界未公开，全部线位为概念建议
- 清河、小月河蓝线未获取，仅表达联系方向
- 停车与非机动车供给底数缺失，列入 assumptions

核心指标复算与证据链

所有指标由 GeoJSON 在 EPSG:4548 下复算 · 图表仅为可读层，JSON 为权威数据

总体设计范围	绿地率	公共空间率	示范项目基底
11.41 km² provisional 复算	16.7% 公园主脊贯通	3.1% 8 处广场体系	11.5 ha 39 个更新示范项目
示范项目规模	道路网概念	重点区	场景卡
120 万m² 原数方案假设	39.1 km 15 条概念线位	3 处 · 368.4 ha provisional 边界	12 张 · 3 测试 6 类用户画像

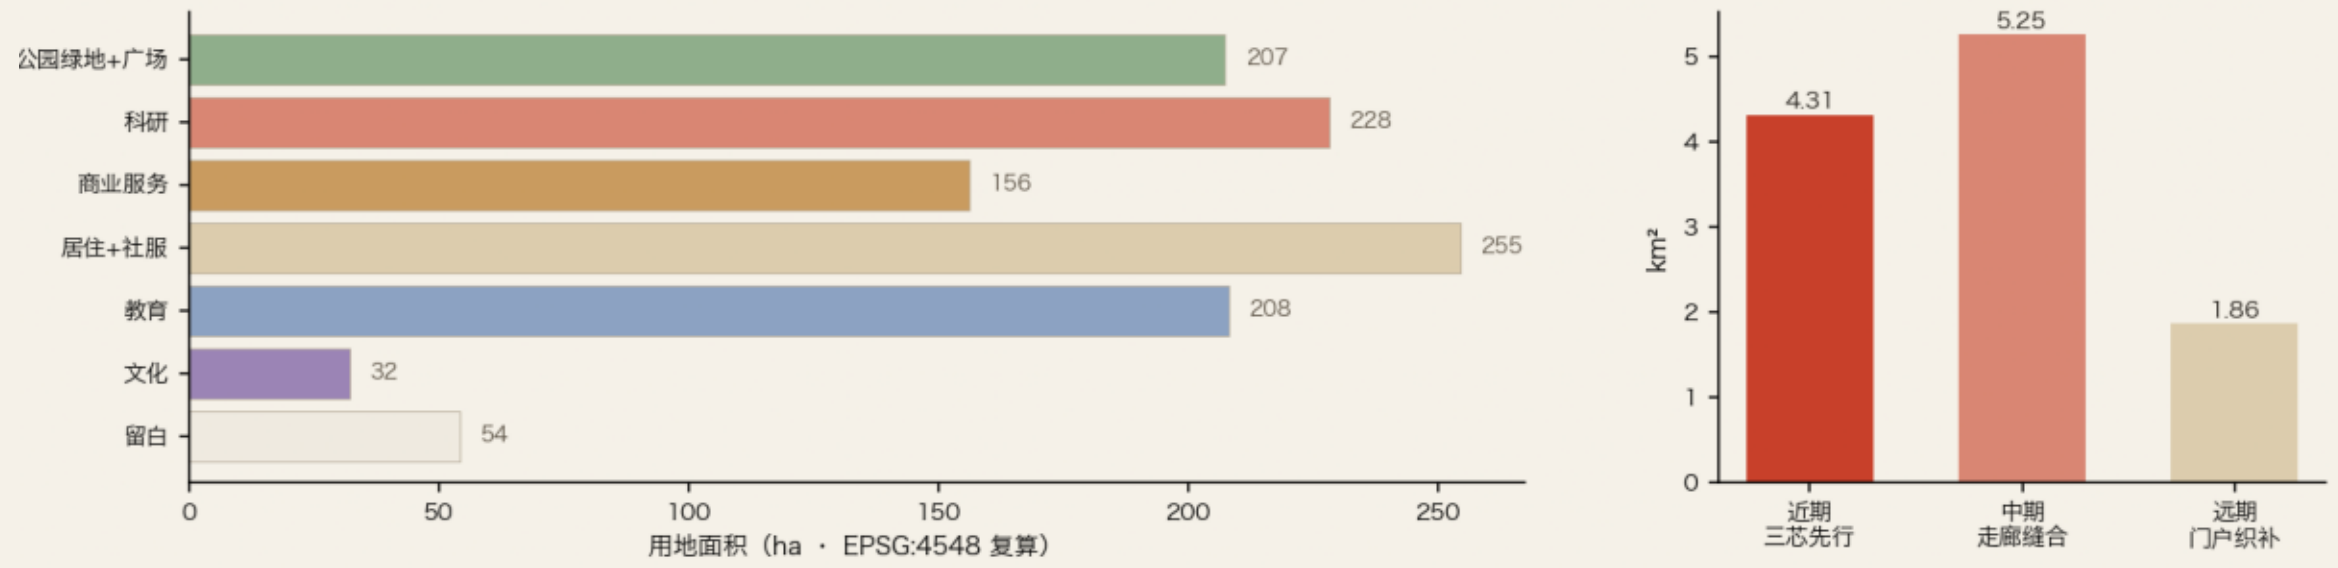

证据链结构



自检状态

✓ 确定性校验

结构/引用/增量完整

✓ 空间审查

拓补无缝无叠 PASS

✓ 视觉打包

高线静态 PASS

✓ 专业证据

标准/深度/指标引用 PASS

已声明缺口（不得虚构）

法定容积率 / 高度管控 / 道路红线 / 现状建筑底数 / 文保与蓝线范围 —— 均为 unknown，待官方数据公布后复算；组织方数据缺口不影响内容评分。

拓扑完整用地剖分

25 个用地单元无缝无叠覆盖总体设计范围，绿地率 16.7%、公共空间率 3.1%（EPSG:4548 复算）；科研两端强、居住内嵌、消费在钟、文化锚南端、留白可进化。

三芯先行 · 三期实施

近期三芯先行 4.31 km²（与 9 月征集落地节赛衔接）→ 中期走廊缝合 5.25 km² → 远期门户织补 1.86 km²。

city-as-repo 城市操作系统

Open Issues（城市命题公开）→ Global PRs（全球智能体与团队提案）→ Review（人类最终判断）→ Merge Day · 鸣钟合并（每年 9 月 · 大钟寺鸣钟 · 碑刻揭幕 · 深化开工 · 全球直播）。

诚实的数据边界

法定容积率 / 高度管控 / 道路红线 / 现状建筑底数均为 unknown——不虚构、不伪装，官方数据公布后整包按既定脚本链路重算。组织方数据缺口不影响内容评分。