
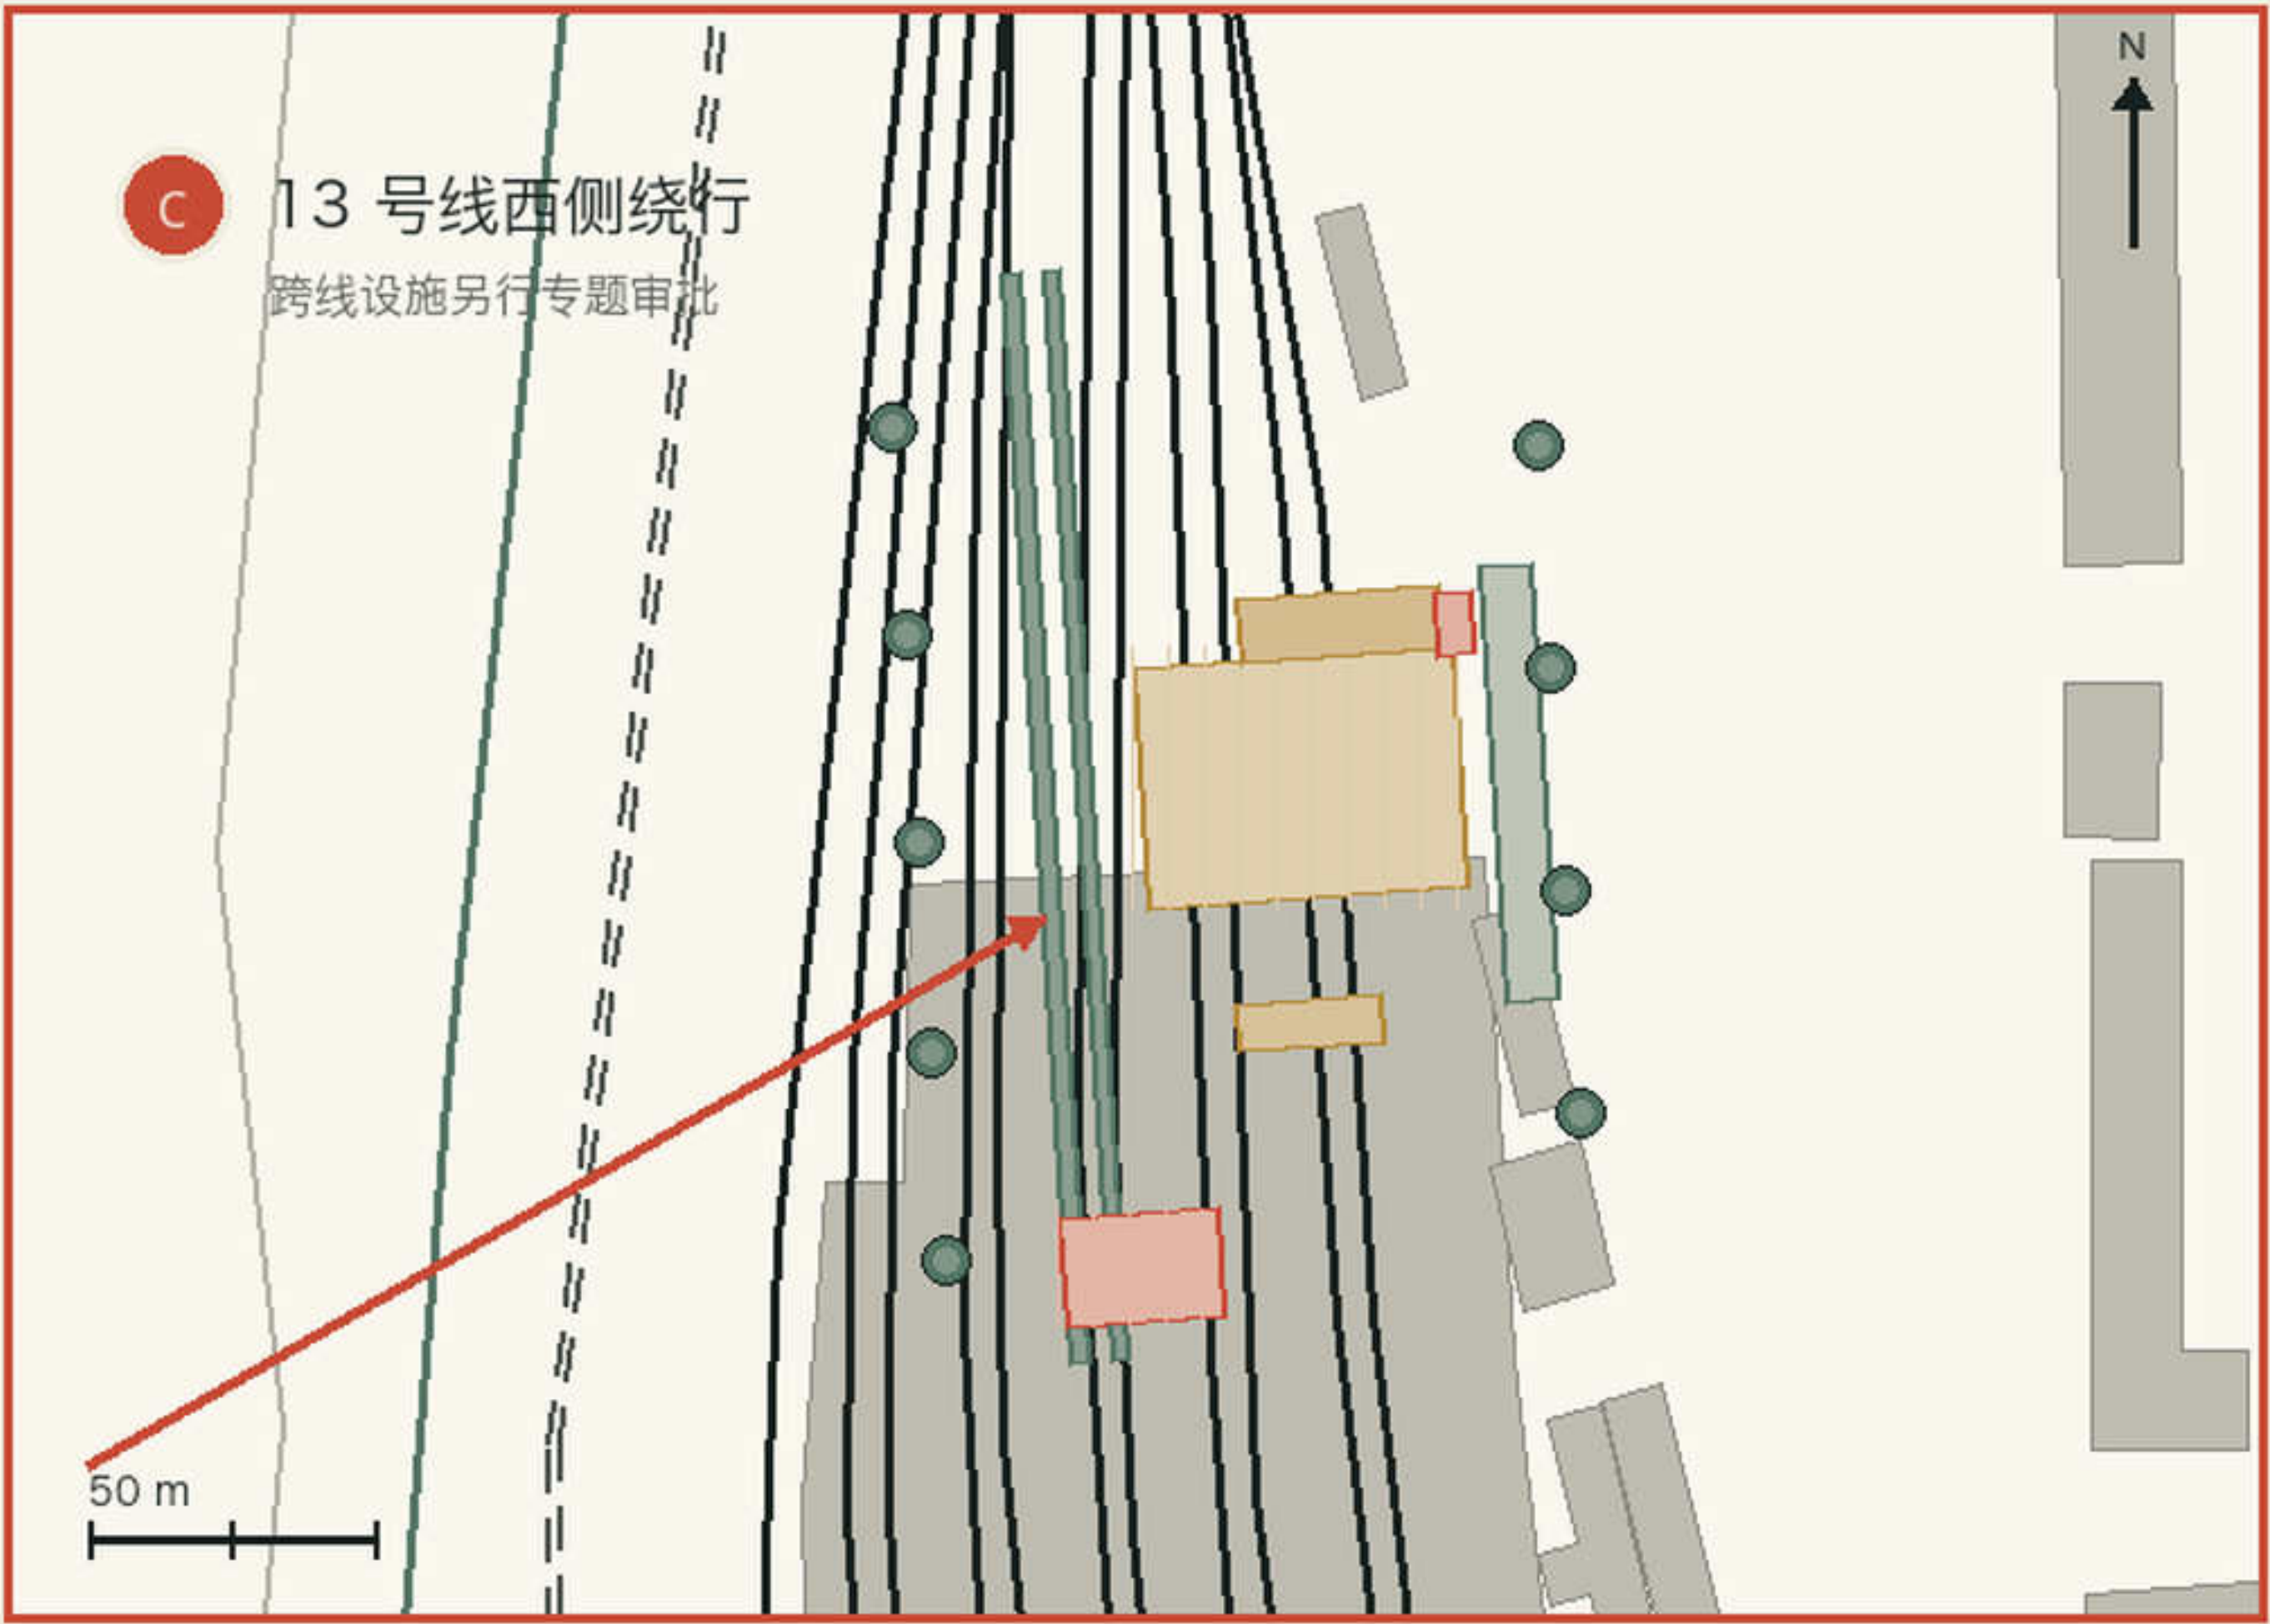
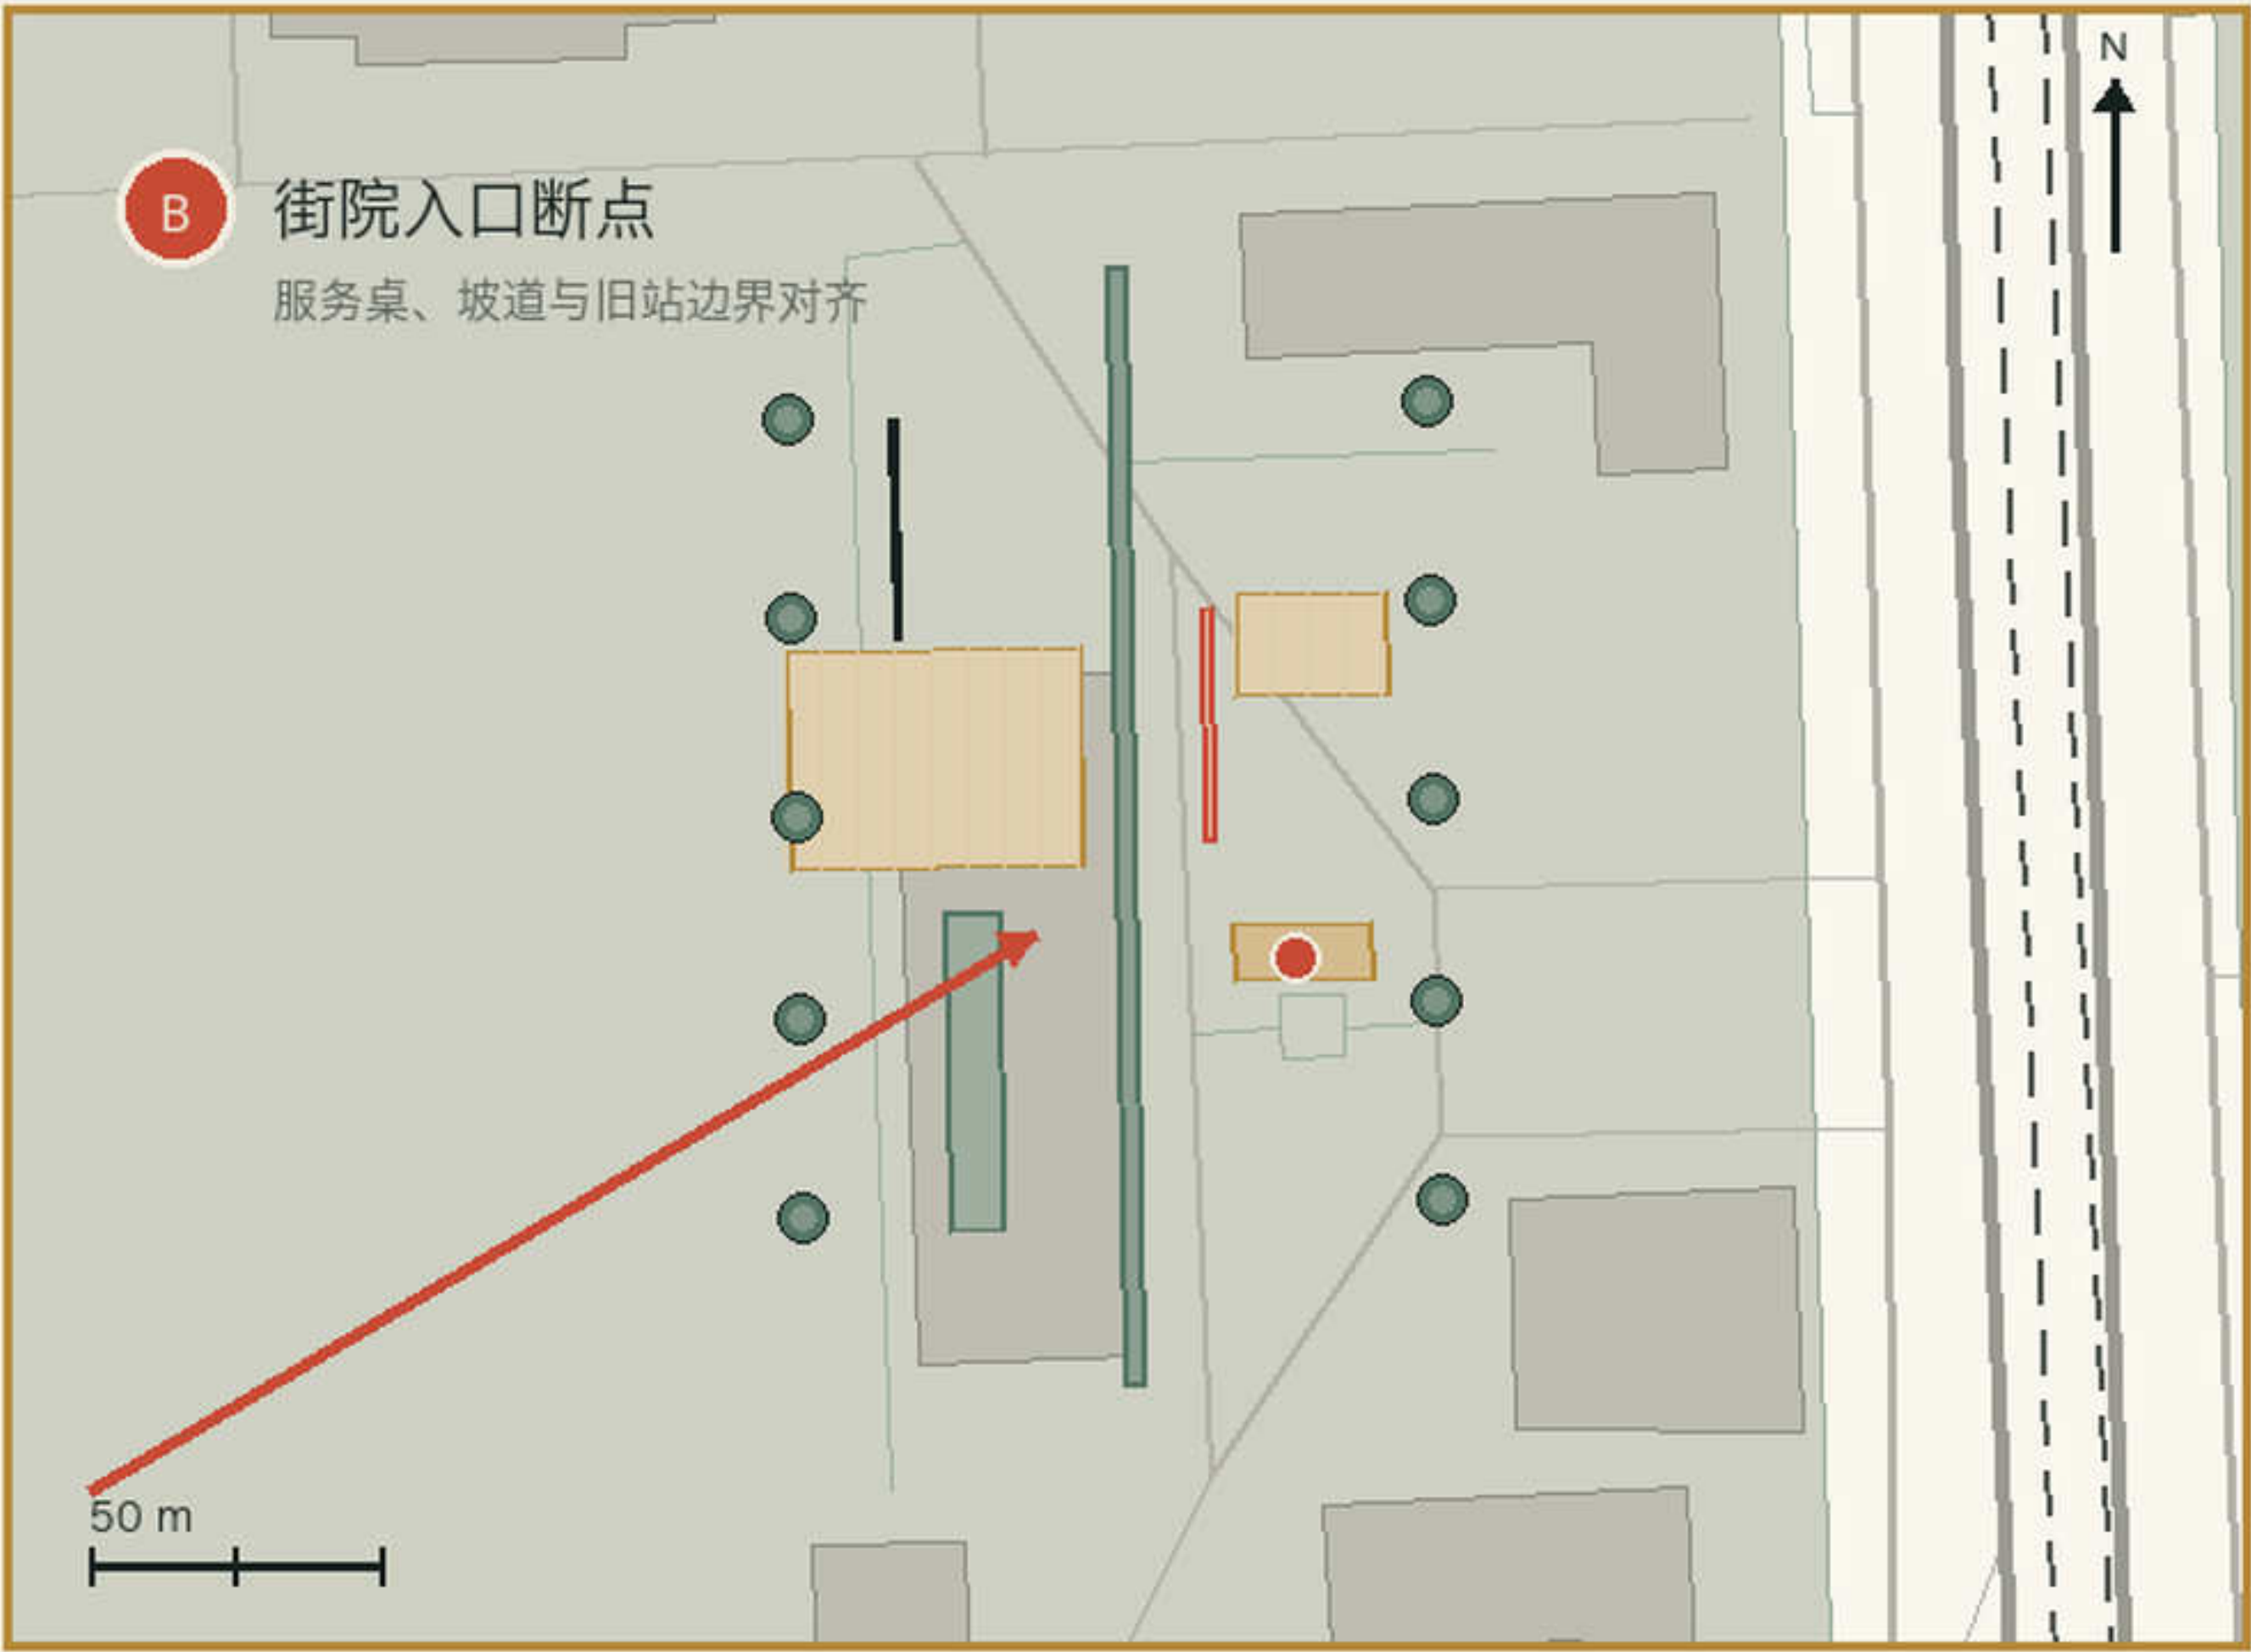


01 先把九公里读清楚

真实底图、公开工程状态与三处断点同图核对

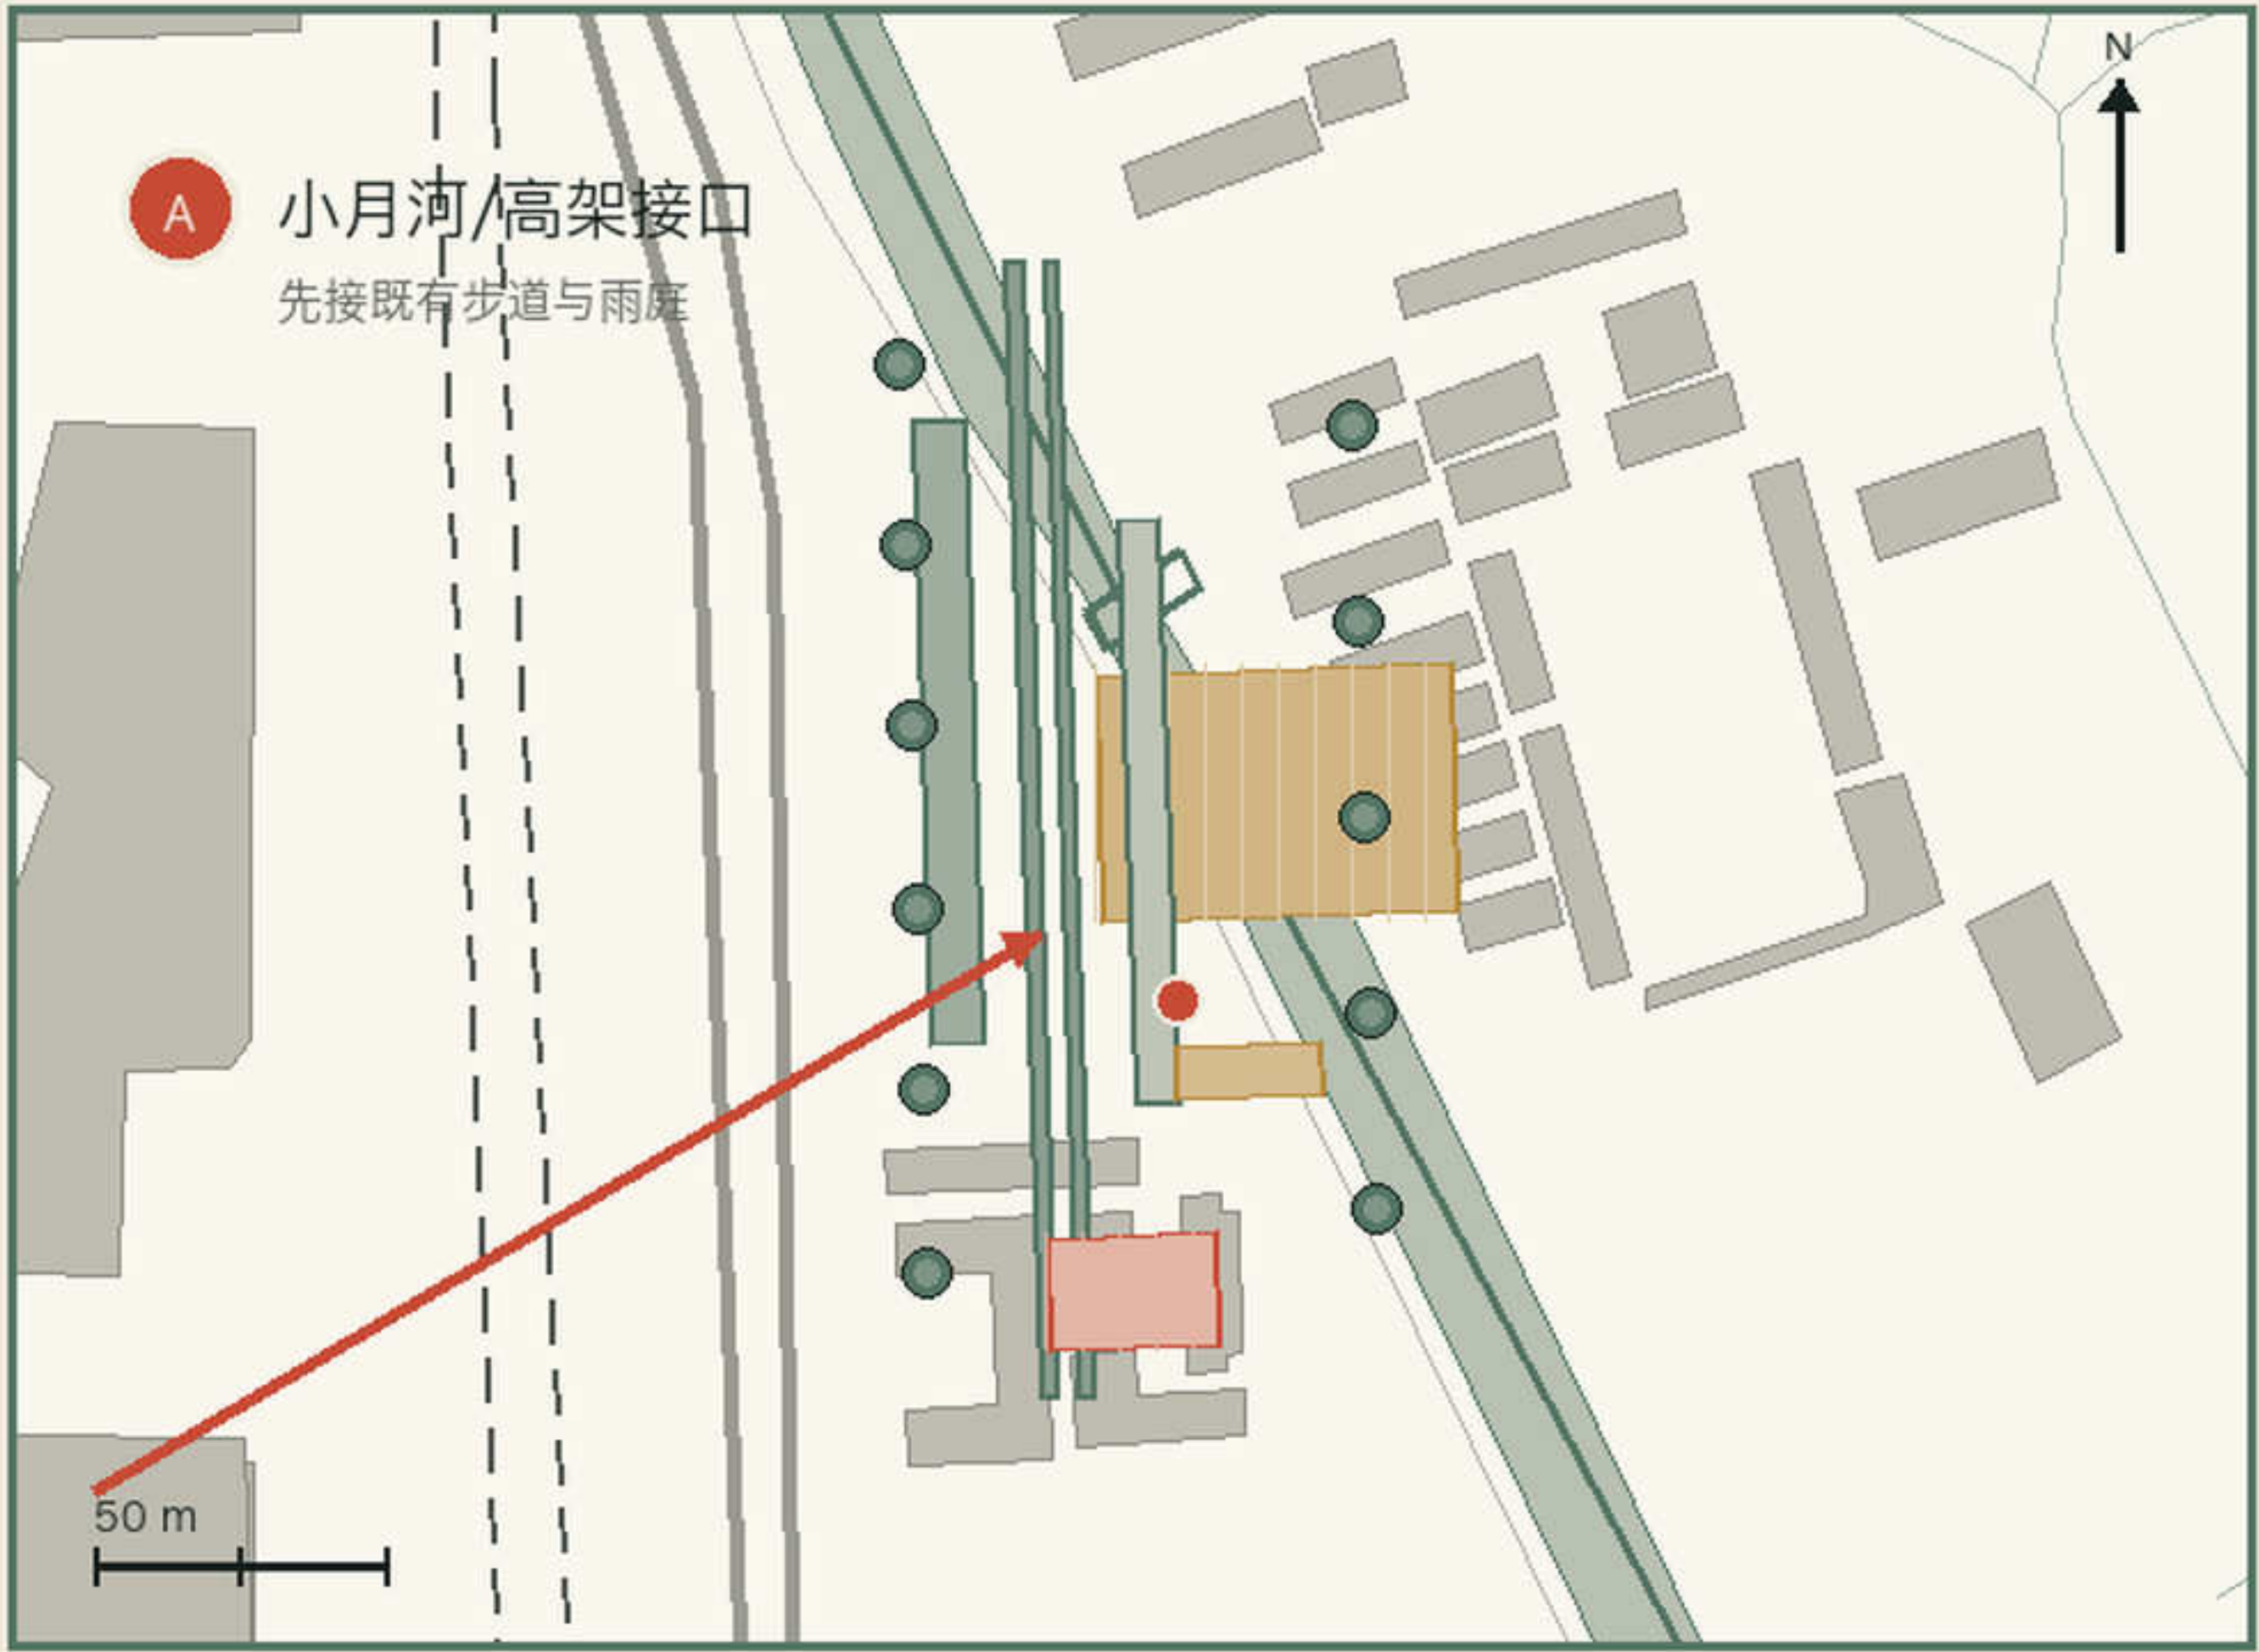

OSM 仅作现状底图 | 概念边界须以测绘、权属与审批复核

STATUS CUT-OFF 2026-08 | PROVISIONAL / CONTEXT ONLY

已建
一期公开信息采用 2.4 km、16.8 ha 口径。

在建
二期与清华东路南侧项目按公开进度标识。

本案建议
只补入口、过街、河岸与三处院落接口。







需审批
跨轨、文保、水务与市政接口不预涂成已建。

03

三座院子详图

约 1:500 景观总平与 AA / CC / EE 对应剖面

步行 慢骑 雨庭 入口/构件 现状界面

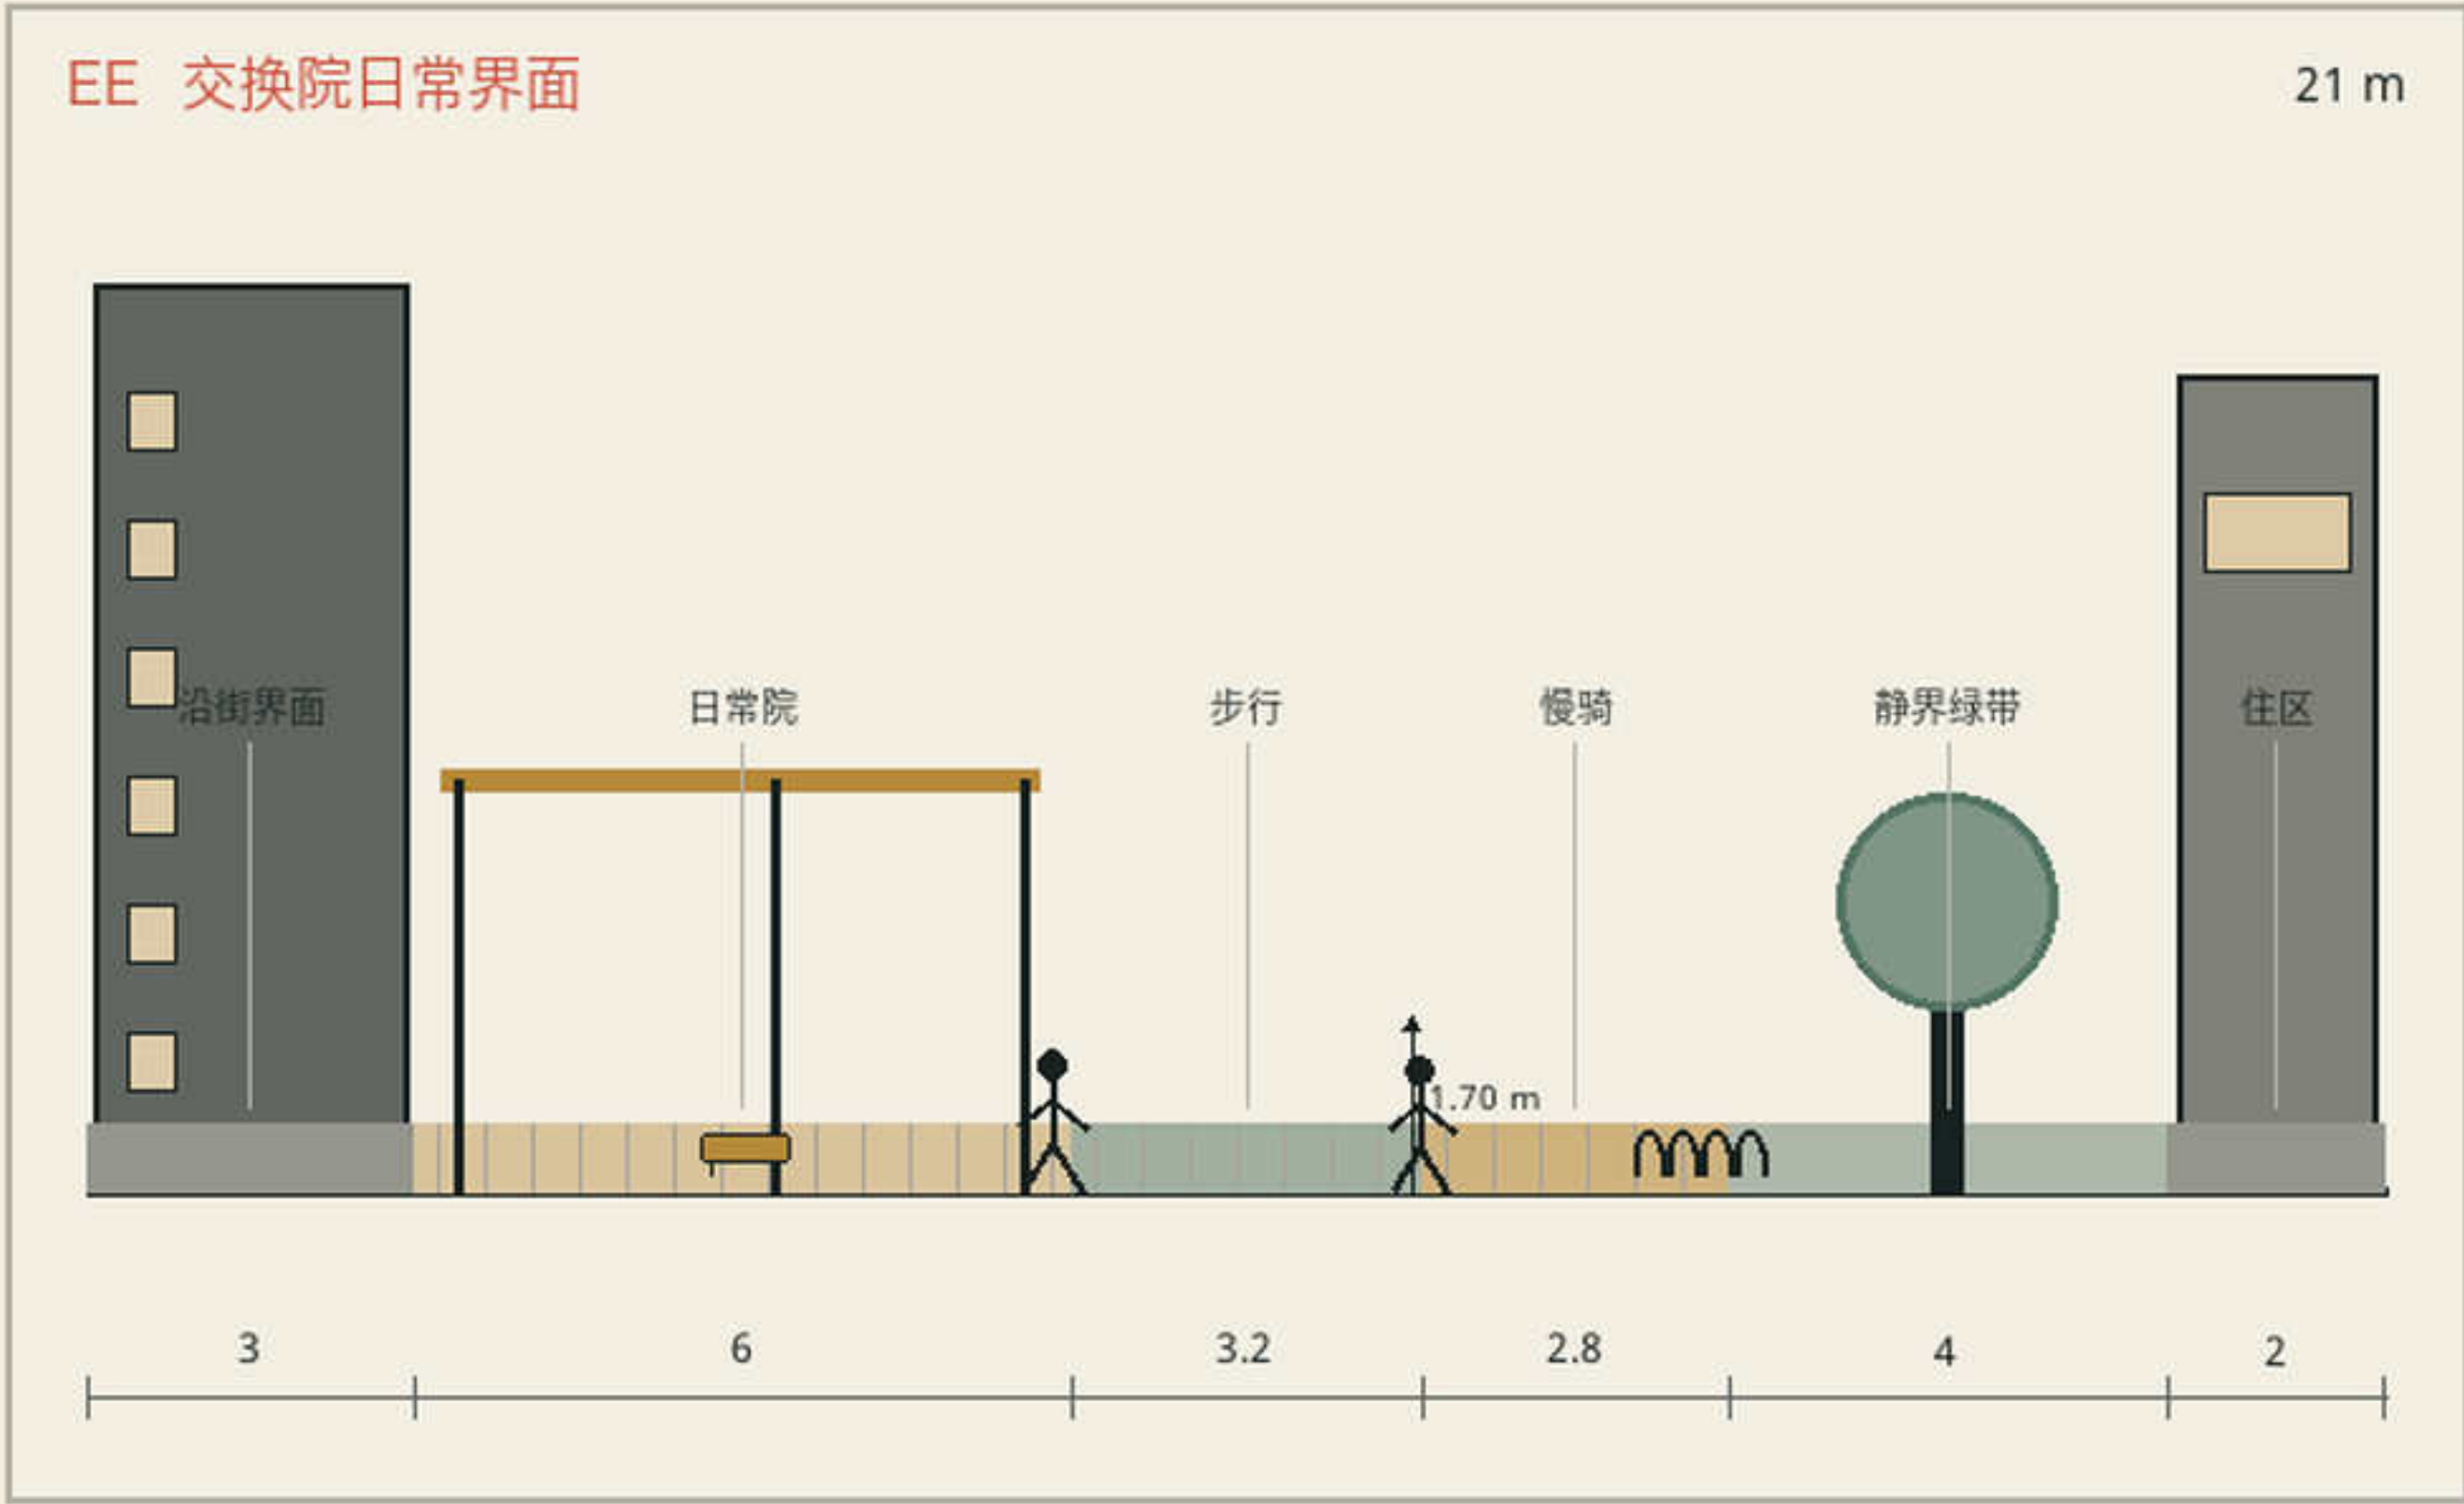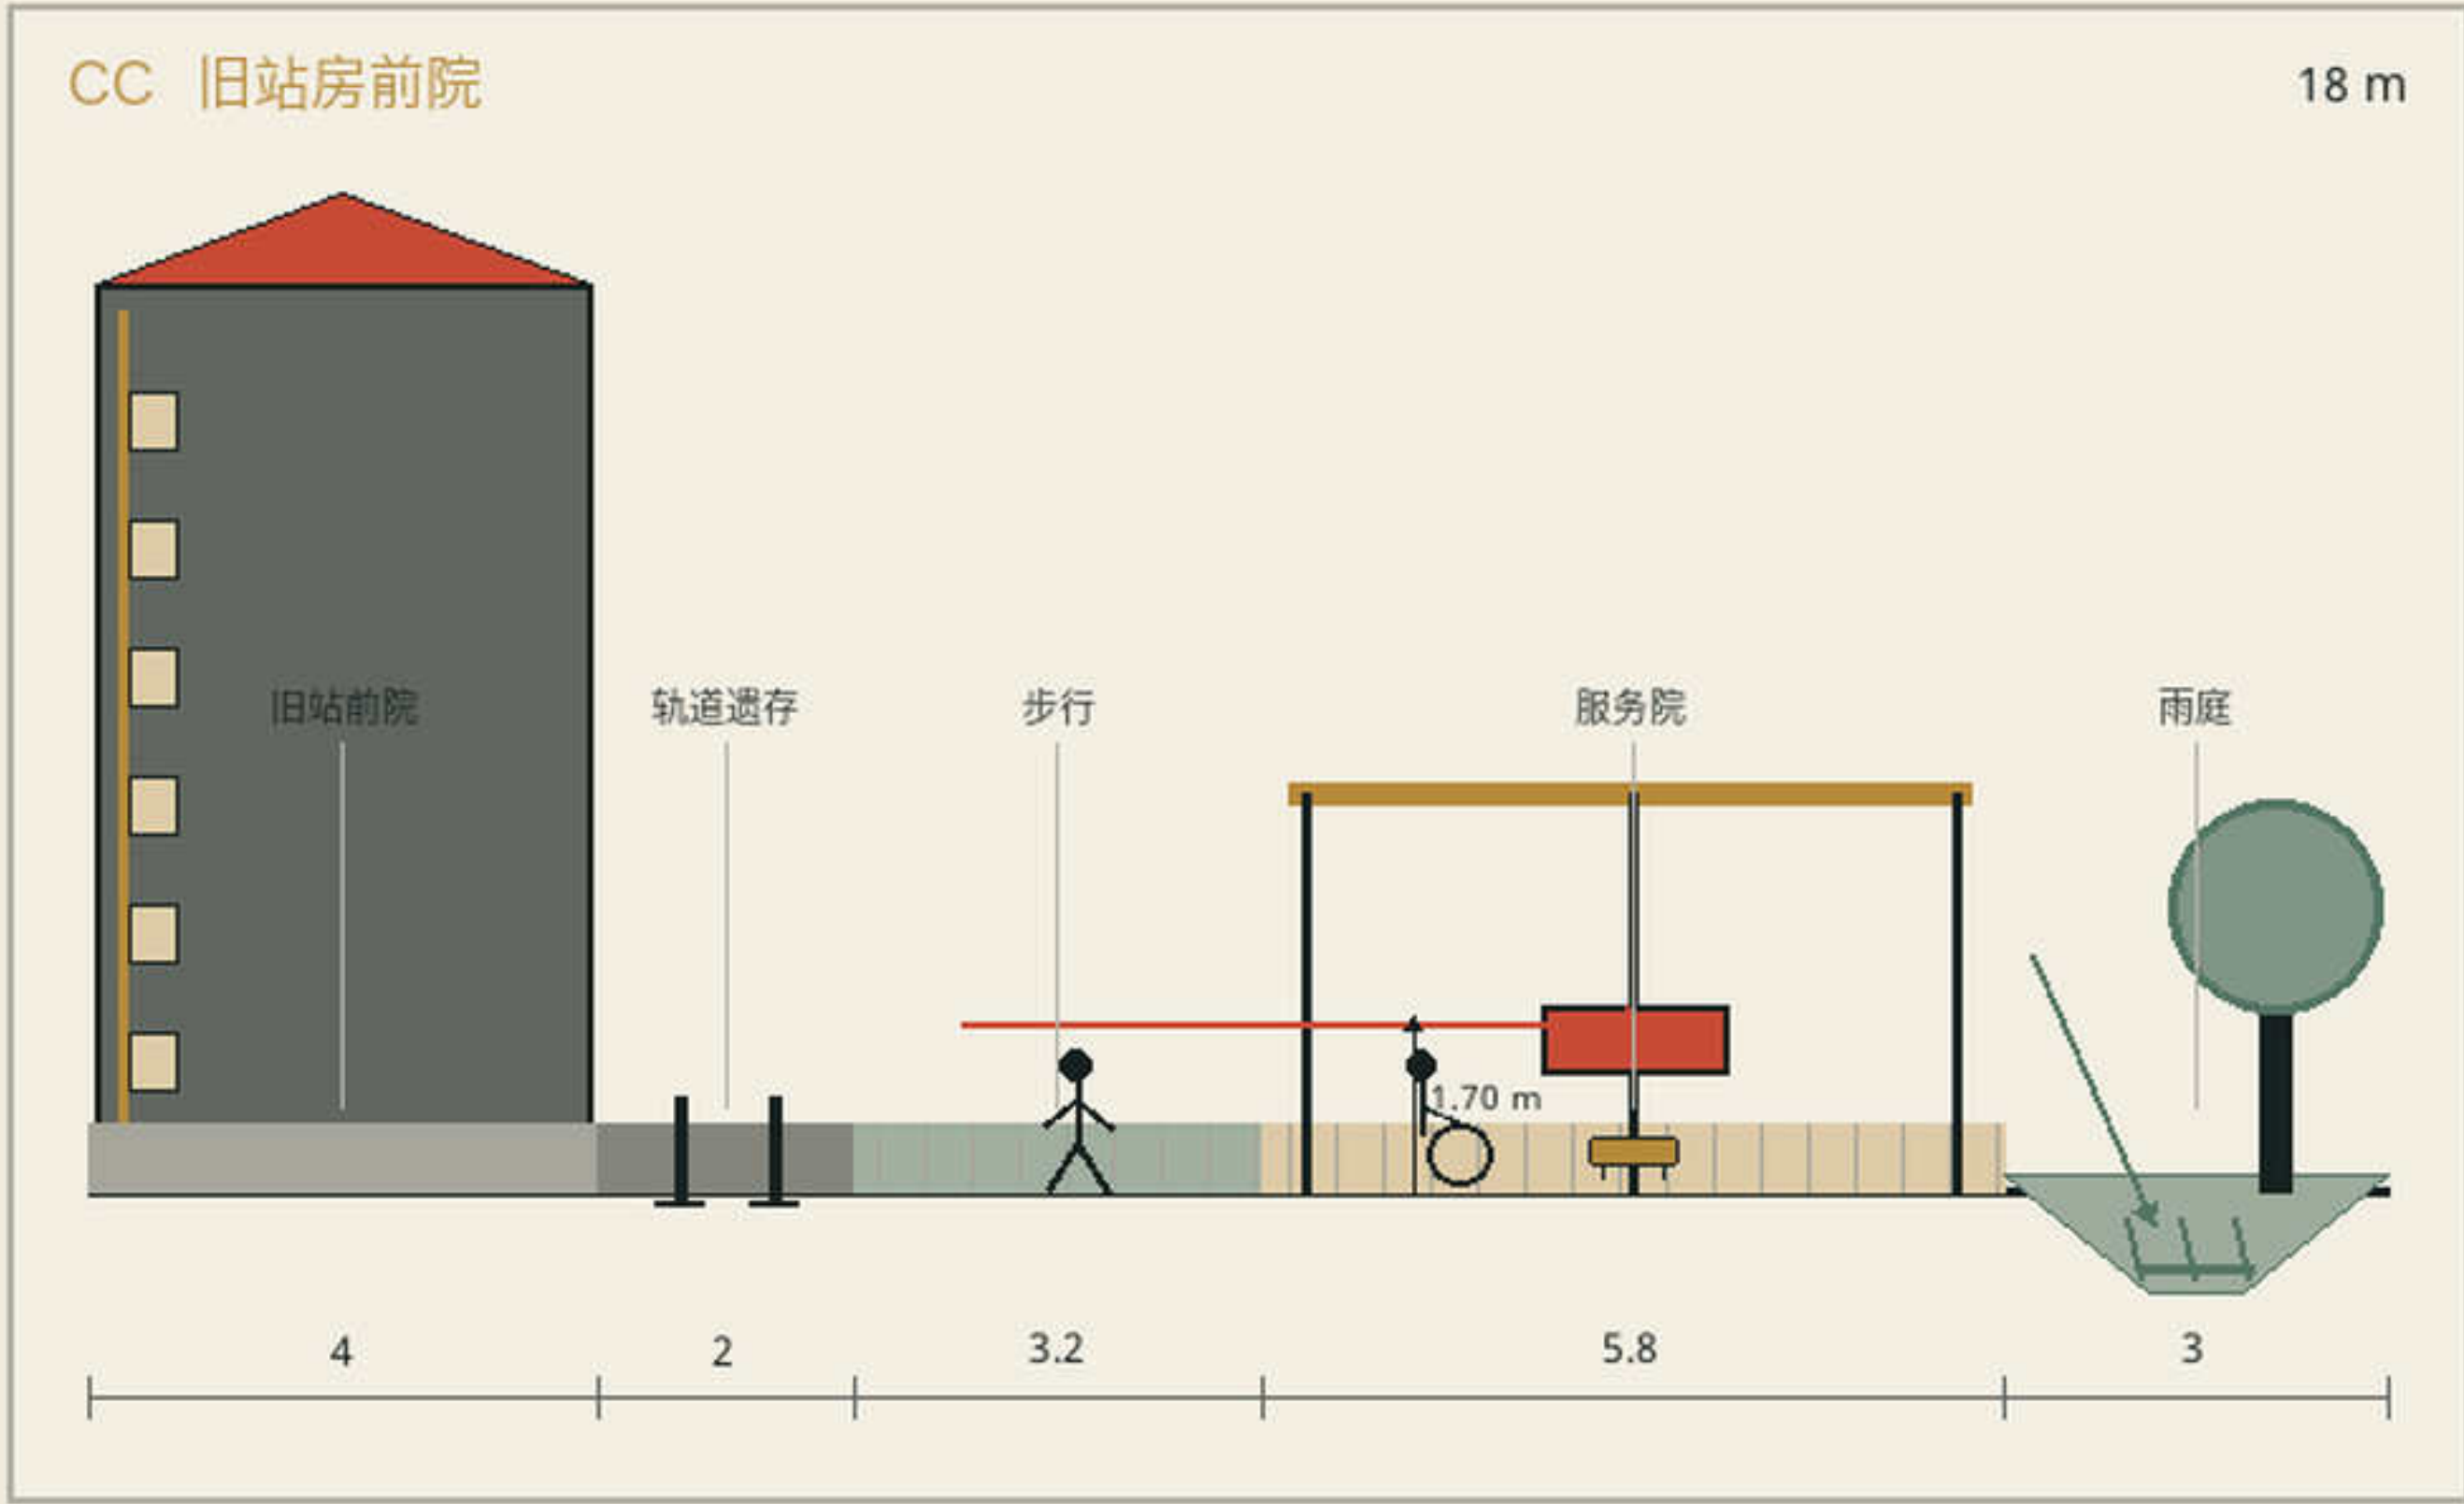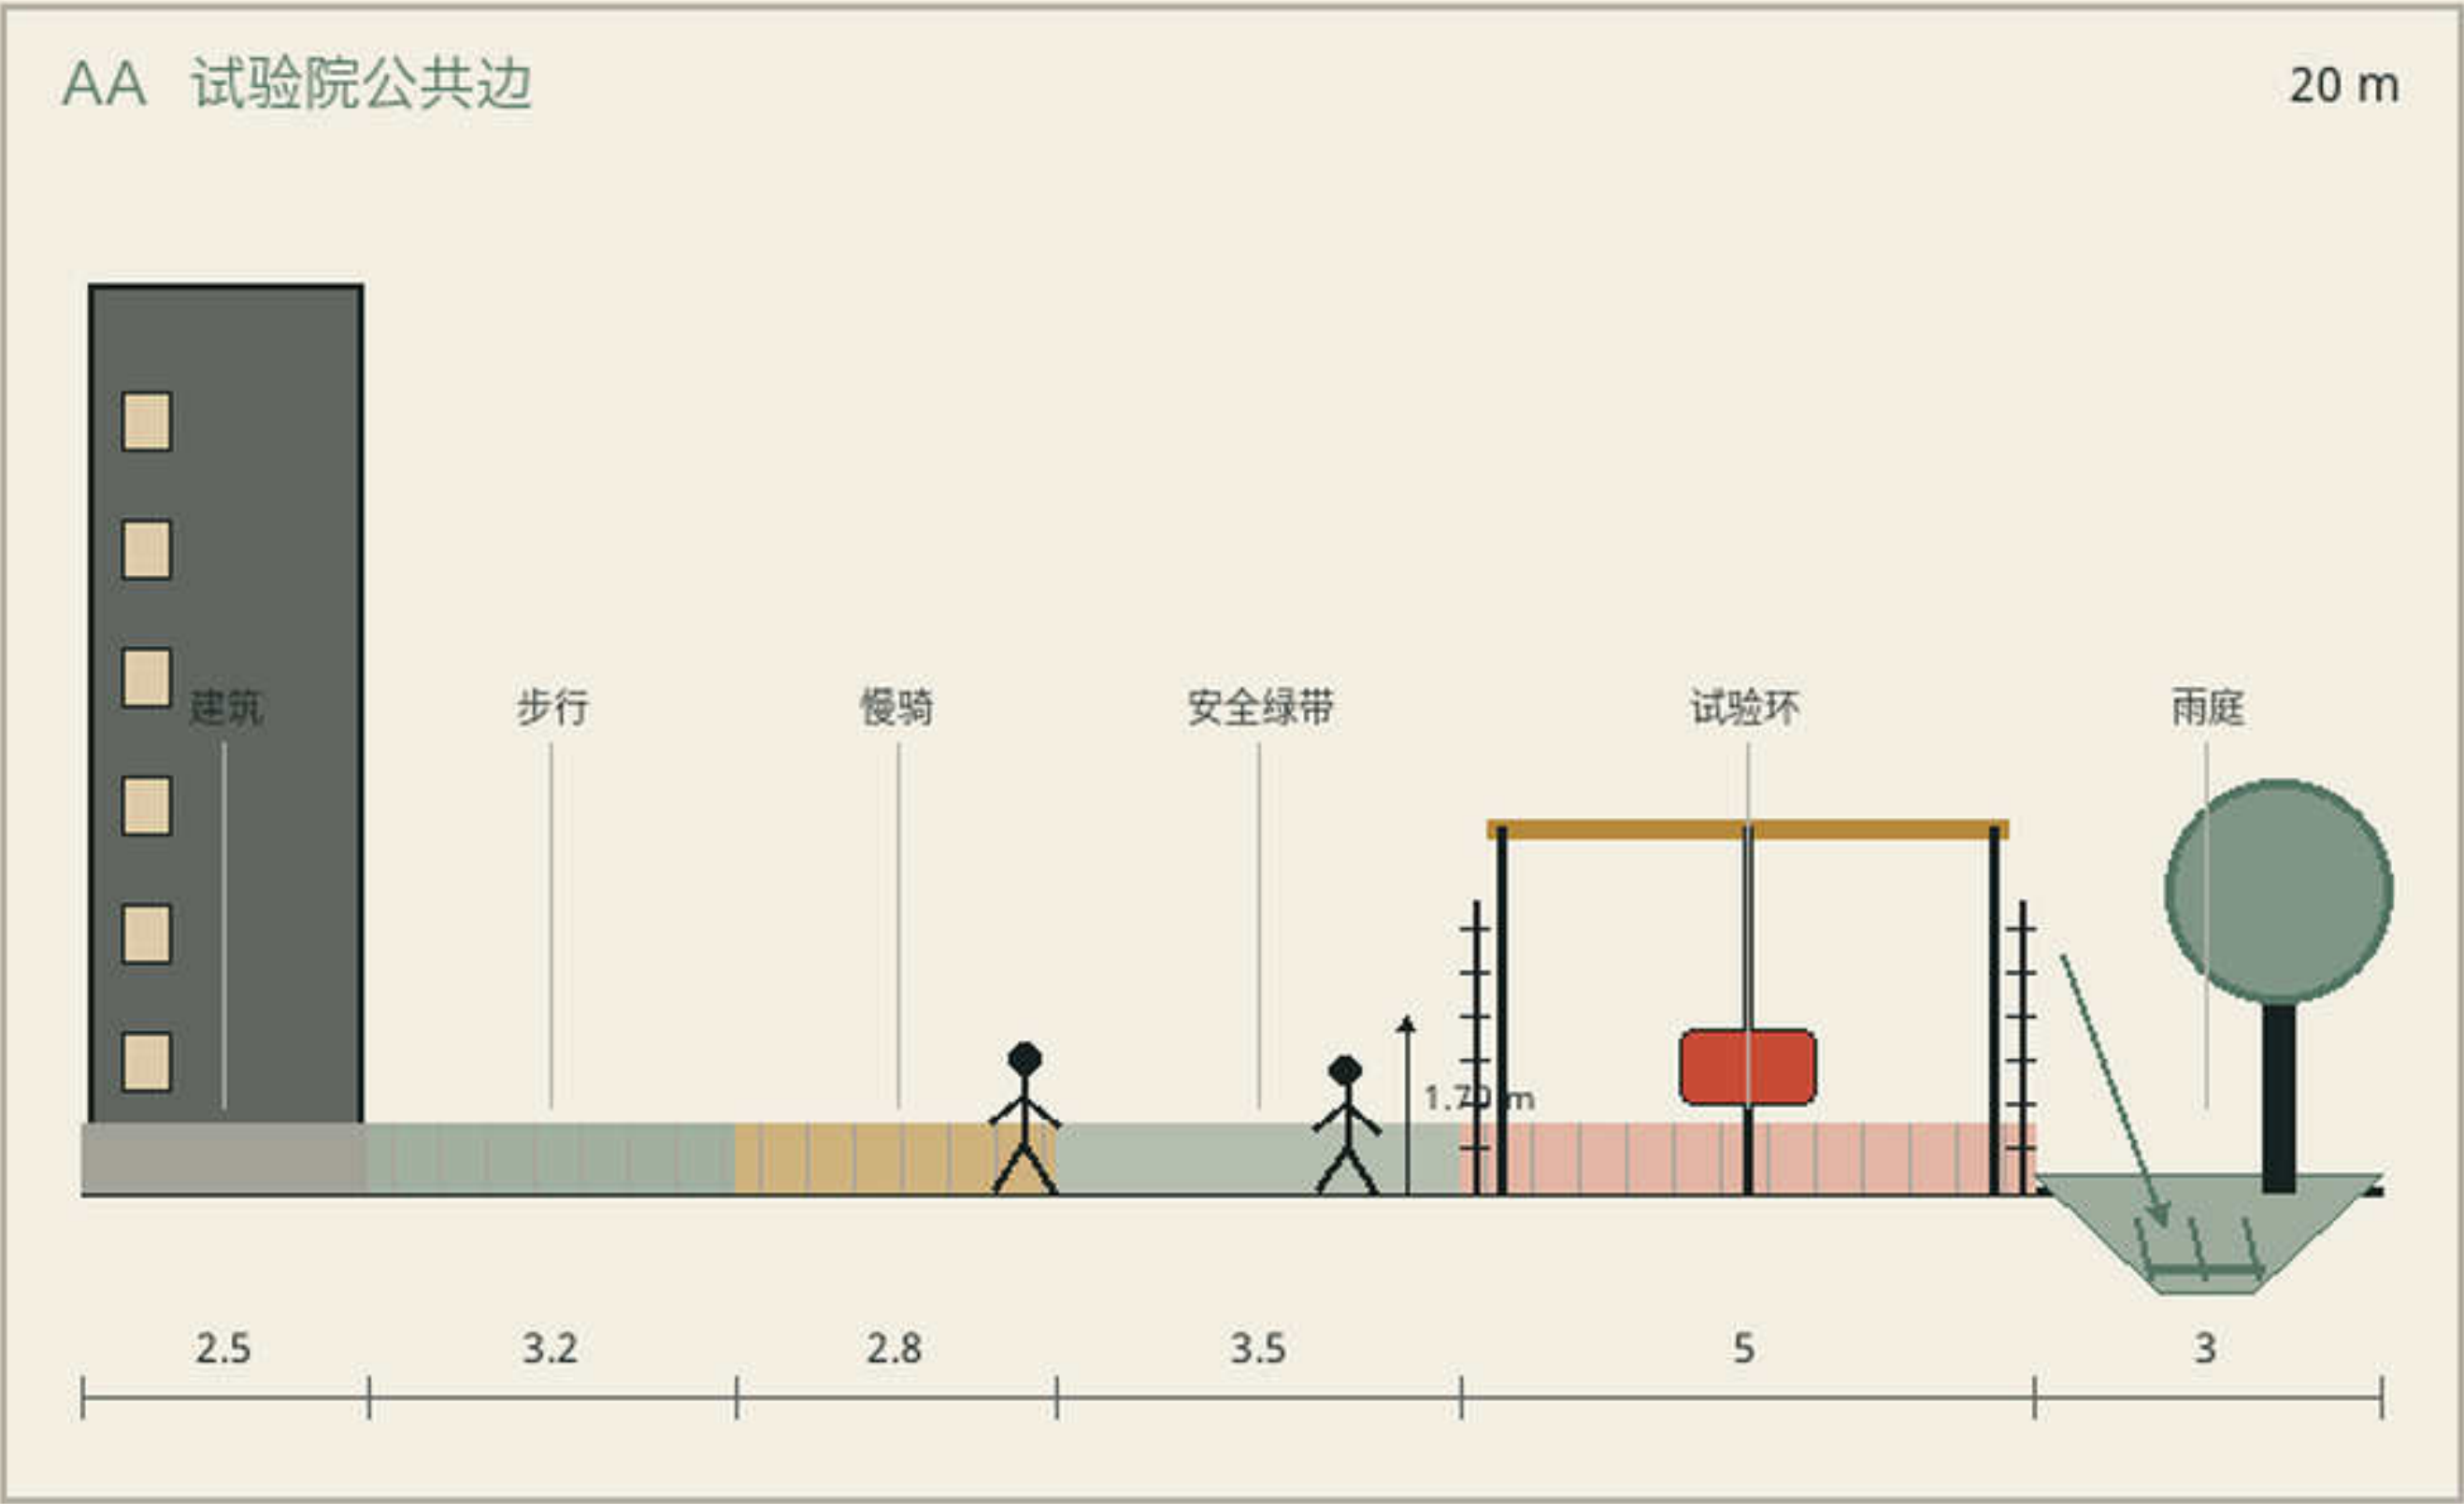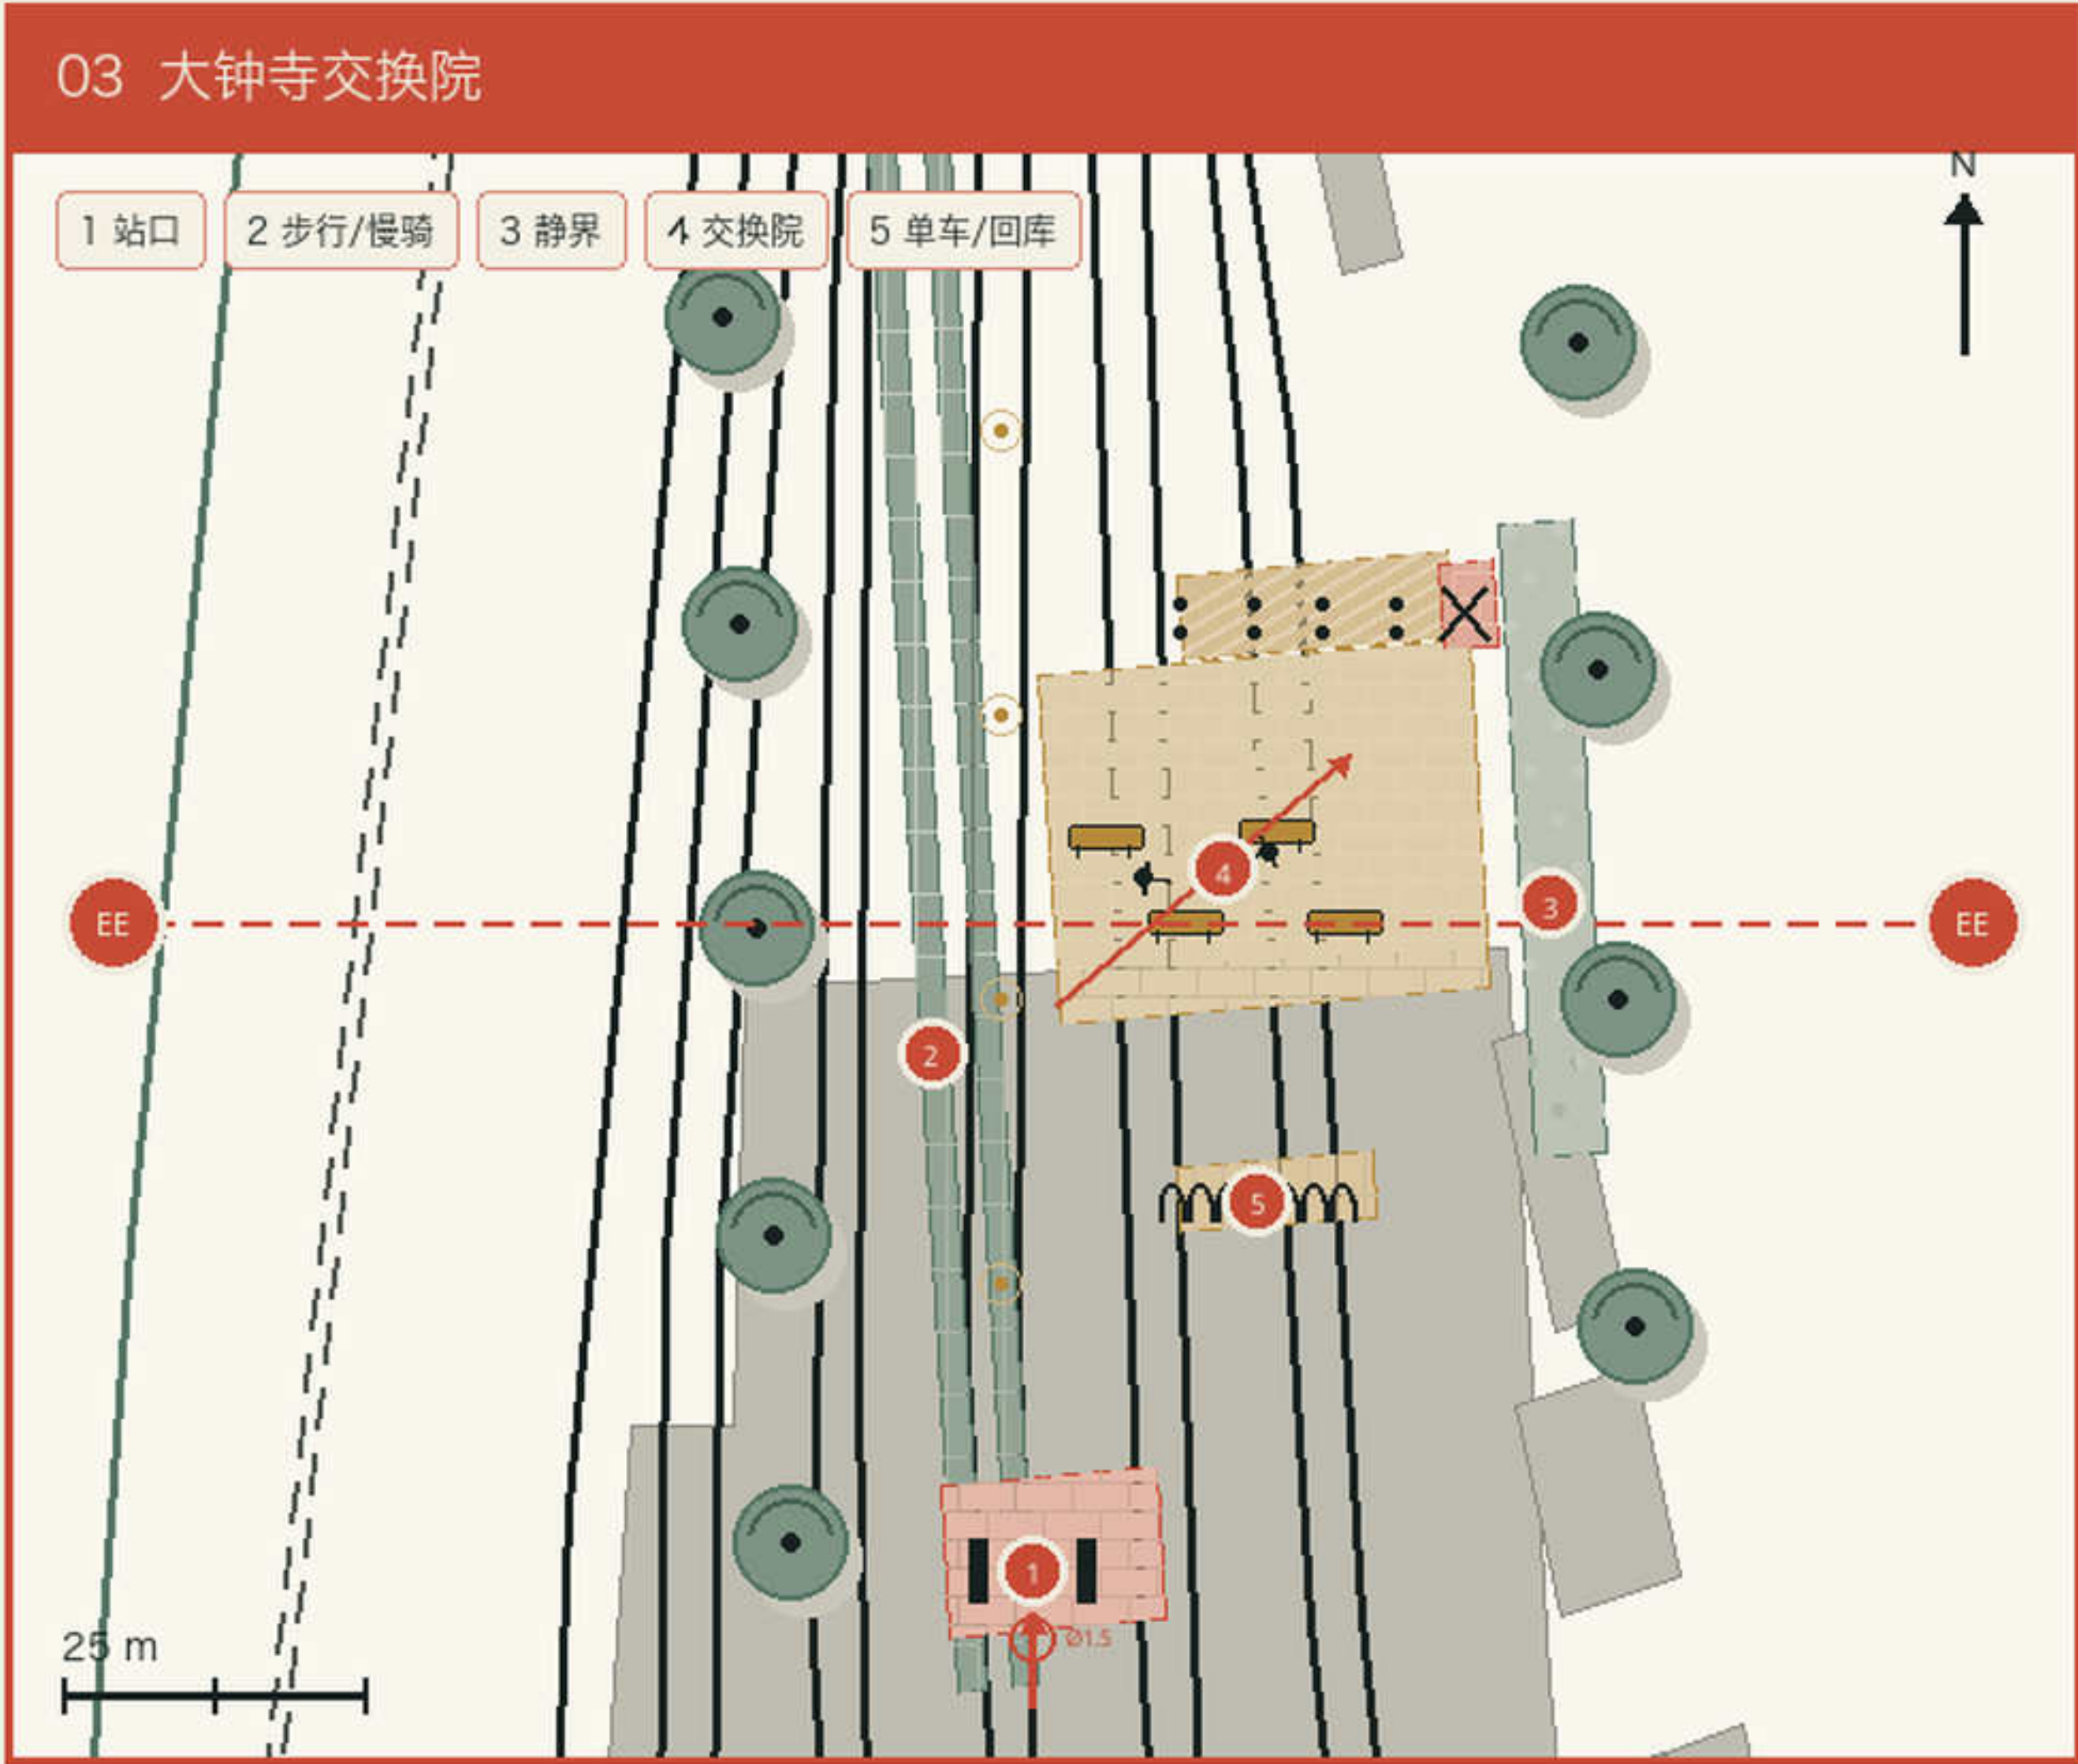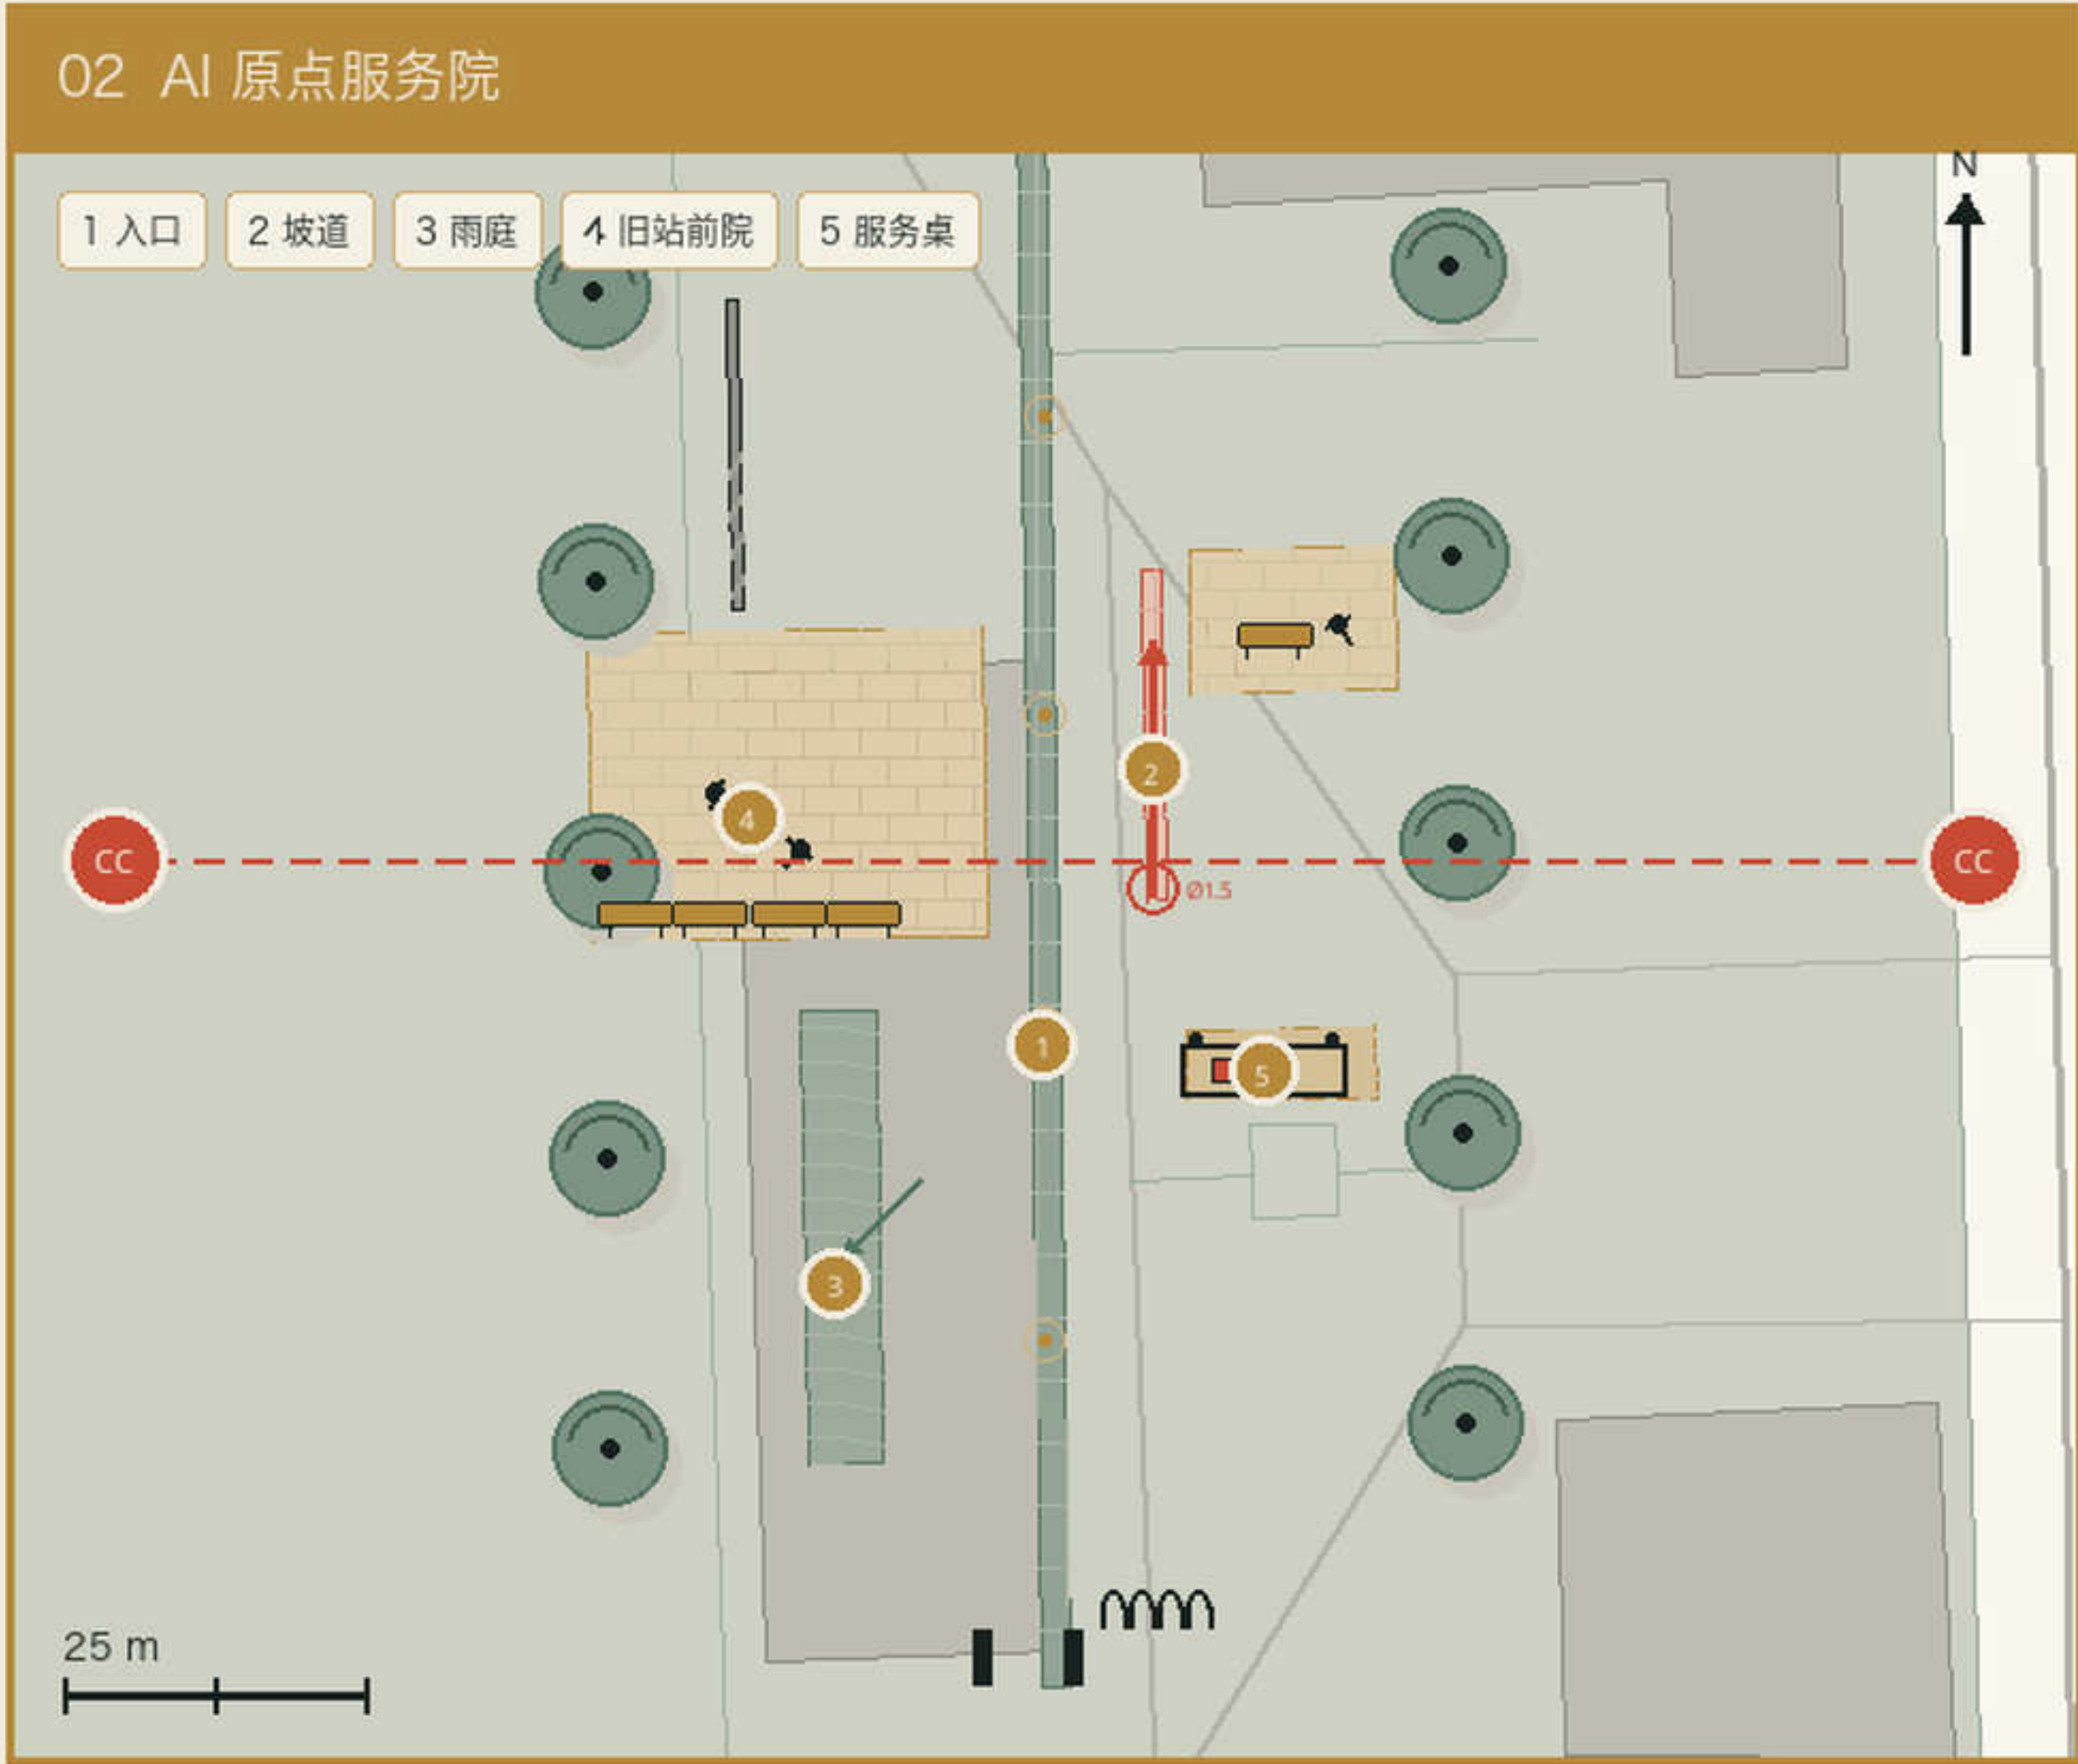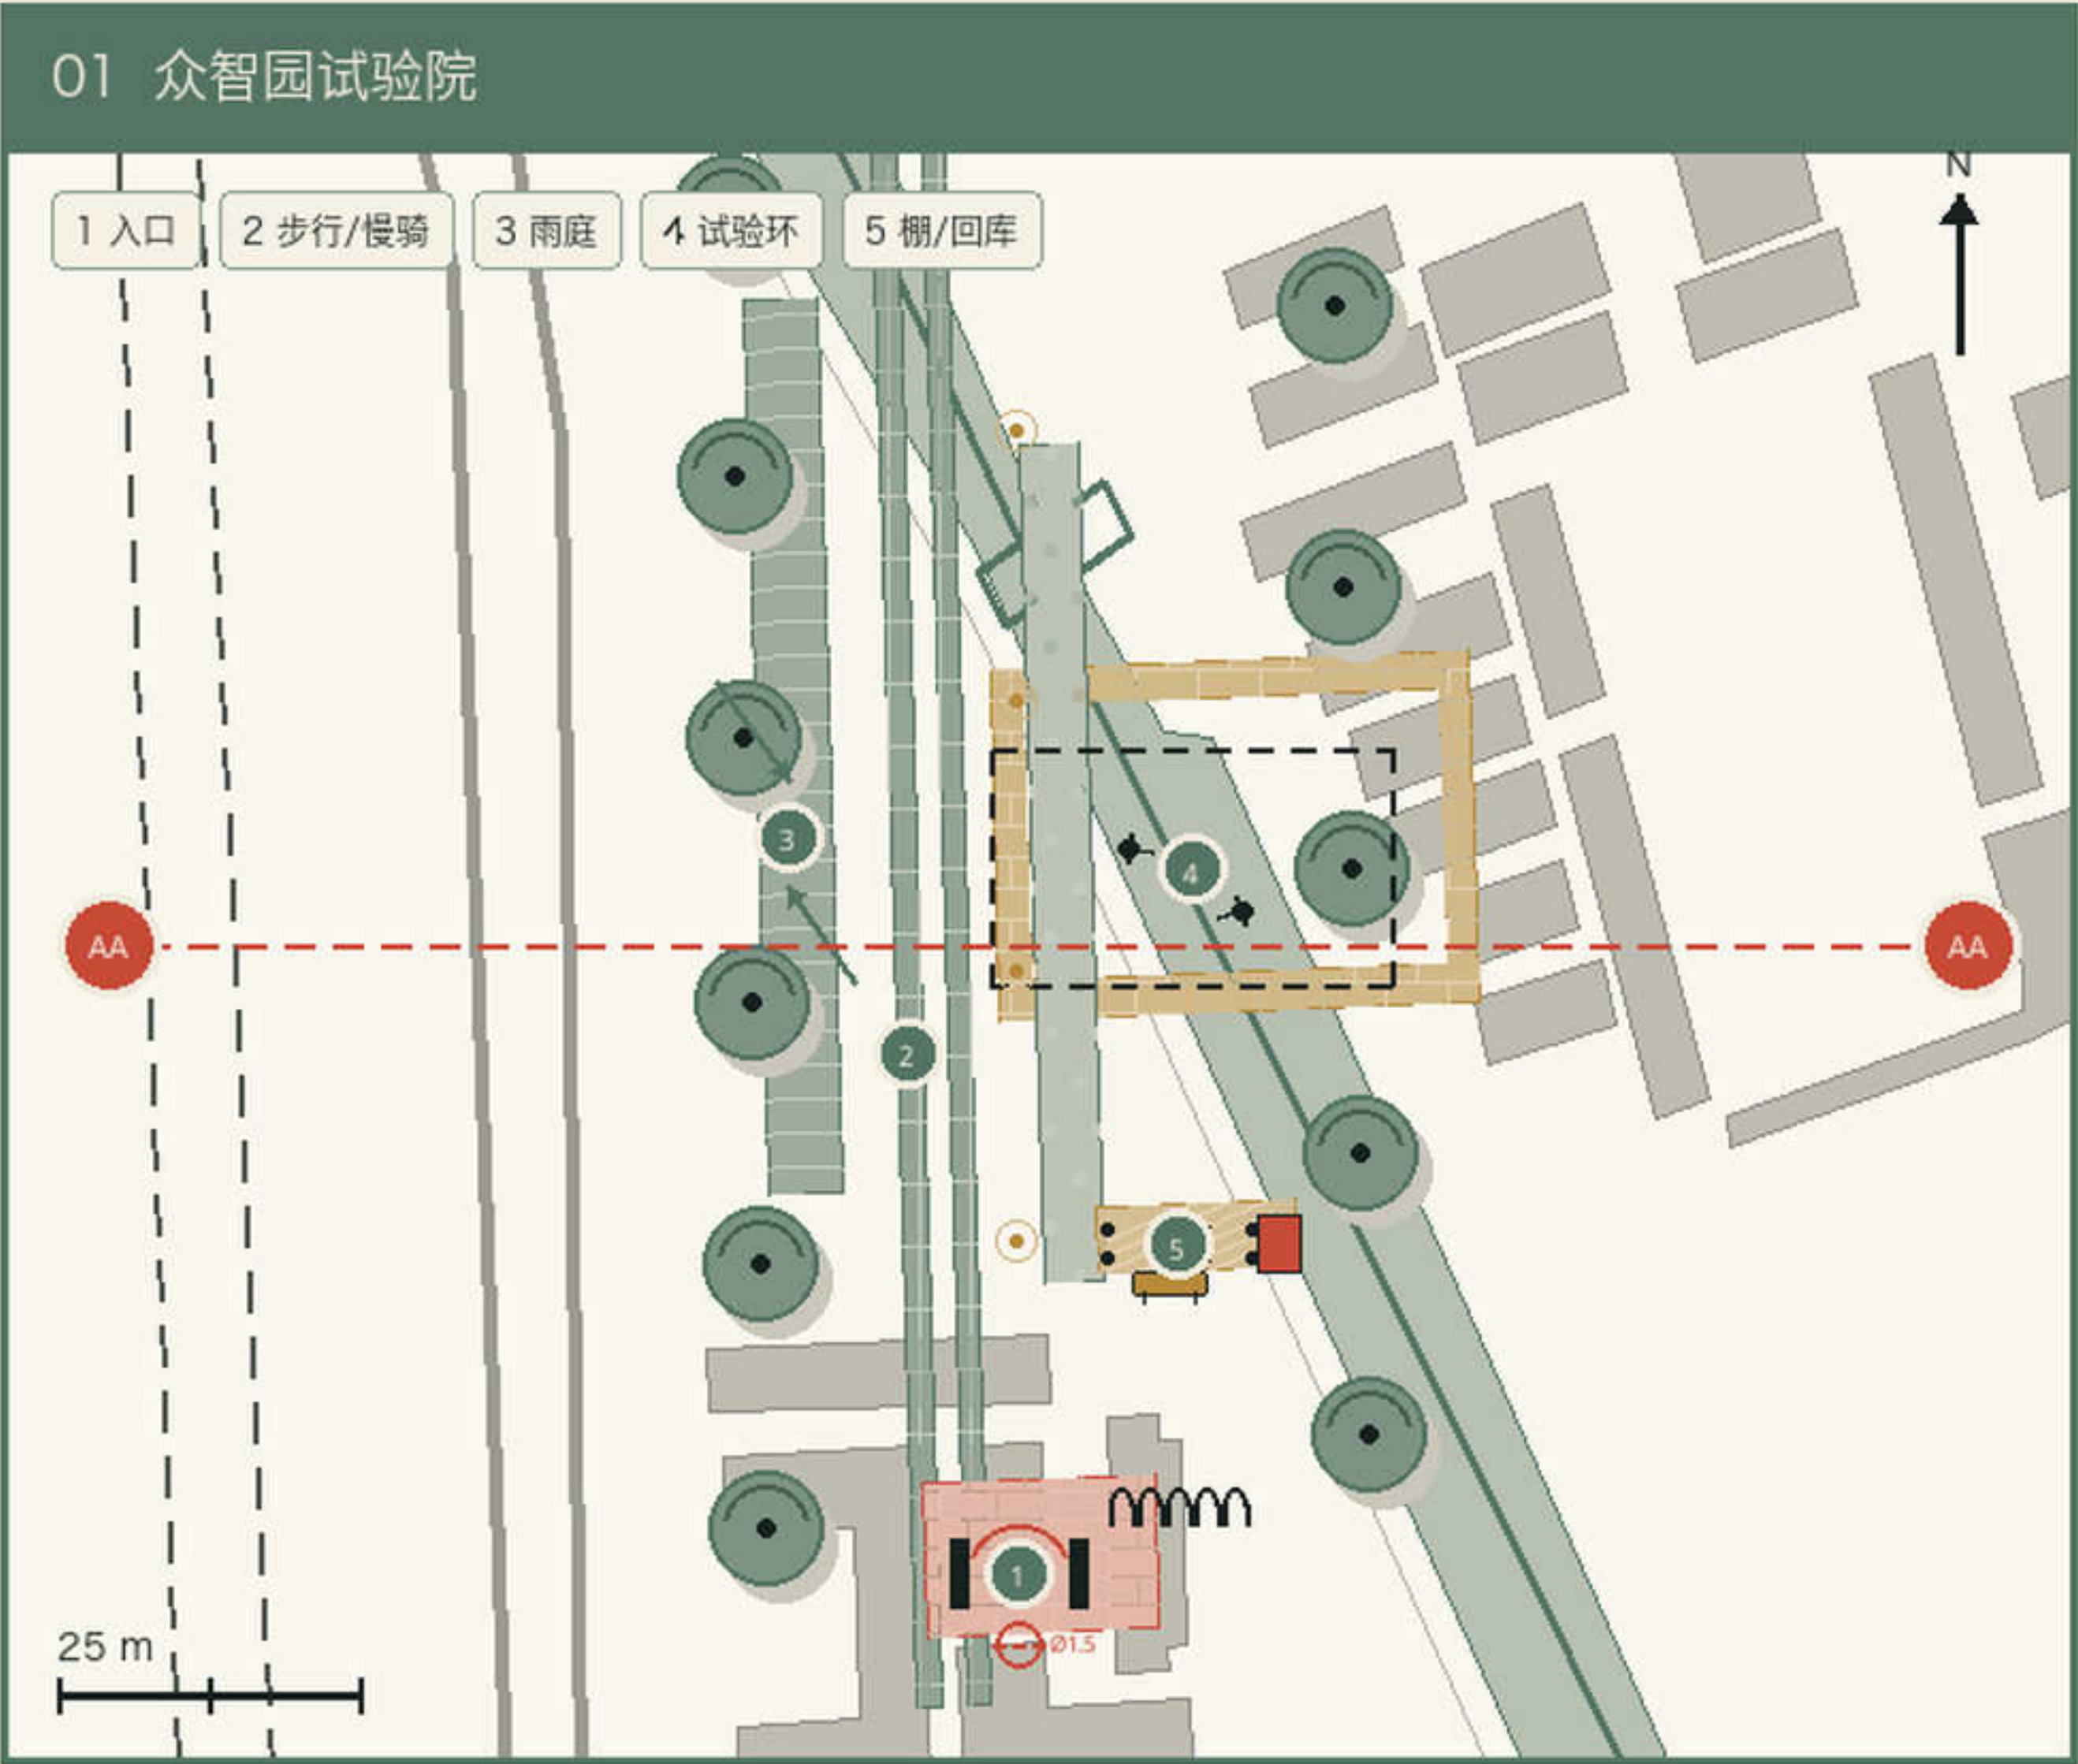

OSM 仅作现状底图 | 概念边界须以测绘、权属与审批复核

approx. 1:500 | WORKING DIMENSIONS | CONCEPT DESIGN



04

慢行、过街、轨道和小月河








路线先过断点，六条剖面再交代宽度、无障碍和排水

步行/雨水

慢骑

无障碍过街

轨道/需审批

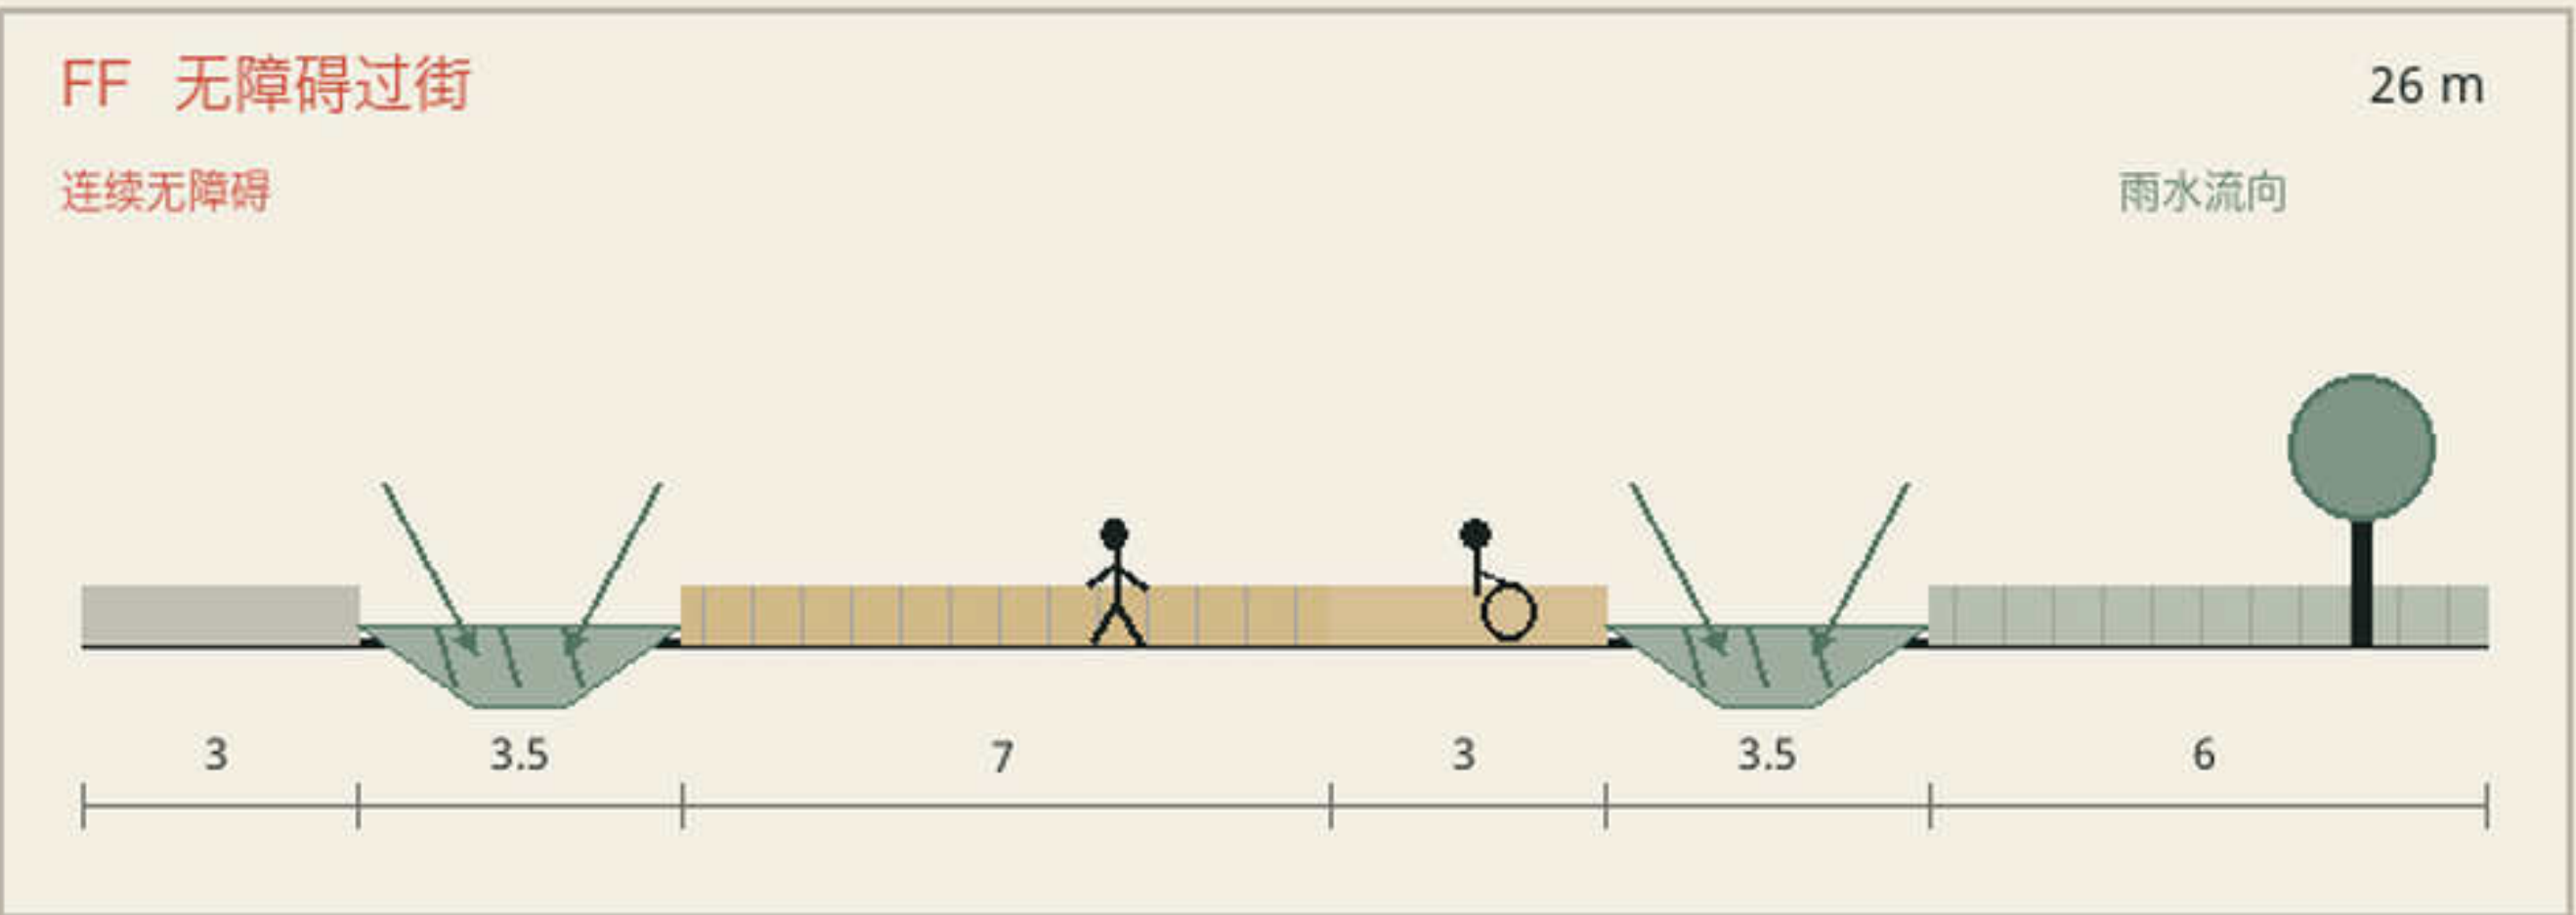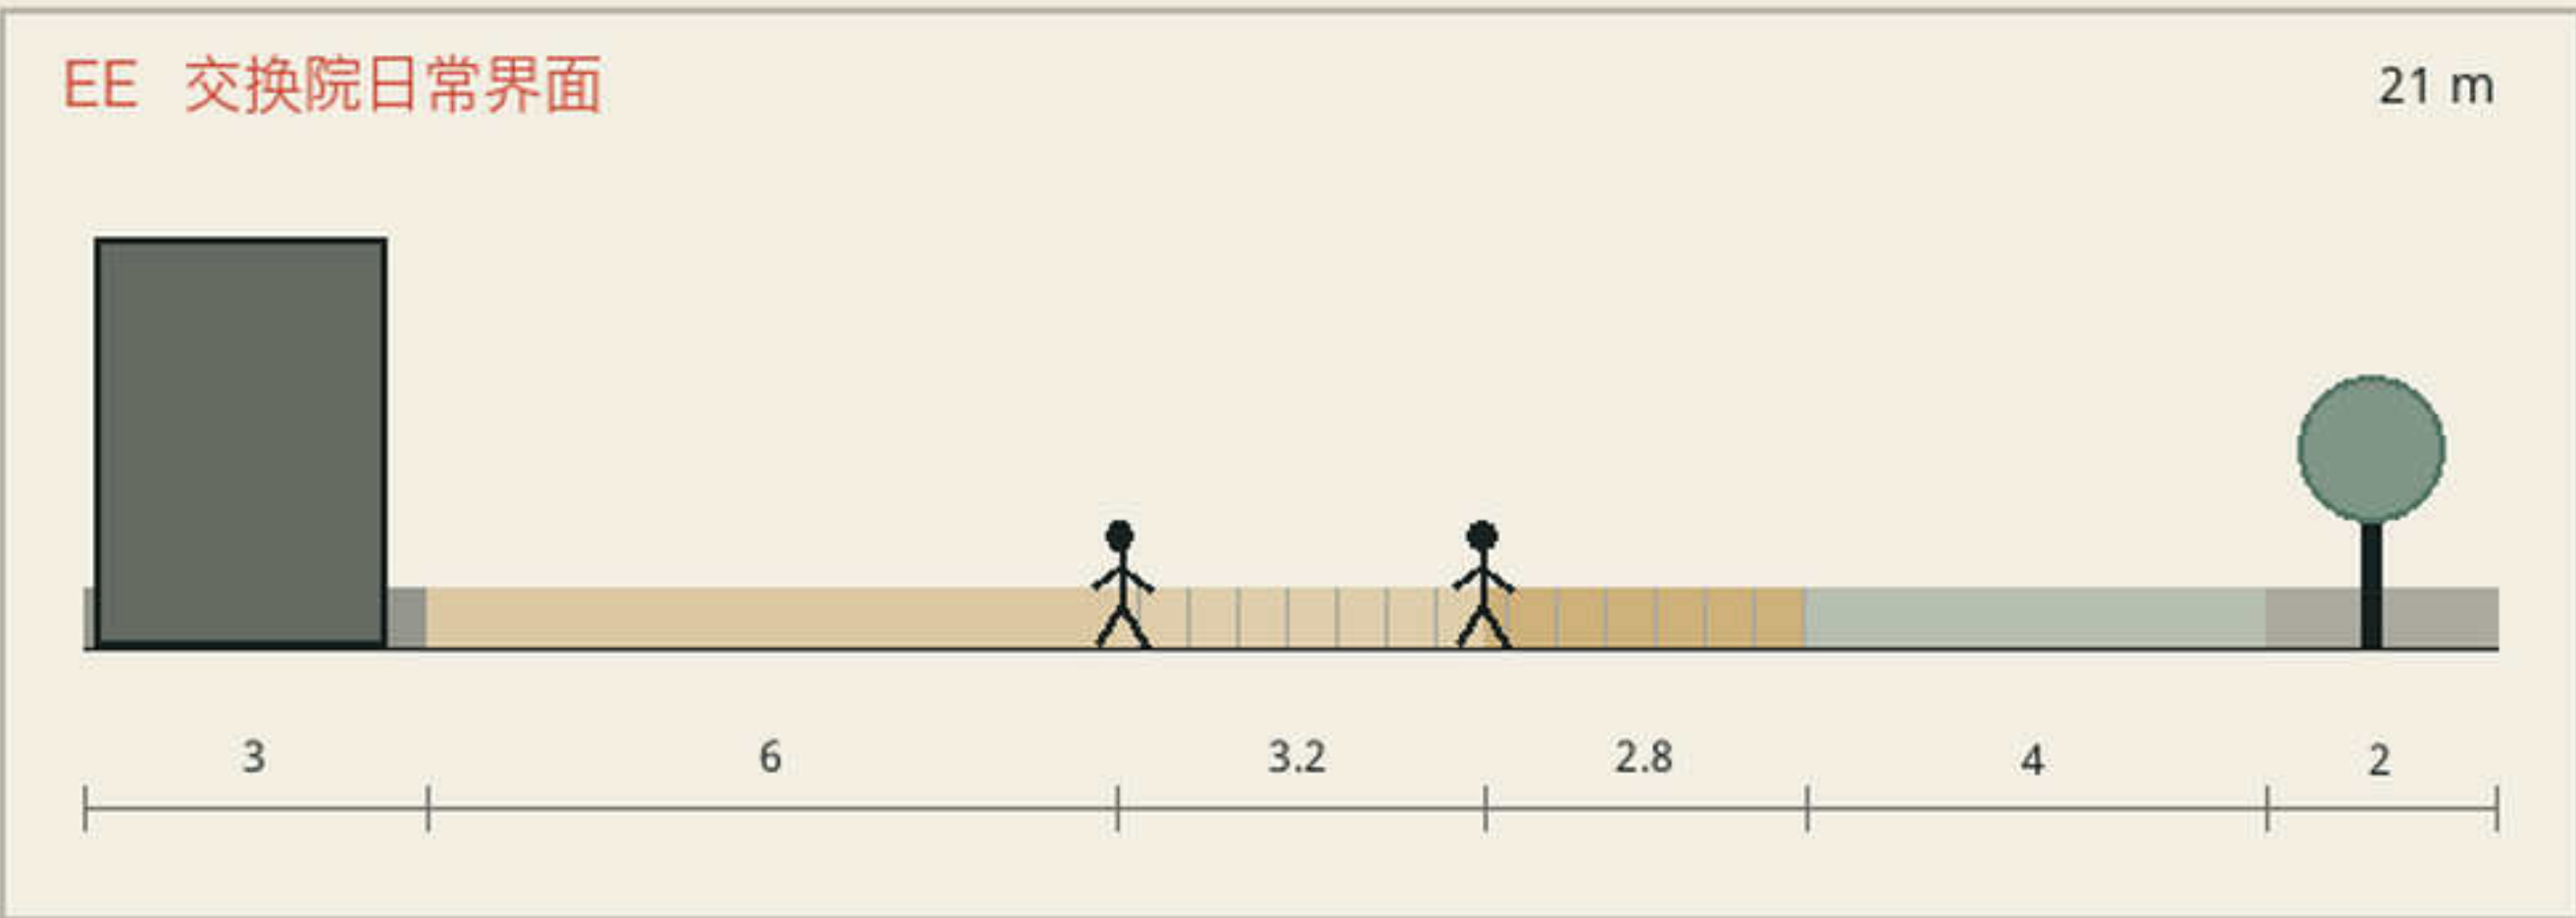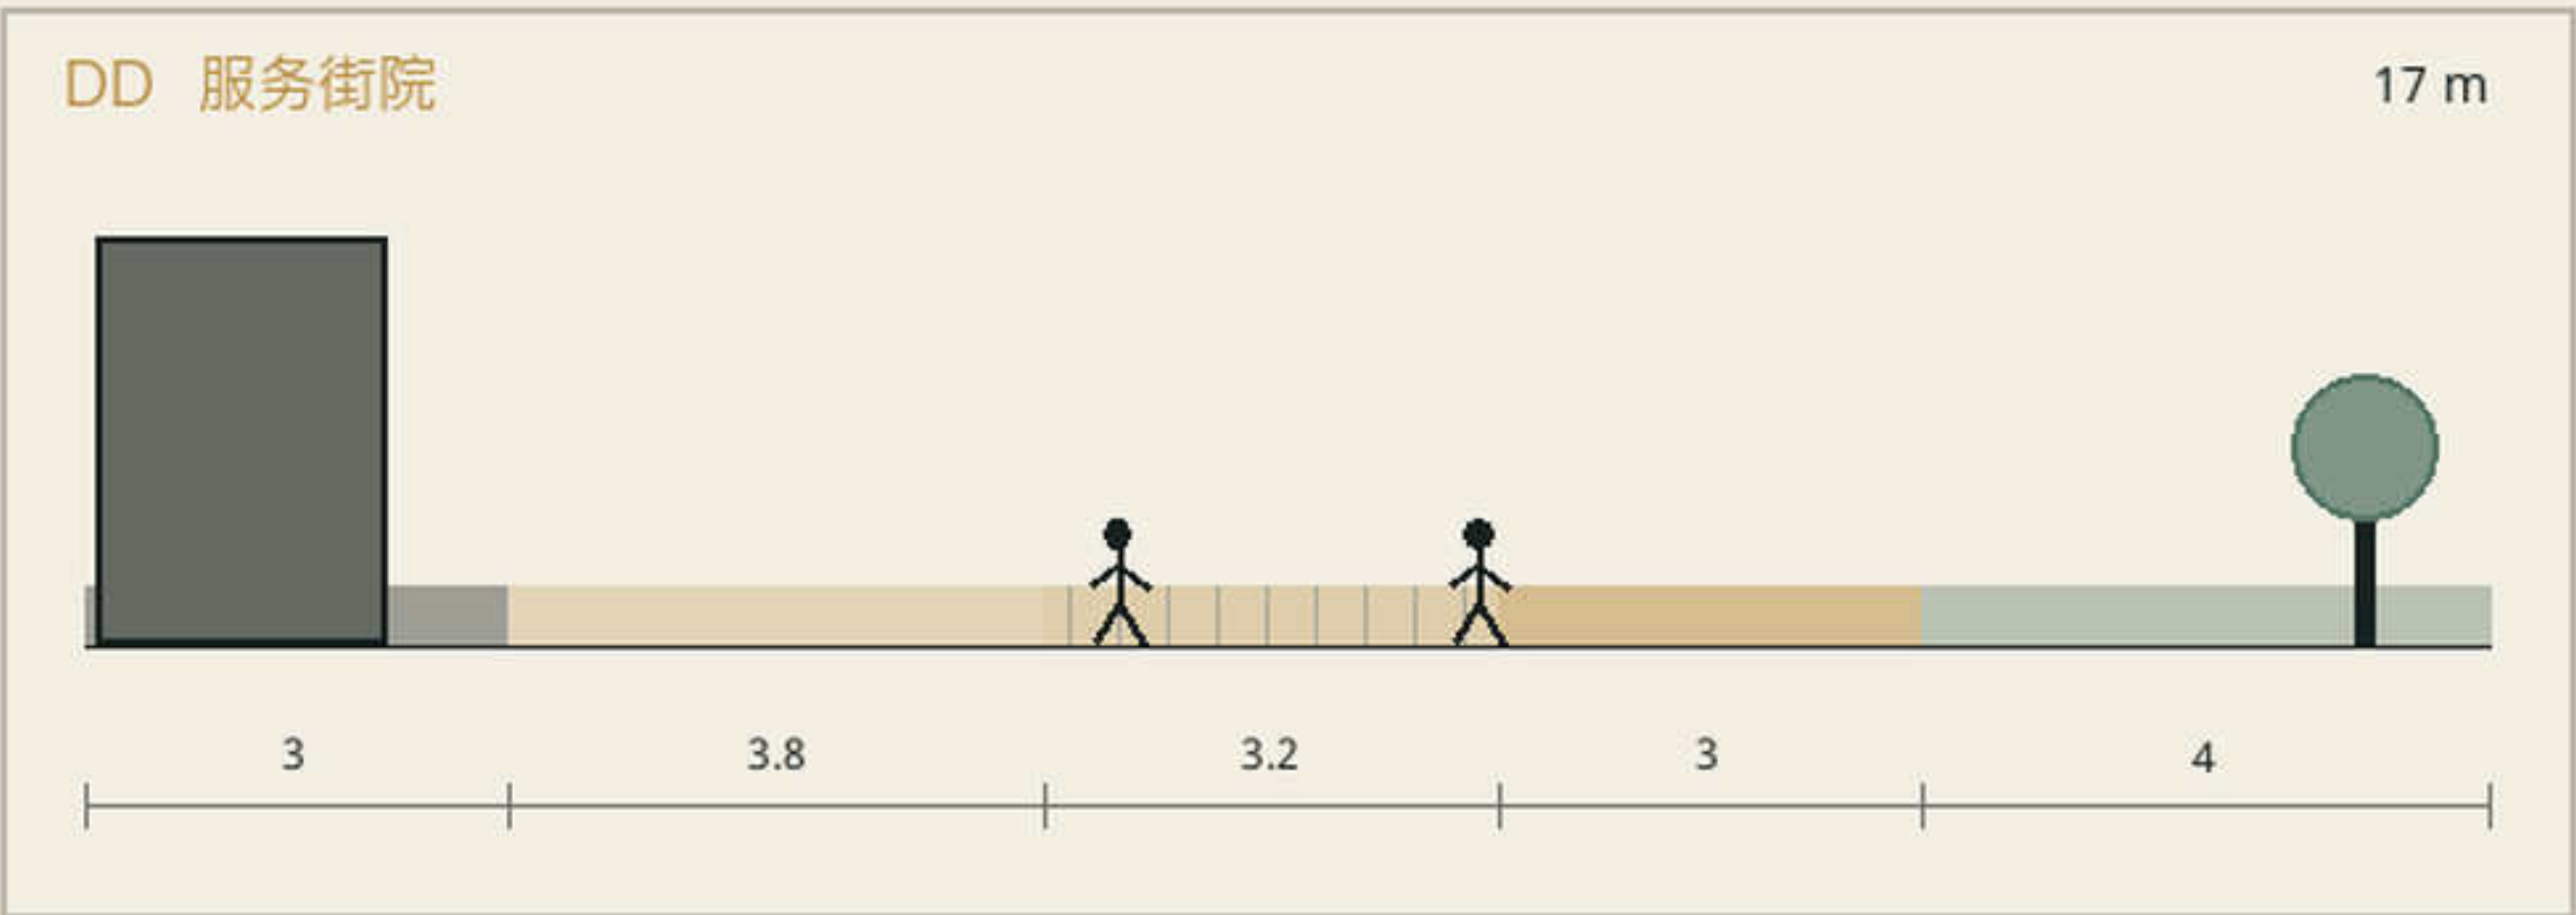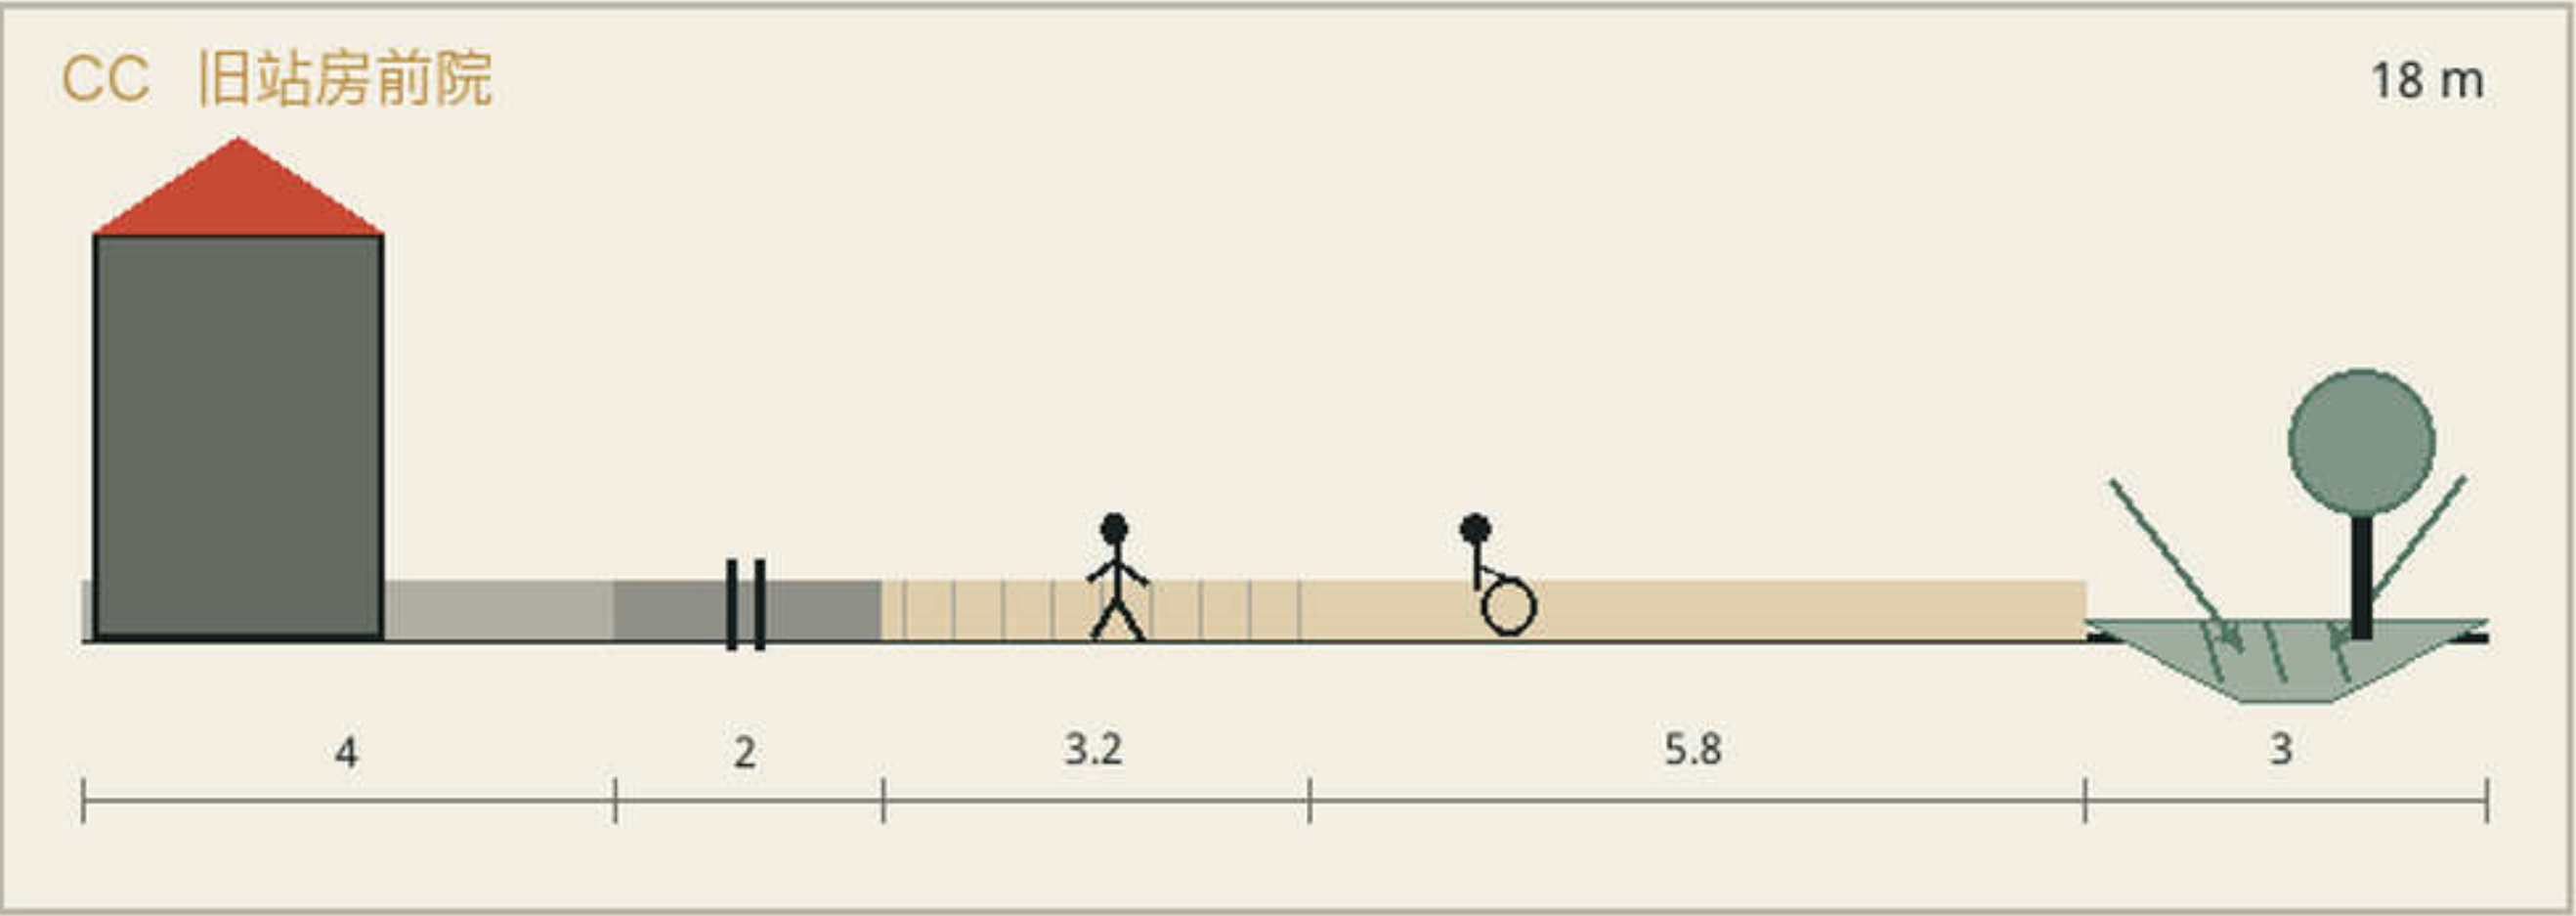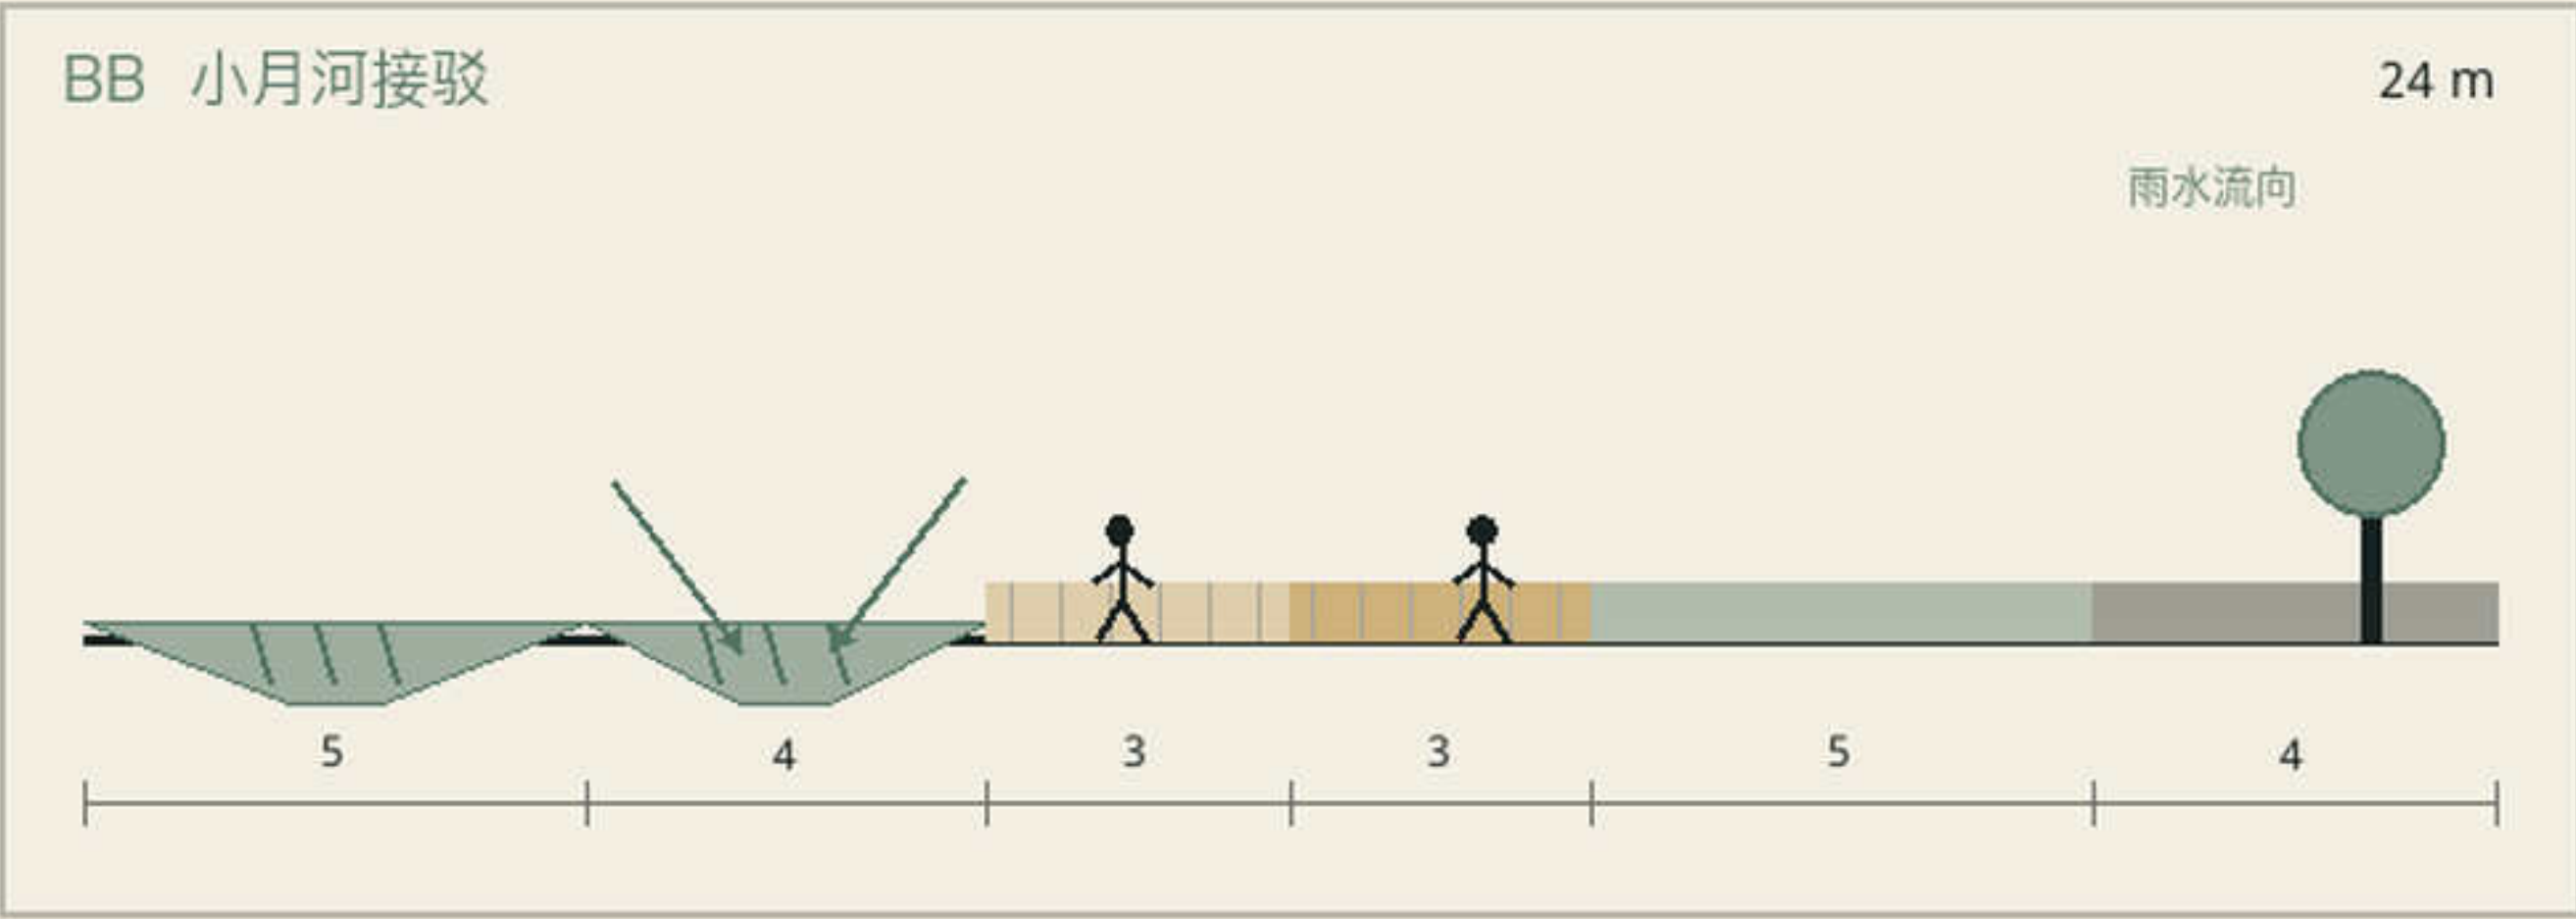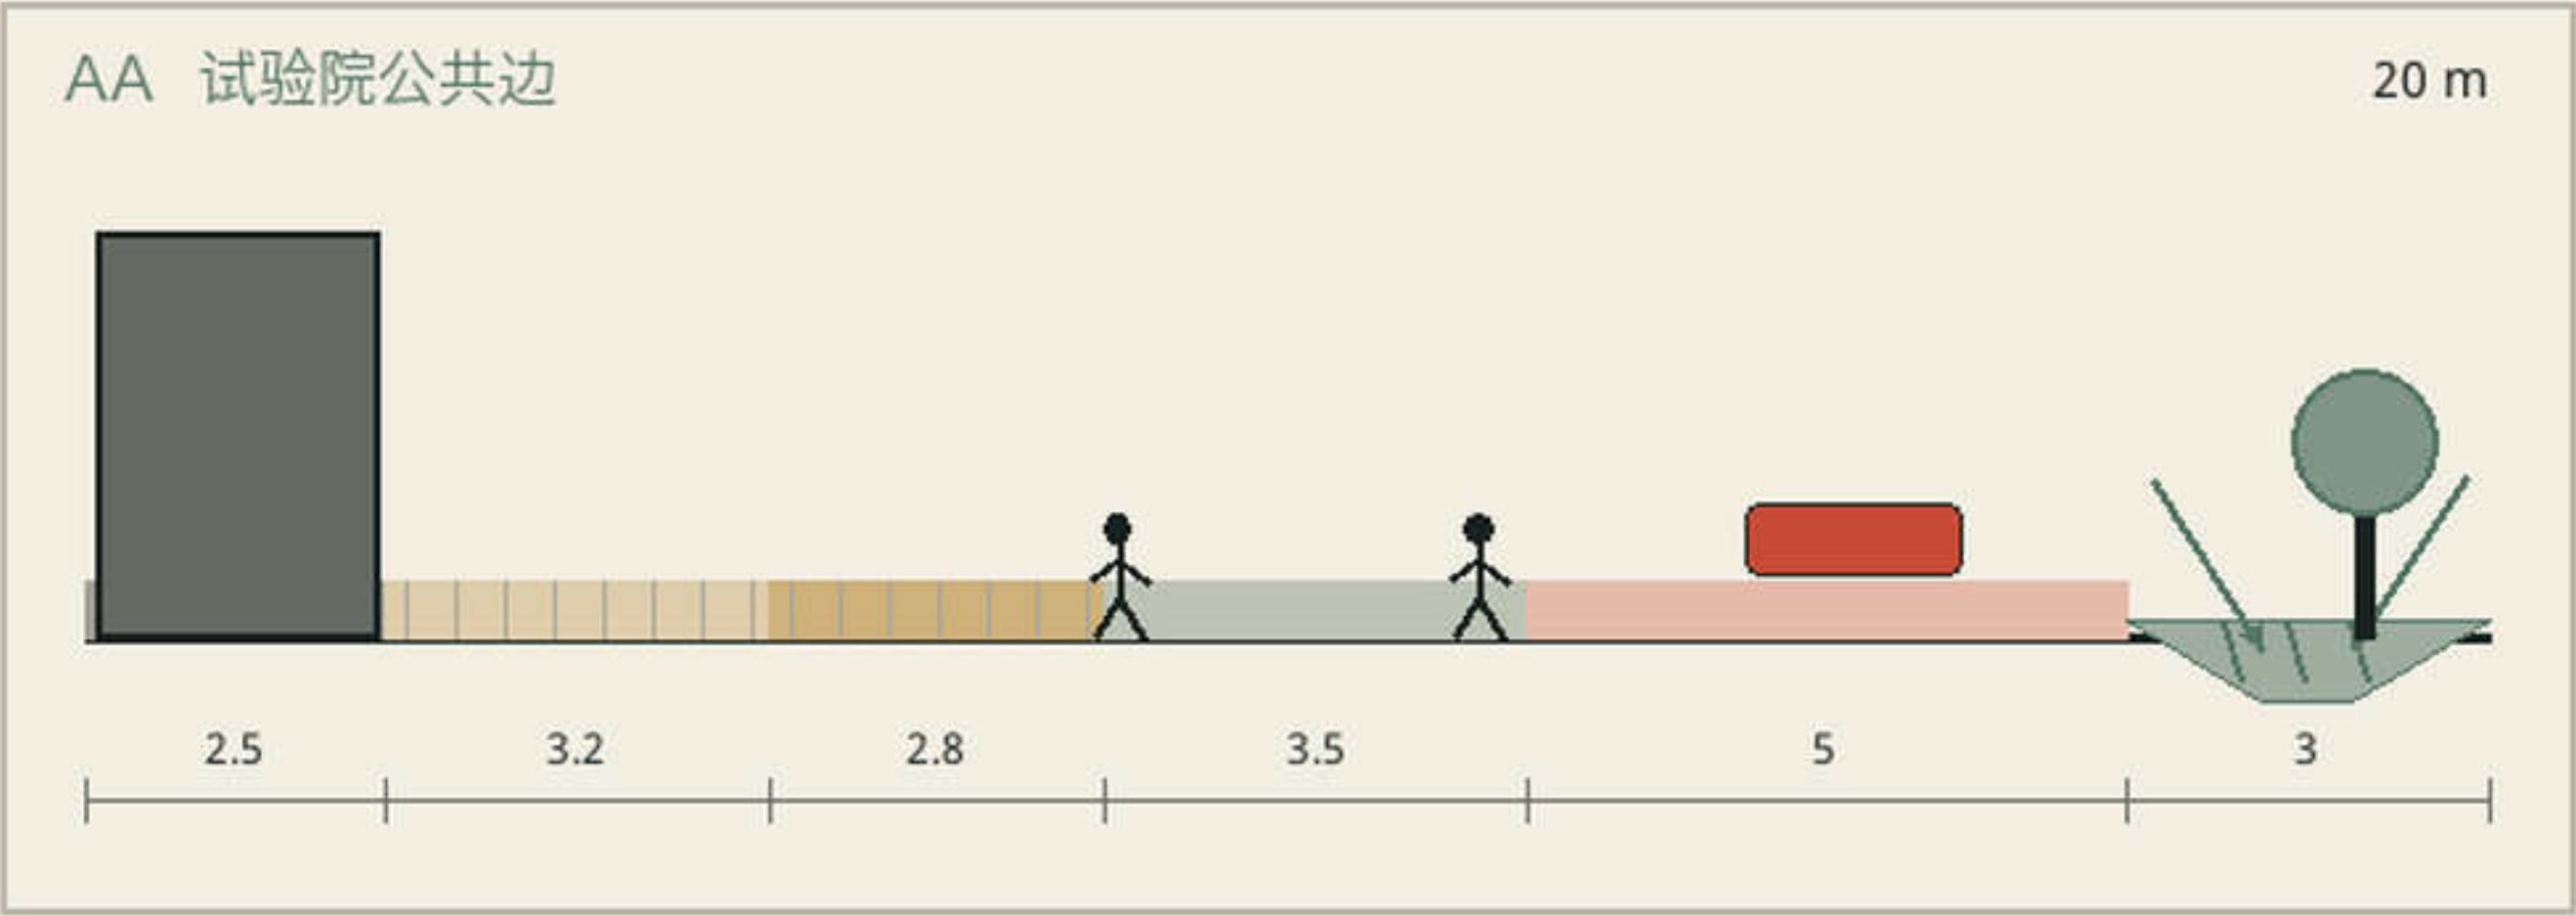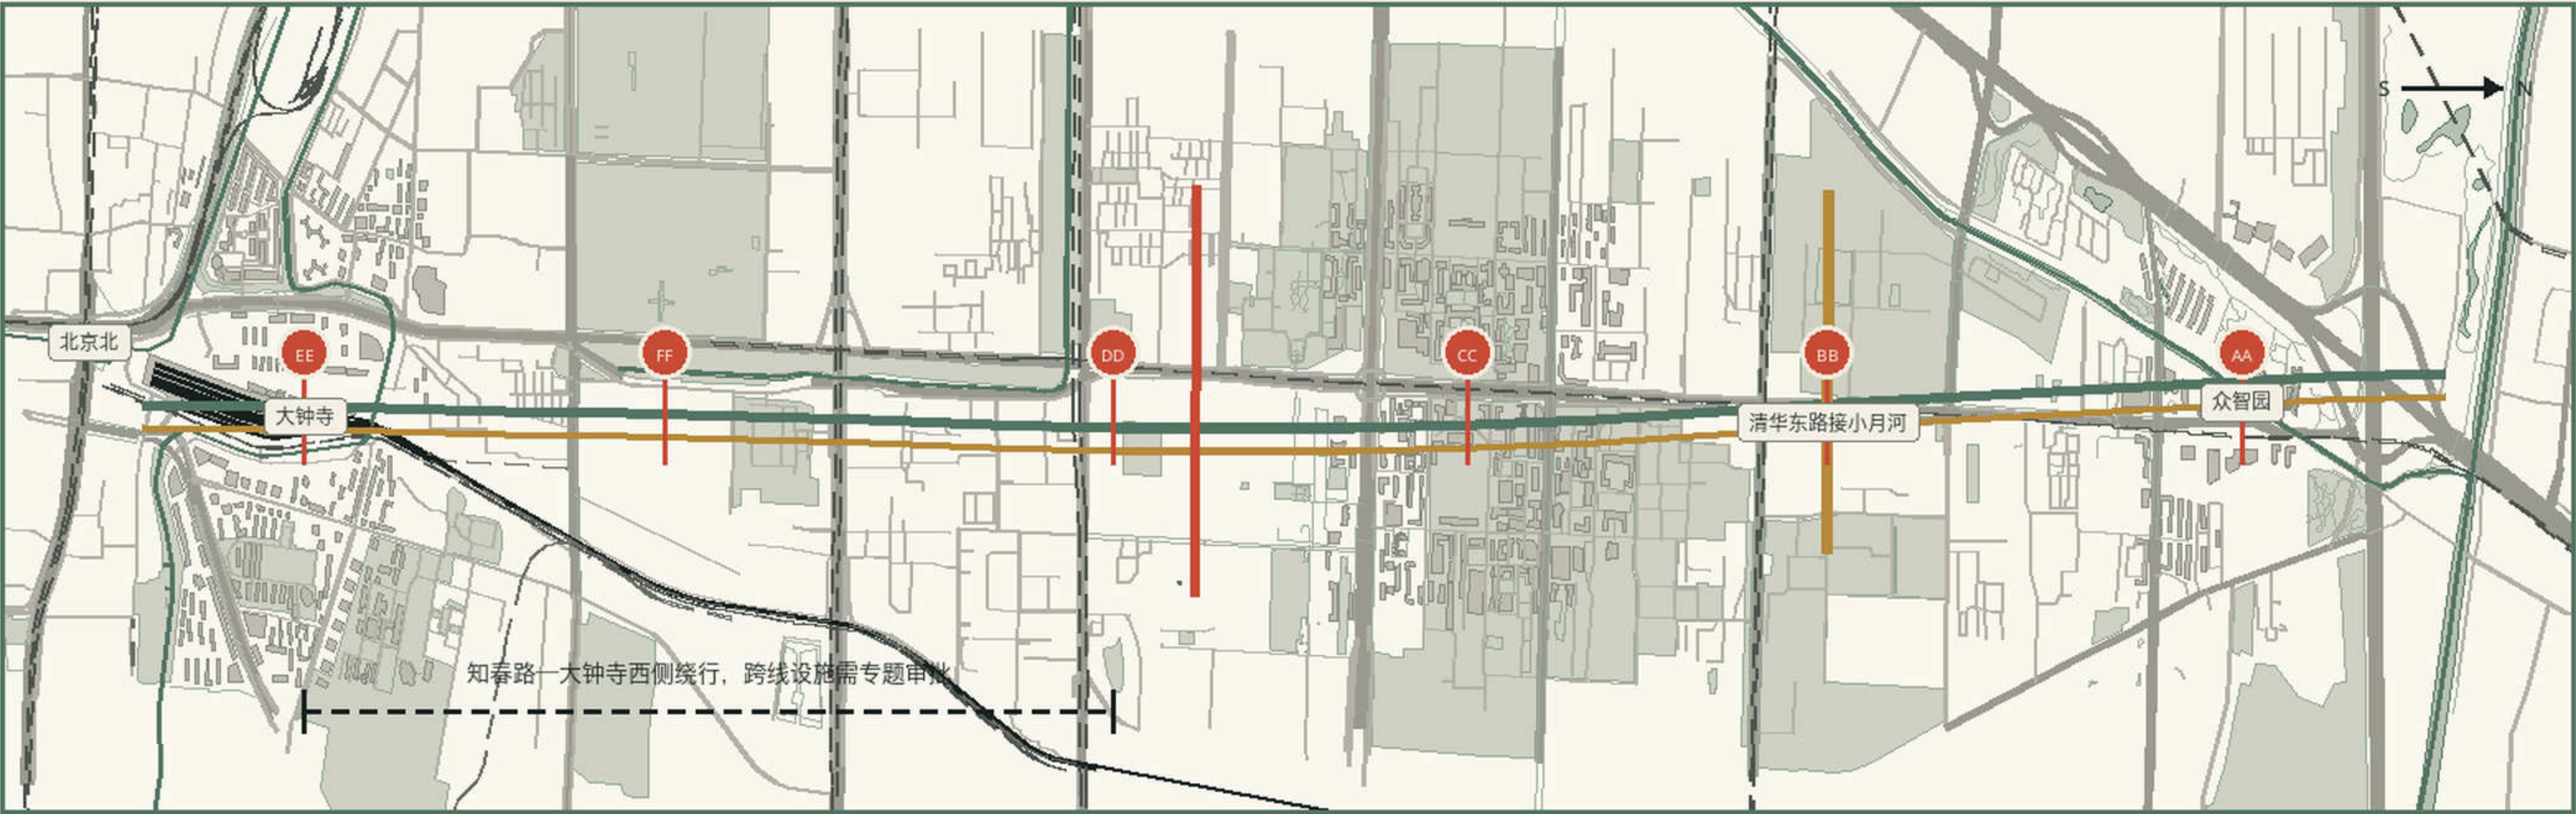

OSM 仅作现状底图 | 概念边界须以测绘、权属与审批复核

WIDTHS IN METRES | DB11/T 1761-2020 WORKING LOGIC



3.2 m
公共步道工作宽度

2.8 m
骑行带工作宽度




6.41 km
小月河治理长度，不改行洪断面

待论证
13 号线跨线通道仅标问题点

04

一个300米节点，怎么真正落地

鸟瞰、平面与剖面用同一套尺寸对话

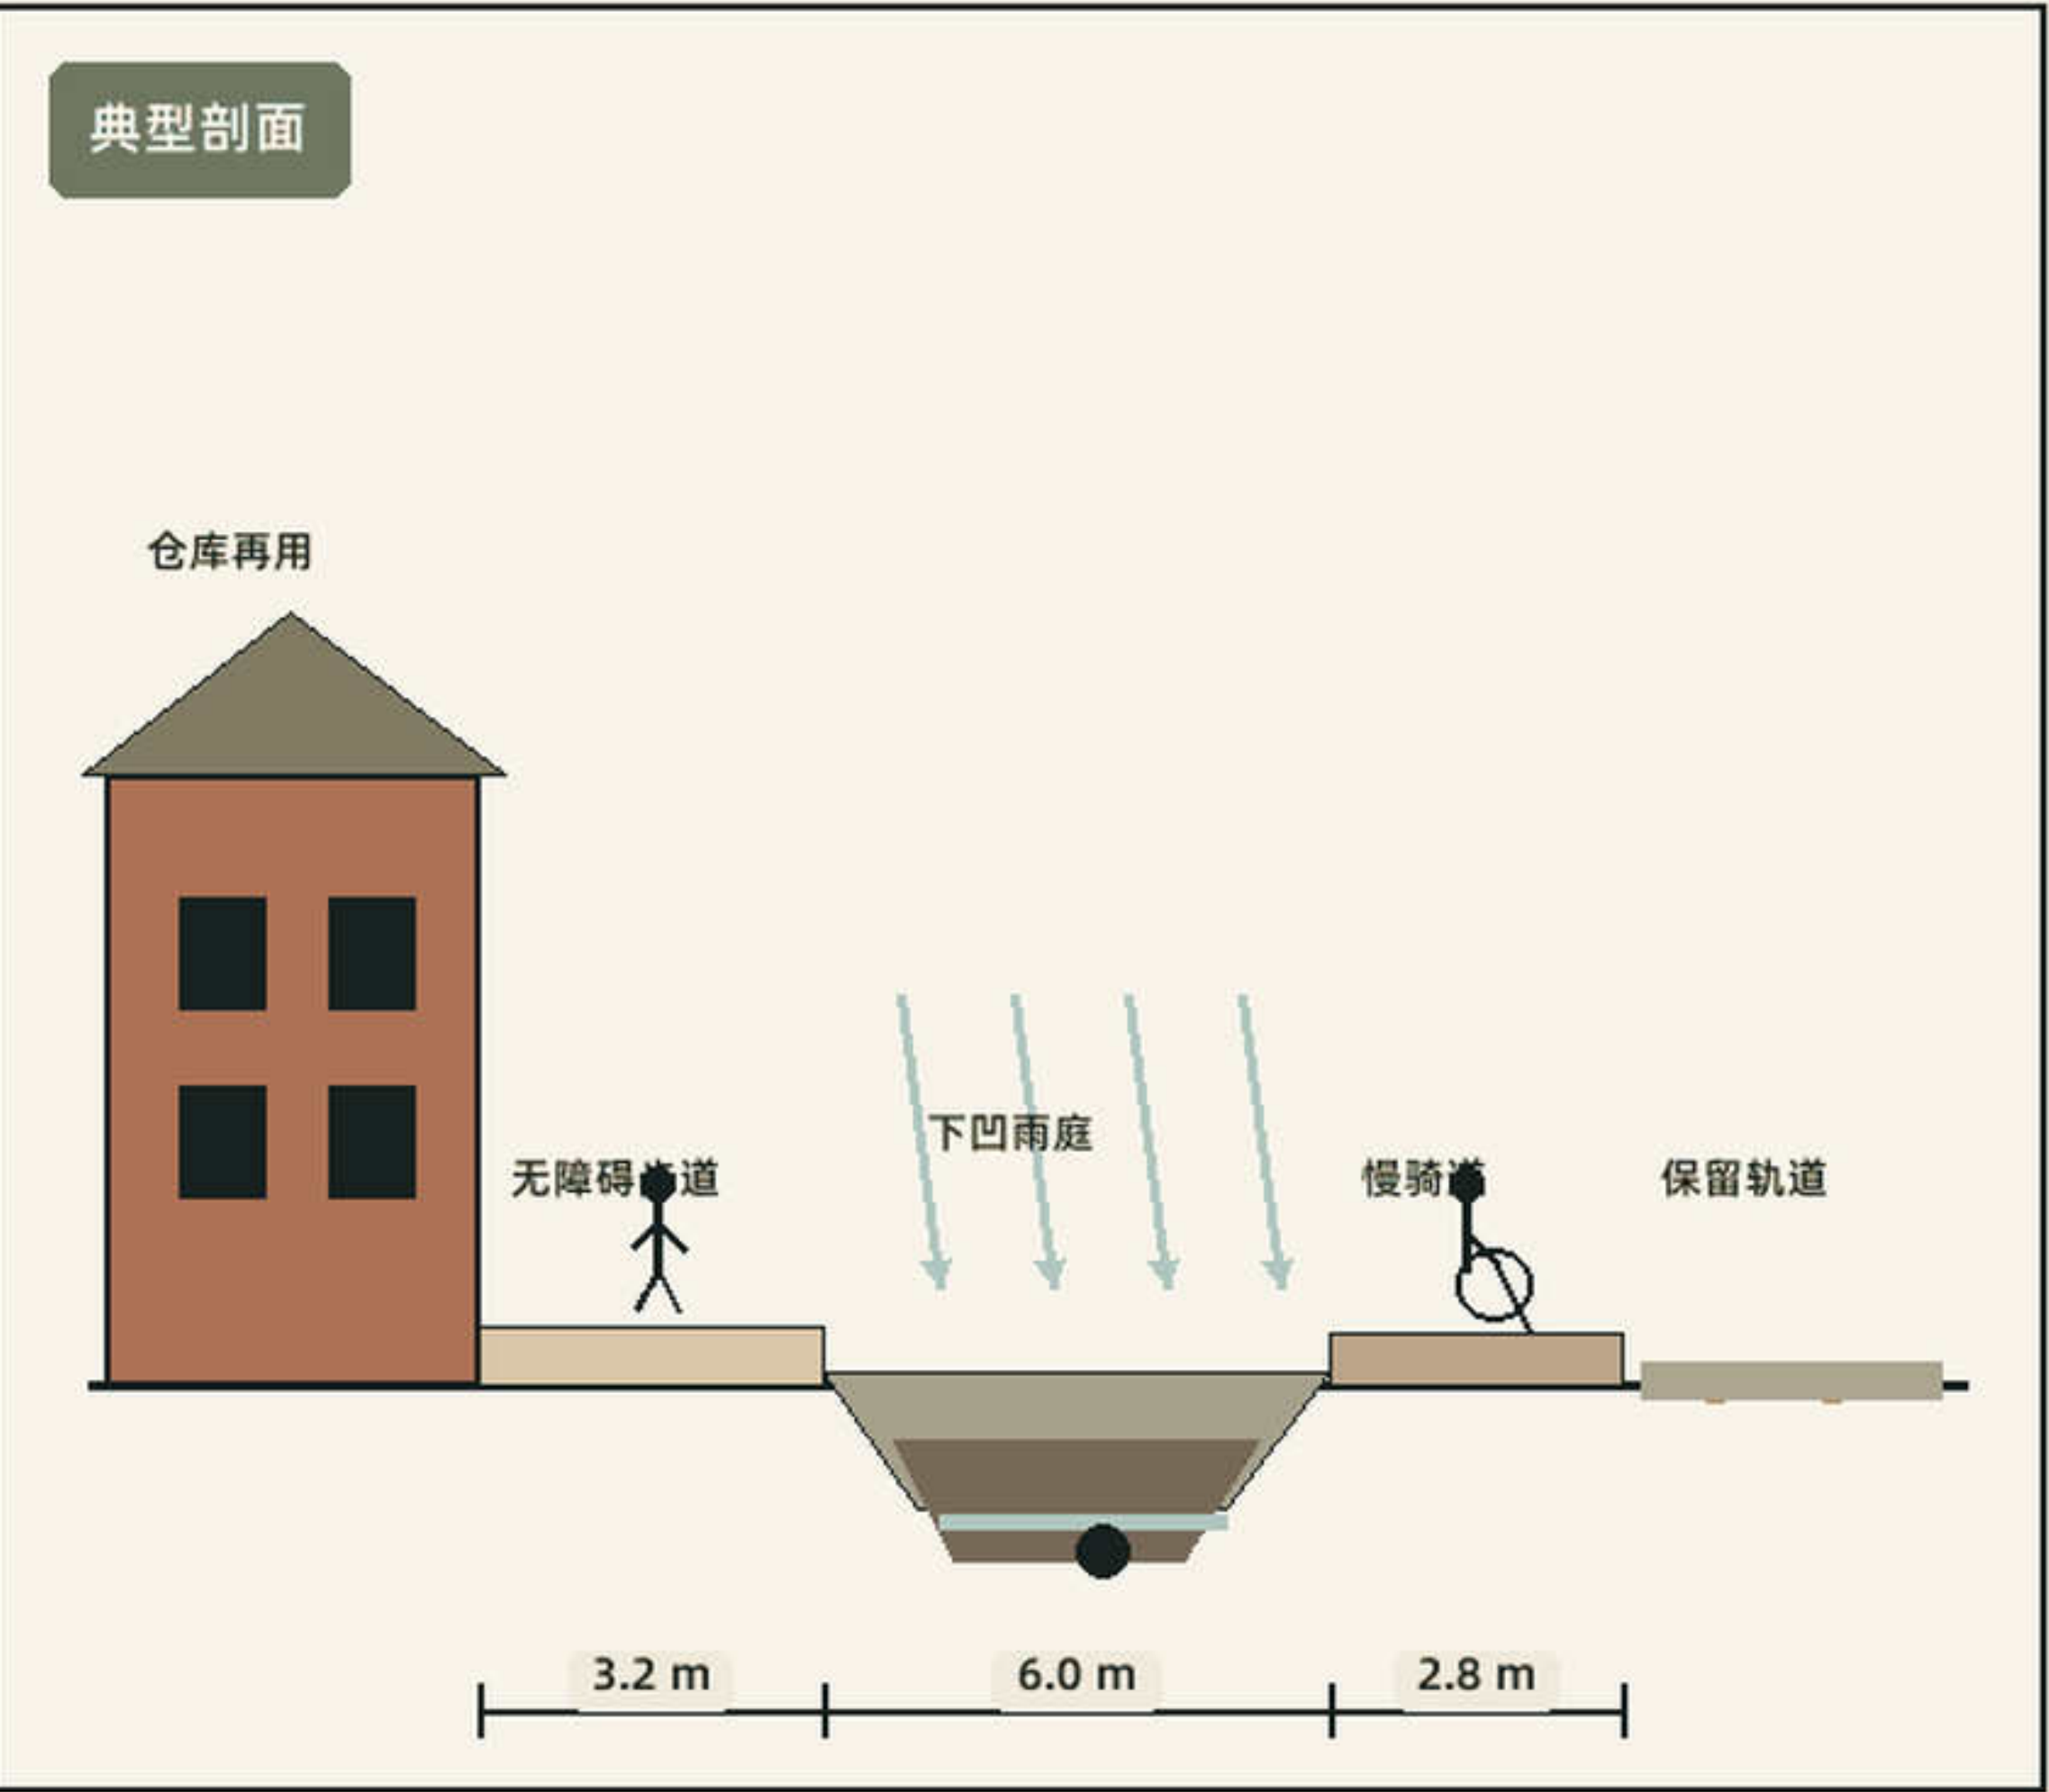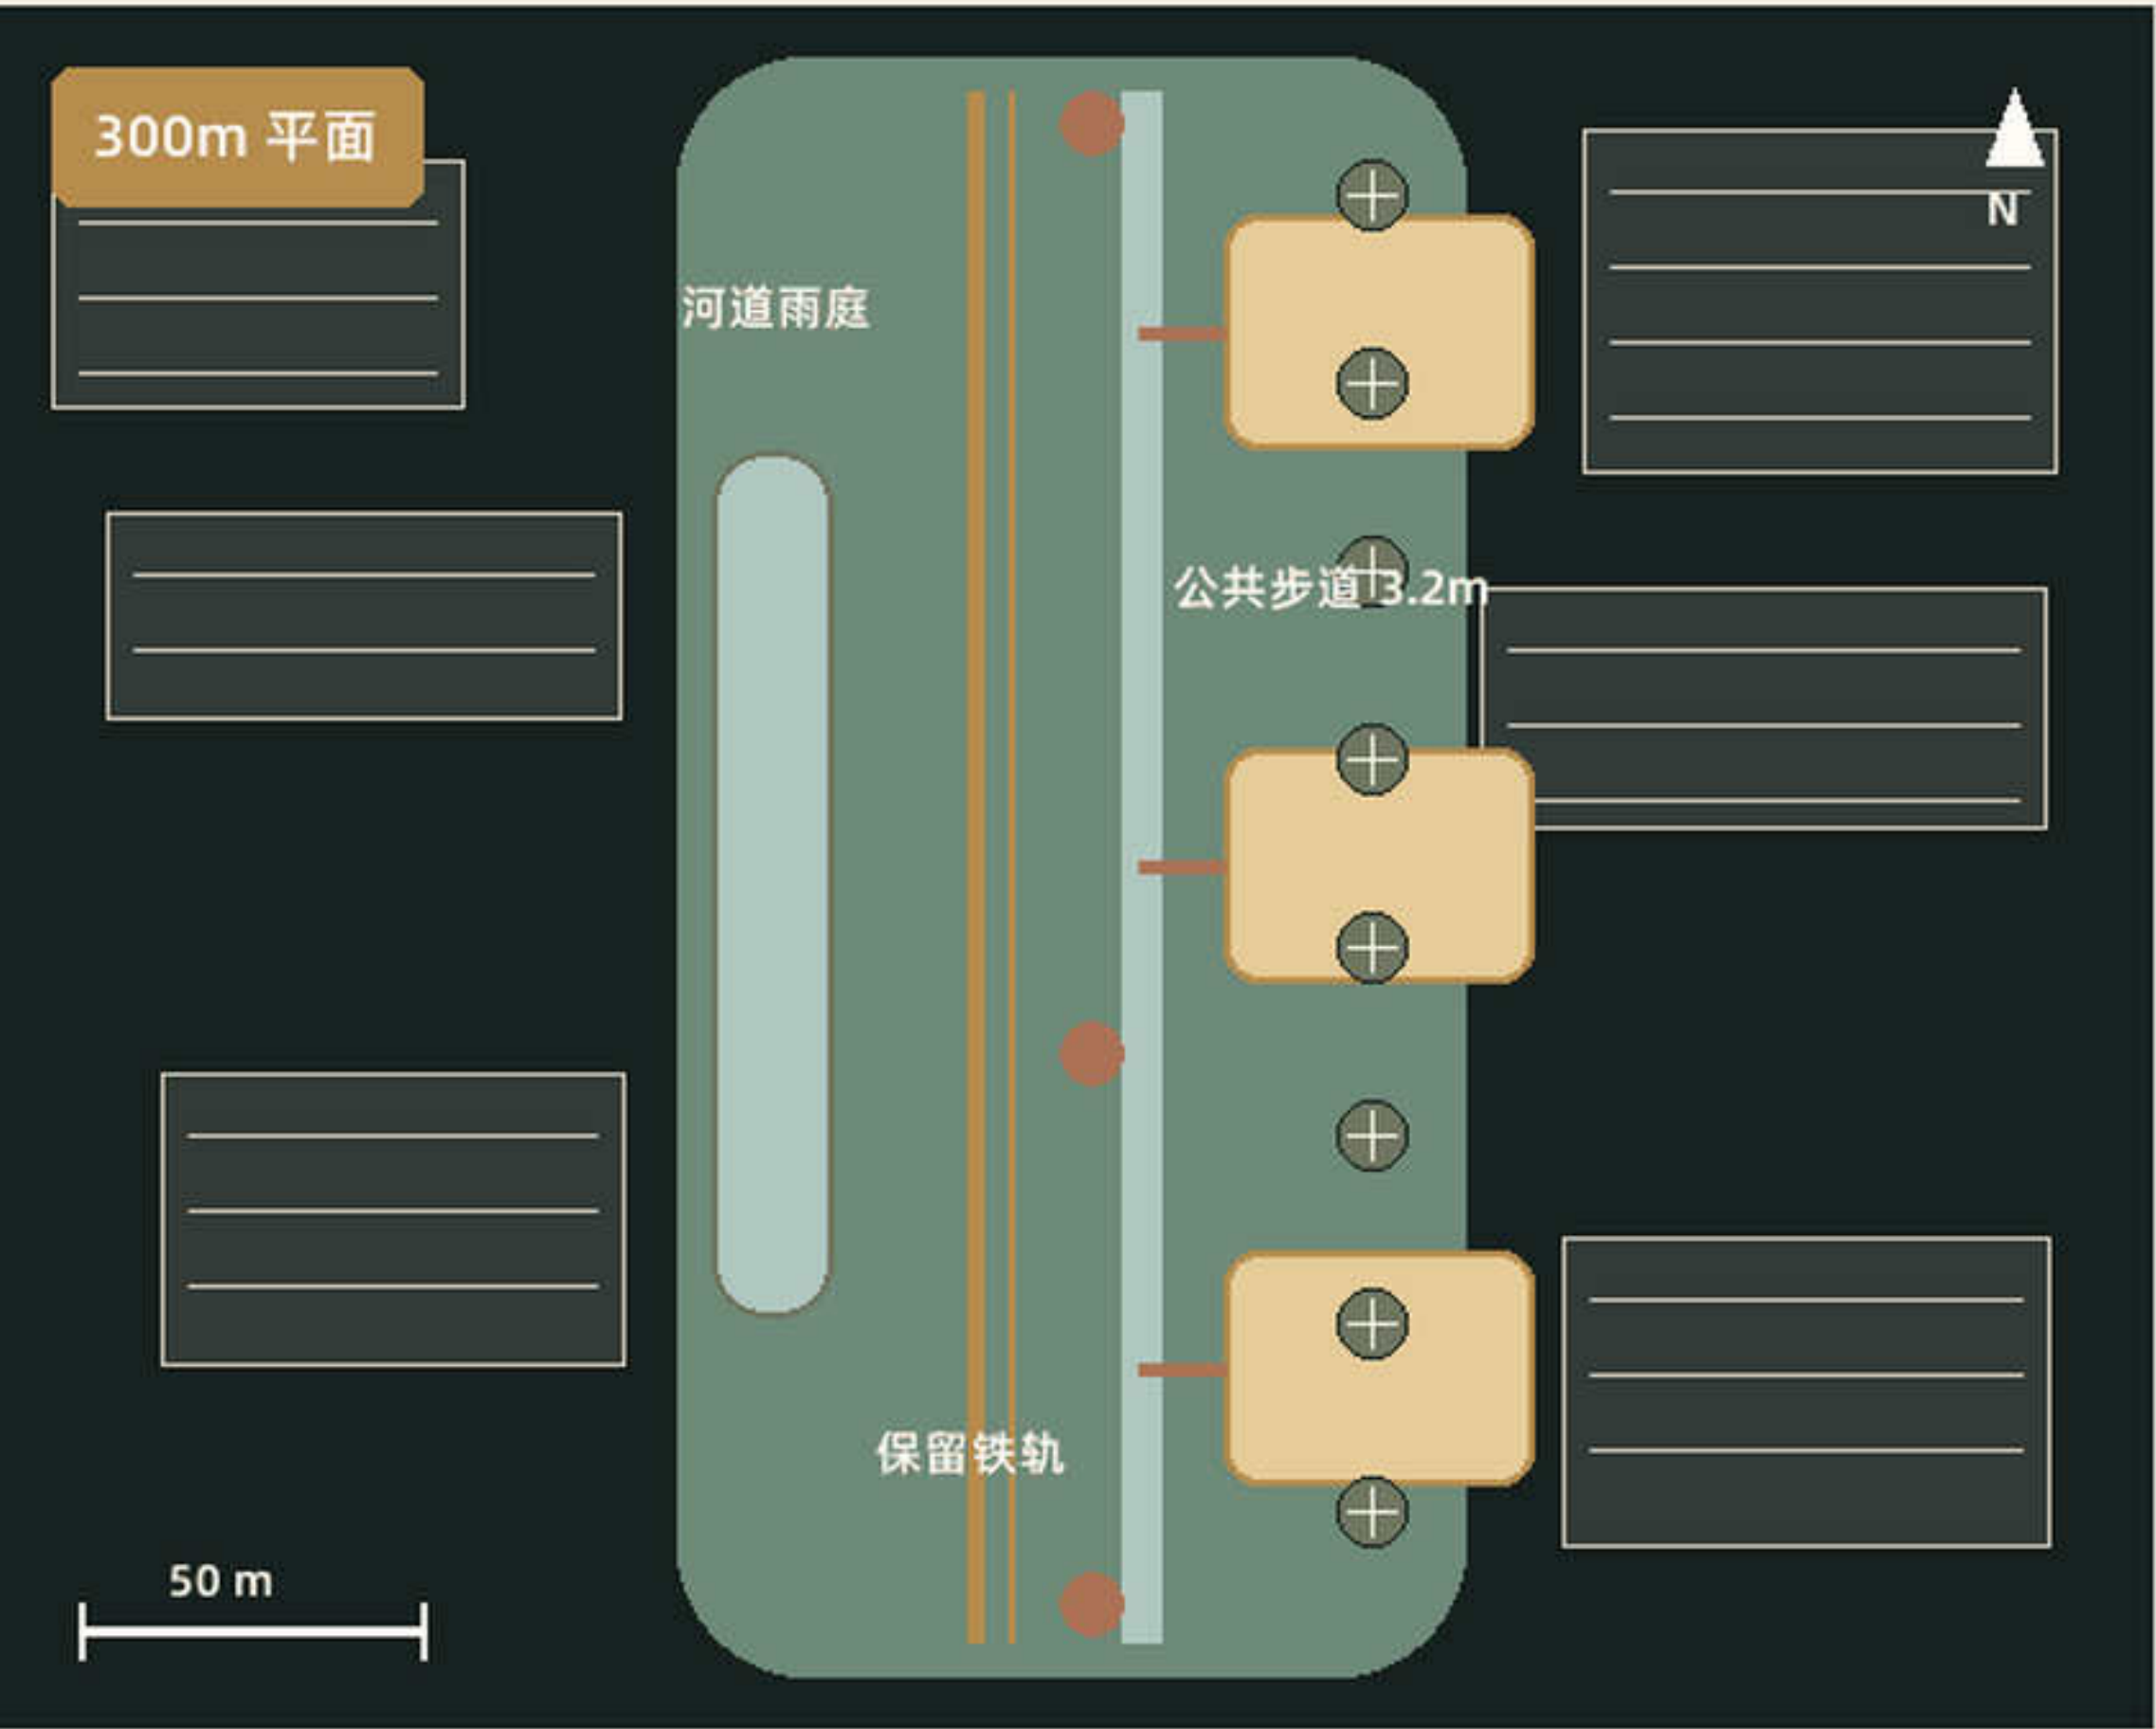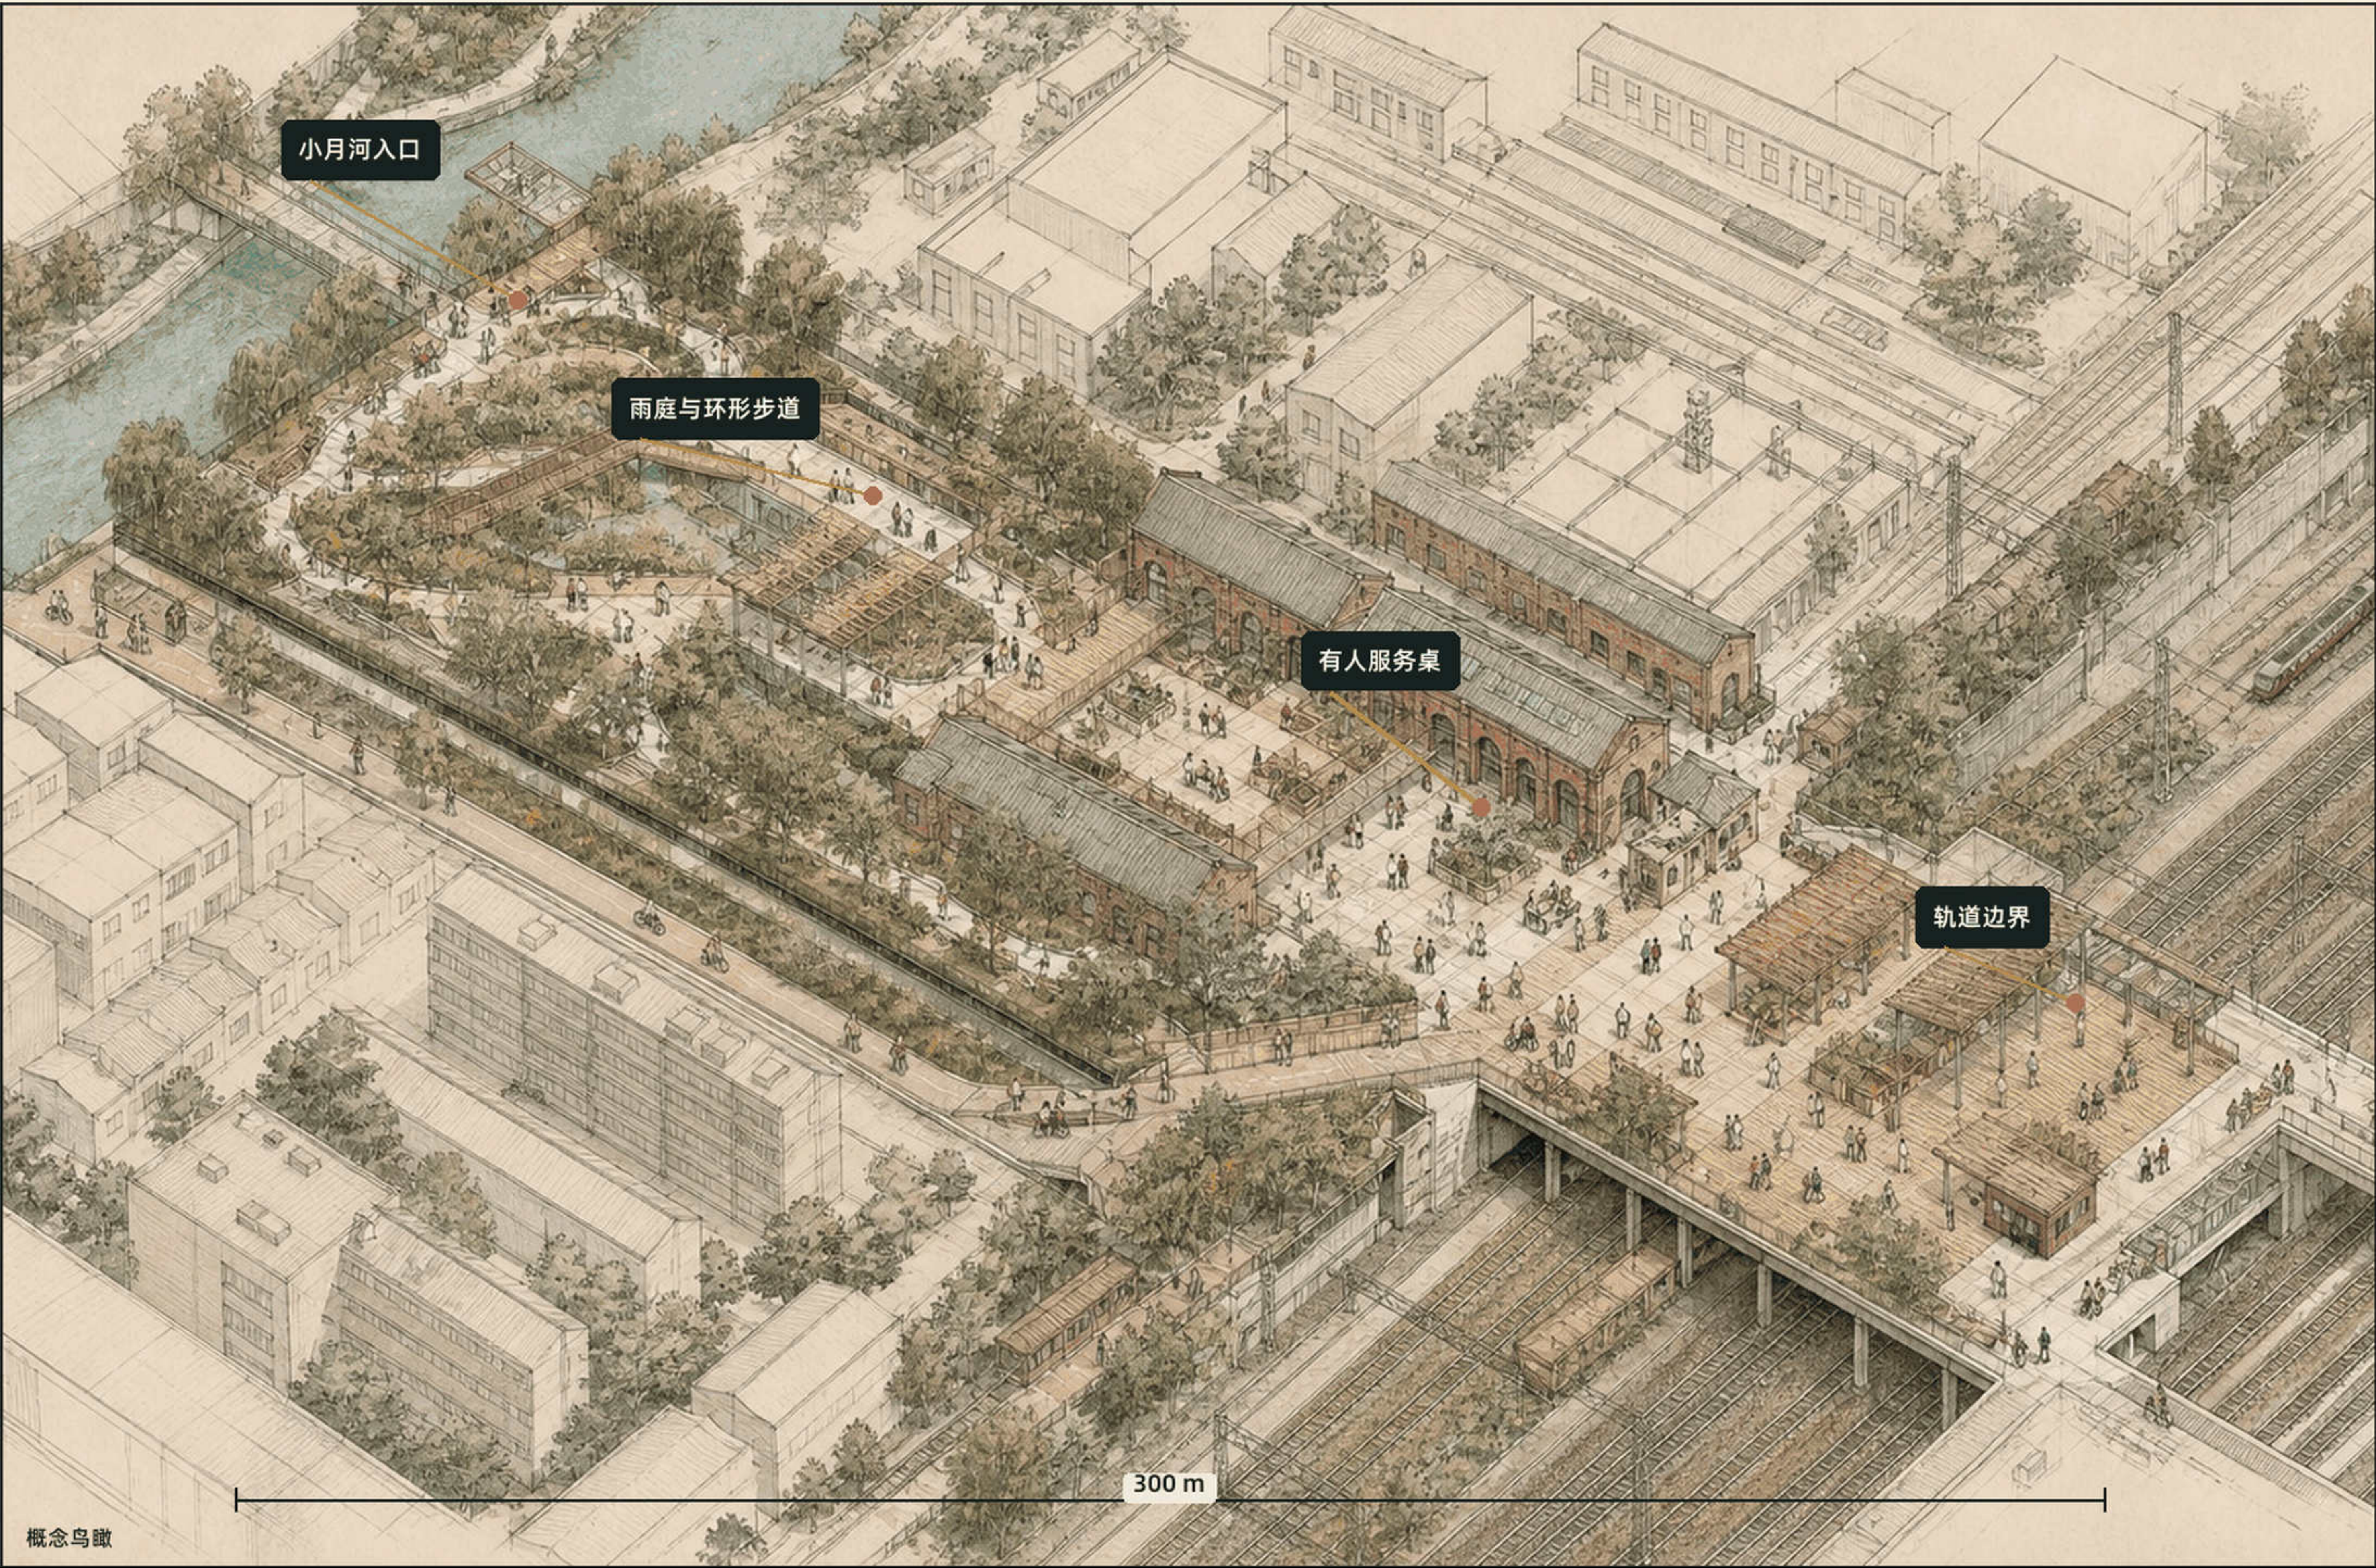

概念节点 | 施工前复核产权、管线与法定高程

OPEN-CITY-AI / HAIDIAN

公共前门
入口、坡道、服务桌首先面向日常使用者。

服务后场
设备库、维修和物流从独立门进出。

安静一边
靠住宅只留树荫、座椅与低亮度照明。

07

开源带的一天

四个时刻，四类使用者，都有人兜底

07:35

小月河入口

通勤者



路线

六道口 → 河边入口 → 学知园

人工兜底


积水时，保洁开排口并手动分流

● 看得到：入口不断行

12:10

AI 原点

老人

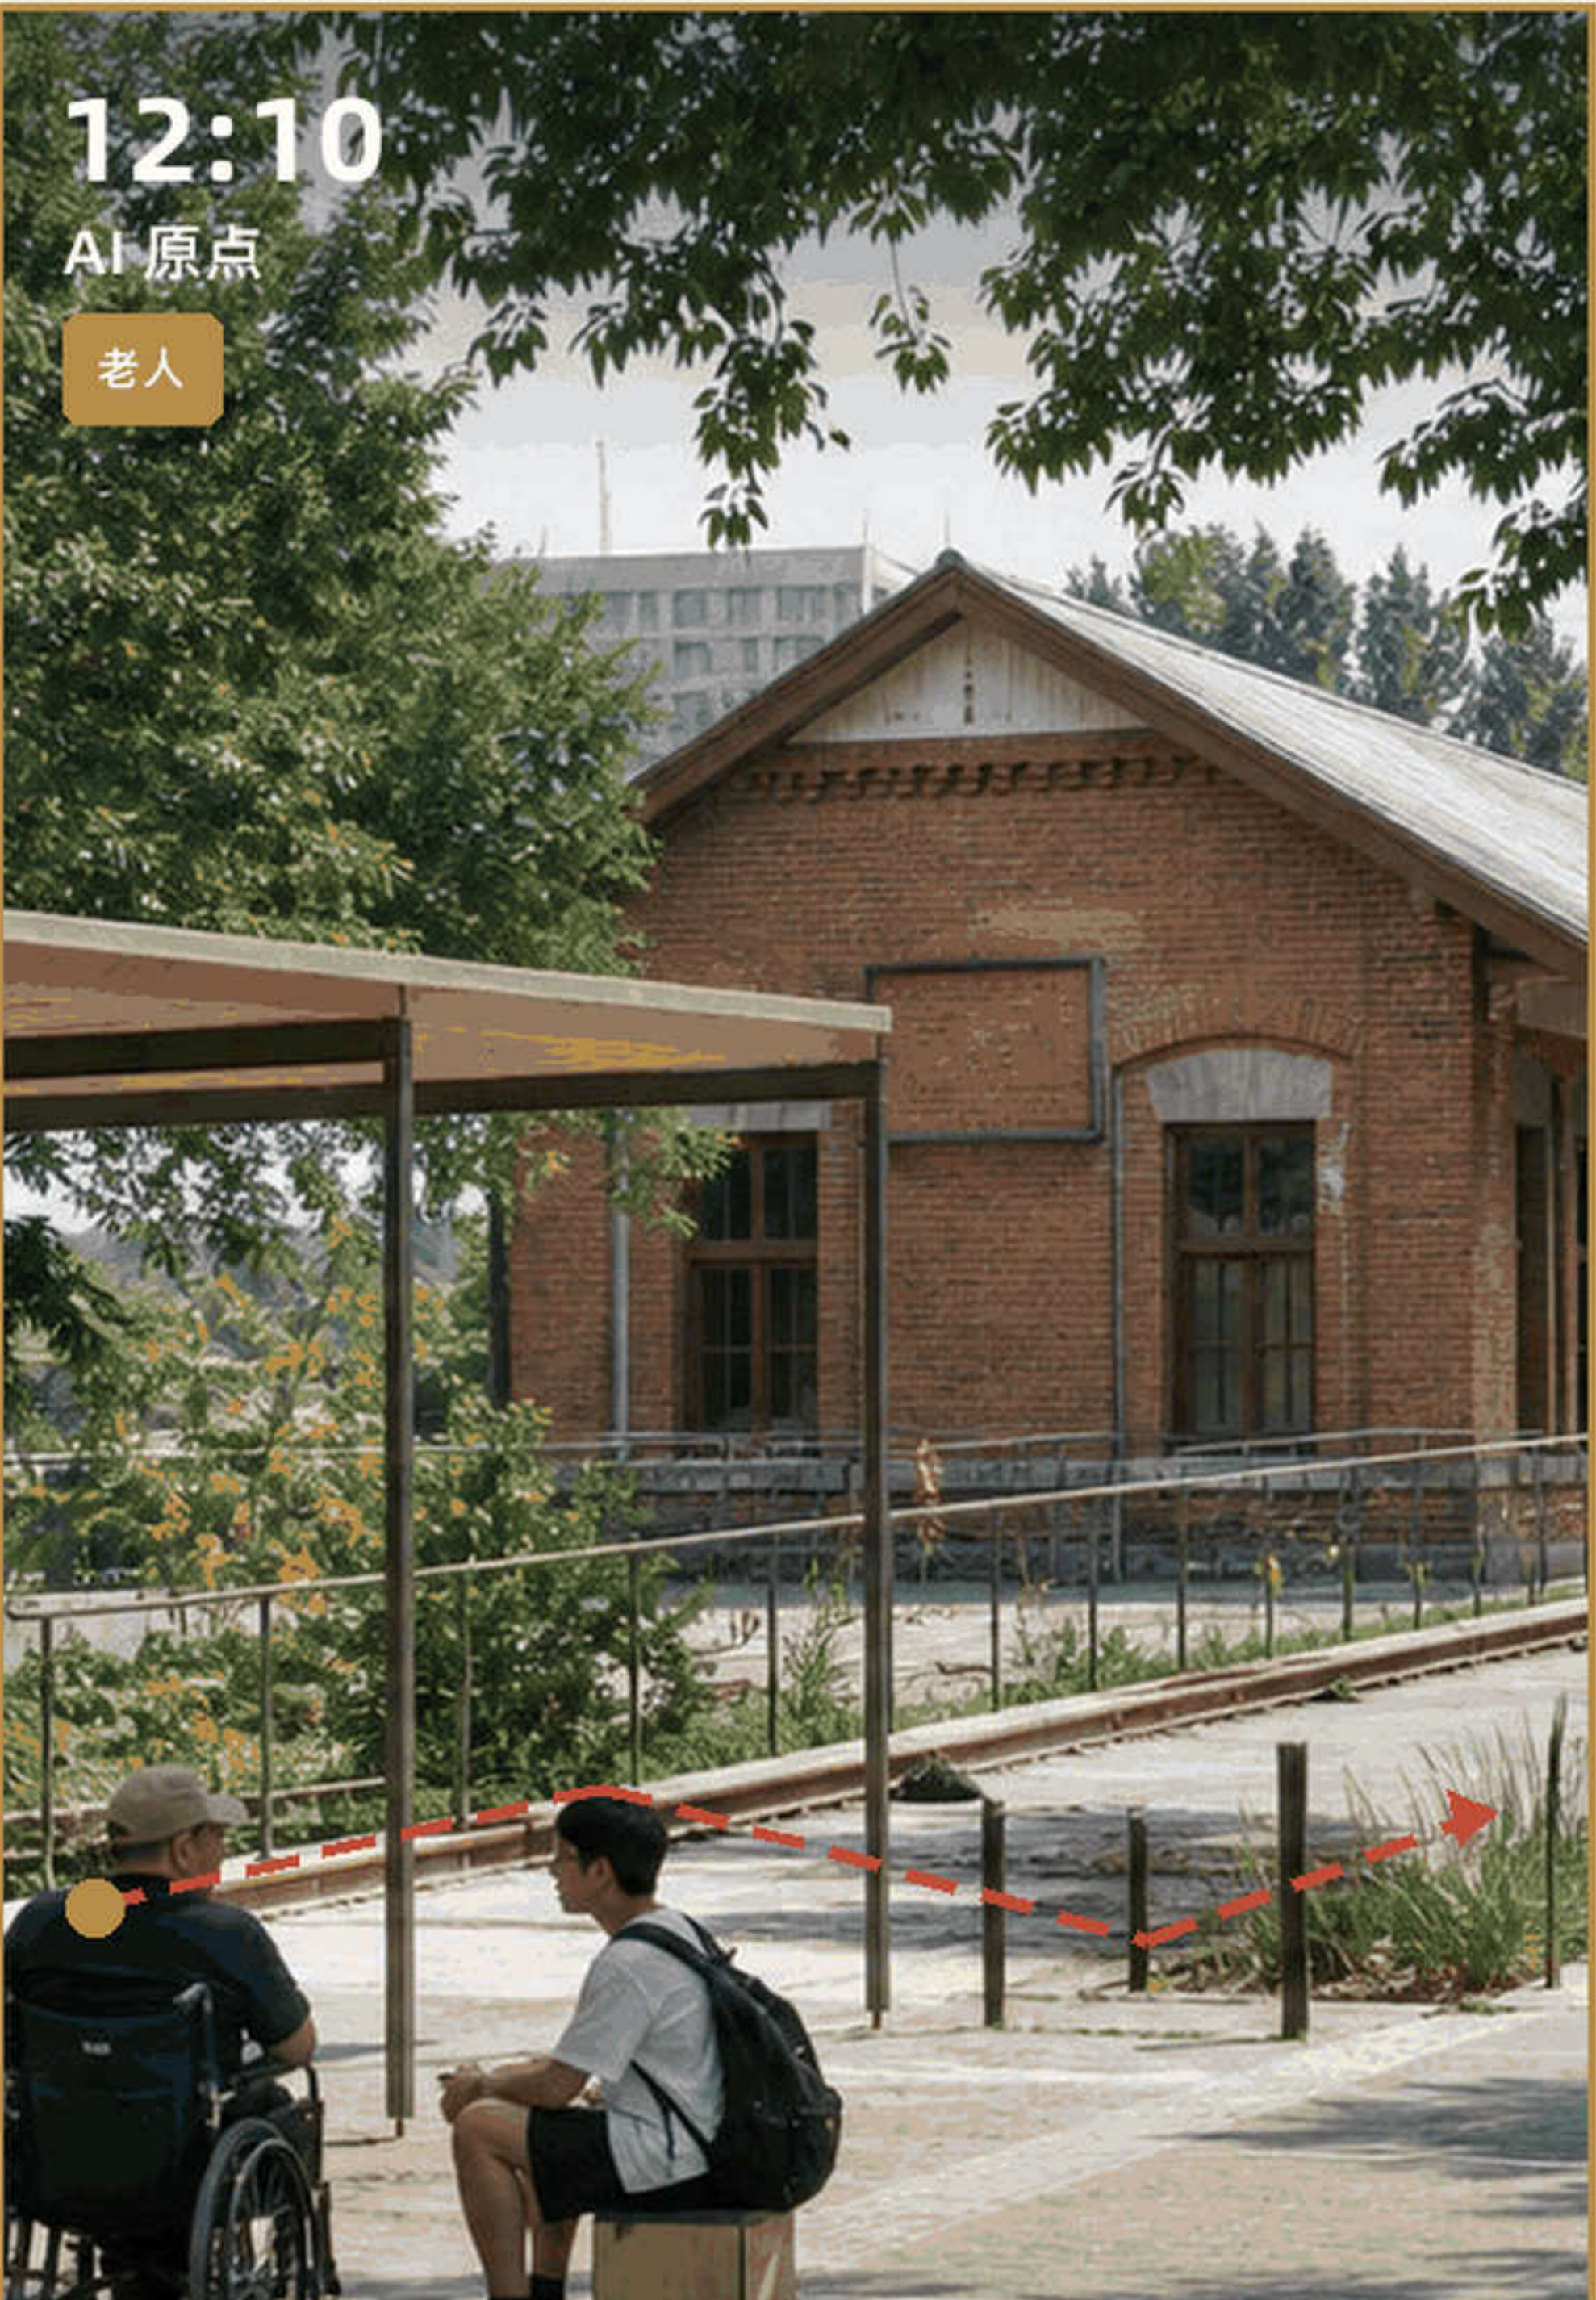

路线

林荫步道 → 服务桌 → 安静候区

人工兜底


不会扫码，值守员当场办

● 看得到：轮椅能并排停靠

16:35

众智园

亲子

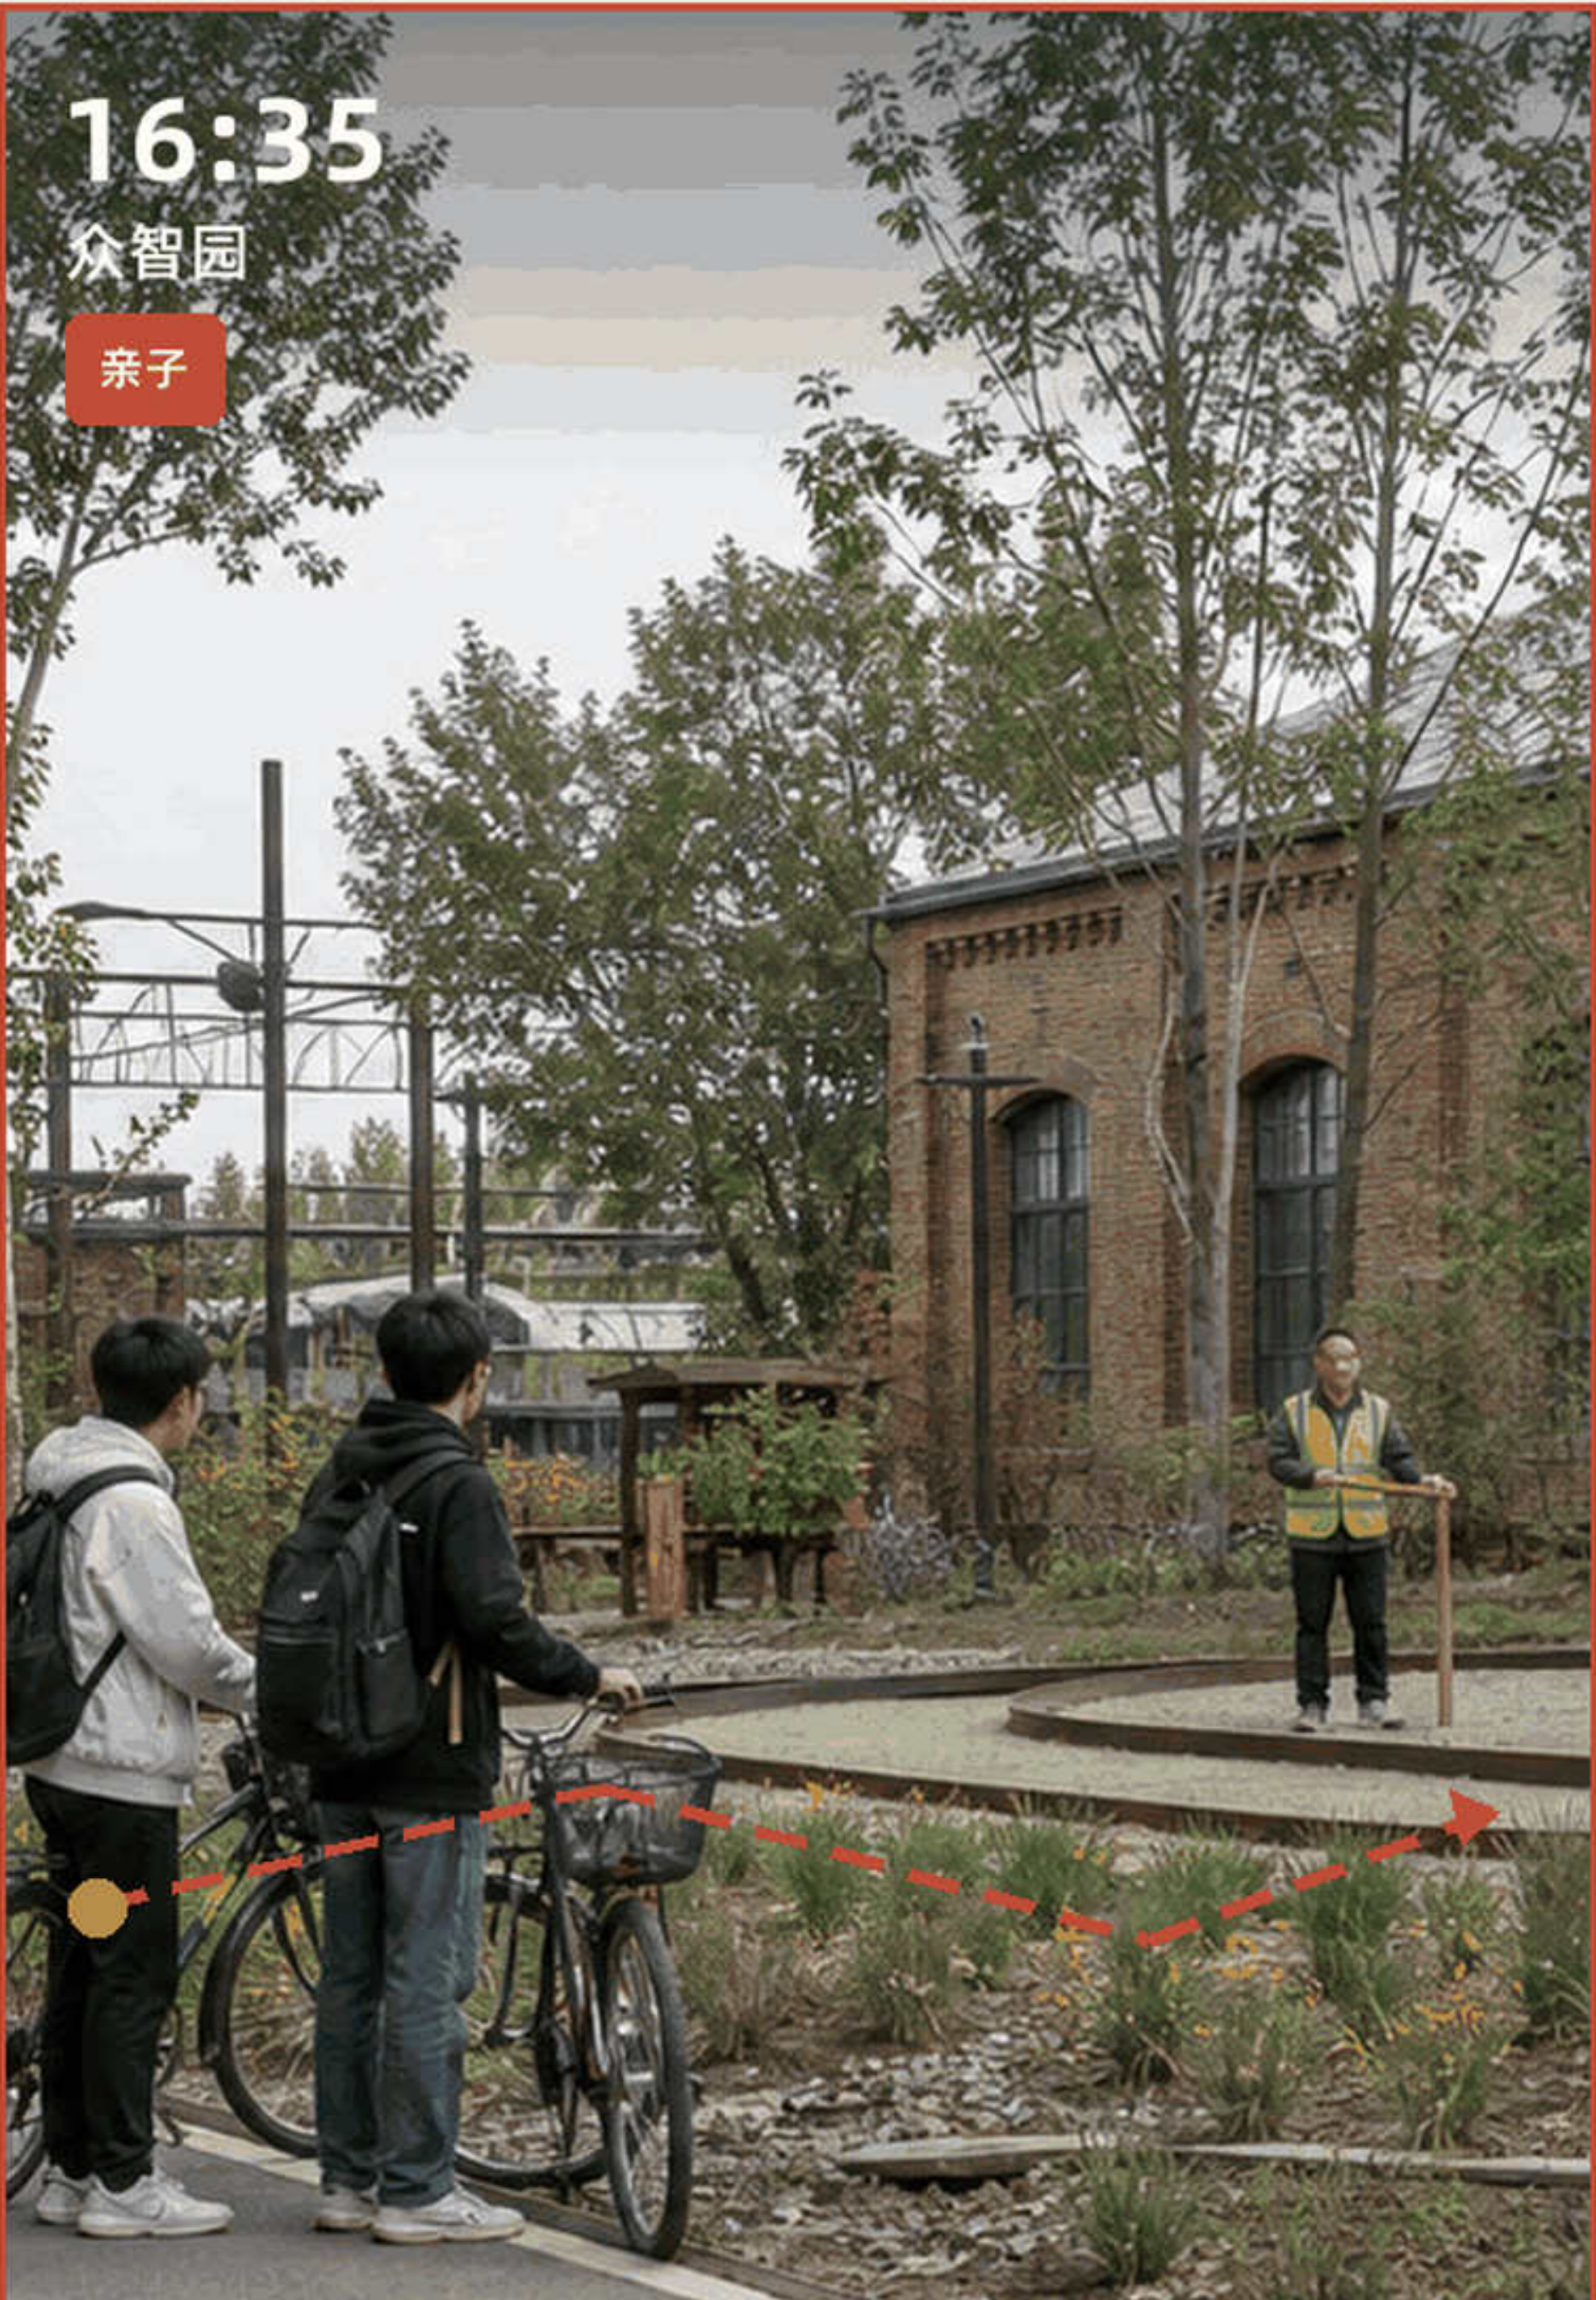

路线

校门 → 试验环 → 雨庭

人工兜底

家长在缓冲带交接，管理员可停试

● 看得到：玩耍不占慢骑道

20:30

大钟寺

巡护员



路线

地铁口 → 广场 → 社区出口


人工兜底

绕行照明异常时，巡护员手动切换回路

● 看得到：暖光不直射住宅

场景检查 | 路线、值守和结果均可在现场复核


OPEN-CITY-AI / HAIDIAN

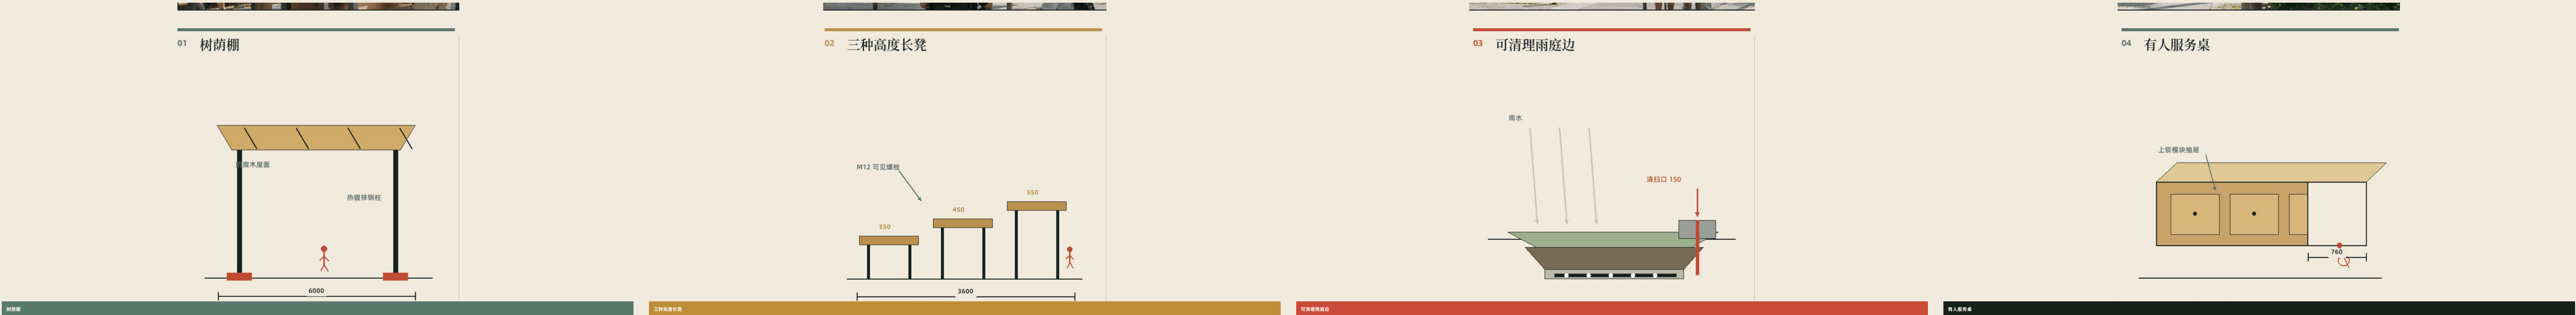

09 先把断点做成，再决定留下什么

同一张真实底图，三次叠加；公开工程、本案增量和审批条件始终分开

已建 在建 本案建议 需审批

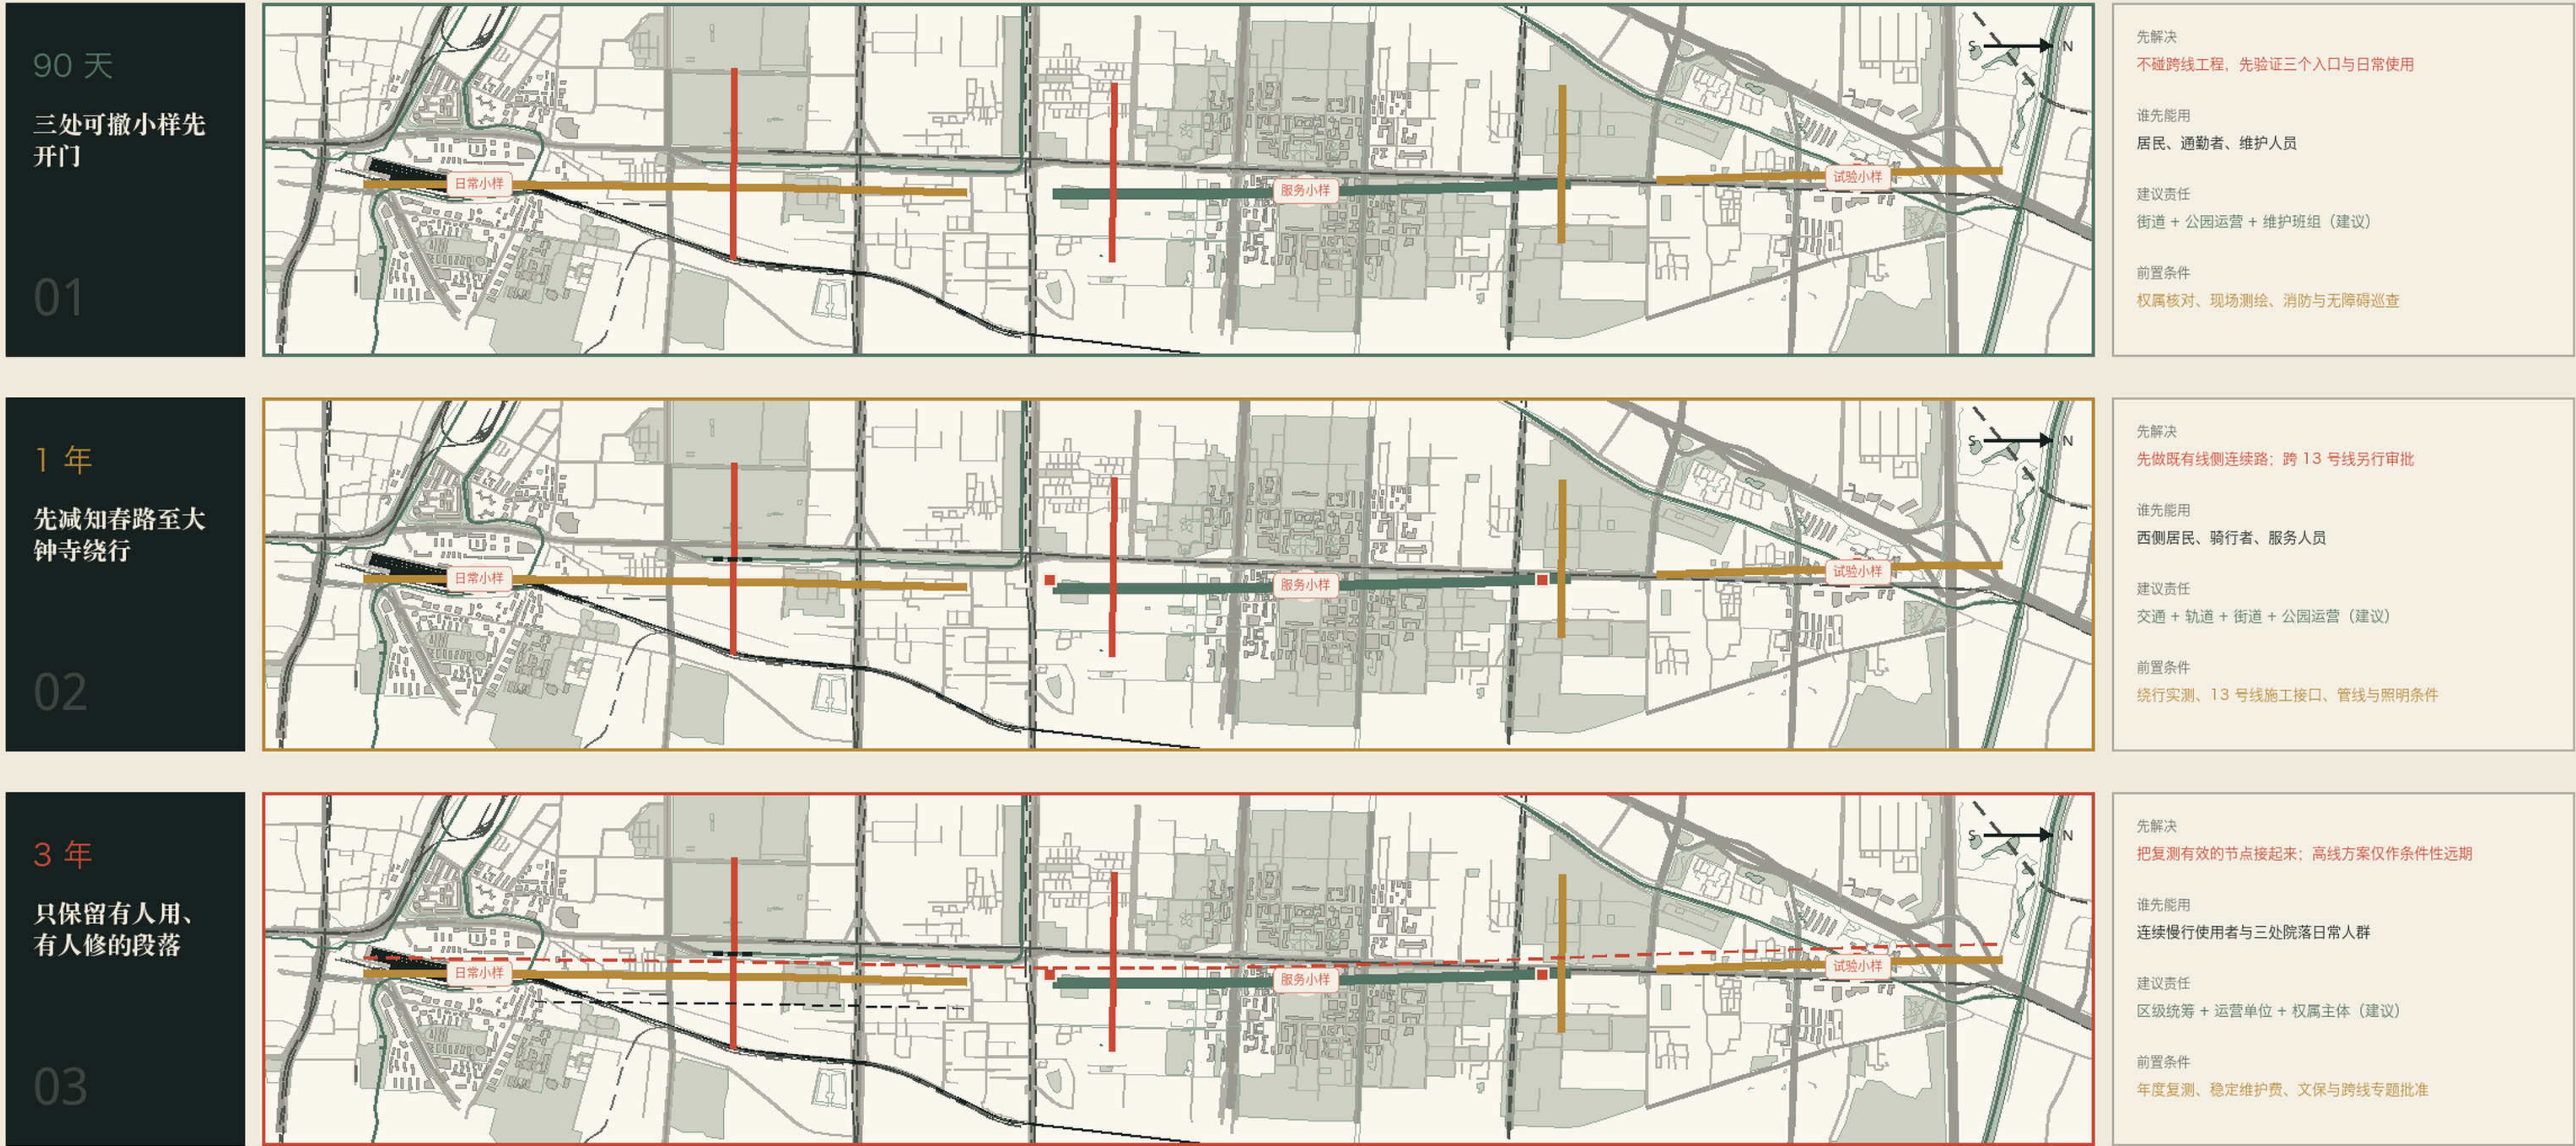

红色只表示本案新增；黑色虚线表示仍需文保、轨道或跨线审批。

OSM 仅作现状底图 | 概念边界须以测绘、权属与审批复核

EVIDENCE-GATED SEQUENCE | NOT A COMMITTED CONSTRUCTION SCHEDULE

90 天
三院落小样、入口计数、冲突位置与维修记录。


1 年
只修现场量得清的过街、雨庭和阅读点。

3 年
复测通行、树荫与维修，再决定什么留下。

09

开放前，先走一遍

知春路—大钟寺段，四项服务验收落到真实街区

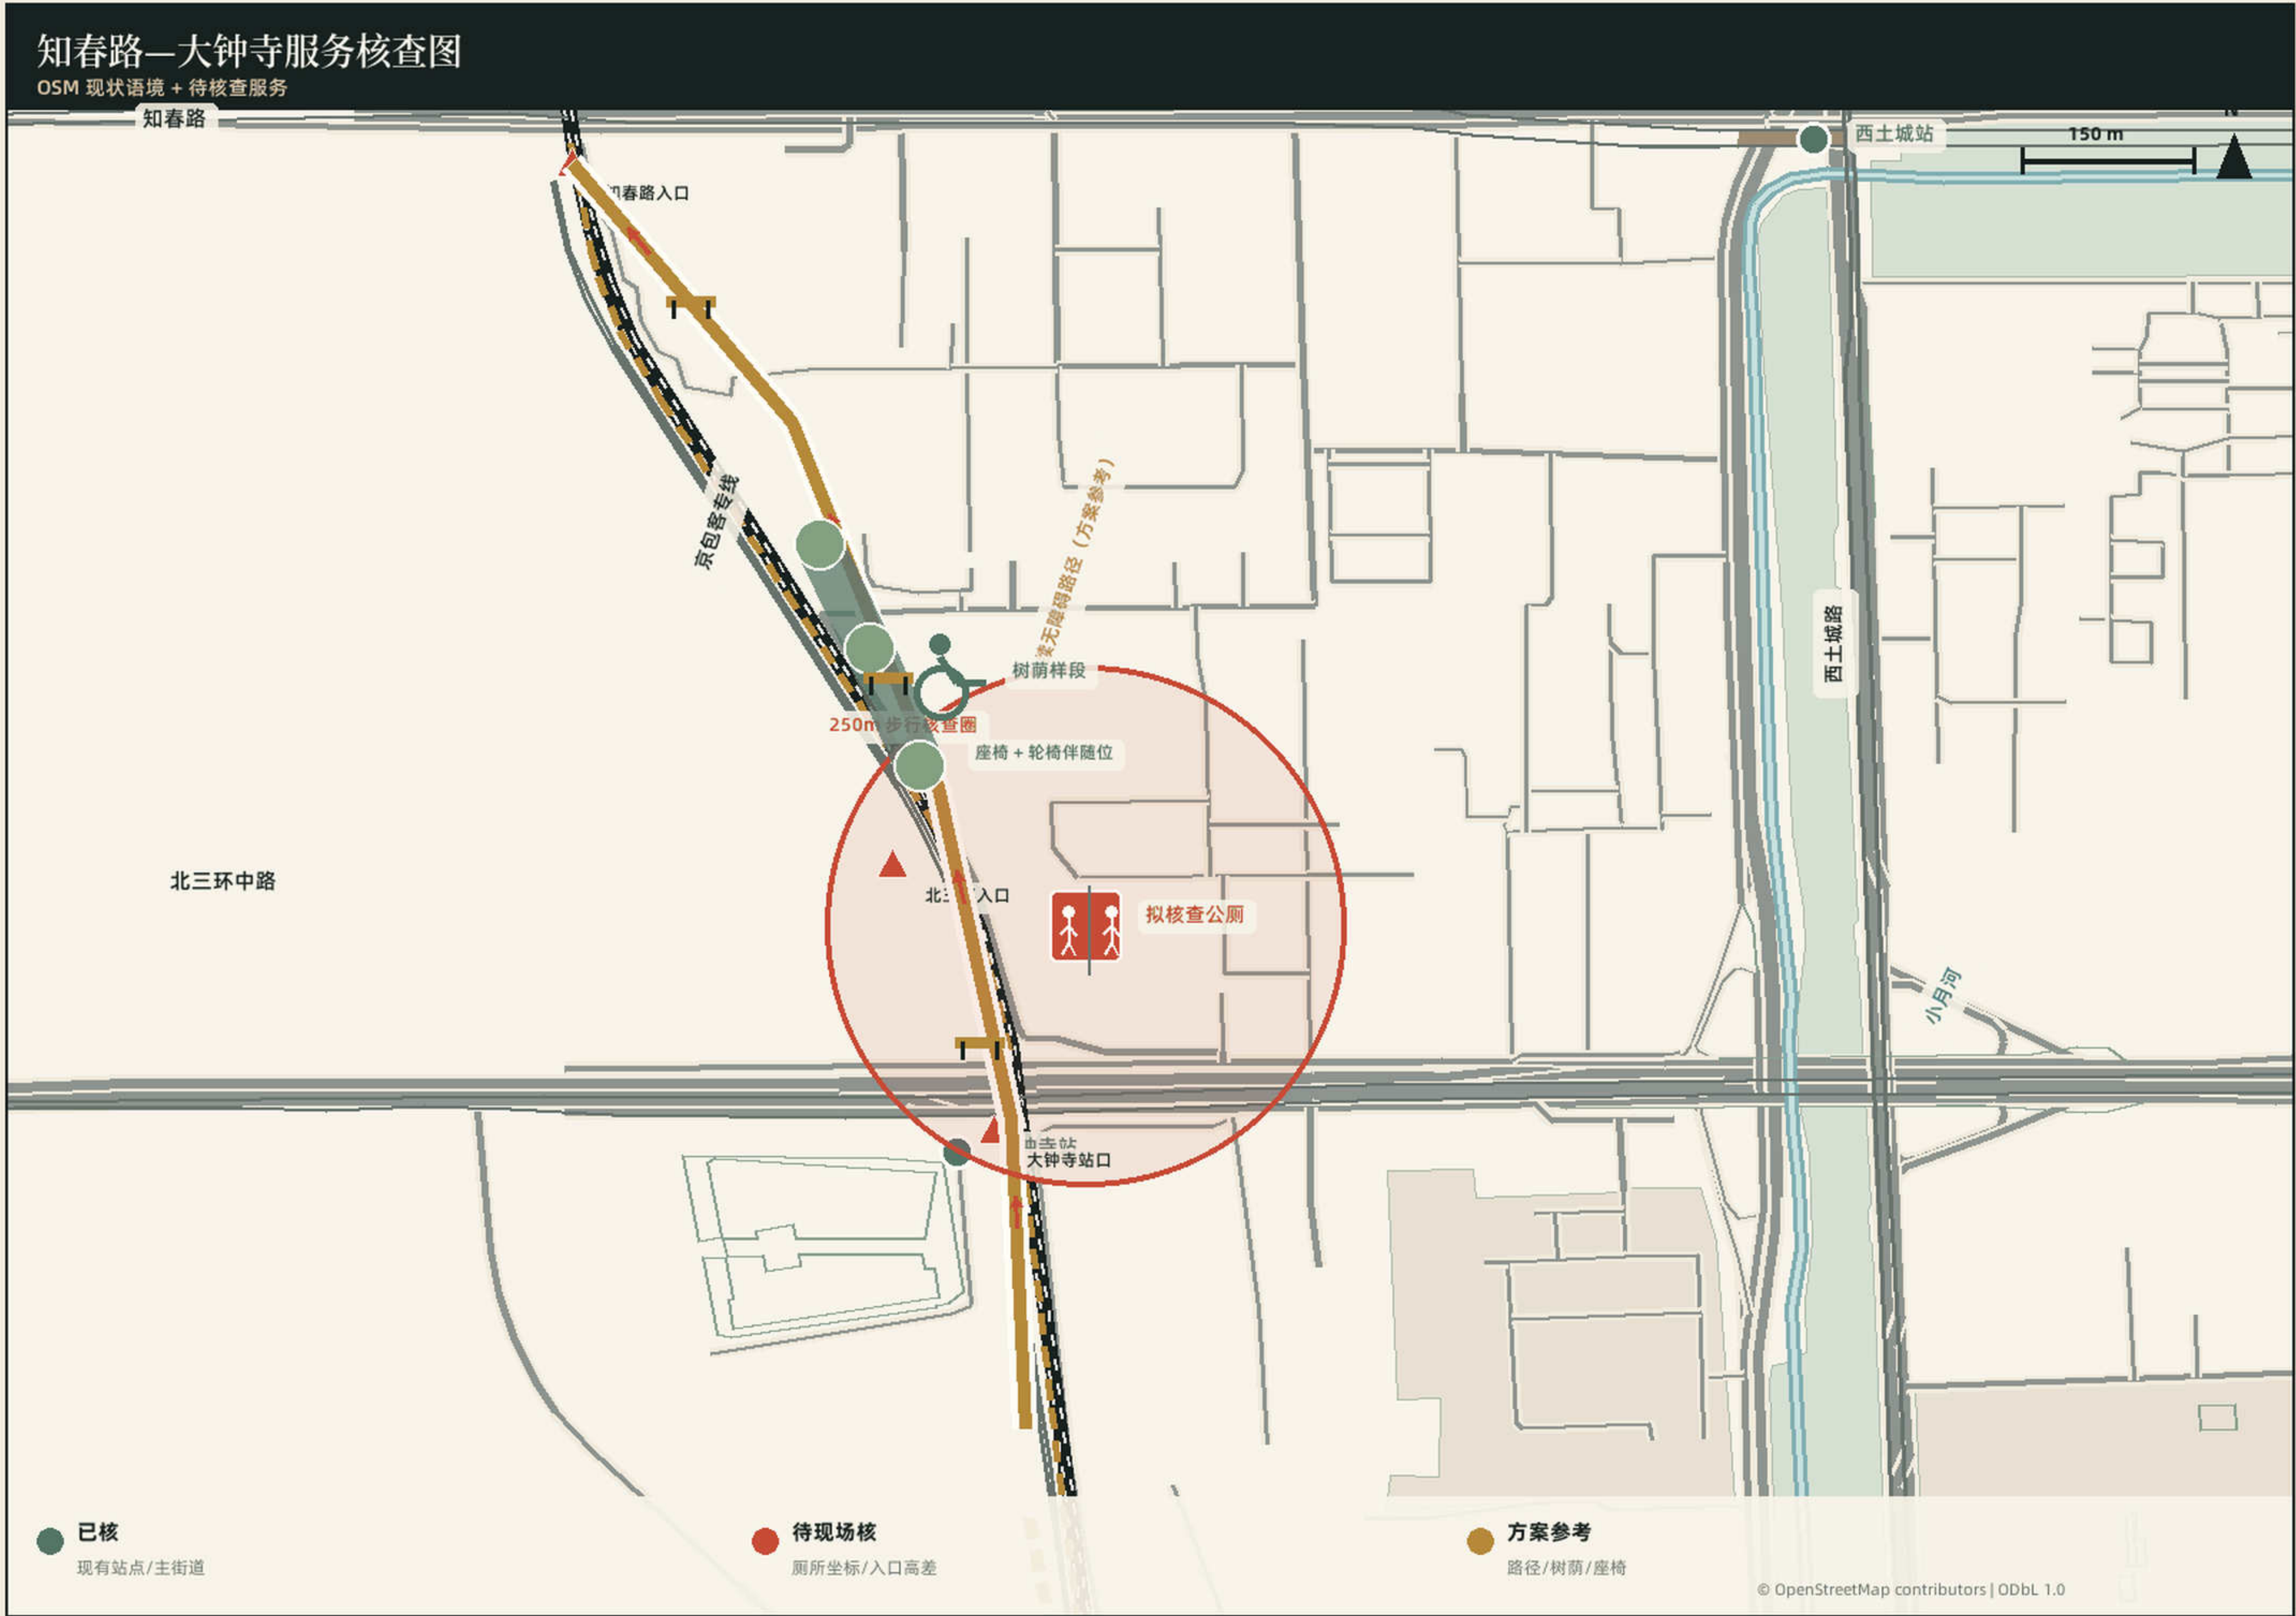

0台阶

连续无障碍路径

站口、北三环与知春路入口逐点复核



≤250m

步行到公厕

GB 51192-2016宜≤250m，坐标与实
走路径待核



>80%*

主次园路林荫覆盖

北京绿隔公园指导参考目标，非强制法定值



20% ~ 30%


座椅容量 / 轮椅位≥10%

轮椅位紧邻靠背、扶手座椅，保留照护视线

公开地图只核语境，高差、厕所和服务仍须现场核验

公众服务审计 | 知春路—大钟寺段

OPEN-CITY-AI / HAI DIAN

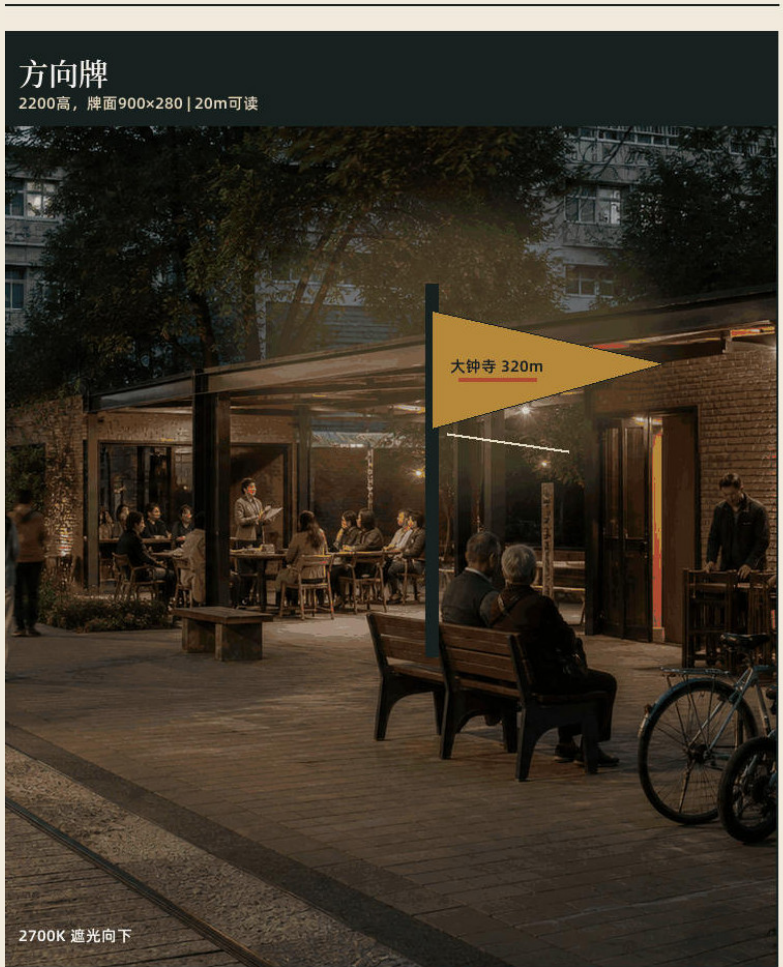

资料边界

- 官方事实
保持发布时间与原口径
- 工作值
OSM + GeoJSON，可重算
- 案例
只支持方法，不证明原张现场