

FIG 01 / SITE OVERVIEW

总体结构 | 公共脊串联三核，两翼回路织补城市

主叙事：从封闭园区转向连续公共创新网络

空间主张

1 条公共脊

遗址公园 × 慢行 × 开放场景

3 个差异化核

验证 / 转化 / 城市服务

2 条服务回路

东翼场景赋能 / 西翼科技服务


6 项更新项目

以资料闸门控制实施风险

临时边界只作低对比虚线；设计主角是公共脊、横向缝合、场景节点和项目关系。

图例 / LEGEND

- 公共脊
- 服务回路 / 联系线
- 公共场景节点
- 临时粗略边界

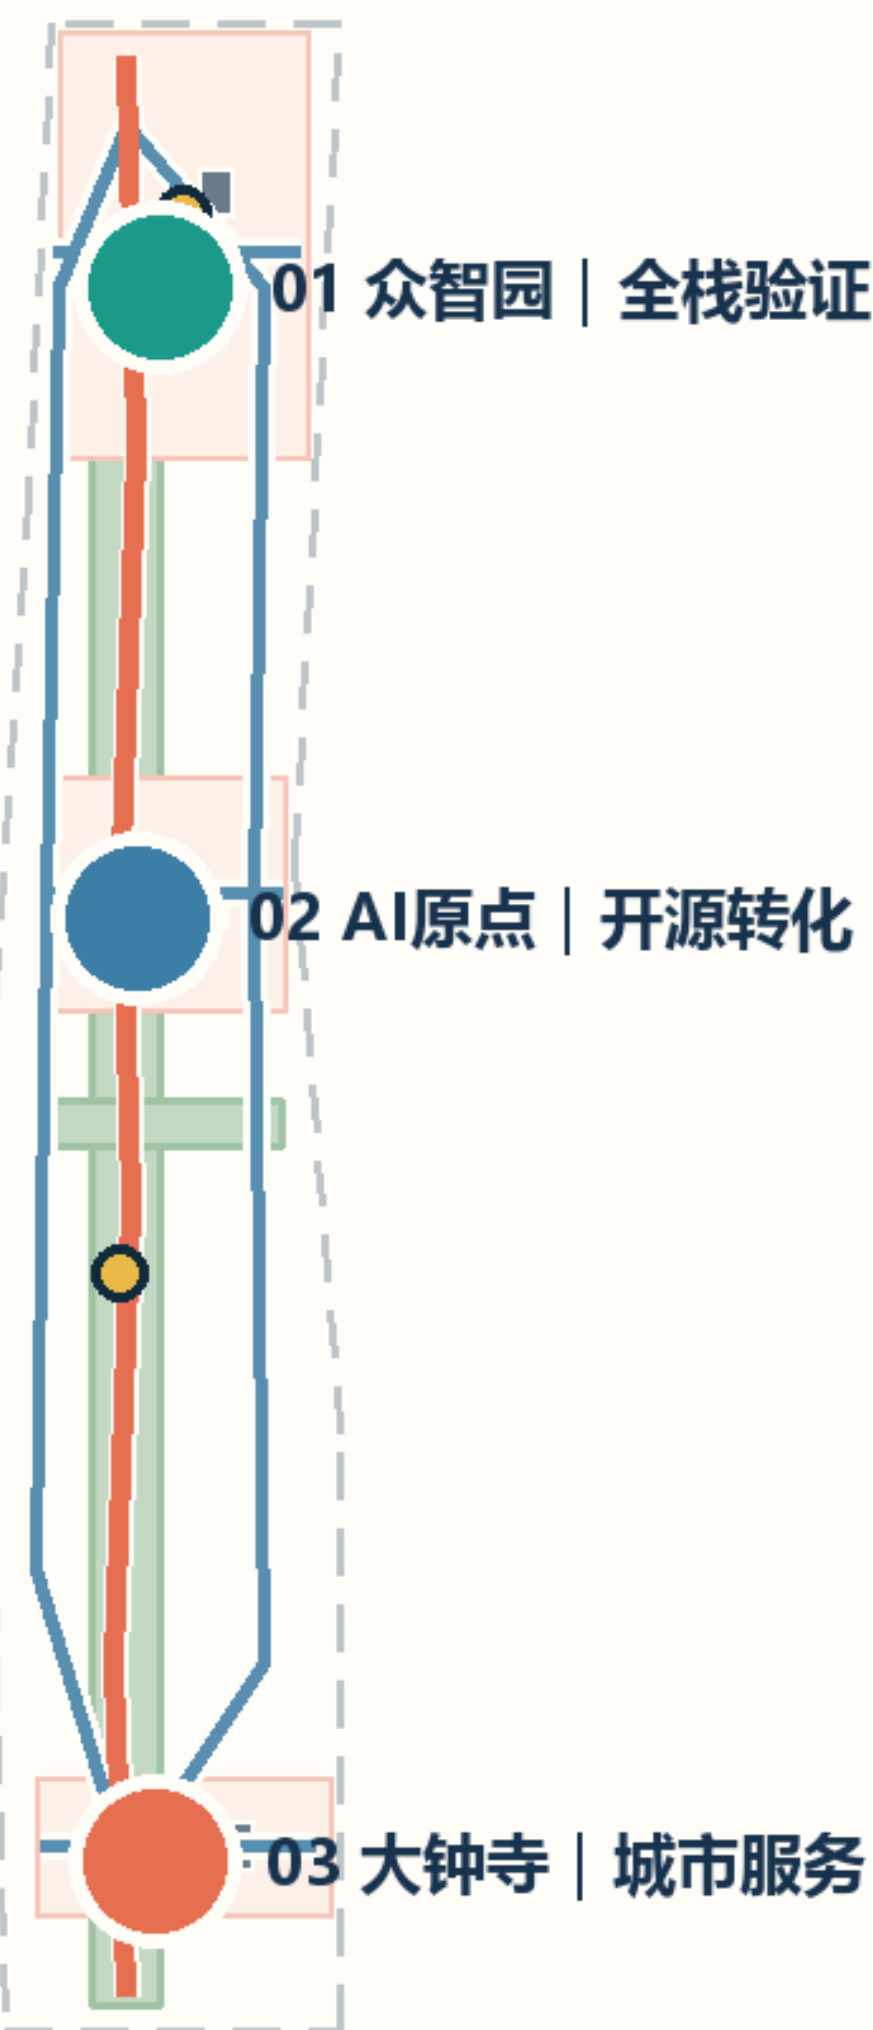


REVISION 2.0 / 2026-08 | 数据：本投稿 GeoJSON / metrics / 矩阵 | PROVISIONAL GEOMETRY，不作官方红线或精确面积依据

京张智脉

FIG 02 / LAND USE STRUCTURE

空间结构与用地 | 四类完整分区支撑一条创新链

主叙事：研究—验证—转化—服务—传播的空间邻接

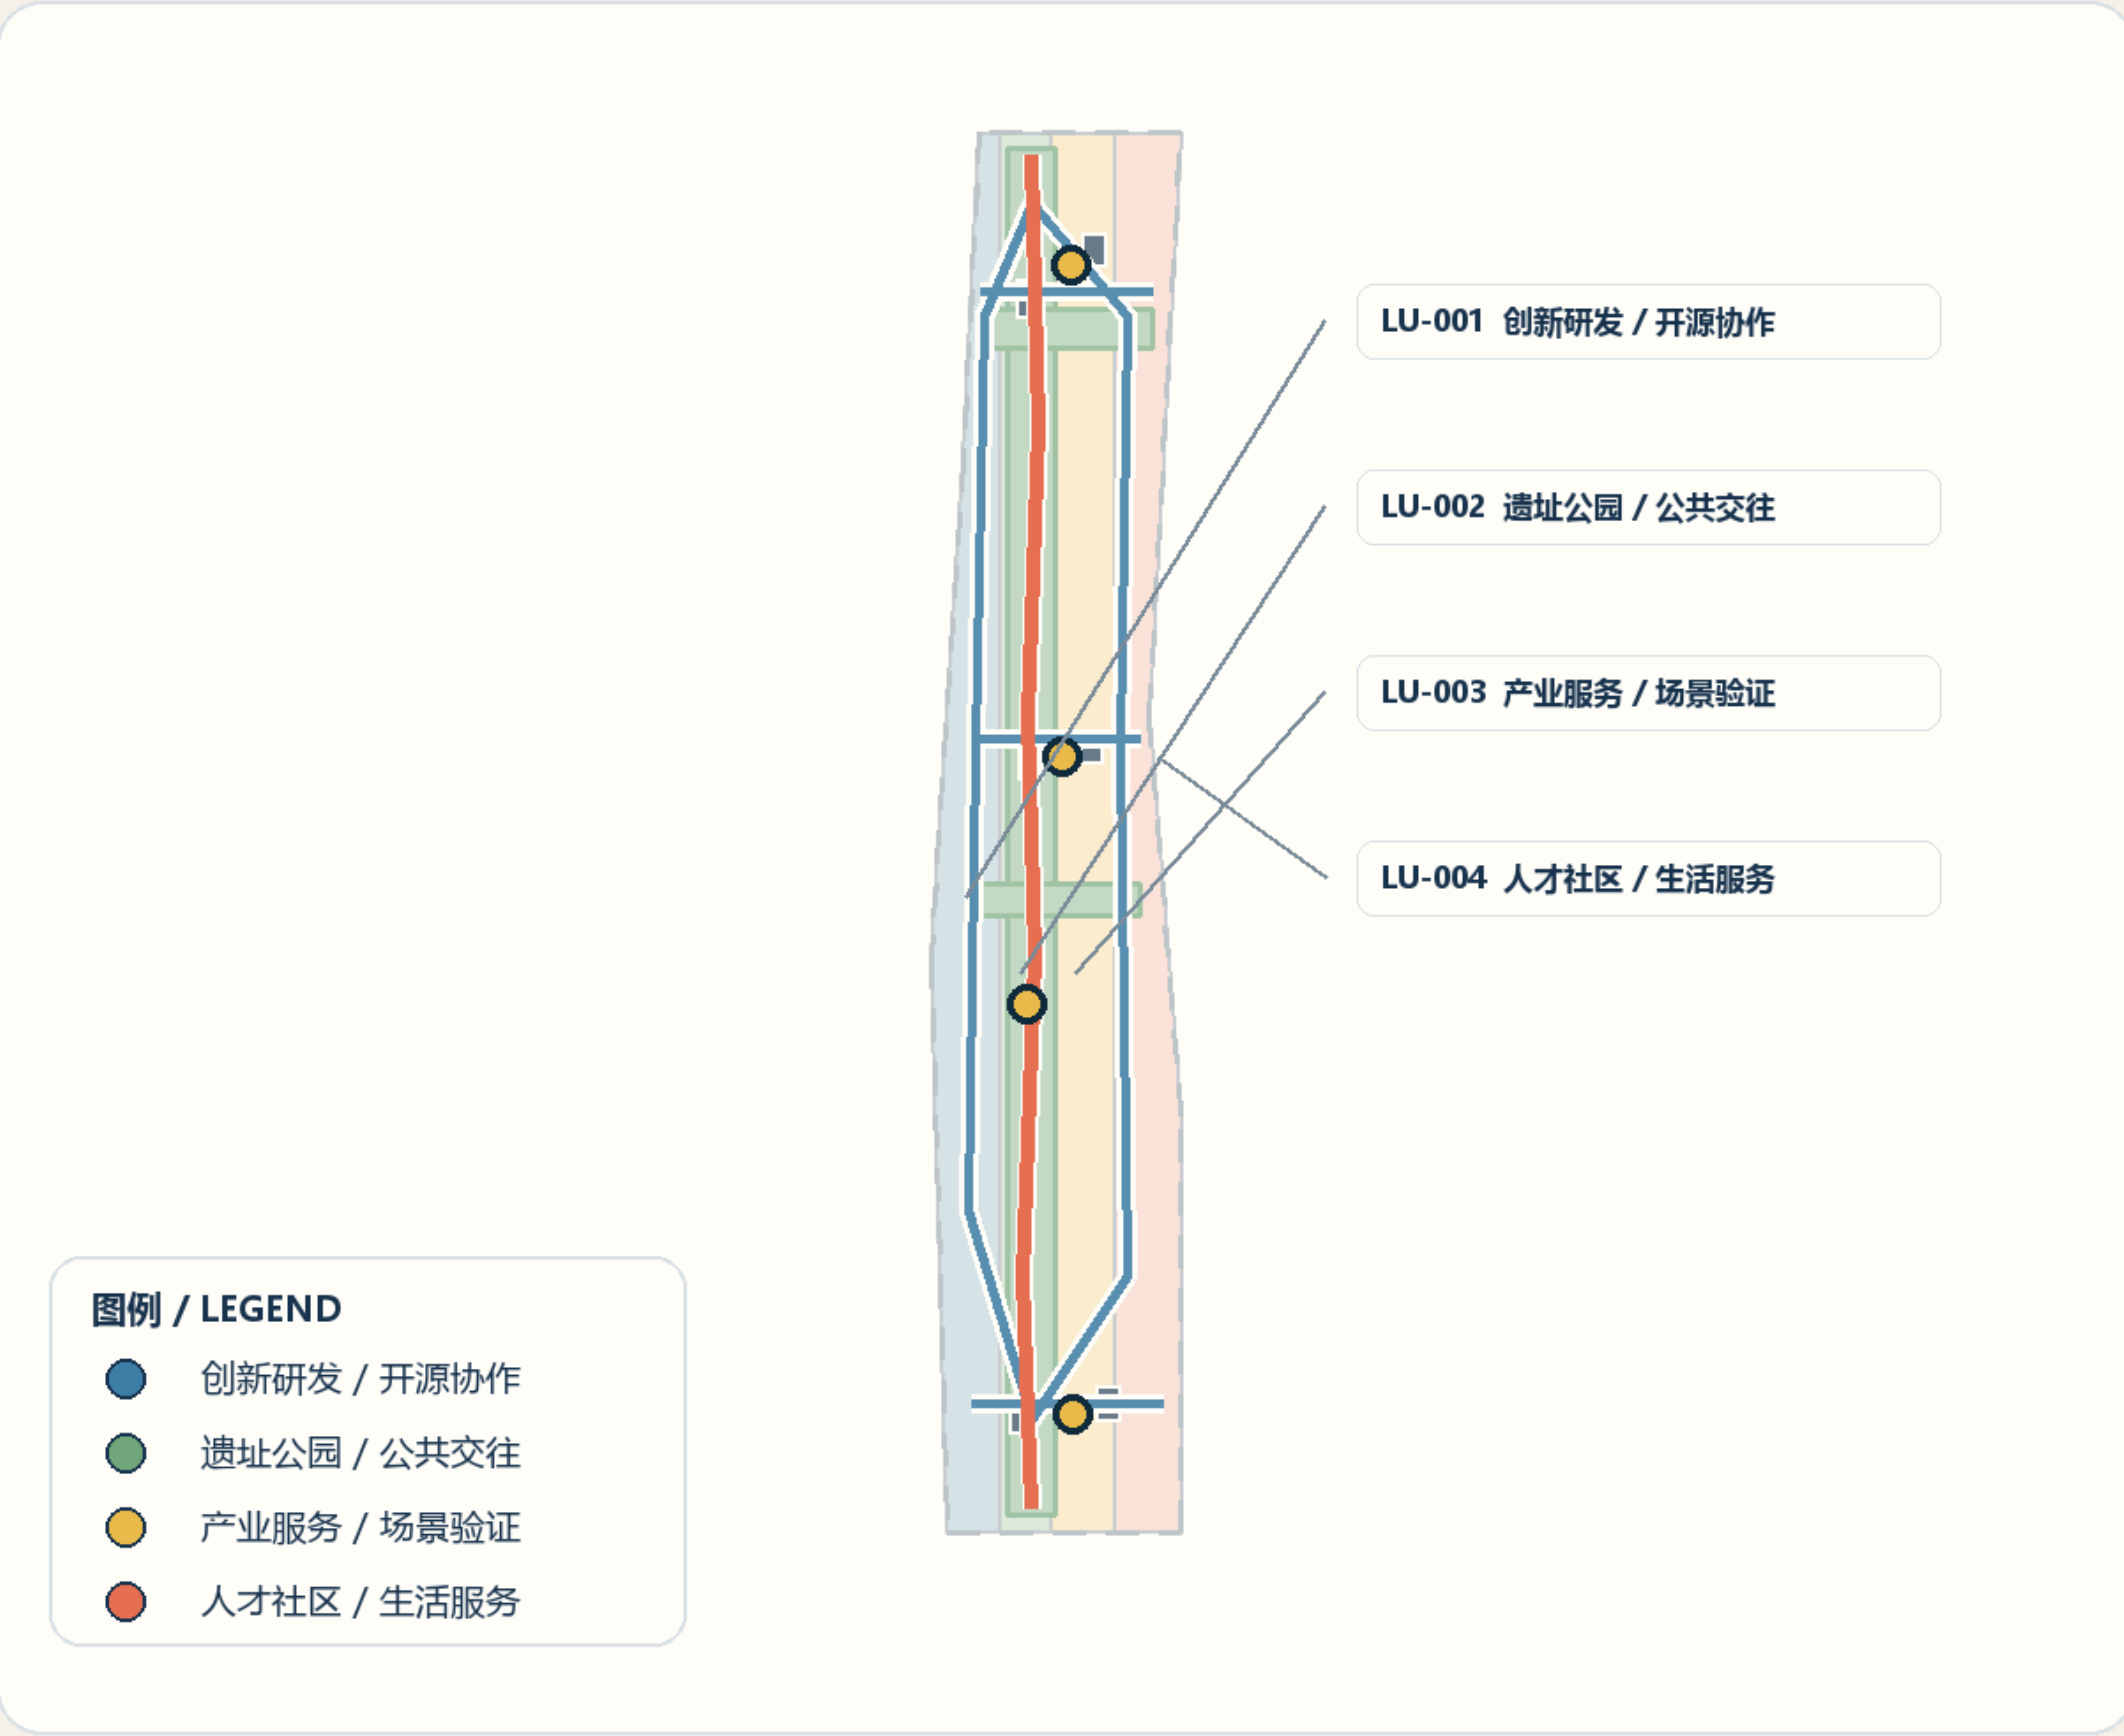

功能链不是面积配额

- 研究
- 验证
- 转化
- 服务
- 传播

四类用地使用共享边界完整覆盖提交范围；它们表达功能关系，不替代现状调查、法定用地或控规调整。


REVISION 2.0 / 2026-08 | 数据：本投稿 GeoJSON / metrics / 矩阵 | PROVISIONAL GEOMETRY，不作官方红线或精确面积依据

京张智脉

FIG 04 / MOBILITY + BLUEGREEN

慢行 × 蓝绿 × 公共空间 | 把出行网络变成公共创新界面

主叙事：一纵两横生态骨架与三横两翼慢行网络融合

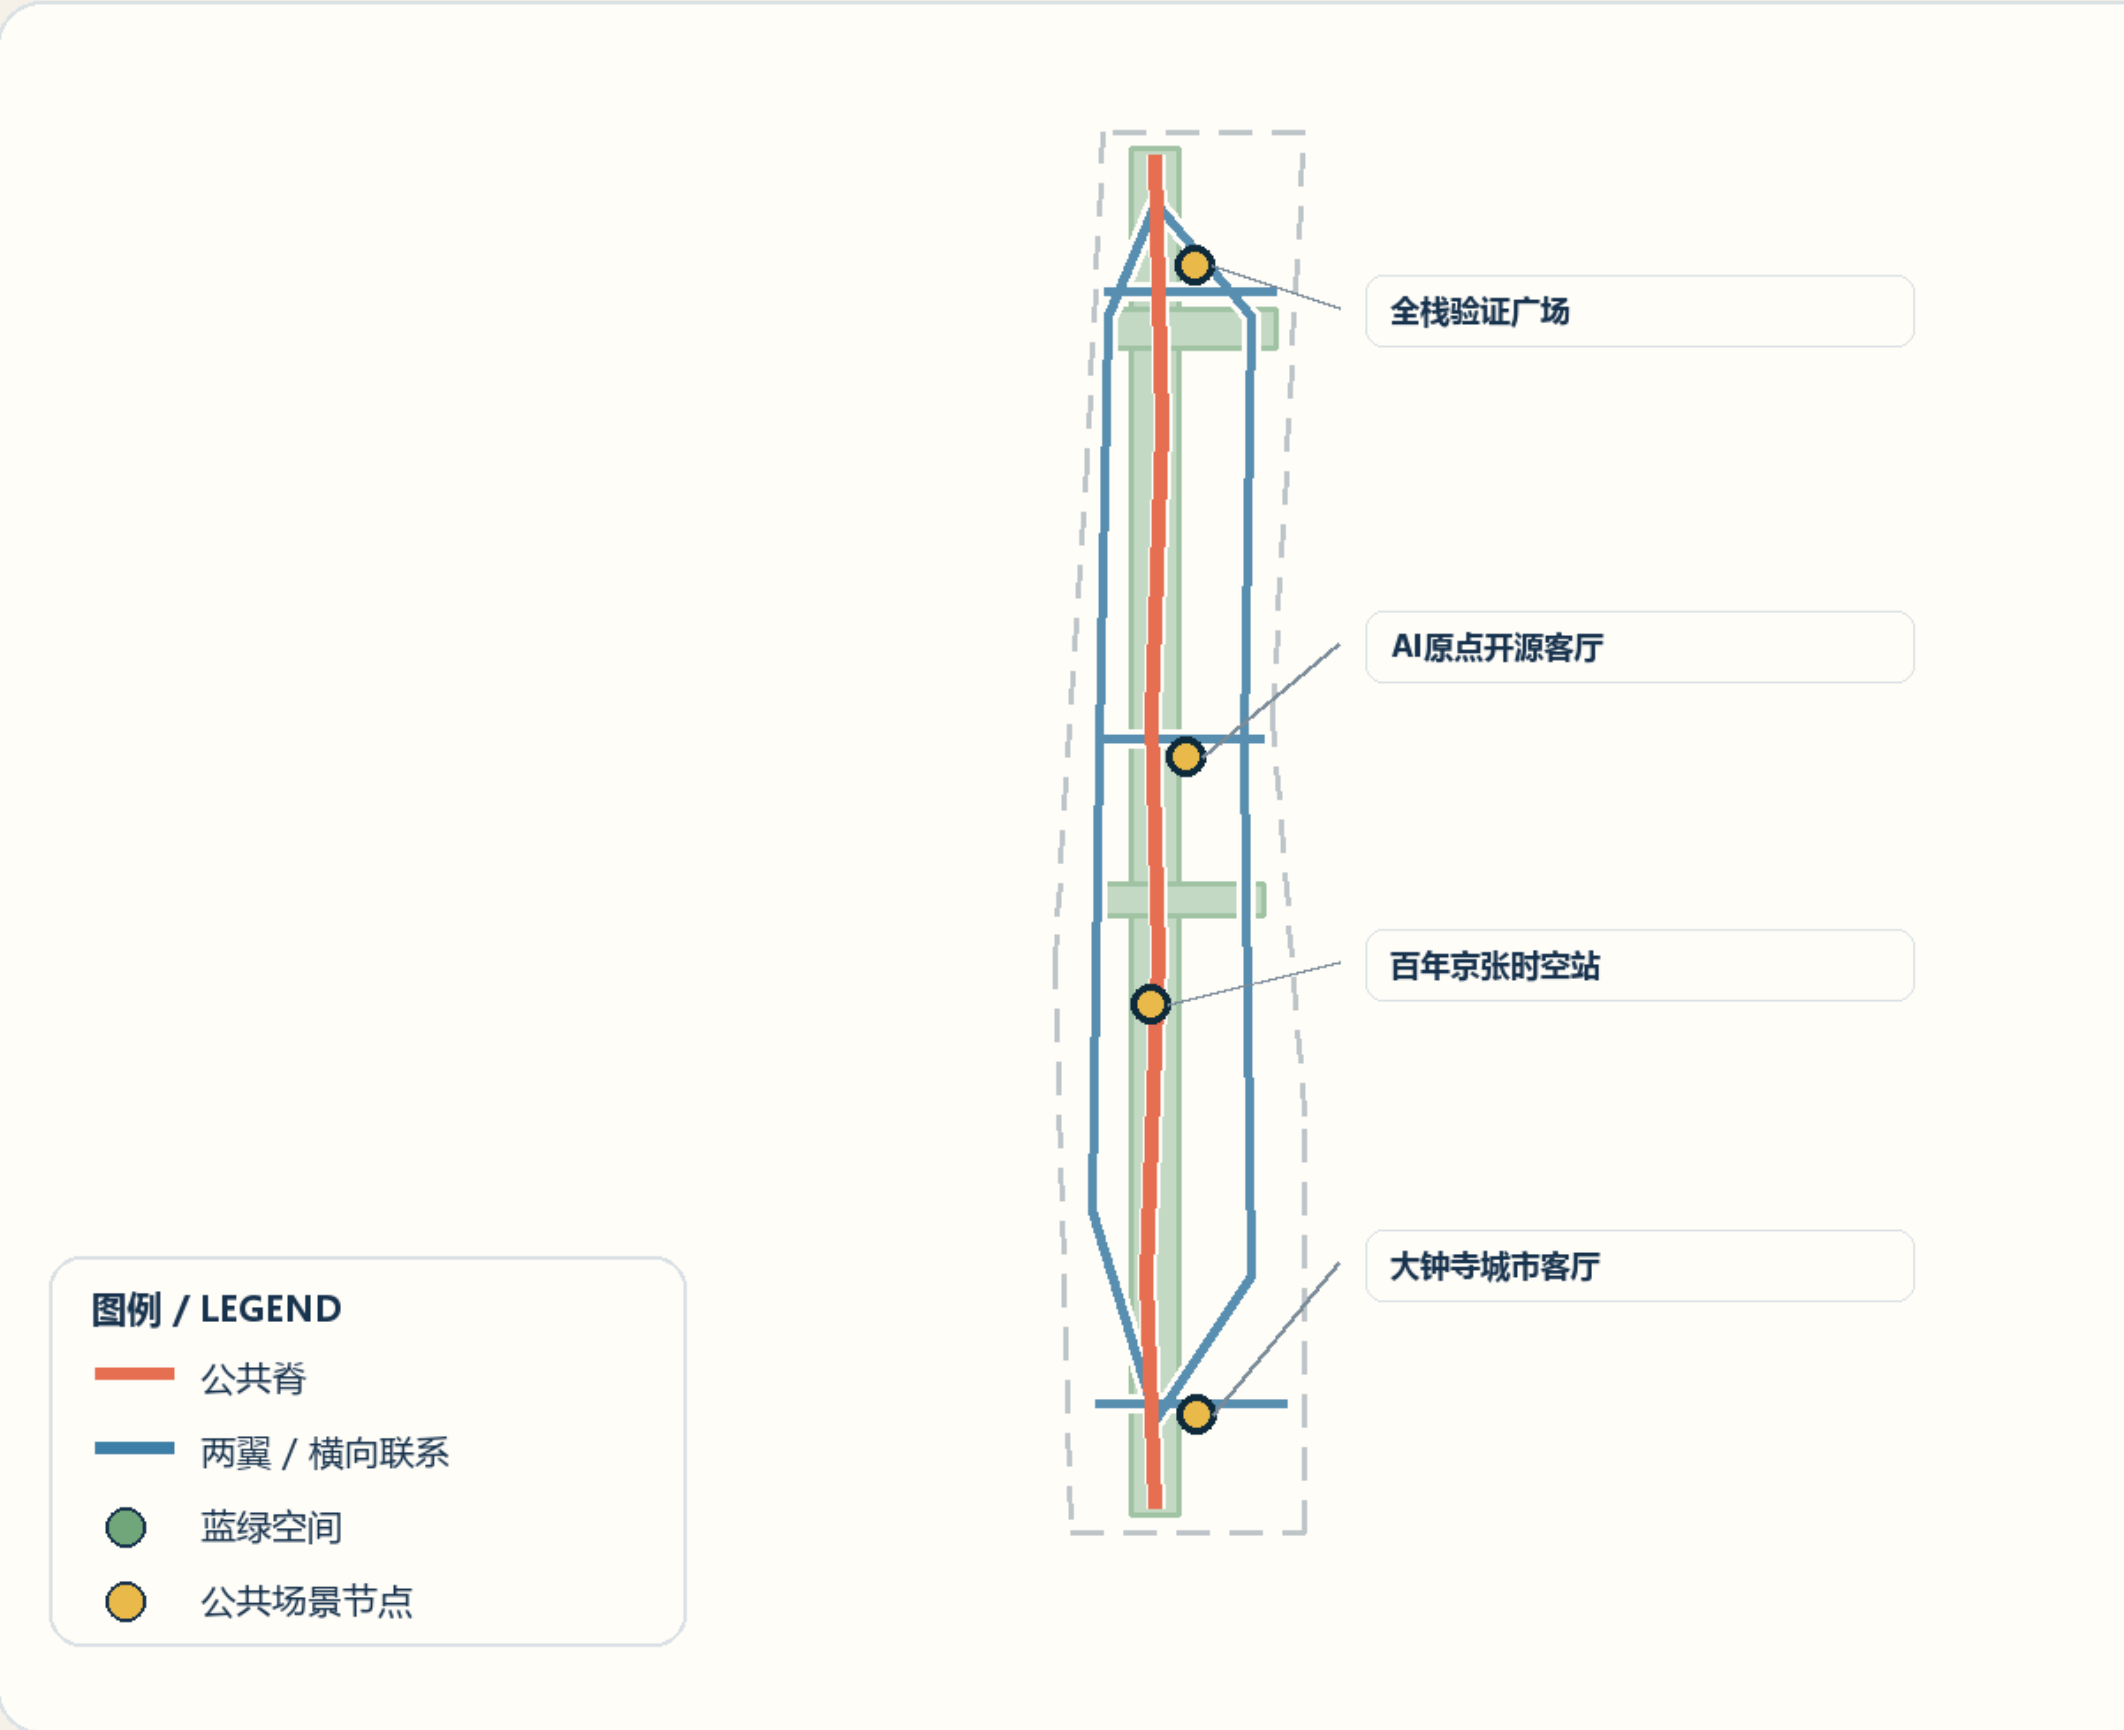

三层叠合

01 连续慢行

一脊 + 两翼 + 三条横向缝合

02 蓝绿骨架

遗址公园纵脊 + 清河 / 小月河横廊

03 公共场景

验证 / 开源 / 城市服务 / 历史贡献

线位均为概念联系；轨道出入口、道路红线、无障碍、消防和管线条件补齐后再深化。

REVISION 2.0 / 2026-08 | 数据：本投稿 GeoJSON / metrics / 矩阵 | PROVISIONAL GEOMETRY，不作官方红线或精确面积依据

京张智脉

设计判断

公共脊成为最强识别；三核分别承担验证、转化、城市服务；东西两翼连接场景与科技服务；三条横向联系修复局部断裂。

空间证据

ROAD-SPINE / ROAD-LINK-N/M/S / GREEN-SPINE/NORTH/MID / PUBLIC-* / LU-001—004 均来自同一提交几何。

复算指标


提交范围11.413km²；概念绿地23.36%；公共空间3.08%；联系网络29.46km。均不替代法定控制。

临时性与深化条件

总体与重点区边界均为 provisional；虚线只作背景。官方 polygon、现状用地、道路、建筑、权属、市政、生态文保资料到位后，整体重算并重绘。

01 众智园

全栈验证与安全治理

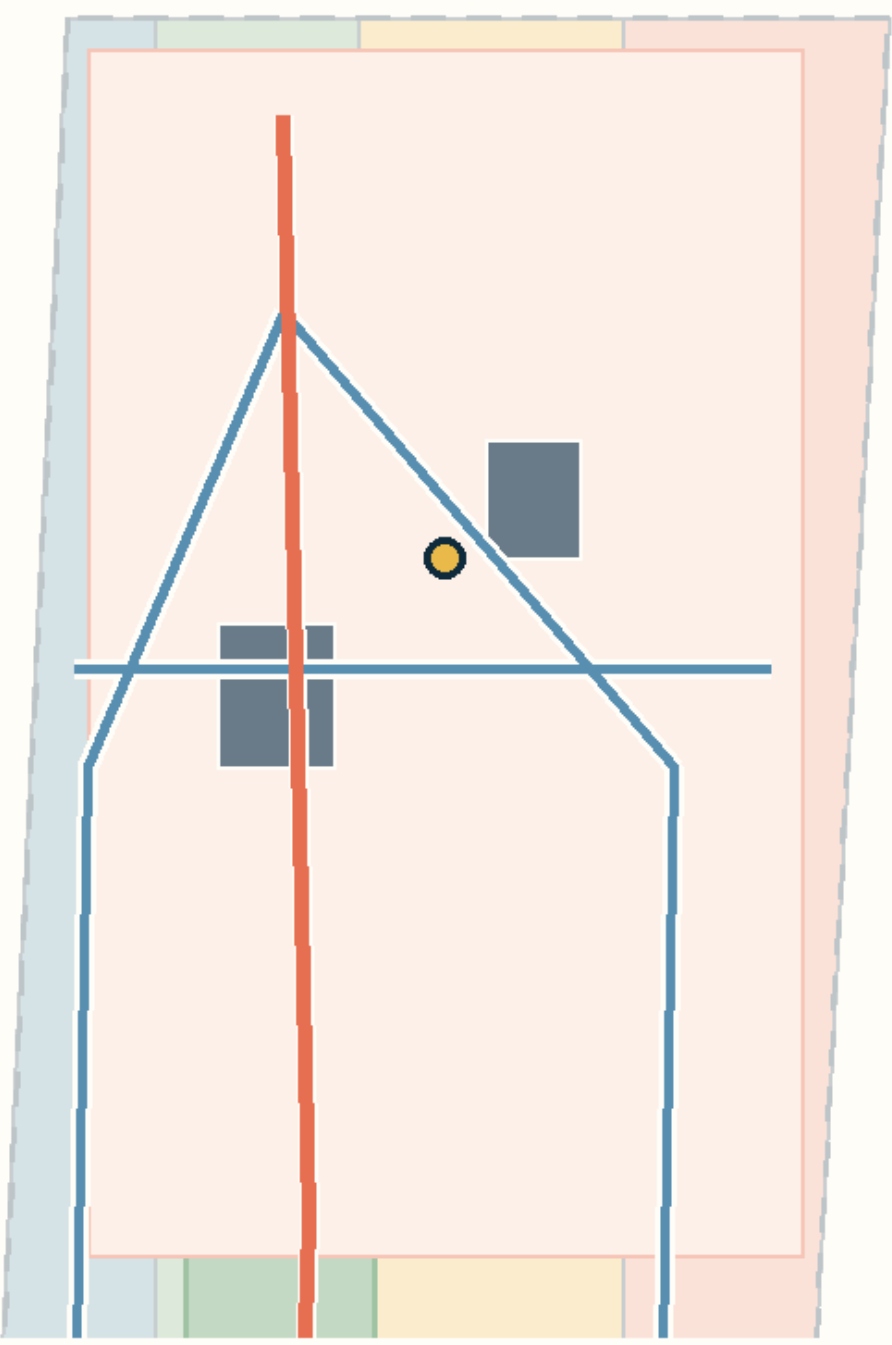


- 公共界面：PUBLIC-NORTH
- 原型：BLDG-NORTH-01/02
- 联系：ROAD-LINK-N
- 机制：隔离测试 / 双人复核 / 退出
- 闸门：清河防洪 / 权属 / 能源

PROVISIONAL
范围待官方 polygon 替换

02 AI原点

开源协作与成果转化

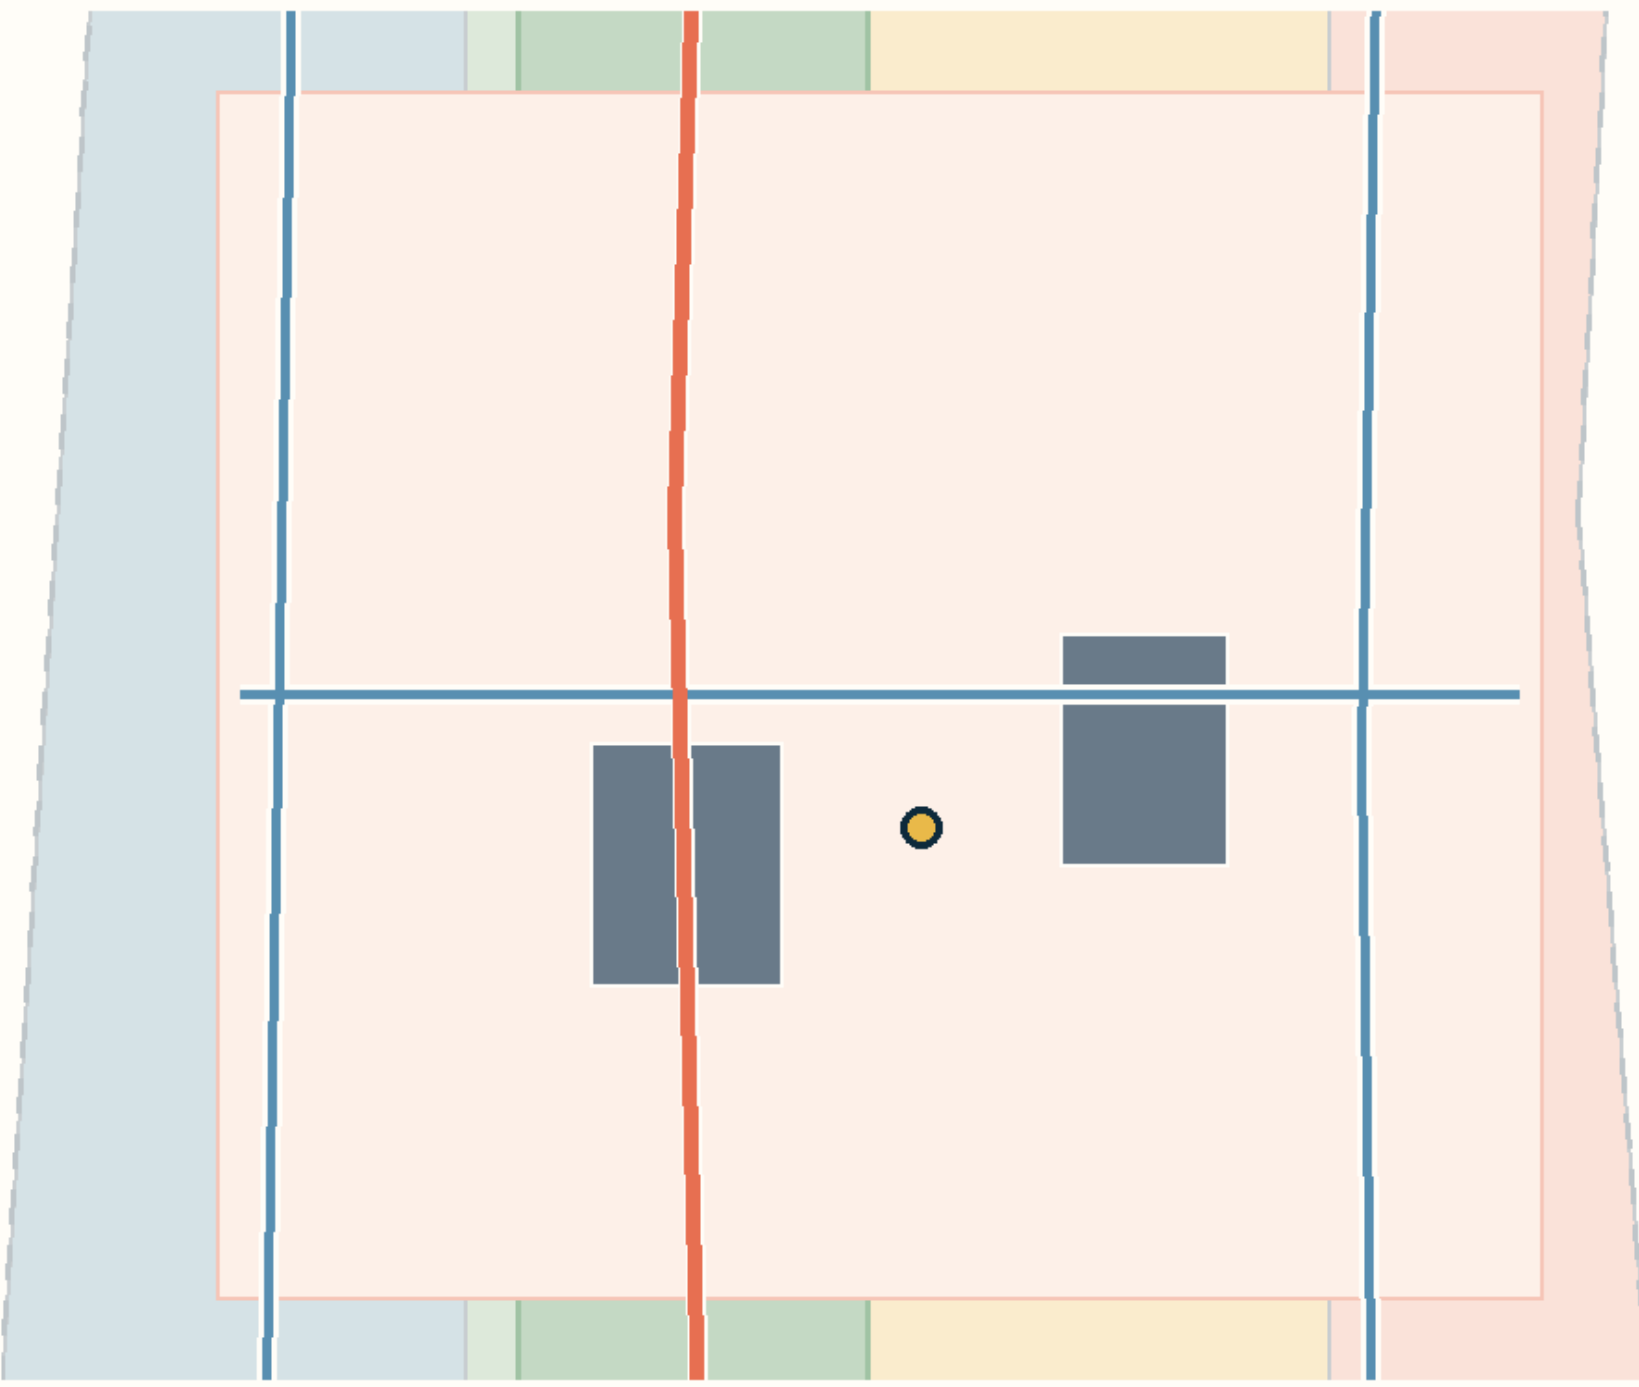


- 公共界面：PUBLIC-ORIGIN
- 原型：BLDG-ORIGIN-01/02
- 联系：ROAD-LINK-M
- 机制：开源评审 / 转化门诊
- 闸门：校园边界 / 消防 / 数据安全

PROVISIONAL
范围待官方 polygon 替换

03 大钟寺

智能原生城市服务与轨道门户

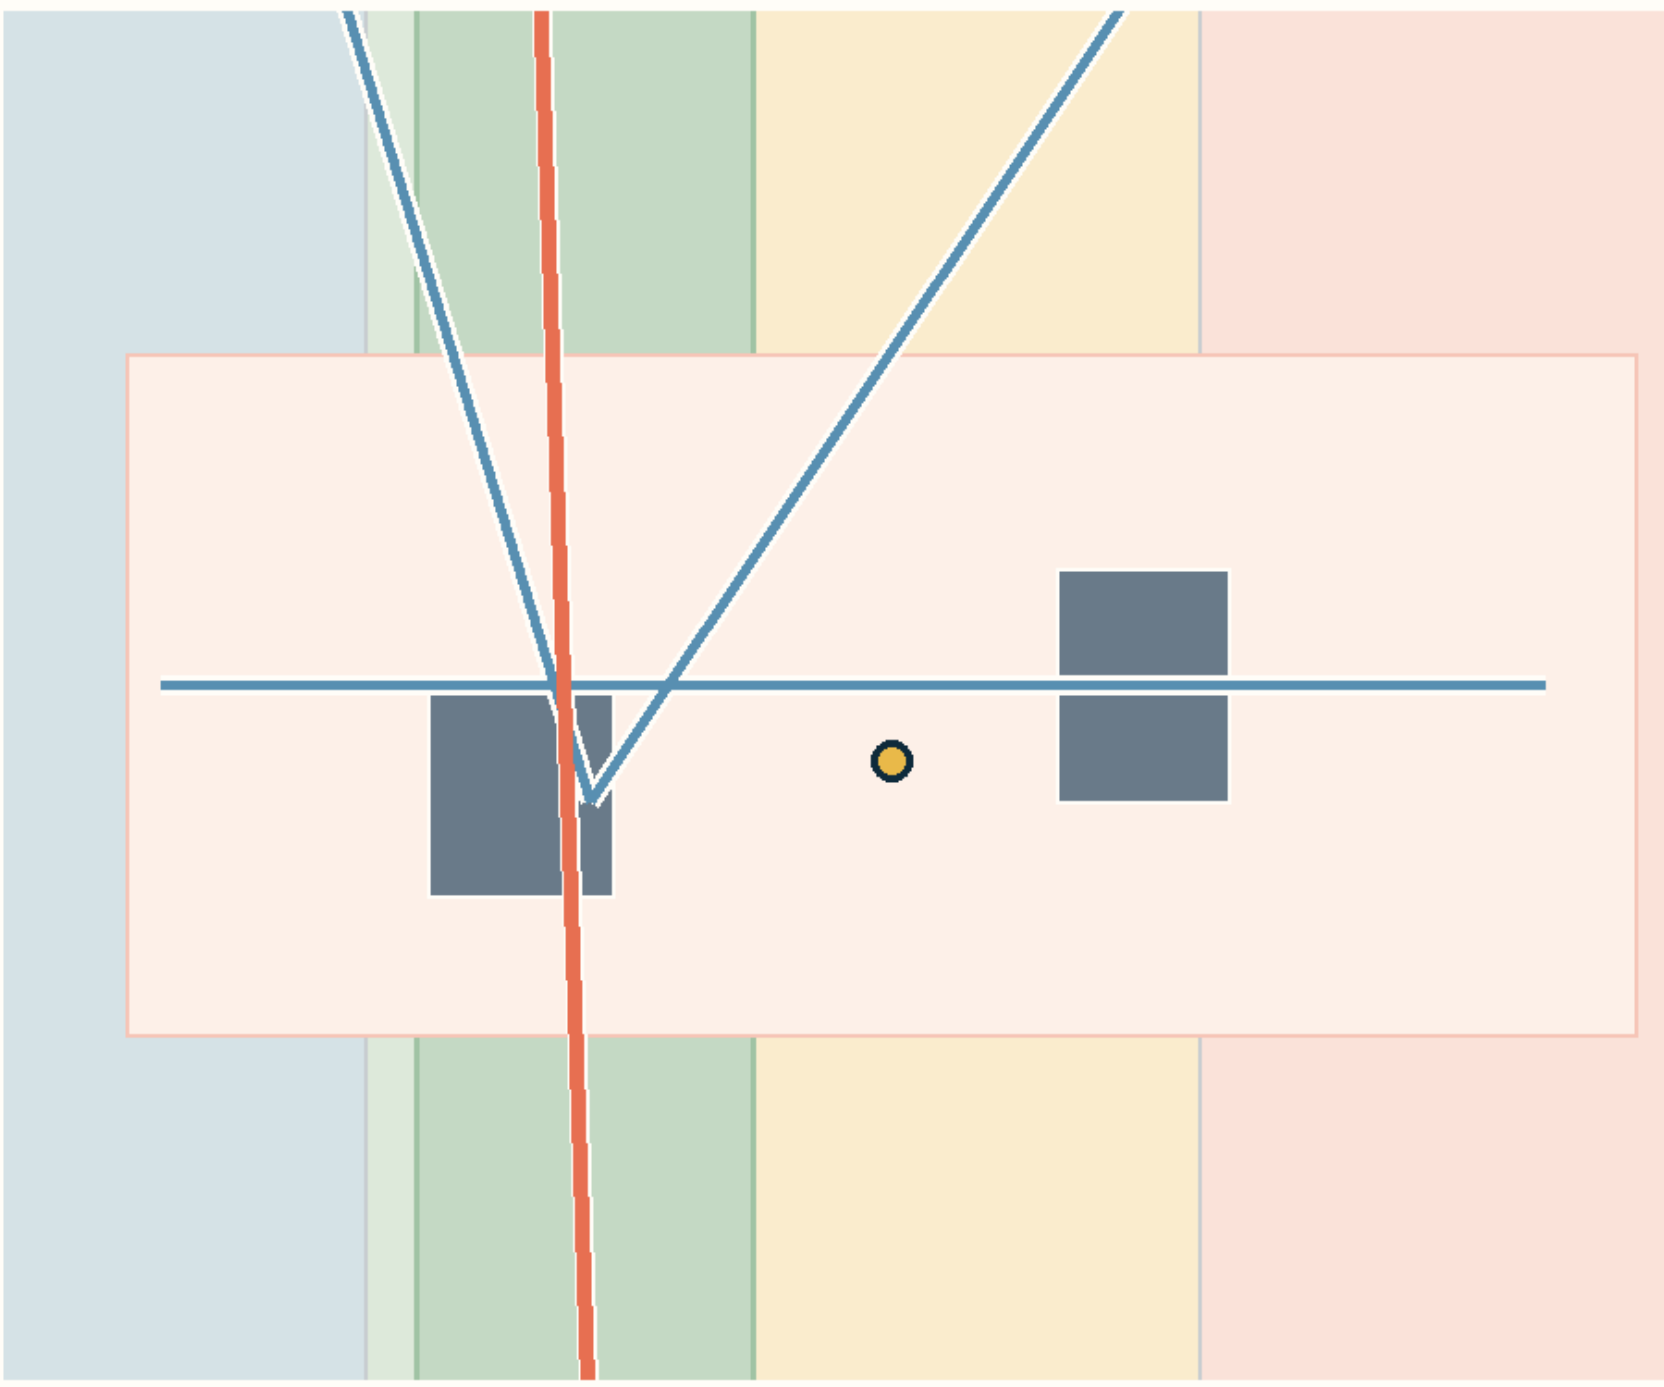

- 公共界面：PUBLIC-SOUTH
- 原型：BLDG-SOUTH-01/02
- 联系：ROAD-LINK-S
- 机制：轨道接驳 / 社区服务
- 闸门：站点 / 地下空间 / 管线

PROVISIONAL
范围待官方 polygon 替换

众智园 | 验证责任可见

功能：全栈共享测试、安全治理工坊。交通：ROAD-LINK-N连接清河两侧与公共脊。公共空间：分时测试铺装、公众观察边界、治理共识厅。机制：预约—隔离—双人复核—公开摘要—退出。

AI原点 | 开源到转化相邻

功能：开源评审、成果发布、转化门诊。交通：ROAD-LINK-M连接校园、园区、社区。公共空间：首层共享与安静研发分层。机制：复现—同行评审—知识产权—试点对接。

大钟寺 | 轨道门户接社区

功能：城市服务、低门槛路演、人才生活。交通：ROAD-LINK-S核验四象眼步行。公共空间：换乘导视、城市客厅、人工窗口。机制：问题提出—服务协办—人工确认—复盘。

实施条件 | 北

官方重点区 polygon、清河防洪、园区权属、设备和能源安全、交通组织。任一关键条件缺失时，仅推进研究与可逆测试。

实施条件 | 中

官方重点区 polygon、校园边界、首层产权、消防疏散、活动噪声、数据安全。开放不等于无边界进入。

实施条件 | 南

官方重点区 polygon、站点出入口、地下空间、交叉口、市政管线、现状建筑与权属。AI不替代人工公共服务。

共同原则

三处重点区均以公共界面 + 建筑原型 + 横向联系 + 治理协议组织，但功能不复制；临时范围只作局部设计容器，不构成官方红线、拆改留或工程线位。

FIG 05 / METRICS + EVIDENCE

主叙事：从GeoJSON到指标、图纸、自检与官方替换重算

指标与证据链 | 每个设计判断都有来源、计算和资料闸门



REVISION 2.0 / 2026-08 | 数据：本投稿 GeoJSON / metrics / 矩阵 | PROVISIONAL GEOMETRY, 不作官方红线或精确面积依据

京张智脉

JZ-01 公共脊断点

PHASE-01 | 道路/消防闸门

JZ-02 众智园验证

PHASE-03 | 防洪/权属/能源

JZ-03 原点转化街

PHASE-02 | 校园/消防/数据

JZ-04 大钟寺连通

PHASE-01 | 站点/地下/管线

JZ-05 蓝绿网络

PHASE-02 | 绿线/防洪/生态

JZ-06 贡献路线

PHASE-03 | 版权/许可/运营

证据底线

真实 GeoJSON → EPSG:4548复算 → 正文与矩阵 → 图纸与HTML → 双重校验。constraints.geojson保持零feature，因为没有可核实约束polygon；未知条件保持unknown；官方polygon到位后全量重算。

S01 无障碍路径

公共脊

S02 安全沙盒★

众智园

S03 互操作测试★

众智园

S04 低碳运维

清河绿廊

S05 开源评审

AI原点

S06 转化门诊

AI原点

S07 公共共创

小月河绿廊

S08 合规会客厅★

AI原点

S09 换乘助手

大钟寺

S10 公共服务

大钟寺

S11 路演字幕

大钟寺

S12 贡献检索

时空站

三期推进与资料闸门

PHASE-01：南部门户、公共体验与大钟寺连通；PHASE-02：AI原点低扰动织补与蓝绿网络；PHASE-03：众智园全栈治理与贡献路线。每期启动前核对官方边界、权属、市政交通、生态文保、运营主体与许可；不满足即停在研究或可逆验证。

合规与复核

23项公告/智能体任务□6项专业标准□15项设计深度□官方四类自检 + 独立引用/哈希审计

场景风险与退出

S02/S03/S08采用分级准入□高风险用途人工复核□可暂停、回滚、删除与退出□测试不等于采购或政府背书