

京张·新轨 THE NEW TRACK

总体设计结构板:一轴两带·三站两翼·多坊

总概念

从自立之轨(1909 京张铁路)到自主之轨(AI 创新带)

空间结构

一轴:新轨主轴(遗址绿廊,界内约 10.7km);两带:文化体验带+小月河蓝绿场景带

三站:钟鸣站(大钟寺)/原点站(AI原点社区)/众智站(众智园)

两翼:中关村科技服务翼(西)/小月河场景赋能翼(东);多坊:保留居住坊/科研转化坊等

定位与功能

三大定位:百年京张文化带 · 都市AI生活体验带 · AI融合创新带

五大功能:全栈自主 / 世界级生态 / 场景赋能 / 活力城市 / 治理话语权

京张·新轨 THE NEW TRACK — 总体概念图

从自立之轨(1909)到自主之轨(AI):一轴两带·三站两翼·多坊 | 概念建议,非官方规划



新轨主轴(慢行绿廊,概念) 小月河滨水场景带 AI场景节点 总体设计范围(provisional)

数据: provisional 临时边界(非官方红线,官方polygon取得后复算) + OSM(e OpenStreetMap contributors, ODbL) + 本方案生成图层 | 面积复算: EPSG:4548 | 全部空间建议均为概念建议 | 图1/5 总体概念

用地与城市更新板

总体设计范围 1141.3 公顷(provisional 复算)

用地构成

居住保留 29.9% / 科研 19.9% / 商业 18.3% / 绿地 13.4% / 留白 6.8% / 文教体卫 7.4% / 道路广场 4.3%

更新逻辑

保留为主(70%+);更新集中于三站周边与主轴两侧;拆改留为类型级概念建议,无具体地块结论

更新项目包



绿廊贯通 / 三站广场群 / 微循环路网 / 场景节点设施 / 既有建筑更新概念包

待确认

控规条件(容积率/高度/密度/绿地率/退线)缺失,待官方资料

用地结构与三层范围传导图

总体设计范围 1141.3 公顷(provisional 复算):保留更新为主、三站触媒、绿廊贯通 [metric:site_area_sqm]

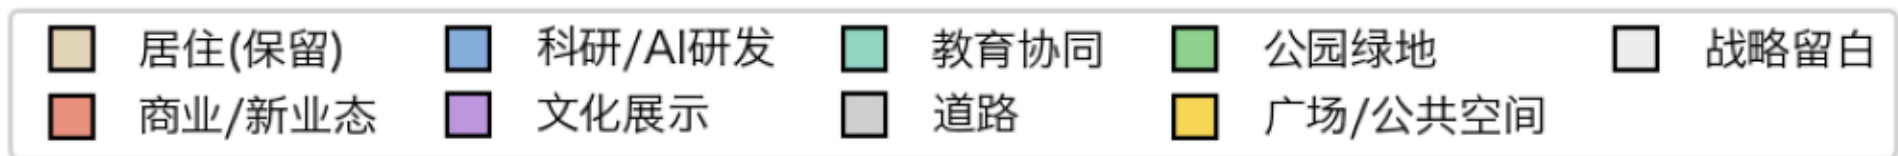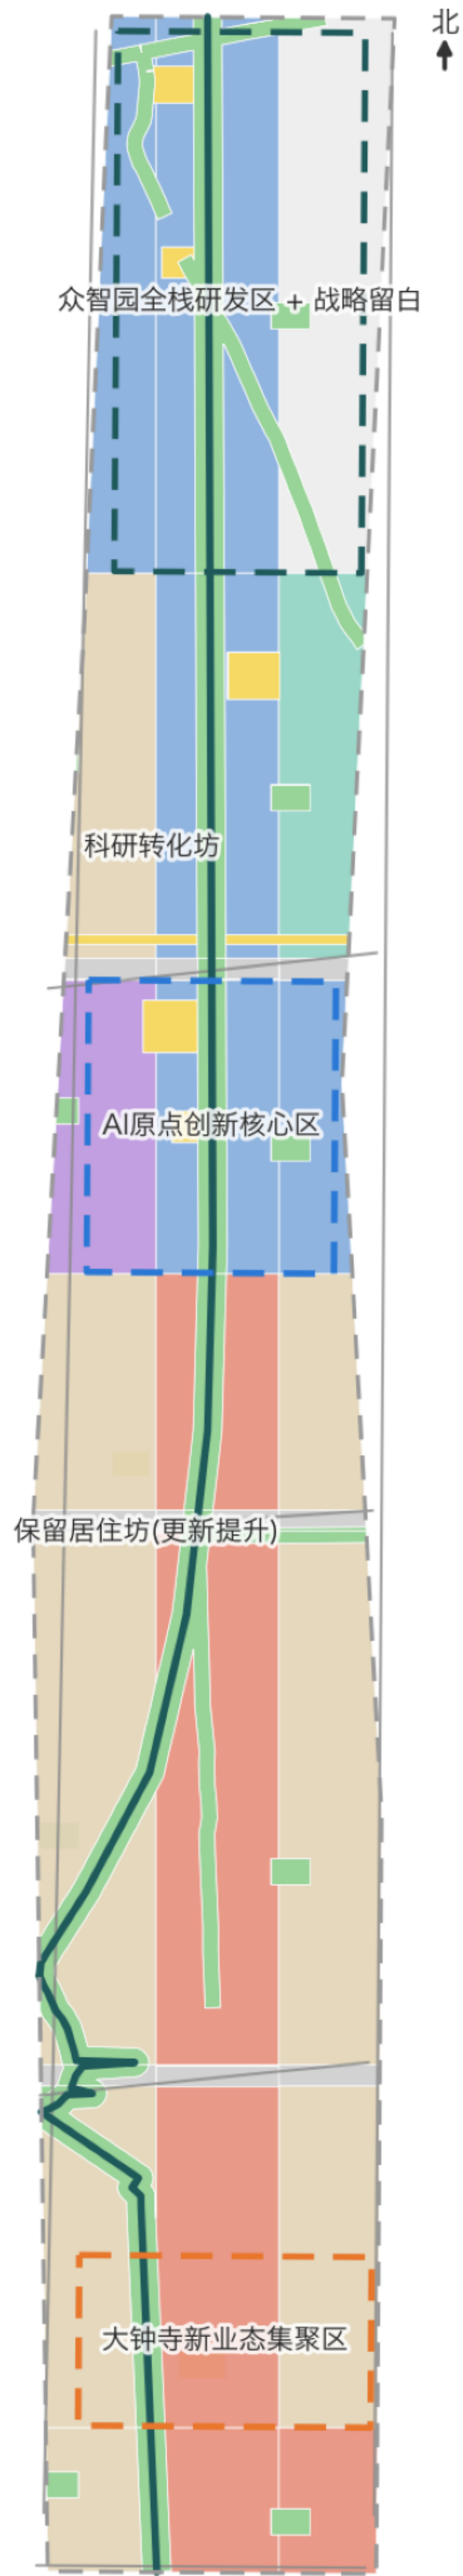

[红线,官方polygon取得后复算] + OSM(e OpenStreetMap contributors, ODbL) + 本方案生成图层 | 面积复算: EPSG:4548 | 全部空间建议均为概念建议 | 图2/5 用地结构(用地编码依据《国土空间调查、规划、用途

轨道接驳

大钟寺(12/13)/知春路(10/13)/五道口(13)/清华东路西口(15)四站最后一公里(概念)

慢行系统

新轨慢行主轴(步行+骑行+无人接驳概念)+ 小月河滨水绿道 + 重点区微循环环

道路与停车


不动主干路网;成府路/知春路断面慢行优先(概念);外围截流+共享停车

市政新基建

算力驿站 / 感知管网 / 智慧灯杆 / 海绵调蓄(均概念,容量不作结论)

交通慢行 × 蓝绿公共空间复合系统图

四站接驳 + 新轨慢行主轴 + 小月河滨水绿道 + 绿廊/广场/场景节点网络(概念建议)

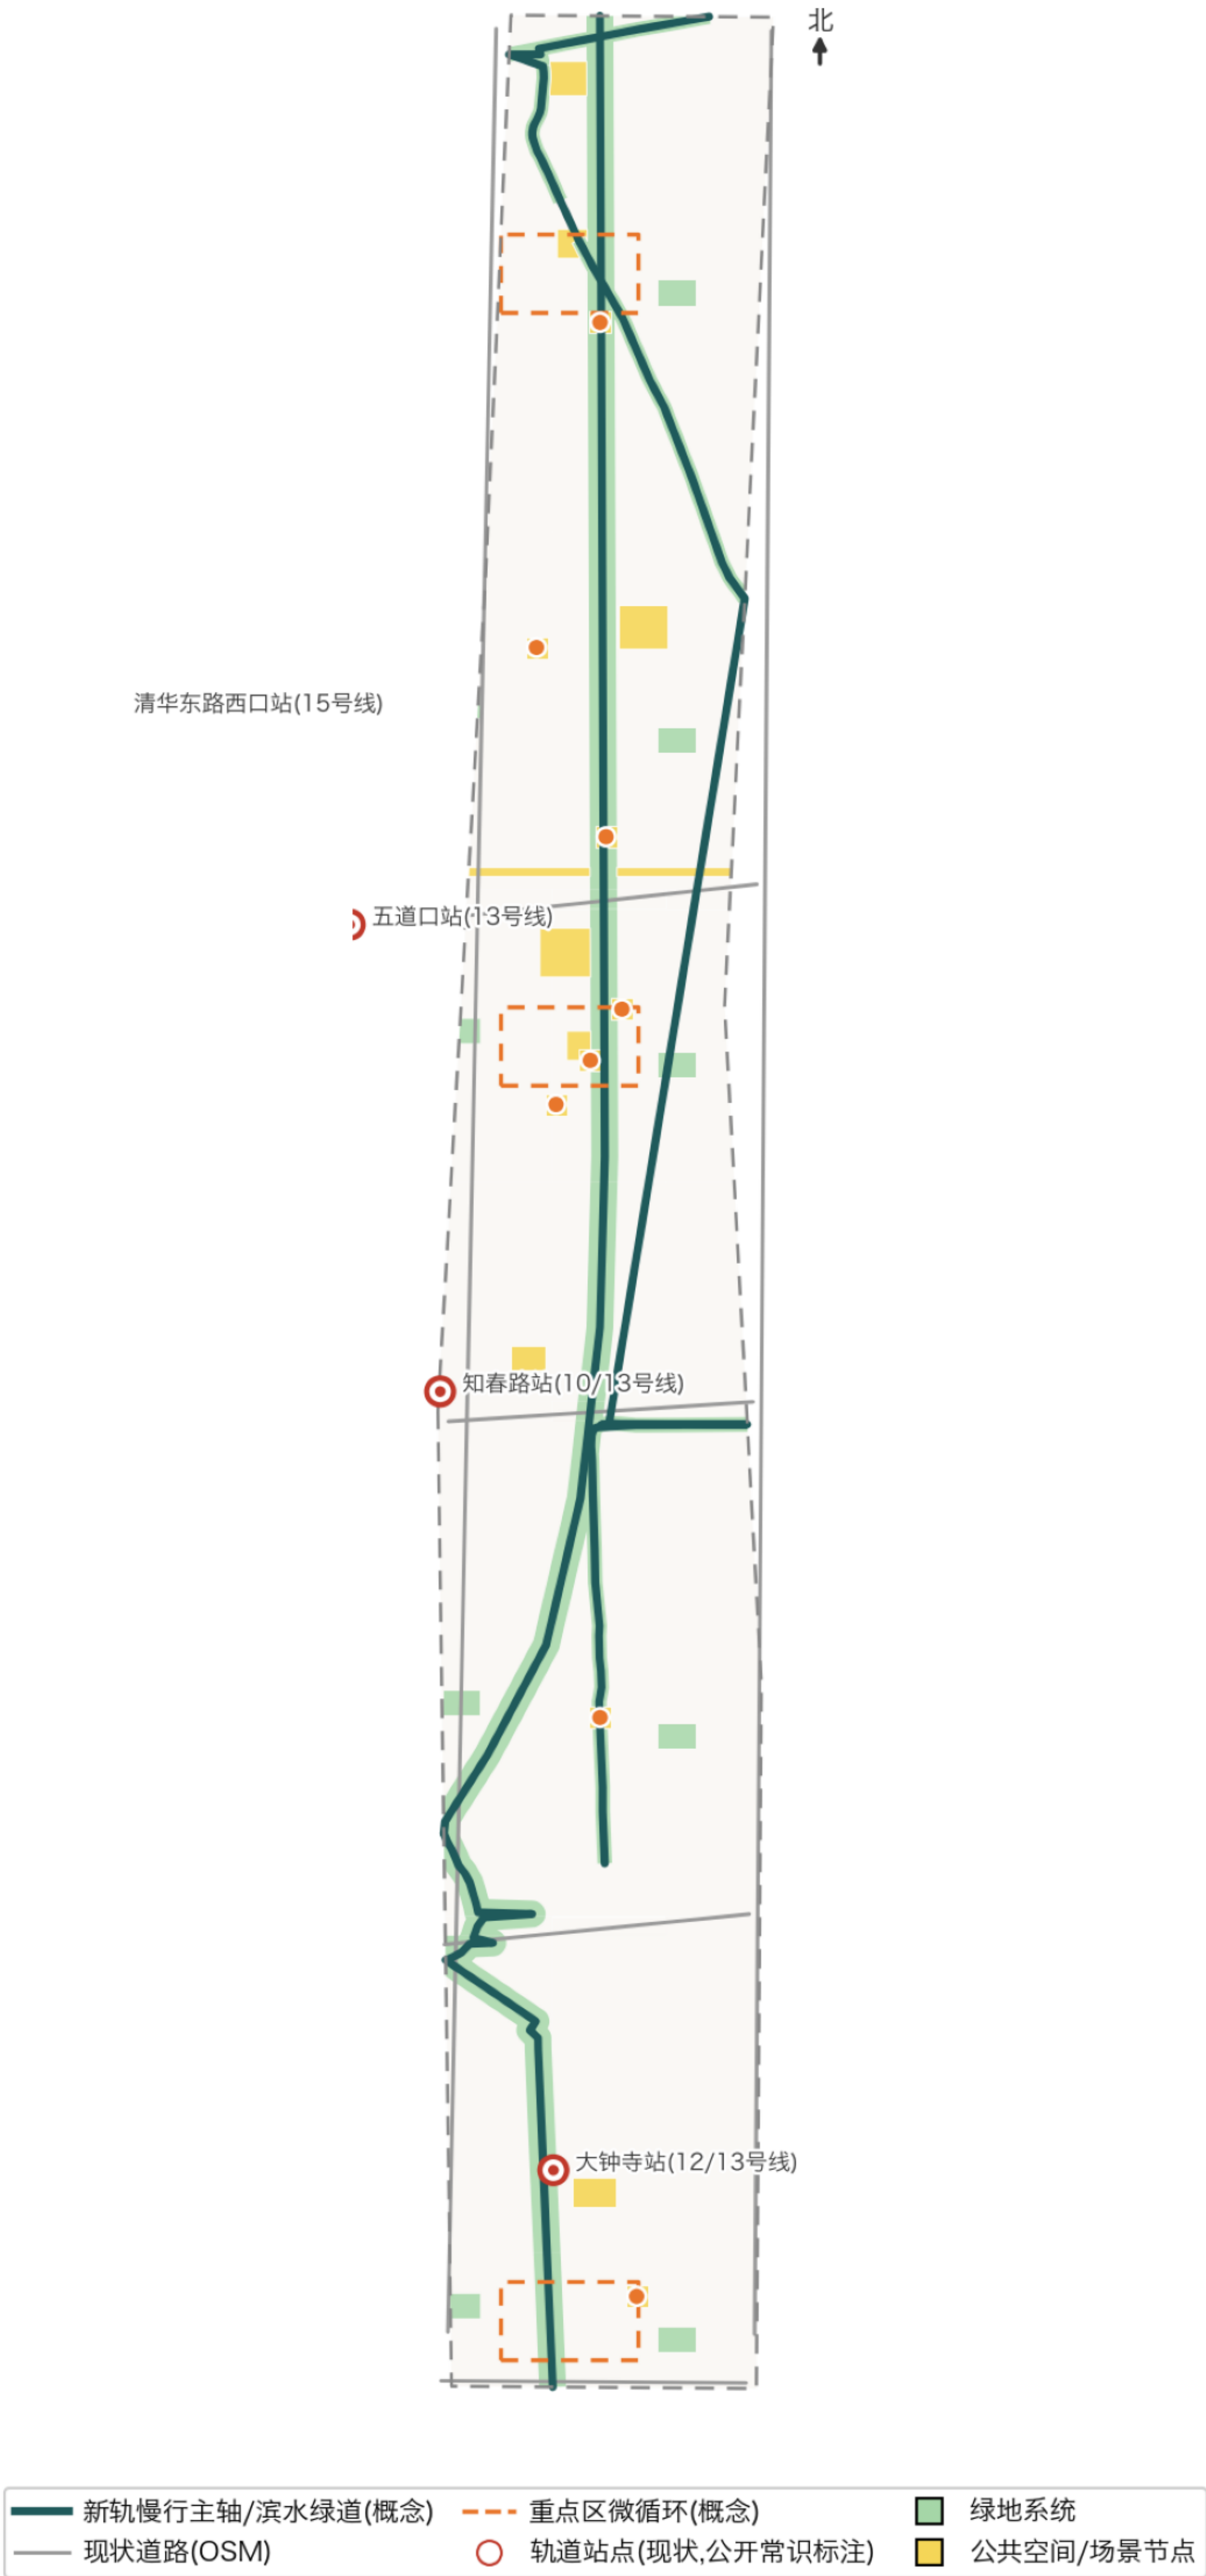

数据: provisional 临时边界(非官方红线,官方polygon取得后复算) + OSM(© OpenStreetMap contributors, ODbL) + 本方案生成图层 | 面积复算: EPSG:4548 | 全部空间建议均为概念建议 | 图4/5 交通与蓝绿

京张遗址公园活力带与蓝绿公共空间板

从铁轨到光轨

蓝绿骨架

新轨绿廊(110m 宽主轴)+ 小月河蓝绿带 + 10 处口袋公园;绿地率 13.4%(复算)

公共空间

五大广场(钟鸣/原点/众智/知春路/清河门户)+ 成府路慢行走廊;公共空间占比 2.2%(复算)

文化表达

三层时间:1909 工业自立 → 1980s 中关村创新 → 2020s 智能自主;


导视系统:信号灯色/道岔符号转译;三站专属色(钟鸣橙/原点蓝/众智青)

朝圣地标(概念)

「新轨原点」纪念场 / 「代码站台」开源荣誉步廊 / 「众智引擎」算力灯塔 / 「钟鸣时刻」(备选)

交通慢行 × 蓝绿公共空间复合系统图

四站接驳 + 新轨慢行主轴 + 小月河滨水绿道 + 绿廊/广场/场景节点网络(概念建议)

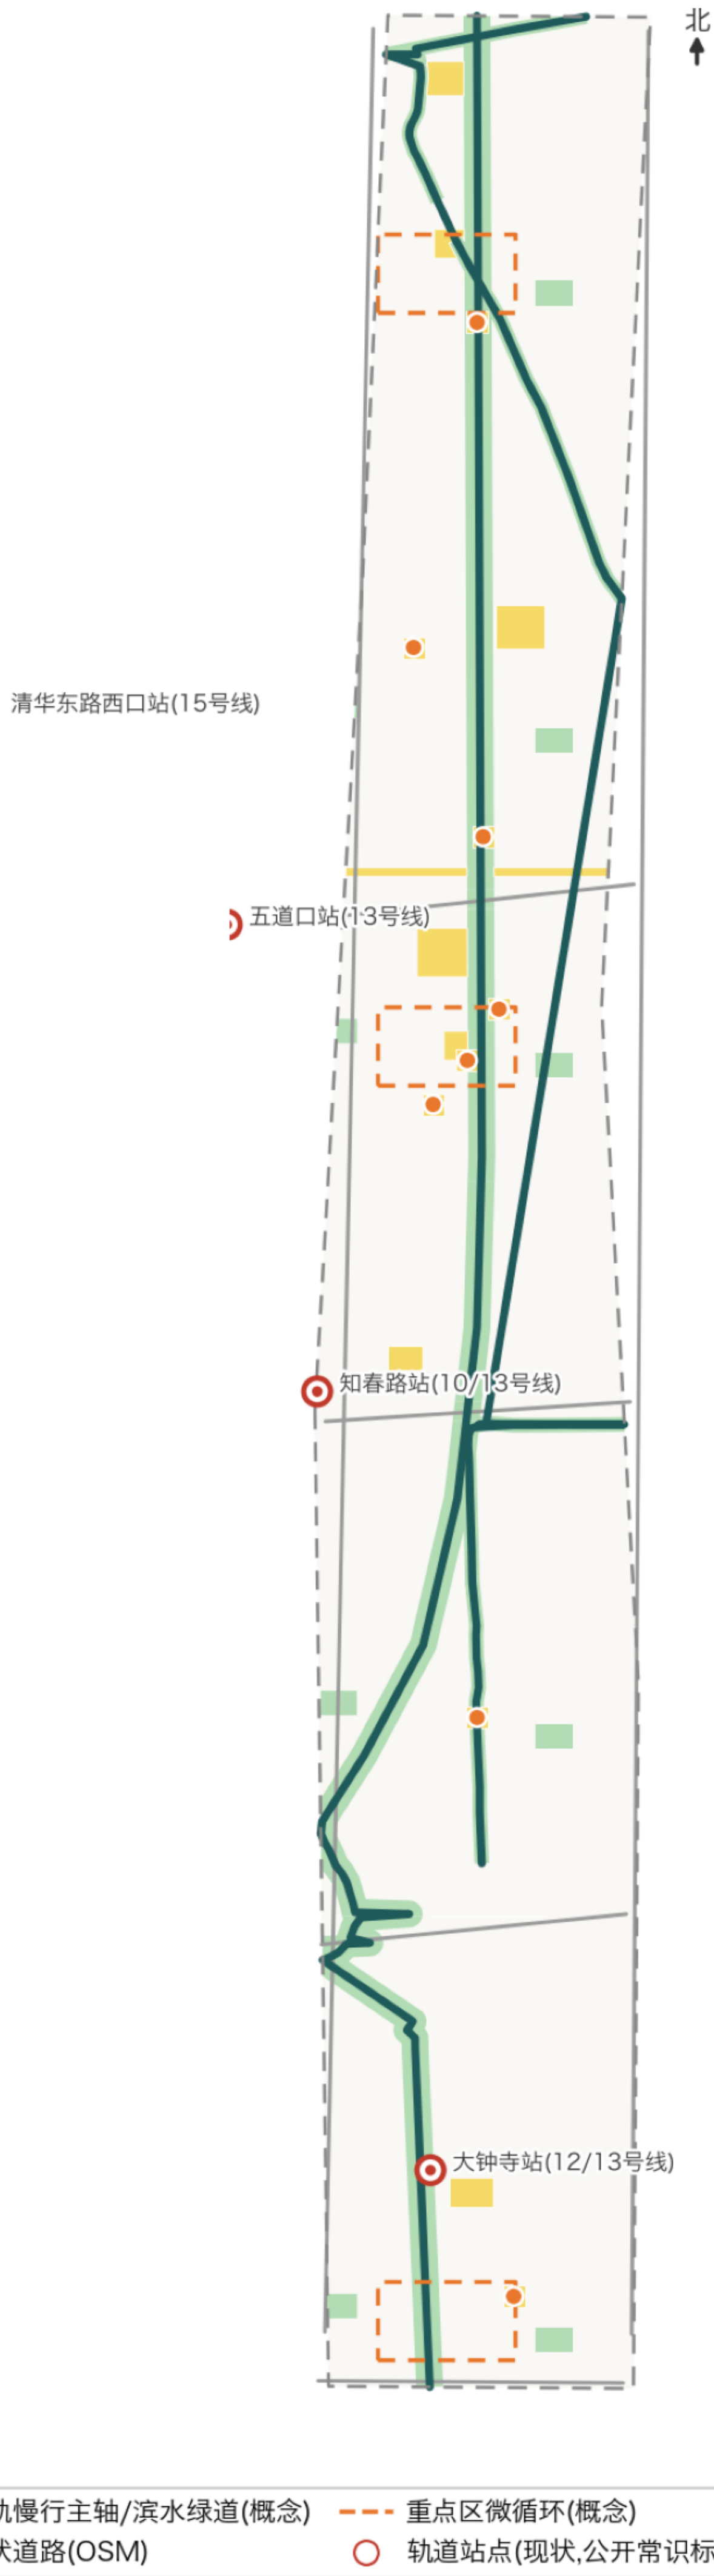

数据: provisional 临时边界(非官方红线,官方polygon取得后复算) + OSM(© OpenStreetMap contributors, ODbL) + 本方案生成图层 | 面积复算: EPSG:4548 | 全部空间建议均为概念建议 | 图4/5 交通与蓝绿

三处重点区域详细设计板

钟鸣站 · 原点站 · 众智站

众智站(北,192.9ha 复算)

AI全栈自主创新总装场:算力驿站+全栈研发组团+战略留白;「众智引擎」 灯塔(概念)

原点站(中,104.3ha 复算)

世界级创新生态中枢:开源荣誉步廊+国际人才服务+孵化器更新;「新轨原点」 纪念场(概念)

钟鸣站(南,72.0ha 复算)


智能原生新业态报时站:AI消费/商务场景首发+夜间活力;「钟鸣时刻」 文化对位(概念)

共同约束


provisional 边界内概念设计;建筑体量为概念基底,非工程结论;文保范围以官方公布为准

三处重点区域详细设计索引(自北向南)


众智站 · 众智园AI自主创新加速区
全栈自主创新总装场:算力驿站+全栈研发组团+战略留白;「众智引擎」 灯塔(概念)

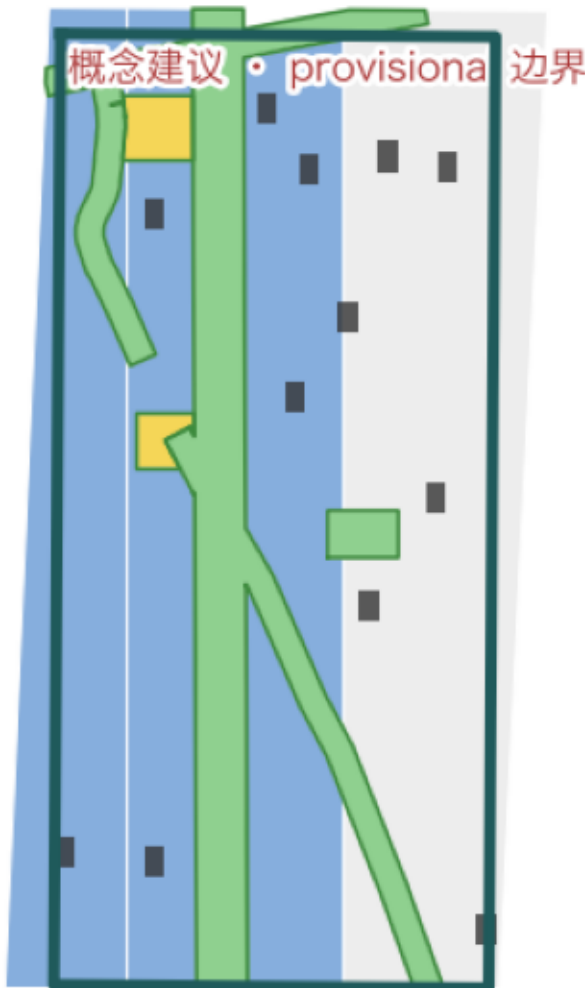

原点站 · 北京AI原点社区
世界级创新生态中枢:开源荣誉步廊+国际人才服务+孵化器更新;「新轨原点」 纪念场(概念)

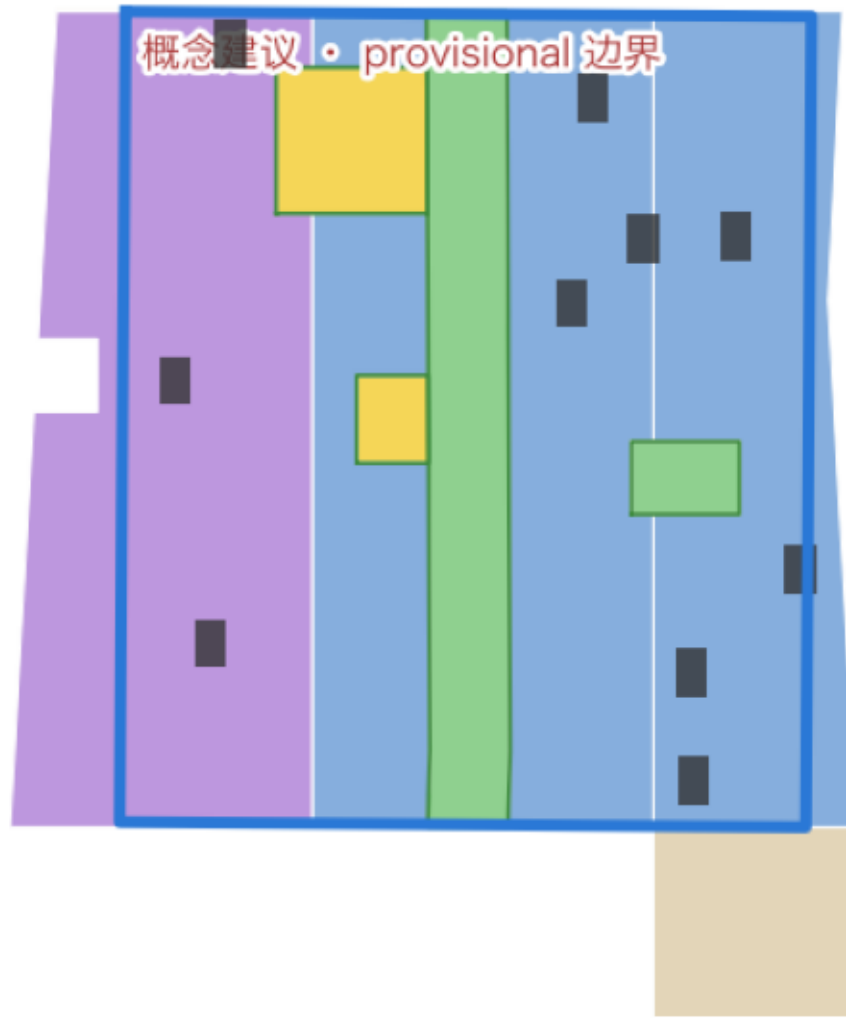

钟鸣站 · 大钟寺AI产业集聚区
智能原生新业态报时站:AI消费/商务场景首发+夜间活力;「钟鸣时刻」 文化对位(概念)

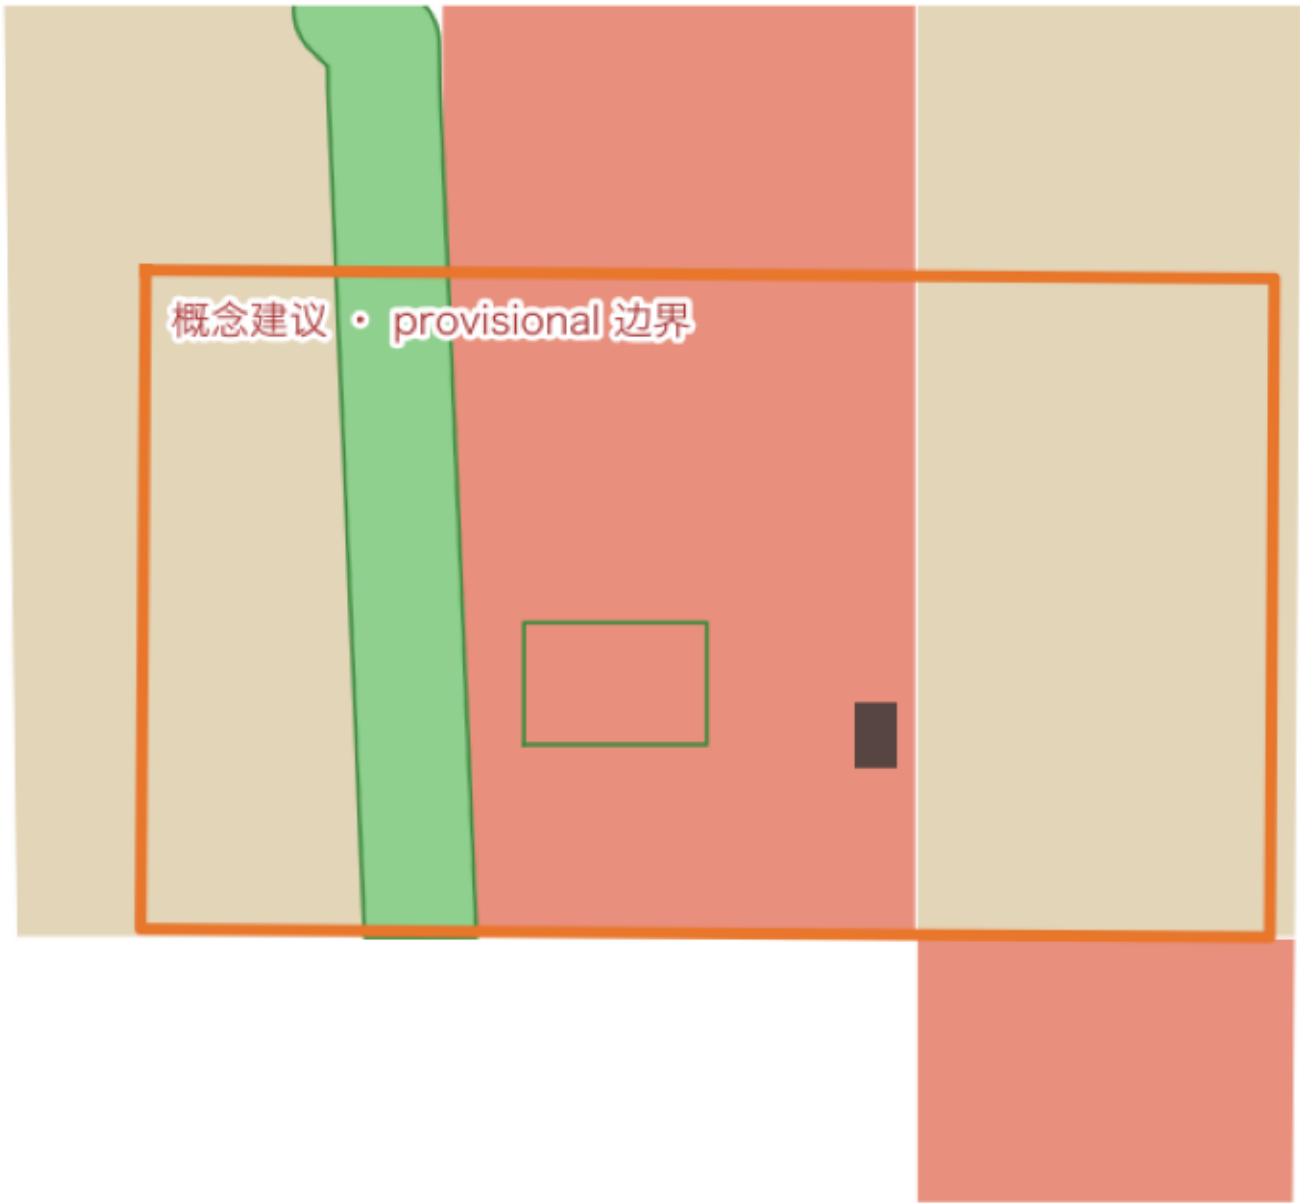

数据: provisional 临时边界(非官方红线,官方polygon取得后复算) + OSM(© OpenStreetMap contributors, ODbL) + 本方案生成图层 | 面积复算: EPSG:4548 | 全部空间建议均为概念建议

AI 场景与实施运营板

12 场景卡 · 6 类画像 · 新轨时刻表

AI+ 场景

12 张场景卡(含隐私边界与人工复核);3 个产业测试验证场景:无人接驳/城市巡检/机器人配送

用户画像

研究员 / 创业者 / 在地居民 / 学生与国际交换生 / 朝圣游客 / 城市运营者

年度活动

春 · 新轨开发者大会 / 夏 · 场景开放季 / 秋 · 京张创新周 / 冬 · 光影编程季(均概念)

长期机制

开发者驿站 / 场景开放申请制 / AI向善年度奖 / 国际招引转化路径(机制建议)

分期

PH-1 近期(大钟寺+原点+南段) / PH-2 中期(中段) / PH-3 远期(众智园)

核心指标复算与证据链

全部面积指标由 geometry/*.geojson 在 EPSG:4548 下复算;provisional 边界口径;官方数据取得后整体复算

指标	数值	公式/来源	备注
总用地面积	11,412,825 m²(≈1141.3 公顷)	polygon_area(site_boundary)	与公告 11.4km² 偏差 +0.11%
绿地面积/占比	1,533,340 m² / 13.4%	green_space/site	绿廊+滨水+口袋公园
公共空间面积/占比	254,012 m² / 2.2%	public_space/site	广场+线型走廊+场景节点
道路用地占比	2.1%	road_area(1207)/site	三条干路带口径
概念建筑基底	94,248 m²	sum(buildings)	仅概念新增/改造,不含现状
重点区面积	众智园 192.9ha / 原点 104.3ha / 大钟寺 72.0ha	polygon_area(key_areas)	与公告偏差 ≤+0.43%
新轨主轴长度	约 10.7 km(界内)	length(axis_centerline)	真实线位段+设计延伸段
总建筑面积	未知	需批准控规条件	待官方资料,不得臆造
容积率	未知	需批准控规条件	待官方资料,不得臆造
AI场景节点 / 朝圣地标	8 处 / 3+1 处	count(geometry)	概念建议

证据链: GeoJSON(权威) → metrics.json(复算) → 三矩阵(合规/标准/深度) → 正文引用 [metric:*] → 本图

自检状态: spatial_review PASS(仅 3 条 provisional 提示) | 待确认: 官方精确边界、控规条件、现状底数、文保范围

数据: provisional 临时边界(非官方红线,官方polygon取得后复算) + OSM(© OpenStreetMap contributors, ODbL) + 本方案生成图层 | 面积复算: EPSG:4548 | 全部空间建议均为概念建议

指标复核与合规响应板

GeoJSON → metrics → 三矩阵 → 正文 → 图件,全链可复算

核心指标

总用地 11,412,825 m² · 绿地率 13.4% · 公共空间 2.2% · 道路 2.1%

重点区三处复算与公告偏差 ≤+0.43%;主轴约 10.7km;场景节点 8;地标 3+1

unknown

总建筑面积/容积率/建筑高度/建筑密度:控规条件缺失,不臆造,待官方资料

合规

compliance 23 条全覆盖 · standard 5 条强制标准 · depth 15 项全部 complete

版权与红线

全部自生成 + OSM(ODbL);无未清权素材;空间建议均为概念建议,不作政府承诺

核心指标复算与证据链

全部面积指标由 geometry/*.geojson 在 EPSG:4548 下复算;provisional 边界口径;官方数据取得后整体复算

指标	数值	公式/来源	备注
总用地面积	11,412,825 m ² (≈1141.3 公顷)	polygon_area(site_boundary)	与公告 11.4km ² 偏差 +0.11%
绿地面积/占比	1,533,340 m ² / 13.4%	green_space/site	绿廊+滨水+口袋公园
公共空间面积/占比	254,012 m ² / 2.2%	public_space/site	广场+线型走廊+场景节点
道路用地占比	2.1%	road_area(1207)/site	三条干路带口径
概念建筑基底	94,248 m ²	sum(buildings)	仅概念新增/改造,不含现状
重点区面积	众智园 192.9ha / 原点 104.3ha / 大钟寺 72.0ha	polygon_area(key_areas)	与公告偏差 ≤+0.43%
新轨主轴长度	约 10.7 km(界内)	length(axis centerline)	真实线位段+设计延伸段
总建筑面积	未知	需批准控规条件	待官方资料,不得臆造
容积率	未知	需批准控规条件	待官方资料,不得臆造
AI场景节点 / 朝圣地标	8 处 / 3+1 处	count(geometry)	概念建议

证据链: GeoJSON(权威) → metrics.json(复算) → 三矩阵(合规/标准/深度) → 正文引用 [metric:*] → 本图

自检状态: spatial_review PASS(仅 3 条 provisional 提示) | 待确认: 官方精确边界、控规条件、现状底数、文保范围

数据: provisional 临时边界(非官方红线,官方polygon取得后复算) + OSM(e OpenStreetMap contributors, ODbL) + 本方案生成图层 | 面积复算: EPSG:4548 | 全部空间建议均为概念建议