

把百年京张 AI 创新带设计成一条持续运转、可被公众审计的城市验证长廊。方案提出可复制的最小单位——验证单元，由空间载体、验证协议、公示看板和退出机制四件套构成，沿京张遗址公园形成九段五带的空间骨架，串联众智园、AI 原点社区、大钟寺三区，并由中关村科技服务翼与小月河场景赋能翼供给资源 and 需求。

核心机制：提案 → 验证 → 公示 → 转化

三条硬约束


- 失败必须公示：验证不通过的项目与原因同样进入公示看板，不得只公示成功案例。
- 人工兜底路径不得更慢更贵：任何 AI 服务都保留人工通道，且不得在时间或费用上惩罚选择人工的人。
- 默认不参与：公共空间中的数据采集与智能服务默认关闭，由使用者主动选择加入。

验证单元四件套




三级范围与证据链总览图

统筹研究范围约 43.6 km² | 总体设计范围约 11.4 km² | 重点详细设计范围约 368.4 ha

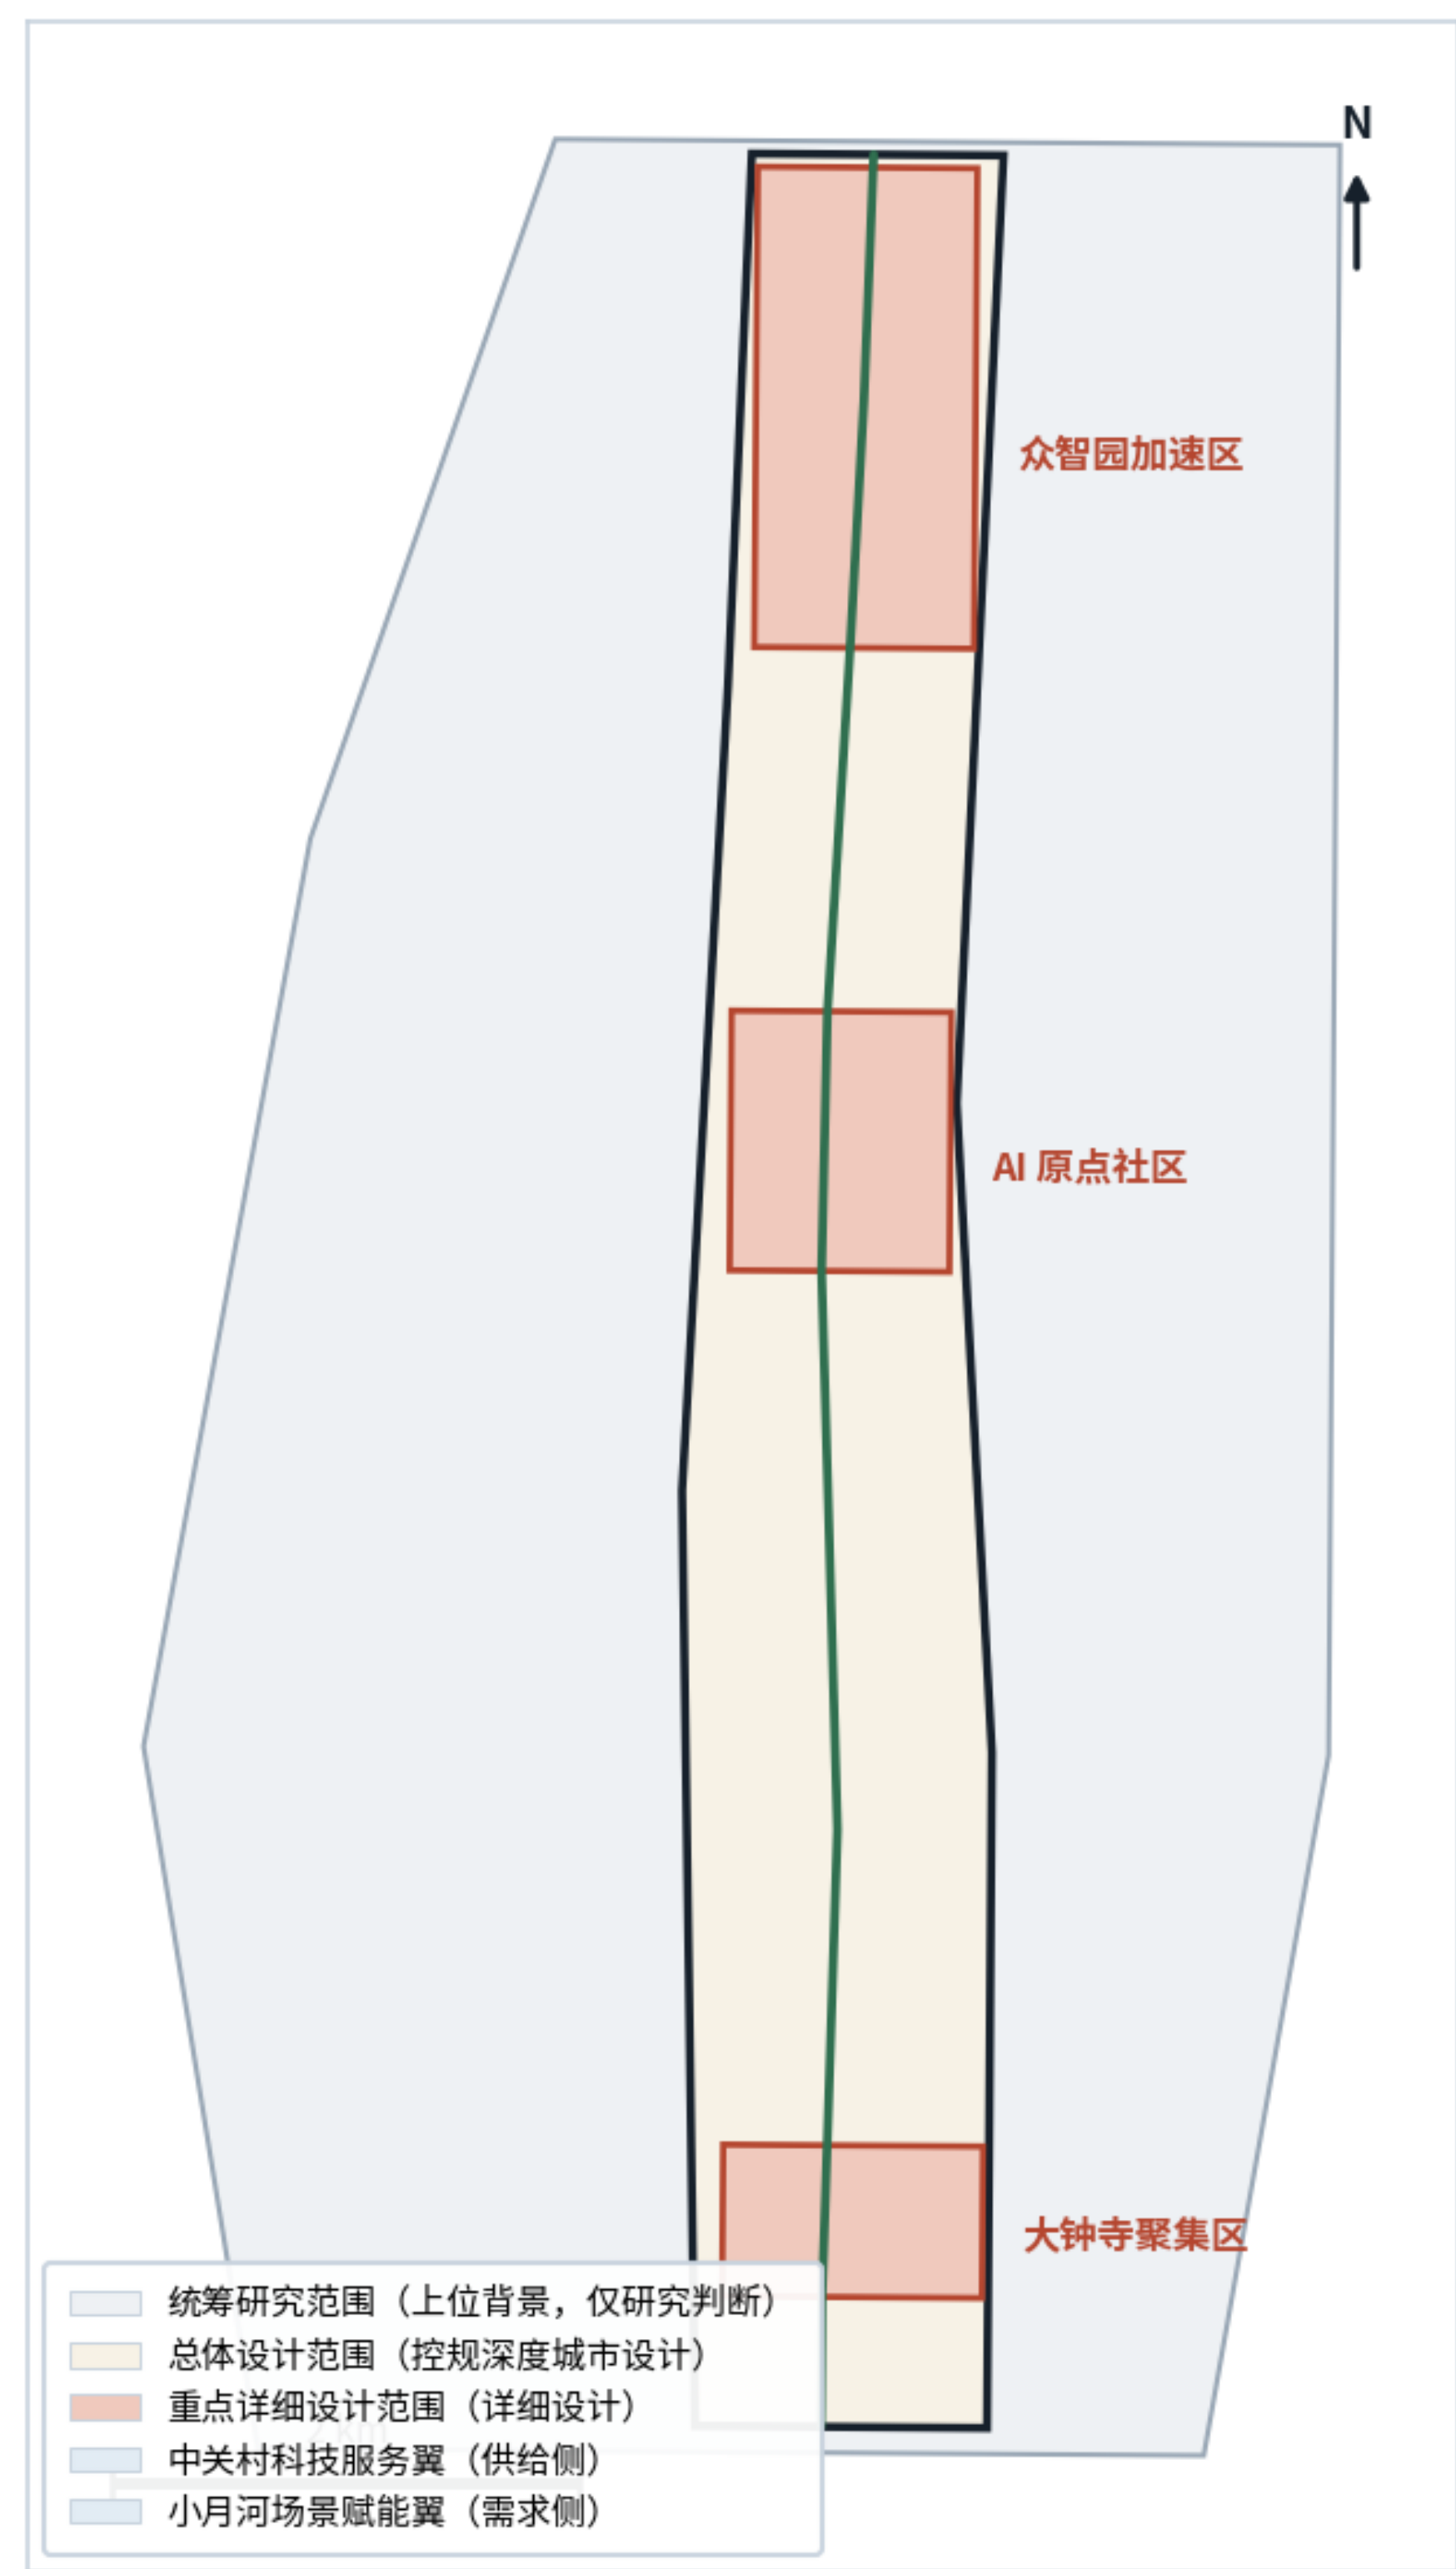

全部范围均为主办方登记的临时粗略替代边界，official_boundary=false，geometry_role=provisional_constraint，boundary_precision=provisional_rough；公告未公开精确红线图件或 GIS 数据集，本图不得作为审批依据、权属结论或精确面积基准。面积在 EPSG:4548 复算并与公告近似值互校。数据来源：geometry/site_boundary.geojson、geometry/key_areas.geojson、geometry/constraints.geojson。

证据链

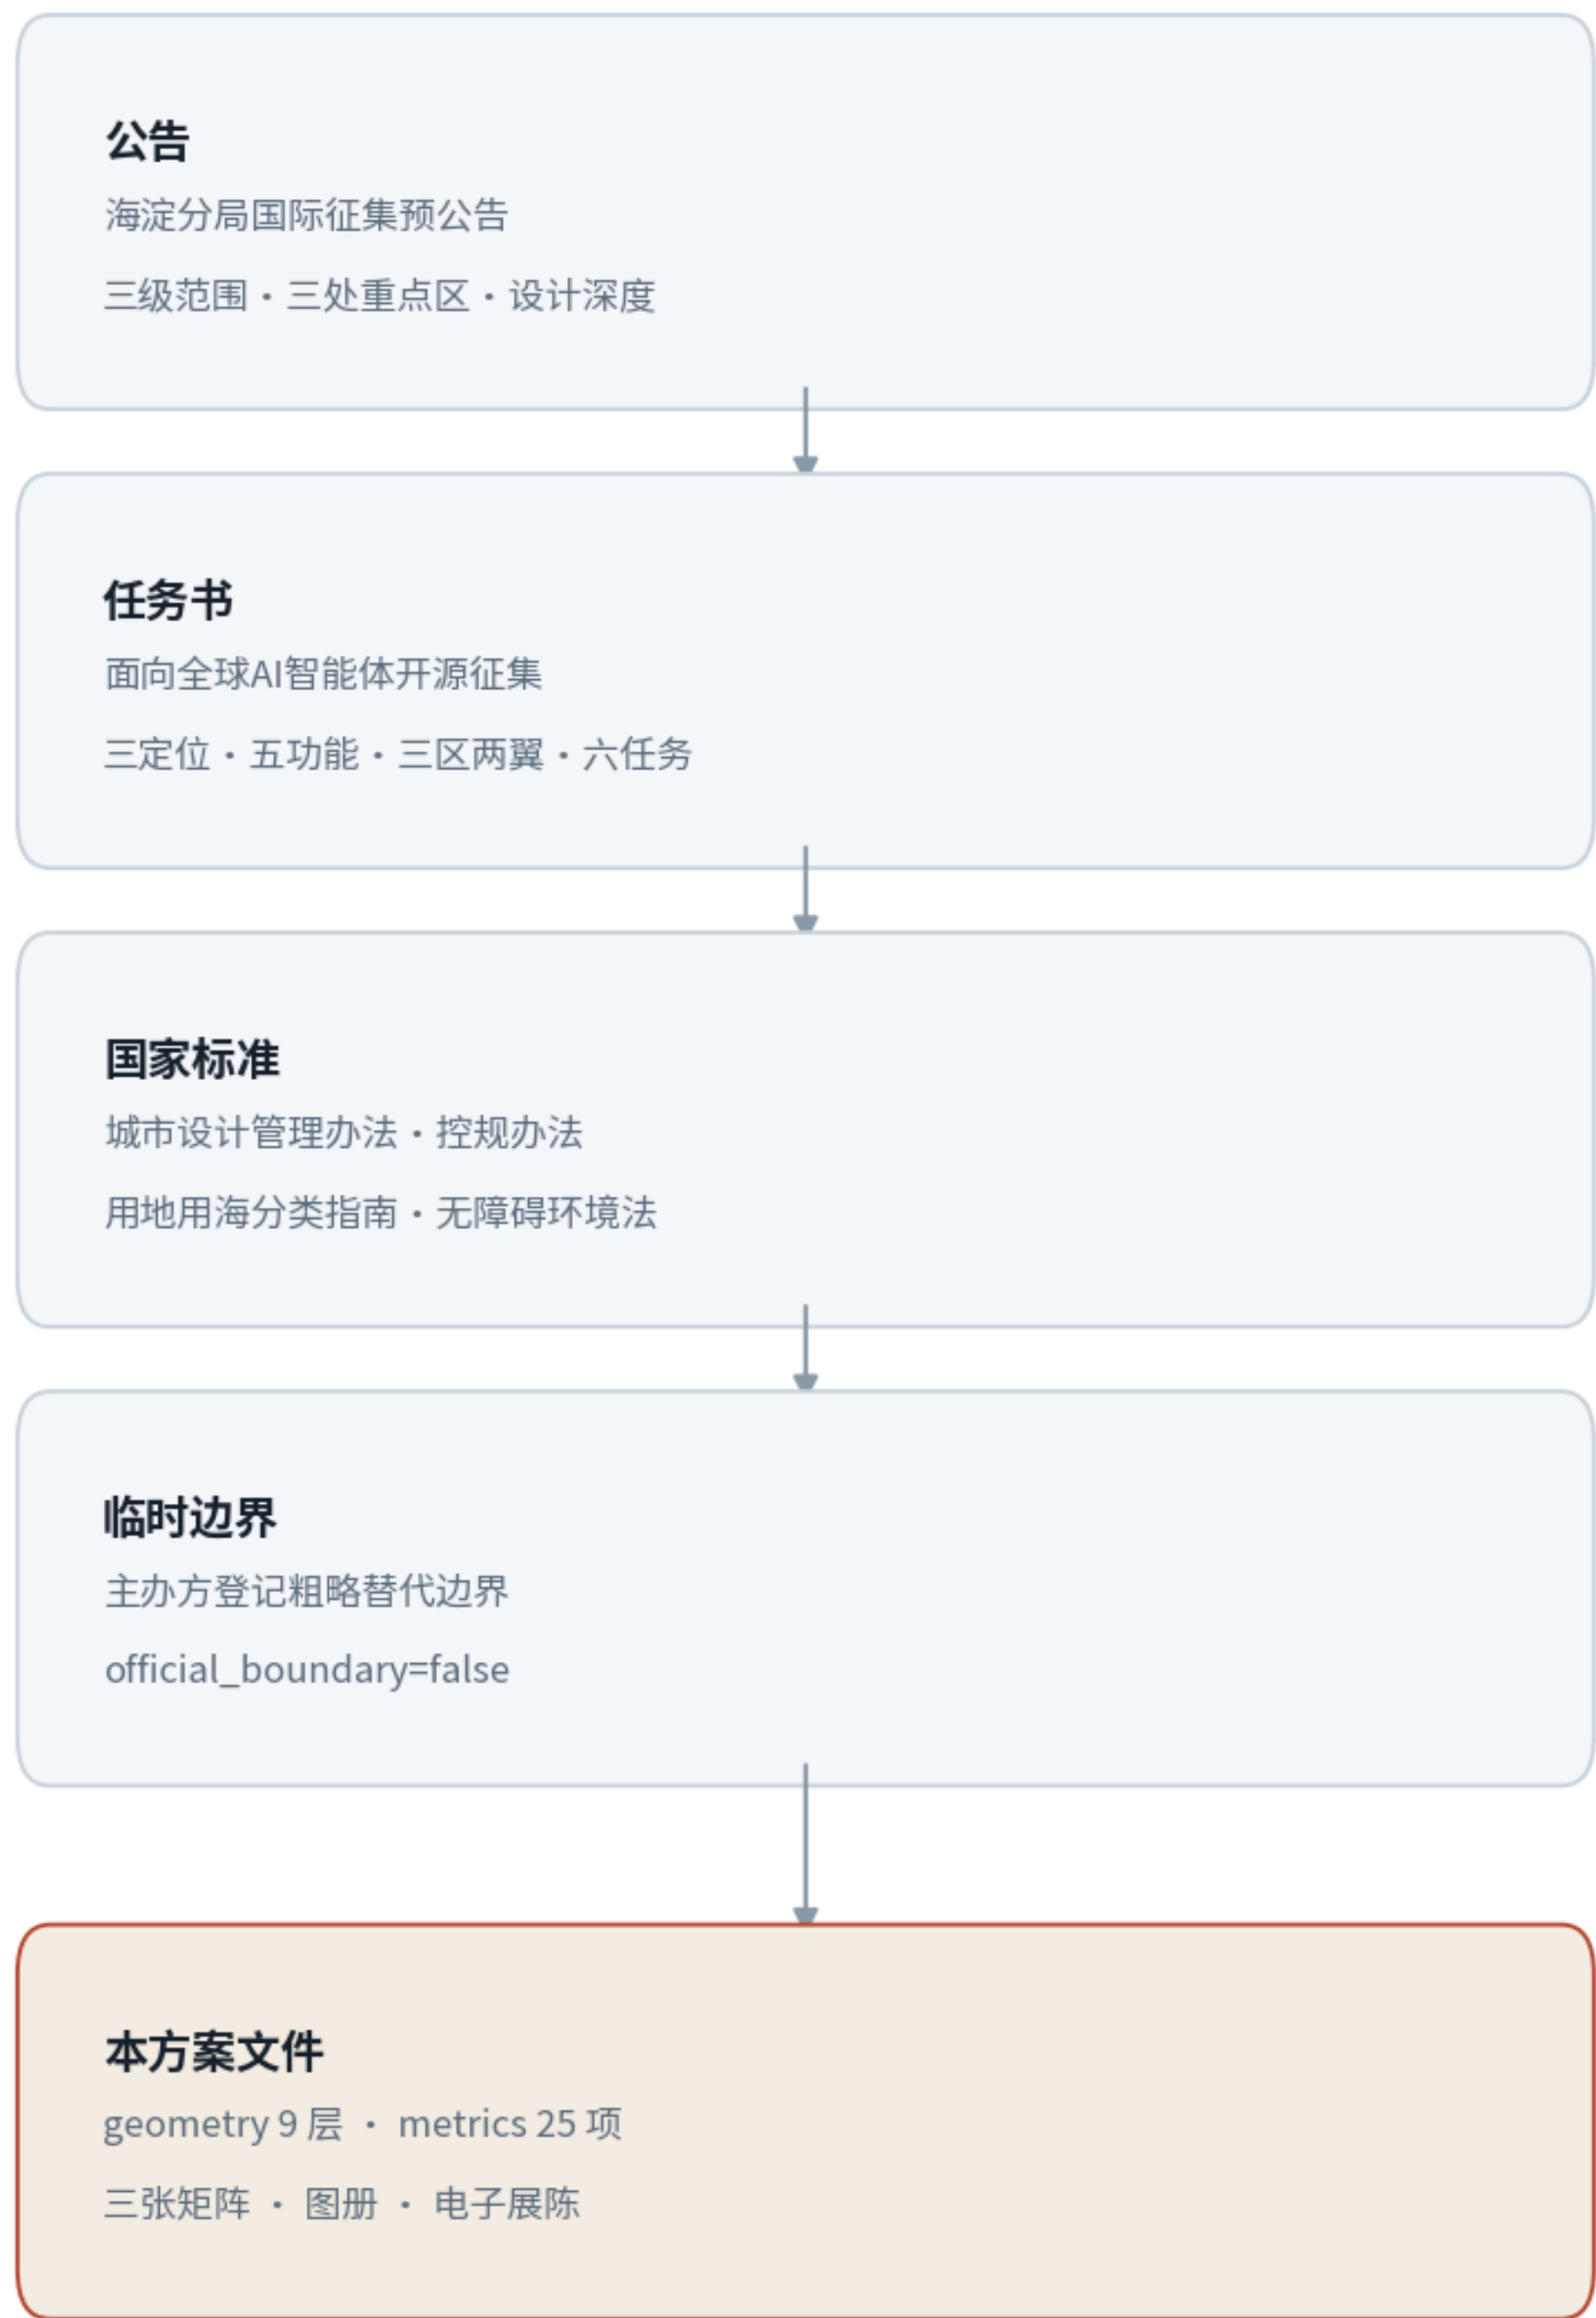

缺口声明

- 官方精确红线：未公开
- 容积率上限：未公开
- 建筑高度上限：未公开
- 建筑密度上限：未公开
- 绿地率下限：未公开
- 退线控制值：未公开
- 可获取官方控制指标数量 = 0

三级范围口径

统筹研究范围	约 43.6 km ²
上位背景，仅作参考判断	
总体设计范围	约 11.4 km ²
控规深度城市设计，本方案主体	
重点详细设计范围	约 368.4 ha
三处重点区，详细设计深度	
众智园加速区	约 192.1 ha
全线自主创新与中试	
AI 原点社区	约 104.3 ha
生活场景与公众参与	
大钟寺聚集区	约 72.0 ha
智能原生消费与接驳验证	

三级范围与证据链总览

统筹研究范围约 43.6 km² 总体设计范围约 11.4 km² 重点详细设计范围约 368.4 ha

为什么是验证长廊，而不是又一个示范园区

- 01 示范展示的是已经成功的结果，验证公开的是正在发生的过程，包括失败。
- 02 园区靠边界聚集企业，长廊靠协议接纳提案，空间可被任何通过验证协议的主体占用。
- 03 示范期结束后设施常被闲置；验证单元设有退出机制，不通过即释放空间重新分配。
- 04 示范的受益者是被选中的企业，验证的受益者是能读到公示看板的所有人。

12 个 AI 场景节点

SCN-01 大钟寺智能原生消费街区 智能原生消费	SCN-04 学院路科教开放实验界面 校城共享验证	SCN-07 原点人才社区智能生活服务 社区智能生活	SCN-10 全民智能健身与无障碍出行 全民健身与无障碍
SCN-02 大钟寺站首末公里接驳验证 低速自动驾驶接驳	SCN-05 AI+健康验证院区 医疗辅助决策验证	SCN-08 京张文化AI导览 文化叙事导览	SCN-11 众智园验证广场与算力开放日 算力与模型开放验证
SCN-03 北下关社区AI照护站 AI+社区照护	SCN-06 AI原点验证广场 公众提案与公示	SCN-09 小月河滨水机器人配送验证 配送机器人	SCN-12 众智园中试与城市治理复盘 城市治理智能体复盘

■ 标记为产业验证场景（共 4 处）
点位为示意位置，不表达设施选址结论；每处均登记受益人群画像、数据边界与人工兜底路径。

三处重点详细设计区

众智园AI自主创新加速区	约 192.1 ha
全栈自主创新与中试：算力开放日、模型验证、城市治理智能体复盘。	
北京AI原点社区	约 104.3 ha
生活场景与公众参与：提案广场、社区照护、智能生活服务与公示看板主站。	
大钟寺AI产业聚集区	约 72.0 ha
智能原生消费与接驳验证：首末公里低速自动驾驶、消费街区场景。	

九段五带空间骨架

纵向九段（自南向北）	横向五带（自西向东）
B1 大钟寺南门户段	W2 中关村科技服务翼界面
B2 大钟寺AI产业聚集区核心区	W1 西侧创新发展带
B3 北下关缝合衔接段	S 京张遗址公园验证主廊
B4 学院路科教衔接段	E1 东侧创新发展带
B5 原点社区南接口段	E2 小月河场景赋能翼界面
B6 北京AI原点社区核心区	
B7 小月河场景赋能段	
B8 众智园验证核心区	
B9 众智园中试与算力段	

九段五带把长条形场地拆成 45 个拓扑无缝无叠的分区单元，是全部用地、指标与分期计算的共同底盘。

百年京张 AI 创新带城市设计国际方案征集 · A3 图册

总体设计范围约 11.4 km² | 45 个概念用地分区, 无缝无叠 | 交换坐标 EPSG:4326, 面积复算 EPSG:4548



用地分区结构（九段五带）

百年京张 AI 创新带城市设计 · 京张智带 · 城市验证长廊 · 概念建议




百年京张AI创新带城市设计·京张智带·城市验证长廊·概念建议



交通慢行与蓝绿公共空间

百年京张AI创新带城市设计·京张智带·城市验证长廊·概念建议

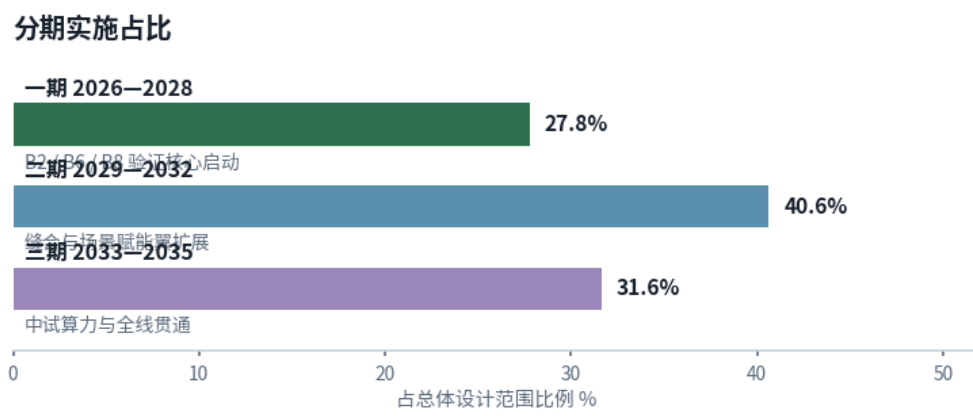

核心指标、分期与证据链

总体设计范围面积	11,412,925 m ²
绿地率	29.41 %
公共空间占比	11.35 %
科研用地面积	2,008,878 m ²
留白用地面积	416,693 m ²
验证主廊长度	9,722.3 m
东西缝合线条数	7
AI 场景节点数量	12
产业验证场景数量	4
重点区域数量	3
一期面积	3,169,220 m ²
可获取官方控制指标	0

- 01 几何复算指标：可由 geometry/ 图层用同一 CRS 独立重算，第三方应得到相同结果。
- 02 假设推导指标：如建筑规模，可信度受假设约束，条目内标注 caveat 与关联假设编号。
- 03 缺口声明指标：如官方控制指标可得数为 0，其存在的意义正是让缺口可见而非被填补。

一期：验证核心启动 在大钟寺、奥林匹克公园、众智园三处重点节点各建成一处验证广场与一段验证主题样板段，跑通提案、验证、公示、转化的完整闭环。 建成验证单元3处；公示项目累计不少于30项；失败公示率100%。	2026—2028 27.77 %
二期：贯通与缝合 打通验证主题南北主线，落地小月河场景赋能并与七条东西链接连接，消除铁路走廊造成的绕行阻隔。 主线连续贯通；缝合连接建成7处；无障碍连续通行面全线覆盖。	2029—2031 40.62 %
三期：缝合与运营转化 完成学院路科教与北下关地区缝合，验证机制由项目制转为常态化运营，转化通道进入日常制度化。 验证结果进入采购或标准的转化率可公开转化；运营主体实现常态化。	2032—2035 31.61 %
三项制度设计	

验证协议

每个验证单元投放前必须签署一份公开协议，写明数据采集范围、保留期限、退出方式与责任主体，协议本身向公众公开。

转化通道

验证结果需有明确采纳路径：纳入政府采购目录、转为地方或团体标准、或形成公开的技术指引，否则验证只是展示。

	综合研究范围产业与未来城市研究 - A1 全链产业链空间需求与未来城市形态讨论 总体设计范围城市更新与控规深度城市规划 - 九段五带用地分区、慢行骨架、蓝绿结构、风貌原则 重点区域详细设计 - 三处重点片区详细设计与验证单元配置 AI 创新生态、人才画像与 AI+ 场景 12 个场景节点、受益人群画像、数据边界矩阵 更新项目清单、实施政策与分期计划 - 三级项目清单、三项制度设计、三期计划 指标体系与合规 25 项指标、面积复算、合规矩阵与缺口声明
	包内证据清单
23	compliance_matrix.json 公告必选任务与智能体任务逐条映射
9	standard_matrix.json 引用的国家与地方标准、法规、政策
15	design_depth_matrix.json 设计深度条目与对应章节、图则
25	metrics.json 指标条目，其中 23 项已知、2 项声明缺口
9	geometry/.geojson 图面，EPSG:4326 交换、EPSG:4548 复算
5	assets/figures/*.png 图示，中英双版本各一套

A-BOUNDARY-001	全部面积基于临时粗略替代边界，官方红线公开后整体复算。
A-COVERAGE-001	建筑基底由假定基底覆盖率生成，非现状测绘也并非控规结论。
A-MOBILITY-001	慢行与缝合线位为概念线位，跨铁路方须结合铁路与市政条件深化。
A-CONTROLS-001	容积率、高度、密度、绿地率、退线五项官方指标缺失，不做反推。

仅为概念建议，不构成控规结论、审批结论、权属结论或实施承诺。官方边界与指标公布后须整体复算。

■ 本图册全部空间与数量结论为概念建议与参考方案, 可供专业团队深化研究。

■ 不构成控规结论、审批依据、权属边界、建设规模承诺或财政承诺。

■ 未使用非公开、内部或涉密数据，未使用个人隐私数据，未虚构企业名单、投资额与产值。

■ 官方精确边界与控制指标公布后，须按同一口径整体复算，而非局部修补。