


Site Overview - Jing-Zhang Warp-Weft Belt Urban Design

Overall design area ~11.4 km2 - Beijing Haidian District - formal submission concept V1.0

Provisional boundary - conceptual suggestion

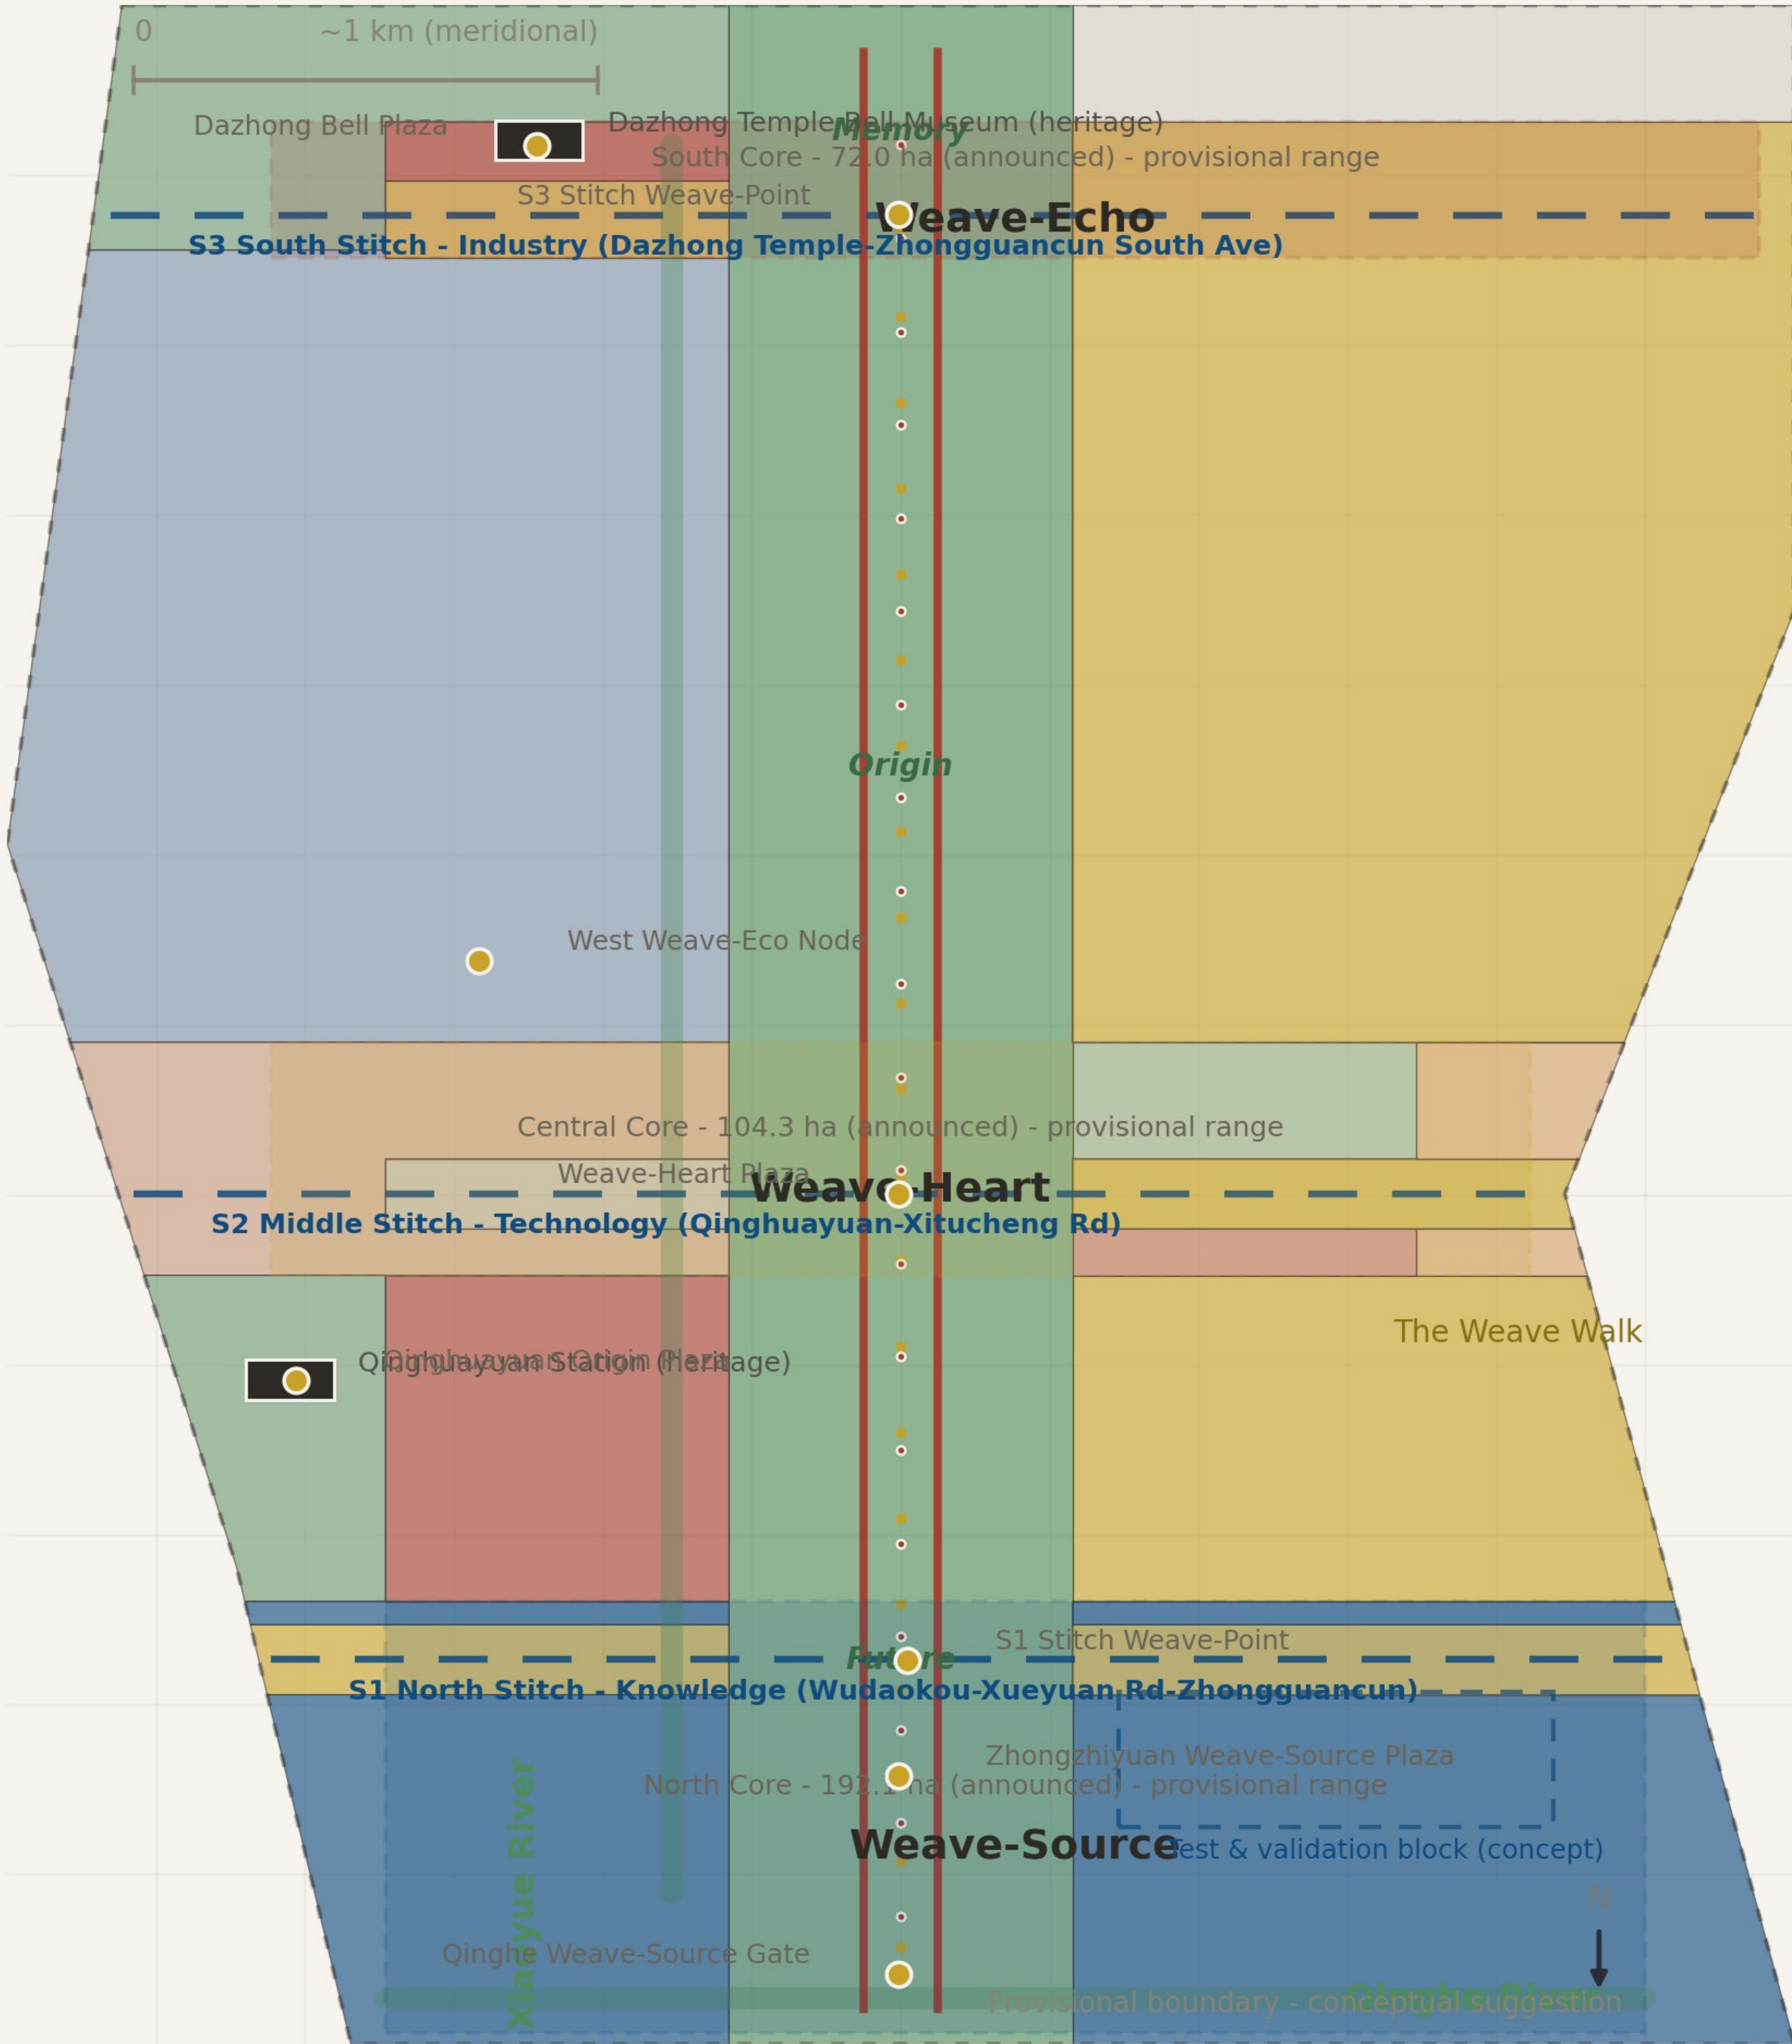

LEGEND

- Jing-Zhang heritage park greenway (warp line, code 1401)
- Double-rail vocabulary - centennial track memory (cultural interpretation)
- Weft stitch corridors S1/S2/S3 (knowledge / technology / industry)
- Qinghe / Xiaoyue rivers (blue-green secondary lines)
- Public-space weave points / plazas
- AI scenario weave points (concept)
- The Weave Walk (gold, dashed)
- Pilgrimage landmarks L01-L05
- Provisional boundary (low-contrast dashed, not an official redline)
- Test & validation block (concept)

THREE-LEVEL SCOPE


- Overall research scope - 43.6 km2
- Overall design scope (this map) - 11.4 km2
- Key areas (three cores) - 368.4 ha

Region system: Weave-Source (North) - Weave-Heart (Central) - Weave-Echo (South) - Weave-Capital (East wing) - Weave-Eco (West wing).
Source: submission package geometry/*.geojson + metrics.json - schematic projection (meridional stretch, not to scale) - display coords EPSG:4326, areas recomputed in EPSG:4548 - site boundary and key areas are provisional (provisional_constraint), not official redlines - all spatial arrangements are conceptual suggestions.

Land-Use Structure - Warp-Weft Belt (MNR Codes)

12 design land-use categories - 23 seamless parcels partition the design area

Provisional boundary - conceptual suggestion

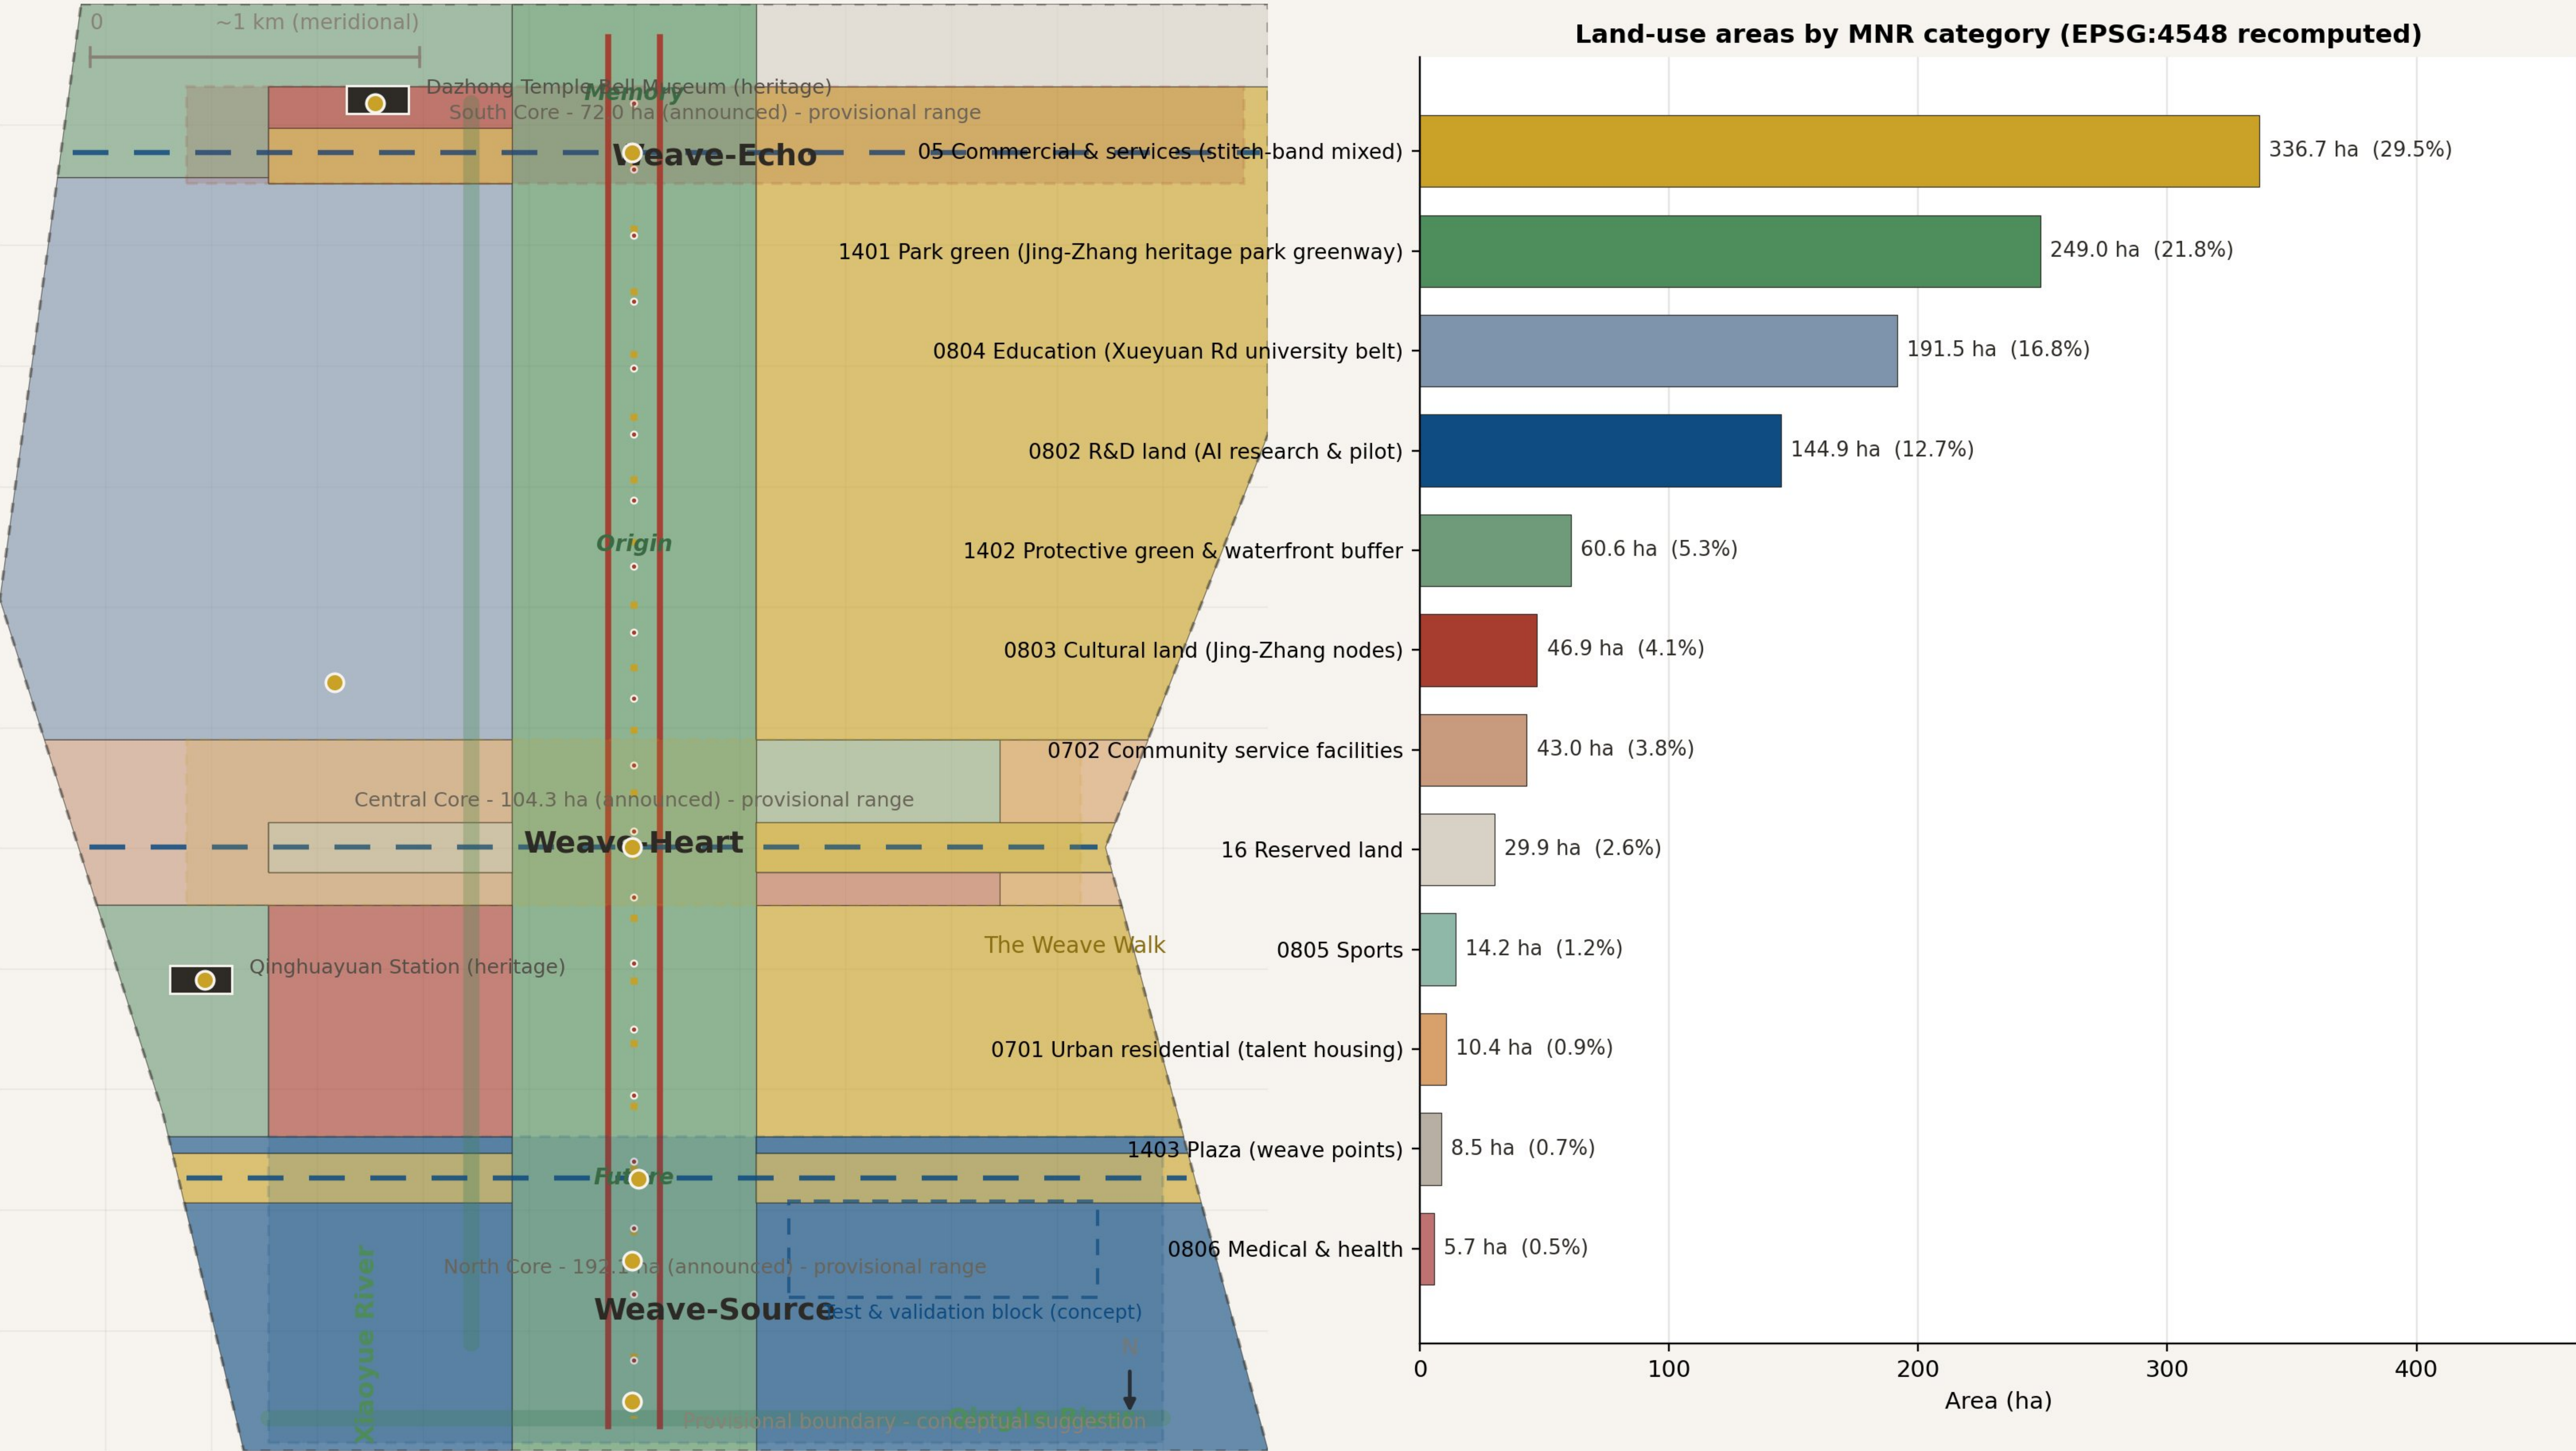


Land-use codes follow the MNR classification list; the 23 parcels cover the design area seamlessly. All land-use assignments are design concepts - statutory land-use status remains unknown (status=unknown) until confirmed against the statutory plan.
Source: submission package geometry/*.geojson + metrics.json - schematic projection (meridional stretch, not to scale) - display coords EPSG:4326, areas recomputed in EPSG:4548 - site boundary and key areas are provisional (provisional_constraint), not official redlines - all spatial arrangements are conceptual suggestions.

Key Areas & Pilgrimage Landmarks

Key Areas & Pilgrimage Landmarks - Three Cores

Key areas: Weave-Source / Weave-Heart / Weave-Echo - all provisional ranges, conceptual suggestions
Provisional boundary - conceptual suggestion

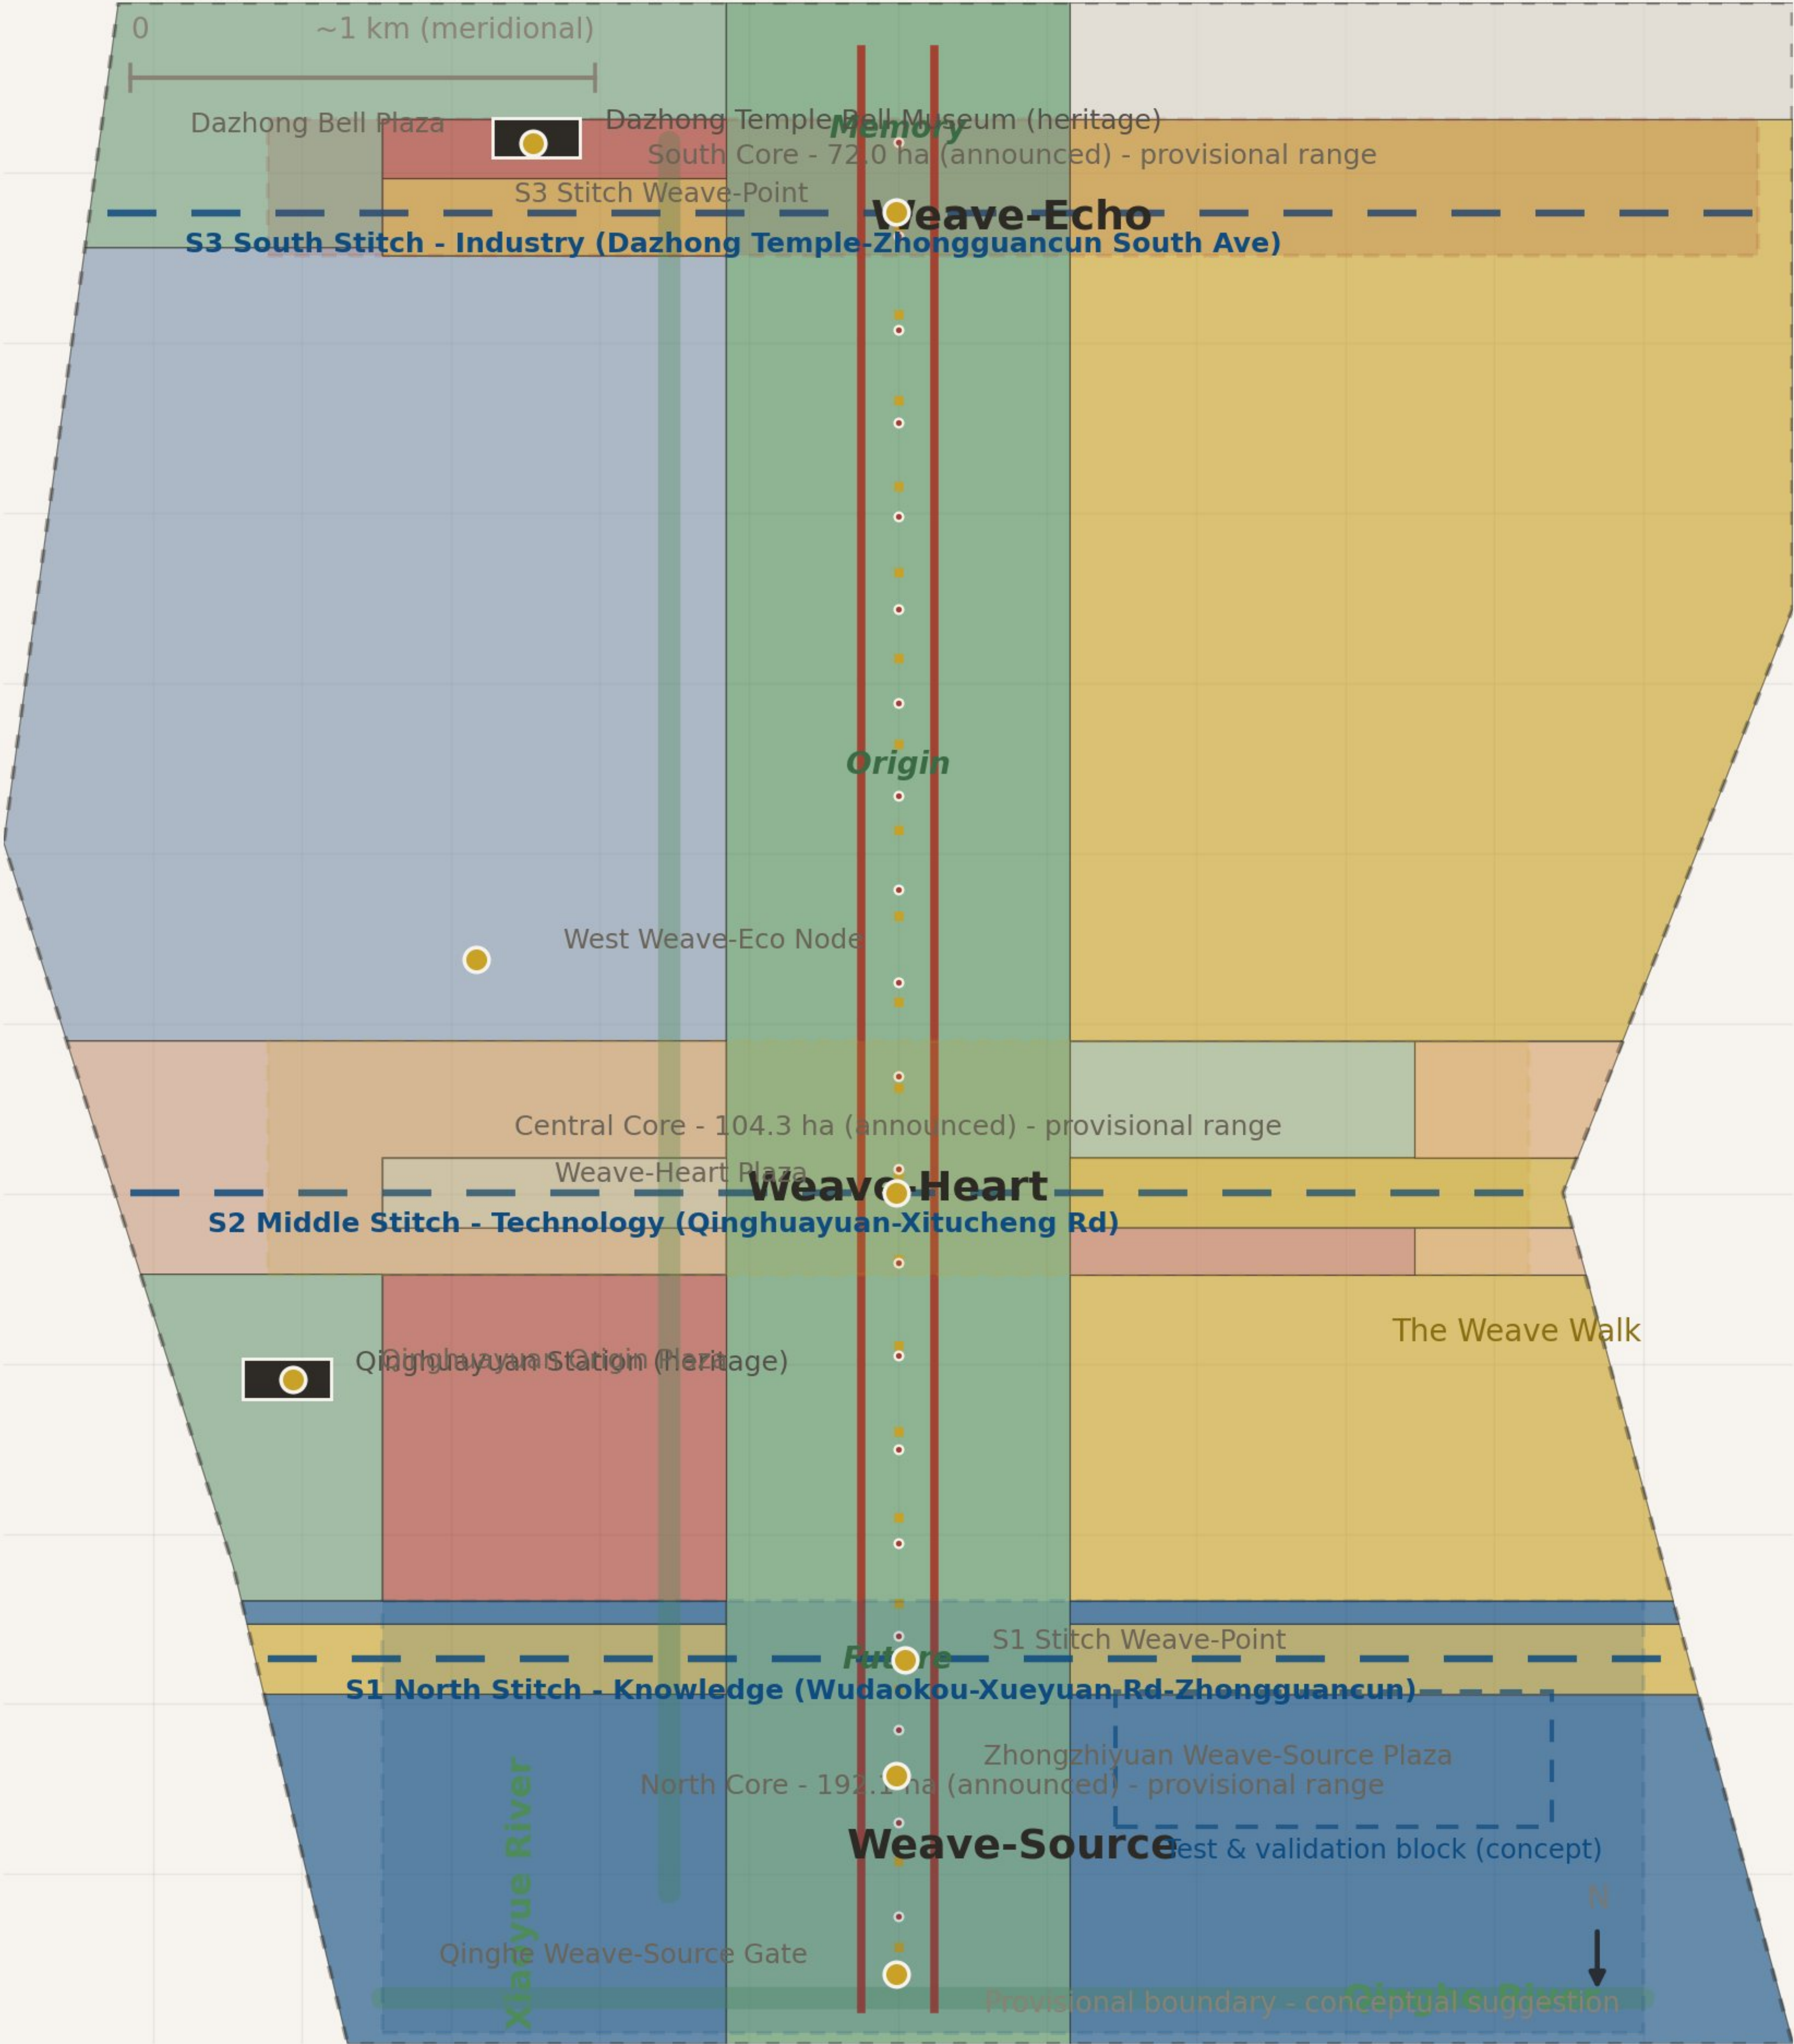

THREE KEY AREAS - provisional ranges (announced areas)

Weave-Source (Zhongzhiyuan) - North Core

Announced area: 192.1 ha (announced) | Phase: P3

AI self-reliance acceleration: shared compute, pilot & test-verification blocks
Provisional rough range (provisional_constraint) - not an official polygon.

Weave-Heart (AI Origin Community) - Central Core

Announced area: 104.3 ha (announced) | Phase: P2

Talent + community + cultural-origin engine of the AI ecosystem
Provisional rough range (provisional_constraint) - not an official polygon.

Weave-Echo (Dazhong Temple) - South Core

Announced area: 72.0 ha (announced) | Phase: P1 + P3

AI industry cluster + AI-native consumption scene
Provisional rough range (provisional_constraint) - not an official polygon.

PILGRIMAGE LANDMARKS - 5 sites, all conceptual suggestions

- L01 Weave-Origin - former Qinghuayuan Station**
Memory x AI origin community: commemorative display, digital narrative, origin ruler.
- L02 Weave-Heart Plaza - Wudaokou**
Railway-crossing memory x AI vibrancy plaza; Weavers' Wall honor board.
- L03 Herringbone Line - Earth Weave - mid-park, Jing-Zhang heritage park**
60-degree herringbone geometry as land art - cultural homage to Zhan Tianyou, not a historical reconstruction.
- L04 Bell-Web - Dazhong Temple Bell Museum**
Digitized bell AI soundscape art + data-sensing installation.
- L05 Weave-Source Gate - north end of Zhongzhiyuan, near Qinghe**
City gateway & innovation display node with a future-milestone clock.




PHASING (conceptual logic only)

- P1 Near 0-3 y: scenario pop-ups, waystations, slow-traffic links.
- P2 Mid 3-5 y: demonstration weave points, stitch pilots, Weave-Heart Plaza.
- P3 Far 5-10 y: full network, industrial scale, regular international events.

Timeline anchors along the warp line: Memory - Origin - Future. All three key areas are provisional ranges located from the official announcement text; rectangular edges must not be read as parcel or road redlines.
Source: submission package geometry/*.geojson + metrics.json - schematic projection (meridional stretch, not to scale) - display coords EPSG:4326, areas recomputed in EPSG:4548 - site boundary and key areas are provisional (provisional_constraint), not official redlines - all spatial arrangements are conceptual suggestions.

Mobility & Blue-Green Network

Warp-line greenway + weft stitch corridors + Qinghe / Xiaoyue blue-green secondary lines + weave points
Provisional boundary - conceptual suggestion

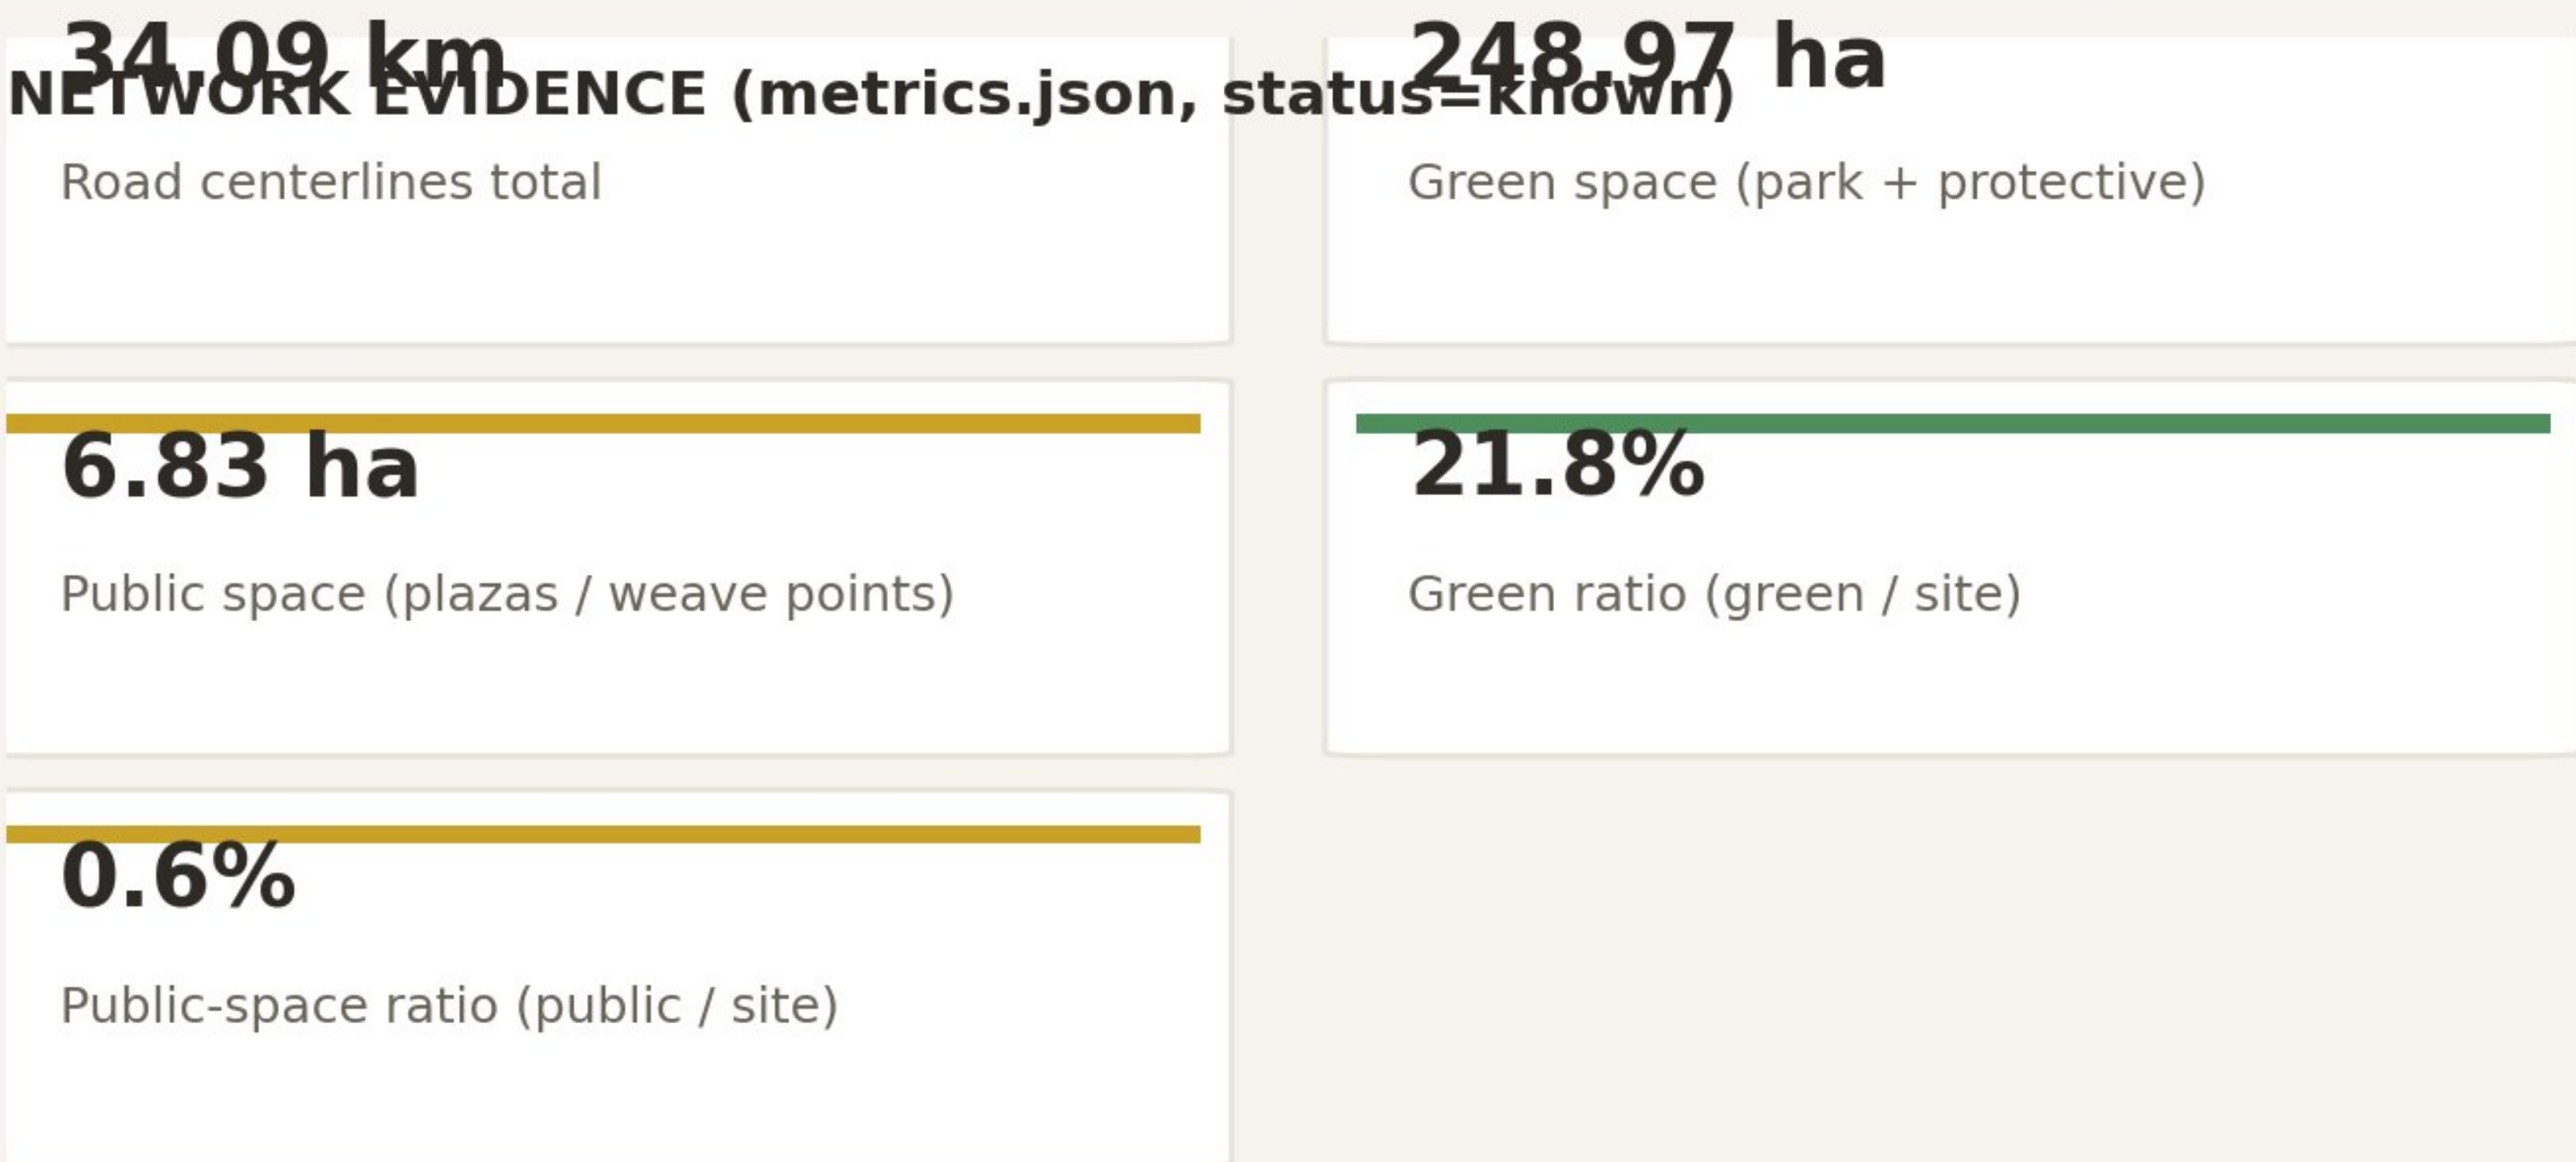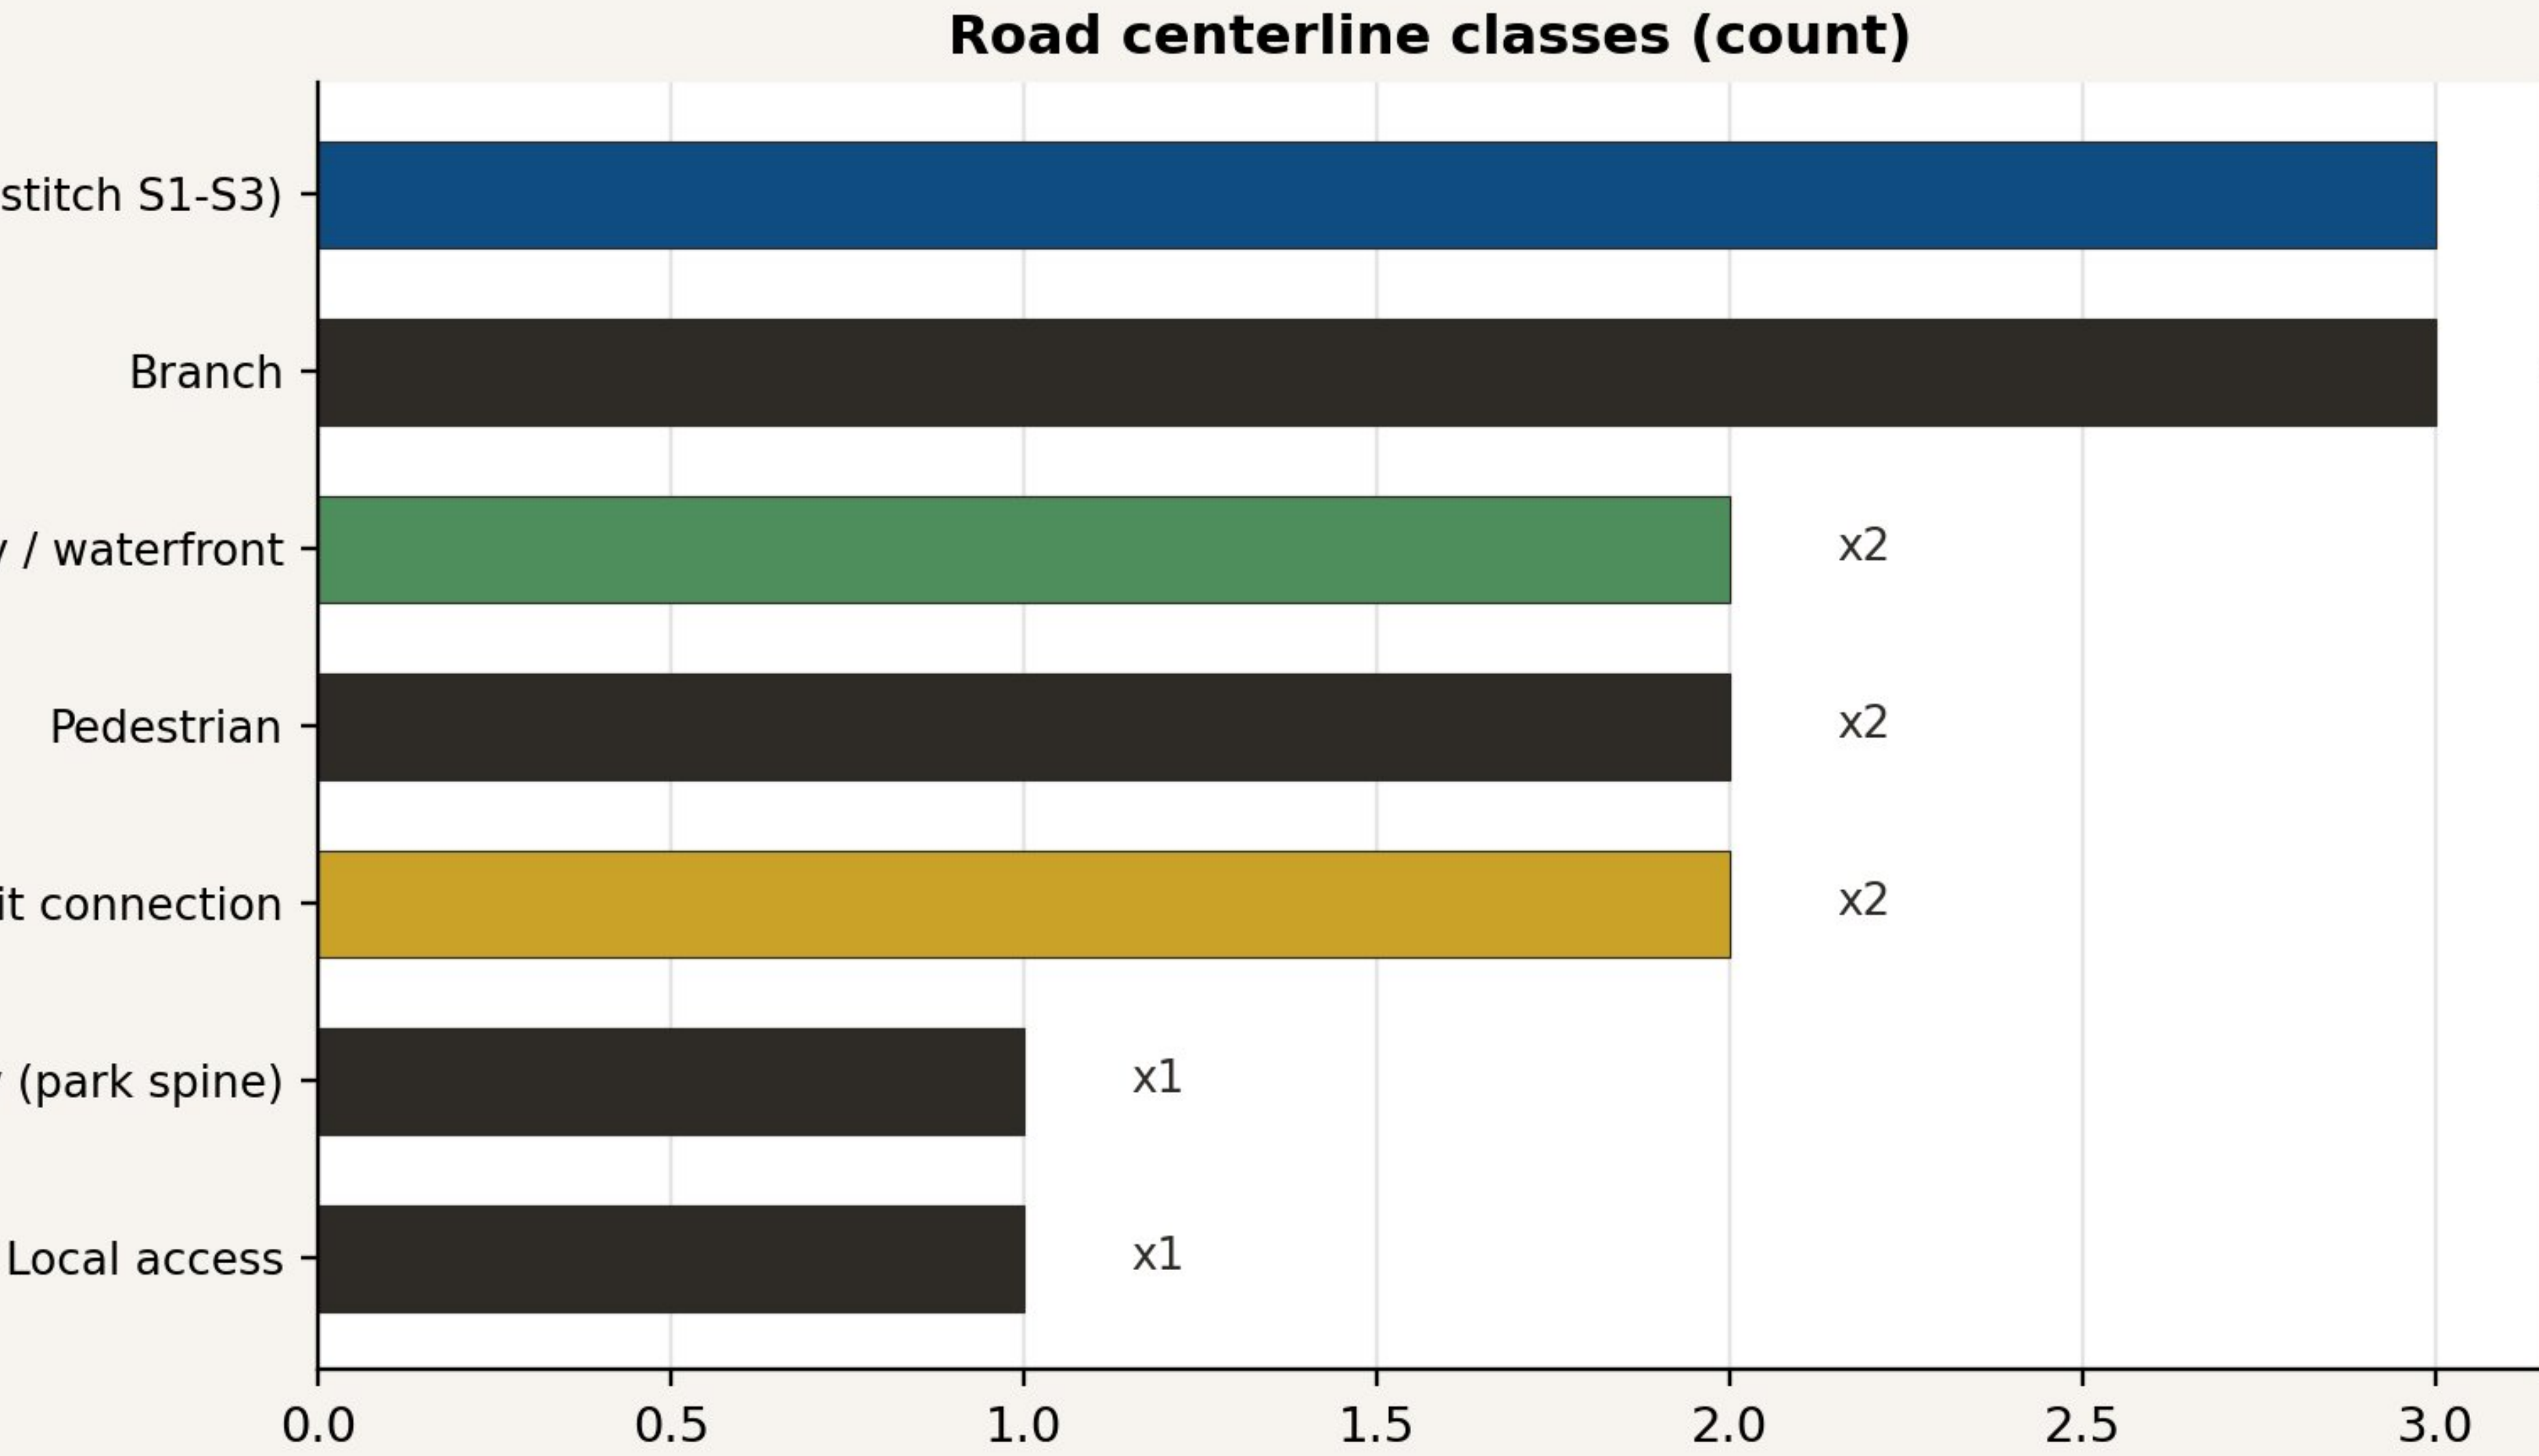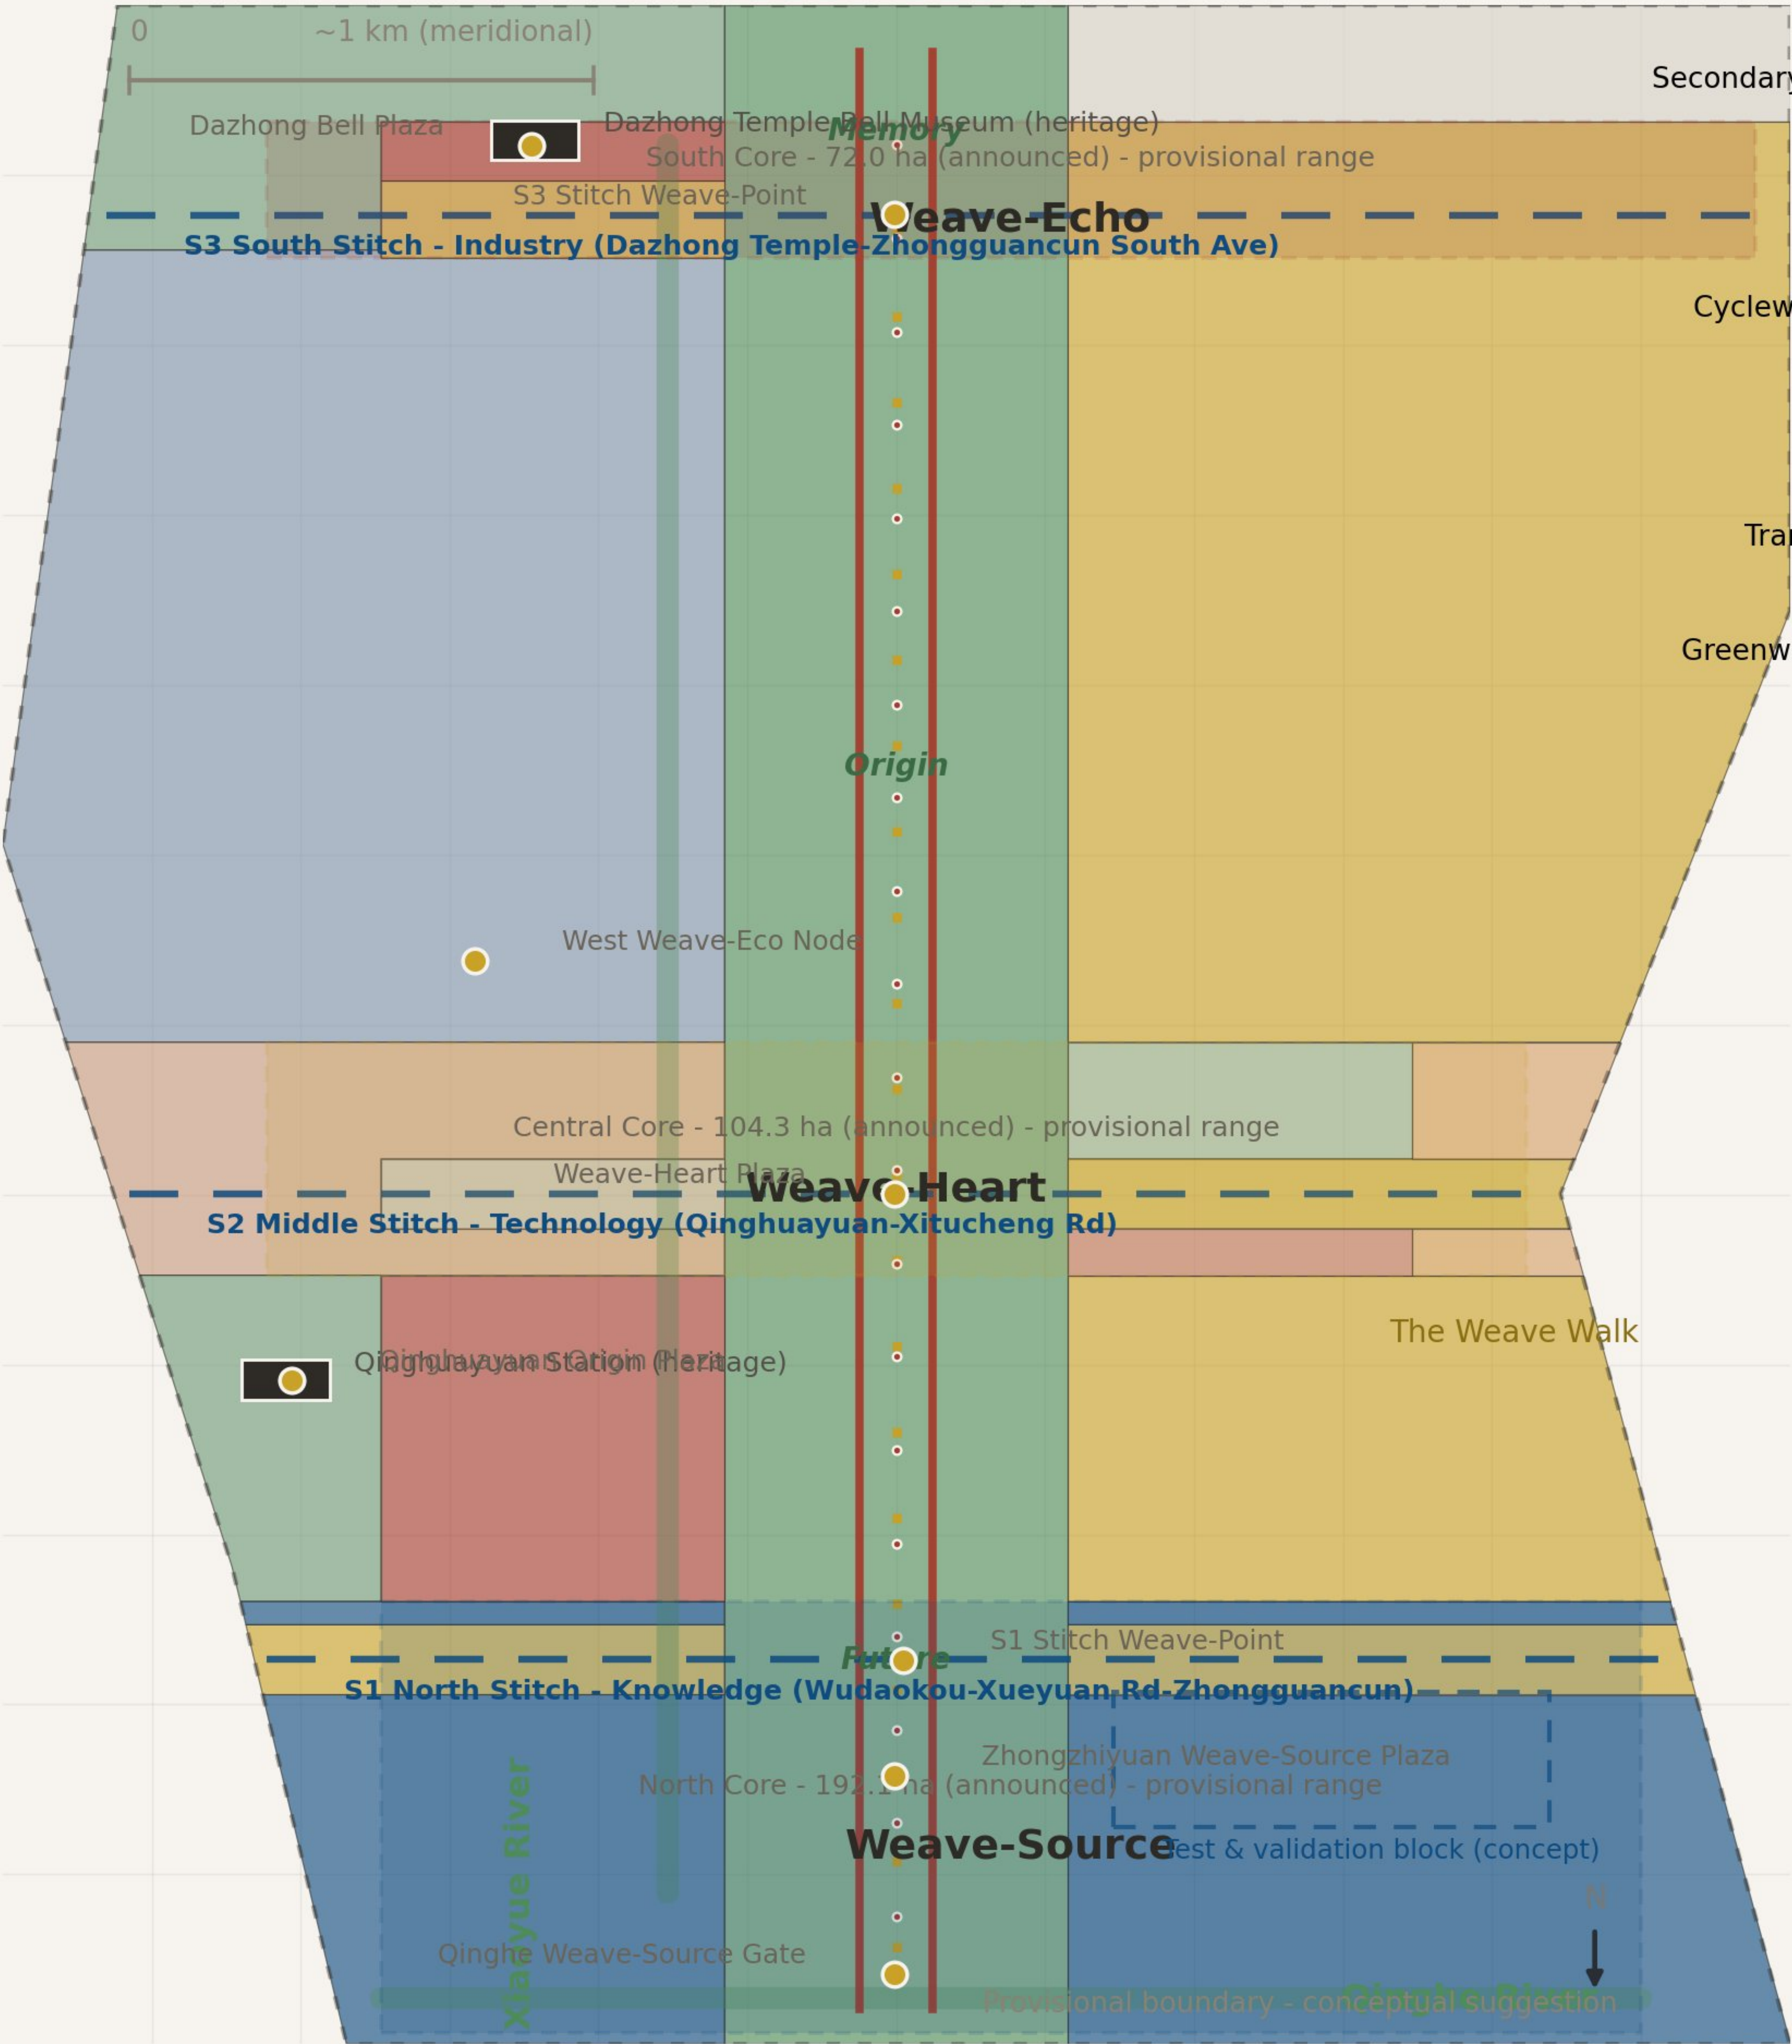

Blue-green network = 1 warp line (greenway) + 2 rivers (Qinghe, Xiaoyue) + 3 weft stitch corridors + N weave points. Waterfront blue lines per the water authority (status=unknown).


Slow-traffic priority along the warp-line greenway; weave points every 300-500 m (conceptual spacing, not a binding standard); transit links at Wudaokou and Dazhong Temple stations (TOD-style concept).
Source: submission package geometry/*.geojson + metrics.json - schematic projection (meridional stretch, not to scale) - display coords EPSG:4326, areas recomputed in EPSG:4548 - site boundary and key areas are provisional (provisional_constraint), not official redlines - all spatial arrangements are conceptual suggestions.

Core Metrics - Evidence Sheet

All values read from metrics.json (status=known), recomputed from geometry layers in EPSG:4548

Provisional boundary - conceptual suggestion

11,412,825 m2 Site area (overall design) = 1,141.28 ha ~ 11.41 km2	21.8% Green ratio green area / site area	0.6% Public-space ratio public space / site area	248.97 ha Green space park green + protective green	6.83 ha Public space plazas / weave points
20.46 ha Building footprint 79 footprints, EPSG:4548	34.09 km Road centerlines incl. slow-traffic & transit links	23 Land-use parcels 12 MNR categories	3 Key areas three cores (provisional)	3 Implementation phases near / mid / far term

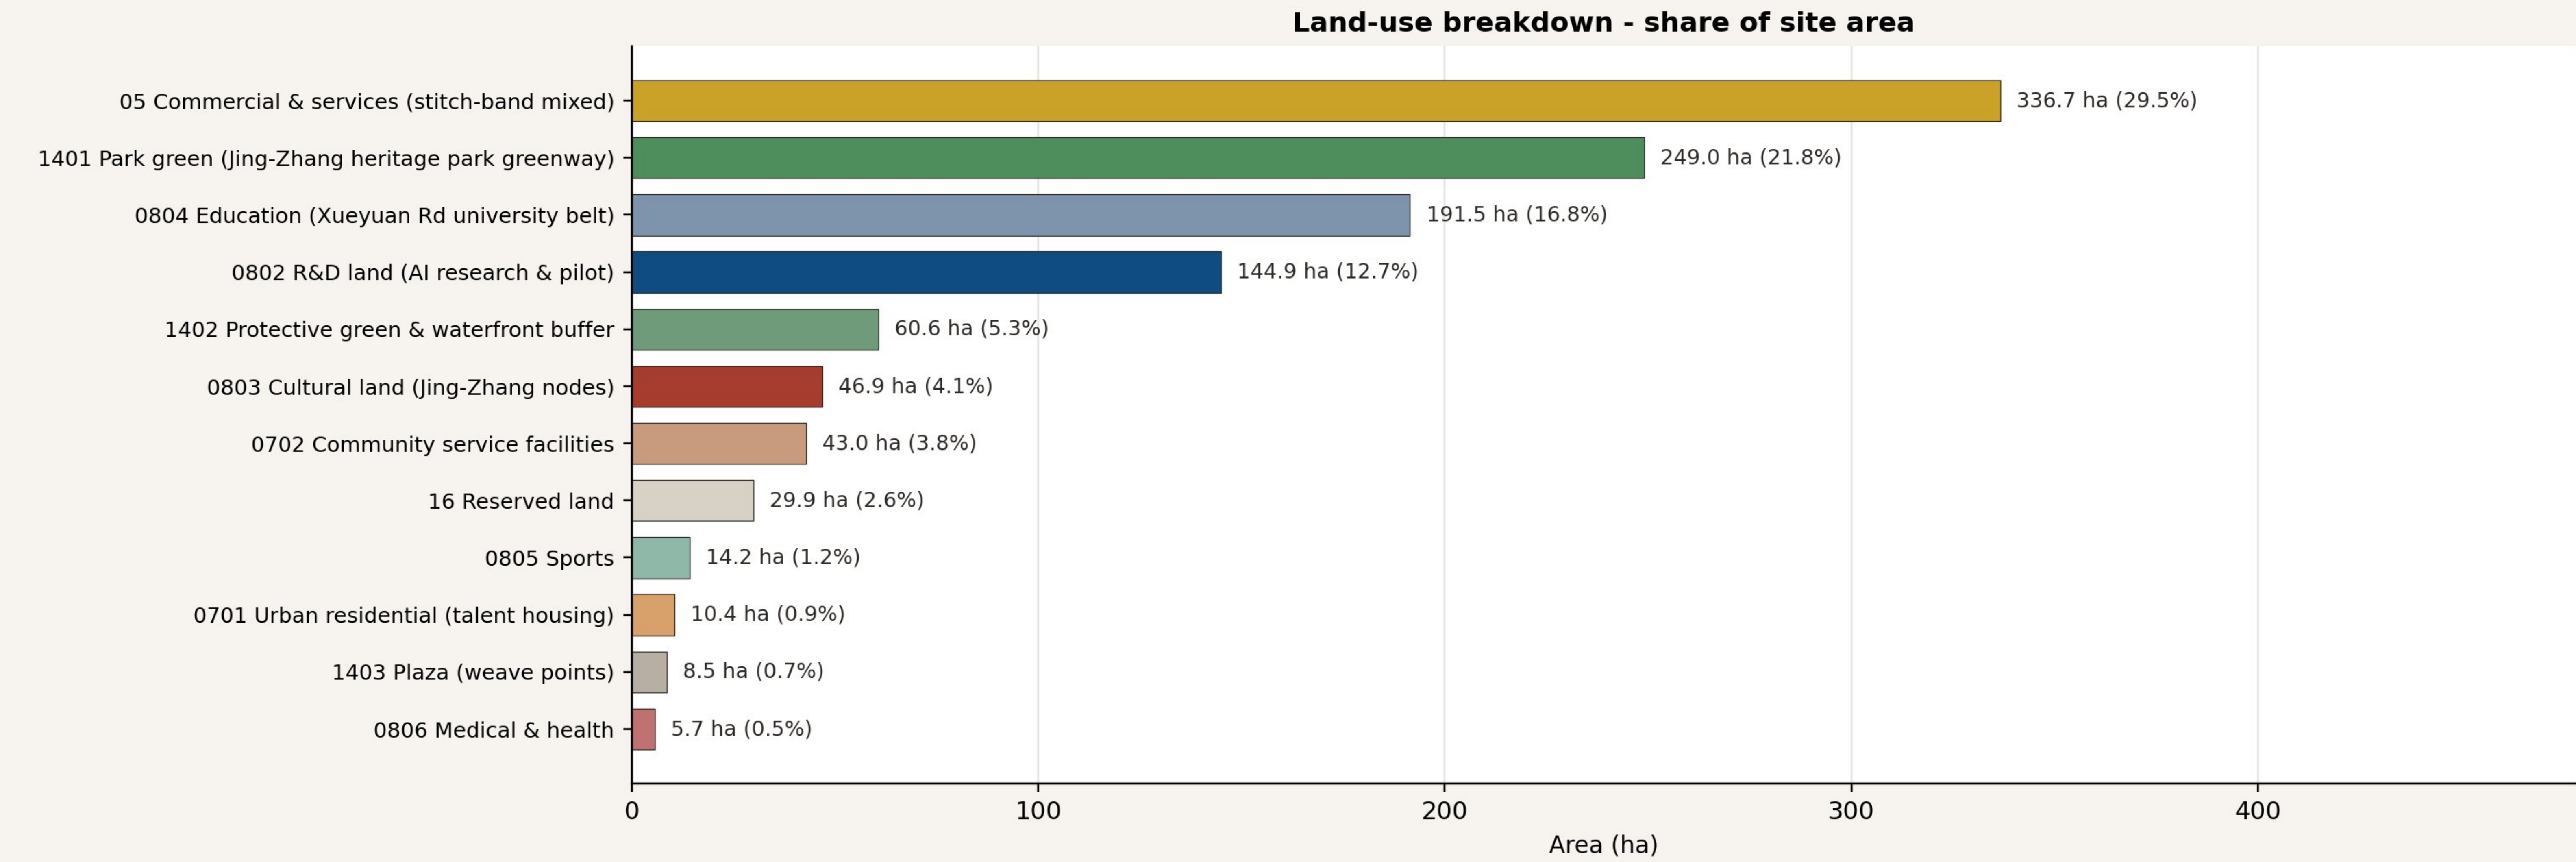

Display text and machine-readable data-value are kept consistent (tolerance 1e-6); areas recomputed under EPSG:4548 from the submission geometry layers.
Source: submission package geometry/*.geojson + metrics.json - schematic projection (meridional stretch, not to scale) - display coords EPSG:4326, areas recomputed in EPSG:4548 - site boundary and key areas are provisional (provisional_constraint), not official redlines - all spatial arrangements are conceptual suggestions.

COMPLIANCE RED LINE

Floor-area ratio (FAR): status=unknown

No public statutory control basis; no value shown. Development intensity follows the statutory plan.

Average building height: status=unknown

Height remains a design concept (conceptual suggestion); must be verified against the statutory plan.

Both values deliberately omitted from figures and metrics - per design-system compliance red line.