

京张智市

JINGZHANG BAZAAR

百年京张 AI 开源市集带 · A0 展板


一街三市 · 两翼十二摊 · 摊位协议 · 双市集

京张智市 · 总体概念结构

JINGZHANG BAZAAR · Overall Concept

一街三市、两翼十二摊：把百年京张组织为开源市集城市（概念建议）

概念图解：城市即仓库 × 双市集

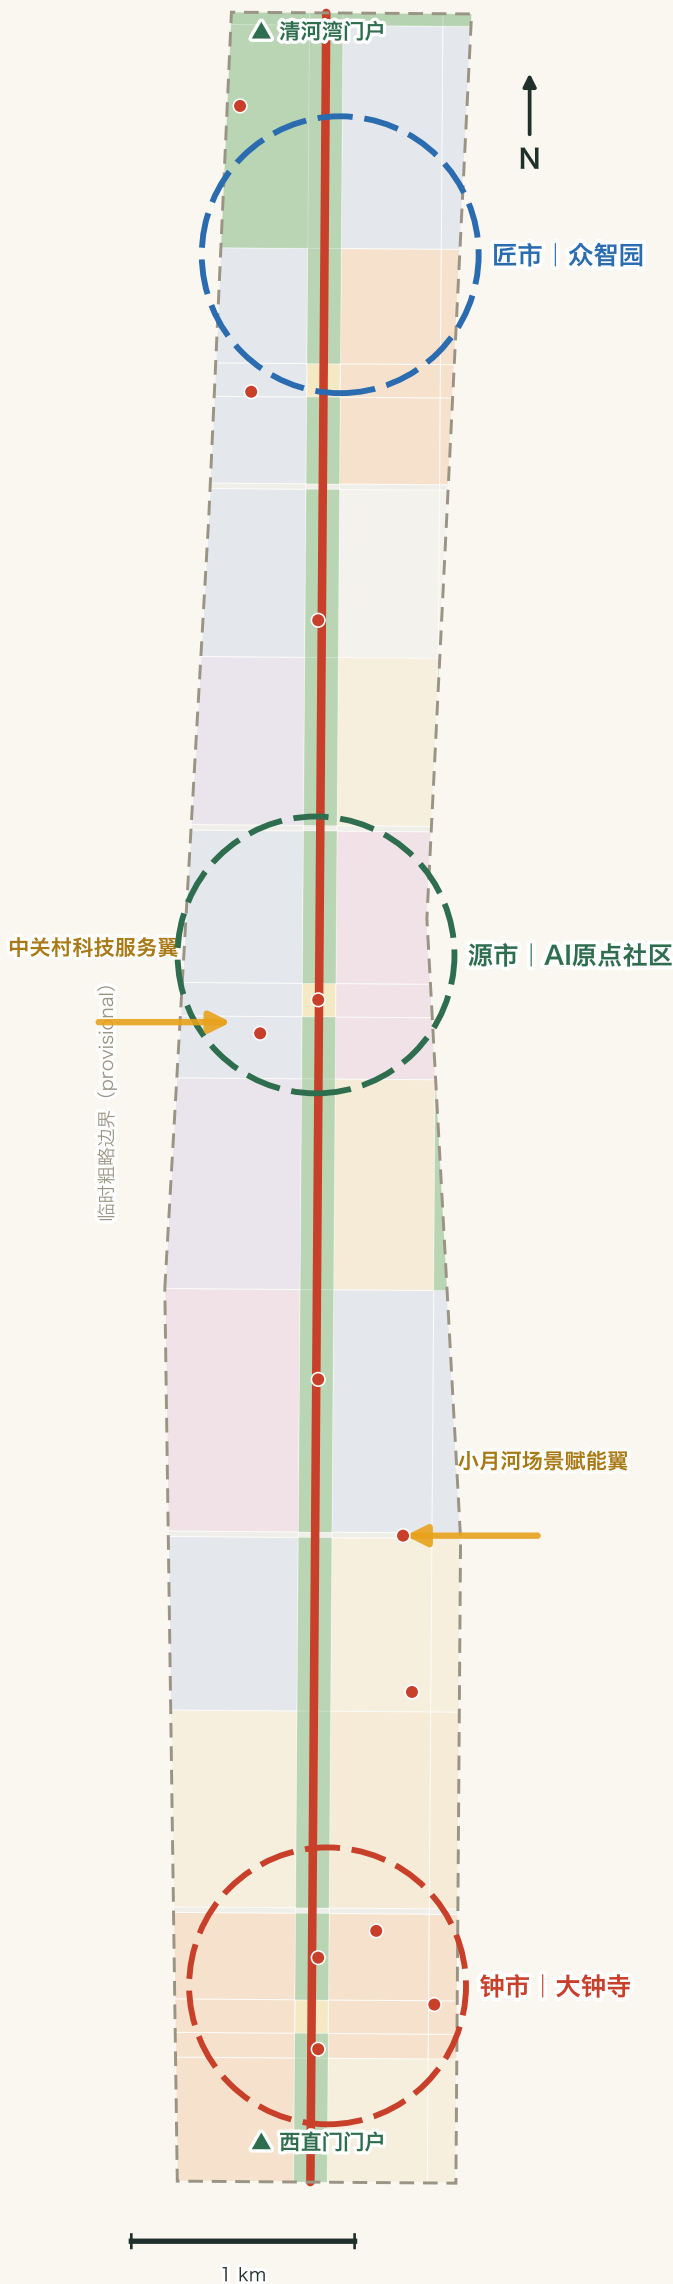

图例




摊位索引 (①-⑫ 见场景卡)

- | | |
|---------|---------|
| ① 班车摊 | ⑦ 数字河长 |
| ② 公平秤 | ⑧ AI 茶馆 |
| ③ 开源之钟 | ⑨ 向导智能体 |
| ④ 学徒工坊 | ⑩ 灵感市集 |
| ⑤ AI 夜市 | ⑪ 通学径 |
| ⑥ 首发摊 | ⑫ 算力驿站 |


空间结构与用地布局

Spatial Structure and Land Use

85 个概念地块无缝覆盖临时边界；三层范围逐级传导（概念建议，非法定用地控制）

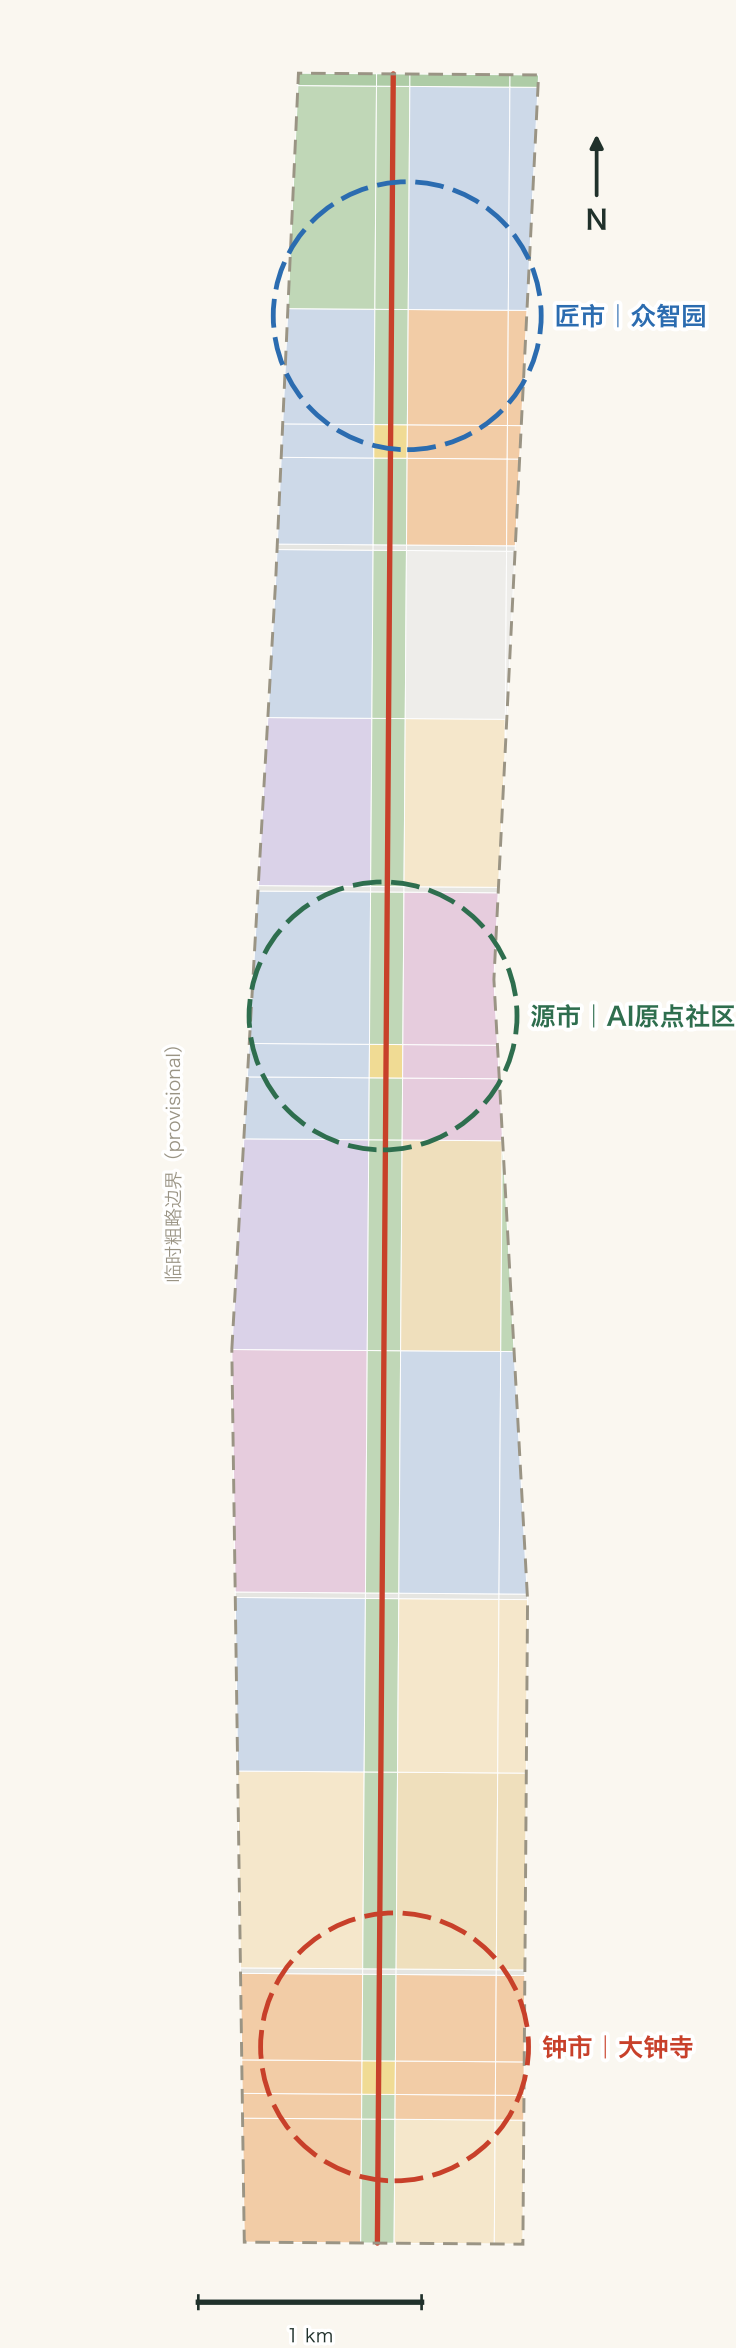

用地构成（EPSG:4548 复算）

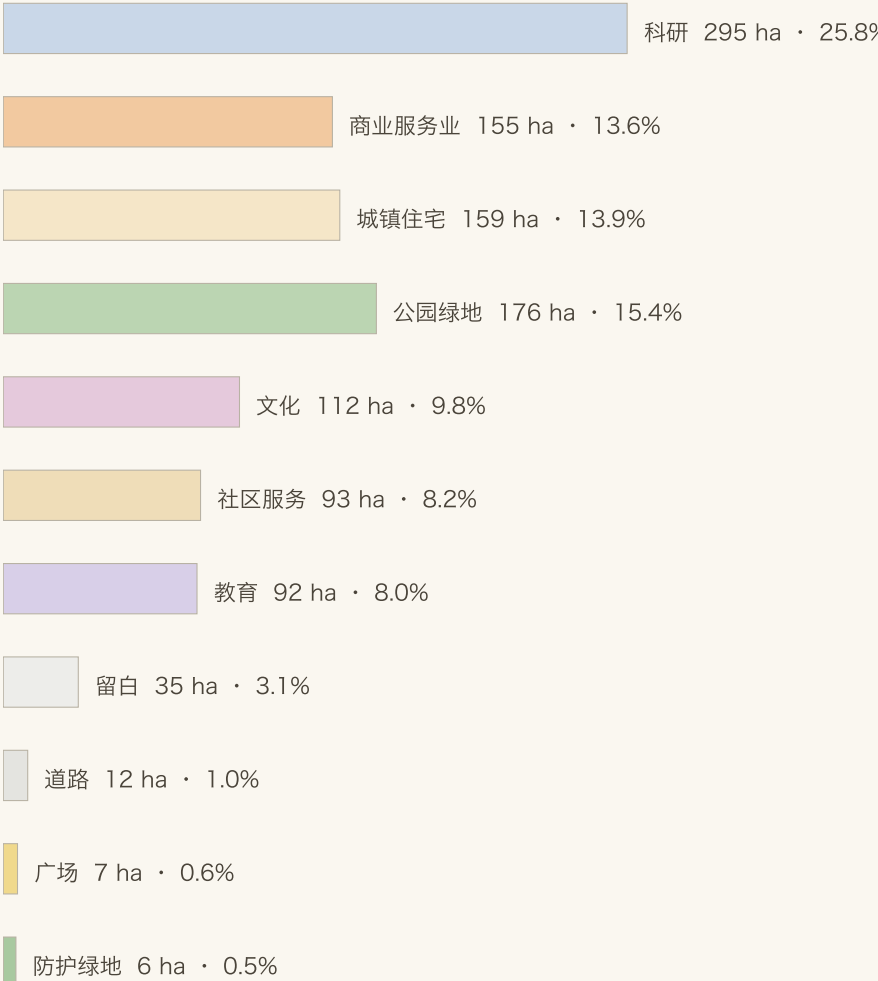

三层范围传导：43.6 km² 统筹研究 → 11.4 km² 总体设计 → 368.4 ha 重点区域


结构要点

- 主街绿廊约 150 m 宽纵贯 9.7 km，是慢行主脊、公共空间主链与文化叙事主线
- 四条东西缝合街打通断点，把公园从「隔离带」转为「缝合器」
- 科研用地 25.8% 为主体，商业与居住沿三市与主街混合布局
- 小月河联络绿廊沿东缘接入场景赋能翼
- 战略留白 35.4 ha = 「未挂牌摊位」的空间表达
- 矩形临时边界仅为低对比虚线约束，非地块或道路红线

三市详细设计

Three Bazaars in Detail


定位差异 · 空间联系 · 项目抓手 · 风险条件（重点区为临时矩形示意，结论为方向性设计）

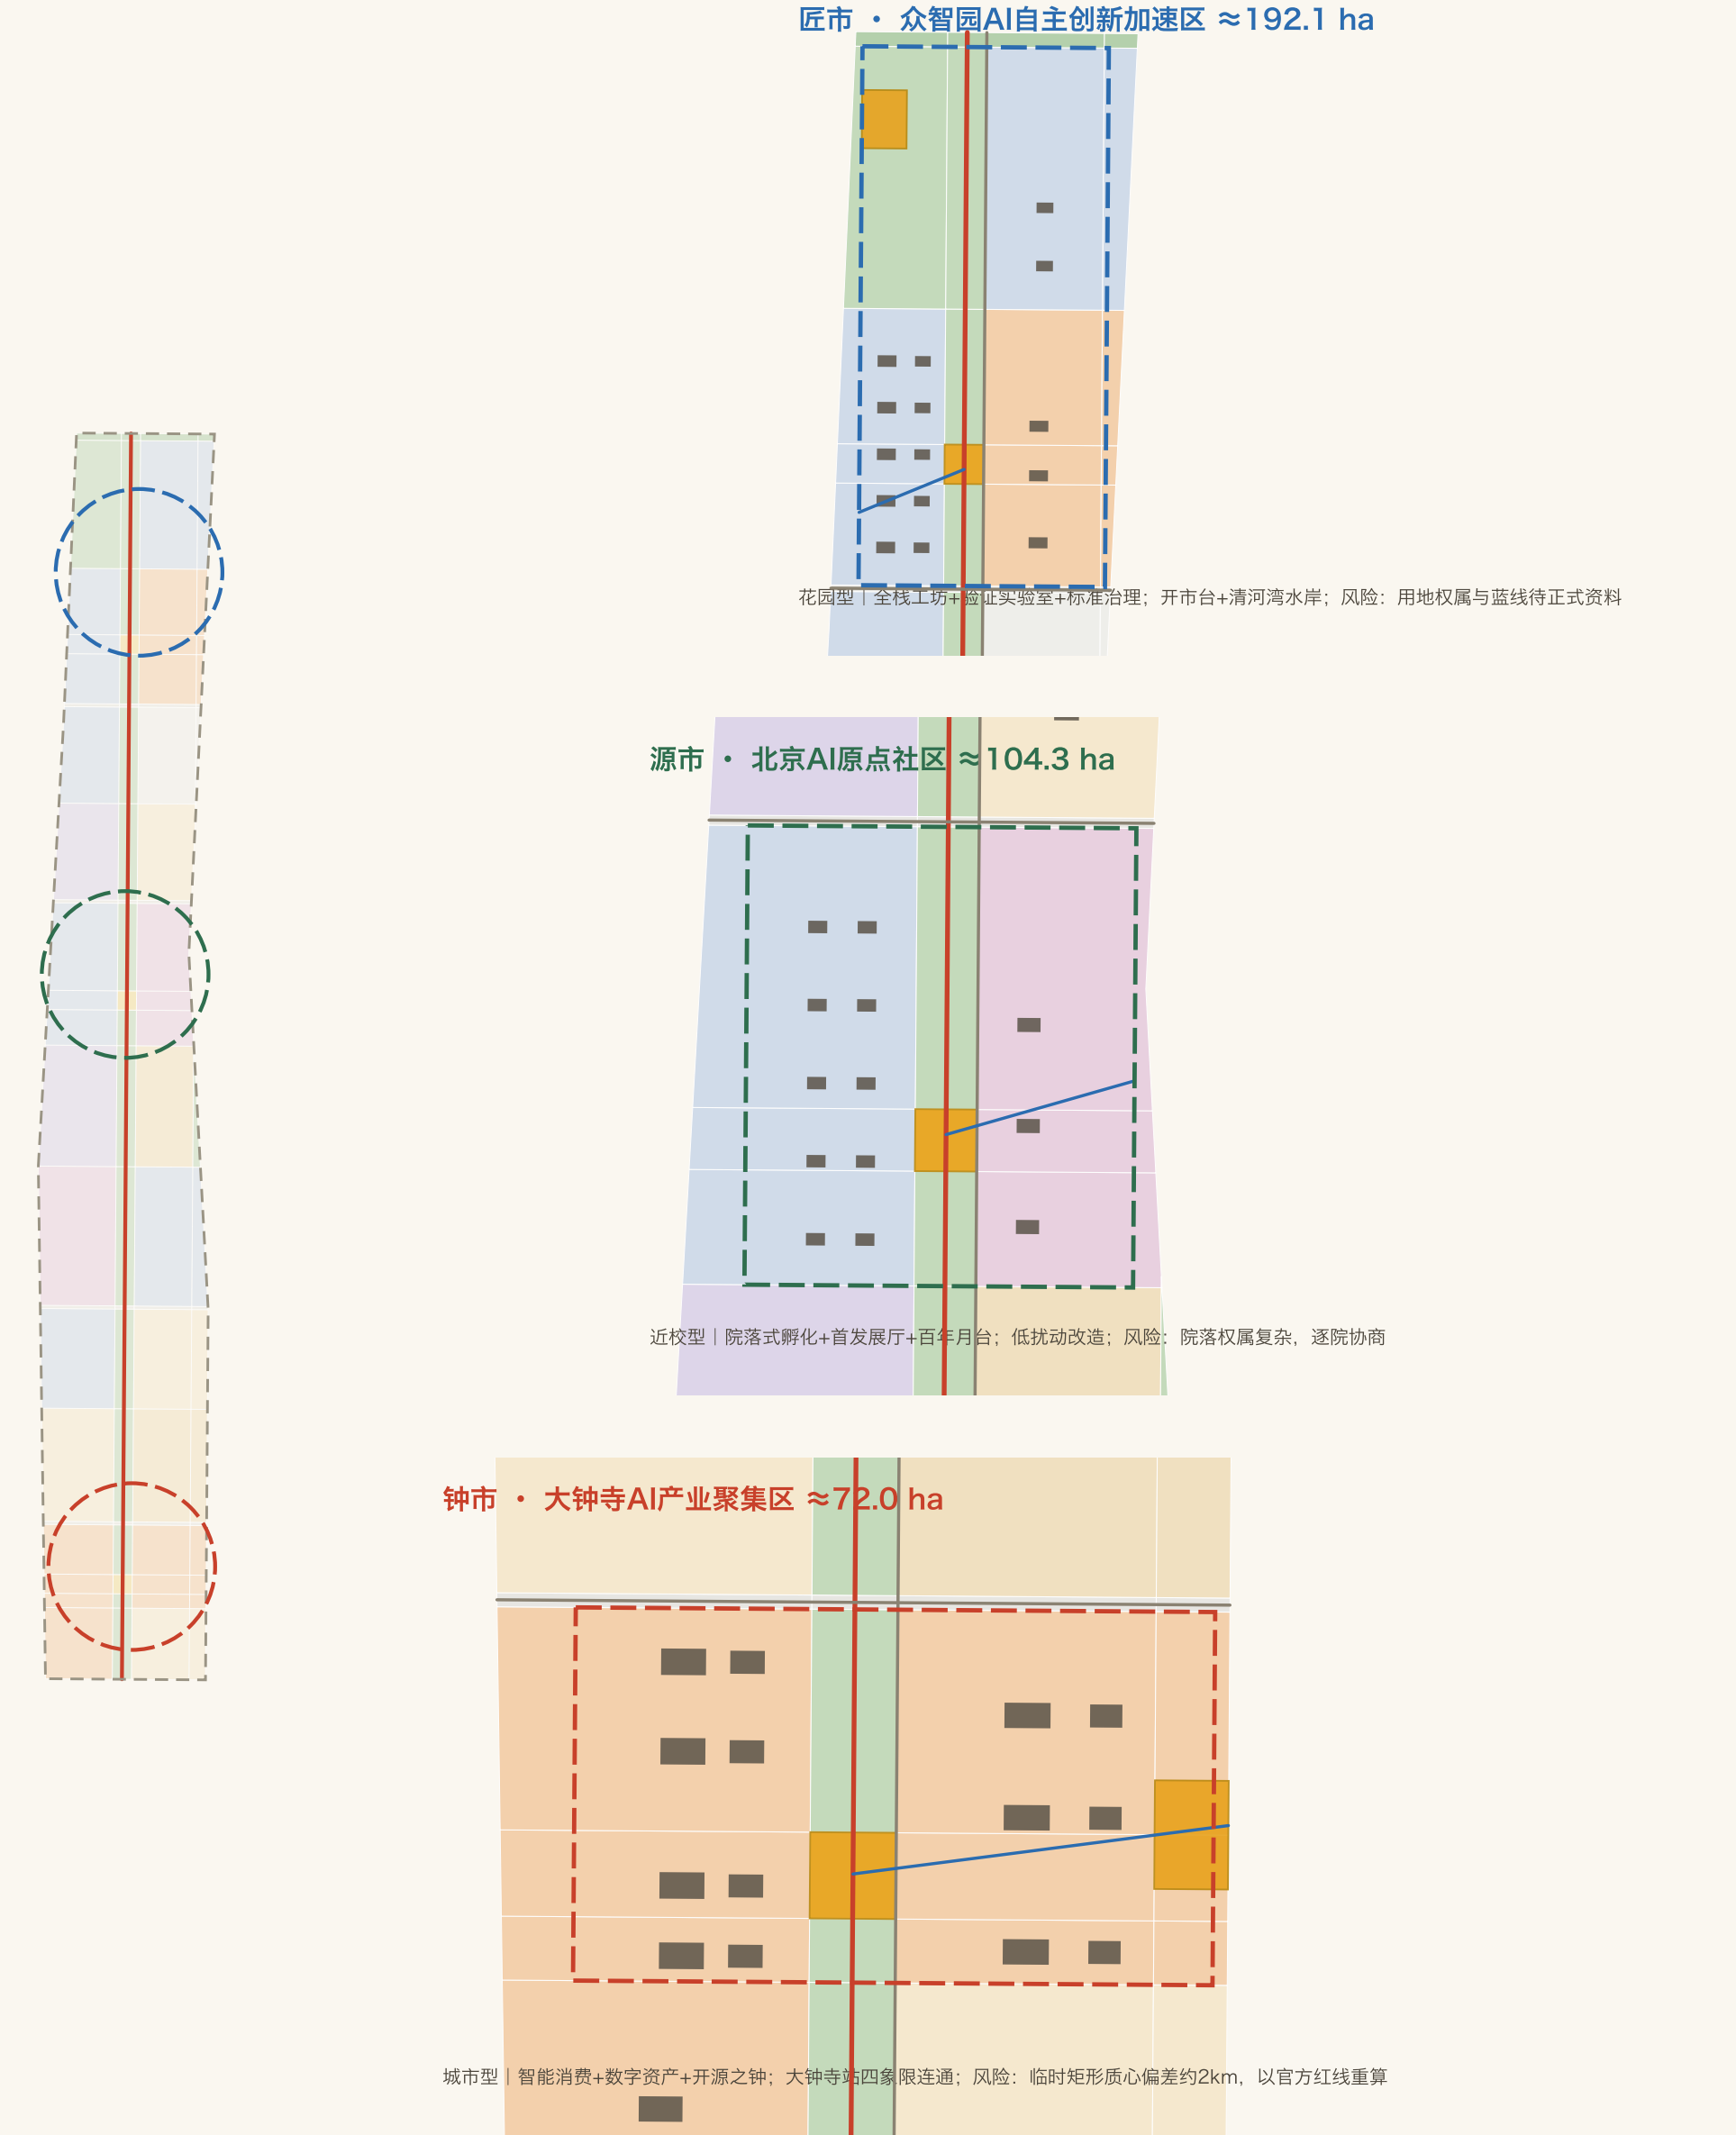

慢行交通与蓝绿公共空间

Slow Mobility and Blue-Green Network

主脊贯通 · 断点缝合 · 站市直连 · 蓝绿连续（概念建议）

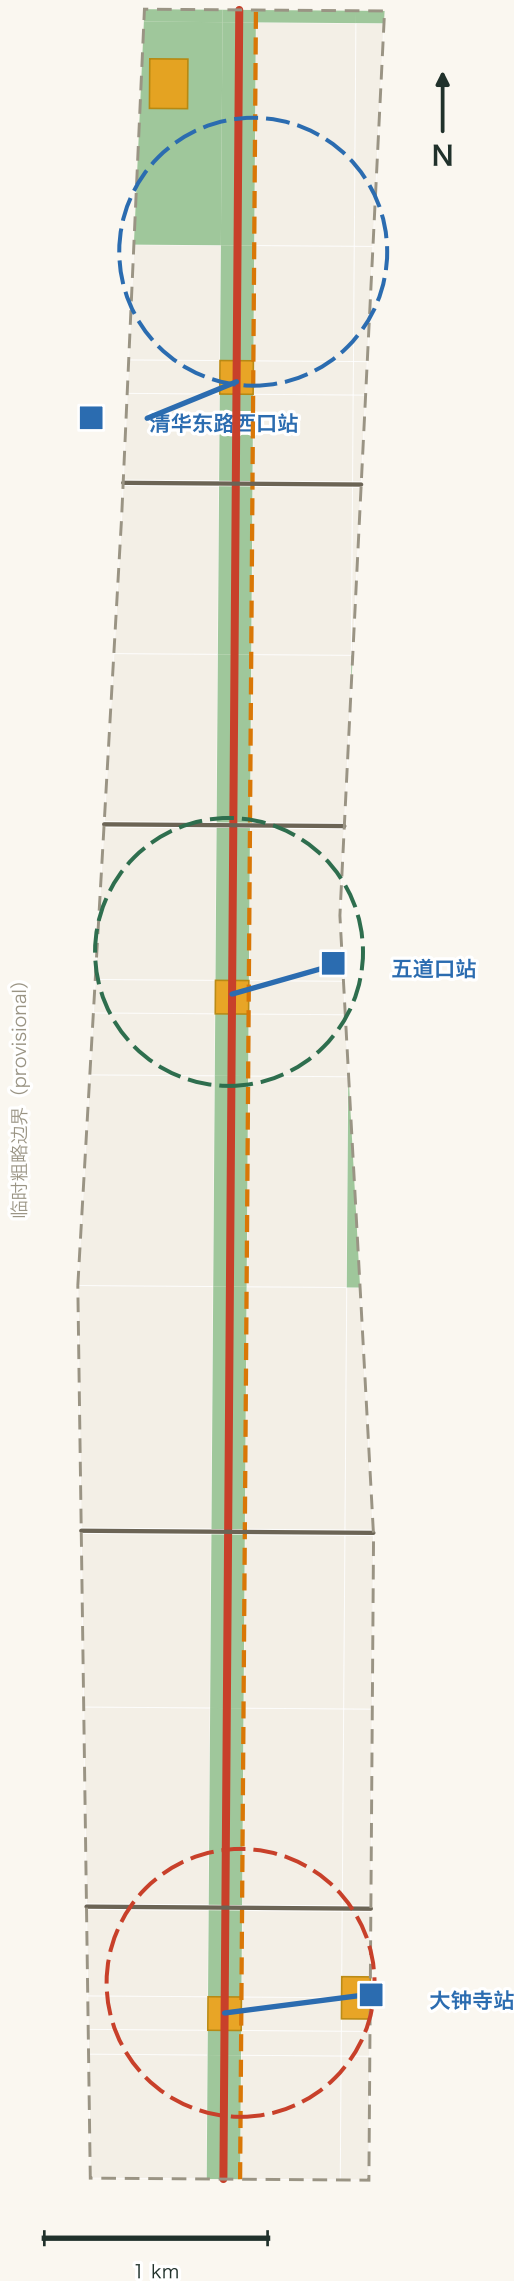

系统组织

- 赶集路主街慢行脊 (9.7 km)
- 骑行道
- 东西缝合街 × 4
- 轨道站接驳径 × 3
- 公园绿地 / 防护绿地
- 市集广场与节点

25.7 km

道路中心线总长

16.0%

绿地率（概念）

13.1%

公共空间率（概念）

蓝绿要点：清河湾收北端、小月河联络东缘；水系精确线位待官方资料，图中不表达蓝线。

断点缝合与站市直连

- 大钟寺站四象限步行连通为最高优先级：站前广场+立体接驳径直连钟市广场
- 五道口、清华东路西口站城一体化为概念方向，衔接源市与匠市
- 端侧算力驿站与光伏棚沿主街布点——「算力如水电」的新型市政概念
- 非机动车停放写入每份摊位档案的配套条款

指标复算与证据链

Metrics and Evidence Chain

已知指标可复算、未知指标如实标注（待正式数据补齐）；全链路自检



用地构成（万 m²，EPSG:4548 复算）



待正式数据补齐（unknown，如实披露）

- 容积率（法定）
缺控规条件与现状底数
- 建筑高度控制
缺法定高度条件
- 官方红线/重点区多边形
官方资料未公开
- 现状建筑与权属底数
待正式资料

证据链与自检



同一数据源派生全部成果：地图、指标、图纸与网页数值一致；
官方红线发布 → 触发整包重算（assumptions 登记触发条件）。

市集活力指标（运营期）：挂牌摊位数 · 赶集人次 · Agent 交易笔数 · 审计通过率 · 碑林铭刻数