


43.6 km² 是城市网络，不是一条景观带

京张纵向公共骨架 × 八条真实横街 × 清河—小月河 × 西侧服务翼；灰虚线为临时研究范围。

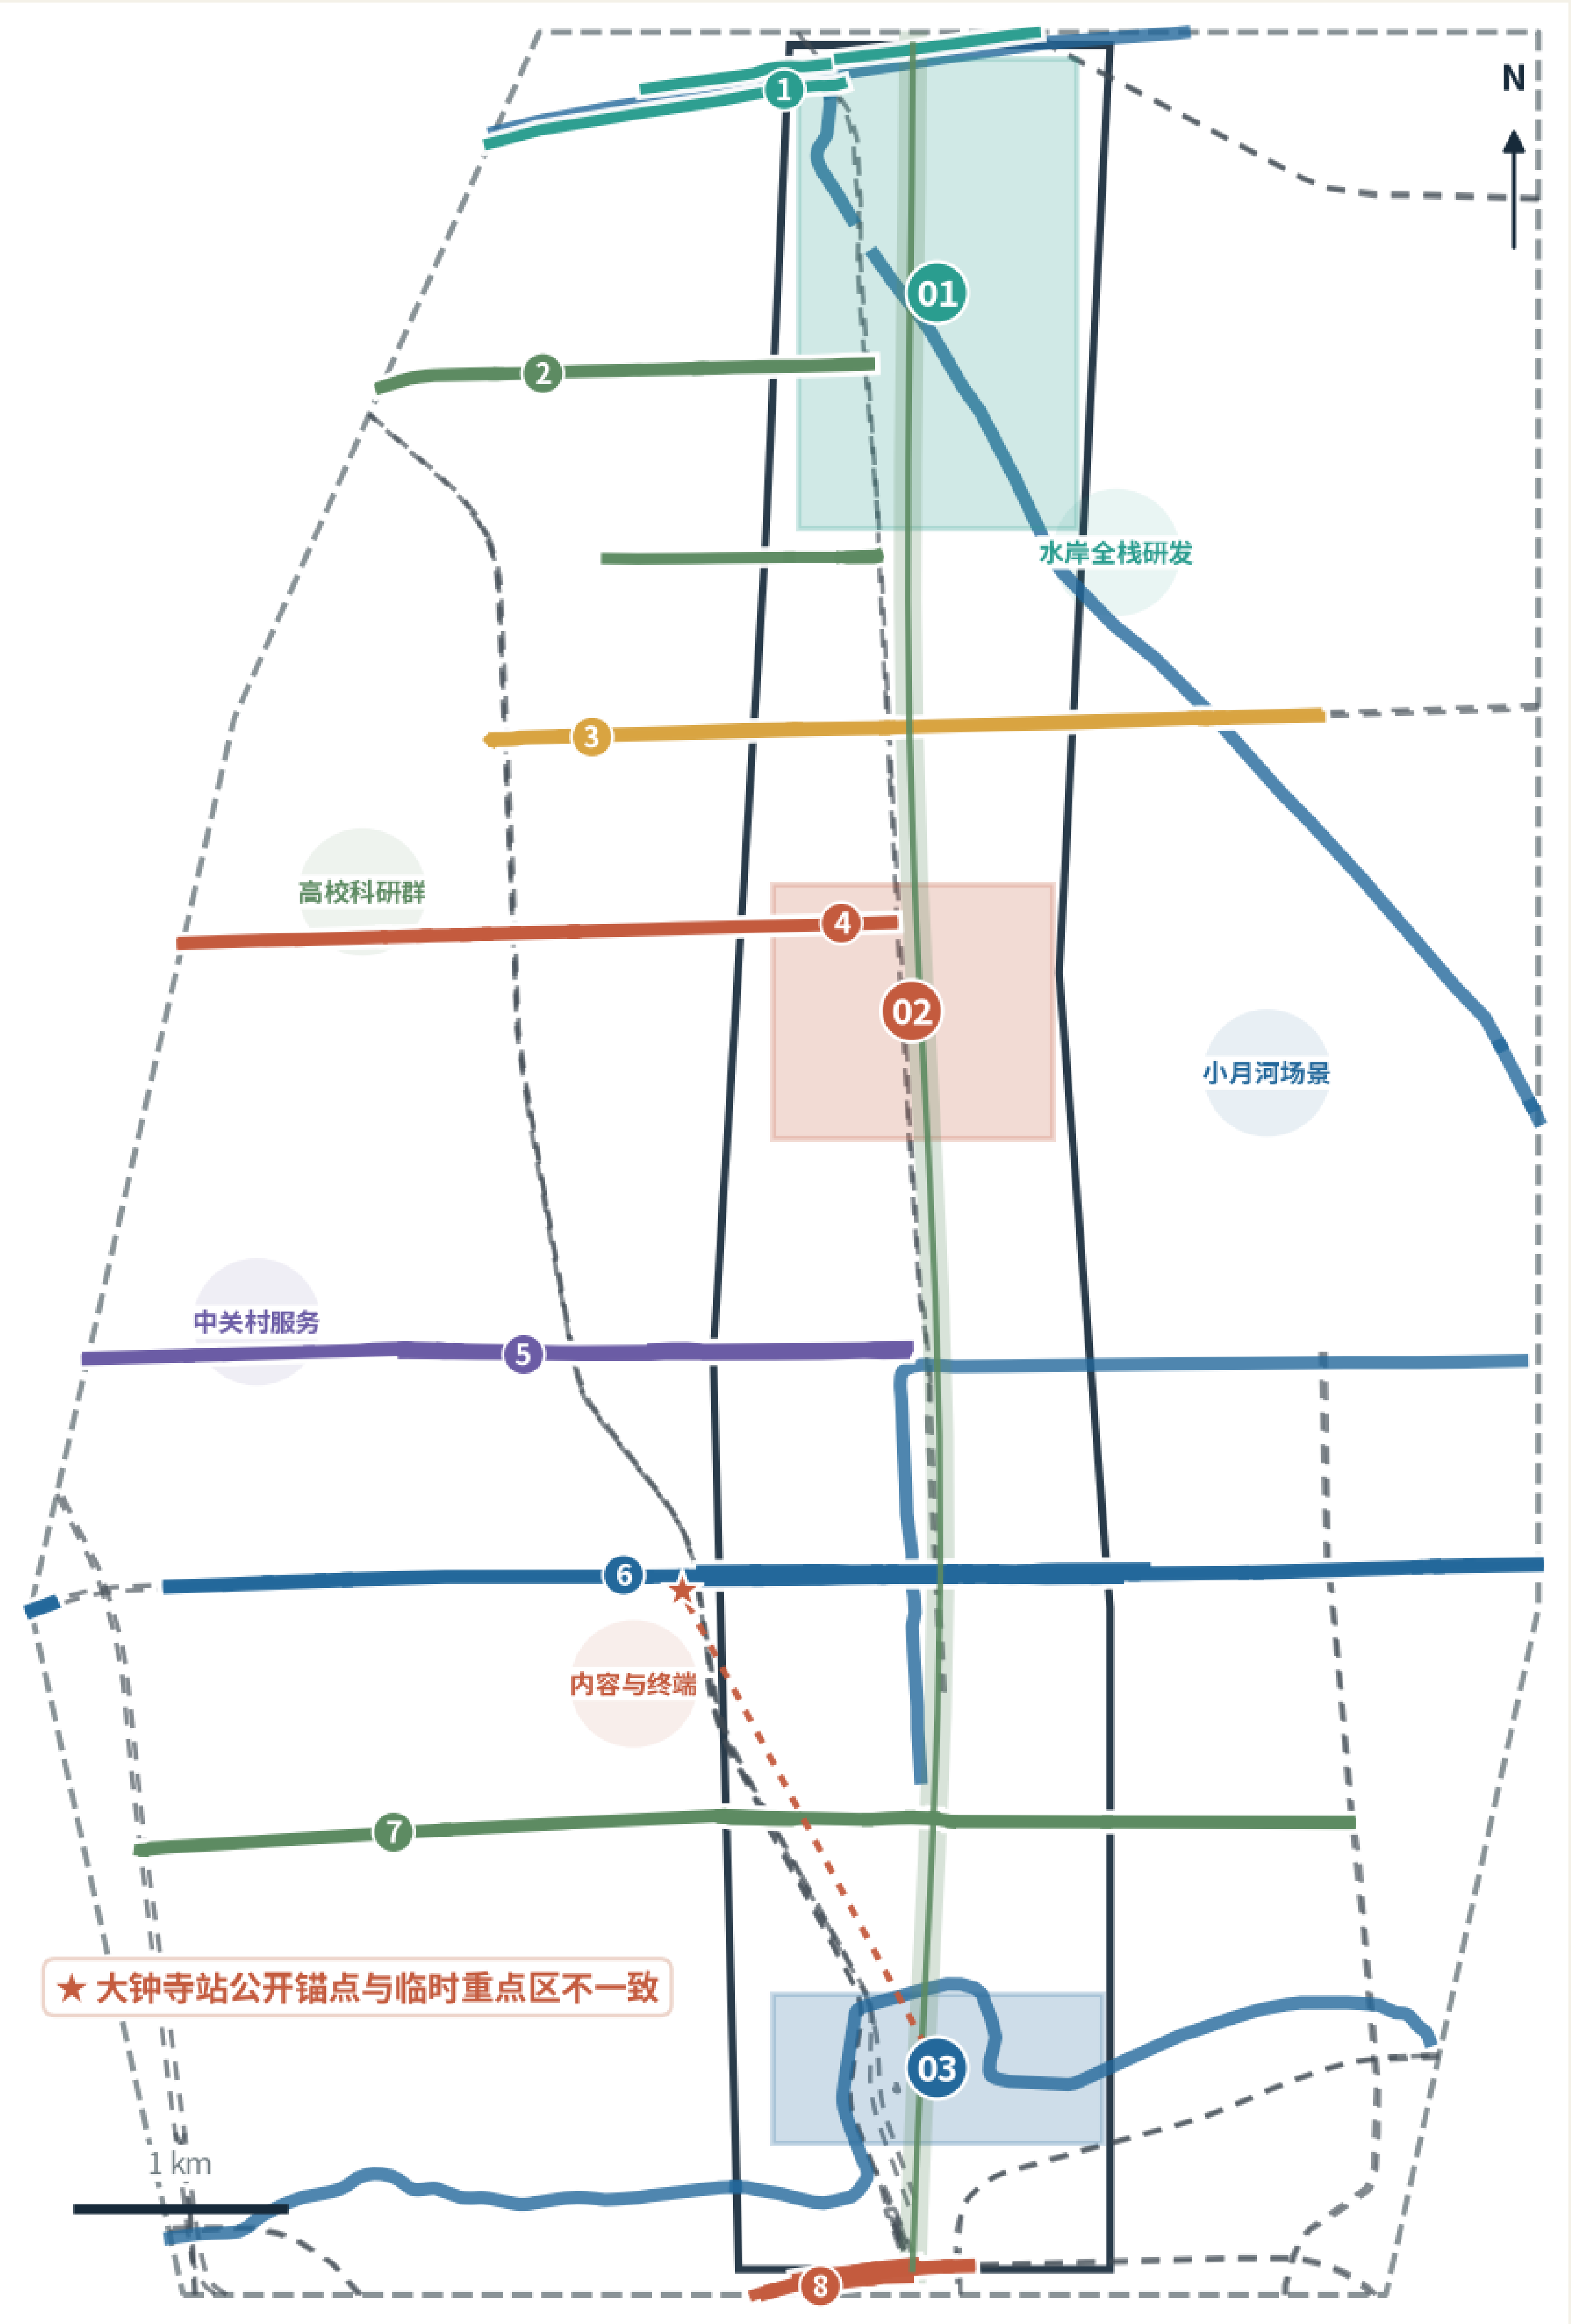

京张横街

让八条真实横向街道进入 43.6 平方公里创新城区

创新资源原本就在铁路两侧。设计的主角不是再造纵轴，而是让人横向穿过校园、社区、站口、产业首层与两条河。

43.6 km²

统筹研究

资源、交通、产业与蓝绿网络

11.4 km²

总体设计

用地、横街、街坊首层与公共空间

368.4 ha

三区详设

建筑前后台、站口、剖面与首批项目

三大定位落在同一空间系统

01 百年京张文化带


02 都市AI生活体验带

03 AI融合创新带

五功能：全栈自主 / 创新生态 / AI+场景 / 活力城市 / 治理规则

11.4 km² 概念用地不是留白

完整拓扑表达功能混合；非现状用地调查、非控规调整、非地块权利。

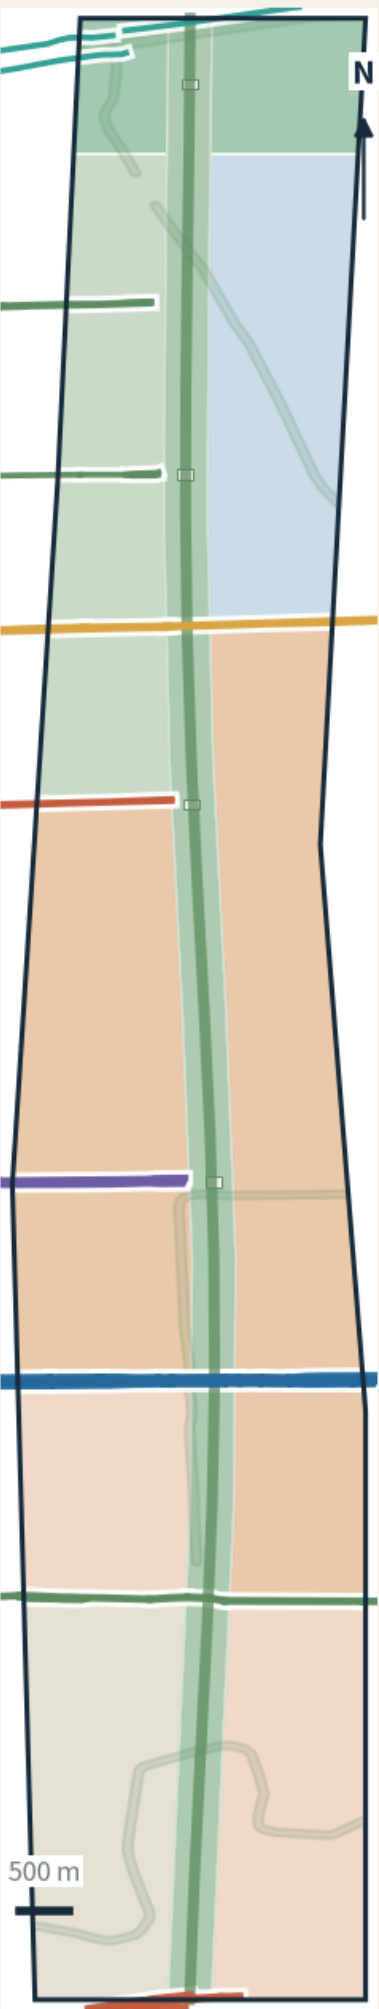

状态截点 2026-08-10 | 概念城市设计；临时边界与 OSM 仅供研究，不替代法定规划、权属或工程测绘。

五类城市材料

- 研发 / 孵化
0802
- 高校 / 科研
0804
- 居住 / 社区
0701/0702
- 商业 / 服务 / 文化
05/0803
- 公园 / 生态
1401/1402
- 横街 / 公共节点
1207/1403


首层动作只分四类

- 01 保留现状
- 02 首层改造
- 03 合作租赁
- 04 条件新增

水岸研发横街：从河岸到研发后场的完整梯度
研究区间：生境12~20m | 净步行≥3m | 需渠6~12m | 公开前场8~15m



近校转换横街：校园门到企业的五分钟短链
研究下段：净步行≥3m | 单向骑行≥2.5m | 工作间连渠6~9m | 入口≥2/100m

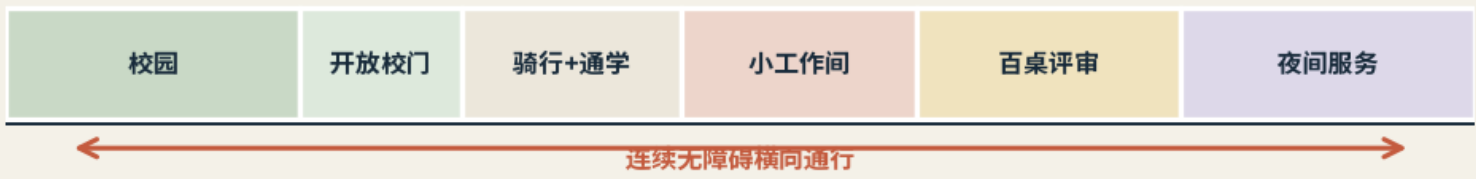

四象限站城：先连续地面，再比选桥下、连桥或地下
研究下段：每角到达面≥12×20m | 地面过街≤2信号阶段 | 车位150~300/角停核


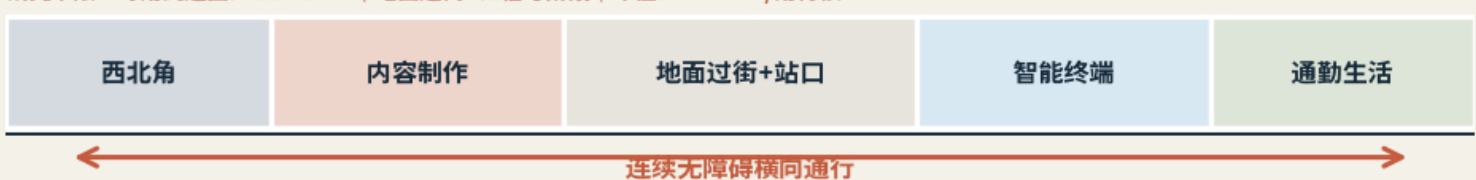


FIG 02 / 05

纵向公园已经存在，设计重点是横向穿越与完整断面

八条横街以真实水岸/道路命名；每条都必须连到建筑首层、站口、校园或社区，而不止于公园边。

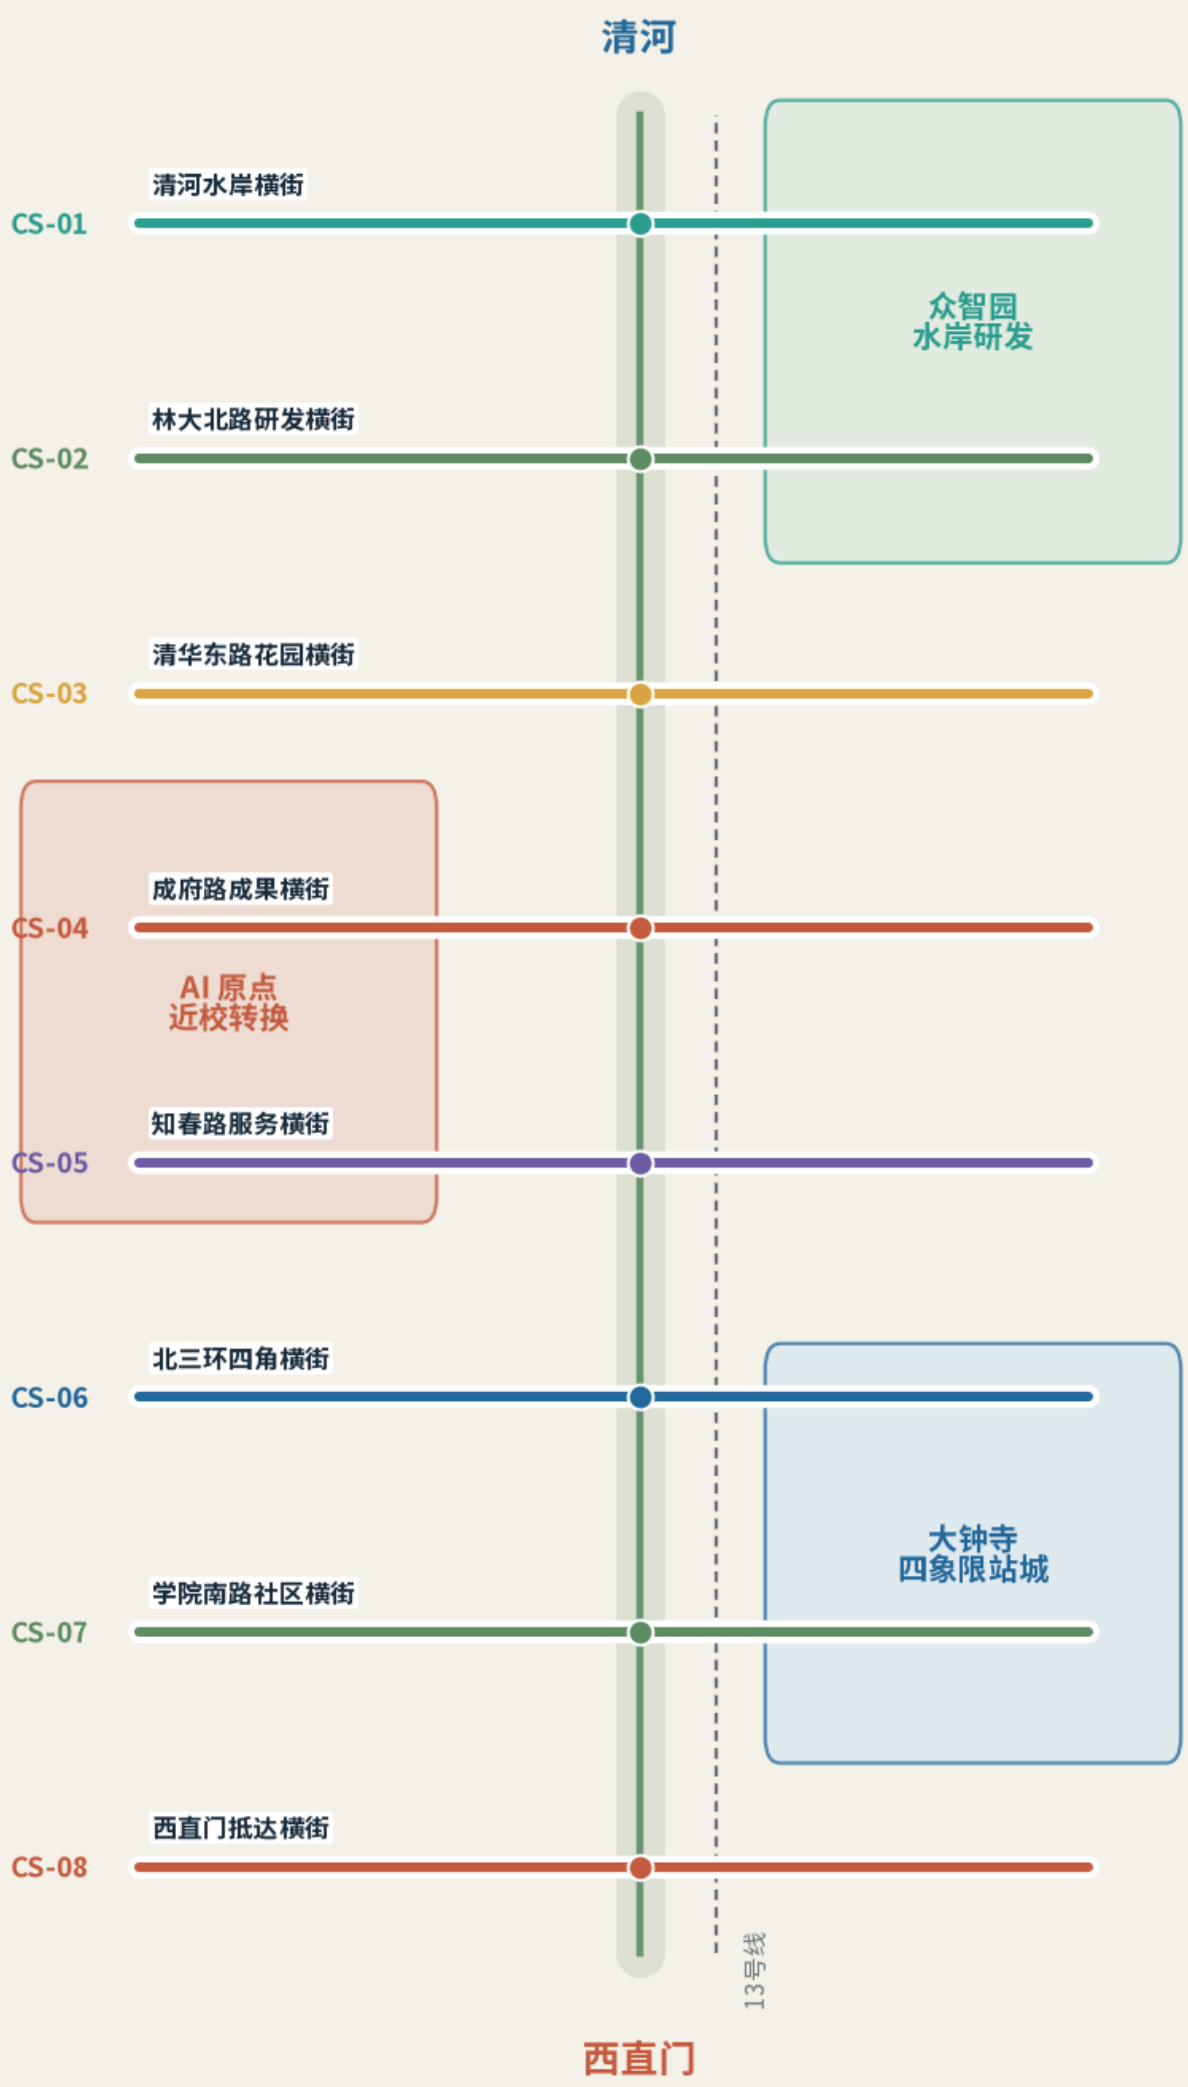

状态截点 2026-08-10 | 概念城市设计；临时边界与 OSM 仅供研究，不替代法定规划、权属或工程测绘。

水岸研发横街：从河岸到研发后场的完整梯度

研究区间：生境12~20m | 净步行≥3m | 需渠6~12m | 公开前场8~15m



近校转换横街：校园门到企业的五分钟短链

研究下段：净步行≥3m | 单向骑行≥2.5m | 工作间连渠6~9m | 入口≥2/100m



四象限站城：先连续地面，再比选桥下、连桥或地下

研究下段：每角到达面≥12×20m | 地面过街≤2信号阶段 | 车位150~300/角停核



FIG 04 / 05

三处重点区：三种街坊，不是三座孤立雕塑

工作视窗采用 OSM 现状建筑；彩色为首层改造，红色为条件新增，横线为主公共路径。

水岸研发街坊



01 众智园 AI 自主创新加速区

清河原型院

首层总平

学知园站—园区公共首层—清河步道形成一条连续公众线；安全研发后场由园区支路独立到达。


概念剖面

生境缓冲12—20m、无障碍净宽≥3m、雨洪台地6—12m、公开前场8—15m；均为待测研究区间。

贡献架

贡献架01：6—12个可替换展格，展示公开标准、开放工具与无障碍改进；季度轮换，禁止研发数据和企业广告。

近校转换街坊

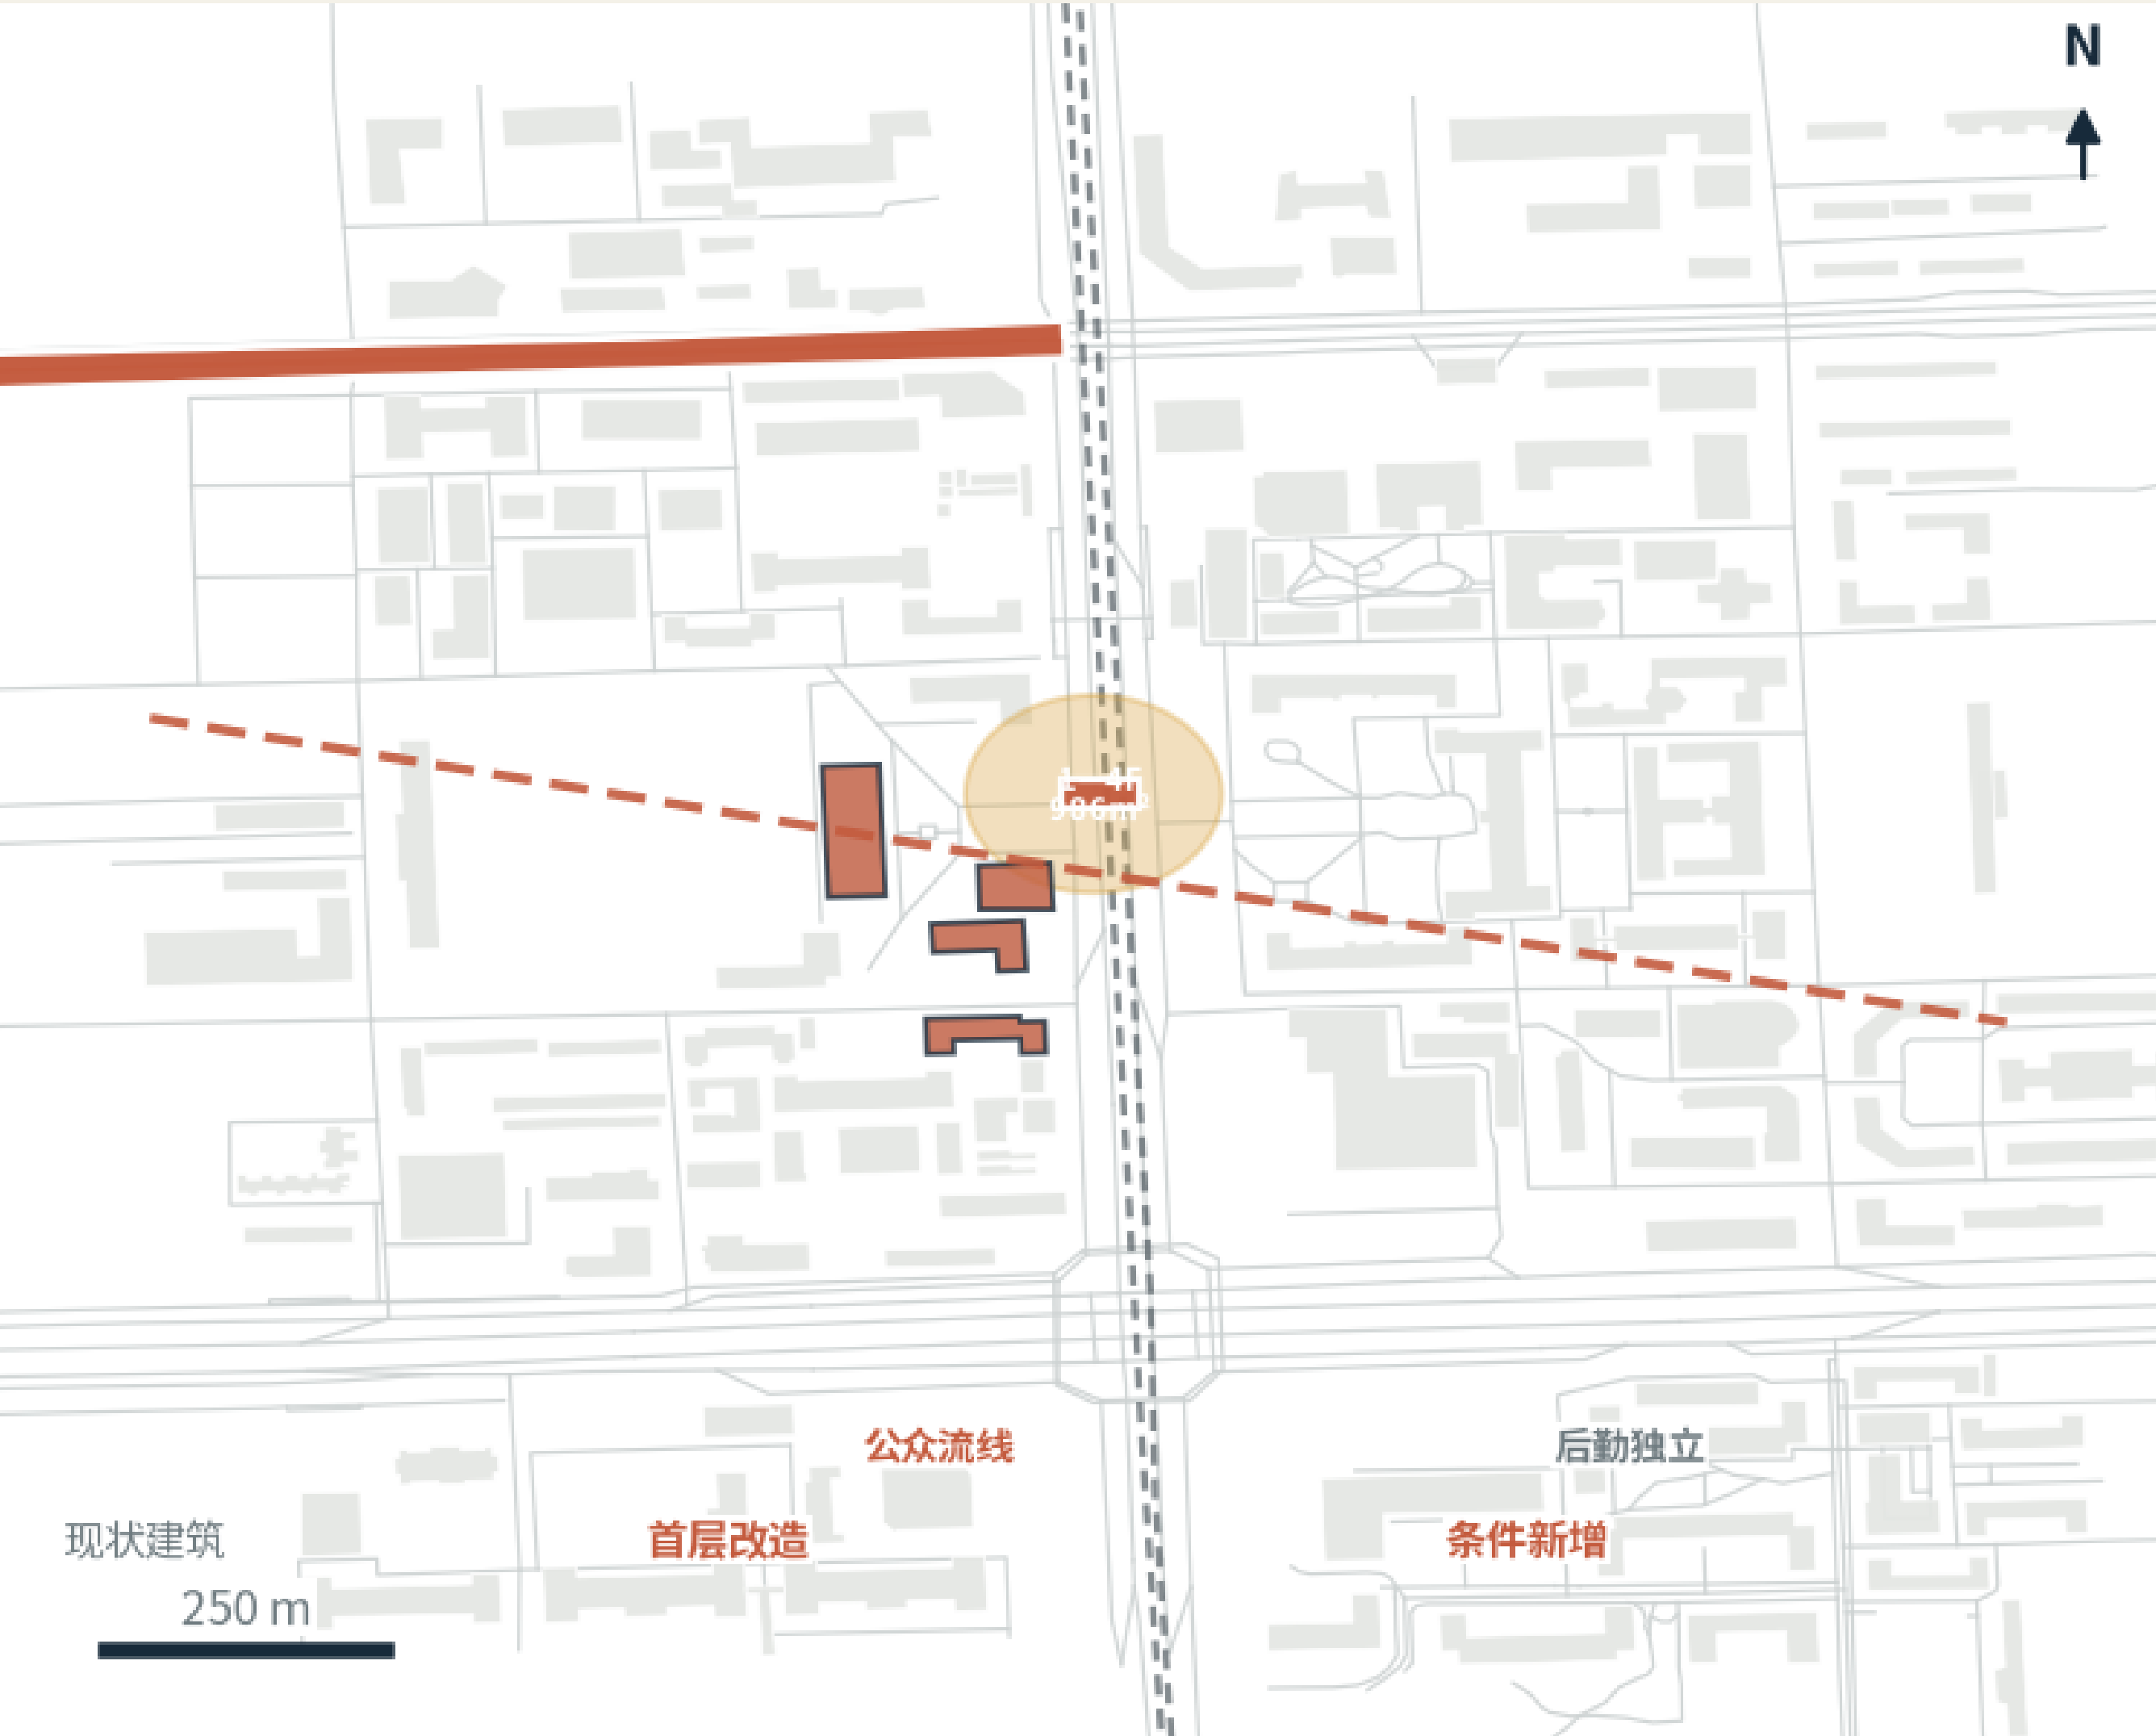

02 北京 AI 原点社区

百桌评审厅

首层总平

校园门—小工作间—百桌评审厅—原点大厦—星光大道首层形成五分钟连续短链，夜间路线接入人才公寓与餐饮。

概念剖面

人行净宽≥3m、单向骑行带≥2.5m、首层进深6—9m、评审模块约9×18m、公众入口≥2/100m；均为研究目标。

贡献架

贡献架02：展示开源工具、同行评审、导师服务与社区问题释法；不设个人积分榜，贡献者可选择署名或团队署名。

四象限站城街坊



03 大钟寺 AI 产业聚集区

大钟寺四角台

首层总平

四个站角先以地面过街和无障碍垂直交通组成连续到达面，再把内容制作、维修退换、夜校和社区服务嵌入四角首层。

概念剖面

每角连续到达面建议≥12×20m、地面过街≤2个信号阶段、每角150—300辆自行车位待需求核定、轨道两侧均有无障碍垂直路线。

贡献架

贡献架03：展示可维修设计、无障碍内容、版权合规与材料再用成果；按修复率和公共服务评议，不按销量排名。

把设计、数据边界和实施权限放在同一张表

已知不等于官方控制；目标不等于现状；未知也不等于不做设计。

官方任务	本包推导	设计目标	保持未知				
• 43.6 km² 统筹研究 • 11.4 km² 总体设计 • 368.4 ha 三区详设 • 9 km 京张公共骨架	• 8 条真实横街 • 535 个 OSM 建筑 • 15 个实施项目 • 12 张场景卡	• 八条横街连续性 8/8 • 无障碍横向通行 100% target • 首层入口密度 >= 2 / 100 m target • 公共首层开放 >= 60 h/week target	• 正式红线 / 地块 / 权属 • FAR / 高度 / 密度 • 结构 / 消防 / 市政容量 • 客流 / 工程投资 / 工期				
15 个项目 × 三类实施权限							
公共空间 / 0—18月	PJT-01 竣工权属图	PJT-02 横街无障碍	PJT-03 13号线跨越	PJT-04 清华东路接口	PJT-05 横街基础服务	PJT-08 大钟寺四角	PJT-11 两河接口样板
合作租赁 / 1—3年	PJT-06 清河原型一期	PJT-07 百乐厅 · 50+50	PJT-09 影像AI首层	PJT-10 终端维修回路	PJT-12 首层合作租赁	PJT-15 基金 · 五年复盘	
法定工程 / 3—10年	PJT-13 大钟寺工程比选				PJT-14 众智园水岸街坊		

停止条件 未取得正式边界与工程资料，不锁定 FAR、高度、拆除、桥隧或投资；未签租赁/维护责任，不宣称首层开放；无人工替代，不运行 AI 场景。

状态截点 2026-08-10 | 概念城市设计；临时边界与 OSM 仅供研究，不替代法定规划、权属或工程测绘。

FIG 05 / 05

国际转化：双语触达 → 预约参访 → 同行评审 → 受控测试 → 专业服务/设备 → 工位或短租 → 长期租赁/研究合作；不承诺招商、资金、政策或审批结果。

场景开放八道门：公开征集 → 权利/隐私/安全筛查 → 匹配房间与运营方 → 限界沙盒 → 人工 go/no-go → 限量公共试用 → 复盘 → 停止/重复/转化

01 发现

横街共测 / 百域评审 / 原型开放日 / 维修与再用月

公开日历、容量、无障碍与停止条件同步发布

02 进入

双语迎新台 + 八项创业门诊 + 14日内一次人工回访目标

活动参与者选择工位、专业服务、设备或社区任务

03 试作

50+50开放工位 + 共享仪器 + 四个受控产业测试

每个项目有责任人、保险、人工接管和退出

04 转化

公开评审 → 试制/内容 → 短租首层 → 长期租赁或合作

记录转化路径与可负担性，不承诺招商结果

05 回馈

贡献聚、导师时段、社区问题清单与年度公开KPI

只记录自愿公开贡献，不建立个人积分或城市行为总账