


京张万象工场 | 场地不是一根直条

用公告文字四至、约面积和四个公开背景锚点重建同一套临时底图；区分竞赛范围、既有核心与影响范围。

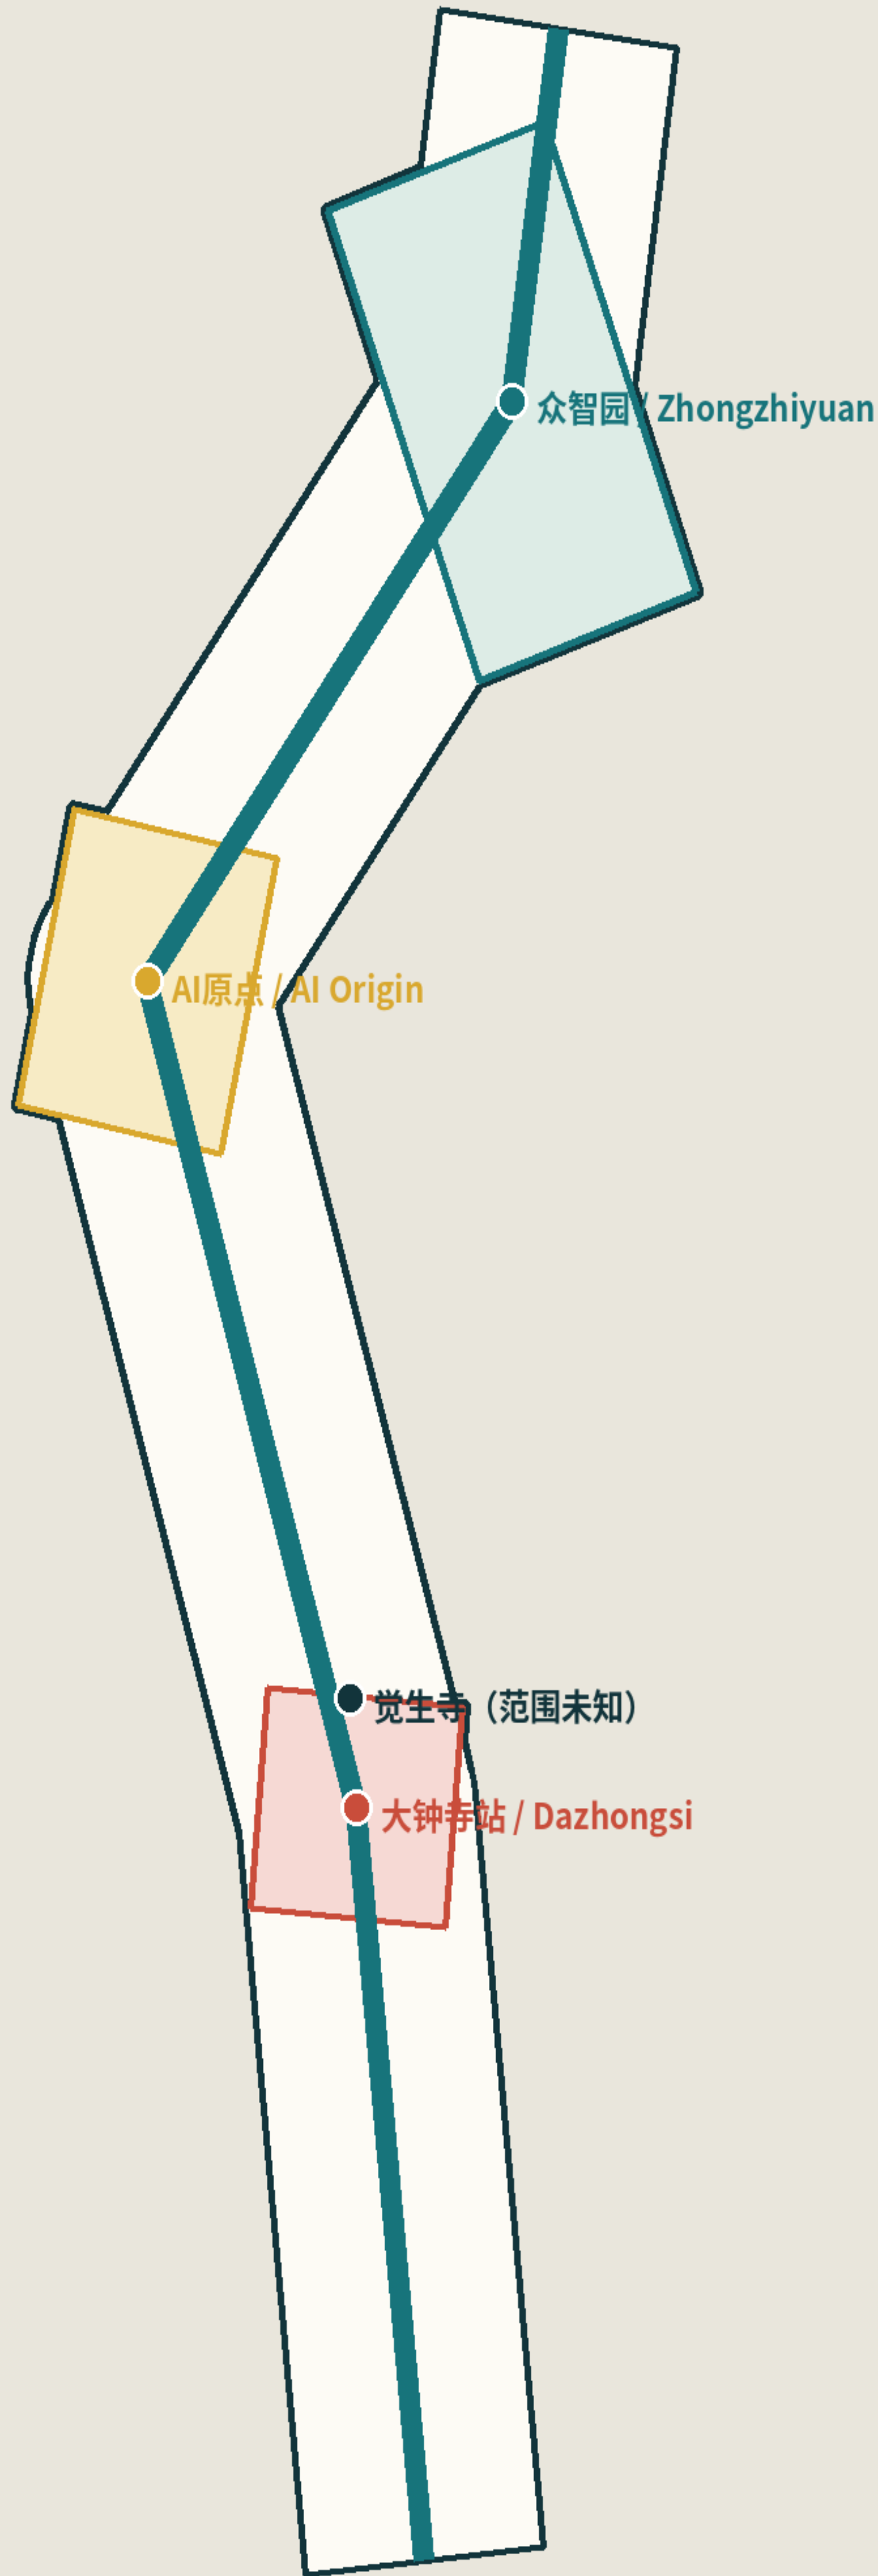

PROVISIONAL / 锚点校准，非官方红线

三层范围不混用

43.6km²统筹研究 / 11.4km²总体设计 / 368.4ha三处重点区。AI原点16ha既有核心与约3km²影响范围只作背景，不冒充104.3ha竞赛边界。

四个锚点

学知园站与众智园、原点大厦、大钟寺站、觉生寺。坐标只用于背景核对；文保范围、道路红线、权属和官方polygon仍为空。

一个空间命题

不是再造一条AI景观轴，而是沿真实街区把文化证据、城市委托、公共样机和一年采用/退出嵌入日常首层与公共空间。

复算合同


官方polygon到达后：九类GeoJSON、指标、五图、A3/A0与网页必须一起重算，不能只换底图。

三处重点区不是同一种AI园区

从街道—街区—地块—建筑组织入手；每一处形成不同的五分钟到达序列、首层界面与验收重点。

众智园 | 花园型创新超级街区

192.1ha 临时范围

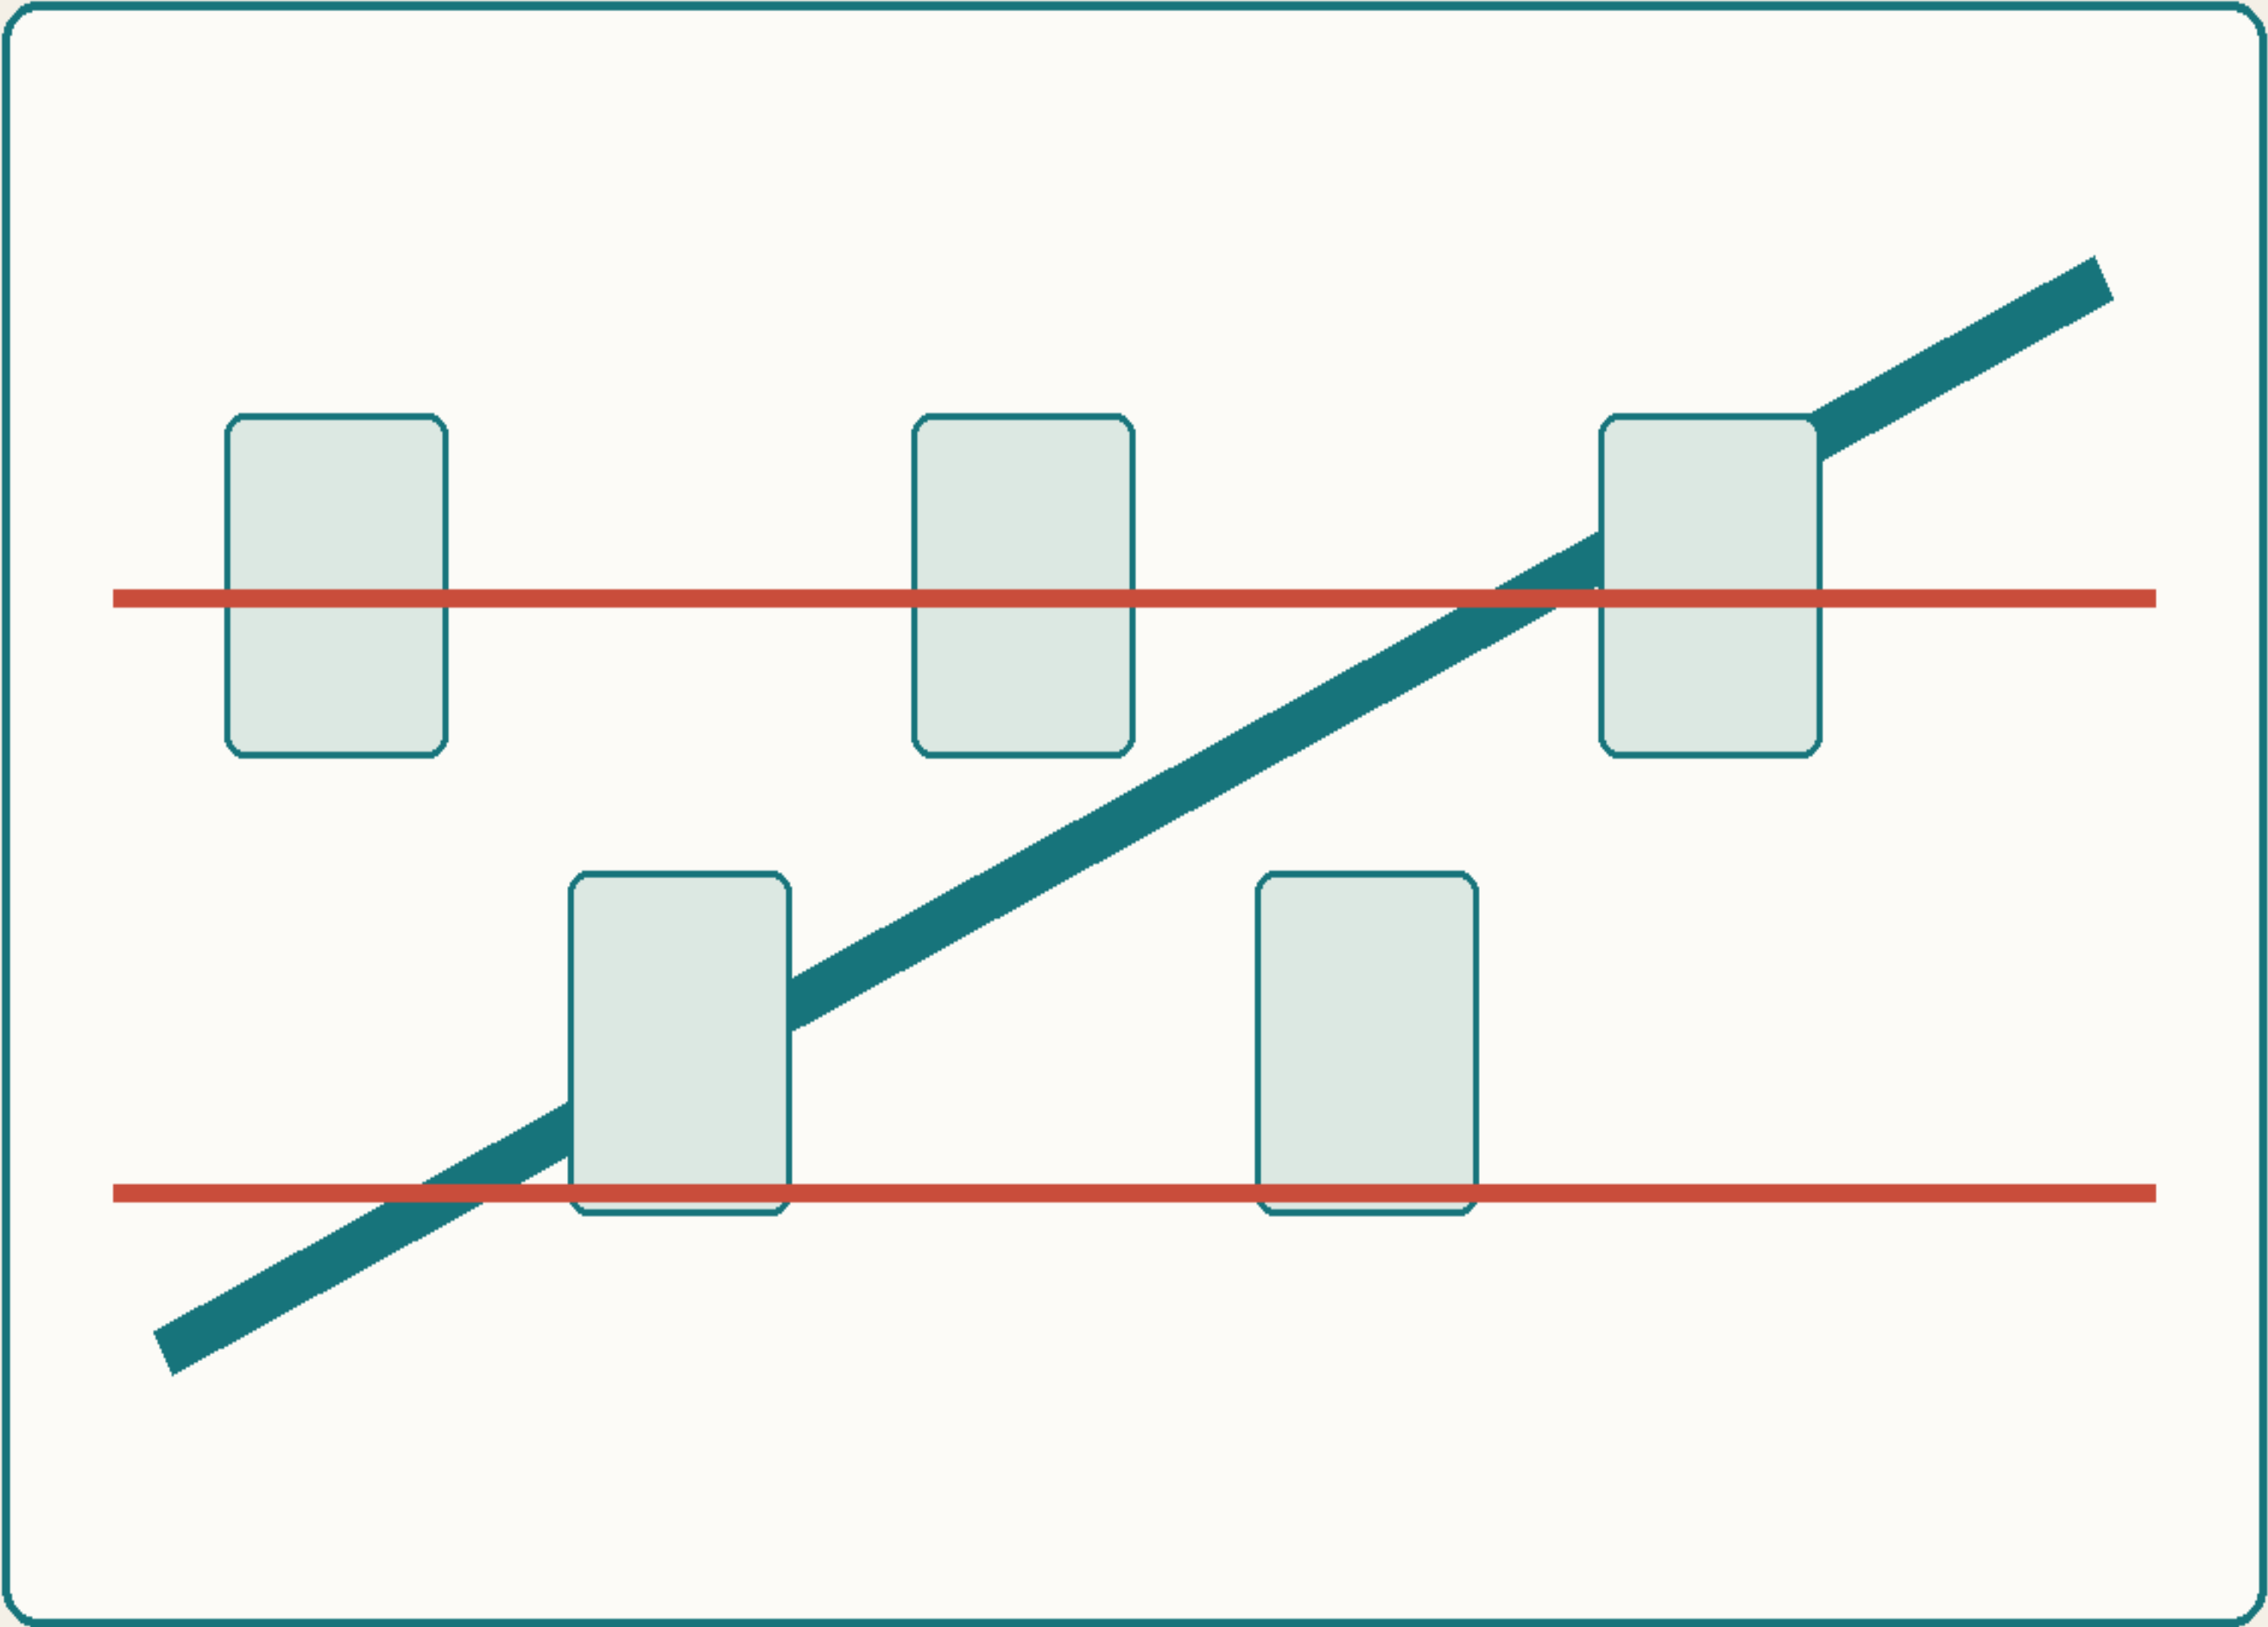

静→试→观→园→退

打开长街区：站—下沉前场—验证边界—花园/水岸—安静退出。物流与公众观察分流；首层拒绝园区式空白围墙。

街区开口


首层连续

物流分流

可逆样机

AI原点 | 近校细颗粒院落织体

104.3ha 临时范围

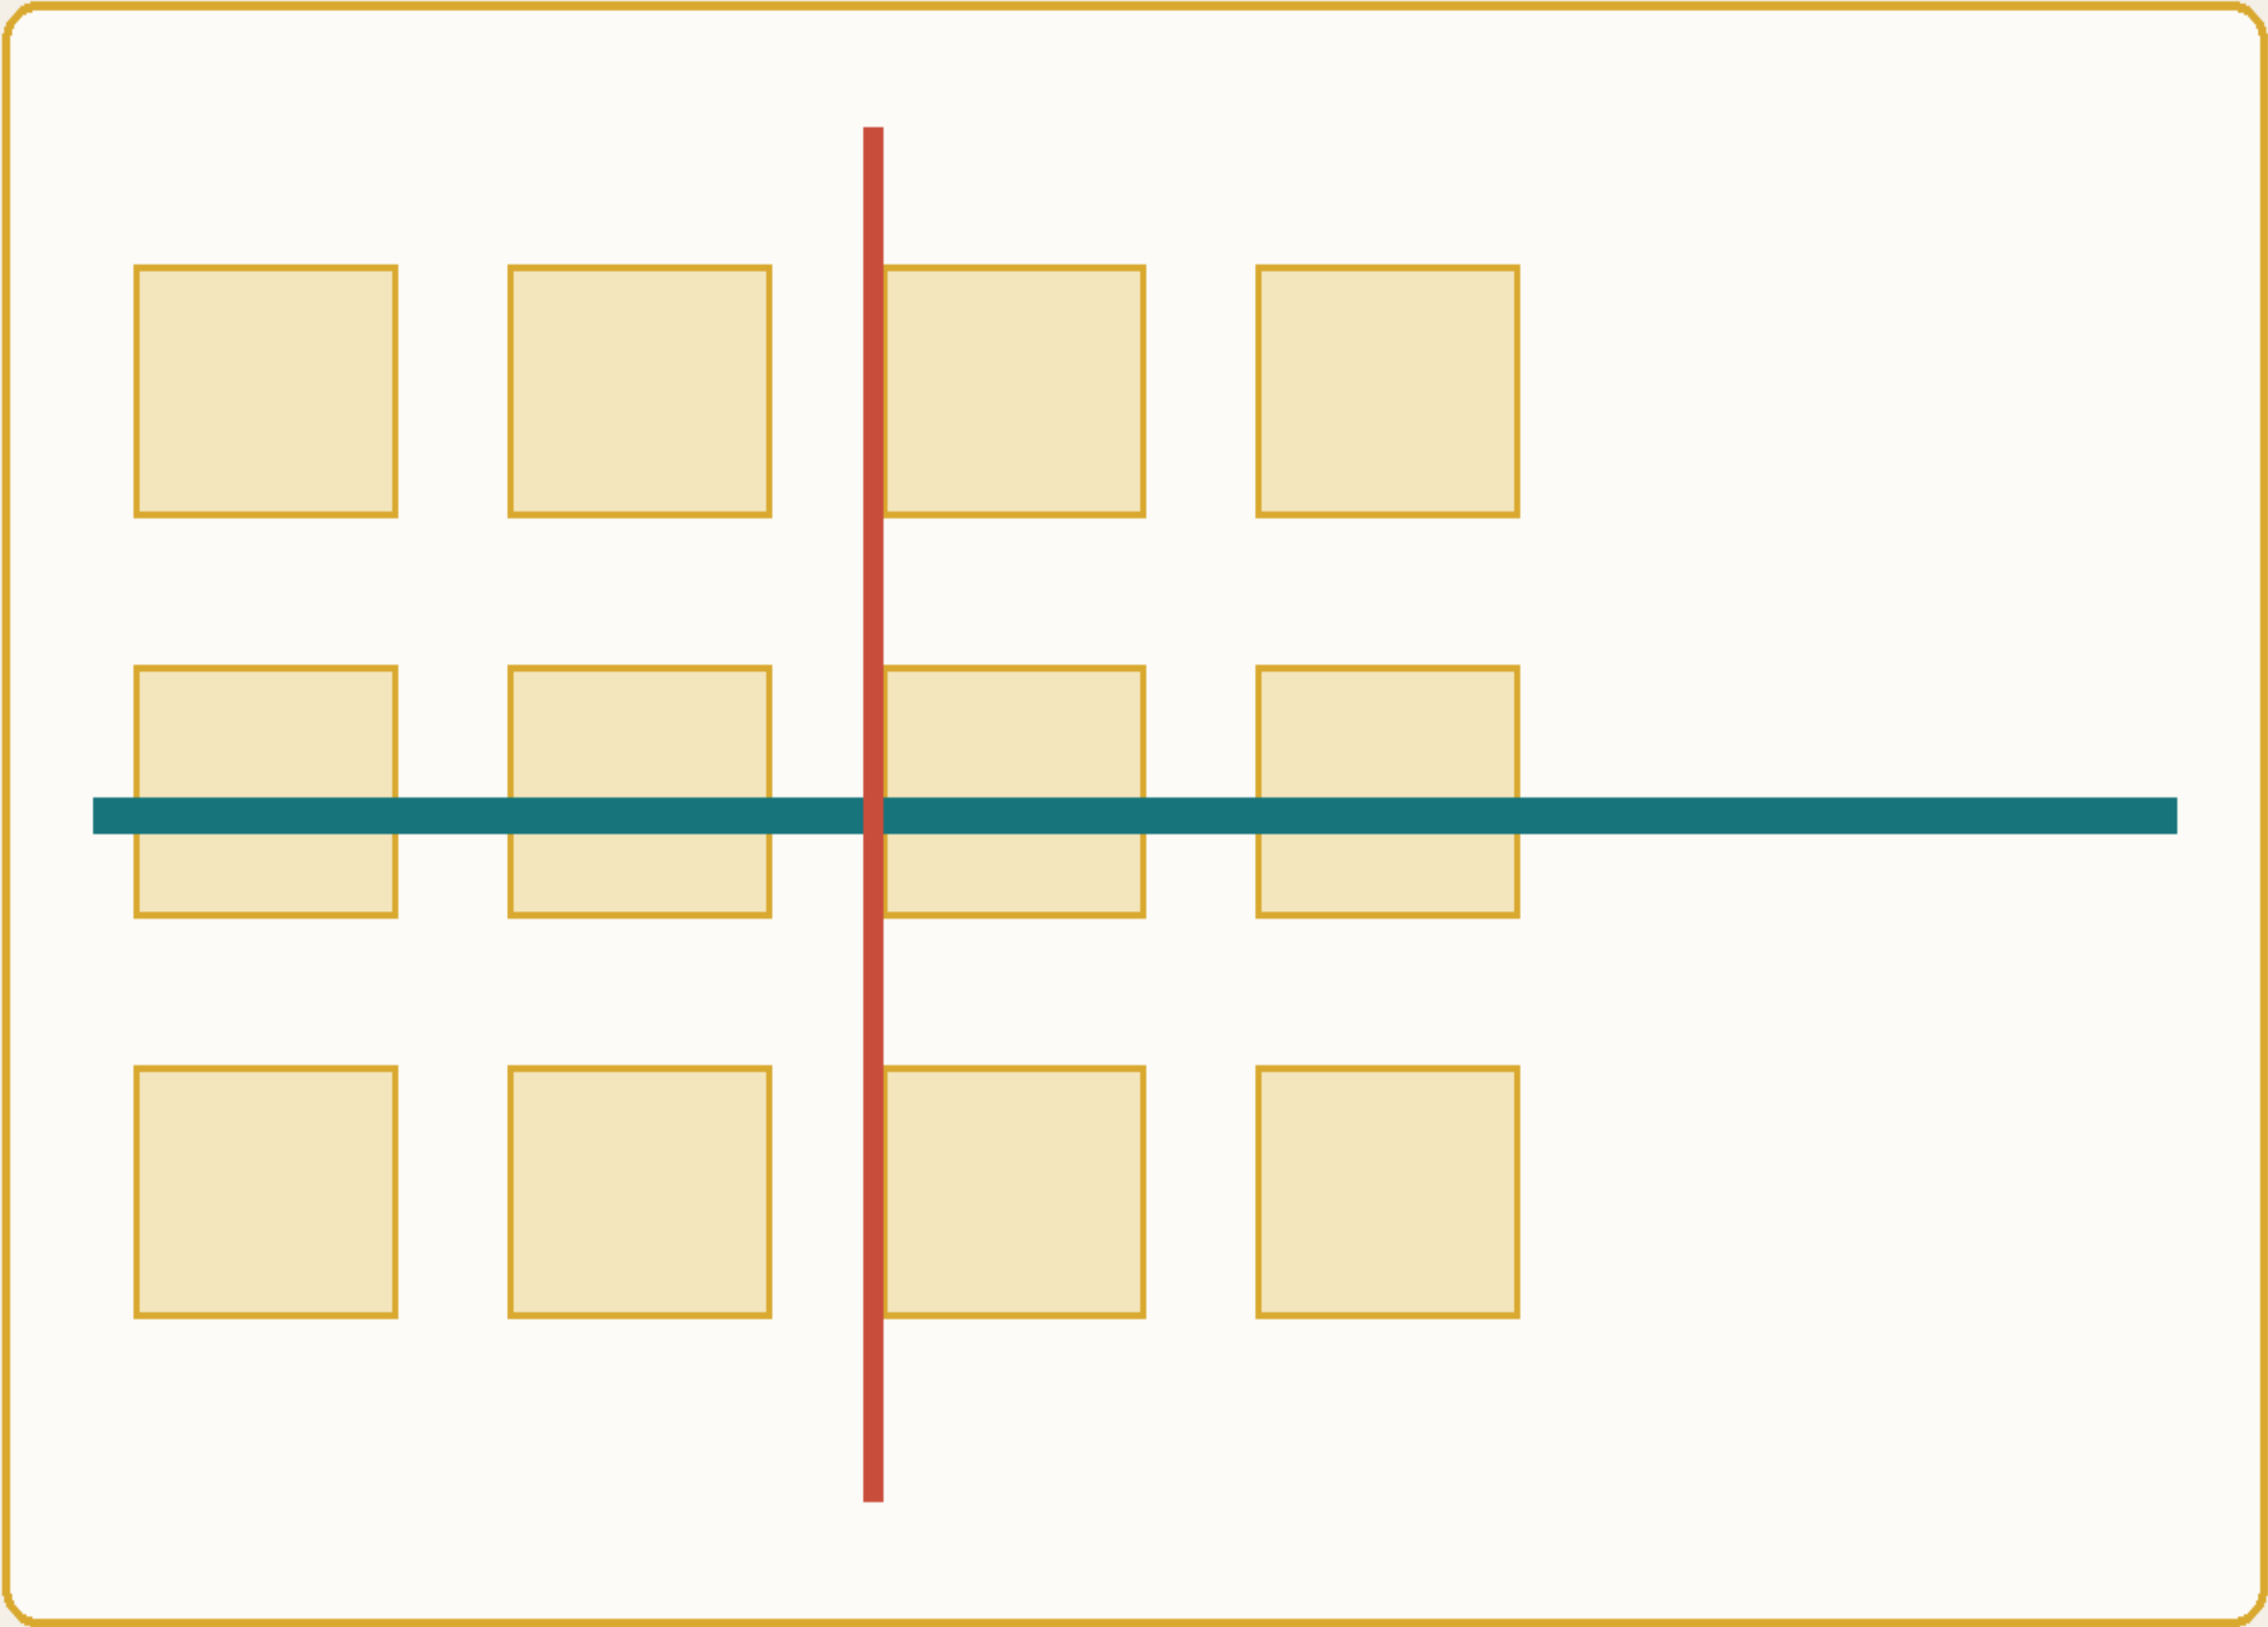

街→廊→庭→坊→校

保留—修补—再利用街—巷—院—坊序列。日常商户、学习、托育和人工服务先于创作活动；权利未清不进入首发。

街区开口


首层连续

物流分流

可逆样机

大钟寺 | 轨道—城市—文保复合街区

72.0ha 临时范围

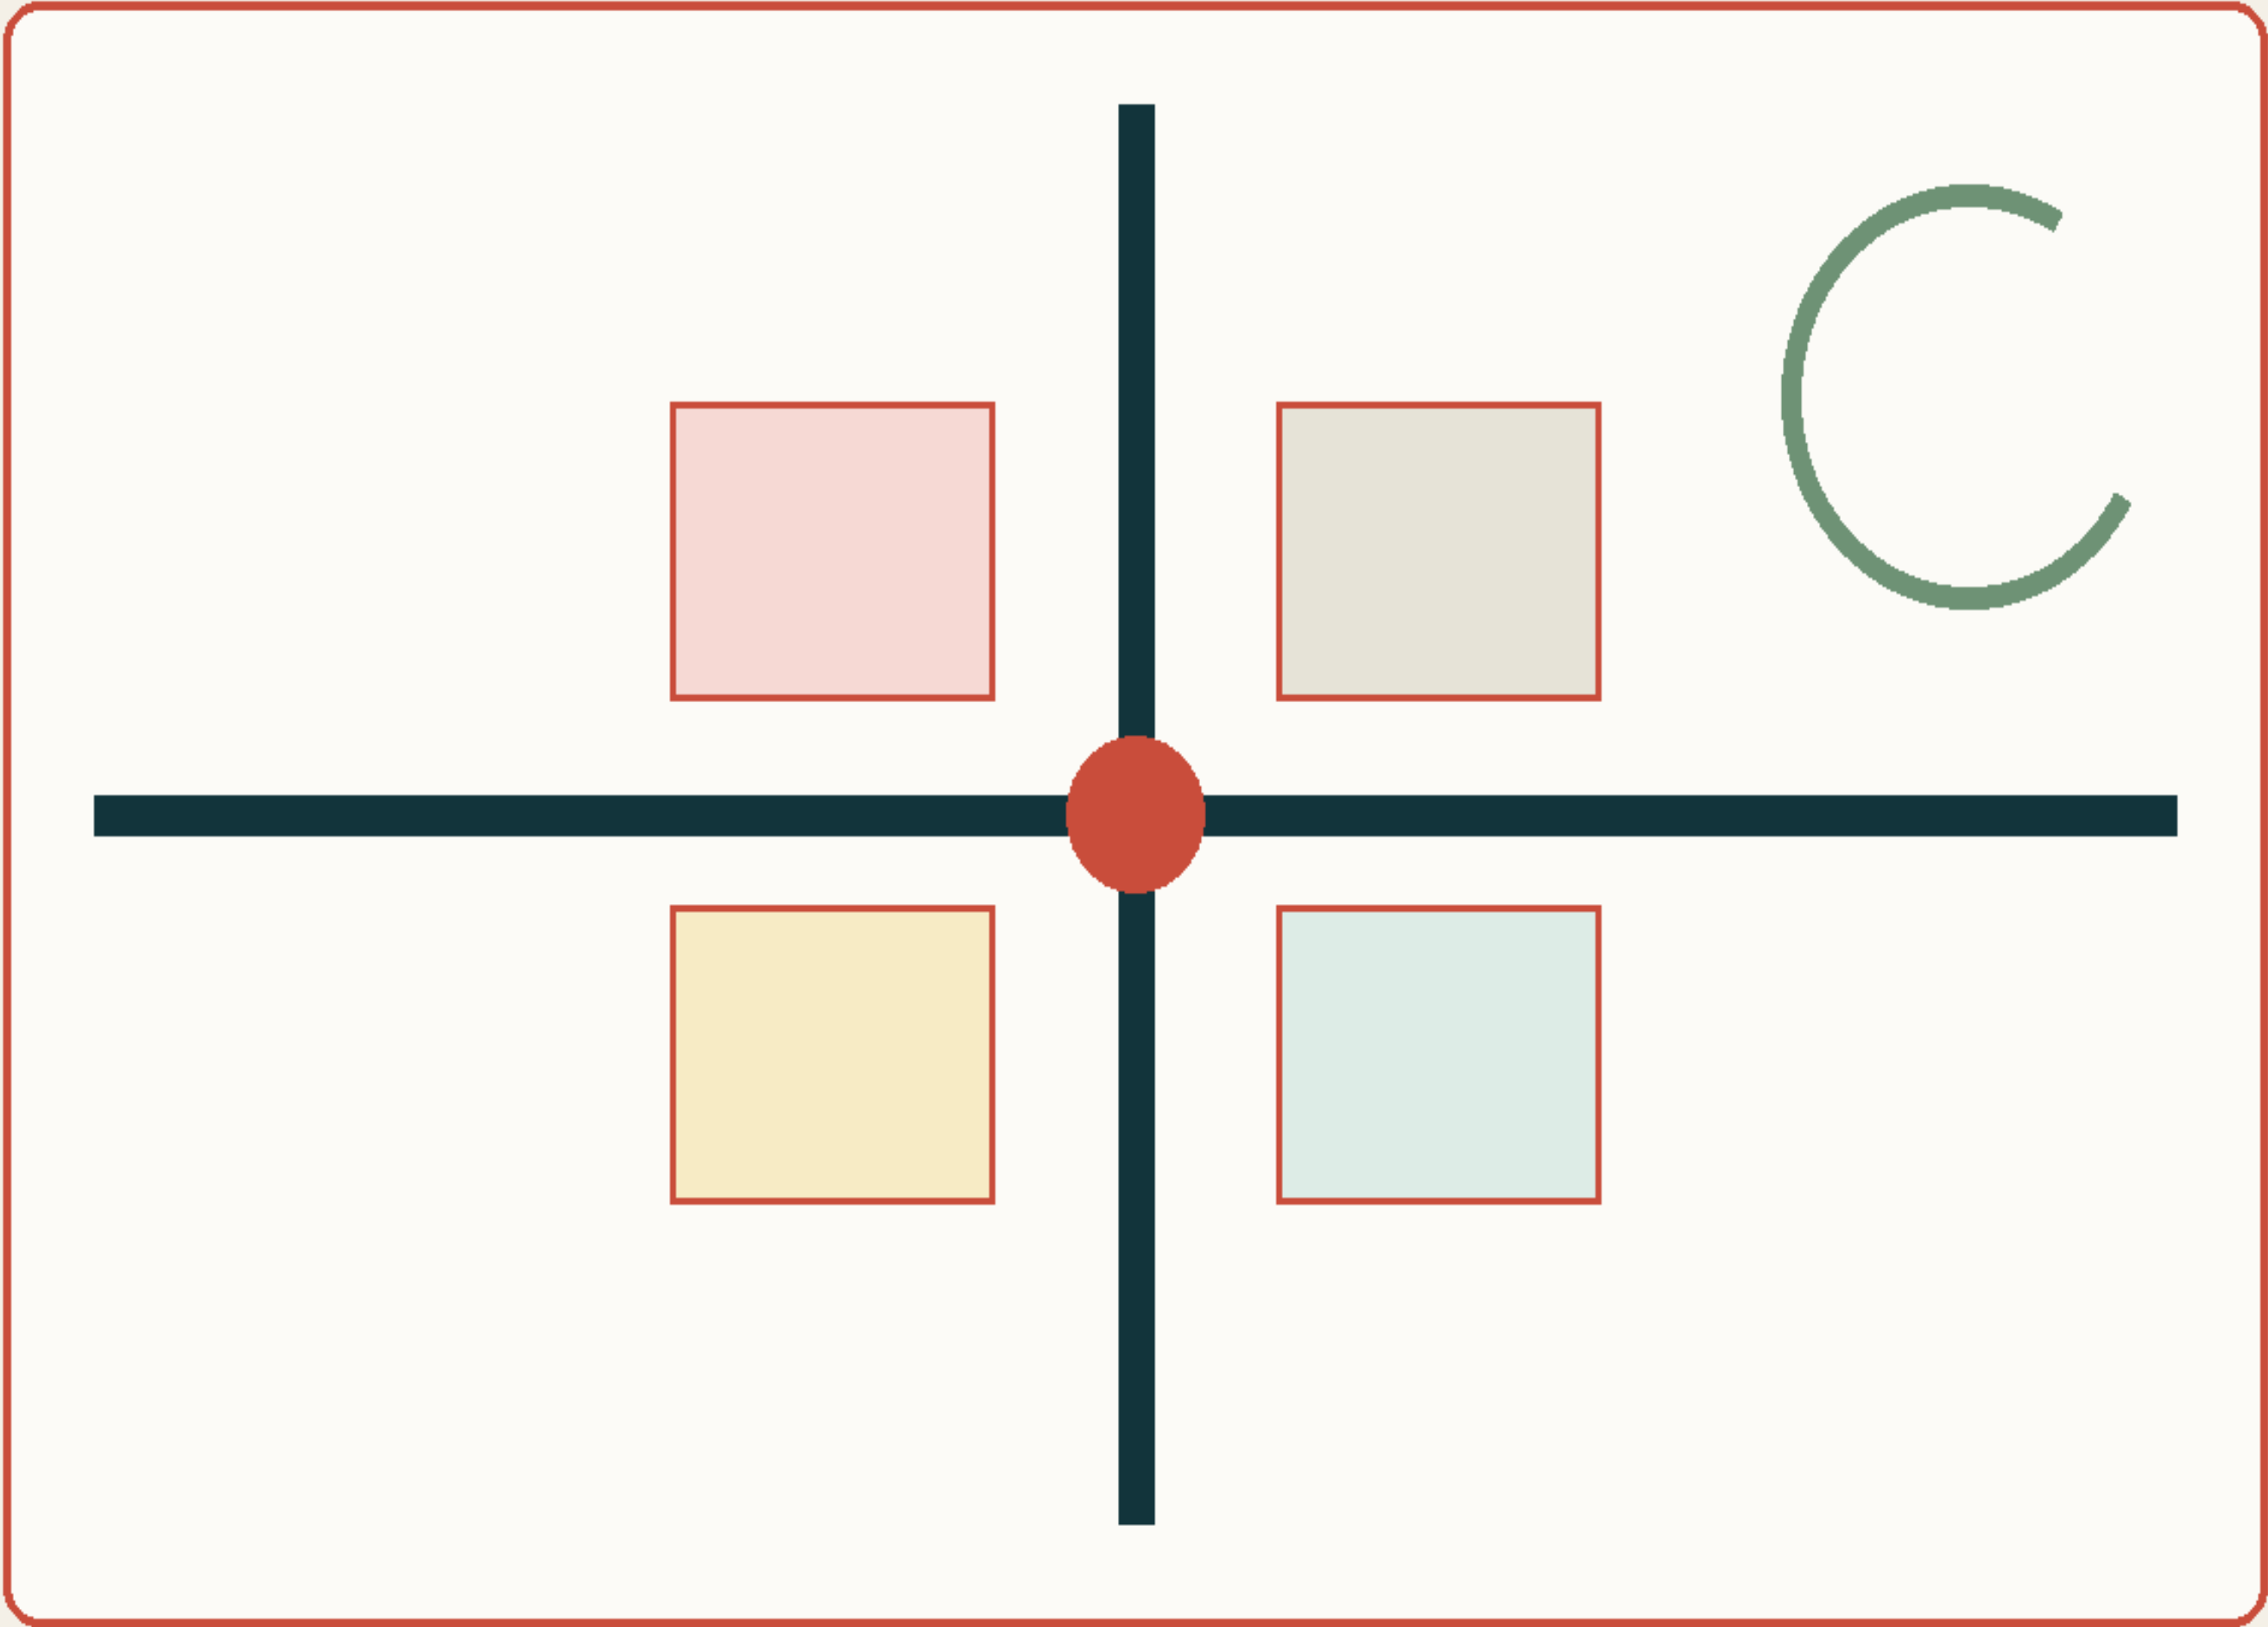

站→街→场→厅→静

四象限步行与自行车停放接入城市首层、蓝景/方恒界面和首发空间；觉生寺只建立安静关系，不伪造保护线。

街区开口

首层连续

物流分流

可逆样机

把专业著作的方法压进交付件

书不是装饰性引用：每一种方法都对应一张必须完成、可以被评审复核的图或表。

KROPF / PANERAI

街道—街区—地块—建筑

三处重点区现状/建议织体矩阵；识别保持、修补、打开、替换。

SPACEMATRIX

FAR × GSI × OSR × 层数

只在法定数据到位后形成地块强度表；不以概念面积伪装控规指标。

ALLAN B. JACOBS

街道用测量说话

五类现状/建议断面：人行、骑行、车行、树荫、首层、装卸和无障碍。

GORDON CULLEN

连续视景与门槛

三区各一条五分钟序列，检验到达、显露、围合、转折、安静与退出。

5 张必须成对的断面 / FIVE PAIRED SECTIONS

01 学知园站—下沉前场—花园/水岸



现状宽度/红线待实测

02 成府路—原点大厦—AI巷/校园



现状宽度/红线待实测

03 大钟寺四象限—蓝景/方恒



现状宽度/红线待实测

04 京张纵向底盘—横向缝合



现状宽度/红线待实测

05 清河/小月河蓝绿边缘



现状宽度/红线待实测

评分不靠词多，靠控制项能否闭环

把“官方事实、方案承诺、验收证据”拆开；未知不是空白，而是带资料请求、责任专业与阻断门的状态。

控制项	官方值	方案承诺	验收证据	门
边界/地块	UNKNOWN	不越正式红线	官方polygon+地块ID	G0
用地兼容	UNKNOWN	文化生产叠层不替代法定性质	批准用地与兼容表	G1
规模/FAR/高度/密度	UNKNOWN	不填概念假值	批复值+逐地块复算	G1
公共设施	UNKNOWN	日常服务不被活动替代	类型/规模/位置/移交	G1
道路/公共通道	UNKNOWN	五断面+九缝合	位置/宽度/开放机制	G2
轨道/文保	UNKNOWN	四象限+安静关系	正式范围与专项意见	G3
消防/日照/风热声	UNKNOWN	专项优先于效果图	现行标准专业报告	G3
无障碍/市政	UNKNOWN	现场任务+断网底线	实测任务与容量确认	G3
形态/第五立面	UNKNOWN	街区—地块—建筑界面控制	控制图则+逐栋审查	G2

G0

资料冻结

资料/坐标/权属

G1

法定控制

零关键unknown

G2

空间交付

100%逐栋+断面节点

G3

专项技术

八类专项通过

G4

建成与使用

移交+12月复盘

进入施工包的硬条件：所有适用法定字段有官方值、来源、批复、效力日期；建设关键 unknown = 0。