

之字京张 ZHI-BELT


以京张铁路“之”字展线为基因的折返迭代型 AI 创新带

百年京张AI创新带城市设计开源征集 · 正式方案（概念建议）

一脊 · 三折 · 两翼
一条9.4公里绿脊 | 三处折返重点区 | 中关村要素翼与小月河场景翼


之字回路：研发→转译→应用→反馈→要素回流

- 依据《百年京张AI创新带城市设计国际方案征集资格预审公告》（海淀分局，2026-05-09）与面向全球智能体开源征集任务书组织全部设计任务。
- 官方精确红线未公开：使用维护者依公告文字四至与约面积推定的临时粗略边界（provisional_constraint），仅在EPSG:4548下复算面积，不构成红线；官方多边形发布后
- 三层范围：统筹研究43.6 km²（战略研究）→ 总体设计11.4 km²（控规级城市设计）→ 重点区域368.4 ha（规划综合实施方案深度）。

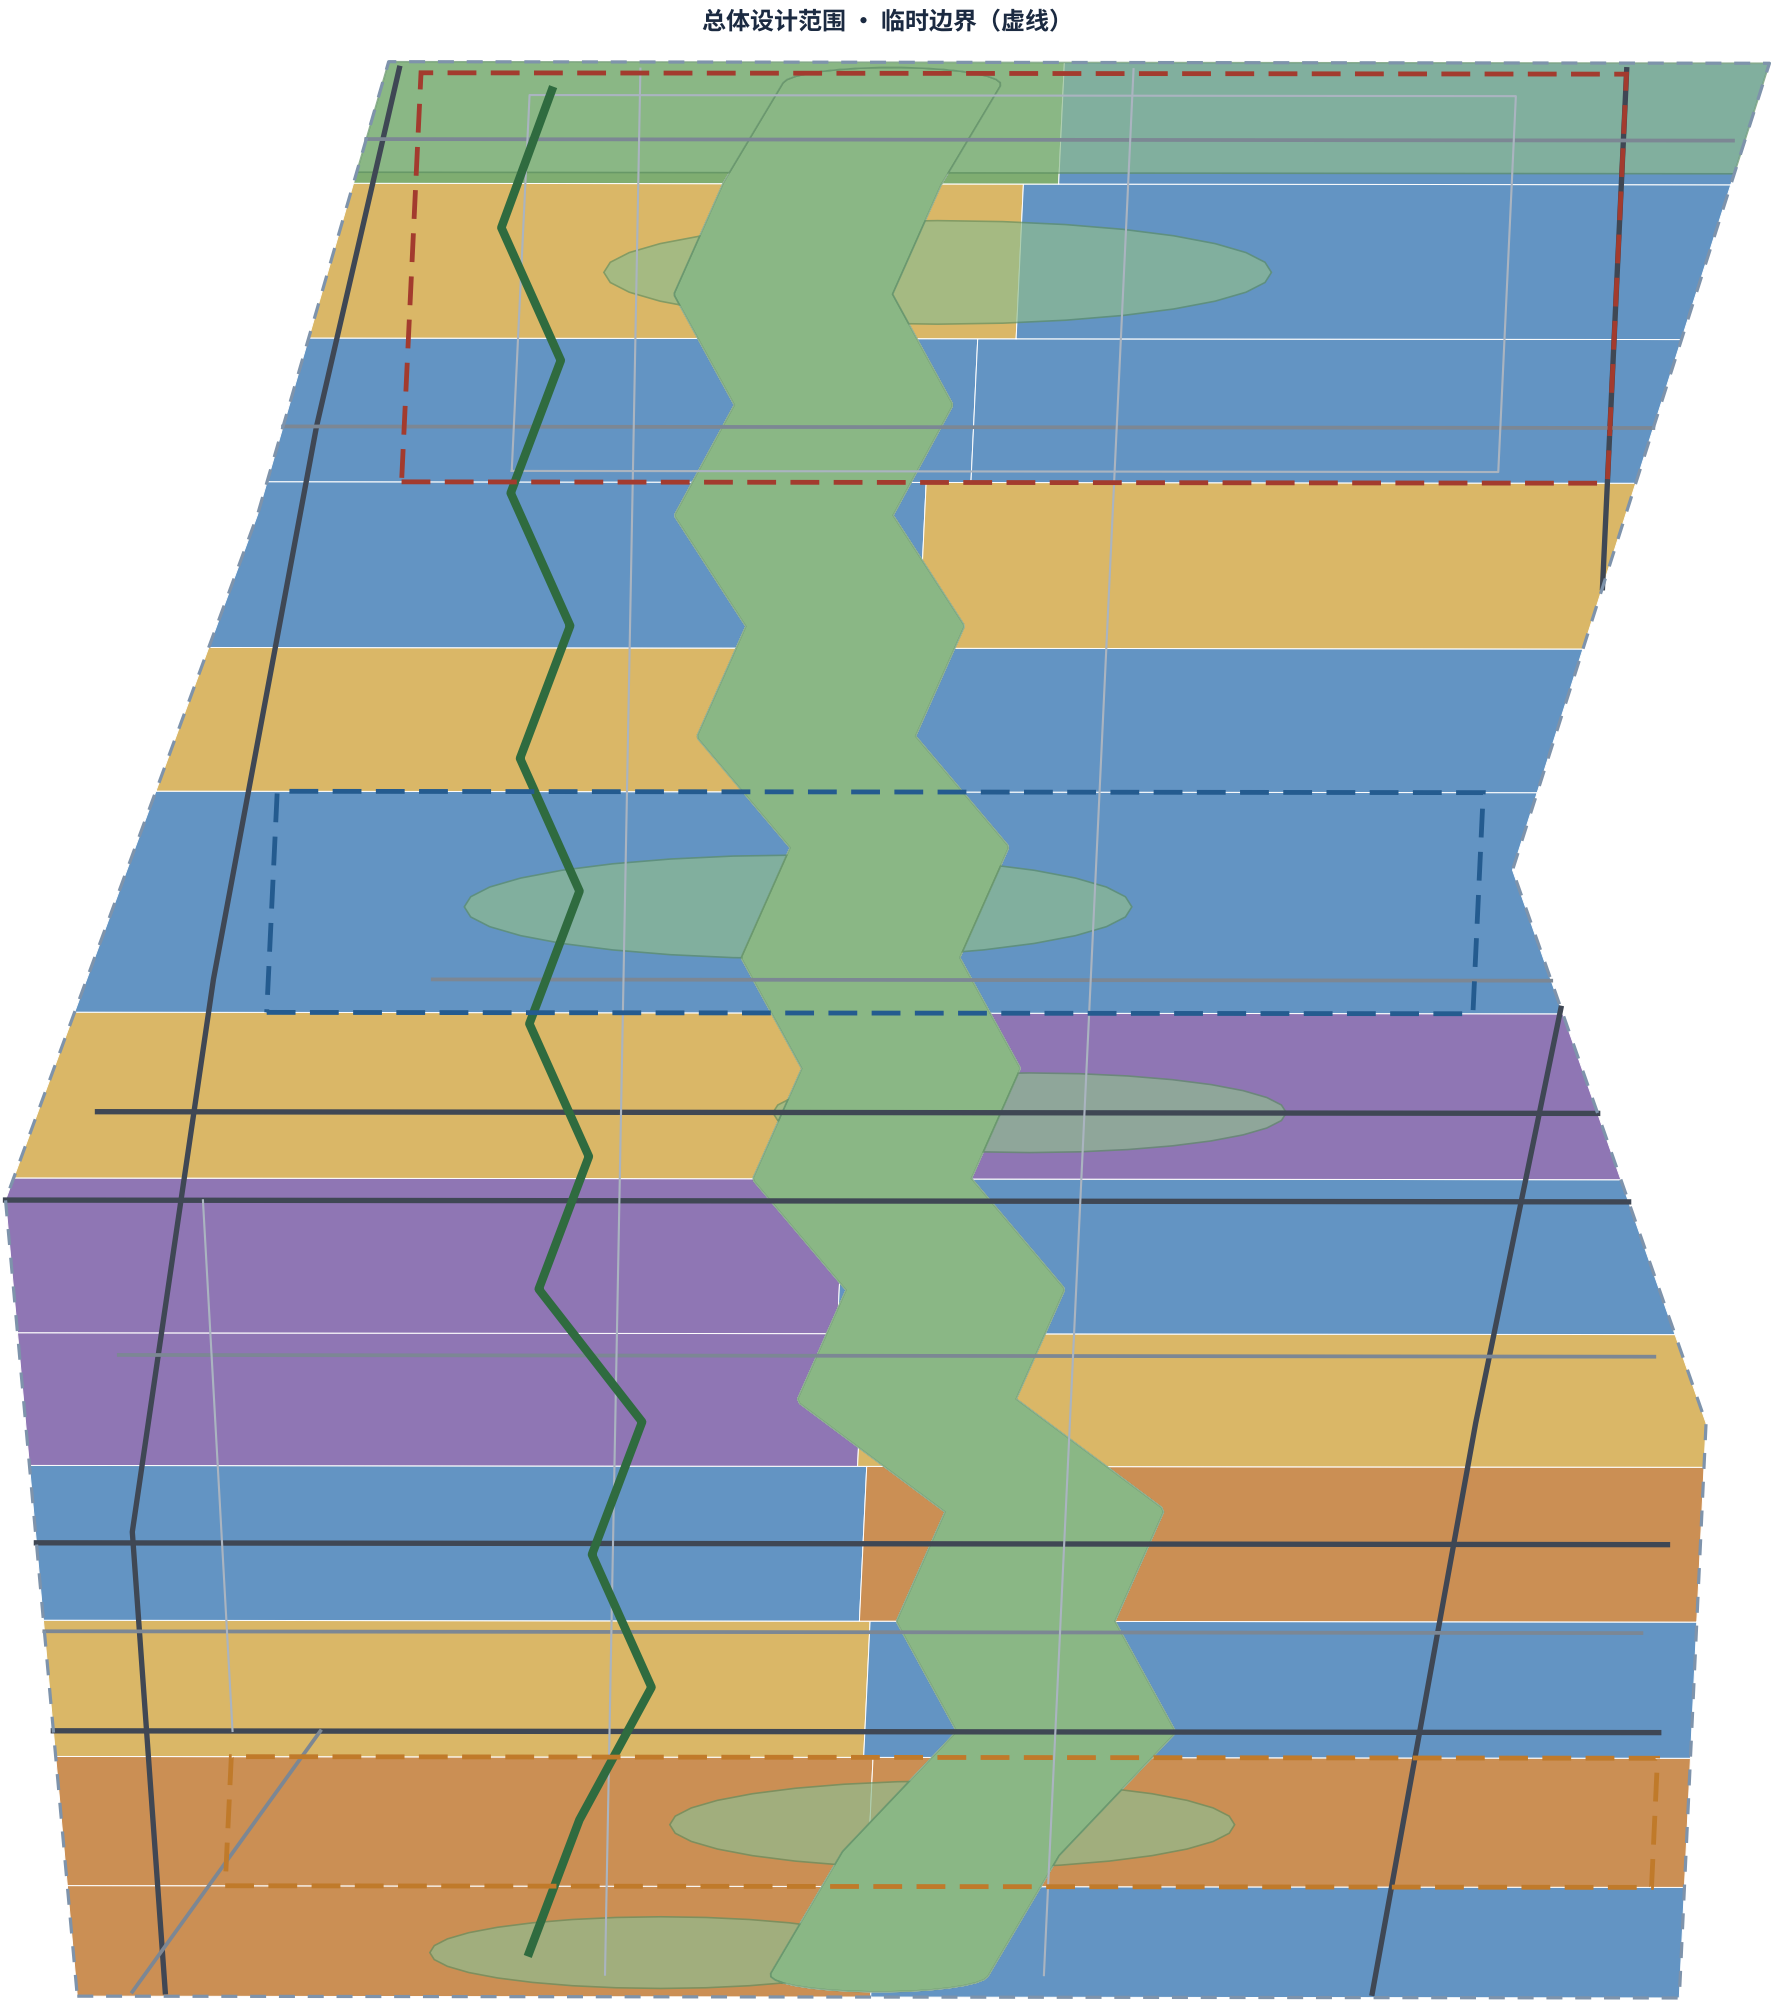


- 命名体系：主名「之字京张」（ZHI-BELT）；“之”为形（之字展线），“智”为义（智能），“志”为向（自立创新）；ZHI在中英文语境双关成立。
- Logo方向：三折线=文化带/体验带/创新带，折点圆点=创新回环；京张砖红、海淀科技蓝、公园绿三色；可延展为导视、公里标与公共装置模件（概念建议）。
- 之字回路：北折·智造（众智园）→ 中折·智源（AI原点社区）→ 南折·智用（大钟寺）→ 东翼场景反馈（小月河）→ 西翼要素回流（中关村）→ 再智造。
- 6个全球案例：斯坦福研究园（校产协同）、云栖小镇（场景驱动）、裕隆创新区（共同治理）、国王十字（站城一体）、河套（制度创新）、首尔DMC（数字文化展示）。
- AI公里标0-9沿绿脊布置，承载荣誉展示与公共AI体验；零公里标（南端）、折返台（原点社区）、智用信号塔（大钟寺）为三处朝圣地标。

一脊三折两翼 · 空间结构

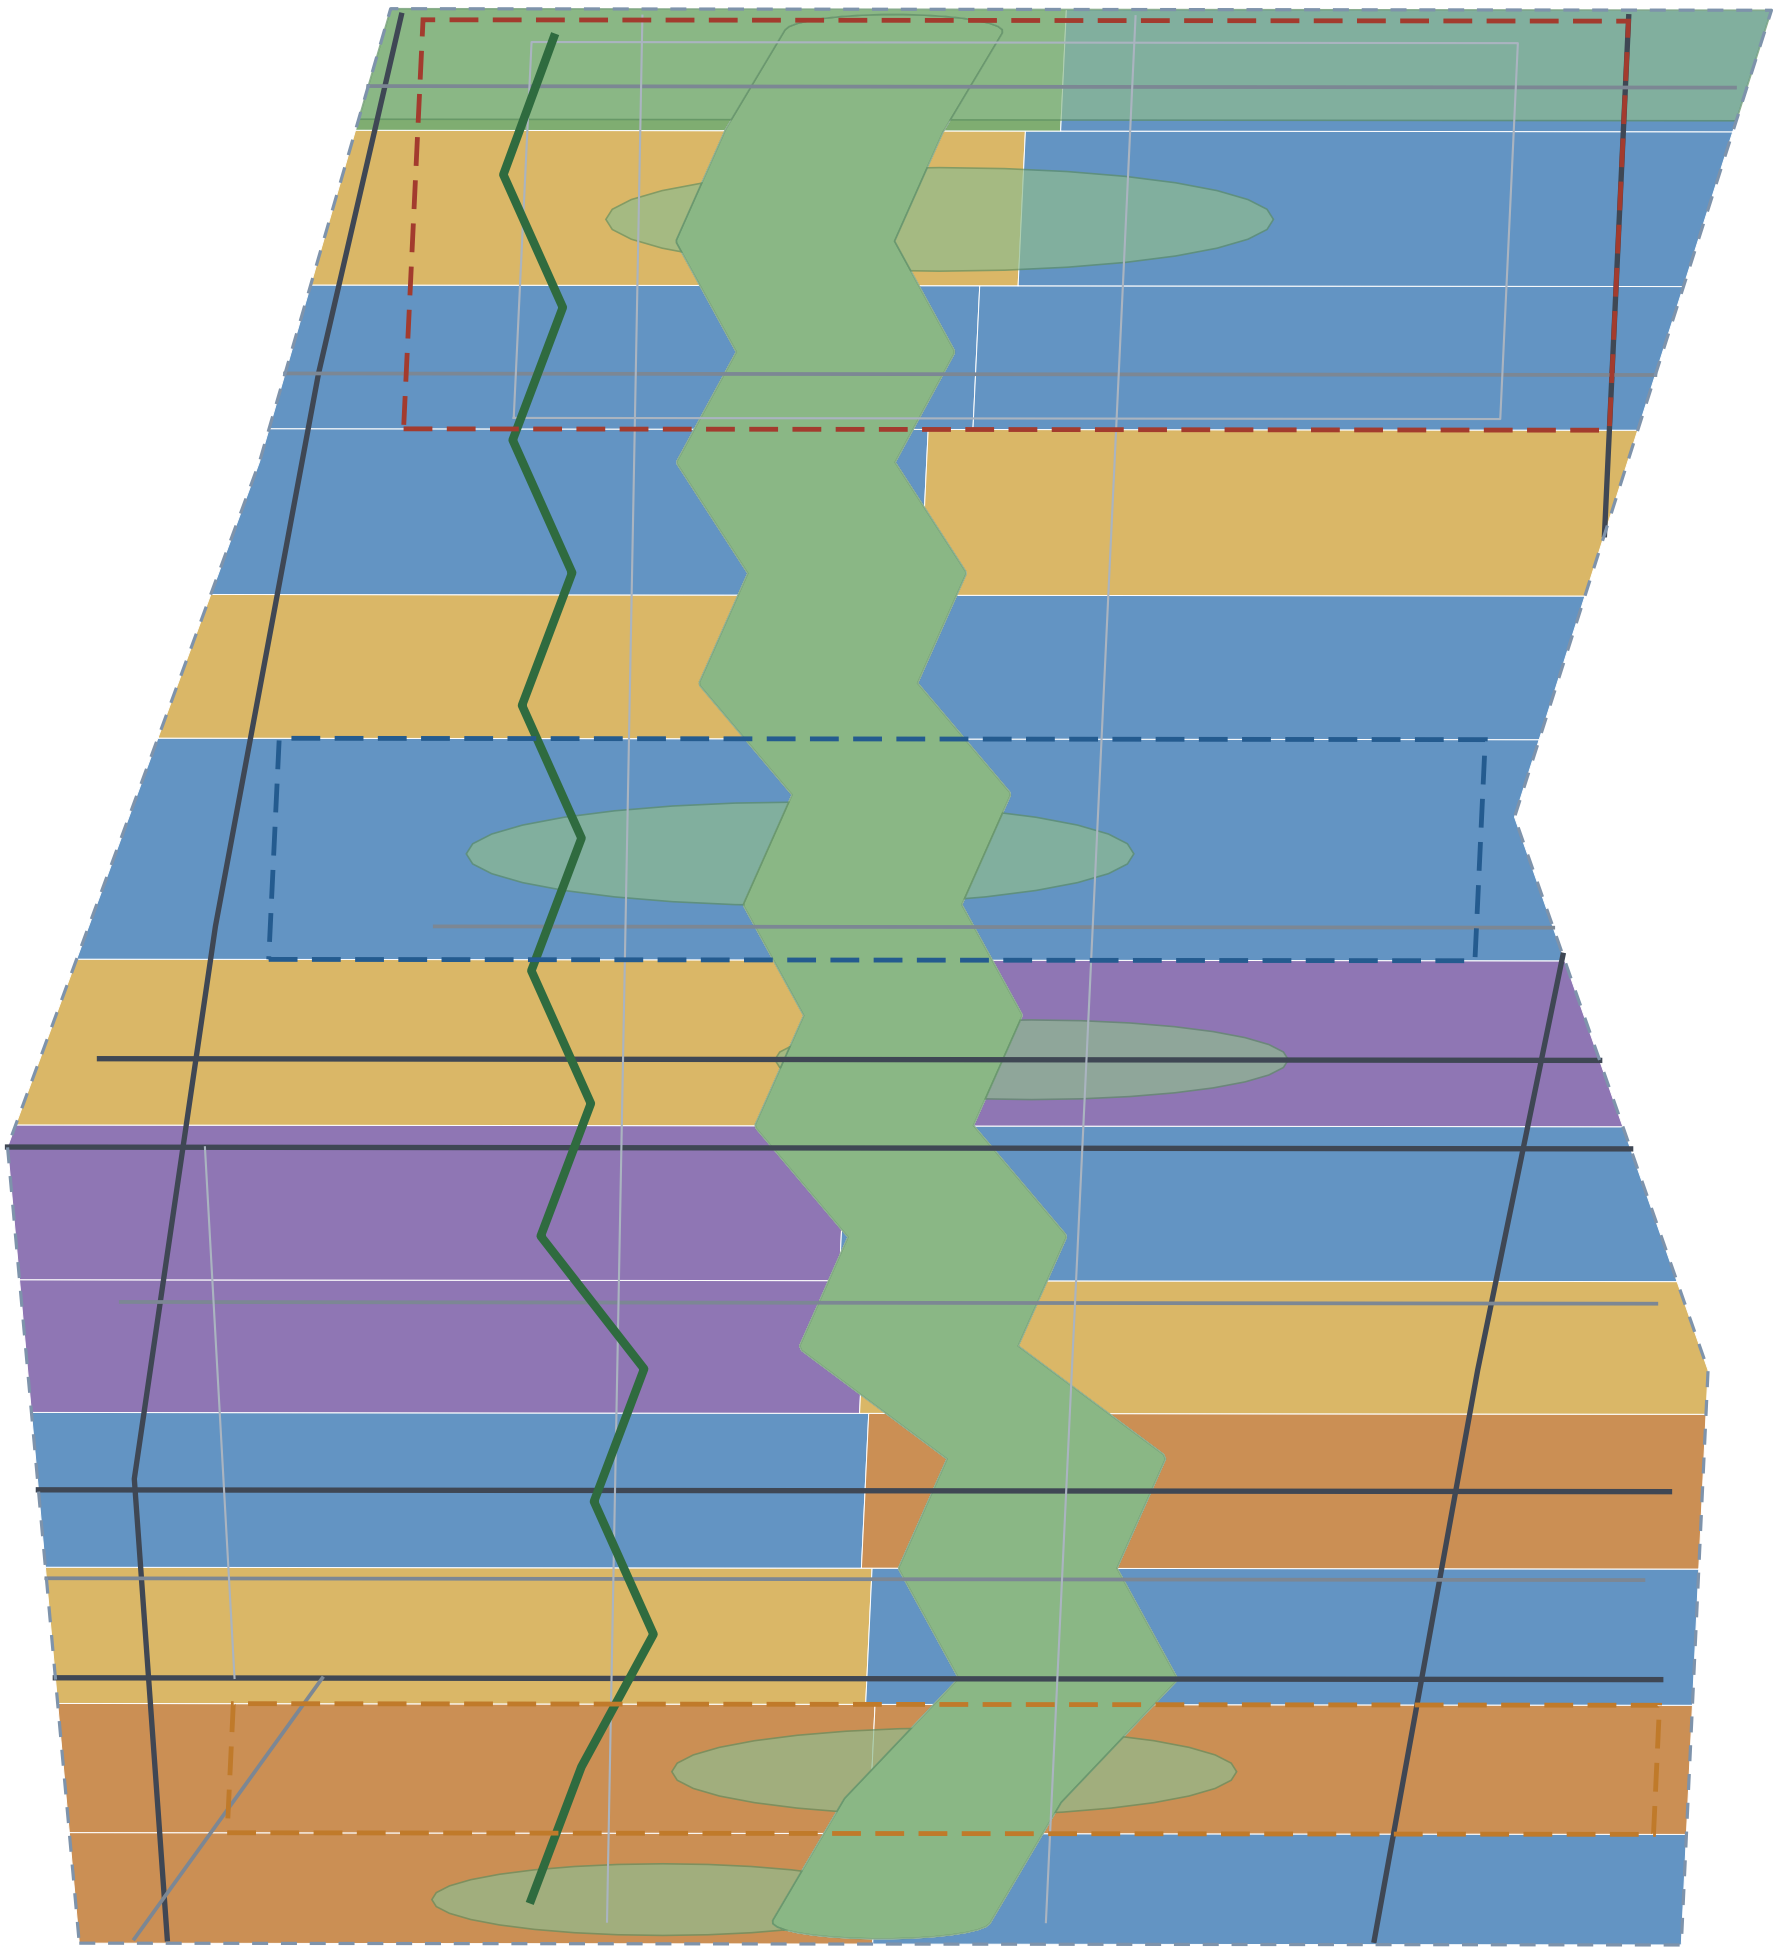


- 用地按国土空间用地用海分类表达：科研0802约458万m²、居住0701约227万m²、绿地1401约188万m²、商业05约140万m²、教育0804约128万m²（EPSG:4548复算）。
- 拓扑安全：全部用地由同一顶点集切分，无缝隙、无重叠，面积可复算；绿脊为主轴组织南北三段功能。
- 建筑概念体量127组表达产业空间供给量级；容积率、高度、密度无官方控规条件，一律待正式数据补齐。


概念用地分区

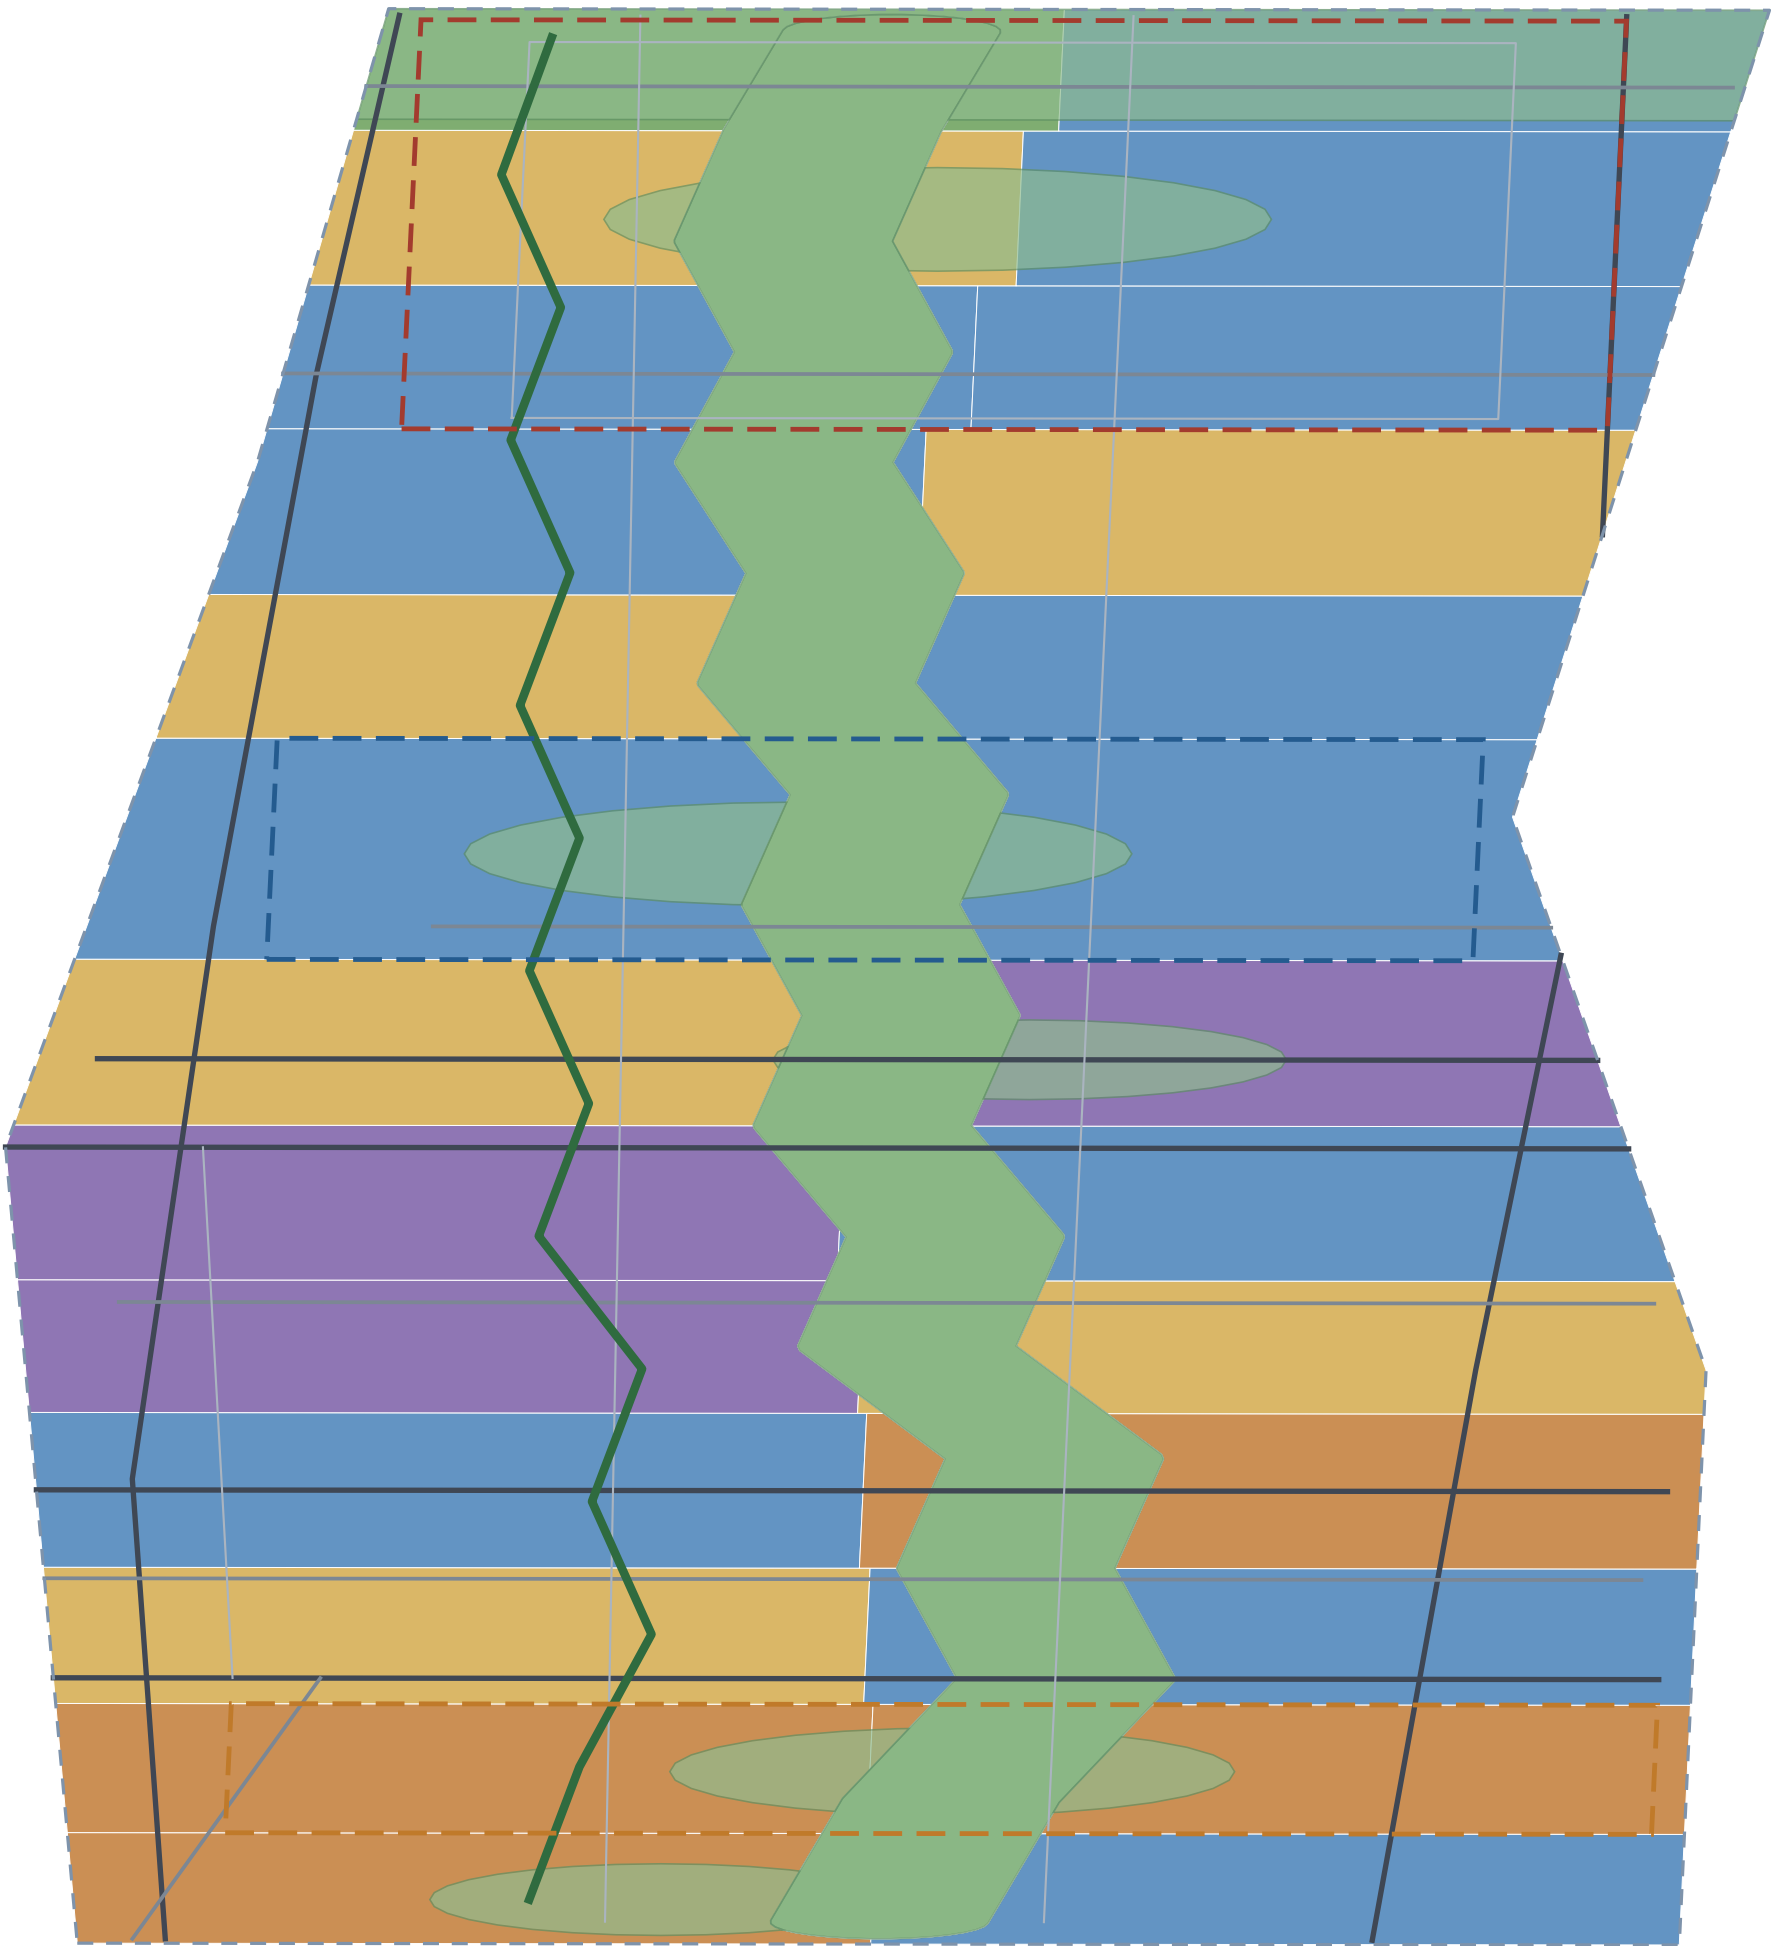

- 北折·智造：众智园AI自主创新加速区（192.1ha）——花园型全栈自主街区；折返实验场、红队沙盘、标准工作坊三处产业测试验证场景；清河界面蓝绿创新廊。
- 中折·智源：北京AI原点社区（104.3ha）——近校型成果转化与开源人才社区；开源发布厅、近校转化街；校区-园区慢行缝合。
- 南折·智用：大钟寺AI产业集聚区（72.0ha）——城市型智能经济与国际交往街区；站四象限步行连通；智用路演客厅、数据要素会客厅。
- 三处重点区多边形均为临时粗略边界，上述结论为方向性概念建议，供专业团队深化。

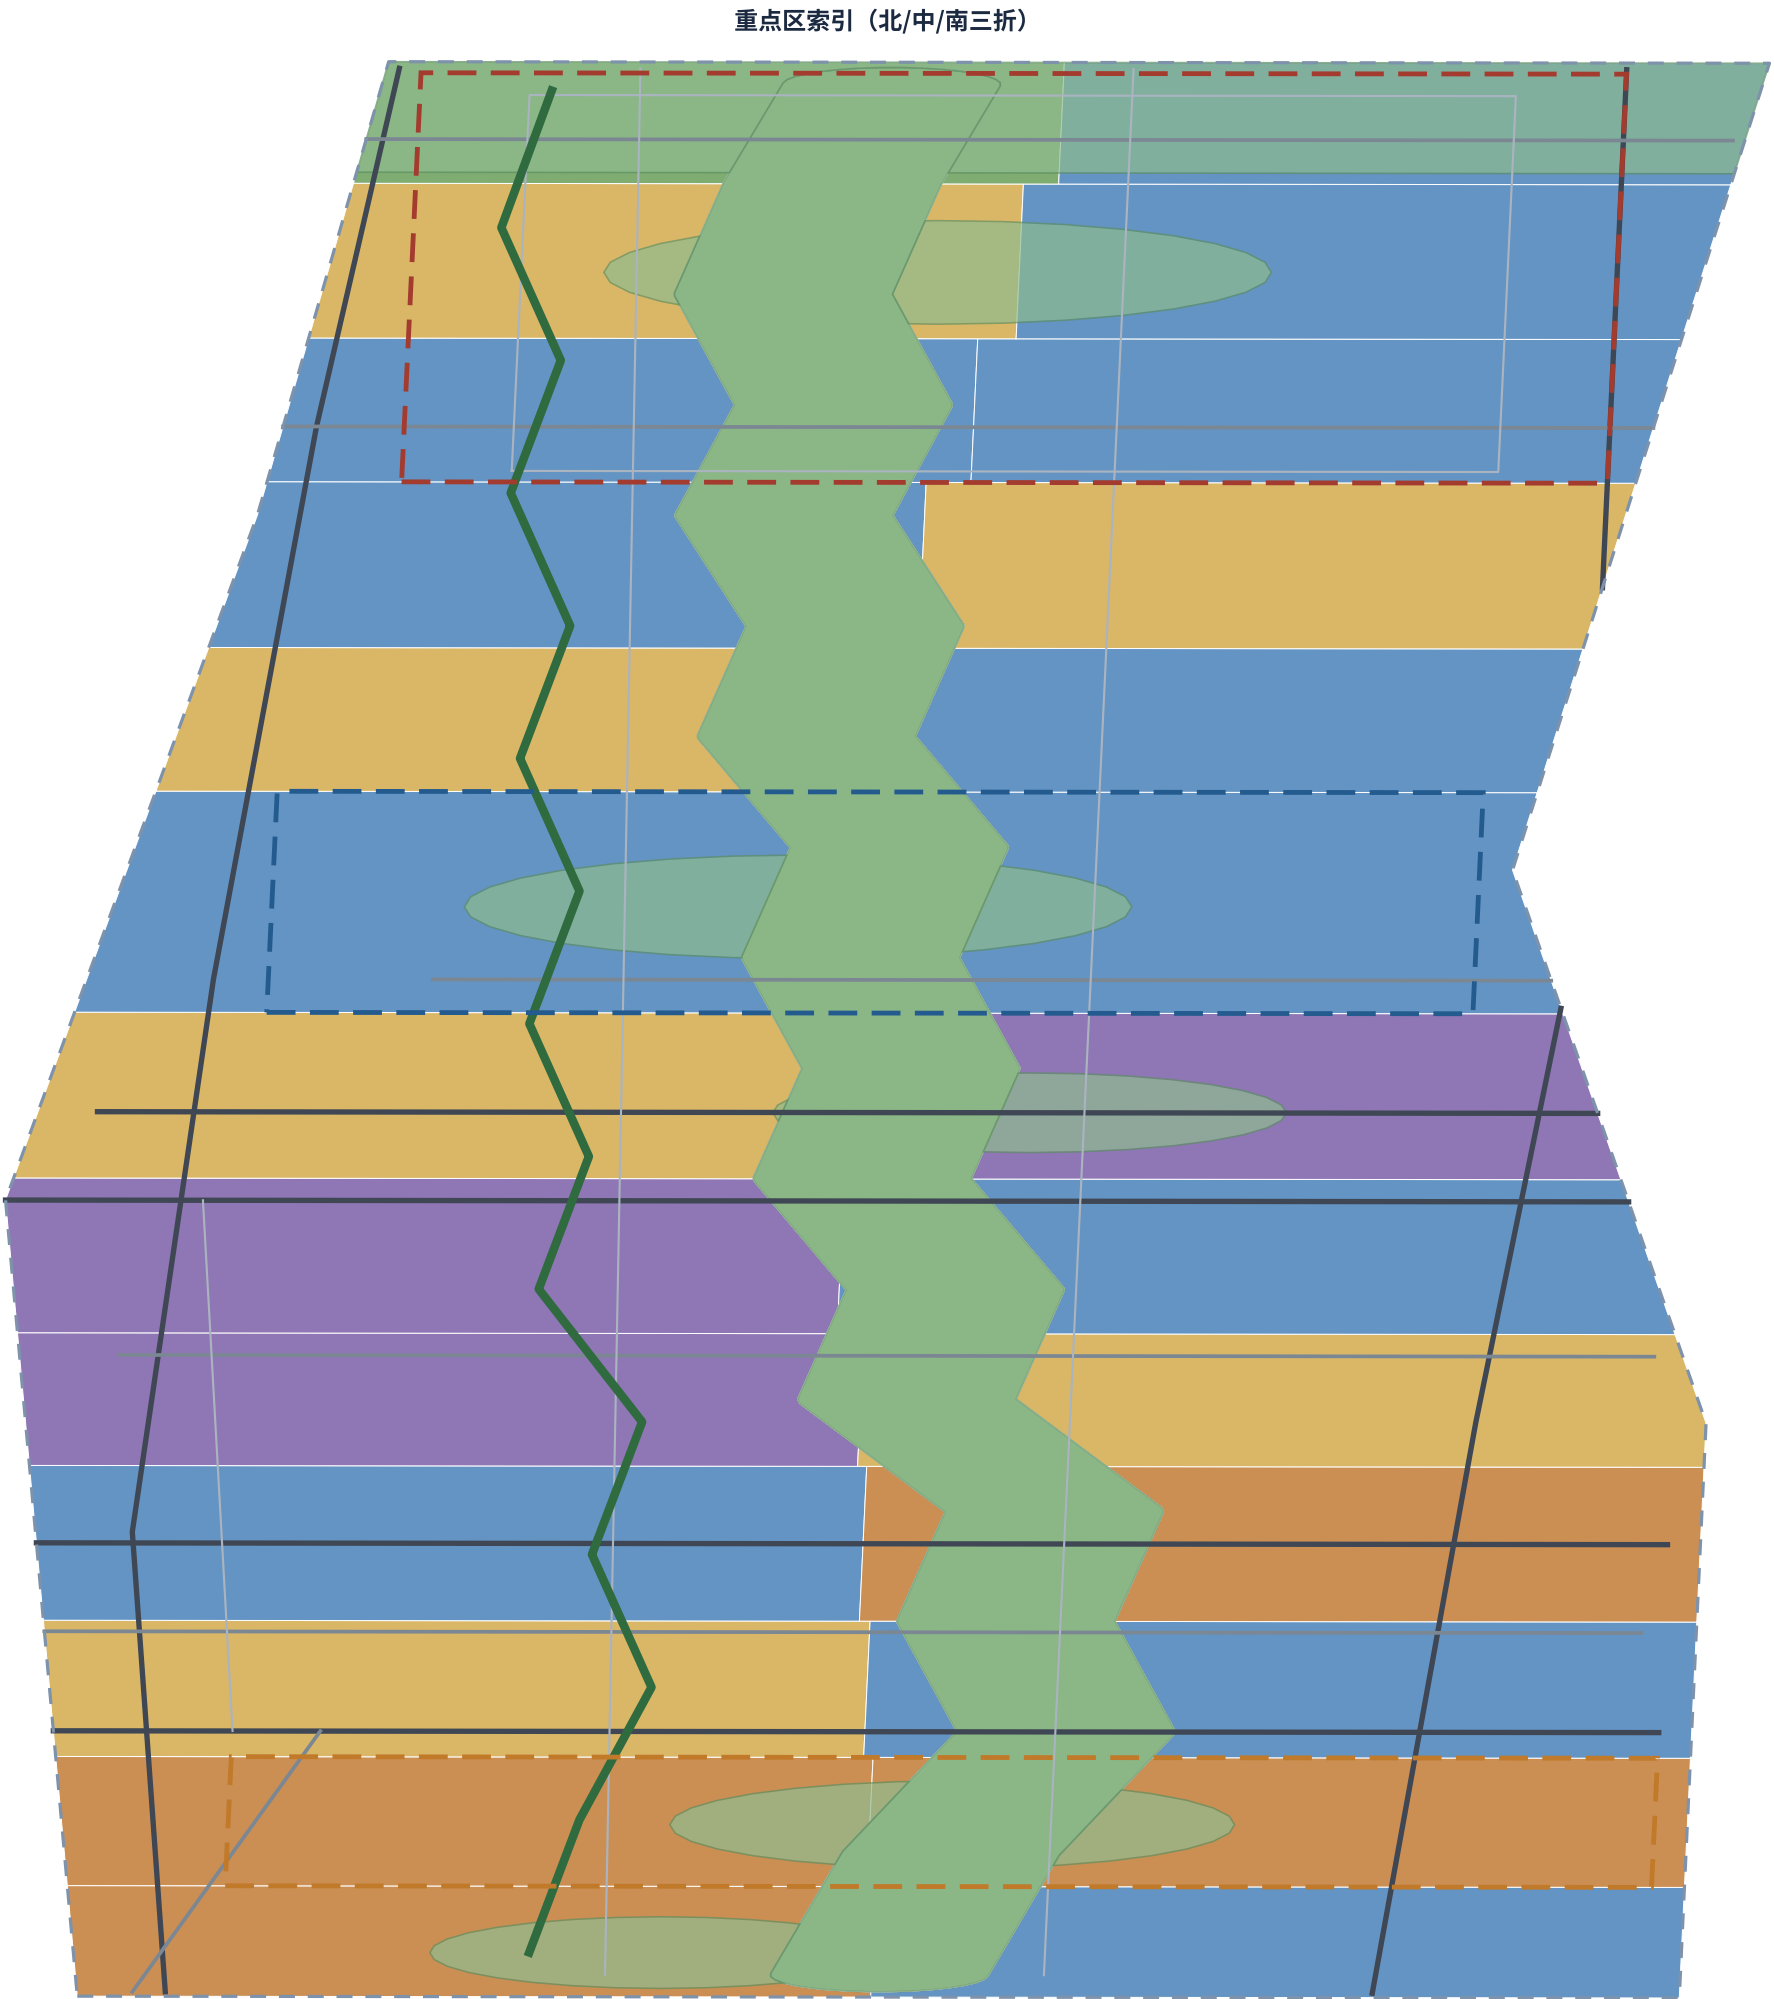


- 交通：纵向走廊（学院路—西土城路 / 大钟寺东路—荷清路）+ 横向缝合（北三环、知春路、成府路、清华东路、五环辅路）+ 绿脊两侧慢行次干（概念）；道路中心线总长约56.0 km。
- 轨道：13号、4号、10号、12号线为近似示意（公开信息），写入constraints图层，不代表官方线网图；站点一体化以概念建议表述。
- 蓝绿：一脊两水多园——9.4km绿脊+清河/万泉河-小月河界面+折返公园；绿地率约23.2%、公共空间占比约1.9%（概念建议值）。
- 道岔缝合口×8修复铁路百年分割；端侧算力驿站与分布式能源为新型基础设施概念原型。

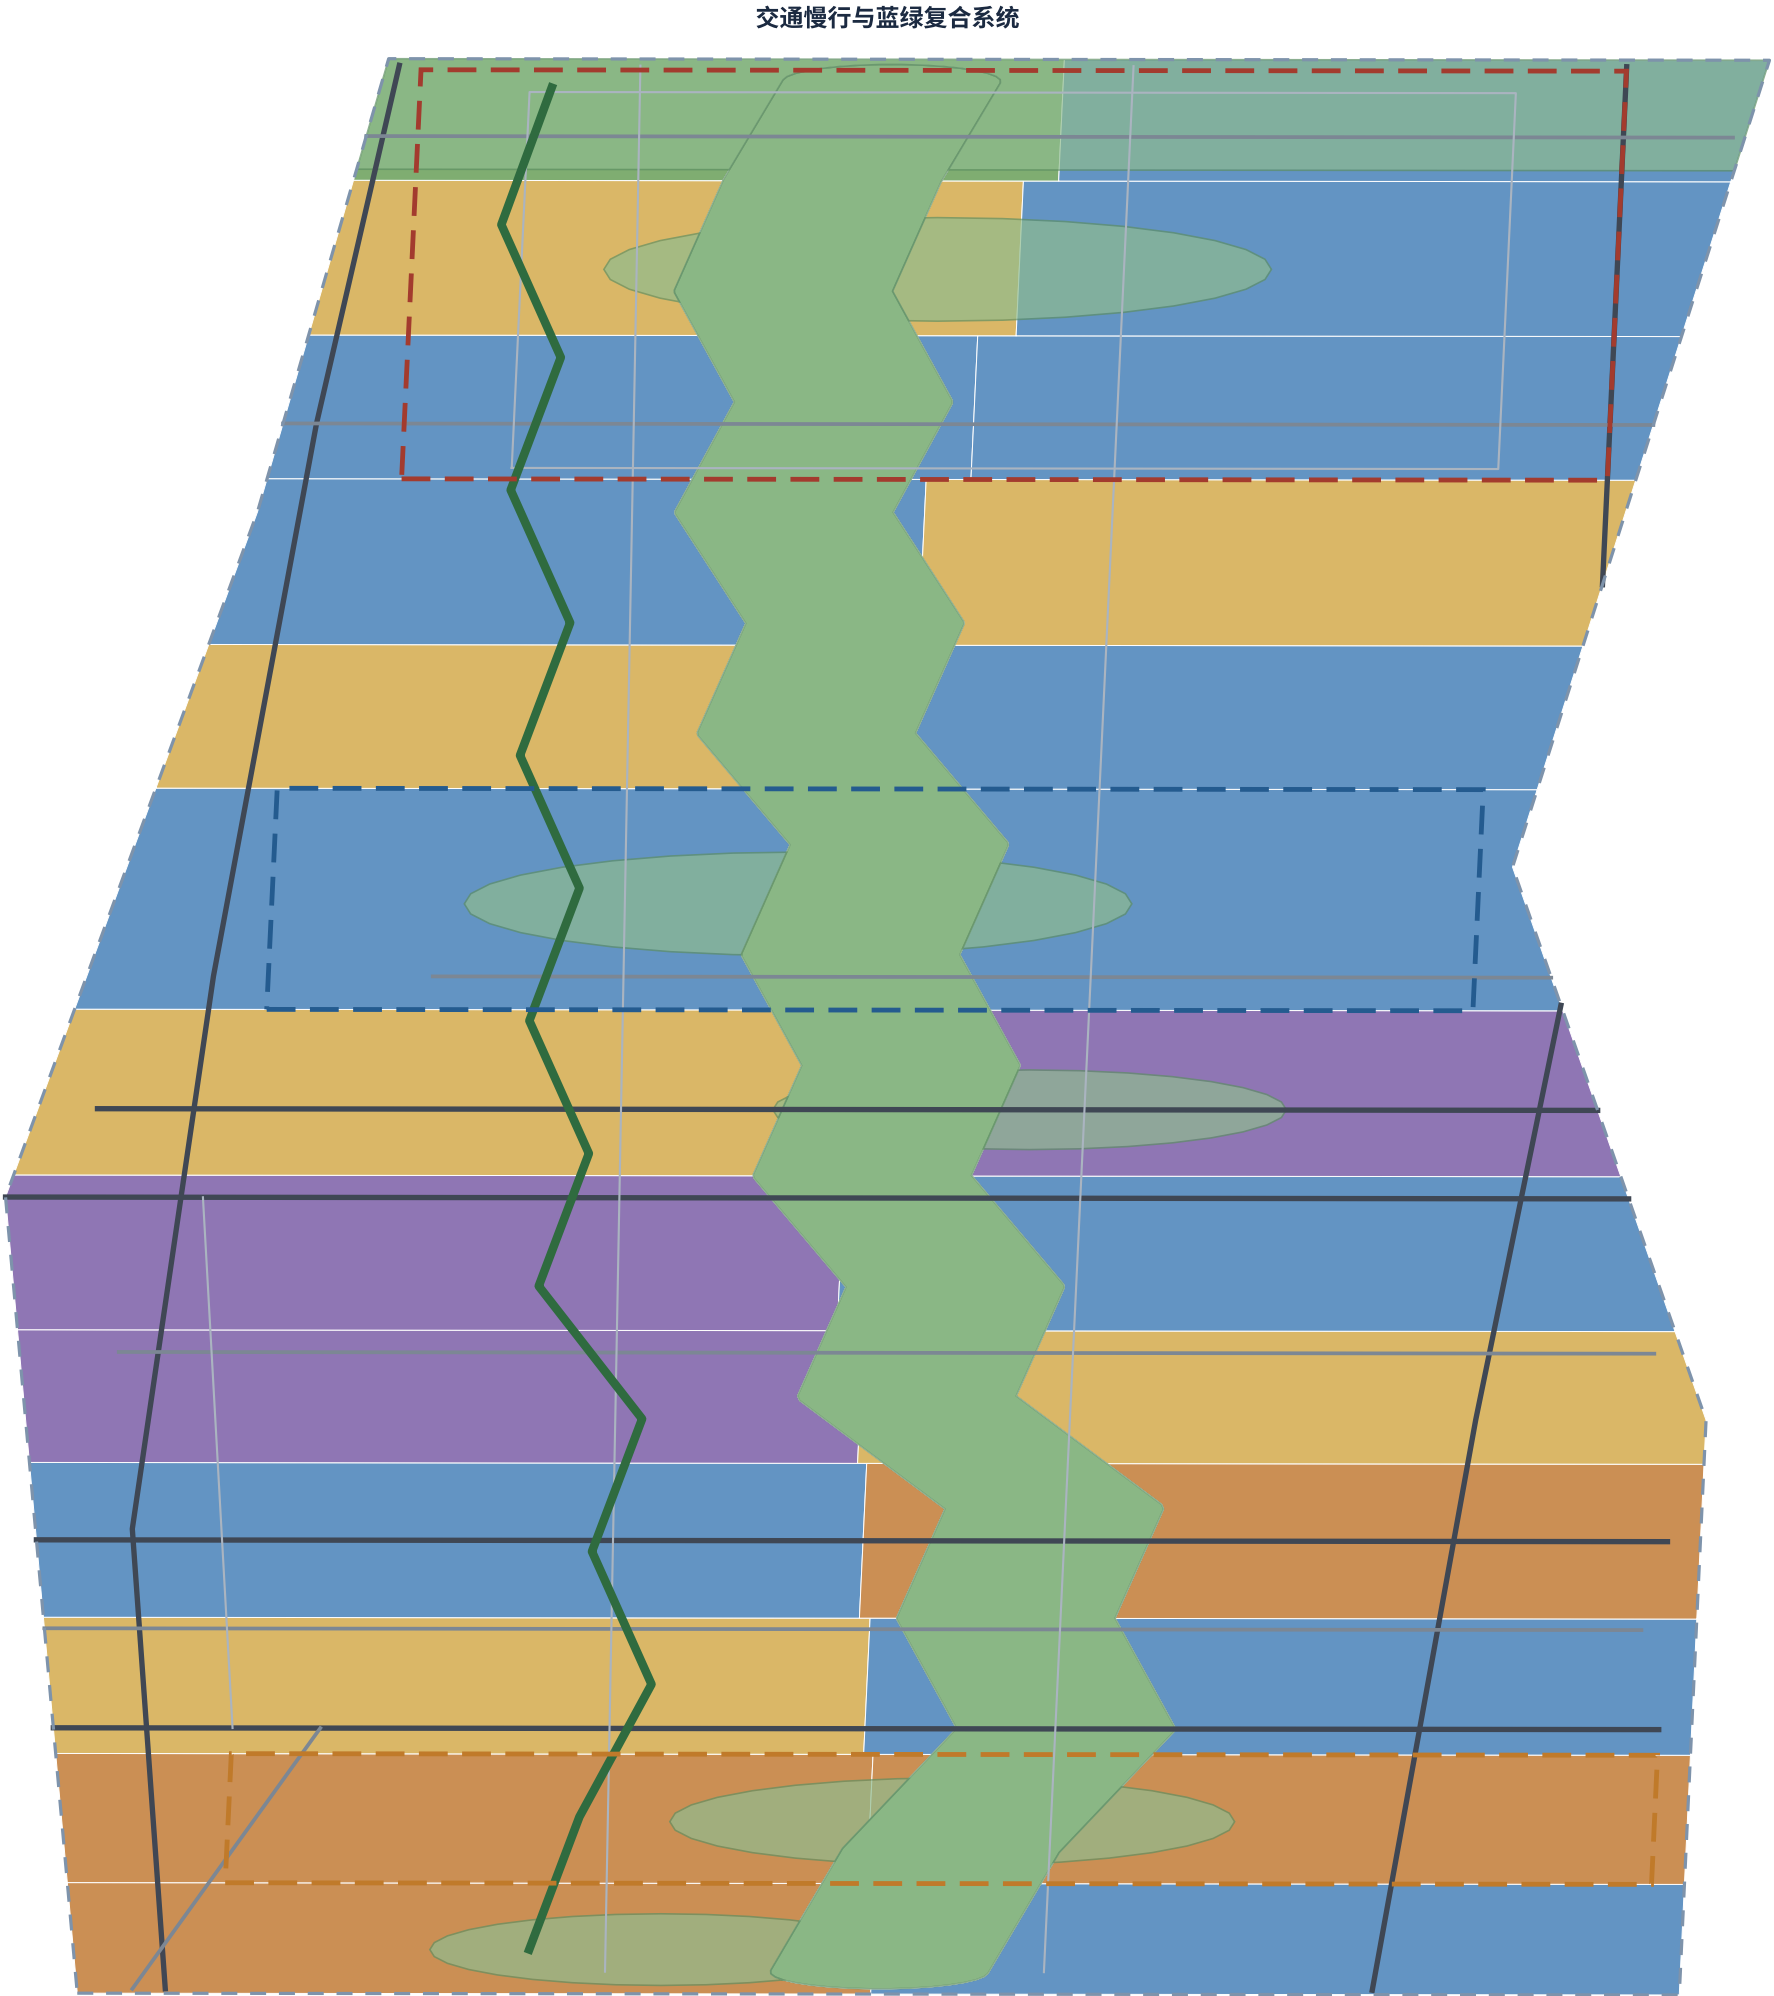

- 8项概念更新项目：零公里原点更新、大钟寺四象限缝合、知春路智会走廊、五道口折返广场、原点社区开源街、众智园测试场与发布广场、清河蓝绿界面、绿脊慢行贯通。
- 分期：近期试点2026-2028（约300万m²）→ 中期2028-2032（约526万m²）→ 远期2032-2035+（约315万m²）。
- 年度活动：开源季（春）• ZHI全球创新峰会（夏）• 场景开放日（秋）• 贡献者年度奖（冬）；公里标贡献制运营开发者社区。
- 所有项目、政策与活动均为概念建议，不构成已确定政府安排。

分期：南段近期/中段中期/北段远期

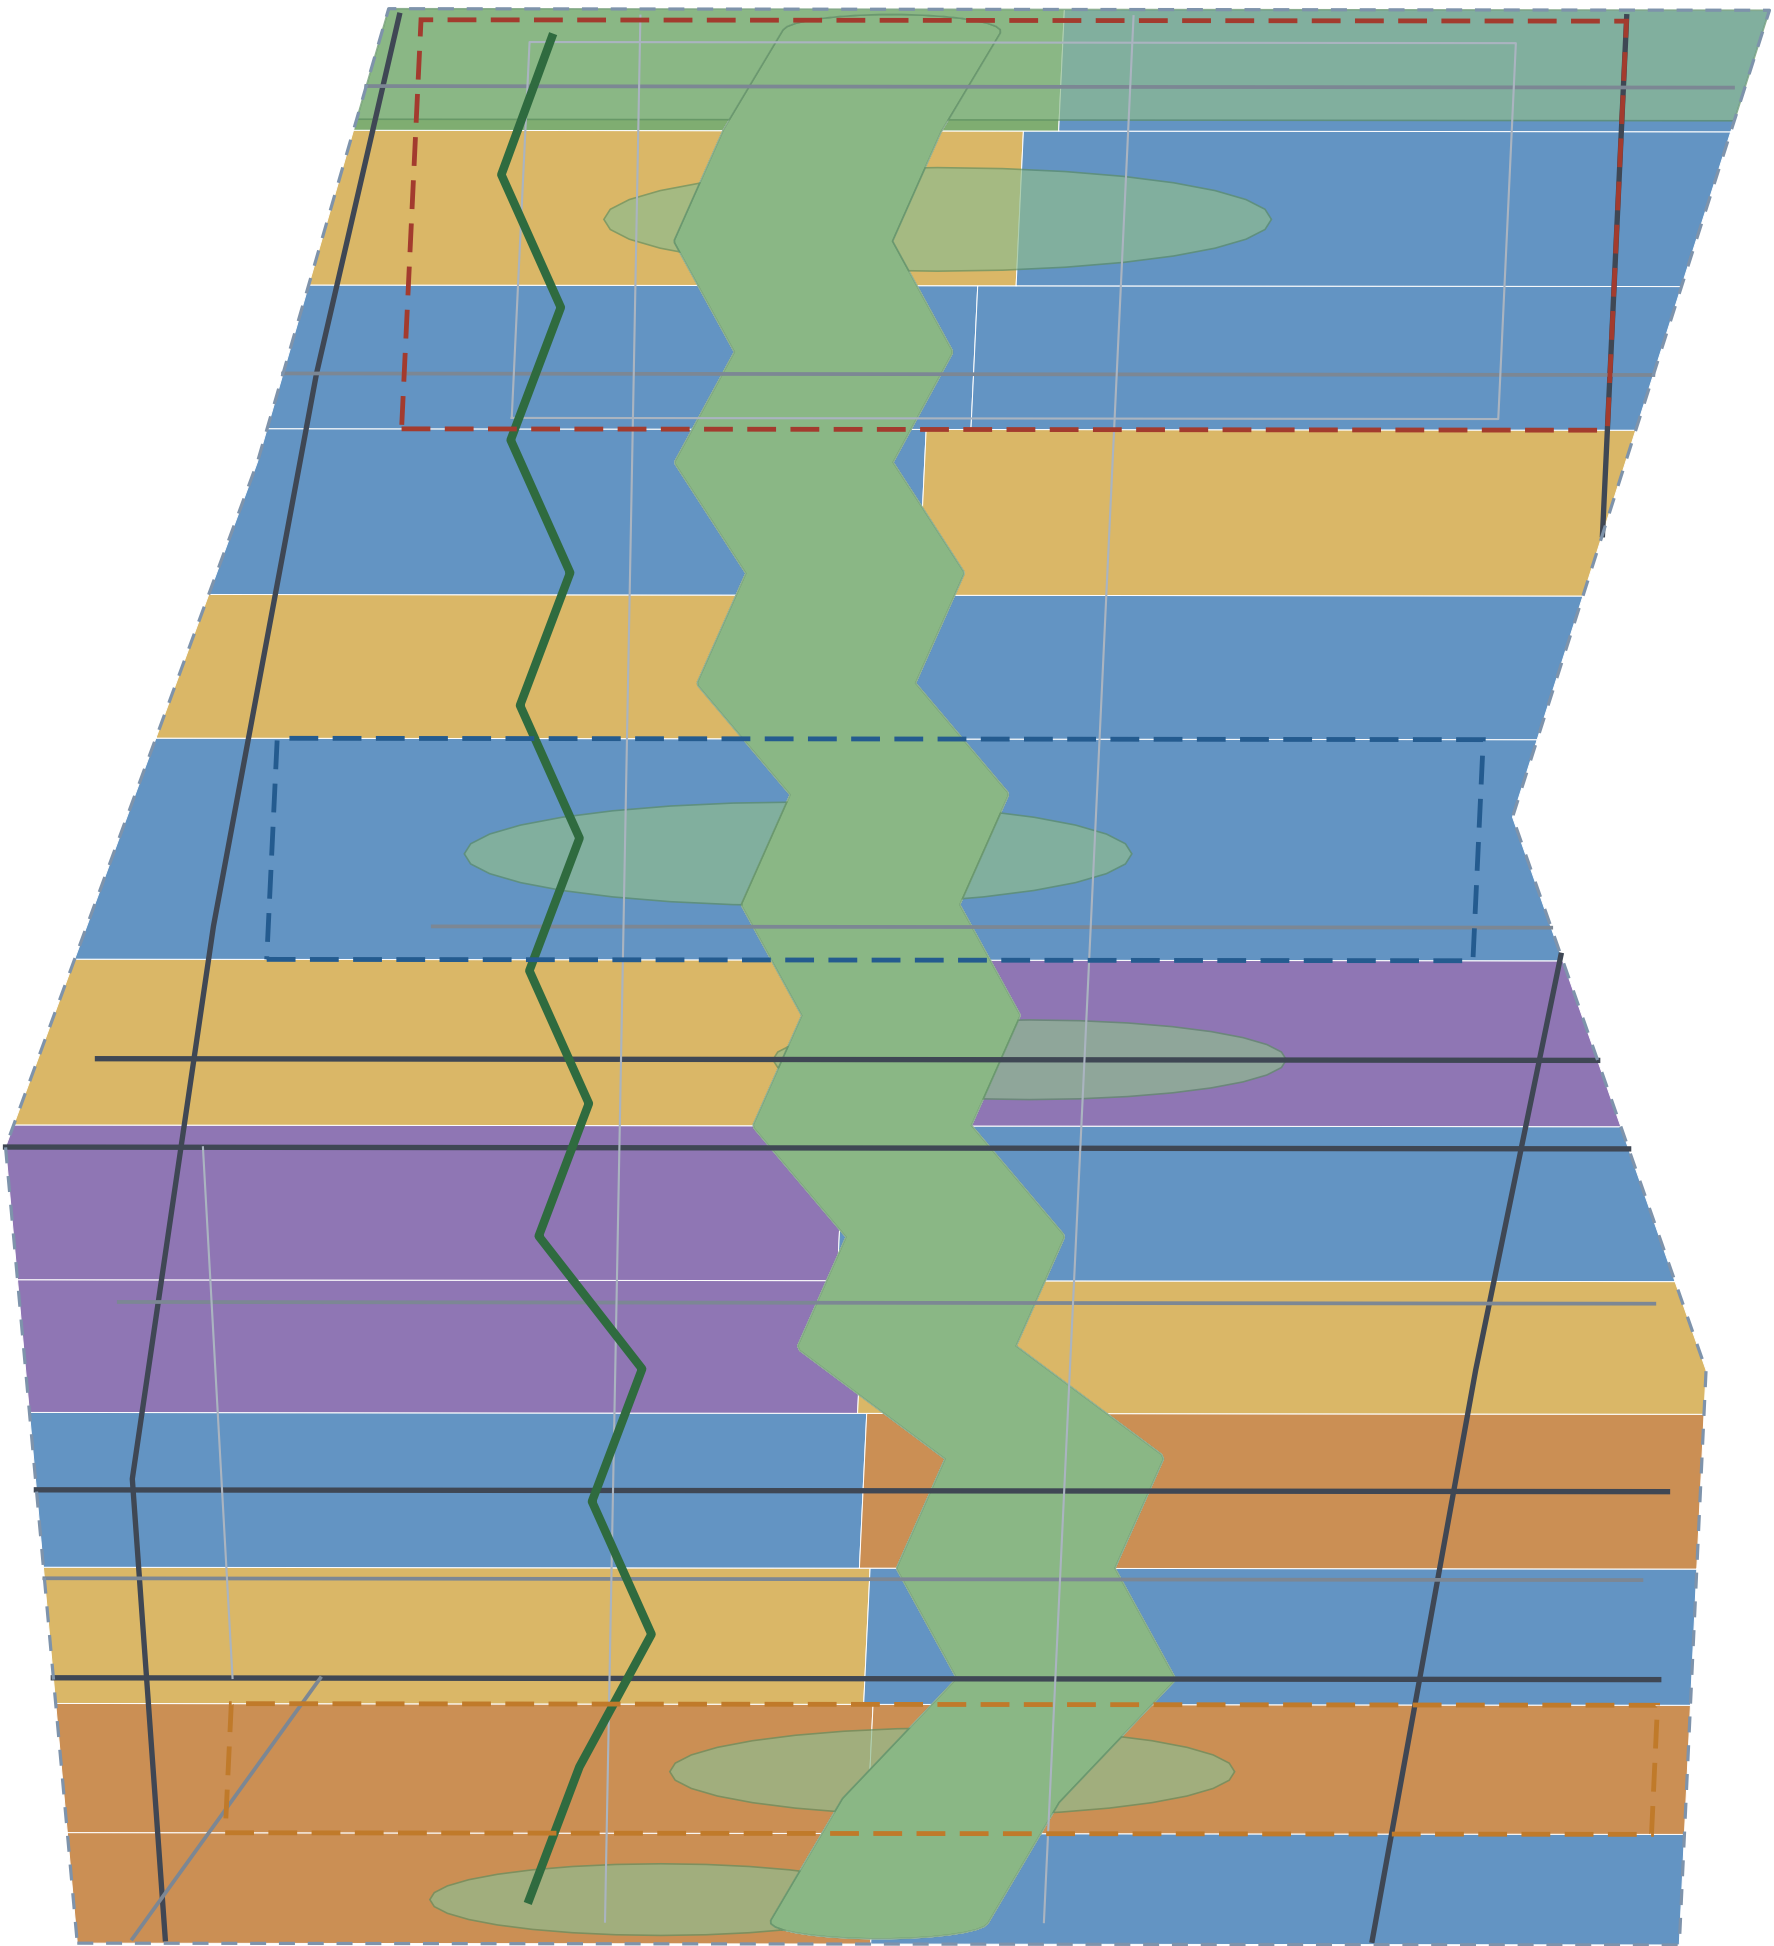

- 复算指标 (EPSG:4548)：总体设计范围11.41 km²、绿地约265万m² (23.2%)、公共空间约21.7万m² (1.9%)、建筑基底约84.8万m²、绿脊9.37 km、道路中心线56.0 km。
- 待补指标 (无官方控规条件)：容积率、建筑高度、建筑密度、退线——统一记为待正式数据补齐。
- 合规覆盖：公告1.3/1.4/1.5共18项任务 + agent.1-agent.6六项任务，全部在compliance_matrix.json逐条挂接章节、图层、指标、图纸与HTML。
- 专业标准：公告、任务书、城市设计管理办法、控规办法、用地分类指南（必答）均已响应；自检四门（确定性/空间/视觉/专业证据）PASS。

