

相护京张 MEND Corridor：照护与修复的百年京张AI创新带城市设计

评审 30 秒摘要板：概念 · 结构 · 指标 · v0.4 机制 | 30-second summary board


一句话概念：沿京张绿脊建一条照护步道与一组照护驿站，四条缝合廊道把被速度撕开的城市重新缝起来——AI 的价值不是更快，而是照护。

相护京张 MEND CORRIDOR · 总体概念

总览：一脊 · 三核 · 两翼 · 四缝合

三层范围传导关系 + 总体空间结构 | 照护与修复主题的百年京张 AI 创新带


总体空间结构（竖向为南北向，北↑）

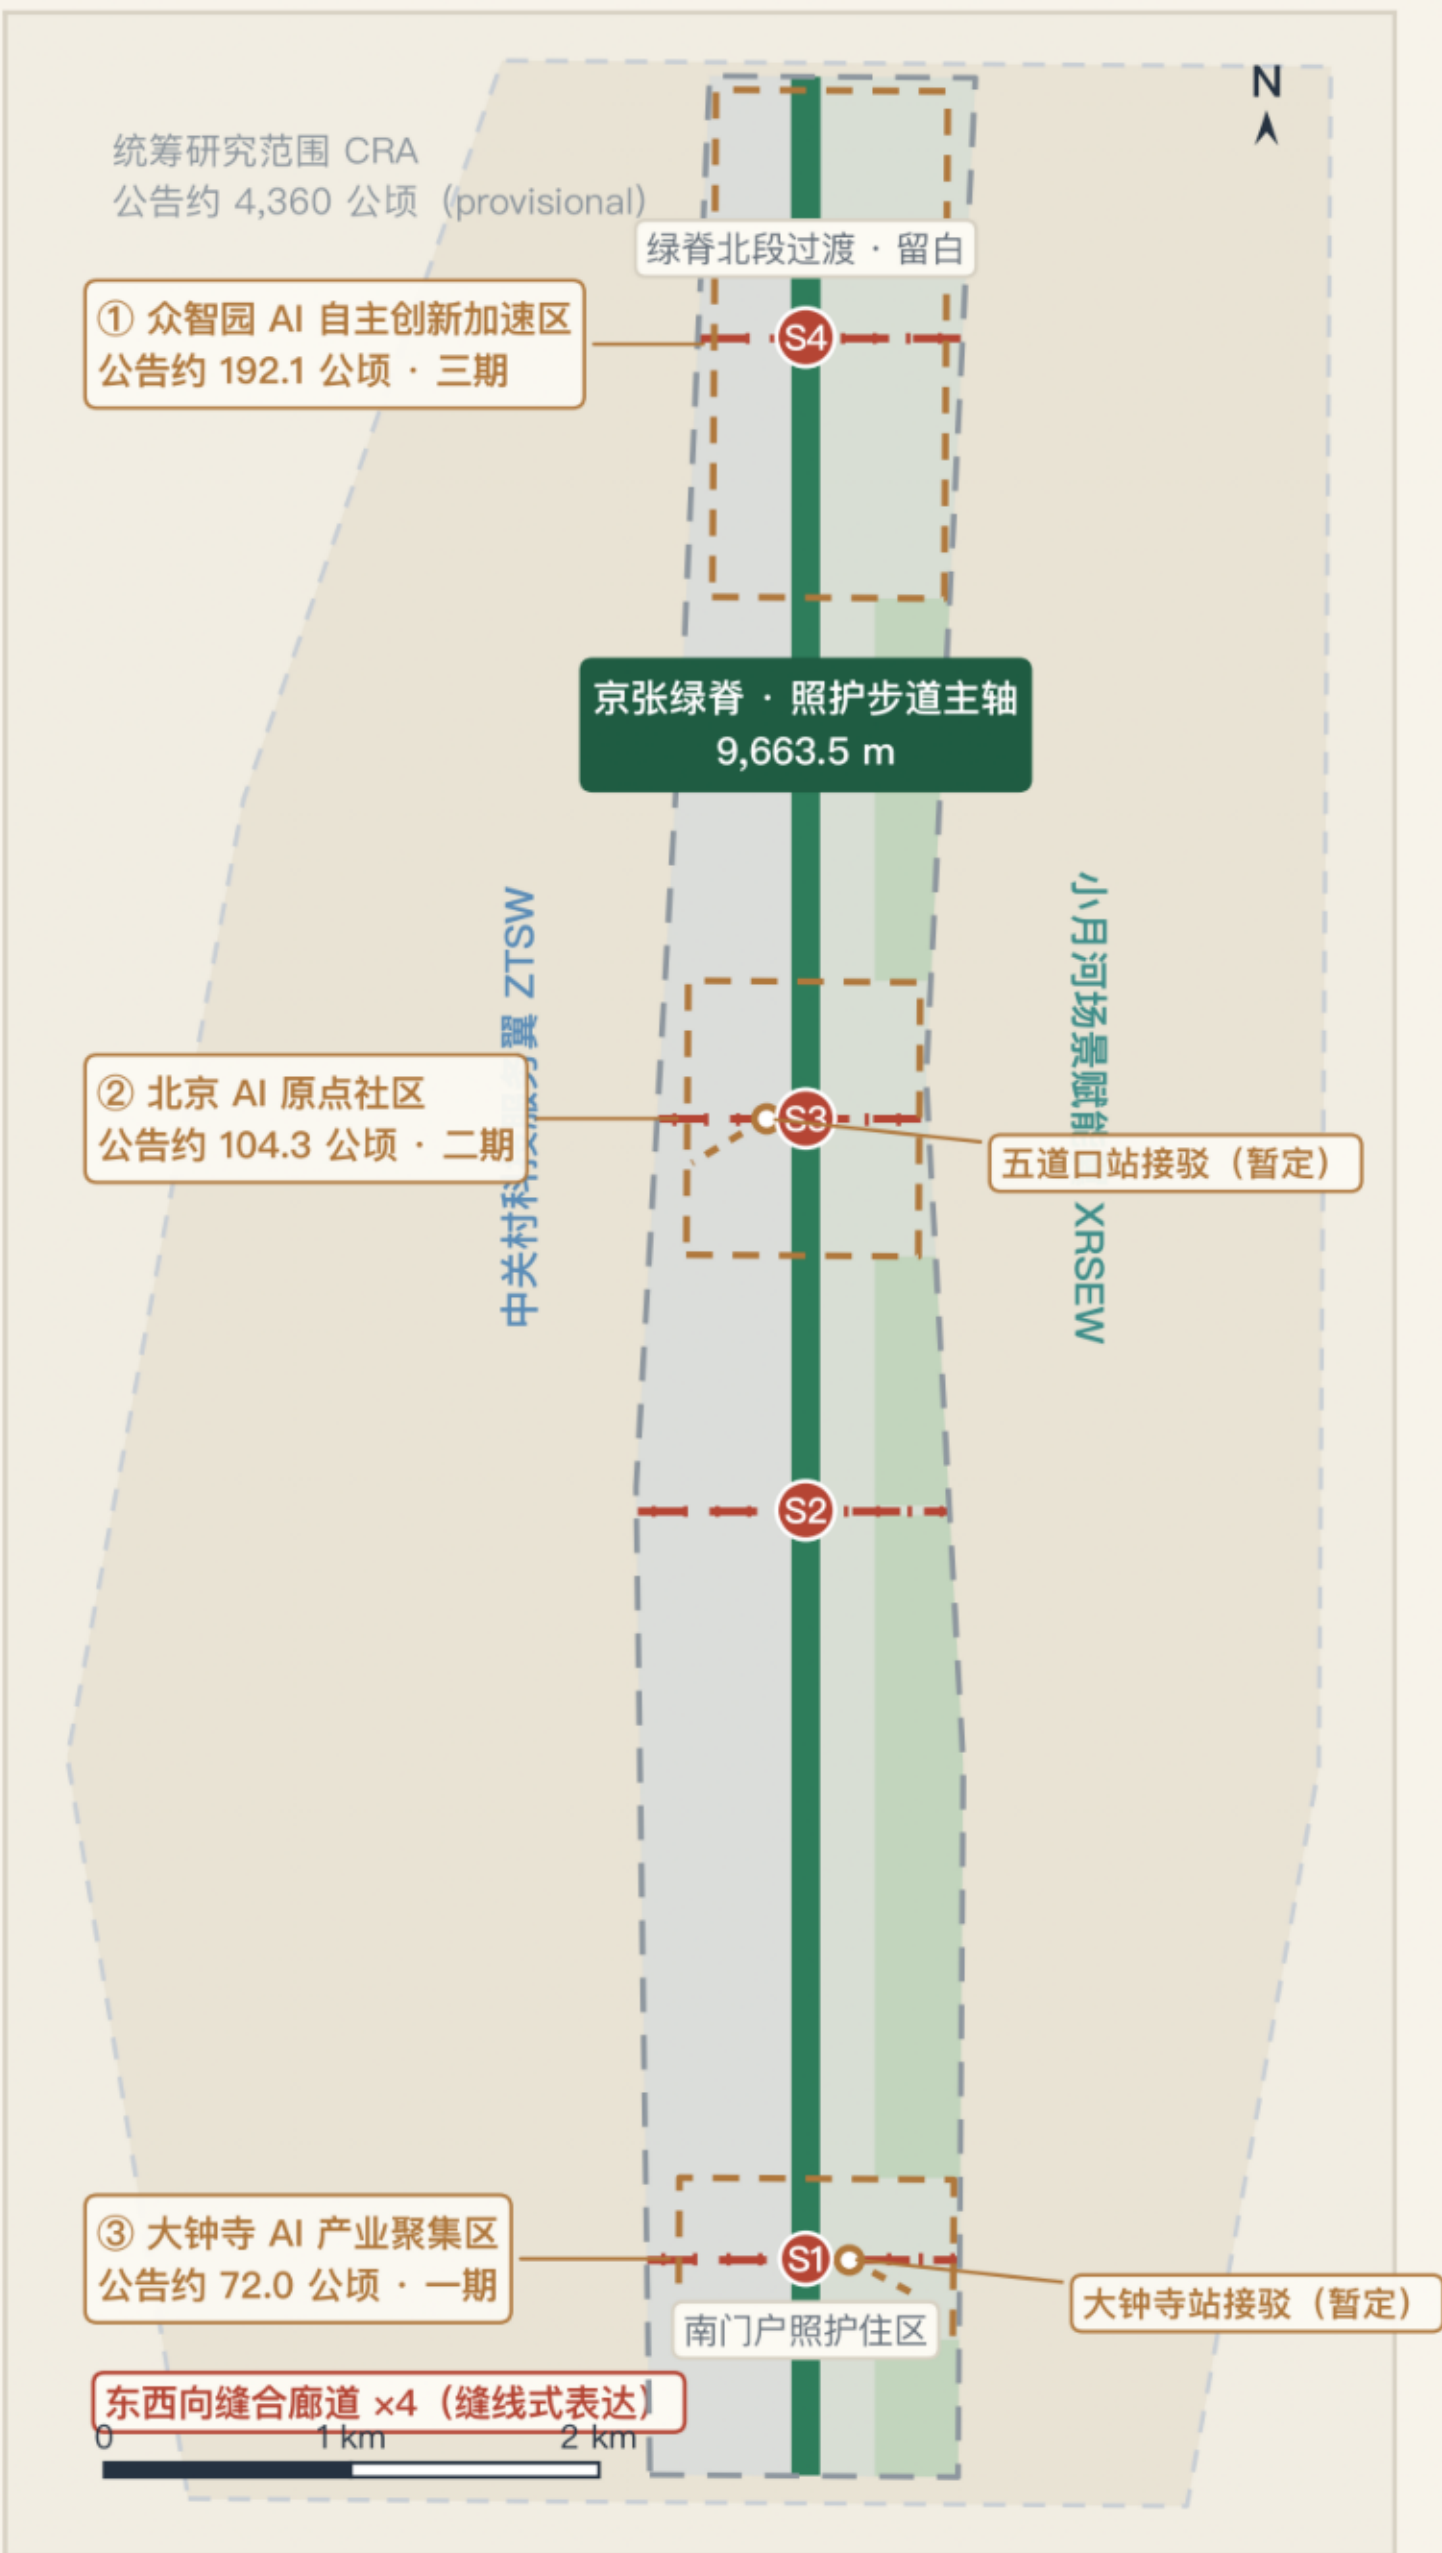

三层范围传导（示意，不按比例）



一脊三核两翼四缝合 · 结构逻辑图（示意，竖向=南北，不按比例）

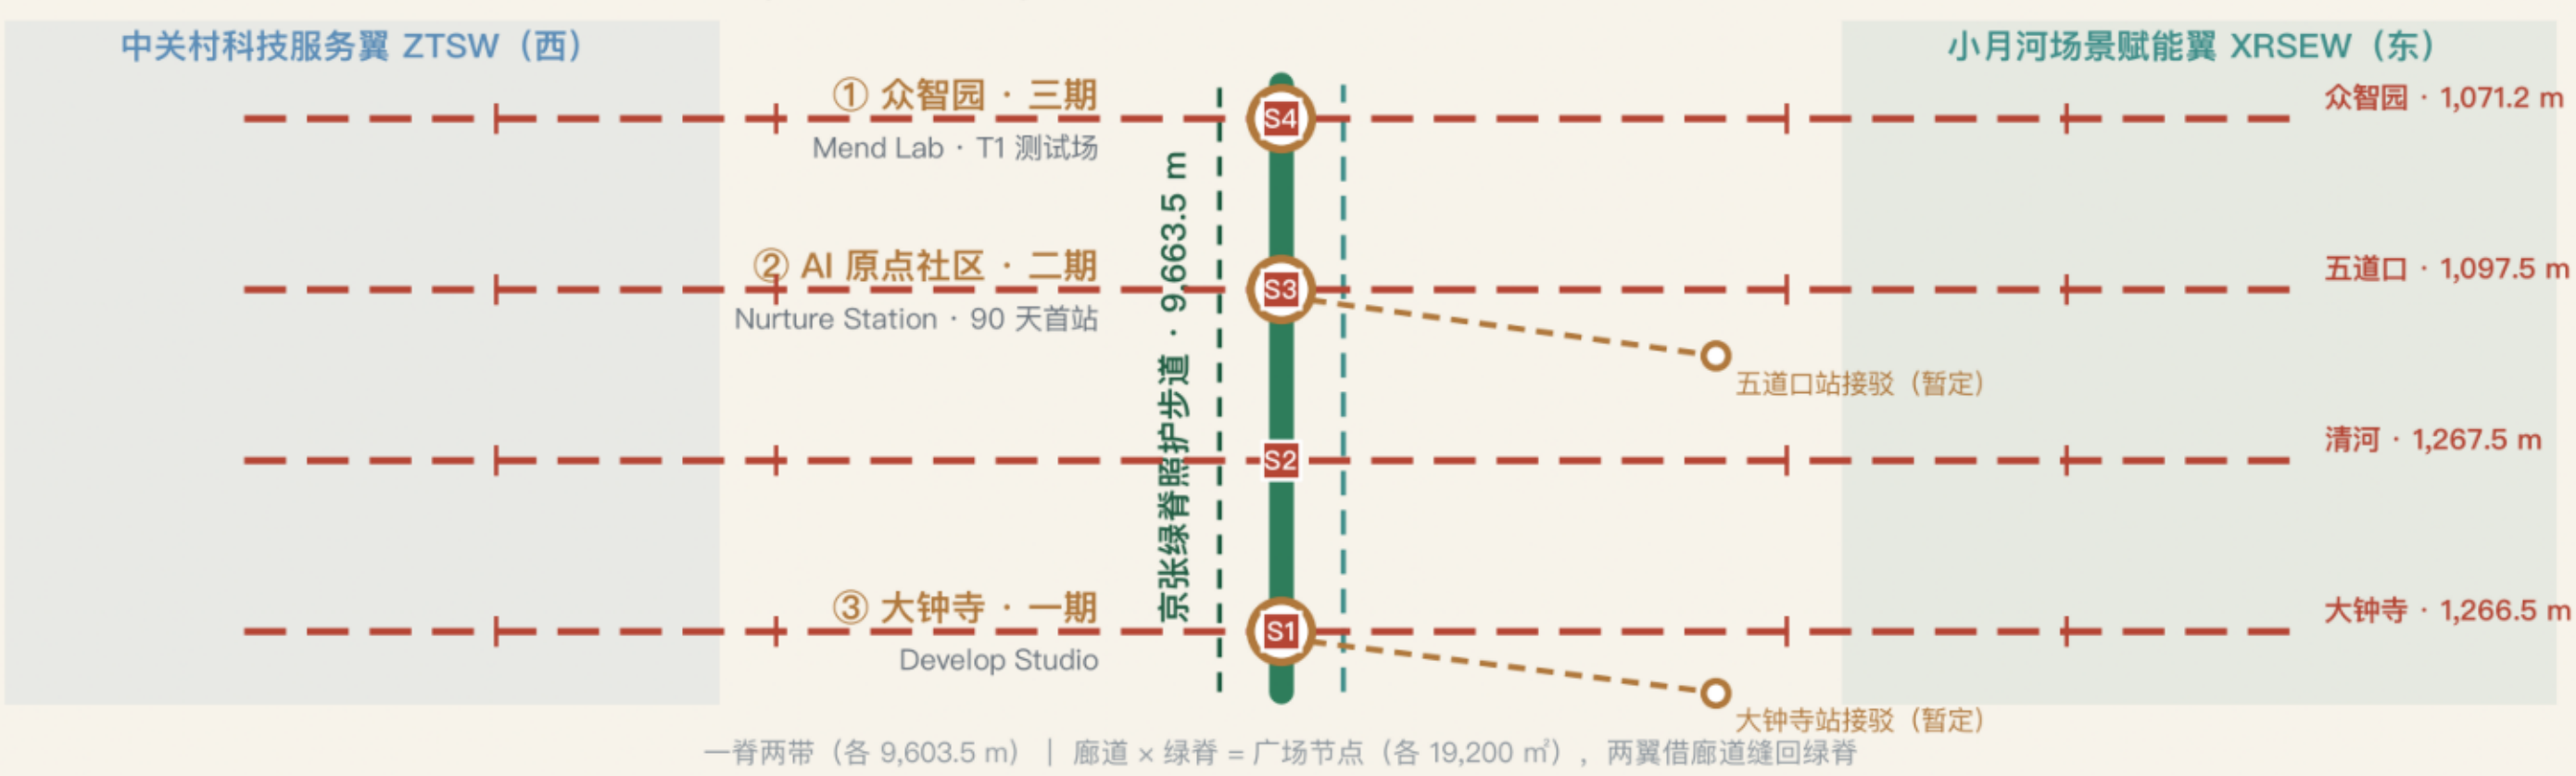

一脊

京张绿脊照护步道主轴

9,663.5 m

120 m 宽遗址绿脊纵贯南北，串联三核四节点

两翼

中关村科技服务翼 | 小月河场景赋能翼

2 协同翼

西翼科研服务支撑，东翼以小月河蓝绿基底承载 AI+ 场景

三核

众智园 · AI 原点社区 · 大钟寺

3 重点区

北-中-南梯度布局，对应三期→一期实施序列

四缝合

东西向缝合廊道 x4

4 条 · 合计 4,702.7 m

修复铁路割裂 · 大钟寺 / 五道口 / 清河 / 众智园，廊道与绿脊交叉处设 4 处广场节点

来源：submissions/yadnuses/jingzhang-mend/geometry/\*.geojson 与 metrics.json (EPSG:4548 复算) | 相护京张 MEND Corridor · 百年京张 AI 创新带城市设计开源征集  
边界说明：总体设计范围与重点区边界为维护者 provisional 临时边界 (official\_boundary=false)，仅供生成、展示与临时复算，非官方红线；正式数据发布后须重算全部图层与指标。

总体设计范围面积

11,412,825.386 m<sup>2</sup>

site\_area\_sqm · provisional 复算

绿地率

0.252649

green\_ratio · 2,883,442.715 m<sup>2</sup>

公共空间率

0.259379

public\_space\_ratio · 2,960,242.715 m<sup>2</sup>

照护契约卡

12 张 × 9 列

键停止/恢复证据/AI-OFF 全登记

首个 90 天合同

三道评估门

第 90 天强制续接/整改/撤场

风险活索引

R-01..R-12

契约卡/项目表/评估门全图索引

PROVISIONAL BOUNDARY · 临时边界声明

provisional 声明：全部面积、比例与范围为维护者 provisional 临时边界下的方案复算值 (official\_boundary=false)，仅供 intake 展示、讨论与返修，非官方红线，不作审批与正式评分依据；正式边界发布后须整体重算。组织方数据缺口不阻断内容评分。

Mend 修复

缝合空间裂痕

从铁路割裂城：绿脊+四廊道

Empower 赋能

缝合社会裂痕

中关村科技服务翼输出 IP 与资本

Nurture 照护

缝合数字裂痕

原点社区照护驿站网络

Develop 发展

照护科技成产业

大钟寺智能原生消费与内容业态



用地与城市更新 · Land Use and Urban Renewal

11 类用地由统一网格切割生成，总面积与总体范围边界差为 0；更新框架：保留织补为主、廊道缝合优先、留白预留弹性。

相护京张 MEND CORRIDOR · 用地结构

用地布局：11 类用地的照护–修复配比


绿地与开敞空间合计 25.94%（含广场） | 用地单元共享边界切割：两两重叠 0 m² | EPSG:4548 复算

概念方案 · 边界为 PROVISIONAL 临时边界

用地分区图（设计建议，非控规）



用地占比 100% 堆叠条（从左到右按面积降序）

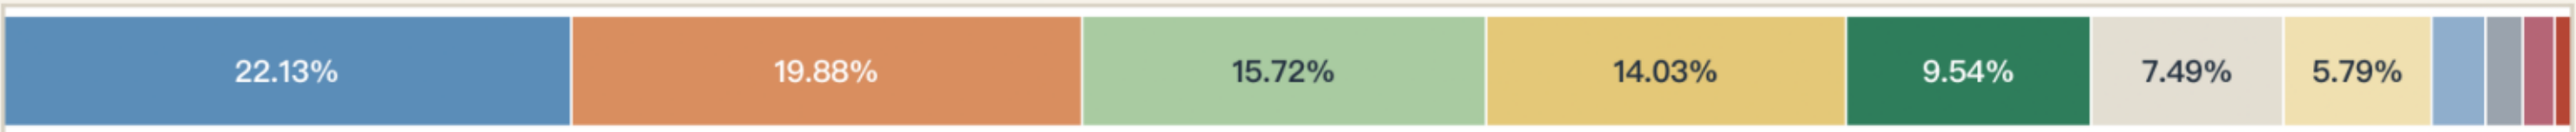

| 代码   | 用地类型       | 面积 (m²)      | 占比      | 设计意图           |
|------|------------|--------------|---------|----------------|
| 0802 | 科研用地       | 2,525,996.6  | 22.13%  | 众智园核 + 科技服务翼   |
| 05   | 商业服务业用地    | 2,269,228.0  | 19.88%  | 大钟寺核 · 服务翼内环   |
| 1402 | 防护绿地       | 1,794,307.8  | 15.72%  | 东翼小月河蓝绿缓冲      |
| 0701 | 城镇住宅用地     | 1,600,676.3  | 14.03%  | 南门户 + 原点社区照护住区 |
| 1401 | 公园绿地       | 1,089,134.9  | 9.54%   | 京张绿脊 · 照护步道主轴  |
| 16   | 留白用地       | 854,767.9    | 7.49%   | 北段过渡 + 东翼中段    |
| 0702 | 城镇社区服务设施用地 | 660,369.8    | 5.79%   | 原点/中段社区照护配套    |
| 0804 | 教育用地       | 236,984.0    | 2.08%   | 原点社区东侧（五道口）    |
| 1207 | 城镇村道路用地    | 168,908.0    | 1.48%   | 4 条东西缝合廊道      |
| 0803 | 文化用地       | 135,652.0    | 1.19%   | 大钟寺核东侧文化意象     |
| 1403 | 广场用地       | 76,800.0     | 0.67%   | 4 处廊道×绿脊广场节点   |
| 合计   |            | 11,412,825.4 | 100.00% |                |

与总体设计范围面积 11,412,825.386 m² 相差 0.0000 m²（共享边界切割，无重叠无空洞）

用地分类依据《国土空间调查、规划、用途管制用地用海分类指南》；本图为概念用地方案，不构成控规结论；重点区铜色虚线为 provisional 粗略范围。

来源：submissions/yadnuses/jingzhang-mend/geometry/\*.geojson 与 metrics.json（EPSG:4548 复算） | 相护京张 MEND Corridor · 百年京张 AI 创新带城市设计开源征集  
边界说明：总体设计范围与重点区边界为维护者 provisional 临时边界（official\_boundary=false），仅供生成、展示与临时复算，非官方红线；正式数据发布后须重算全部图层与指标。

绿地面积

2,883,442.715 m²

绿地率 0.252649

公共空间

2,960,242.715 m²

占比 0.259379

更新框架 · Renewal framework

城市更新总体框架：保留织补为主、廊道缝合优先、留白预留弹性。1401+1402 构成 2,883,442.715 m² 绿地基底；1207+1403 构成缝合系统；16 留白承载分期弹性。科研+商业约 42% 用地承载「1+X+1」产业体系。



交通、轨道、慢行与市政支撑 · Transport, Rail, Slow Mobility, Municipal

第一命题是「缝合」：4 条东西向缝合廊道修复铁路慢性割裂，慢行骨架为「一脊两带」。

相护京张 MEND CORRIDOR · 交通慢行 + 蓝绿网络

一条照护步道，四道城市缝线

慢行系统 WCN：绿脊主轴 + 双侧辅道 + 4 条缝合廊道 + 2 处轨道接驳（暂定） | 蓝绿空间 BGS 连续成网

概念方案 · 边界为 PROVISIONAL 临时边界

慢行 + 蓝绿网络（缝合廊道为缝线式表达）



图例 | 网络分级

- 京张绿脊照护步道主轴 · 9,663.5 m
- 西侧无障碍漫步道 · 9,603.5 m
- 东侧通勤自行车道 · 9,603.5 m
- 东西向缝合廊道 ×4 · 合计 4,702.7 m
- 轨道接驳通道 ×2（暂定）
- 翼内支路 ×2
- 公园绿地 1401（绿脊）
- 防护绿地 1402（东翼缓冲）
- 广场节点 S1—S4 · 各 19,200 m<sup>2</sup>
- 小月河（示意水系 · 低置信）
- 京张旧线（示意线位 · 低置信）
- 遗址廊道暂定保护控制范围（推定）

| 绿脊主轴                             | 缝合廊道 · 合计 4,702.7 m       | 轨道接驳 TSI          | 照护驿站广场                            |
|----------------------------------|---------------------------|-------------------|-----------------------------------|
| 9,663.5 m                        | 4 条                       | 2 处               | 4 × 19,200 m <sup>2</sup>         |
| heritage_spine_greenway_length_m | suture_corridor_count = 4 | 大钟寺站 / 五道口站（暂定接驳） | 1403 · 合计 76,800.0 m <sup>2</sup> |

蓝绿指标 | 与 metrics.json 逐字一致

|                      |                               |        |                    |
|----------------------|-------------------------------|--------|--------------------|
| 绿地（1401+1402）        | 2,883,442.715 m <sup>2</sup>  | 25.26% | green_ratio        |
| 公共空间（1401+1402+1403） | 2,960,242.715 m <sup>2</sup>  | 25.94% | public_space_ratio |
| 总体设计范围面积             | 11,412,825.386 m <sup>2</sup> | —      | site_area_sqm      |

蓝绿连续性：绿脊 120 m 宽主轴纵贯 9.66 km，4 条缝合廊道把东西两翼的绿地与住区缝回绿脊；小月河示意水系沿东界汇入住区公园。  
CONS-001/002/003 为 agent\_inferred 示意要素（confidence=low），非测绘成果，正式资料发布后替换。

来源：submissions/yachnuses/jingzhang-mend/geometry/\*.geojson 与 metrics.json（EPSG:4548 复算） | 相护京张 MEND Corridor · 百年京张 AI 创新带城市设计开源征集  
边界说明：总体设计范围与重点区边界为维护者 provisional 临时边界（official\_boundary=false），仅供生成、展示与临时复算，非官方红线；正式数据发布后须重算全部图层与指标。

缝合廊道

4 条东西向缝合廊道，每条约 40 米宽；与绿脊交叉处放大为 120×160 米广场节点（每处 19,200 m<sup>2</sup>）

慢行骨架「一脊两带」

绿脊绿道主轴复算 9,663.5 米；西侧步行带、东侧骑行带并行

轨道接驳（概念）

大钟寺站、五道口站方向两条暂定接驳线；站点一体化按五道口、清华东路西口组织

慢行断点


跨环路、跨铁路断点只提概念对策（上跨/平交口方向比选），不给工程线位（GAP-ROAD-001）

市政与新基建



## 京张活力带与蓝绿公共空间 · Jing-Zhang Vitality Belt and Blue-Green Public Space

以京张绿脊为骨架的蓝绿系统 + 3+1 朝圣地标 + 「修路→修车→修城→修身」文化叙事。

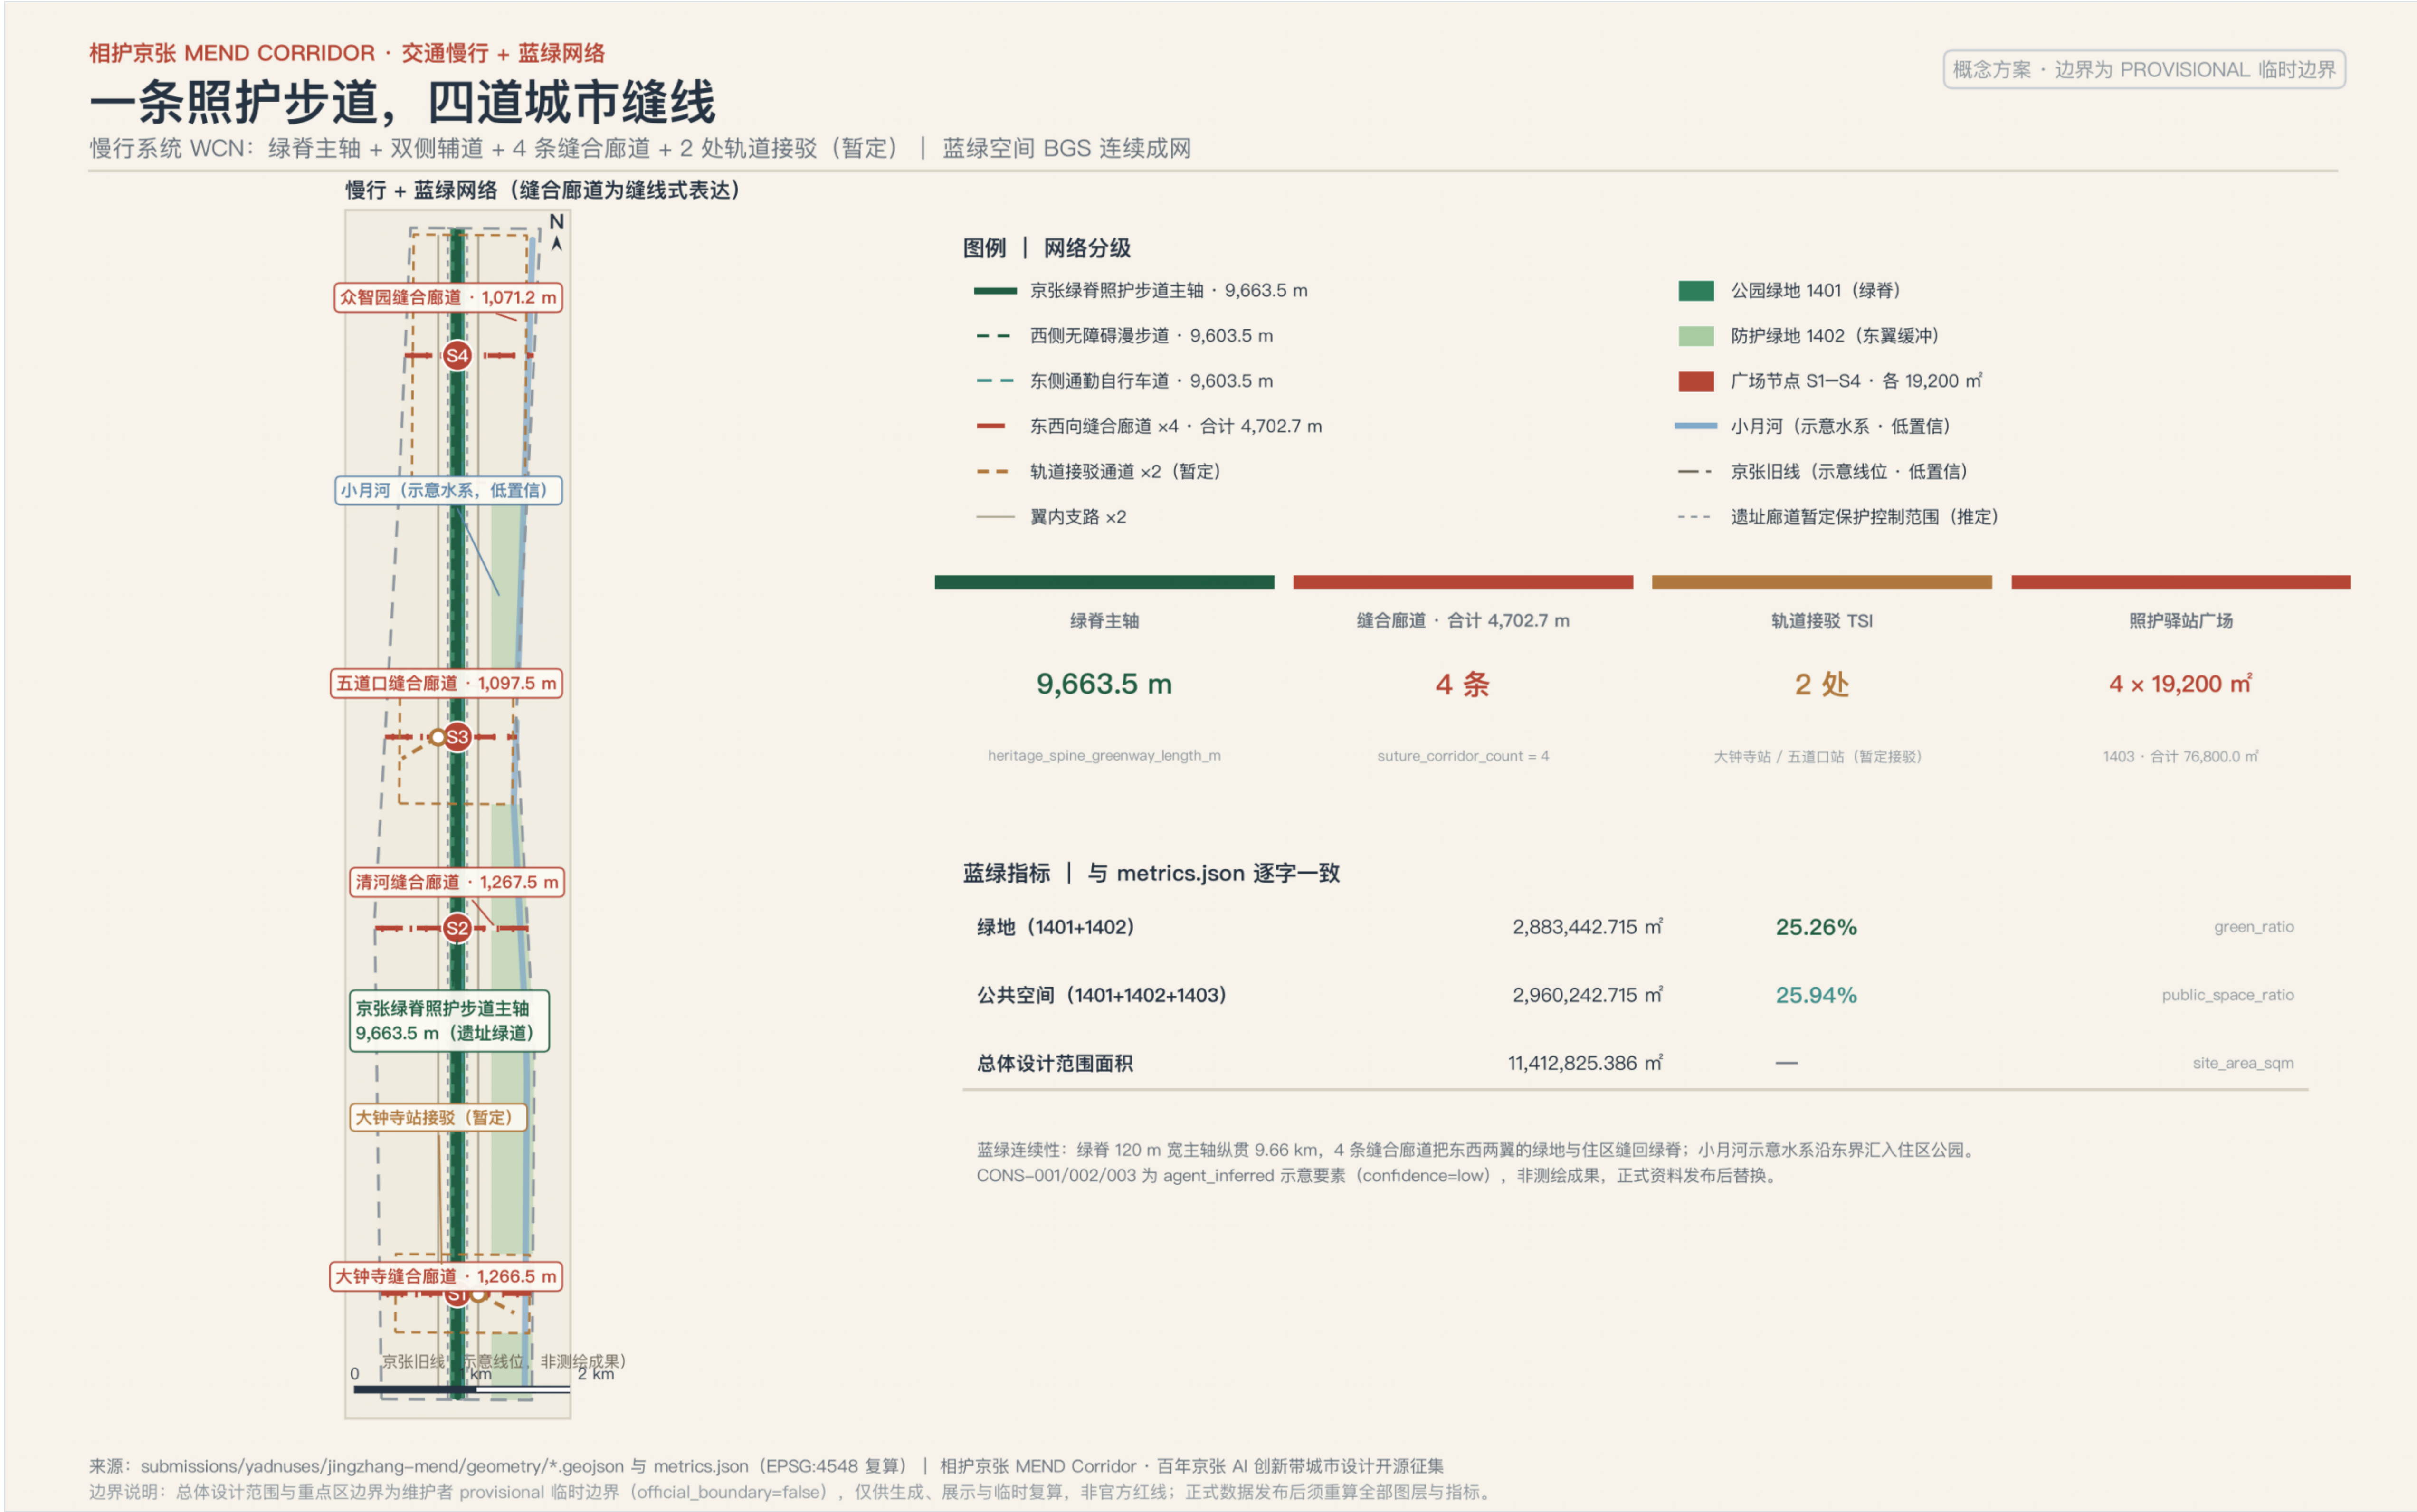

## 绿地面积

2,883,442.715 m<sup>2</sup>

绿地率 0.252649

## 公共空间

2,960,242.715 m<sup>2</sup>

占比 0.259379

## 绿脊主轴

120 米宽 × 9,663.5 米

公园绿地 1401

## 广场节点

4 处 × 19,200 m<sup>2</sup>

1403 广场用地

照护步道空间语言（概念标准，供专业团队深化）：连续遮荫、不大于 1:12 坡道方向、每 300—500 米一处带座椅与直饮水的休憩点。清河界面承载众智园低碳叙事；小月河为东翼蓝绿基底（示意水系，非测绘成果）。

## AI 朝圣地标（3+1，均为概念建议）

① 詹天佑自主营造纪念节点（道钉雕塑群 + 「人」字形铺地）② 照护者荣誉墙（护工/家属照护者/照护科技开发者并列上墙，每年增补）③ AI 原点开源贡献墙（可编程灯光展示真实贡献记录）④ 备选：大钟寺智能原生消费客厅。地标、导视与 Logo 共用「道钉+缝线」母题，全部须原创清权。



三处重点区域详细设计 · Detailed Design of the Three Key Areas

众智园（硬核）→ AI 原点社区（温度）→ 大钟寺（界面）；provisional 矩形边界下的方向性详细设计。

相护京张 MEND CORRIDOR · 重点区域

概念方案 · 边界为 PROVISIONAL 临时边界

三重点区详细设计导览：北-中-南 · 三核三策

每区：用地构成 + 缝合廊道 + 广场节点 + 照护场景 + v0.3 机制带 | 面积对公告偏差均在 ±0.5% 内 (provisional 原水平)

区位索引

1

2

3

2. AI 原点社区 | 公告 1,043,000 m<sup>2</sup> | 复算 1,043,236.9 m<sup>2</sup> | 偏差 +0.02%

3. 大钟寺 | 公告 720,000 m<sup>2</sup> | 复算 720,454.2 m<sup>2</sup> | 偏差 +0.06%

1. 众智园 | 公告 1,921,000 m<sup>2</sup> | 复算 1,929,201.9 m<sup>2</sup> | 偏差 +0.43%

3 大钟寺 AI 产业聚集区

一期 · 启动核

v0.3 机制

契约卡 12 (智能原生消费体验) 落此；站点四象限步行连通列为第一公共工程；

质心勘误后全部结论仅方向性 (R-01)

定位

文化门户+产业集聚：05 商业与 0803 文化用地承载大钟寺意象，南接南门户照护住区

抓手

大钟寺站轨道接驳通道 (暂定) 接入缝合廊道与 120×160 m 广场节点，商业-文化-居住混合激活

场景

照护场景：遗址步道南端门户、文化展廊与社区服务设施沿街布局

风险

风险：边界为 provisional 粗略范围；接驳通道线位暂定，须与轨道专业深化

2 北京 AI 原点社区

二期 · 中段缝合

v0.3 机制

照护契约主战场：首个 90 天合同 = Nurture Station

首站 + 绿脊样段，三道评估门、第 90 天强制去留 (R-11)；契约卡 01/02/06/11 落此

定位

居住保留与社区照护：0701/0702 为主体，0804 教育用地衔接五道口学院氛围

抓手

五道口站轨道接驳 (暂定) 加五道口缝合廊道与广场节点，绿脊照护步道示范段穿区而过

场景

照护场景：无障碍漫步道与社区服务设施按 5 分钟生活圈逻辑布局 (概念)

风险

风险：不作设施容量承诺；保留与留白比例待专业团队深化

1 众智园 AI 自主创新加速区

三期 · 北段留白

v0.3 机制

Mend Lab 承载 T1 康复机器人实测路线 (测试区备案+保险，R-10)；「研发-中试班车」写入区域交换接口表

定位

全栈自主创新加速核：0802 科研用地为主体，05 商业服务配套

抓手

清河与众智园双缝合廊道、双广场节点，北接绿脊过渡留白 (16) 预留生长弹性

场景

照护场景：科研社区的绿色通勤与午间修复花园 (概念)

风险

风险：北段留白不作用途承诺；科研规模指标待控规条件

来源：submissions/yadnuses/jingzhang-mend/geometry/\*.geojson 与 metrics.json (EPSG:4548 复算) | 相护京张 MEND Corridor · 百年京张 AI 创新带城市设计开源征集 | 图例：色块=用地分类 (同用地结构图) | 深色=建筑基底示意 | 红缝线=缝合廊道 | 铜虚线=轨道接驳 (暂定)

边界说明：总体设计范围与重点区边界为维护者 provisional 临时边界 (official\_boundary=false)，仅供生成、展示与临时复算，非官方红线；正式数据发布后须重置全部图层与指标。

| 重点区                                 | 定位与空间动作                                                                                        | 第一空间动作    | 主场景           | 实施风险                      |
|-------------------------------------|------------------------------------------------------------------------------------------------|-----------|---------------|---------------------------|
| 众智园 AI 自主创新加速区<br>Mend Lab 修复实验室    | 花园型全栈自主创新街区：0802 科研用地为主体，沿清河界面组织低碳创新文住廊：模型测试、标准制定、安全治理展示。公告约 1,921,000 m <sup>2</sup> (+0.43%) | 清河界面低碳创新廊 | 自主模型测试、标准治理展示 | 五环对外交通条件待核                |
| 北京 AI 原点社区<br>Nurture Station 照护驿站  | 近校型照护主战场：高校原始创新孵化转化 + 最好沿街界面留给照护：0702 照护驿站网络：陪诊、托管、数字扫盲。公告约 1,043,000 m <sup>2</sup> (+0.02%)  | 照护驿站网络嵌入  | 陪诊、托管、数字扫盲    | 校区边界与权属待核                 |
| 大钟寺 AI 产业聚集区<br>Develop Studio 发展工坊 | 城市型智能原生消费街区：智能体/智能终端/内容消费业态群；站点四象限步行连通为第一公共工程。公告约 720,000 m <sup>2</sup> (+0.06%)              | 站点四象限步行连通 | 智能终端与内容消费     | 质心偏差 (Issue #1029)，仅方向性表达 |

勘误声明 / Erratum：勘误声明：Issue #1029 确认 PROV-KEY-003 质心偏离约 2.26 公里，故大钟寺片区全部空间结论仅为方向性表达，正式边界发布前不作任何地块级承诺。

概念建议 (Conceptual Recommendation)：全部面积/比例/范围为临时边界下方方案复算值，非官方红线；正式边界发布后整体重置。

Jingzhang MEND Corridor · 相护京张



AI 场景与实施运营 · AI Scenarios and Implementation Operations

12 张场景卡（3 张产业测试验证 T1–T3）+ 7 类用户画像；场景—空间—运营映射与长期运营机制。

01 AI 陪诊与挂号助手

测试验证 T2

转介号源与限诊市面查；医疗建议一律人工复核

02 认知症防走失守护圈

服务

家属授权电子围栏；社区专员人工确认

03 无障碍慢行导航

测试验证 T3

路况众包+低侵入传感；标注「非审定交通方案」

04 康复机器人社区实测

测试验证 T1

跟速实测；安全员全程陪同

05 社区助餐与低速配送

服务

人机进行微速与人工接管

06 儿童课后托管协同

服务

家长授权、社工复核

07 京张文化 AI 导览

体验

文史顾问复核；AI 内容明确标注

08 企业服务 Copilot

产业

不替代专业法律意见

09 公共安全与活动运营复核

治理

任何处置决定由人作出

10 社区共修工坊

运营

修家电/修鞋/修代码/技能匹配

11 数字扫盲陪伴课堂

服务

一对一慢教学；零数据采集

12 大钟寺智能原生消费体验

消费

明示 AI 生成内容

用户画像（7 类） · User personas

用户画像（7 类，照护弱勢群体优先）：儿童（安全通学径/不采集未成年人轨迹） · 老人（陪诊/健康信息不采集） · 残障人士（无障碍导航/匿名化路况） · 低数字素养居民（人工窗口/服务记录最小化） · 照护者（喘息服务/排班数据归机构） · 开源开发者（开源发布厅/活动数据仅聚合） · 初创团队（共享测试场/算力另授权）。

场景—空间—运营映射 · Mapping

场景—空间—运营映射：体验与治理场景落在 2,960,242.715 m<sup>2</sup> 公共空间基底；服务场景落在 0702 社区服务用地与驿站网络；测试验证场景（T1–T3）只在划定测试路线与时段内运行，建议与北京经开区场景开放机制互认。开放空间占比 0.259379、绿地占比 0.252649 是照护场景的物理容量上限。

年度活动与长期运营 (agent.6) · Annual program & operations

年度活动按 MEND 四动词：春季照护者大会（荣誉墙增补+照护科技展） · 夏季修复工作坊（社区共修日+高校联合设计周） · 秋季开发者开放日（贡献墙点亮+场景测试招募） · 冬季过冬压力测试周（暴雪极寒照护调度演练）。长期运营建议「绿脊之友」独立机制（参照高线公园经验）：场景开放审批、活动排期、数据治理年报、居民议事会。



指标复核与合规响应 · Metrics Verification and Compliance Response

12 项 known 指标可从 GeoJSON 复算；3 项控规类指标保持 unknown；合规覆盖公告 17 条 + agent 6 条。

| 指标                               | 数值       | 单位             | 公式与来源                                  | 置信度                  |
|----------------------------------|----------|----------------|----------------------------------------|----------------------|
| site_area_sqm                    | 总体设计范围面积 | 11,412,825.386 | polygon_area(site_boundary), EPSG:4548 | medium (provisional) |
| land_use_total_area_sqm          | 用地总面积    | 11,412,825.386 | sum(land_use_cells), 与边界面积差为 0         | medium               |
| green_space_area_sqm             | 绿地面积     | 2,883,442.715  | 1401+1402 并集面积                         | medium               |
| green_ratio                      | 绿地率      | 0.252649       | green_space_area_sqm / site_area_sqm   | medium               |
| public_space_area_sqm            | 公共空间面积   | 2,960,242.715  | 1401+1402+1403 并集面积                    | medium               |
| public_space_ratio               | 公共空间占比   | 0.259379       | public_space_area_sqm / site_area_sqm  | medium               |
| building_footprint_area_sqm      | 建筑基底面积   | 846,000.0      | 423 栋示意基底并集                            | medium (示意)          |
| design_site_coverage_ratio       | 方案基底覆盖率  | 0.074127       | 基底/总面积 (非控规建筑密度)                       | medium               |
| key_area_count                   | 重点区数量    | 3              | 重点区计数                                  | high                 |
| key_areas_total_area_sqm         | 重点区总面积   | 3,692,893.005  | 重点区面积和 (对公告 3,684,000 偏差 +0.24%)       | medium               |
| heritage_spine_greenway_length_m | 绿脊绿道长度   | 9,663.5        | 绿脊绿道中心线长度                              | medium               |
| suture_corridor_count            | 缝合廊道数量   | 4              | 缝合廊道计数                                 | medium               |

相护京张 MEND CORRIDOR · 指标证据

指标证据仪表盘：每一个数字都可回溯

全部数值源自 metrics.json | 面积在 EPSG:4548 复算 | unknown 指标不能成数字

绿地率

25.26%

2,883,442.715 m² 绿地  
green\_ratio = 0.252649

公共空间率

25.94%

2,960,242.715 m² 公共空间  
public\_space\_ratio = 0.259379

方案基底覆盖率

7.41%

846,000.0 m² 基底 · 非控规密度  
design\_site\_coverage\_ratio = 0.074127

绿脊绿道

9,663.5 m

100 m 宽绿脊绿道总长  
heritage\_spine\_greenway\_length\_m

缝合廊道

4 条

大特等/无进口/慢行/绿道  
suture\_corridor\_count = 4

重点区

3 处

合计 3,692,893.005 m²  
key\_area\_count = 3

可信数据源 v0.3

A1 用地等值线

A2 缝合廊道

A3 风险识别

A4 90 天可验收

证据链 | 复算关系 (formula → value)

重点区面积复核 | 对公告值偏差 (provisional 原水平)

待确认控规指标 | status = unknown (绝不编造)

自检状态 | self\_check\_submission.py

来源: submissions/yehuses/jingzhang-mend/geometry/\*-geojson 与 metrics.json (EPSG:4548 复算) | 相护京张 MEND Corridor · 数据流程 A1 数据等值线设计并源证据  
边界说明: 总体设计范围与重点区边界为相护窗 (provisional 临时边界, official\_boundary=false) 。仅供生成、展示与临时复算, 非官方红线。正式数据发布后证据重算全部范围与指标。

本图为展示用, 权威数据以 geometry/\*-geojson 与 metrics.json 为准。

UNKNOWN 指标 · 不给数值结论

unknown 指标 (公开场地包标记 missing, 不给数值结论) : floor\_area\_ratio 容积率 · building\_height\_control\_m 建筑高度控制 · building\_density\_control 建筑密度控制。正式控规条件补齐后整体重算。

合规矩阵摘要 · Compliance summary

合规覆盖: 公告 17 条必选任务 + agent 任务书 6 条任务 (合计 23 条) , 每条挂接章节、图层、指标、图纸、HTML 区块、来源、假设与自检项 (compliance\_matrix.json) 。标准响应 9 条 (1 条 data\_gap) ; 设计深度 15 个核心项全部 complete (design\_depth\_matrix.json) 。

数据缺口 (8 项) · Missing-data checklist

- GAP-BOUNDARY-001/002 三层范围 official polygon 缺失
- GAP-CONTROL-001 控规条件缺失 (容积率/高度/密度保持 unknown)
- GAP-ROAD-001 道路红线与断面缺失 (断面仅概念组织)
- GAP-PARCEL-001 宗地权属缺失 (折改留只绘方法不给结论)