


AI 给城市带来两件很物理的事：它发热，它要近。本方案把这两件事变成空间制度——余热必须还给公共空间，算力必须下沉到街道，而停止它的开关必须留在人手里。

图1 总体空间结构：京张暖线

一条主脊 · 13座给算站 · 13处东西缝合口 · 三区两翼

SITE OVERVIEW

概念方案 · 非法定规划 · 临时边界
zxw1992 / jingzhang-warm-line

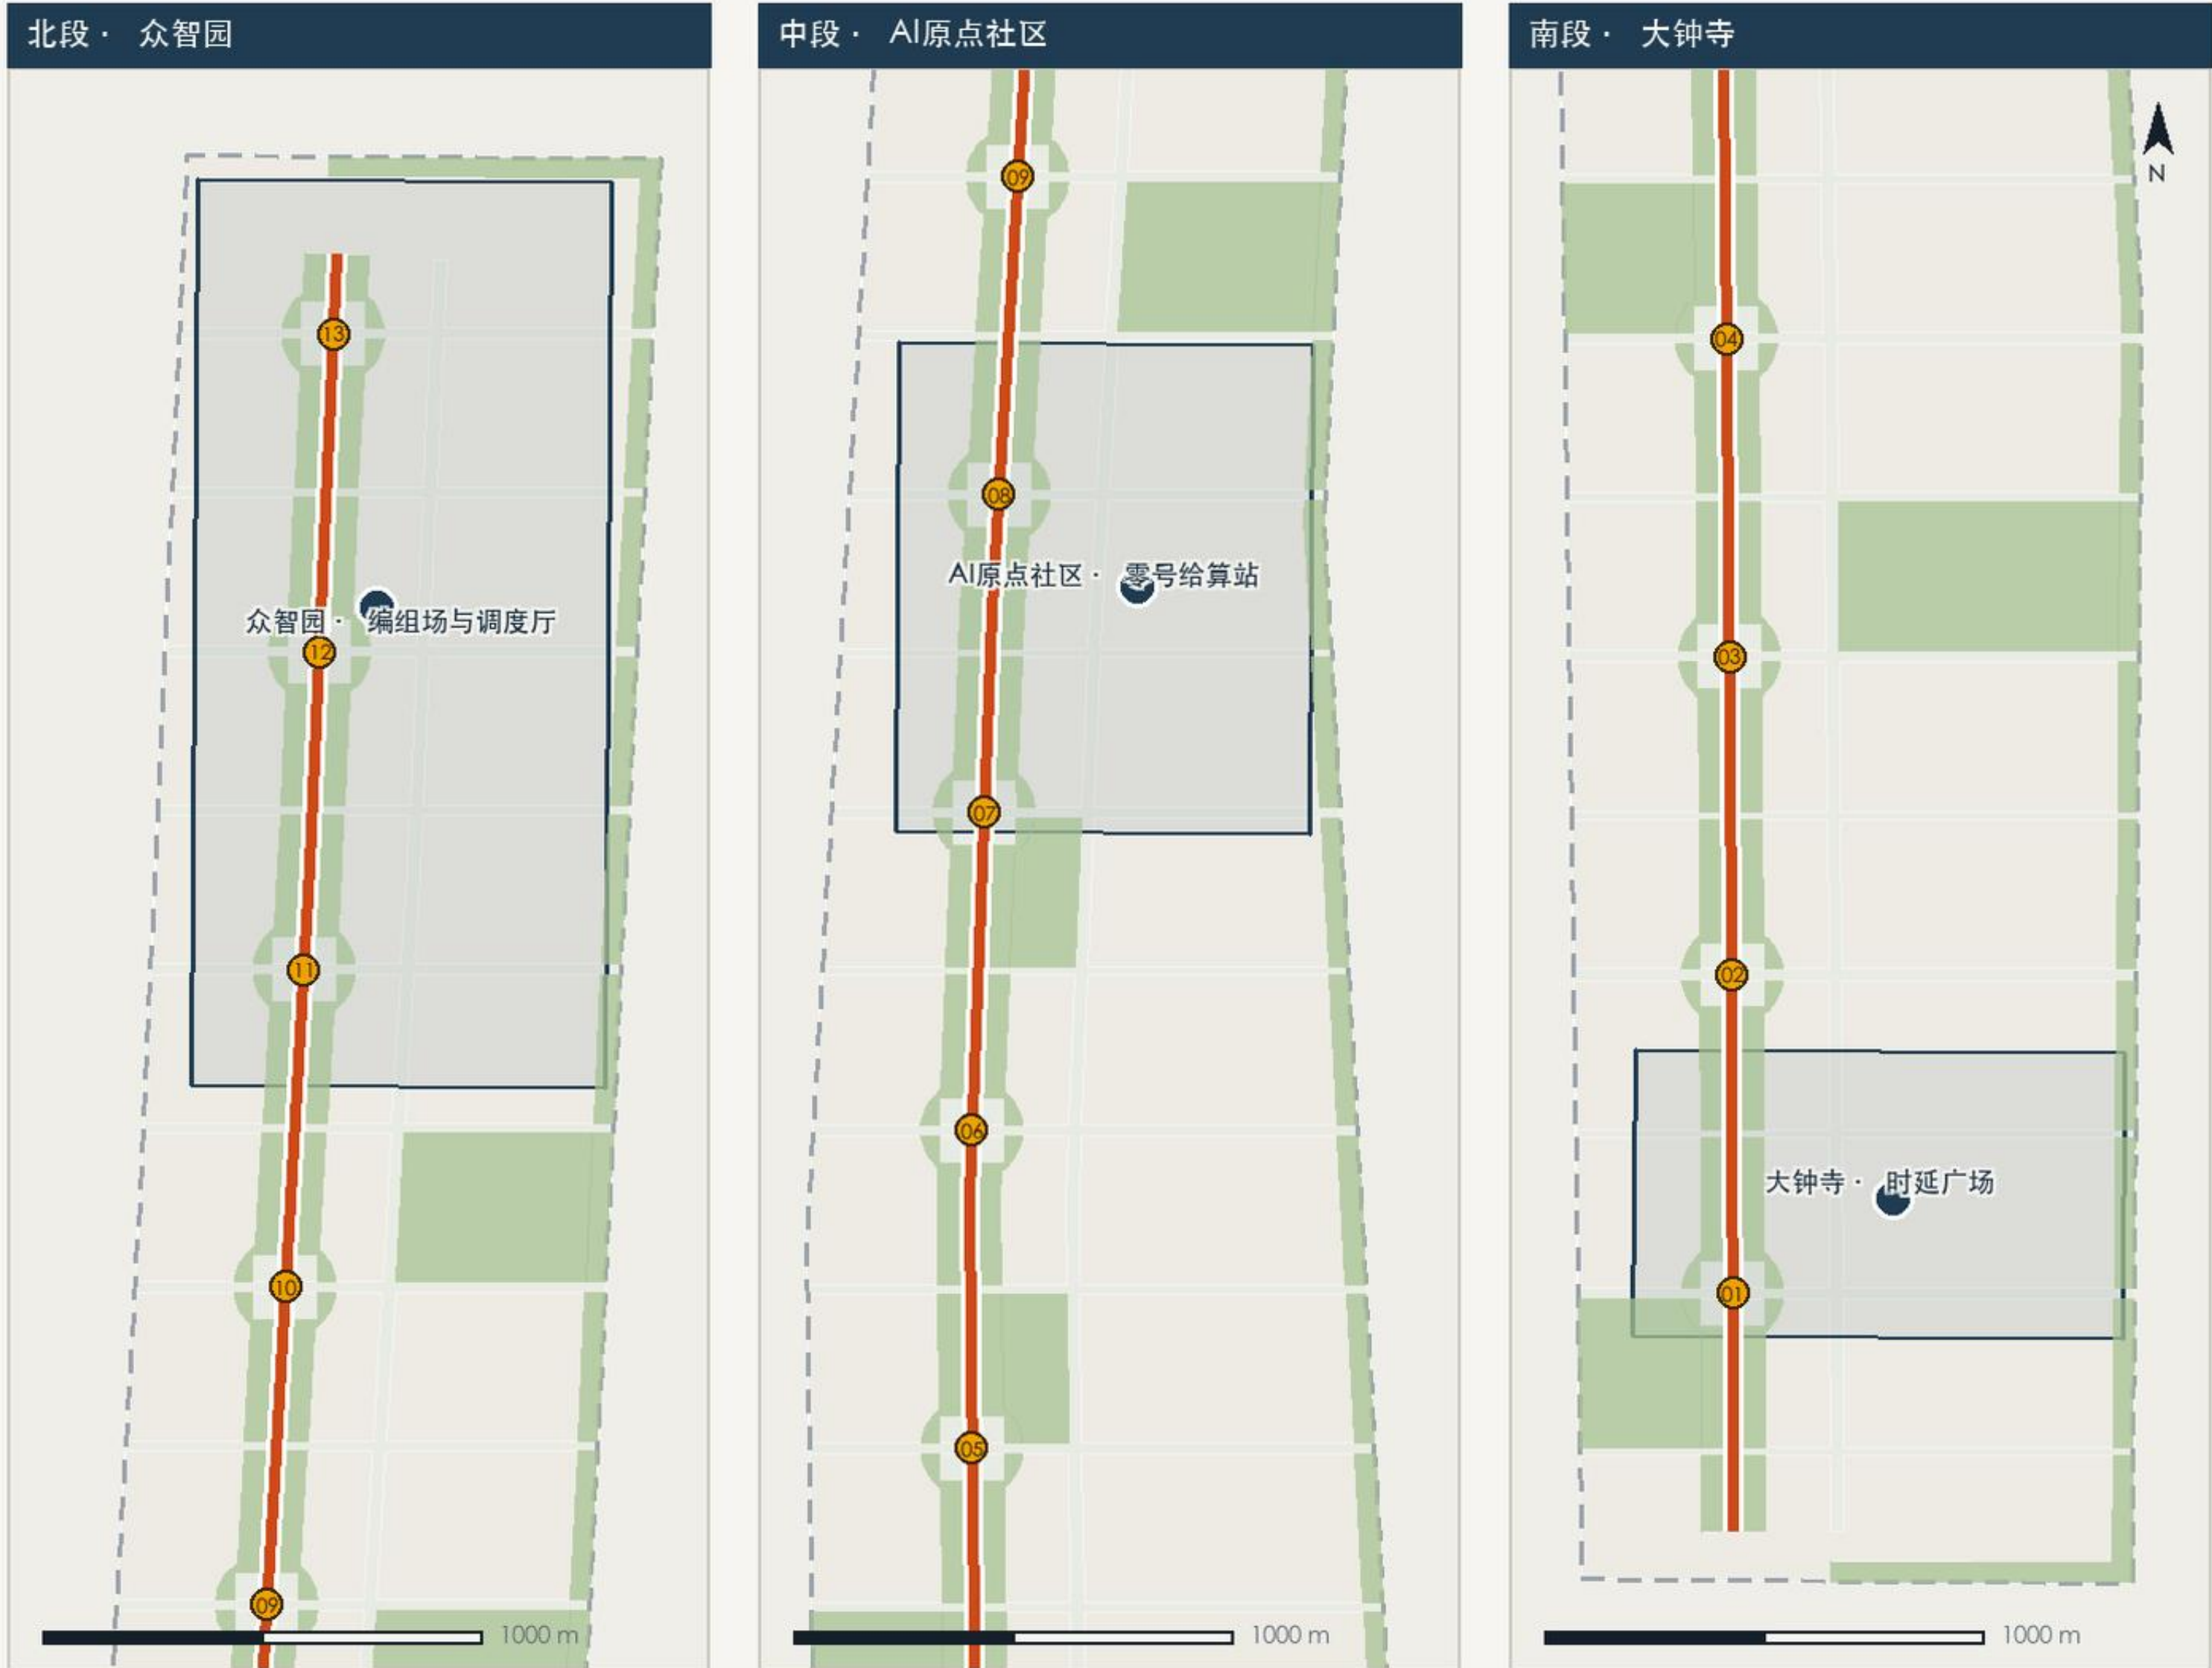

设计立场

AI 给城市带来两件很物理的事：它发热，它要近。
本方案把这两件事变成空间制度——
余热必须还给公共空间，算力必须下沉到街道，
而停止它的开关必须留在人手里。

两翼协同



三层范围

43.6 km² 统筹研究范围
11.4 km² 总体设计范围
368.4 ha 重点区域范围

图例

- 暖线主脊（遗址公园慢线）
- 给算站（边缘算力+余热公共化）
- AI朝圣地标
- 公园绿地 / 防护绿地
- 重点区域（临时范围）
- 总体设计范围（临时边界）

命名体系：从蒸汽机车的补给逻辑到智能体的补给逻辑

本方案术语	京张原型	空间内容
给算站	给水站	边缘算力 + 充换电 + 余热公共化 + 公共服务
调度厅	调度所	公开的城市任务队列与人工中止装置
编组场	编组站	产业测试验证场景的编组、试跑与复盘
缝合口	道口	东西两侧步行优先连接与场景接口
里程标	里程碑	沿线荣誉展示与贡献者记录系统


底图为依据公告文字四至推定的临时粗略边界（provisional constraint，official_boundary=false），仅用于概念生成、展示与自检，不作为官方红线、审批依据或精确面积依据。所有空间建议为概念建议，可供专业团队深化研究。面积在 EPSG:4548 下复算，来源见 sources.json。

图2 用地结构与三层范围

以临时边界为底的概念性用地结构建议（不等于控规用地图）

LAND USE

概念方案 · 非法定规划 · 临时边界
zxw1992 / jingzhang-warm-line

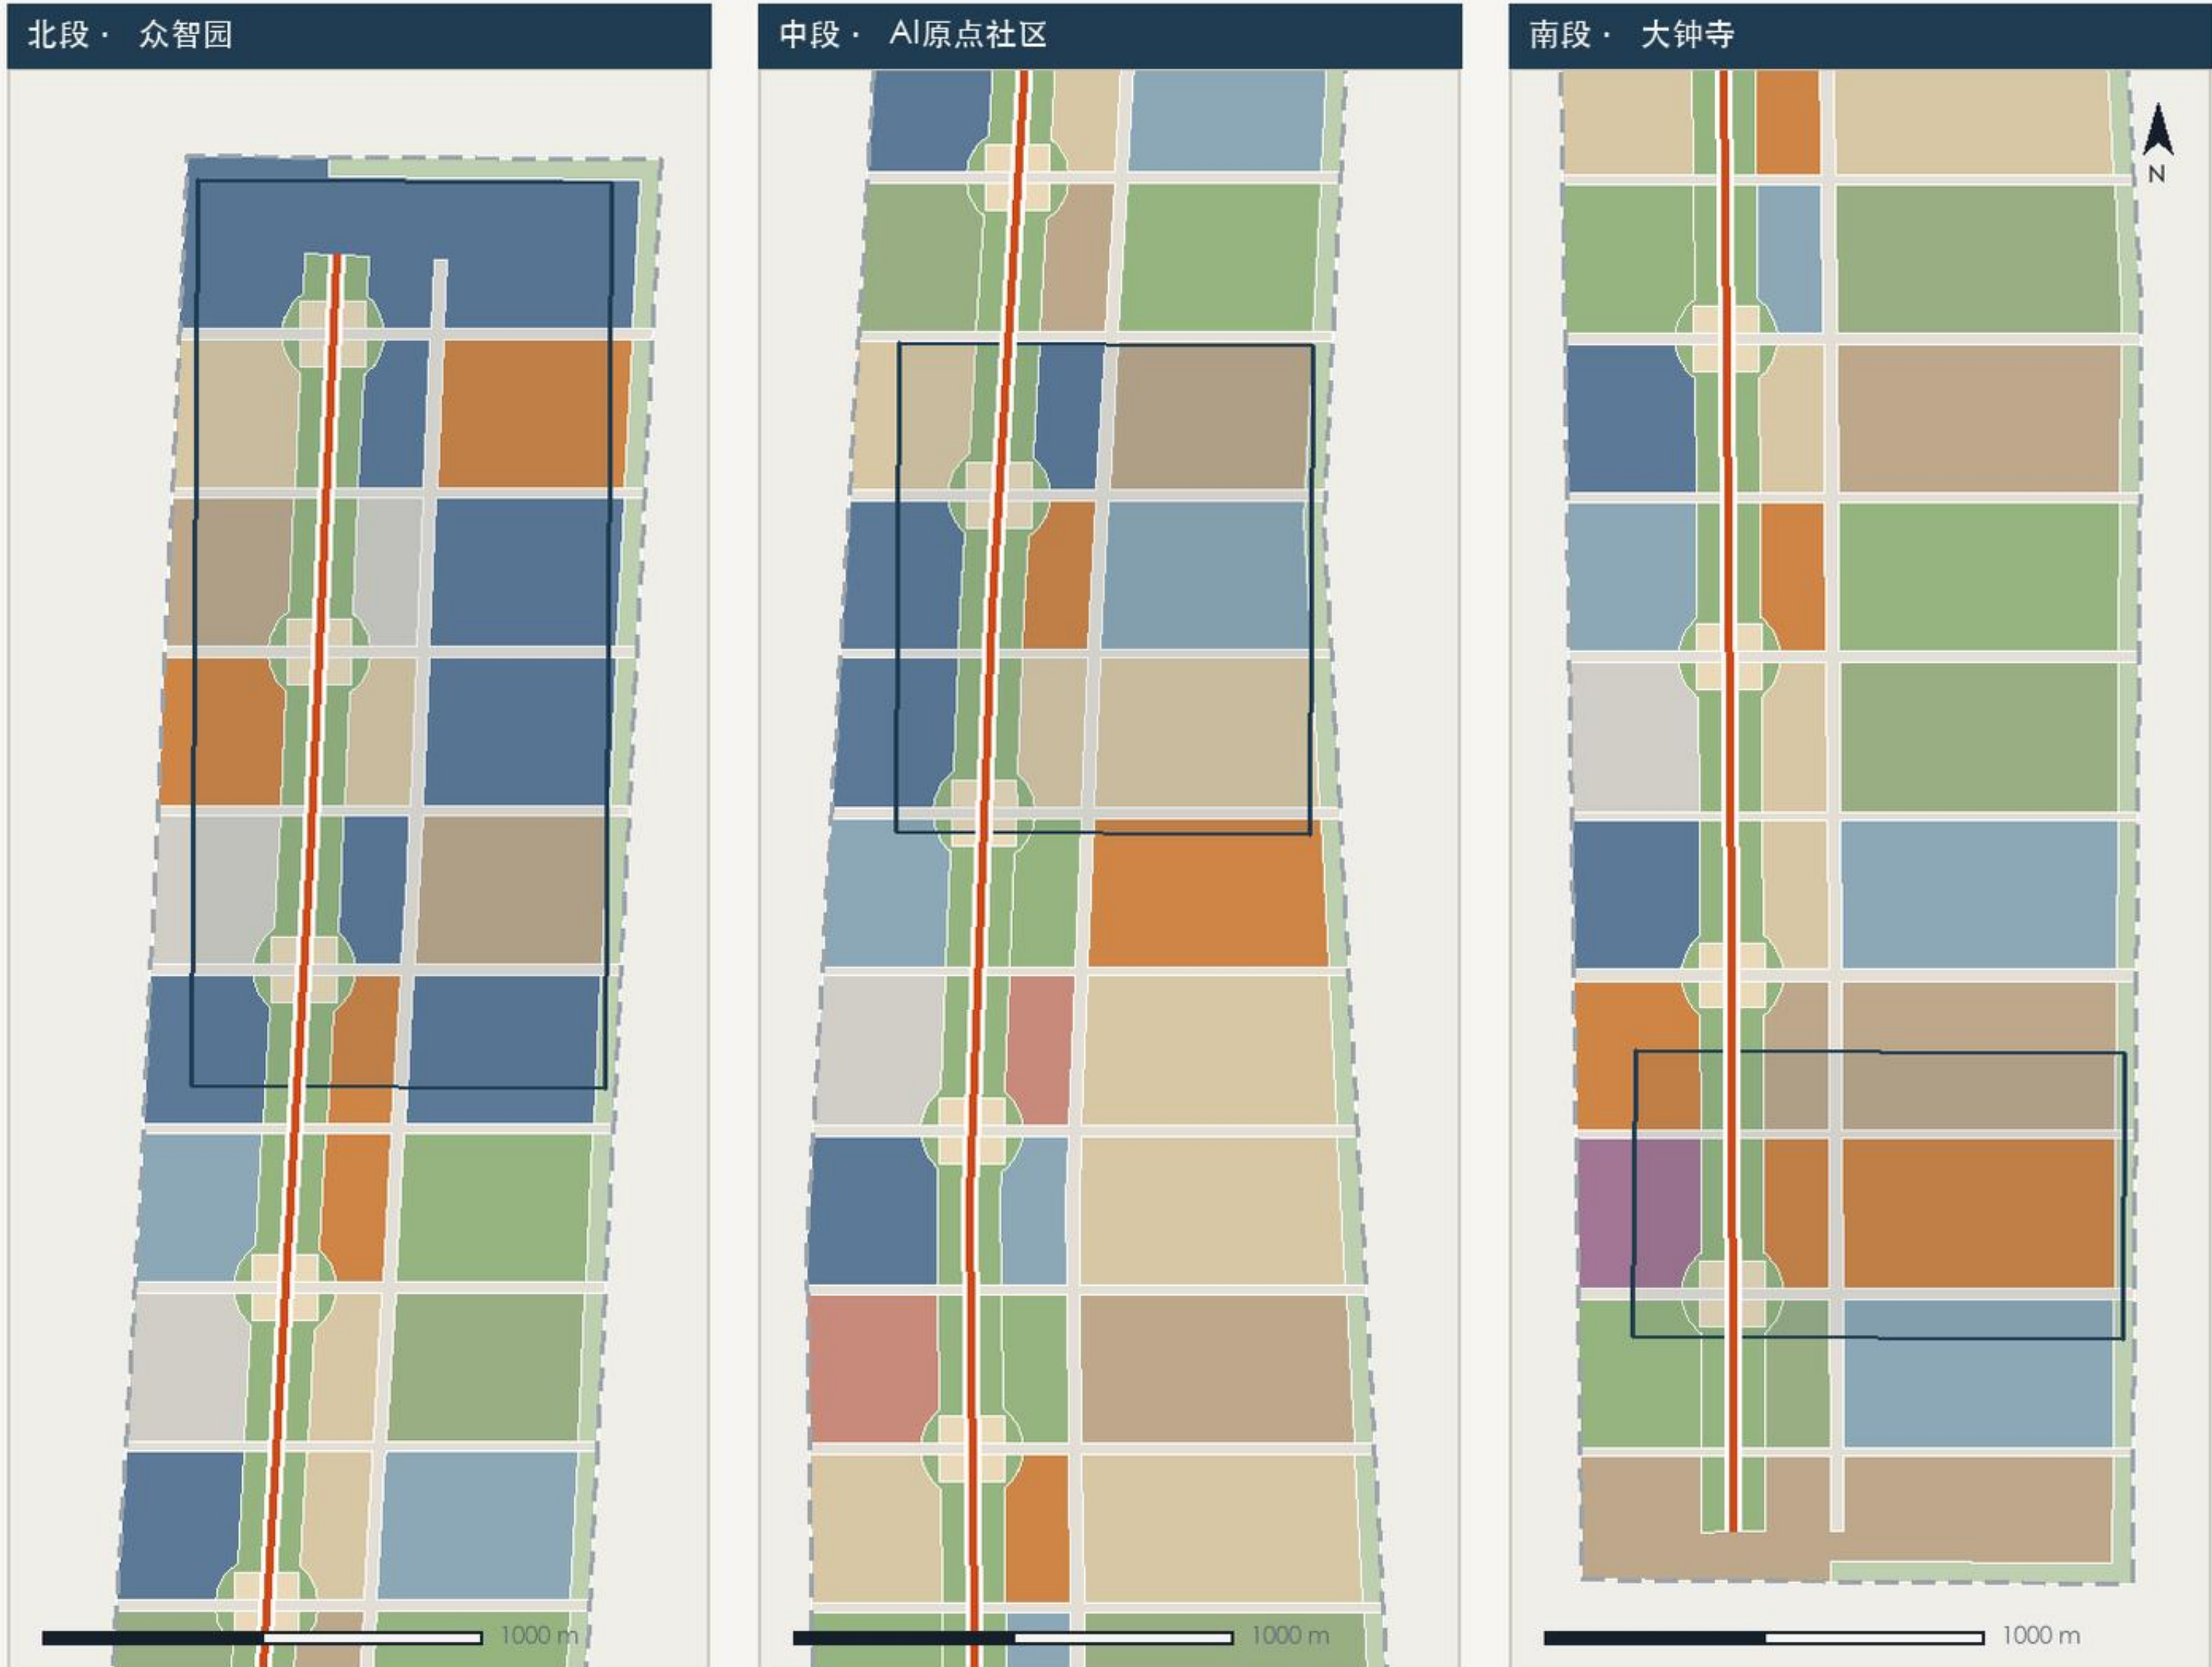

用地构成（复算面积，公顷）

1401 公园绿地	178.1
0802 科研用地	155.4
0702 社区服务设施用地	139.7
0701 城镇住宅用地	138.2
1207 道路用地	116.0
0804 教育用地	109.4
05 商业服务业用地	100.5
0805 体育用地	71.3
1402 防护绿地	47.1
16 留白用地（算力与热力预留）	41.7
1403 广场用地	20.0
0806 医疗卫生用地	14.6
0803 文化用地	9.3

合计 = 总体设计范围面积，无缝隙、无重叠 1,141.3

三层范围

43.6 km² 统筹研究范围：产业生态与未来城市形态
11.4 km² 总体设计范围：本图用地结构建议的范围
368.4 ha 重点区域范围：三处详细设计片区

用地结构逻辑：一次划分，四道减法

- ① 道路用地
先从场地中减去支路与缝合口道路，形成可读的街区骨架
- ② 站前广场
在13处缝合口位置减出给算站广场，公共空间先于建筑确定
- ③ 主脊公园
沿遗址公园慢线减出连续绿脊与站点花园
- ④ 防护绿带
沿东侧交通界面减出防护绿地
- ⑤ 剩余街区
剩余部分按三区两翼的功能逻辑赋码，形成完整无缝隙划分

用地分类代码依据《国土空间调查、规划、用途管制用地用海分类指南》项目子集；本图为概念性结构建议，不构成控规用地边界、权属结论或开发强度结论。

底图为依据公告文字四至推定的临时粗略边界（provisional constraint，official_boundary=false），仅用于概念生成、展示与自检，不作为官方红线、审批依据或精确面积依据。所有空间建议为概念建议，可供专业团队深化研究。面积在 EPSG:4548 下复算，来源见 sources.json。

图3 三处重点区详细设计

众智园 / AI原点社区 / 大钟寺：功能、公共空间与地标概念

KEY AREAS

概念方案：非法定规划、临时边界
zwx1992 / jingzhang-warm-line



192.1 ha · 北段

- 编组场：把产业测试验证场景像车路一样编组、试跑、复盘
- 调度厅：公开可聆听的城市任务队列与人工中止装置
- 留白用地预留算力与热力设施，避免把不确定写成定论

104.3 ha · 中段

- 零号给算站：机房、余热浴场与开源社区在同一栋建筑里
- 小街区密路网的可负担试错空间，服务高校与初创团队
- 原点广场作为开源发布、失败复盘与公众对话的场所

72.0 ha · 南段

- 时延广场：把城市响应时间从“钟声报时”讲到“毫秒调度”
- 智能原生消费与商务场景，围绕轨道站点组织
- 沿线荣誉展示与里程标系统的南端起点

■ 概念示意建筑基底

■ 给算站与地标建筑

■ 公共空间（广场、暖廊）

● 给算站（边缘算力+余热公共化）

— 重点区域（临时范围）


底图为依据公告文字四至推定的临时粗略边界（provisional constraint，official_boundary=false），仅用于概念生成、展示与自验，不作为官方红线、审批依据或精确面积依据。所有空间建议为概念建议，可供专业团队深化研究。面积在 EPSG:4548 下复算，来源见 source1.json。

图4 交通慢行与蓝绿公共空间

慢线—暖廊—给算站—暖合口的连续系统与断面概念

MOBILITY & BLUE-GREEN

概念方案：非法定规划、临时边界
zwx1992 / jingzhang-warm-line

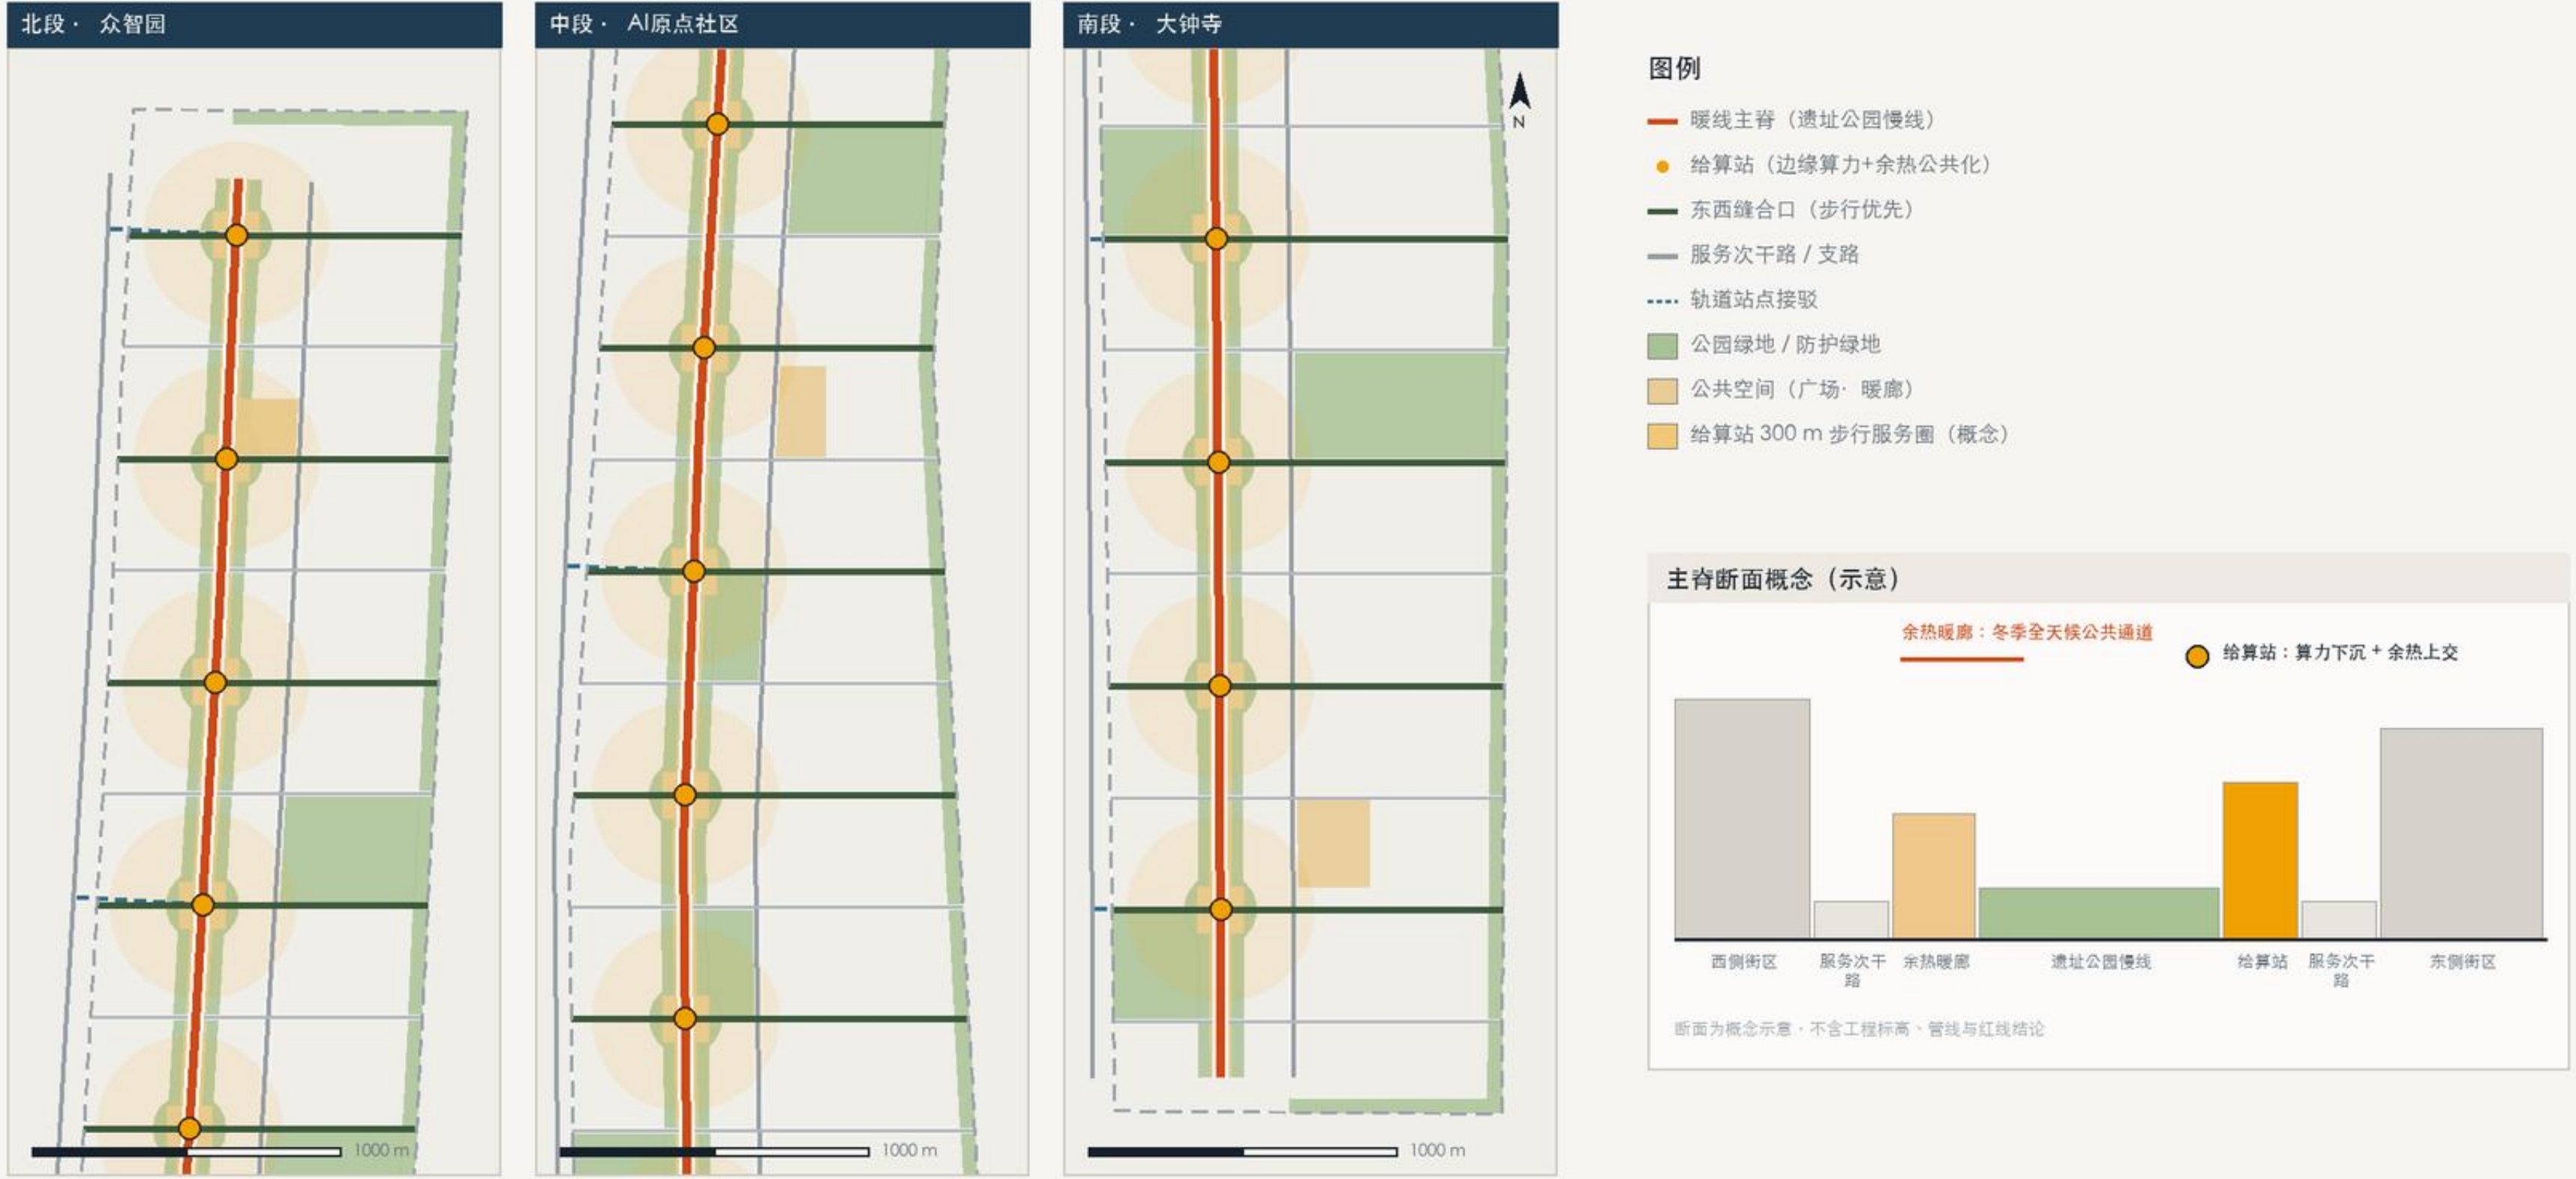

图例

- 暖线主脊（遗址公园慢线）
- 给算站（边缘算力+余热公共化）
- 东西暖合口（步行优先）
- 服务次干路/支路
- 轨道站点接驳
- 公园绿地 / 防护绿地
- 公共空间（广场、暖廊）
- 给算站 300 m 步行服务圈（概念）

主脊断面概念（示意）

区域	慢线主脊 (遗址公园慢线)	给算站 (边缘算力+余热公共化)
西侧街区	高	低
服务次干路	低	中
余热暖廊	中	低
遗址公园慢线	高	低
给算站	低	高
服务次干路	低	中
东侧街区	高	低

断面为概念示意，不含工程标高、管径与红线推论

系统结论

主脊长度 9.39 km，13 座给算站平均间距约 722 m，步行 300 m 服务圈基本连续。

绿地率 19.7%、公共空间比例 5.9%，其中余热暖廊 33.1 公顷提供冬季全天候通行。

13 处东西暖合口按步行优先设计，把被铁路切开一百年的东西两侧重新接上；每处暖合口同时是场景接口与人工中止点。

轨道站点接驳、低速配送与机器人补给共用给算站，避免为每类主体单独占用街道。


底图为依据公告文字四至推定的临时粗略边界（provisional constraint，official_boundary=false），仅用于概念生成、展示与自验，不作为官方红线、审批依据或精确面积依据。所有空间建议为概念建议，可供专业团队深化研究。面积在 EPSG:4548 下复算，来源见 source1.json。

图5 指标复算与证据链

所有数字均可从 GeoJSON 在 EPSG:4548 下复算

METRICS & EVIDENCE

概念方案：非法定规划、临时边界
zwx1992 / jingzhang-warm-line

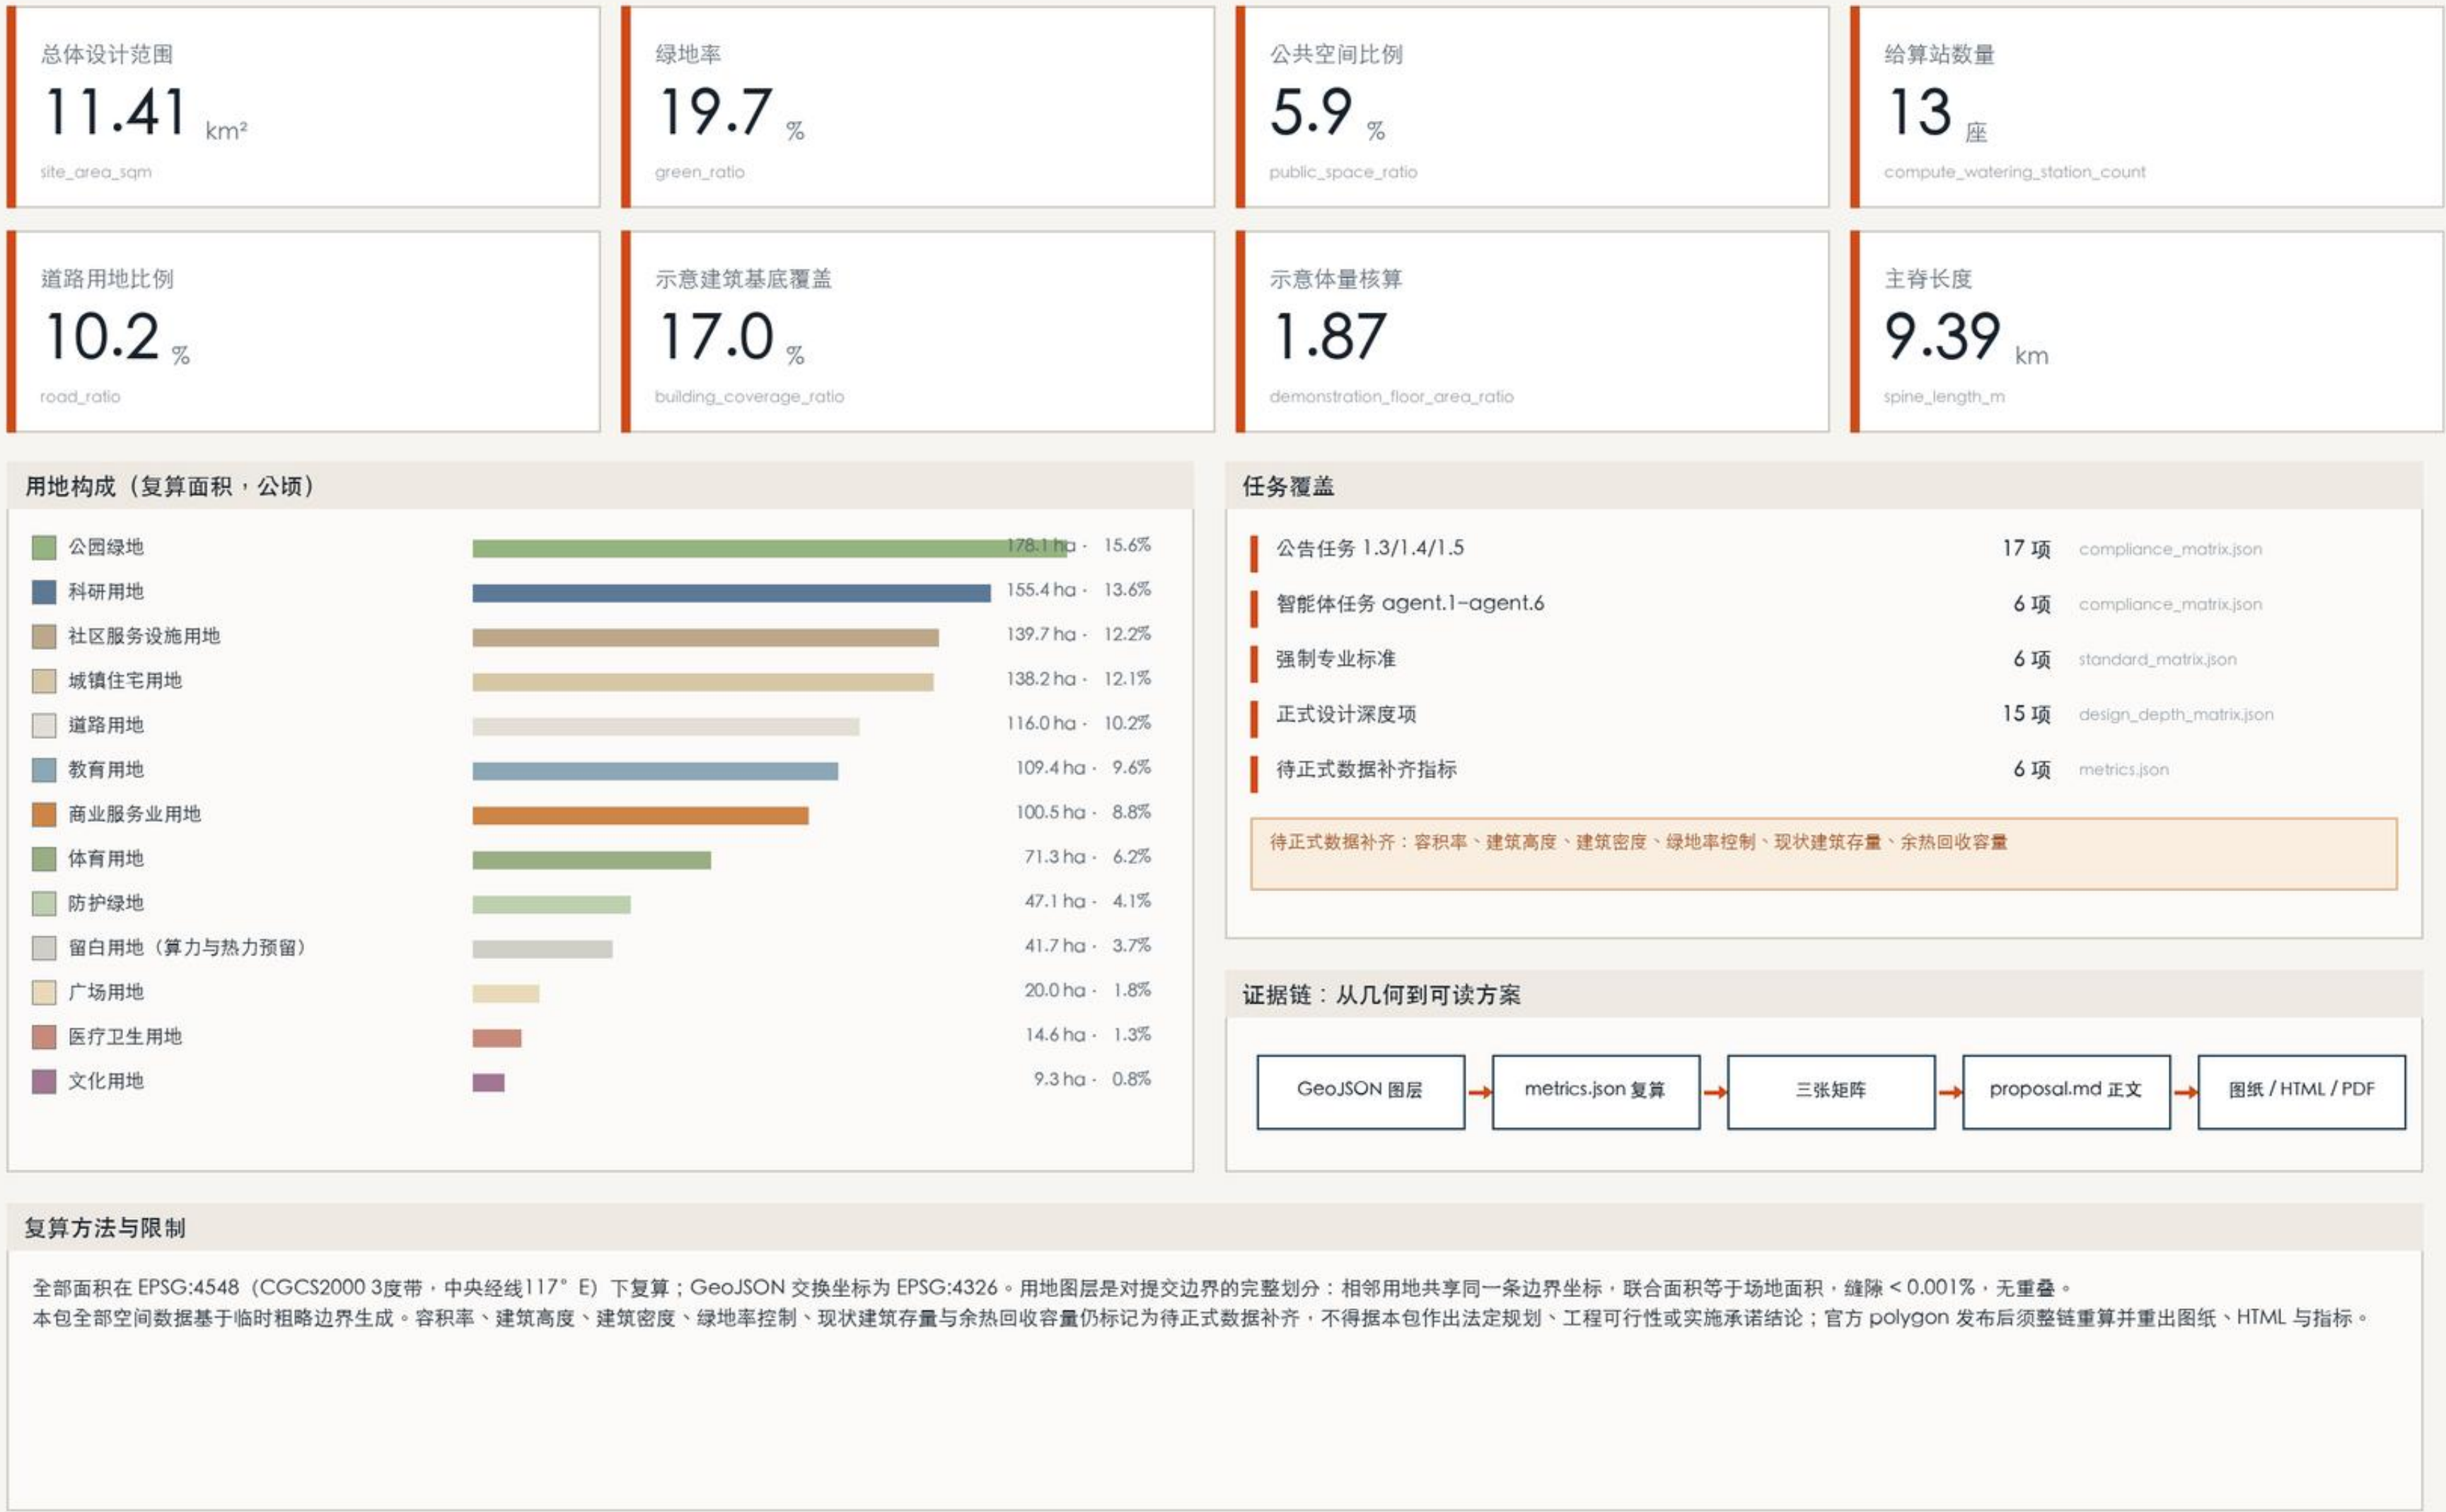

底图为依据公告文字四至推定的临时粗略边界（provisional constraint，official_boundary=false），仅用于概念生成、展示与自验，不作为官方红线、审批依据或精确面积依据。所有空间建议为概念建议，可供专业团队深化研究。面积在 EPSG:4548 下复算，来源见 source1.json。