



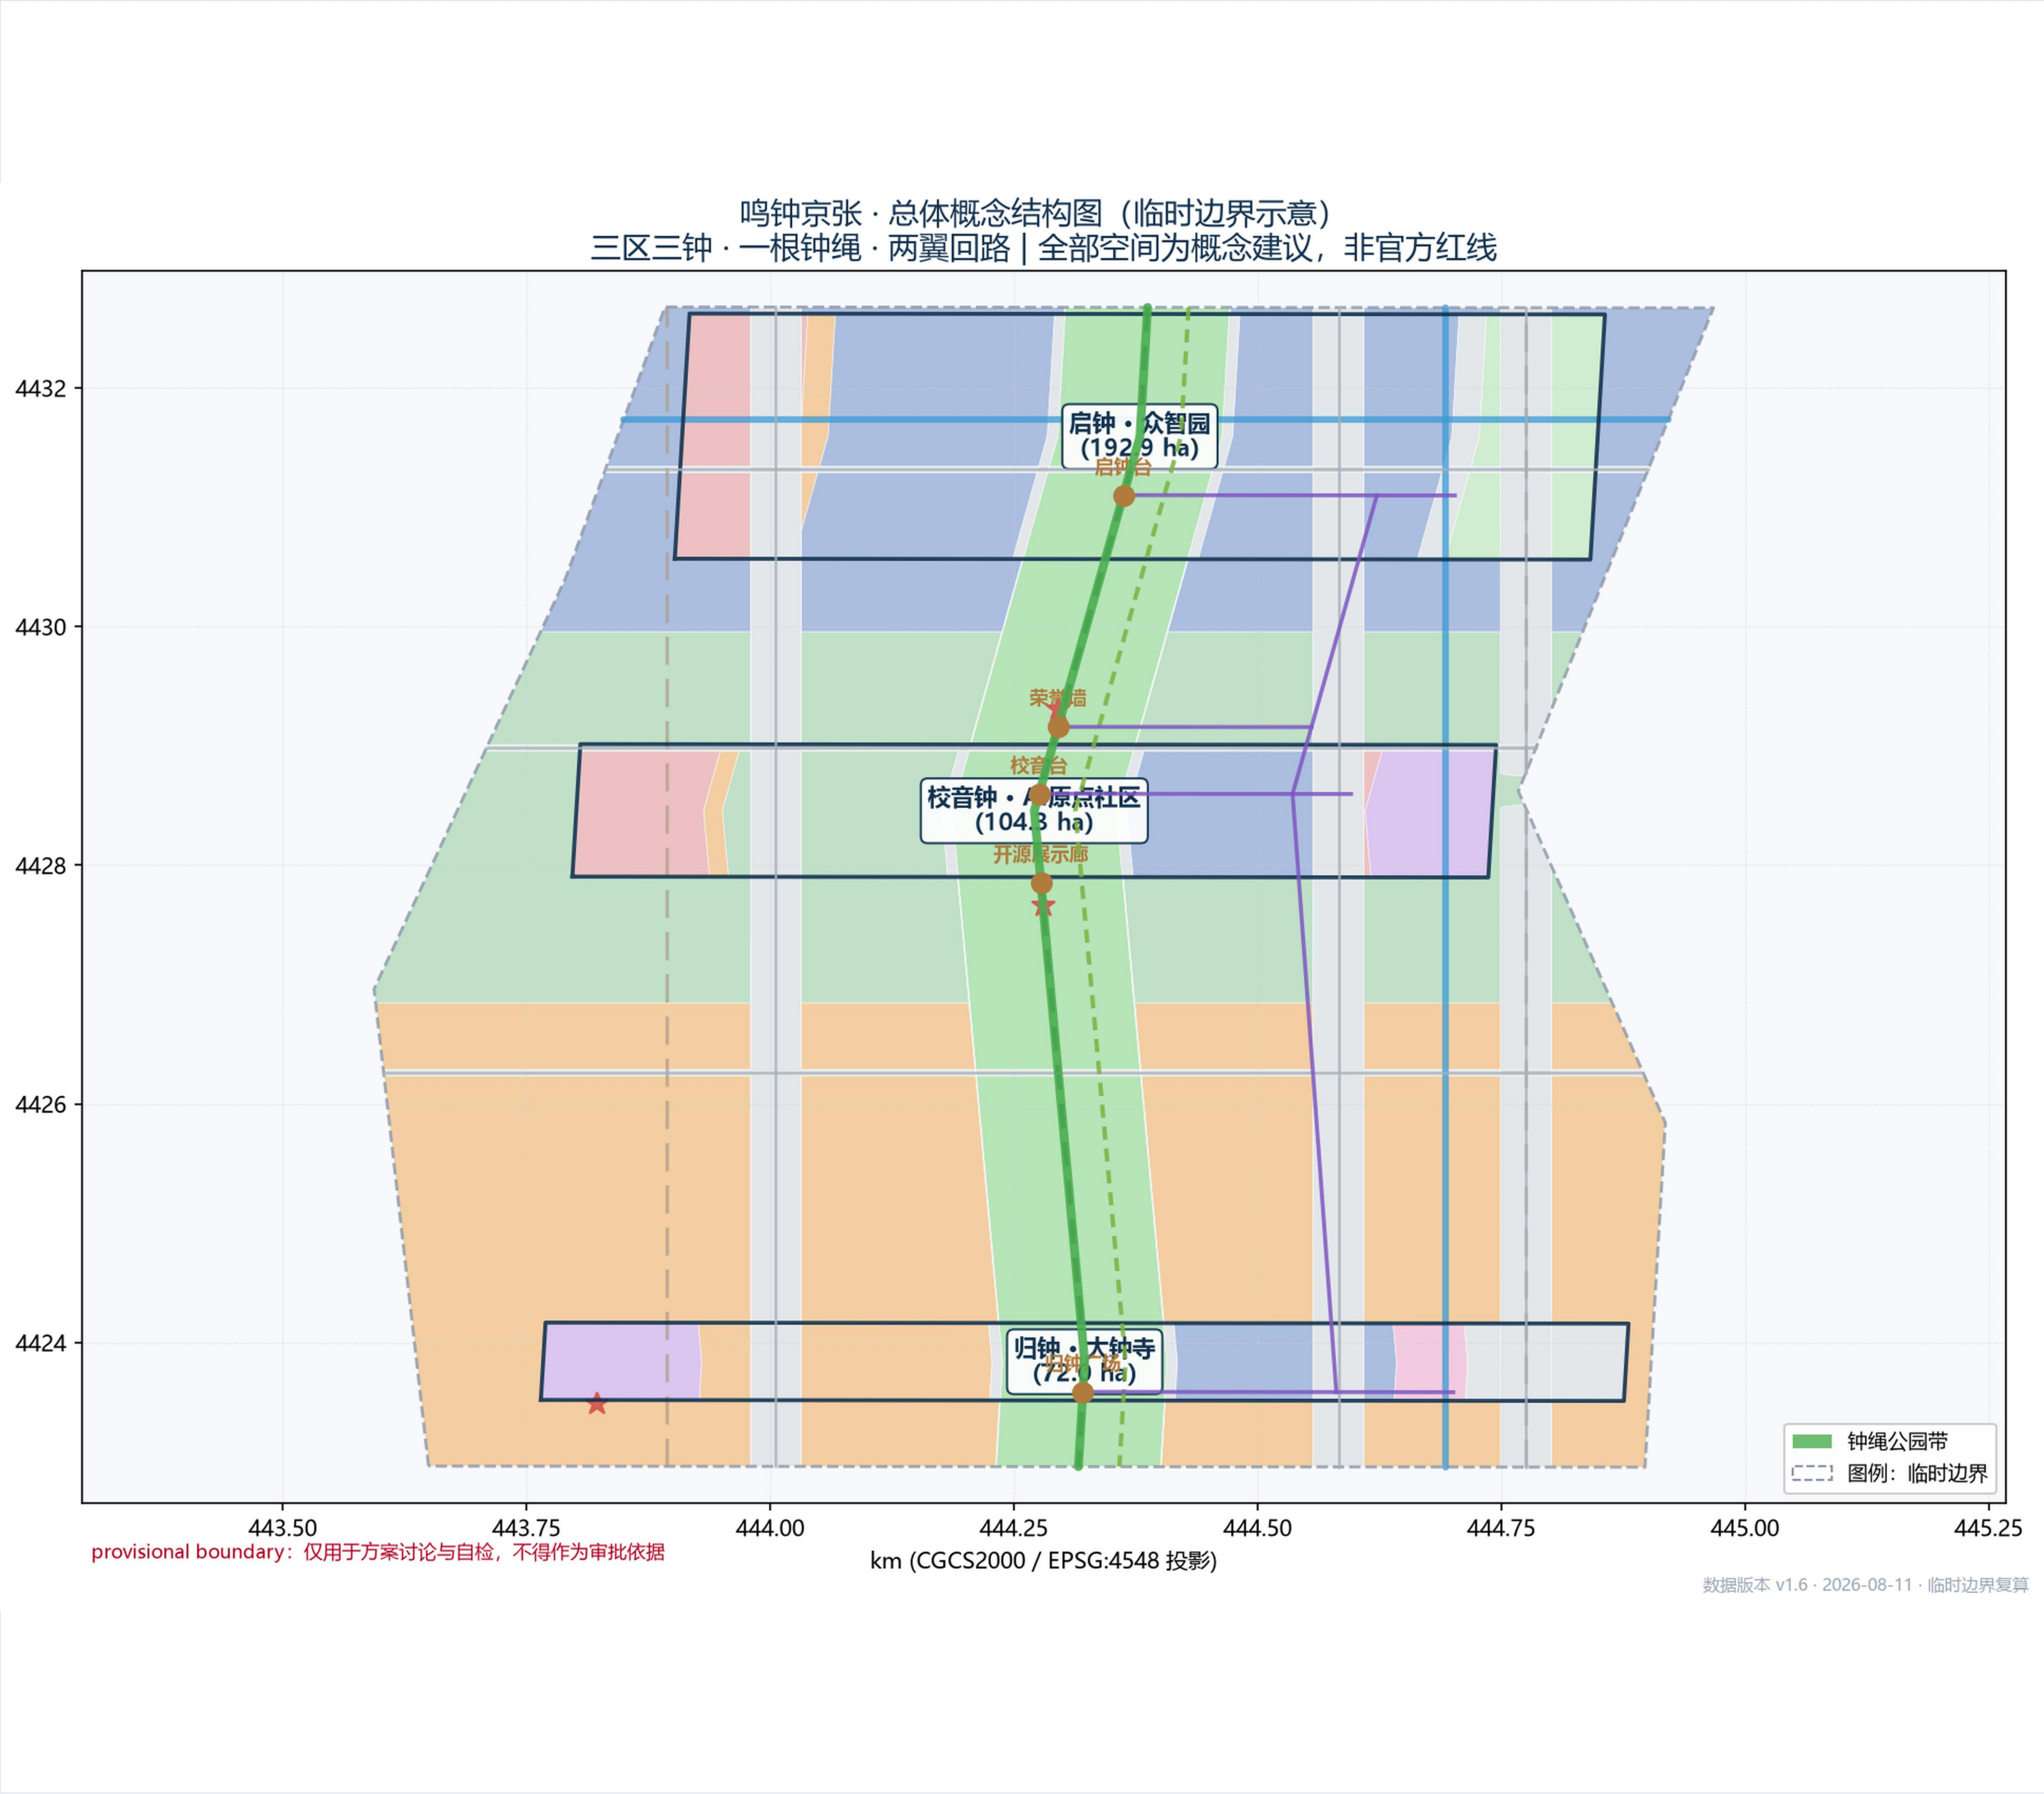

一根钟绳 · 三区三钟 · 两翼回路


统筹研究 43.6 km² → 总体设计 11.4 km² → 重点区域 368.4 ha；钟绳约 9.7 km 贯穿南北。

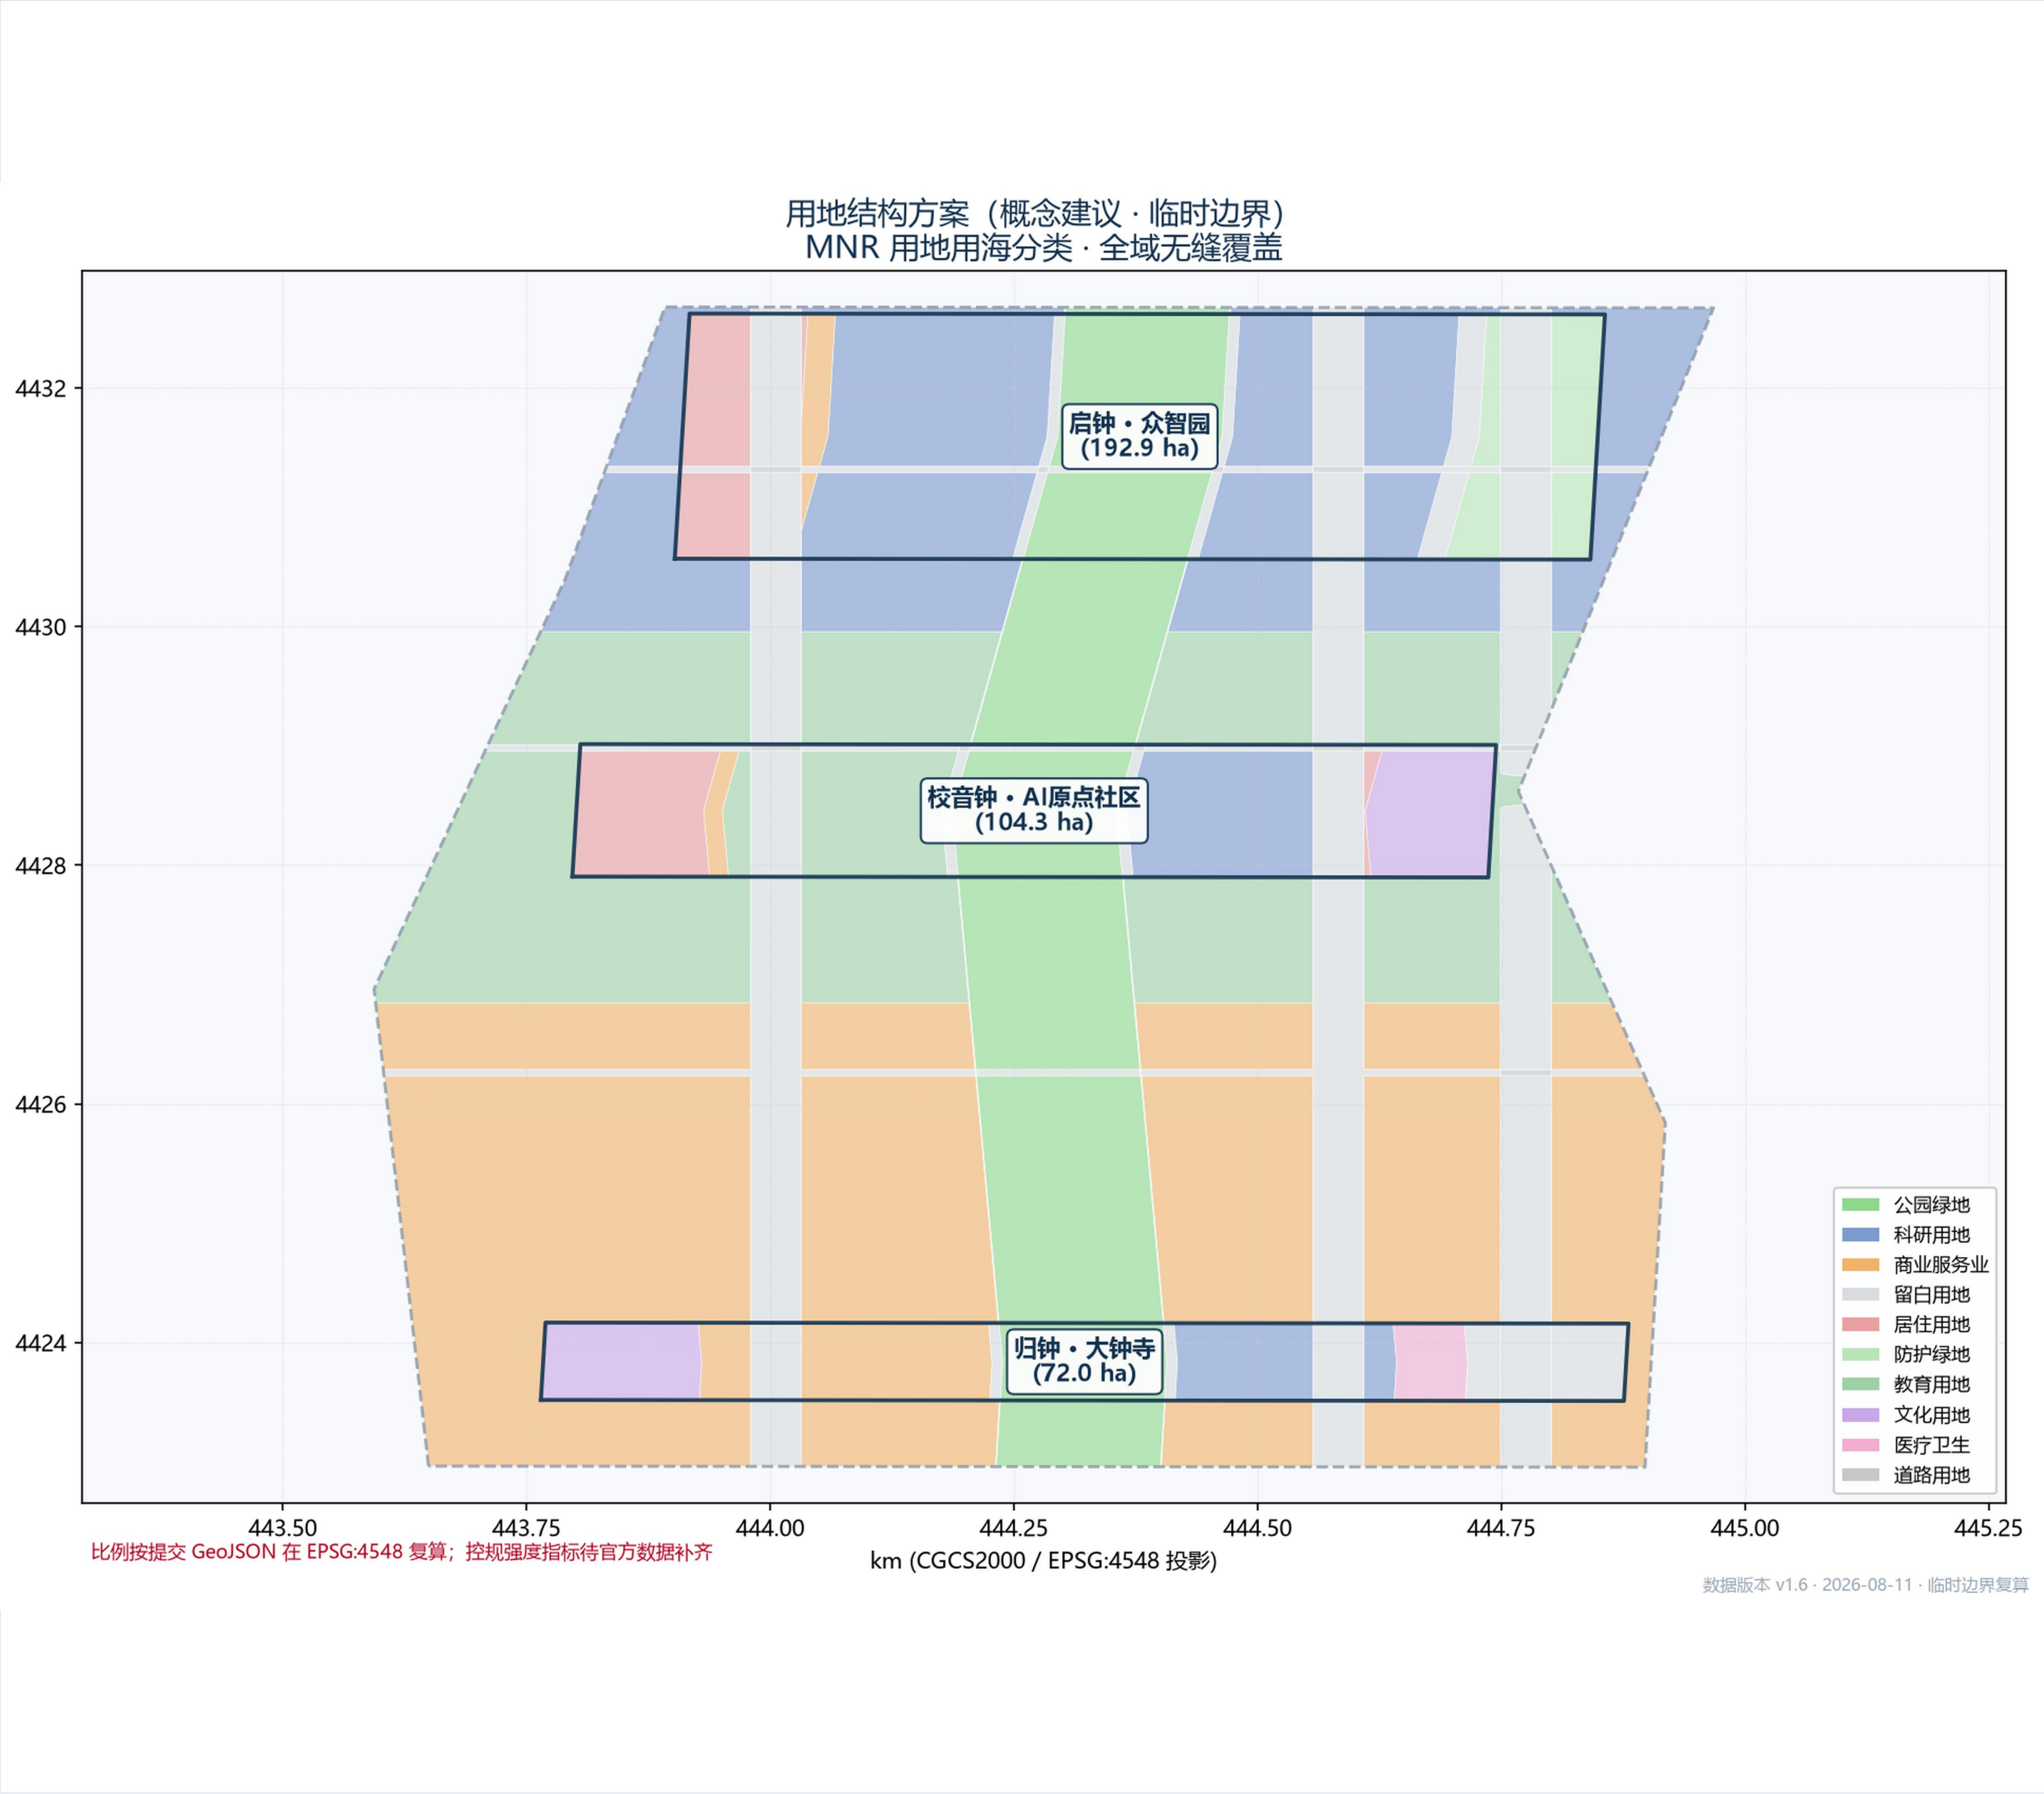



北研发 — 中教育孵化 — 南消费转化

科研 16% / 商业 30% / 教育 17% / 绿地 16% / 留白 16%; 开发强度待官方数据。

三处重点区域详细设计索引（临时边界）
启钟（自主创新）→ 校音钟（生态校准）→ 归钟（市场回响）

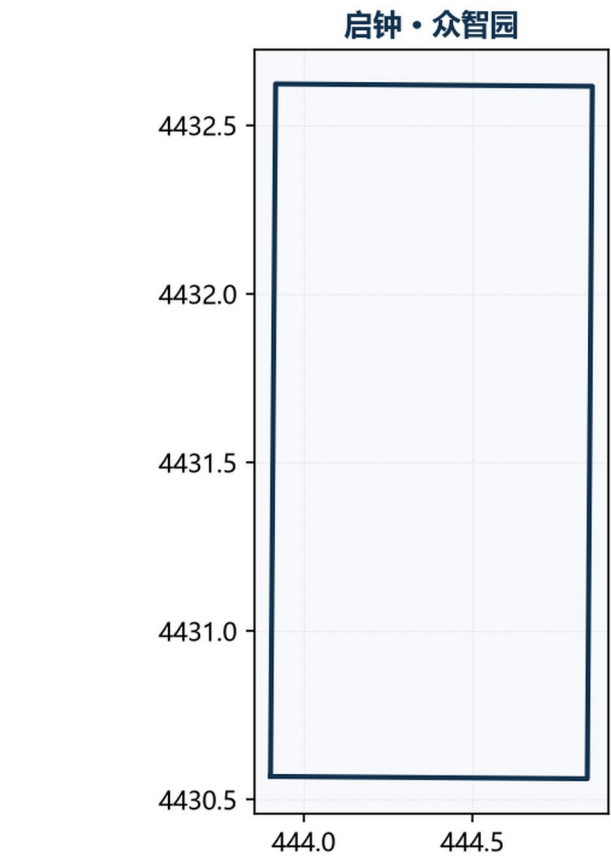


重点区面积为临时边界复算；拆改留与强度为方向性概念建议

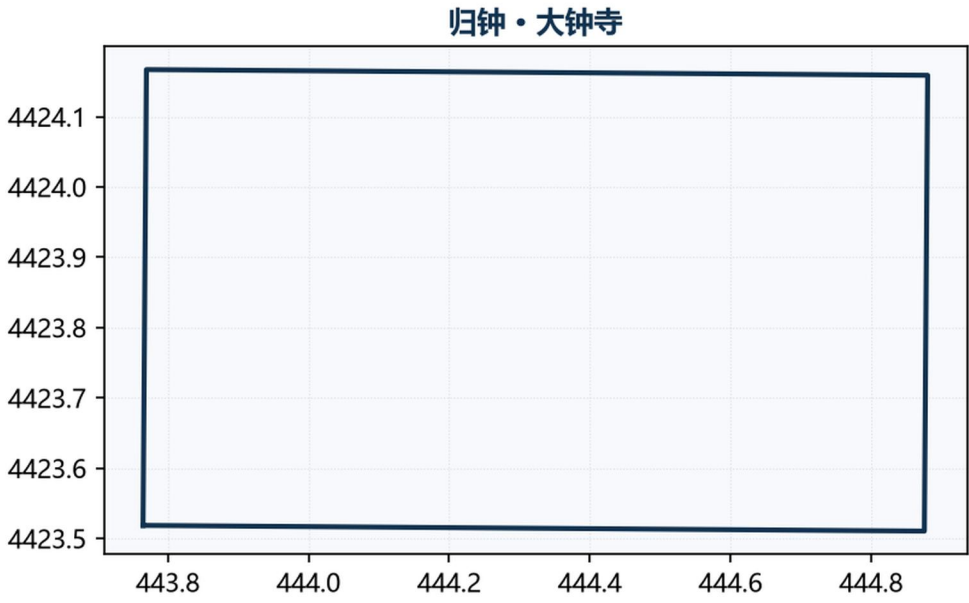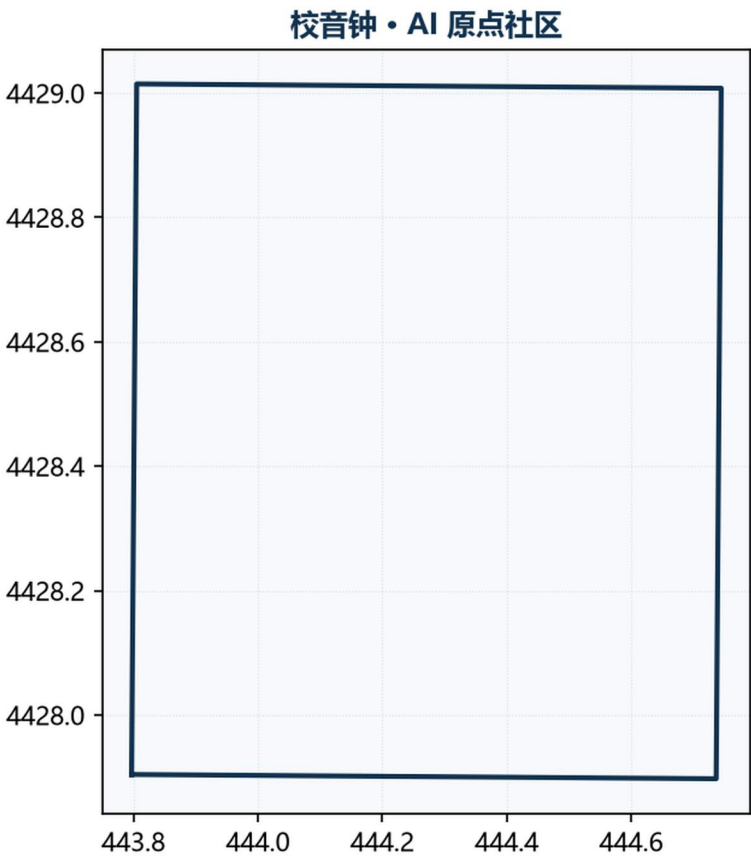

数据版本 v1.6 · 2026-08-11 · 临时边界复算

众智园 • 原点社区 • 大钟寺


花园型 193 ha / 近校型 104 ha / 城市型 72 ha；各配空间结构、更新策略与 AI 场景。

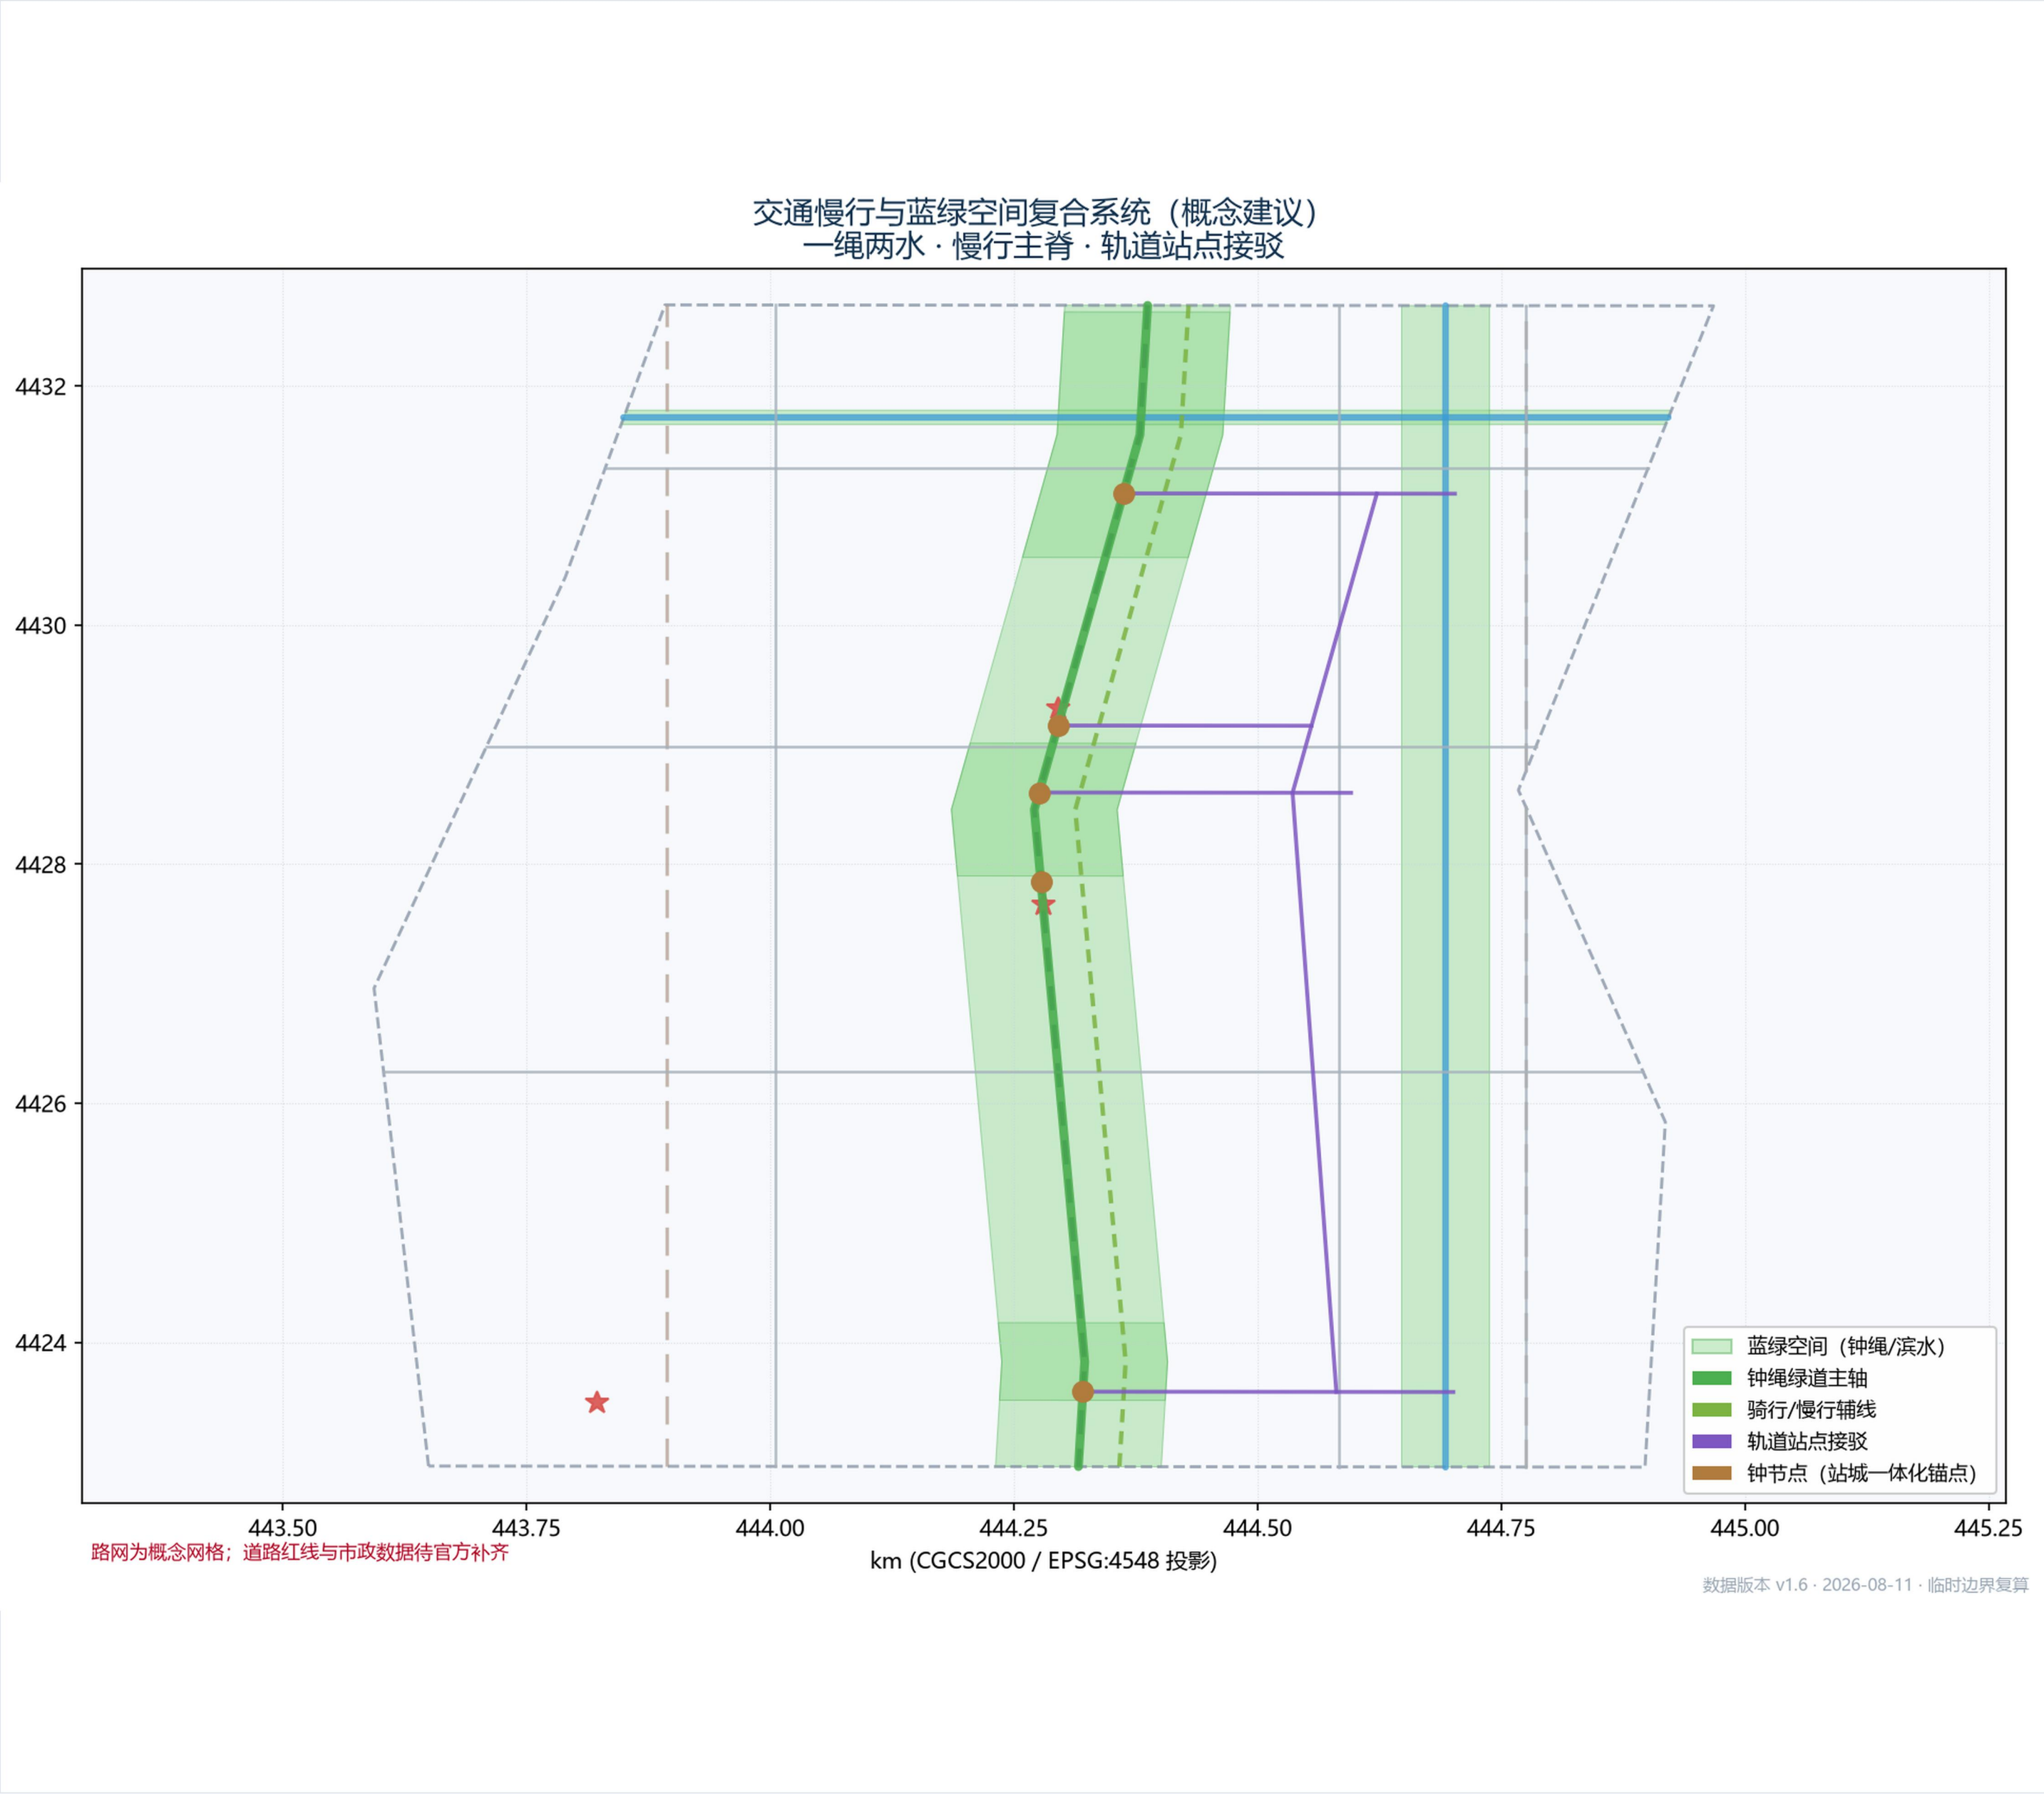

钟绳绿道 + 三站一体化




路网 60.5 km（概念网格）；绿地率约 23%；大钟寺/五道口/清华东路西口 500m 圈层耦合钟节点。

交通慢行与蓝绿空间复合系统（概念建议）
一绳两水 · 慢行主脊 · 轨道站点接驳

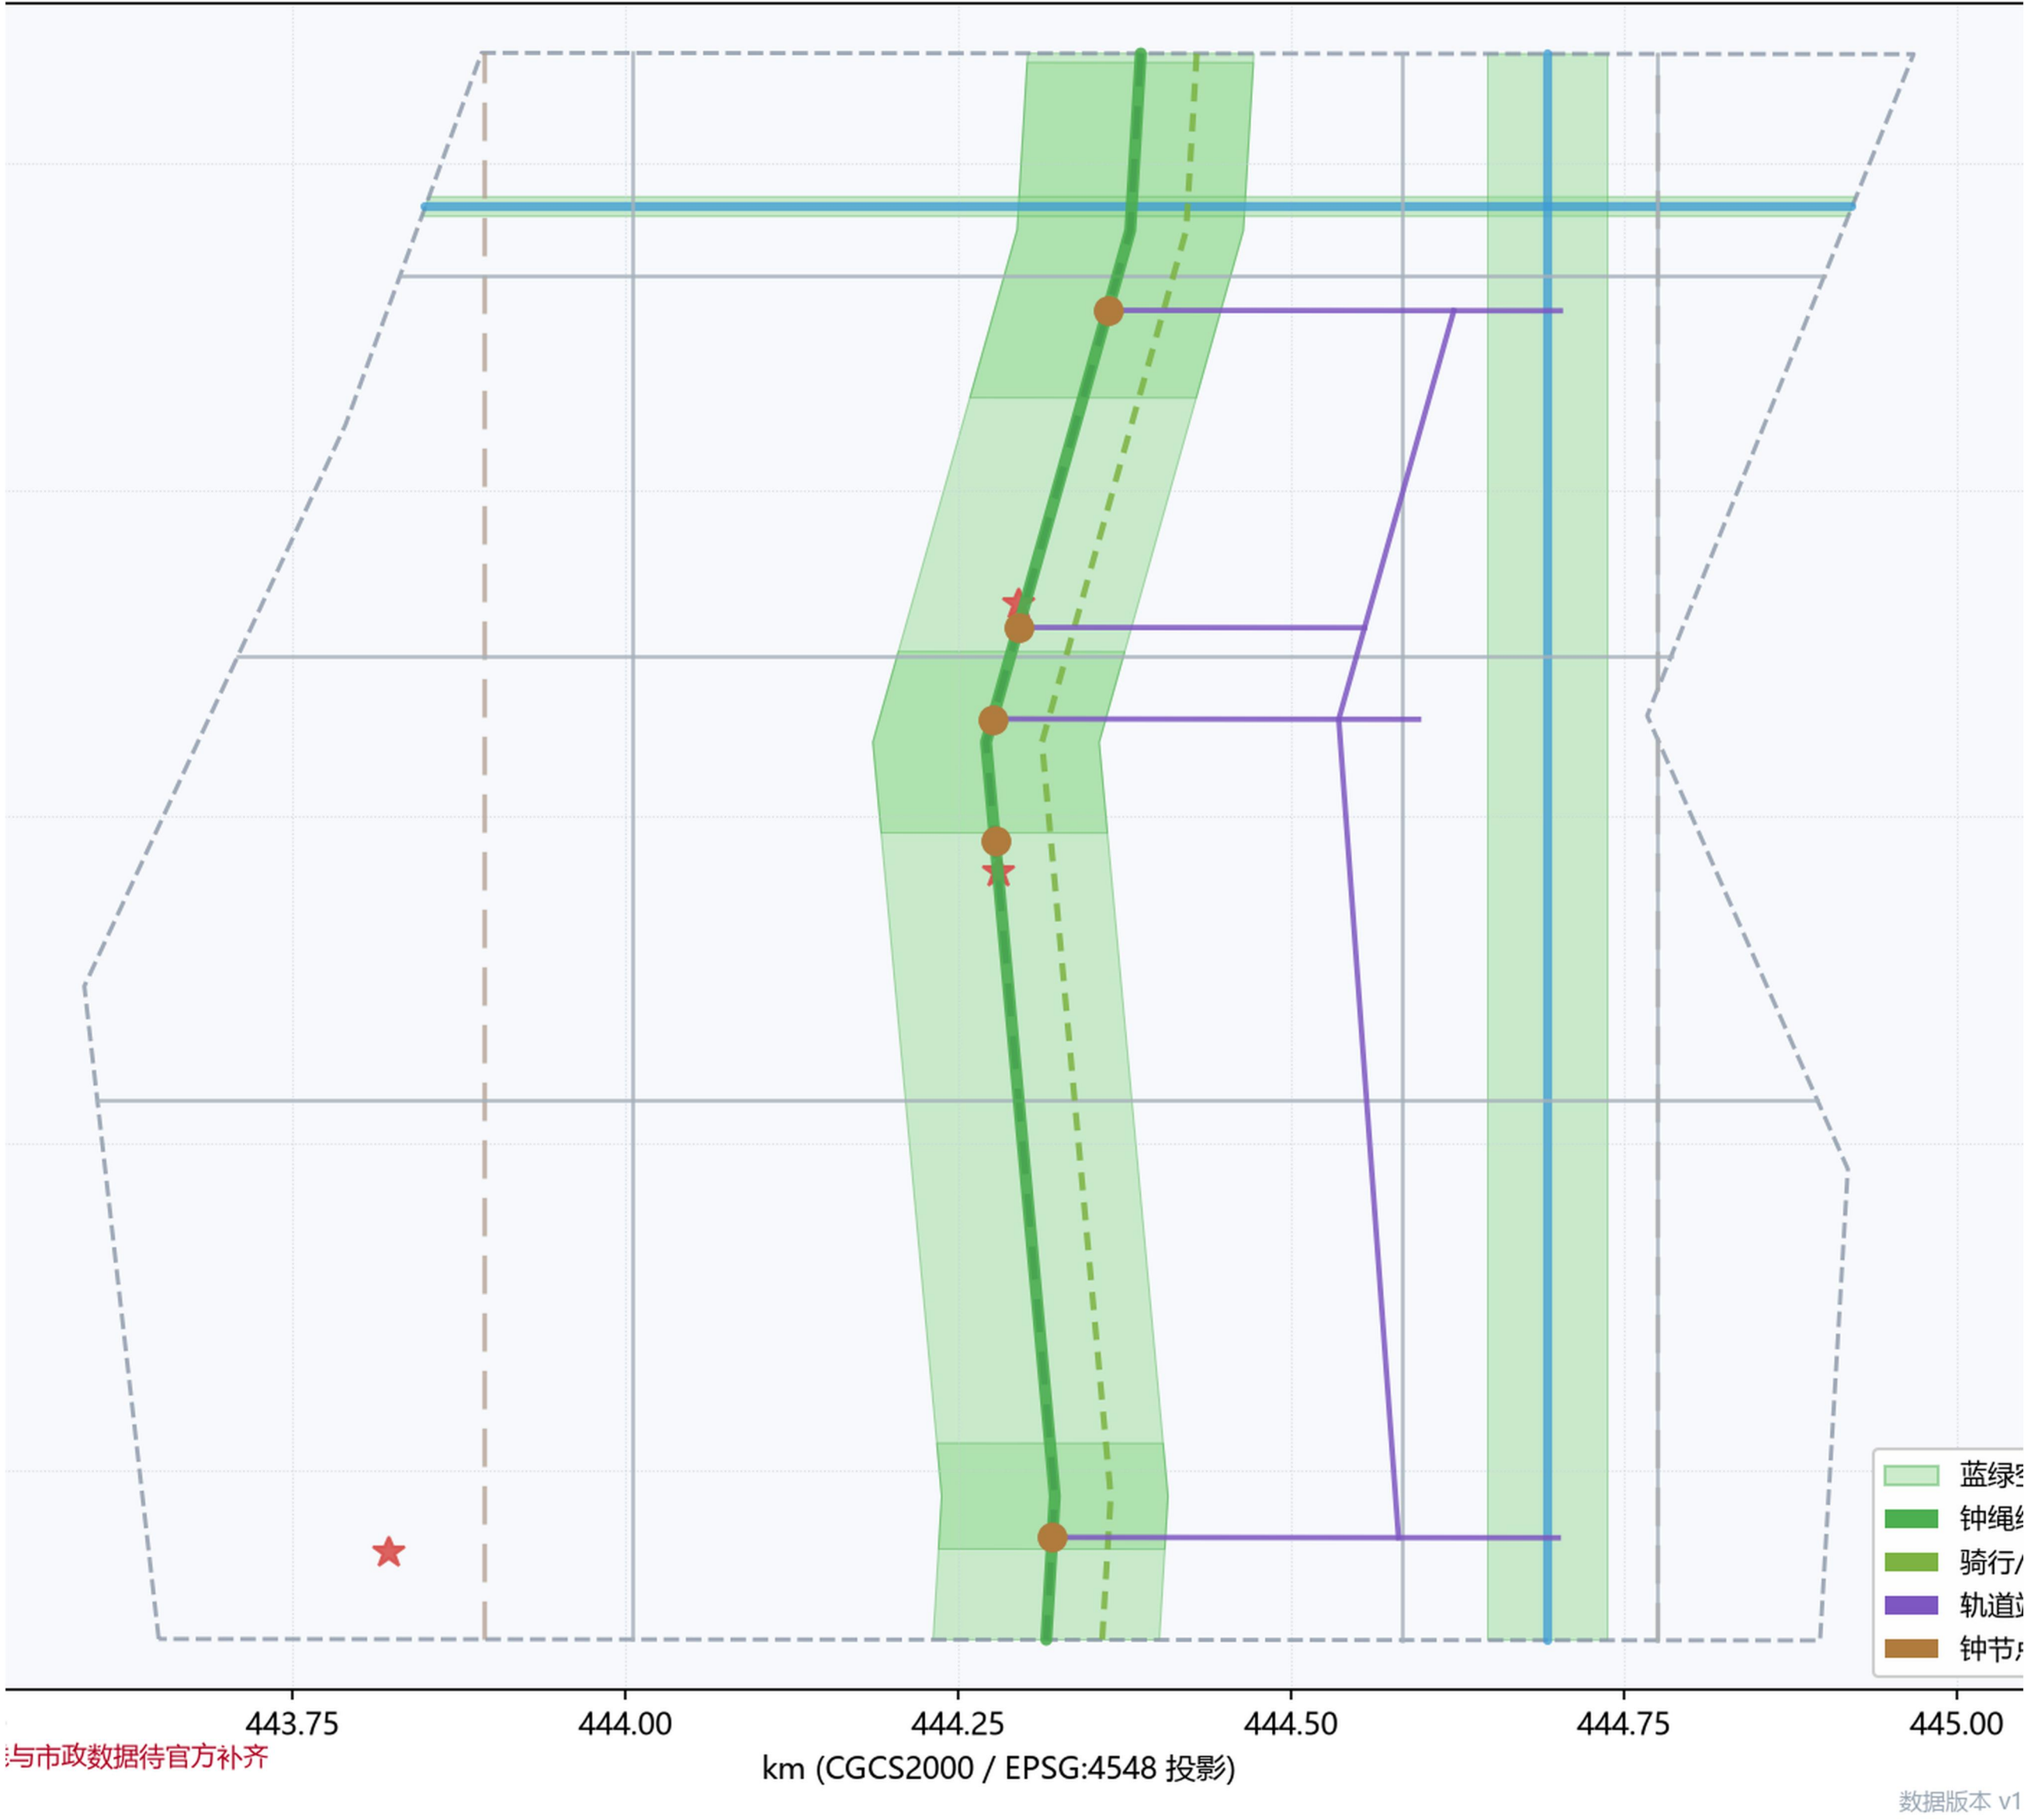

钟绳 = 京张遗址公园活力带的空间转译

南端归钟广场 · 北端启钟台 · 上跨环路节点；绿道/骑行/步行复合断面组织。

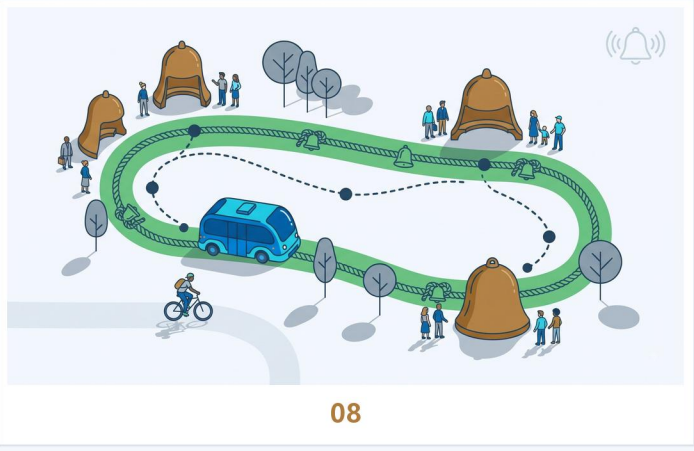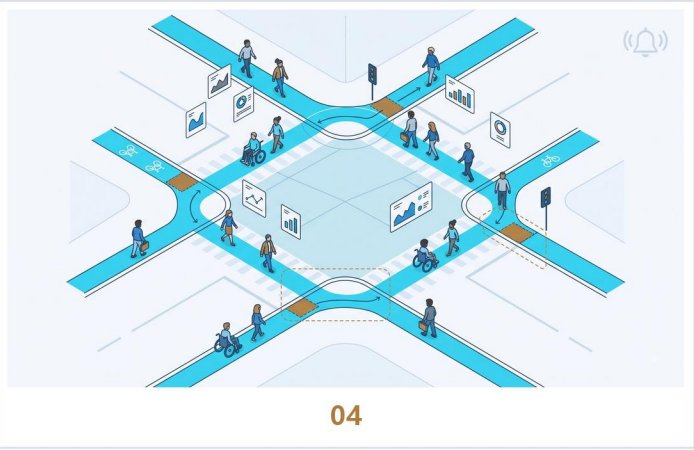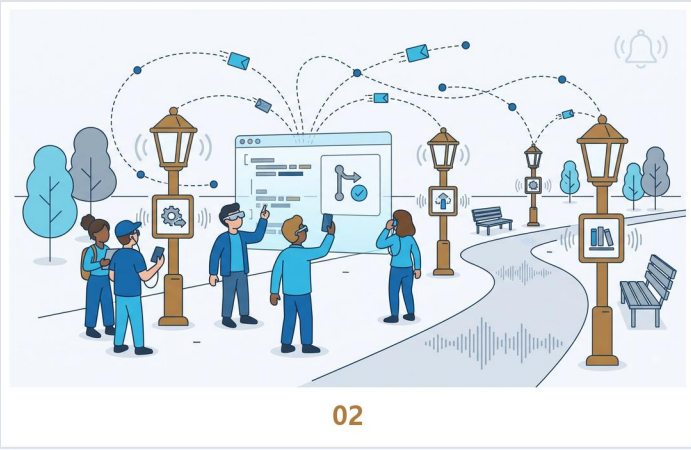


鸣钟登记协议 + 静音时段

重大发布/里程碑编号登记，可验证可追溯；深夜/考试季/纪念日 AI 服务自动降级人工。

三级准入门

试音门（原型）→ 校音门（有界部署）→ 鸣钟门（扩展）；硬门槛失败即降级，不以平均分掩盖。

核心指标复算与证据链 (EPSG:4548)
全部指标可由提交 GeoJSON 复算 · 控规强度待官方数据

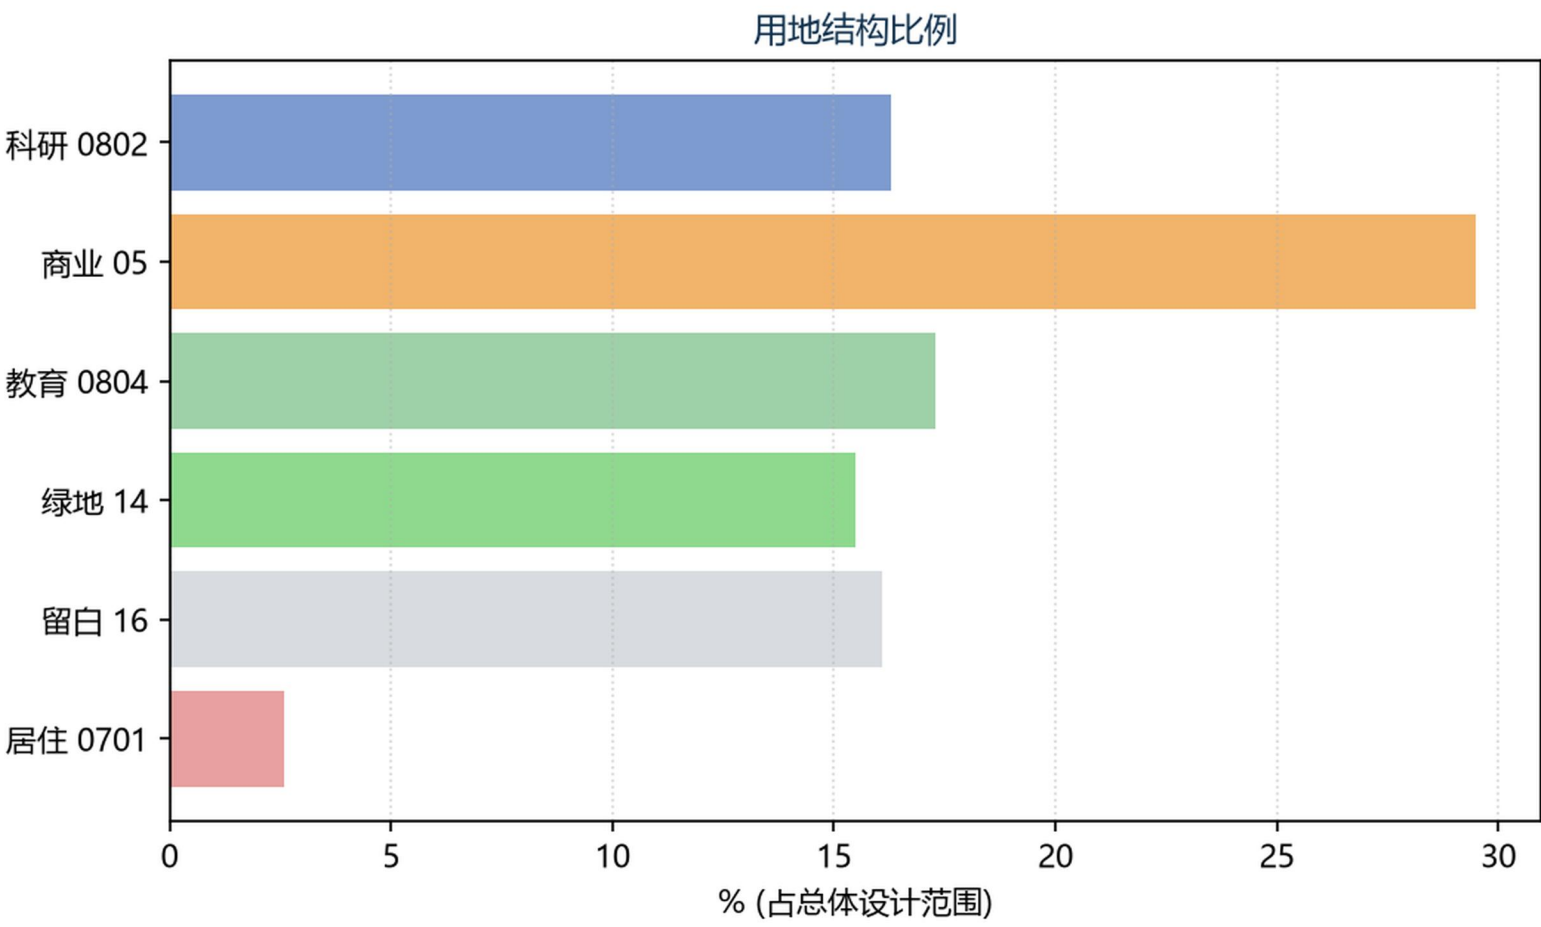

空间与设施指标

	数值
场地面积	11.41 km²
钟绳长度	9.72 km
绿地率	23.00 %
公共空间占比	1.10 %
建筑基底	40.19 万m²
路网总长	60.54 km
钟节点	5 处

临时边界下复算；官方边界发布后整包重算
metrics.json: site_area_sqm, corridor_length_m, green_ratio, public_space_ratio

数据版本 v1.6 · 2026-08-11 · 临时边界复算

指标可复算 • 合规有边界

27 项指标 (23 known / 4 unknown) , EPSG:4548 复算; 场地 11.41 km² · 钟绳 9.7 km · 建筑基底约 40.2 万 m² (概念) ; 负面清单禁止人脸/情绪识别与信用评分。