
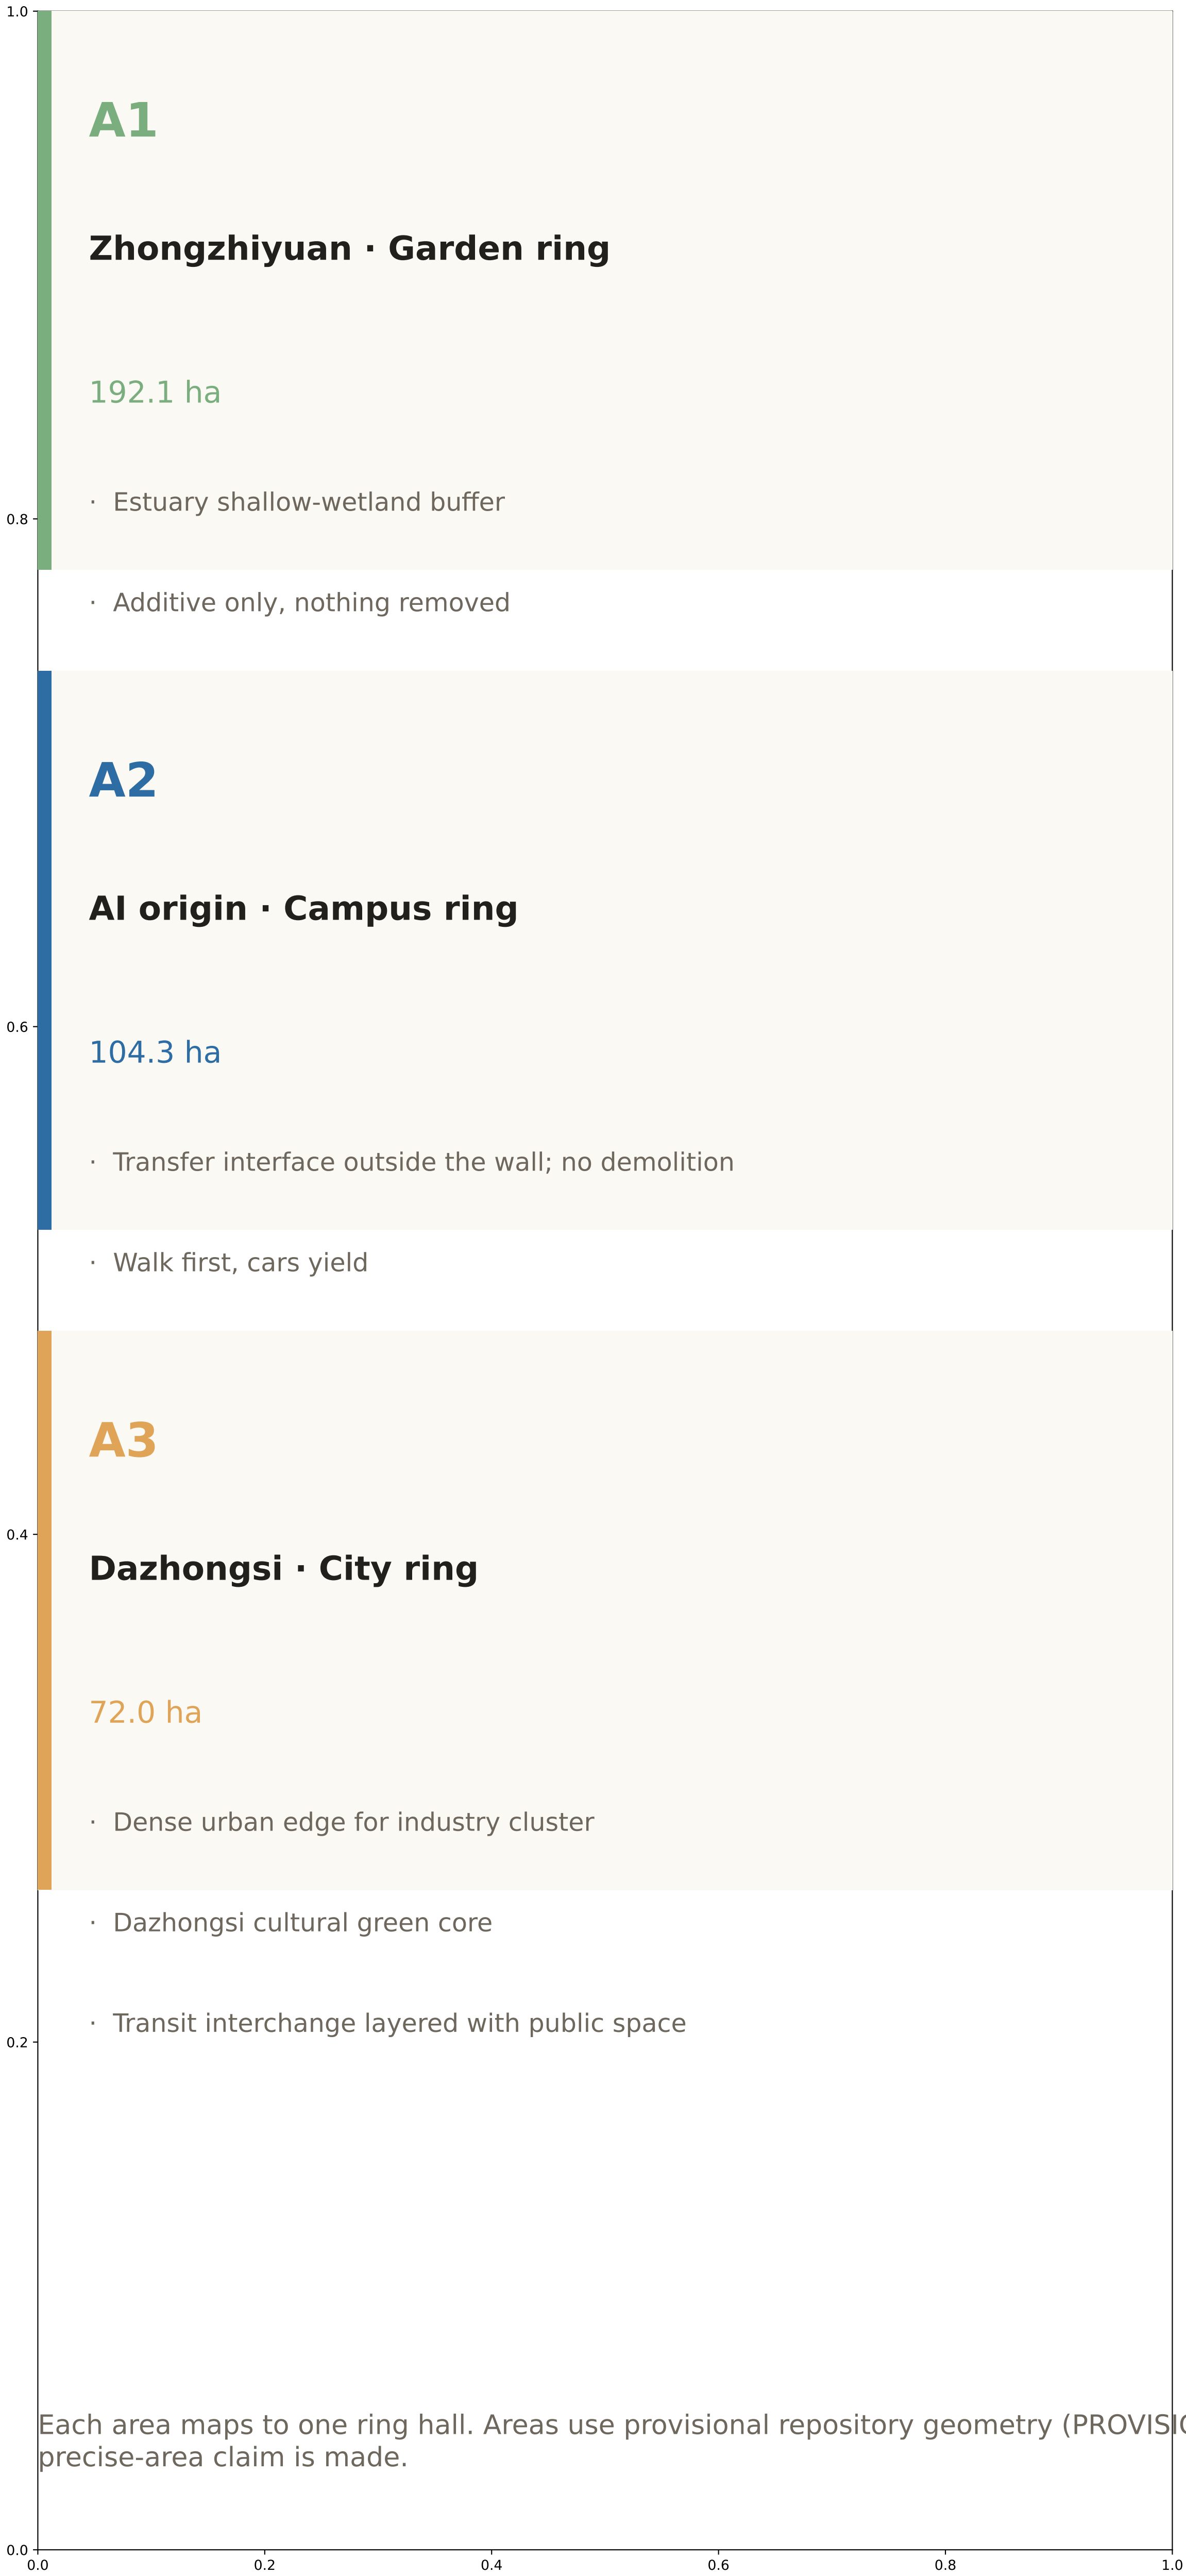
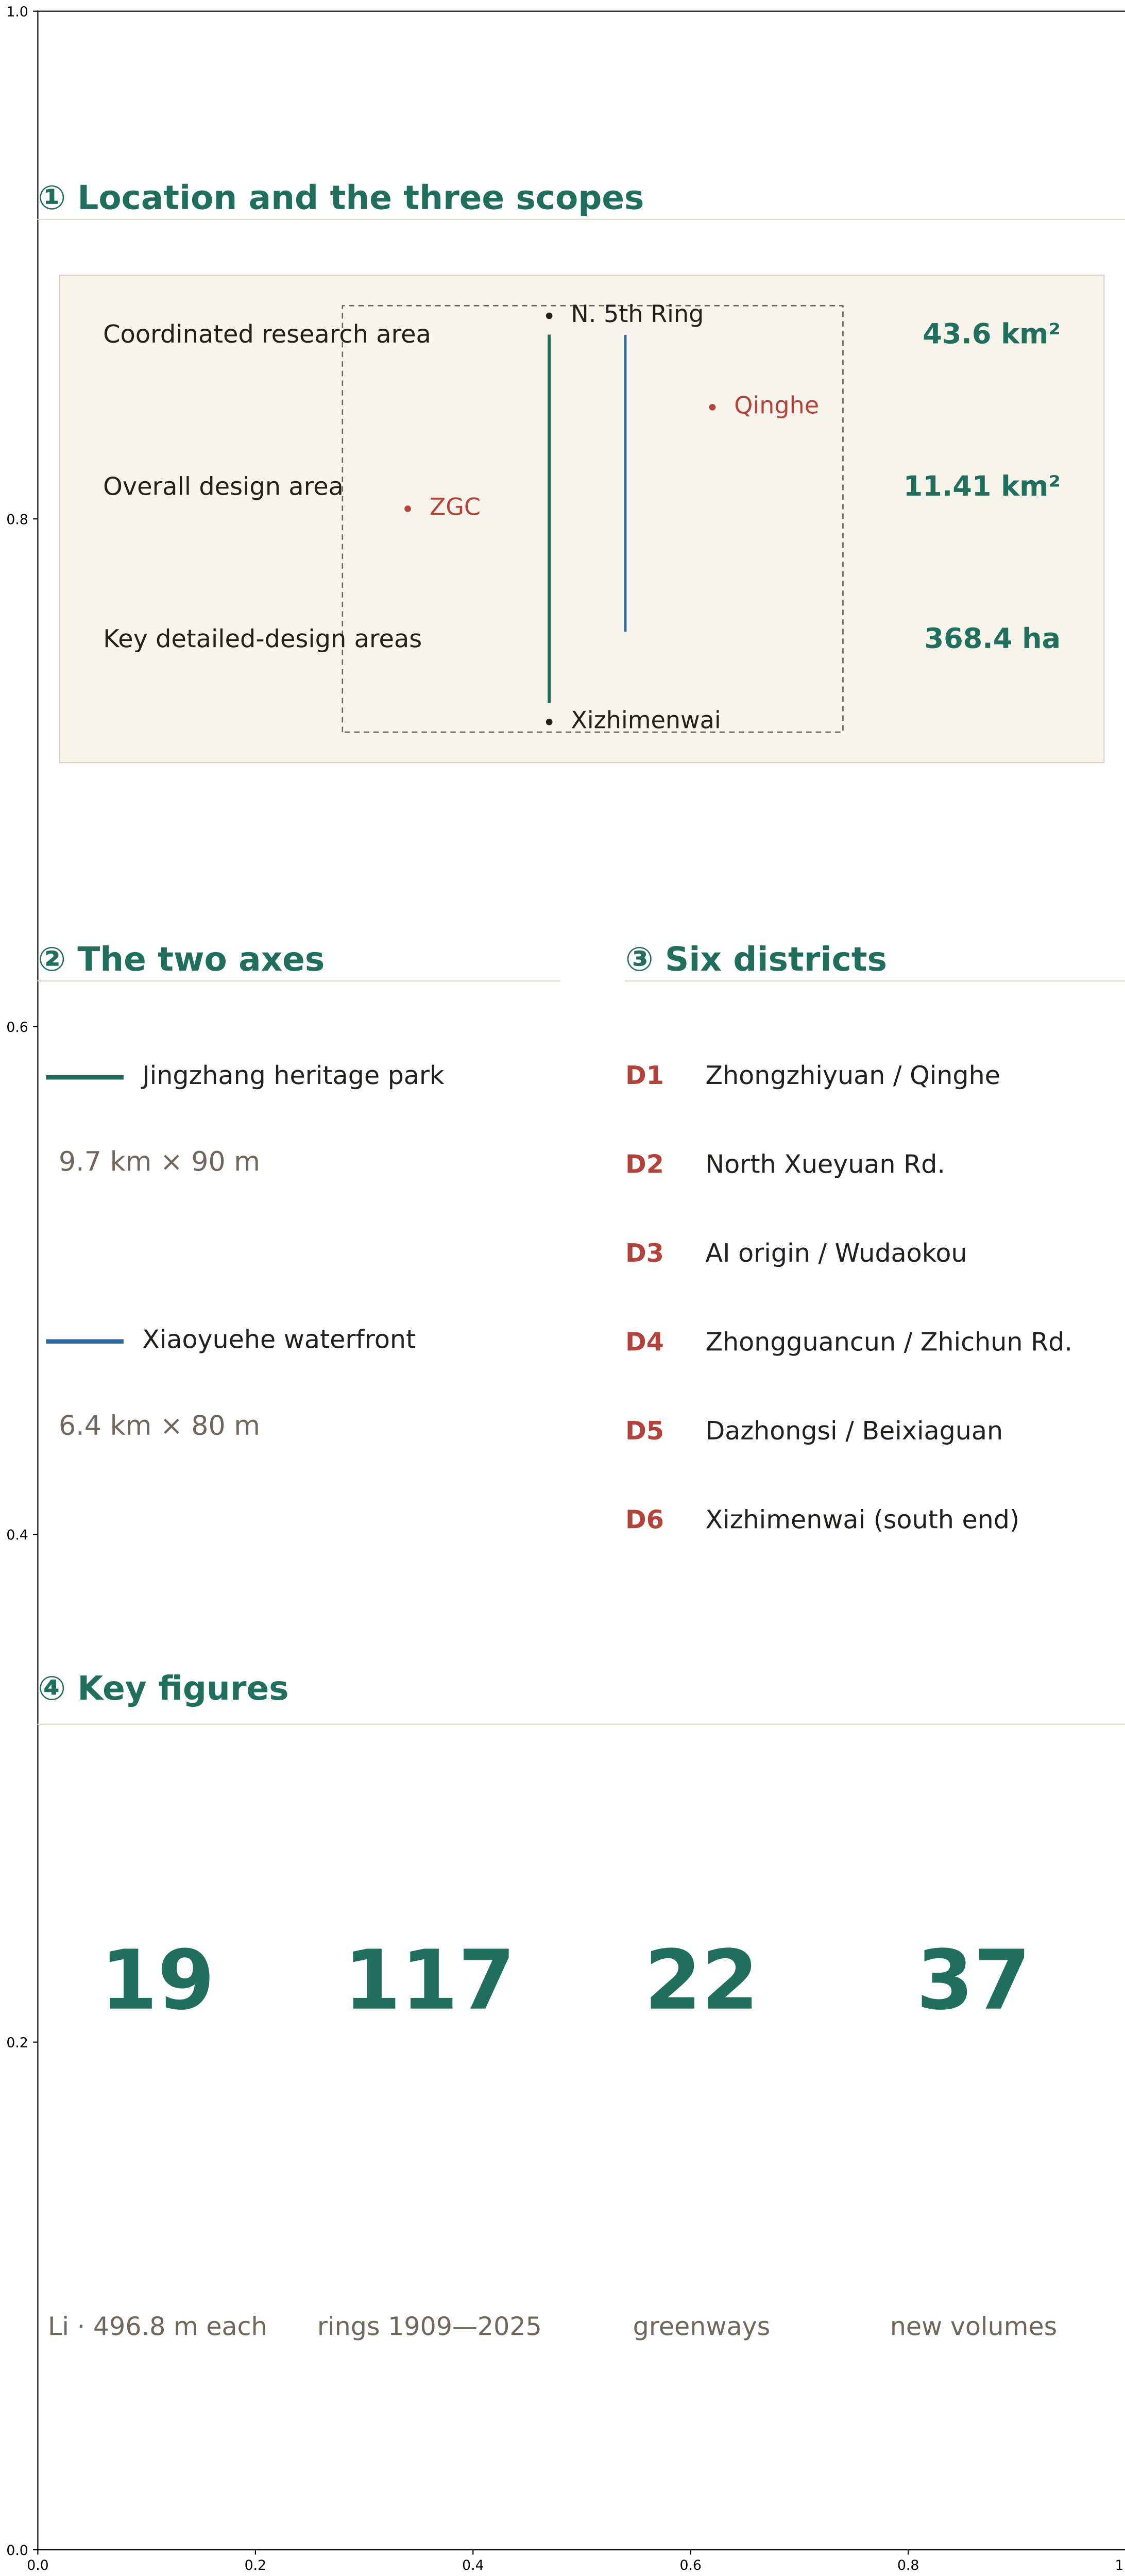


The Jingzhang Rings · Urban Design

A 9.7 km history axis and a 6.4 km ecological axis (6.2 km drawn) frame the Eight Great Colleges and Zhongguancun

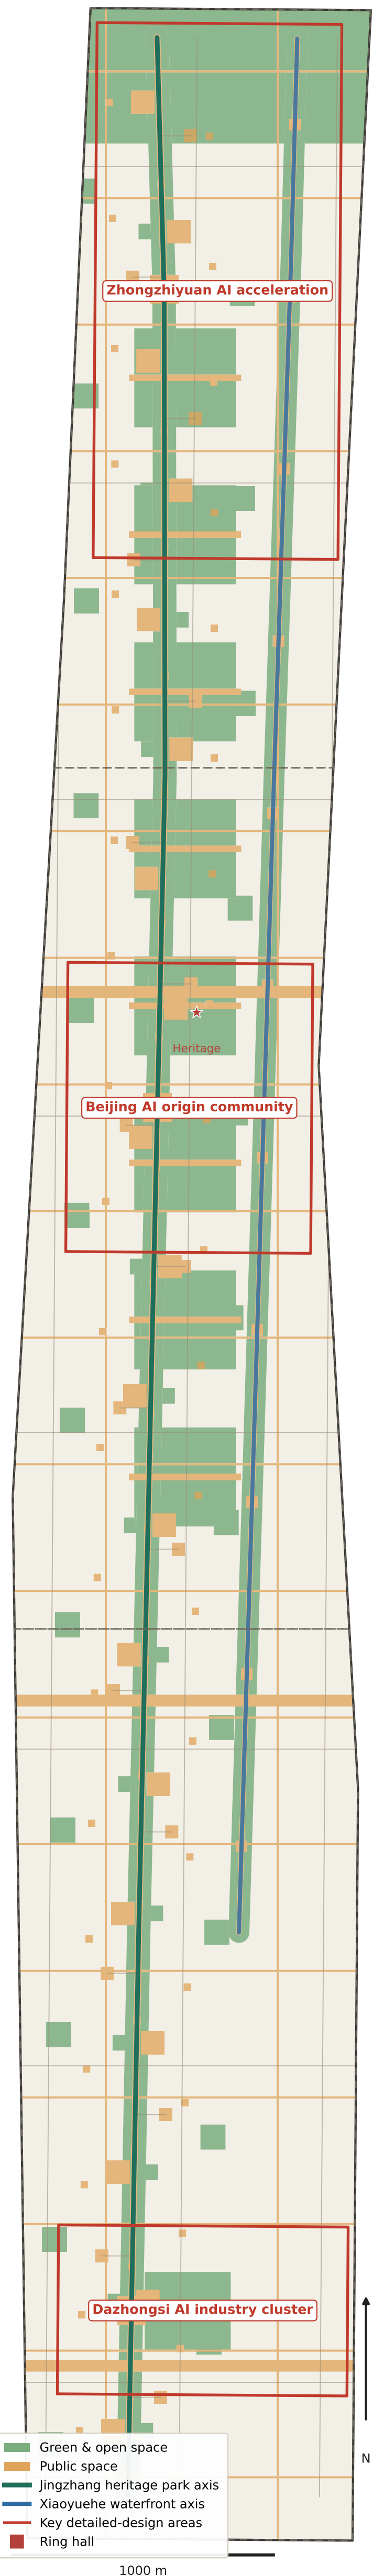

① Slow-traffic network

Greenway length	40.3 km
Greenway count	22
Li plazas	19
Interchange / waterfront	17 / 11
Road centrelines	50

② Heritage clearance

★ Qinghuayuan Station (heritage)

Protection and class-I control zones are low-confidence conservative envelopes. Minimum screening distance from new volumes ≈ 12.2 m. No new volume inside the control zone; no eaves limit. Future work requires heritage-authority approval.



③ Test-road grading



Low-speed delivery and interchange trials allowed Time-boxed, speed-limited, human review required No trials inside secured or campus redlines

The Jingzhang Rings · Land use and metric recomputation

Land use is a strict partition: no gaps, no overlaps, areas recomputable

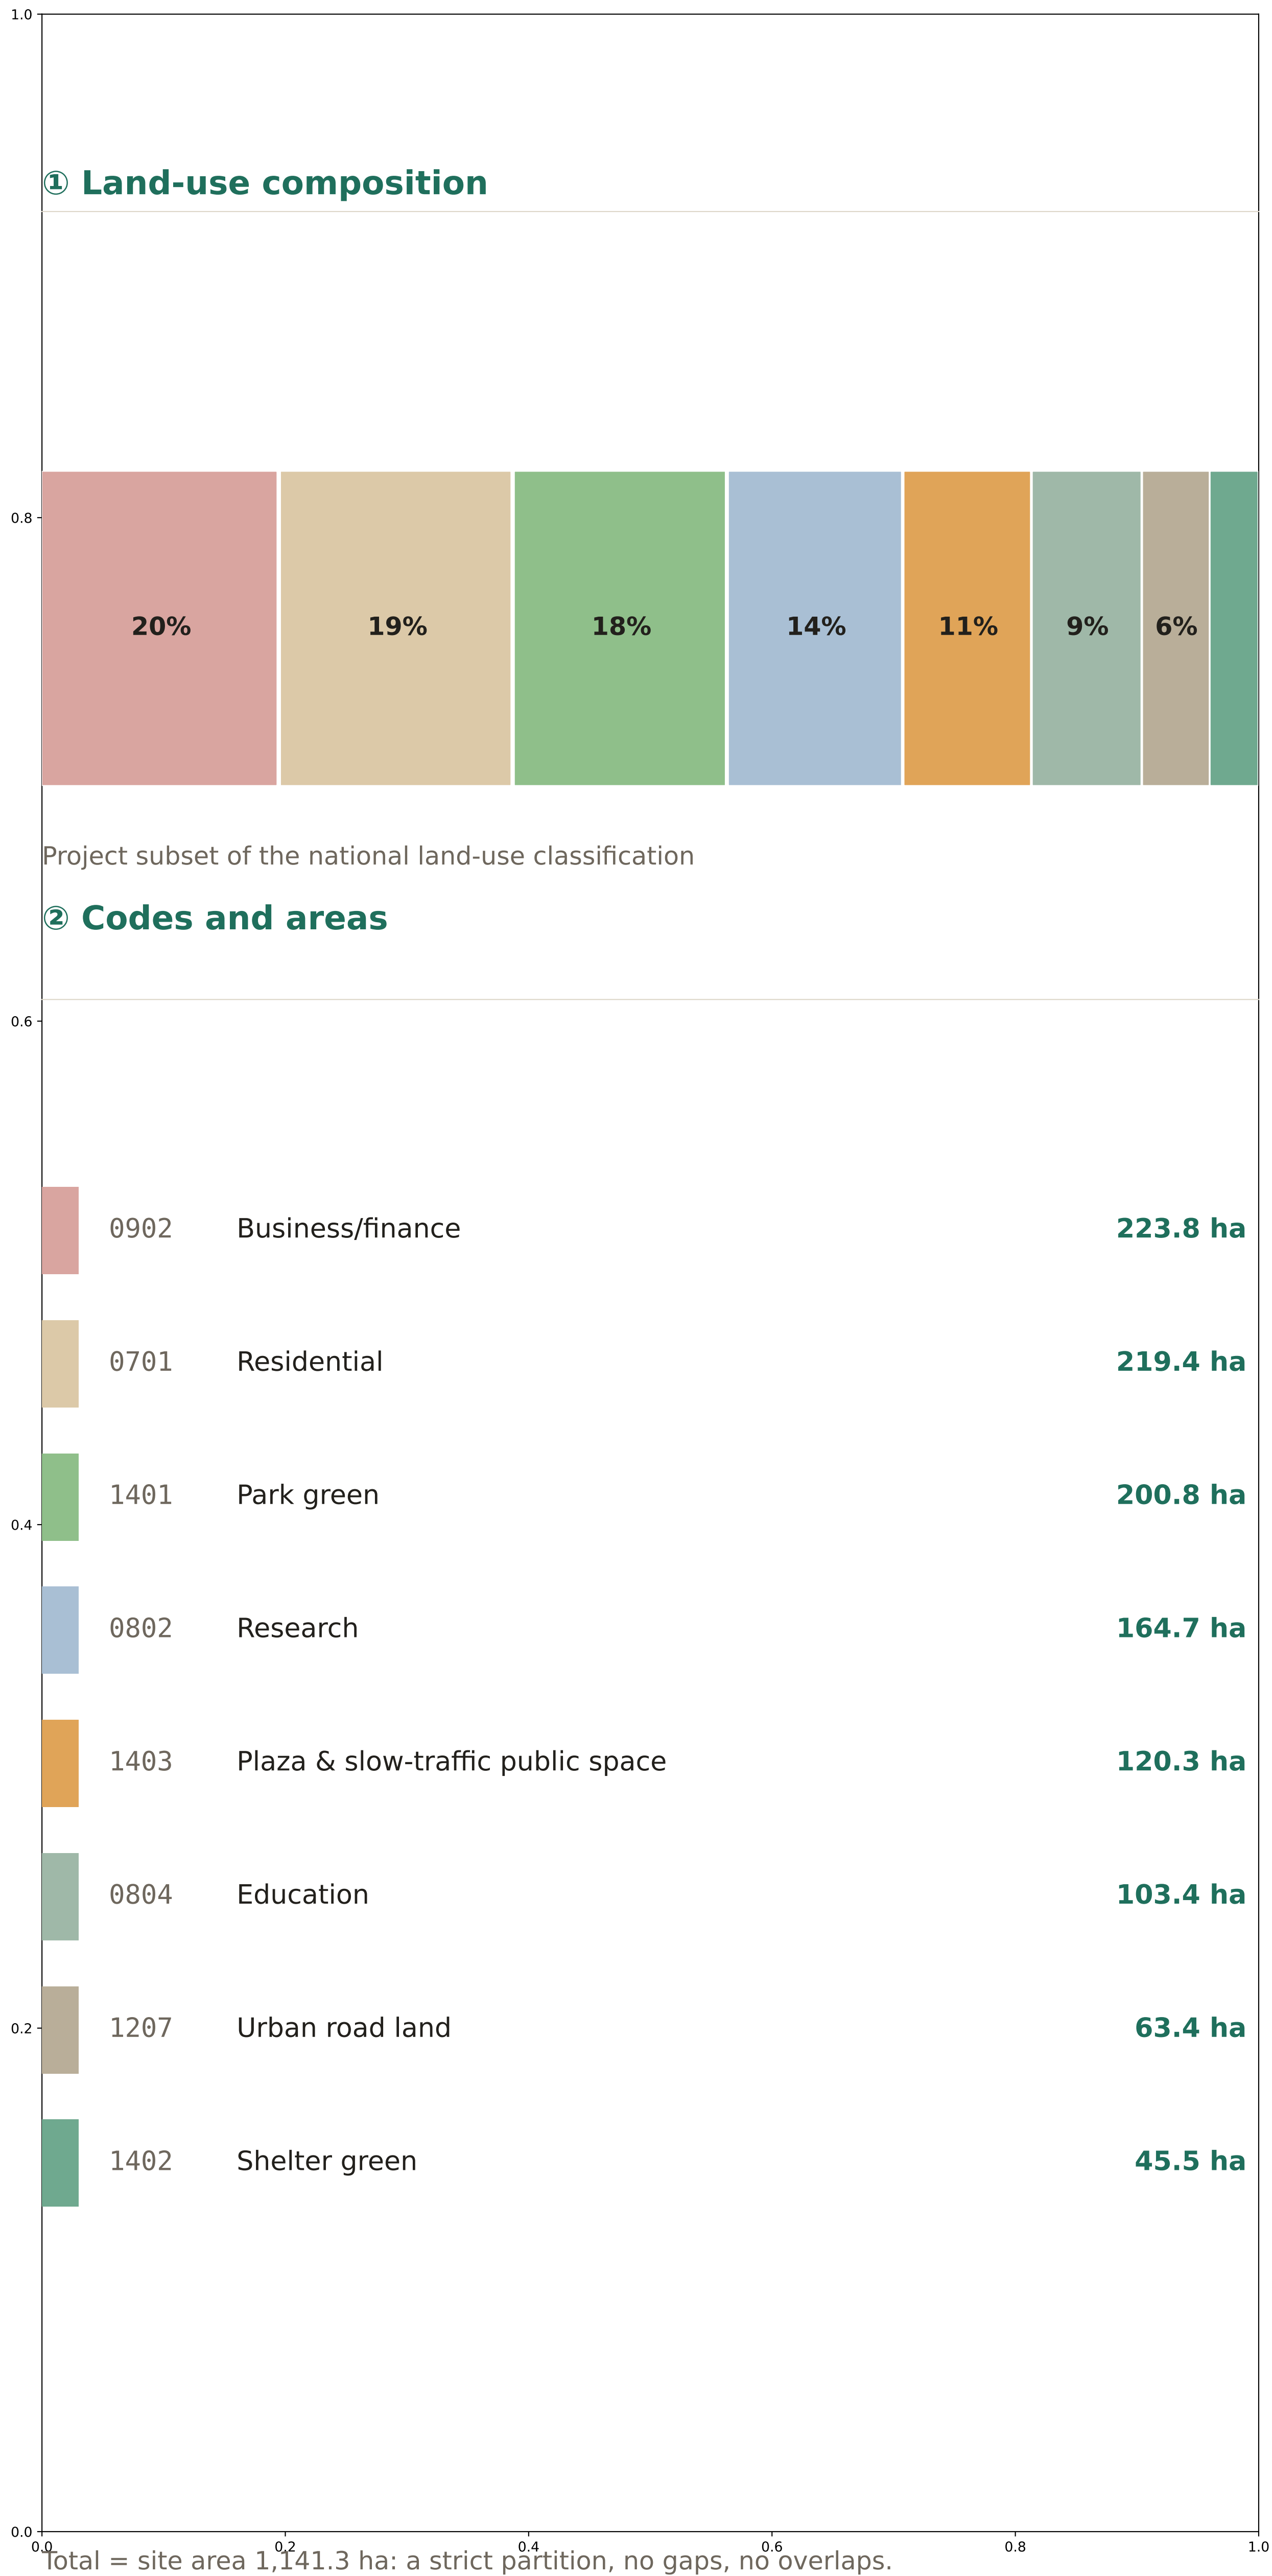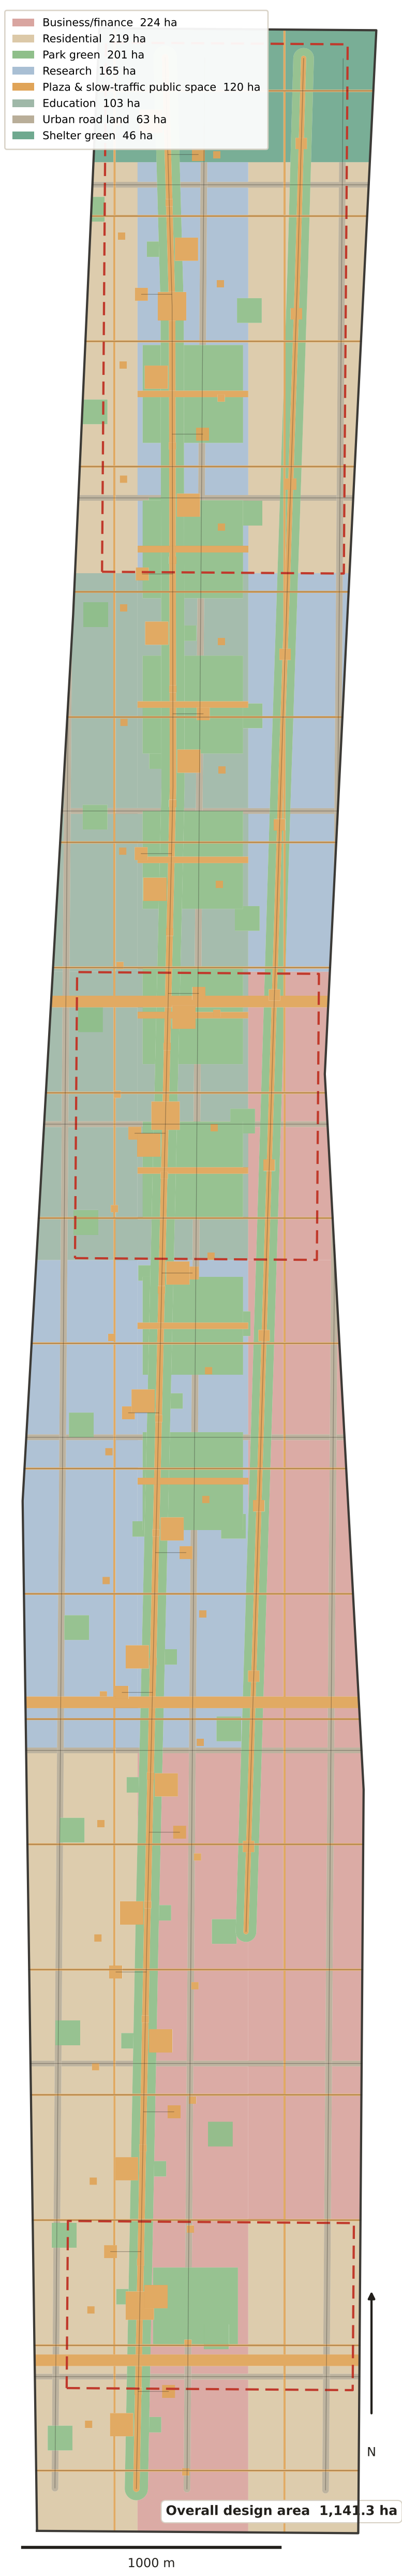


A · Recomputed from submitted geometry

site_area_sqm	11,412,825.386 sqm
PROVISIONAL_REPOSITORY boundary · EPSG:4548	
green_space_area_sqm	2,463,013.830 sqm
union of green_space.geojson	
public_space_area_sqm	1,203,476.584 sqm
union of public_space.geojson	
building_footprint_area_sqm	15,855.006 sqm
37 new conceptual volumes	
green_ratio	0.2158 ratio
green/site, not a statutory figure	
public_space_ratio	0.1054 ratio
public space/site	

C · Unknowns: left blank on purpose

- floor_area_ratio — regulatory controls missing, existing building stock unknown
- Height / density / setback / demolition / investment — conceptual advice only

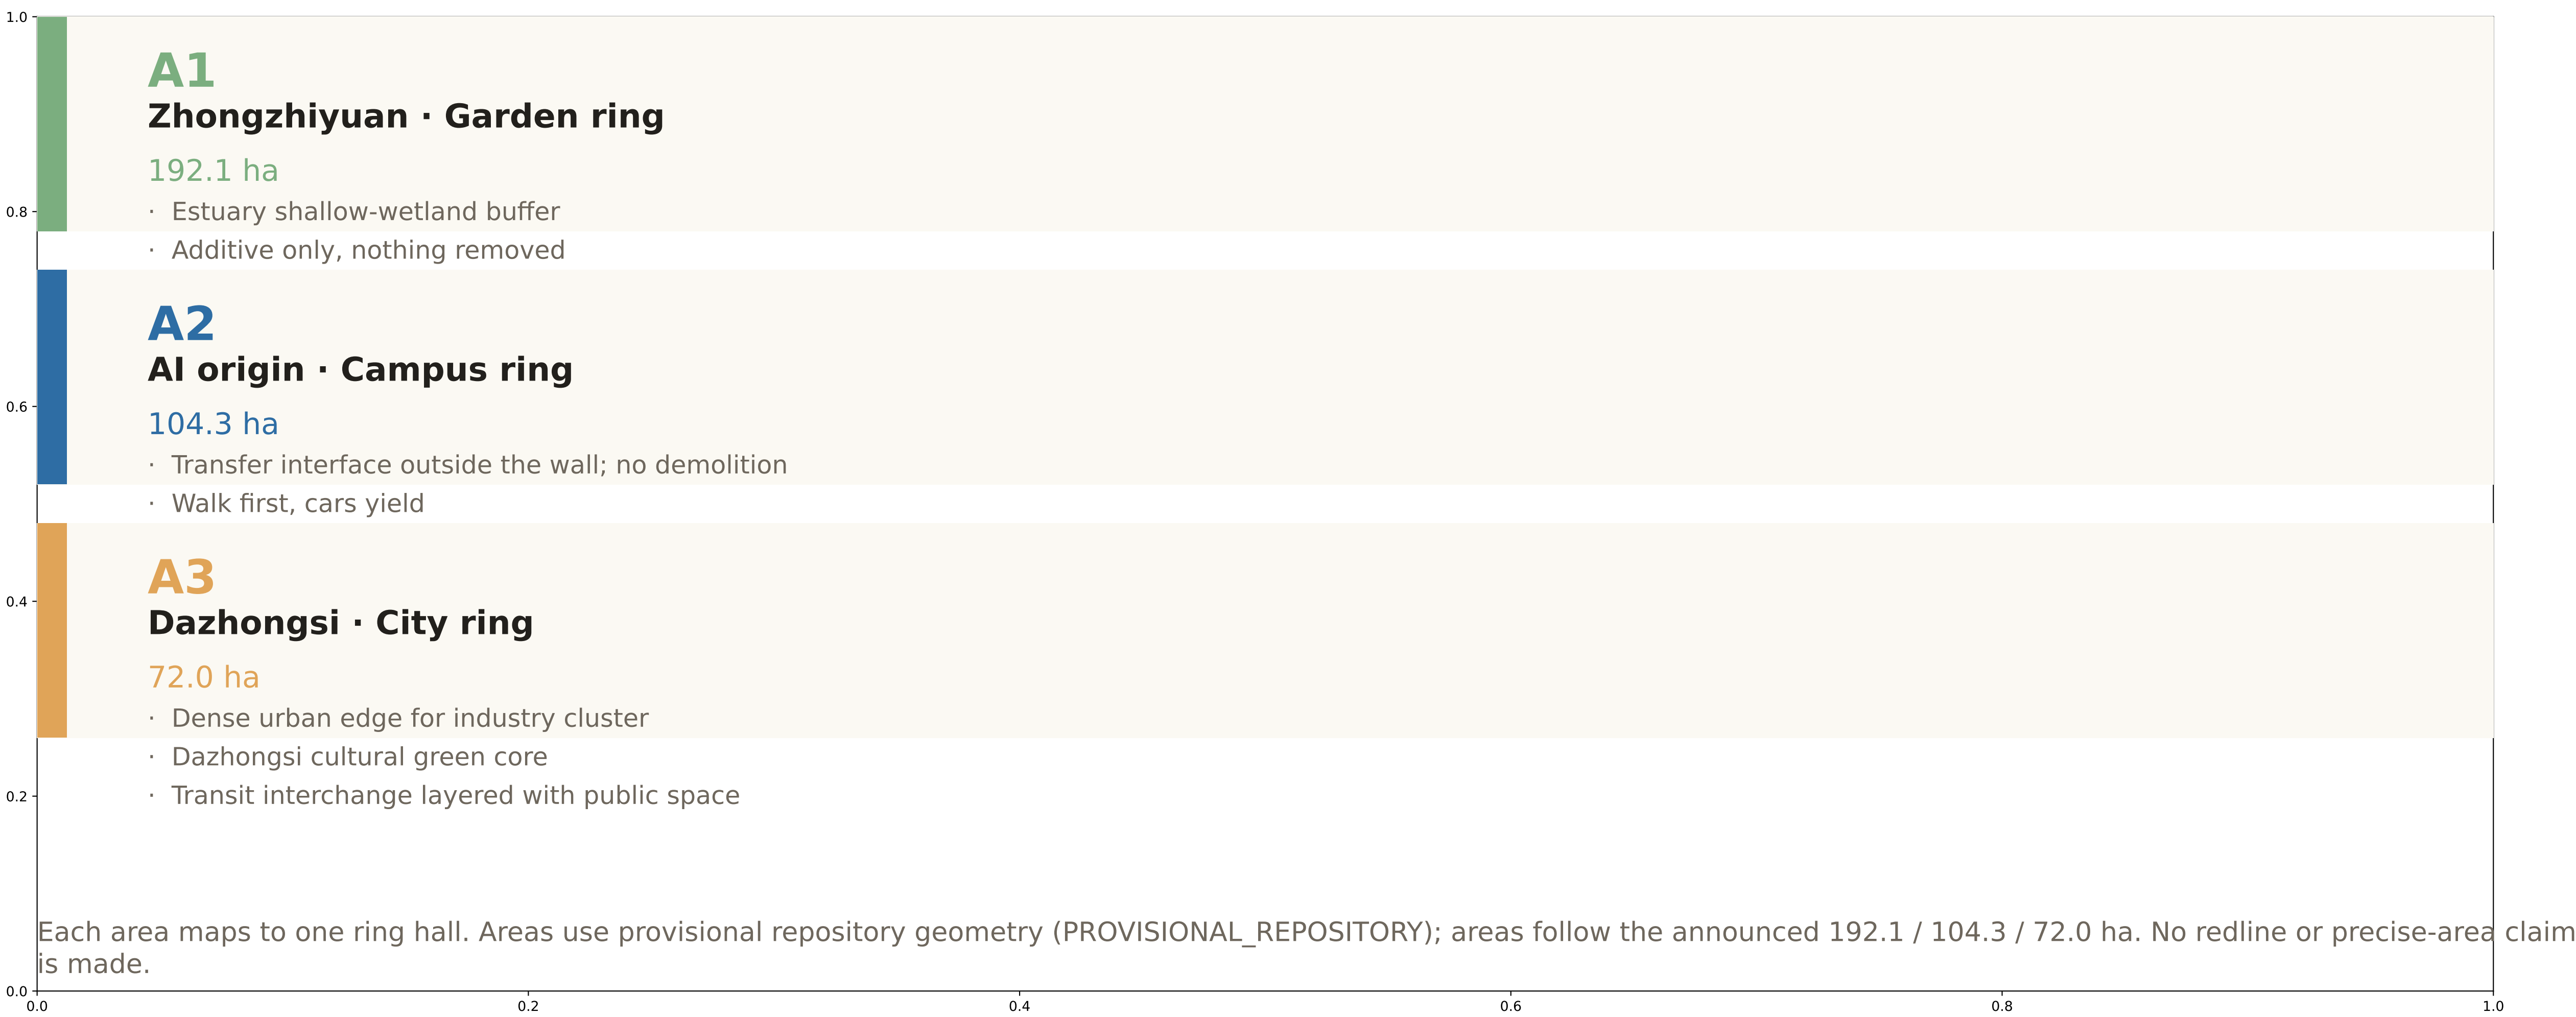

B · Evidence chain: every number traces to a file

geometry/site_boundary.geojson	PROV-SITE-001	PROVISIONAL
geometry/green_space.geojson	49 features	EPSG:4548
geometry/public_space.geojson	145 features	EPSG:4548
geometry/buildings.geojson	37 features	EPSG:4548
geometry/land_use.geojson	223 features	strict partition
metrics.json	status=known	same pipeline

