


京张年轮 · 总体城市设计

9.7 km 技术史轴 + 6.4 km 治理段生态轴（图上绘制 6.2 km），中间夹住八大学院与中关村

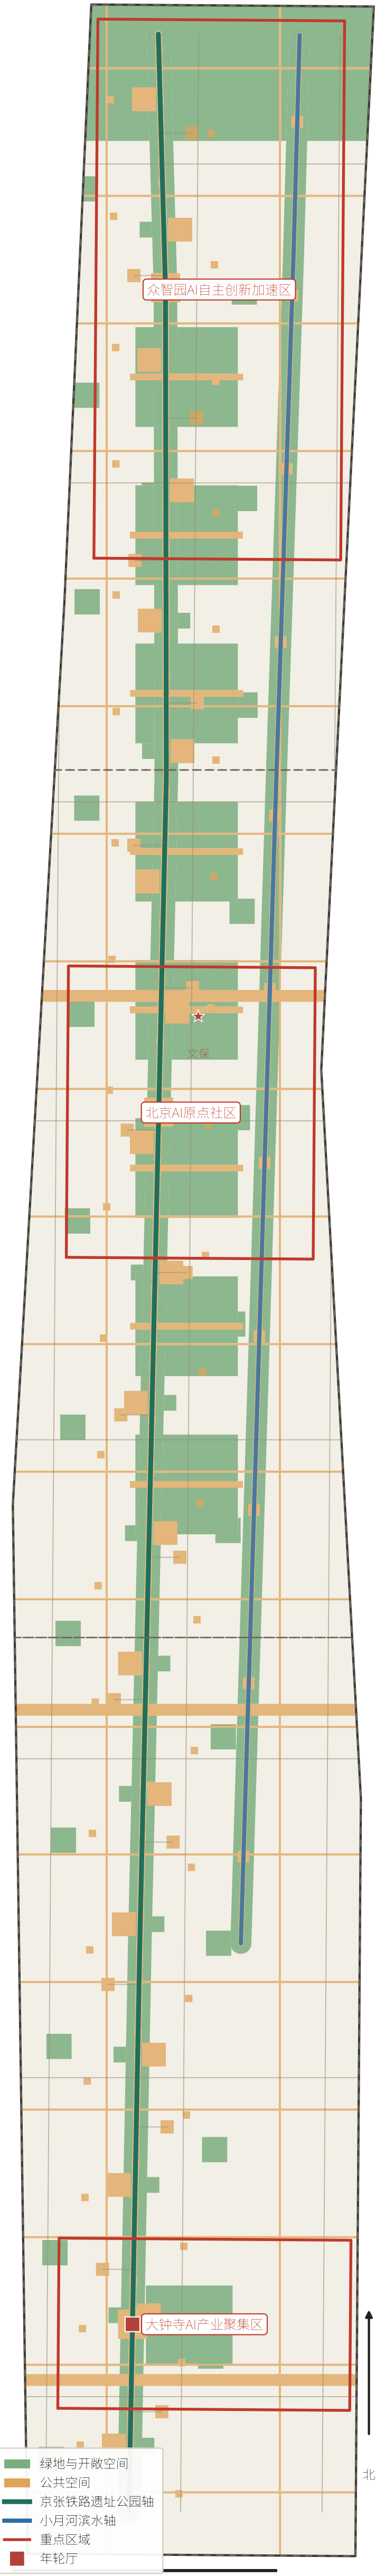

① 慢行网络

绿道总长	40.3 km
绿道条数	22
里院广场	19
接驳 / 滨水驿站	17 / 11
道路中心线	50

② 文保避让

★	清华园车站旧址（文保）
保护范围与Ⅰ类建控地带为低置信保守外包；新增体量与建控地带最小筛查距离 ≈12.2 m。控制地带内不布置新增体量，故不设限高；后续如涉及，以文物主管部门审批为准。	


③ 测试道路分级

开放	限制	禁入
----	----	----

允许低速配送与接驳测试 限时段、限速度、需人工复核 涉密院所、部队、校园红线内不测试

京张年轮 · 用地结构与指标复算

用地为对场地边界的严格剖分：无缝隙、无重叠、面积可复算

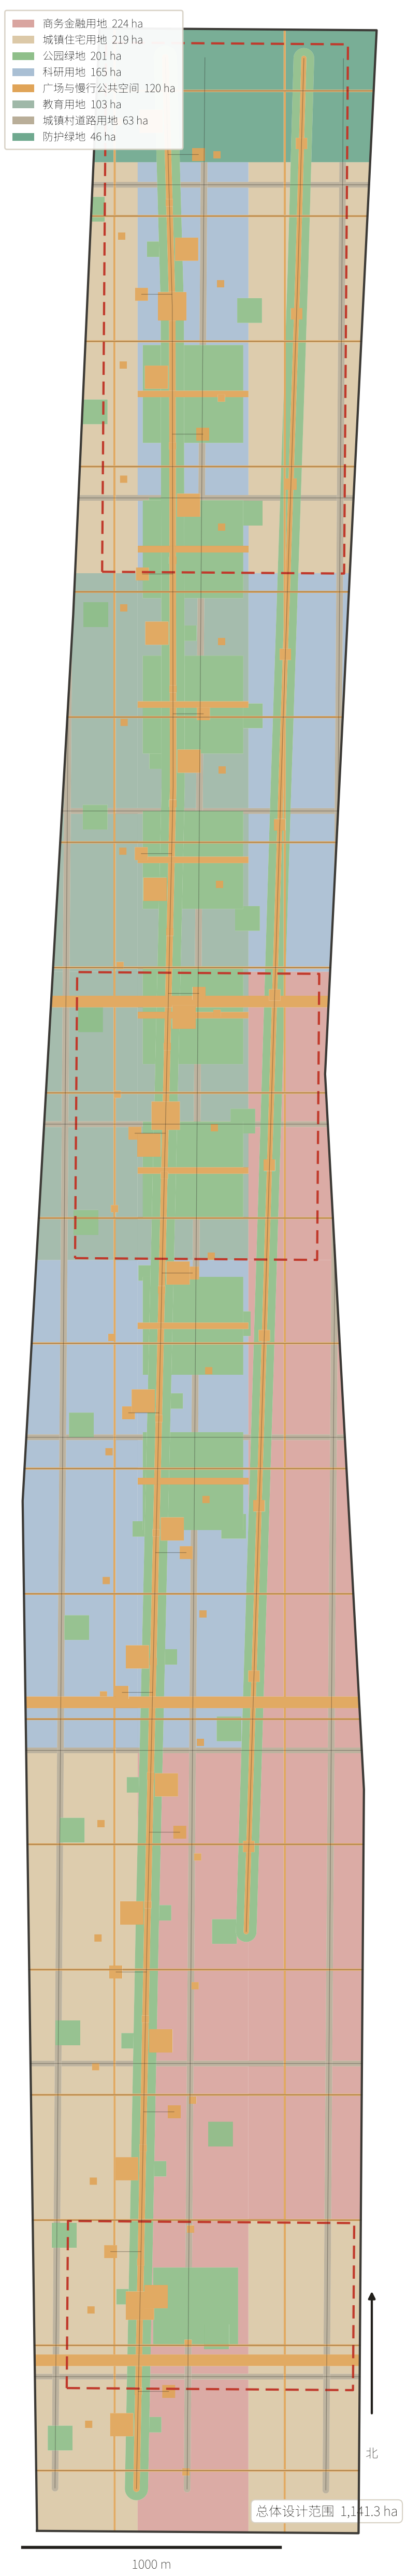

A · 提交几何复算值

site_area_sqm	11,412,825.386 sqm
green_space_area_sqm	2,463,013.830 sqm
public_space_area_sqm	1,203,476.584 sqm
building_footprint_area_sqm	15,855.006 sqm
green_ratio	0.2158 ratio
public_space_ratio	0.1054 ratio

PROVISIONAL_REPOSITORY 边界 · EPSG:4548

green_space.geojson 并集

public_space.geojson 并集

37 处新增概念体量

green_ratio

0.2158 ratio

绿地/场地，非法定指标

public_space_ratio

0.1054 ratio

公共空间/场地

C · 未知项：如实留白，不编造

- floor_area_ratio — 控规缺失，现状建筑底数缺失
- 建筑高度 / 密度 / 退线 / 拆改留 / 投资测算 — 一律概念建议



B · 证据链：每个数字都能追到文件

geometry/site_boundary.geojson	PROV-SITE-001	临时粗略几何
geometry/green_space.geojson	49 features	EPSG:4548
geometry/public_space.geojson	145 features	EPSG:4548
geometry/buildings.geojson	37 features	EPSG:4548
geometry/land_use.geojson	223 features	严格剖分
metrics.json	status=known	同管线复算

