


京张共智带 · 01 总体概念

一带三核两轴多节点 | 11.41 km² | 294 街坊 | 主脊 9.72 km

京张共智带 · 一带三核两轴多节点

总体设计范围 11.41 km² | 294 街坊 | 绿地率 27.6% | 公共空间 35.3% | 三处重点区 192.9 + 104.3 + 72.0 ha

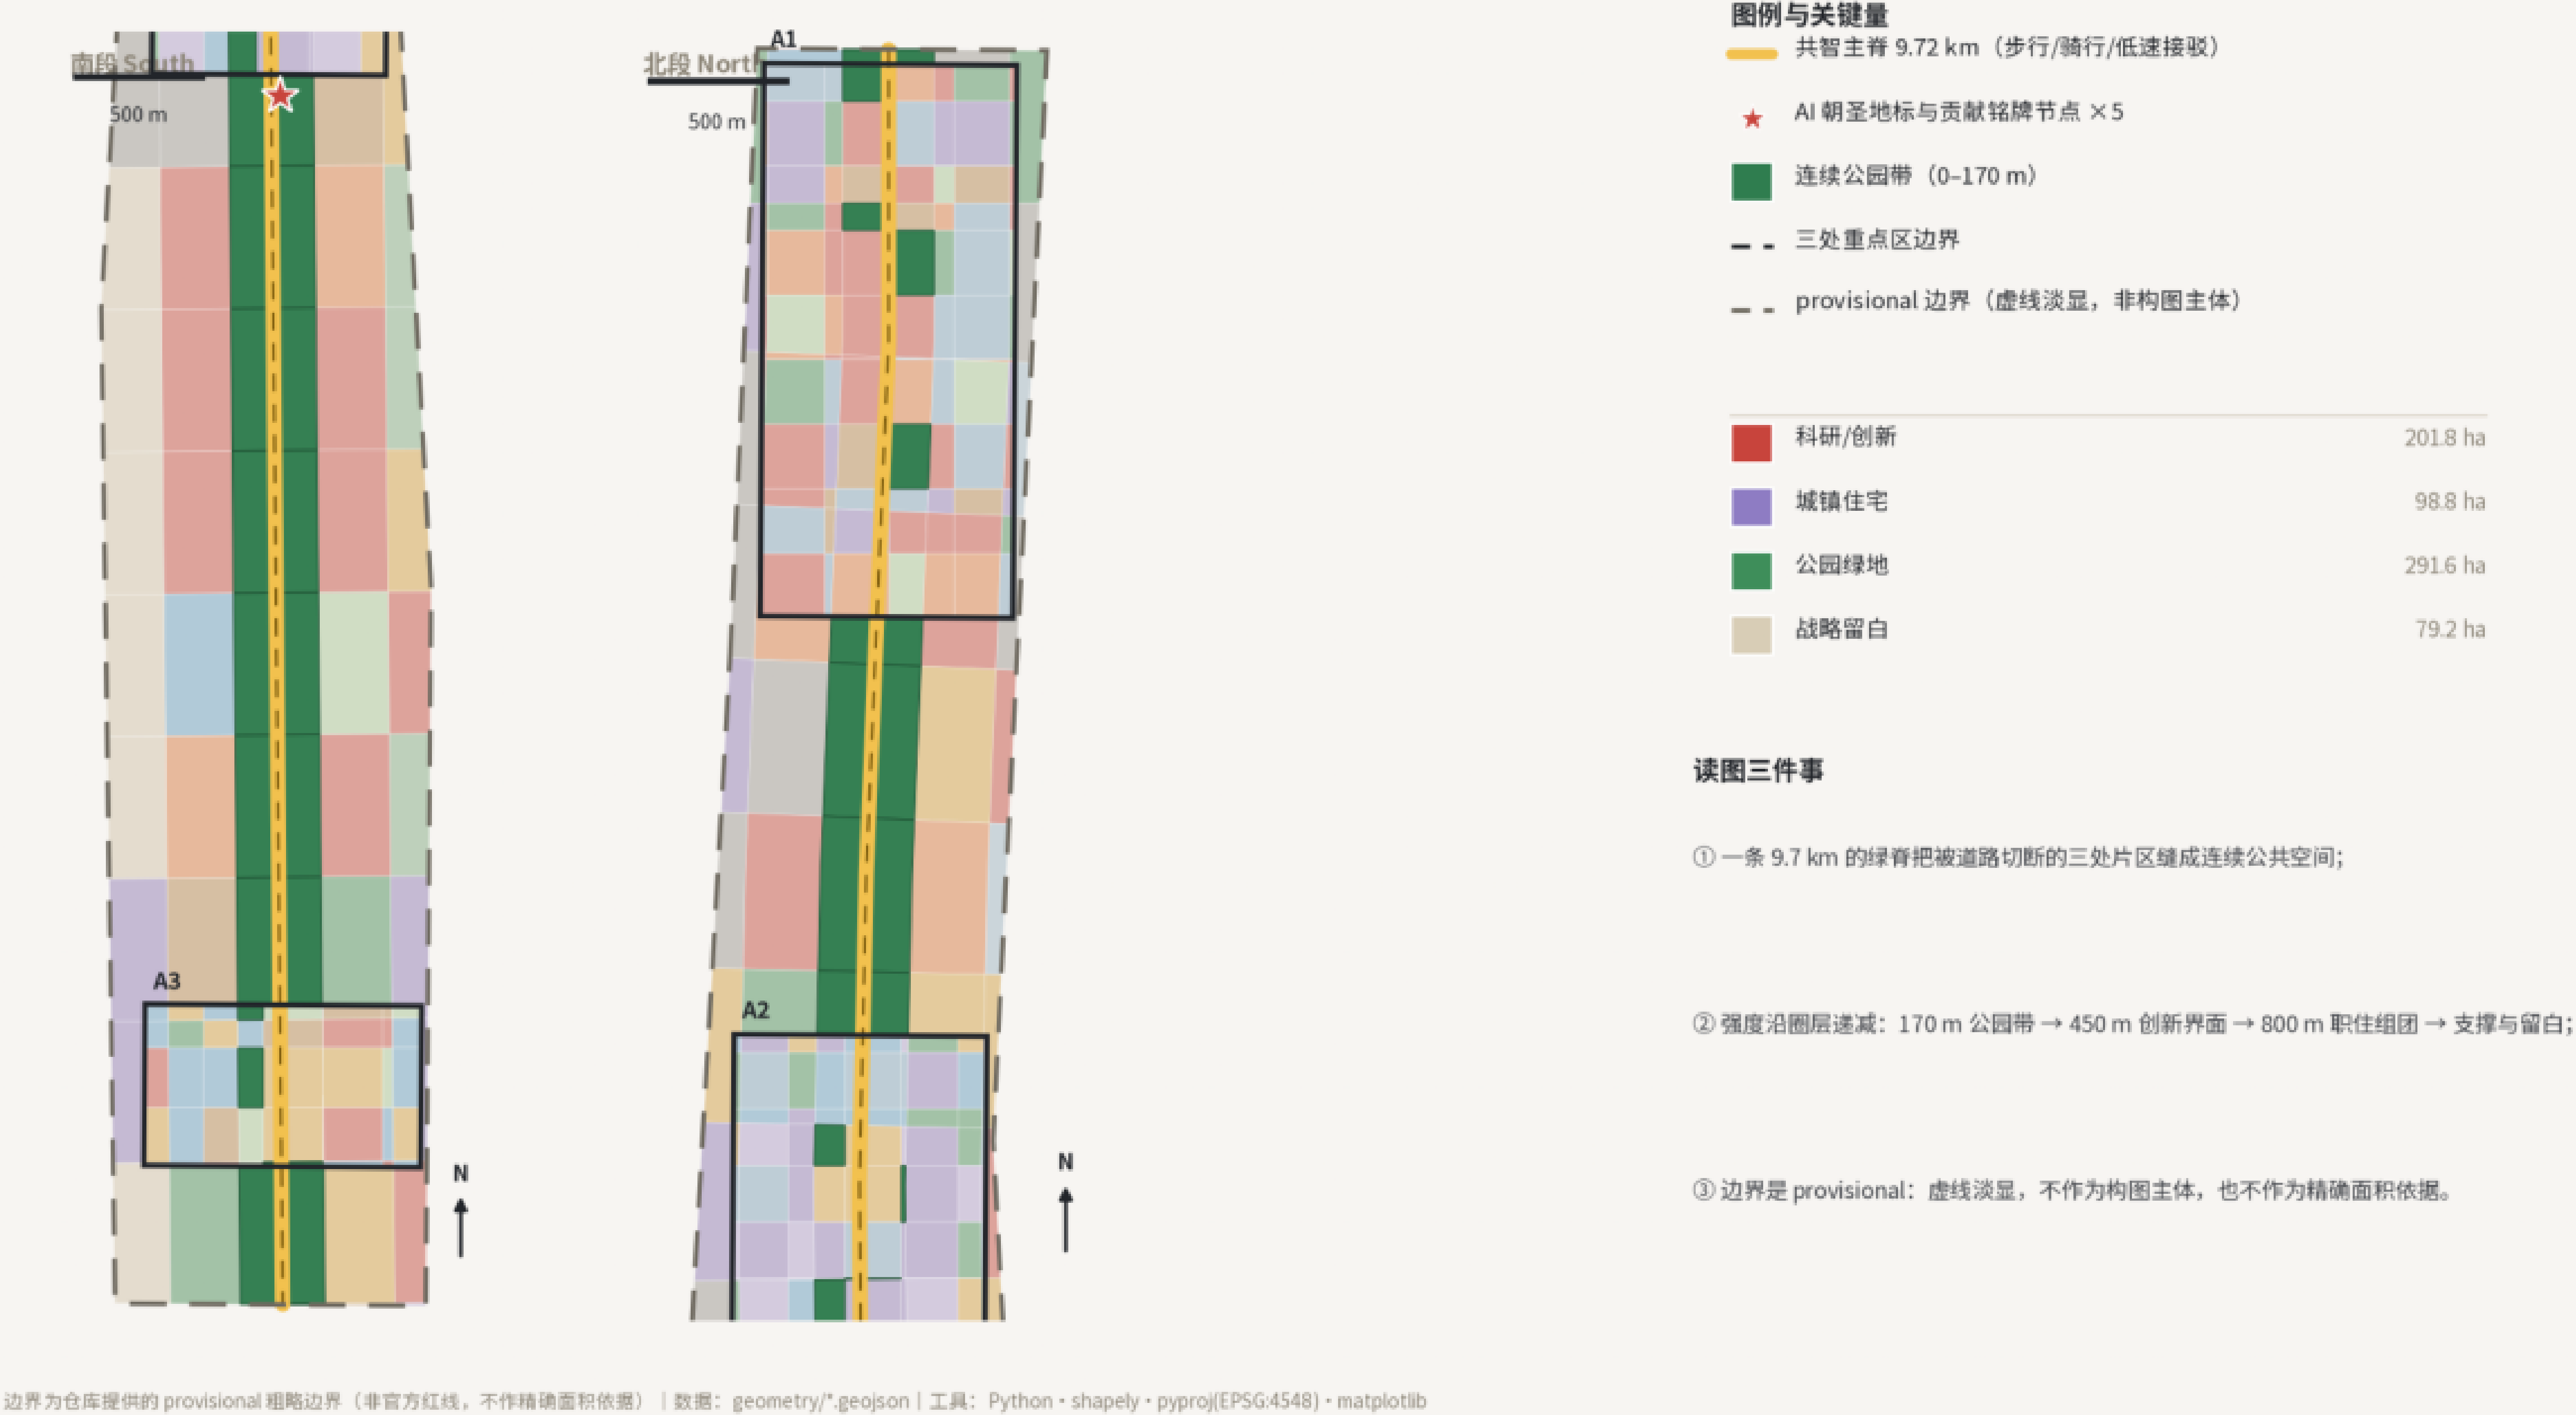

结构主张

一带: 遗址公园共智主脊全线贯通为步行优先公共空间

三核: 众智园发动机 · 原点社区第一公里 · 大钟寺公共客厅

两轴: 北四环—学清路创新服务轴 · 清河—西直门城市功能轴

多节点: 5 处朝圣地标与贡献铭牌节点

边界声明

总体设计边界为 provisional rough, 非官方红线

三处重点区为 provisional polygon, 面积不得作精确依据


图面以虚线淡显临时边界, 重点落在设计意图

官方 polygon 发布后触发全链复算与重绘

用地结构与圈层传导

创新+绿廊双主体，拒绝昼夜空城 | 294街坊无缝隙不重叠（复算缺口0m²）

圈层：0-170 m 公园带 → 170-450 m 创新界面 → 450-800 m 职住组团 → 800 m 以外支撑与战略留白

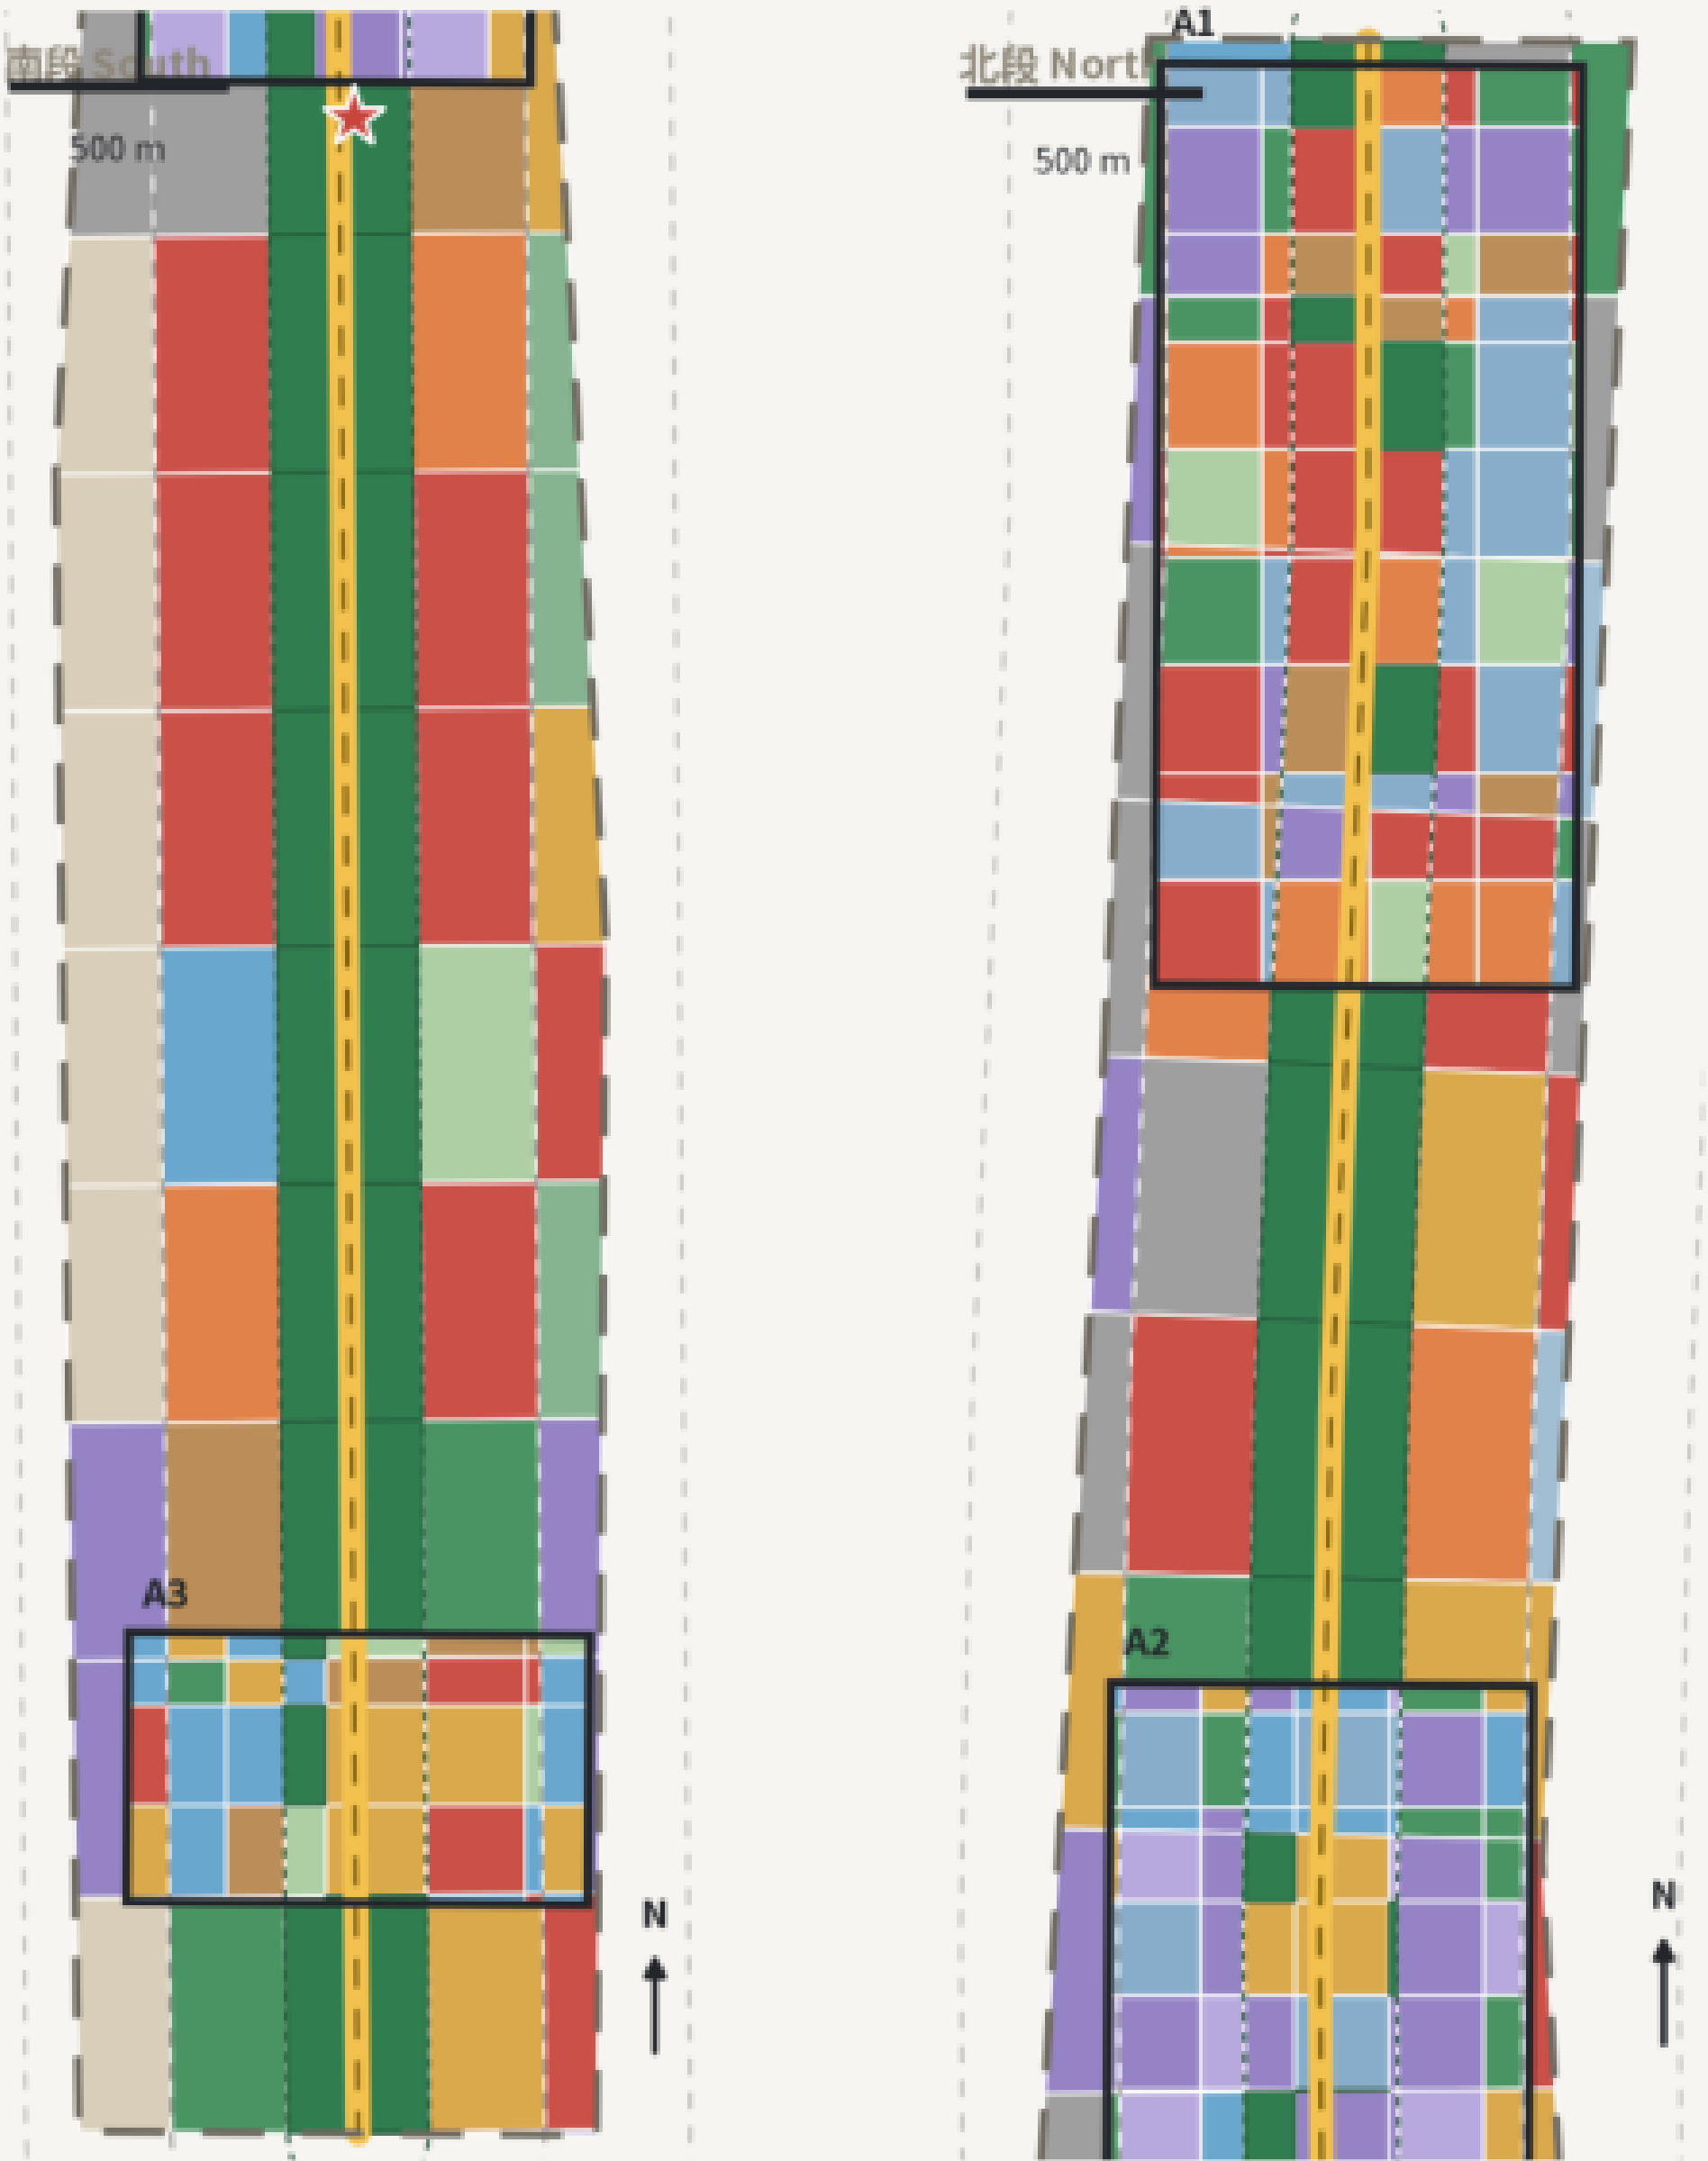

边界为仓库提供的 provisional 粗略边界（非官方红线，不作精确面积依据） | 数据: geometry/"geojson | 工具: Python · shapely · pyproj(EPSG:4548) · matplotlib

用地代码 · 占比 · 面积

1401 公园绿地	25.5% / 291.6 ha
0802 科研/创新	17.7% / 201.8 ha
0701 城镇住宅	8.7% / 98.8 ha
0901 商业混合	8.5% / 97.5 ha
0902 商务金融	7.0% / 79.5 ha
16 战略留白	6.9% / 79.2 ha
1207 道路用地	5.3% / 60.6 ha
0804 教育	5.0% / 56.5 ha
0803 文化	4.2% / 48.0 ha
0904 孵化加速	4.1% / 46.7 ha
1403 广场	3.1% / 35.2 ha
1402 防护绿地	2.0% / 23.0 ha
0702 社区服务	1.4% / 15.8 ha
0805 体育	0.6% / 6.6 ha
0903 娱乐	0.0% / 0.0 ha

圈层

0-170 m 公园带 | 170-450 m 创新界面
450-800 m 职住组团 | 800 m 外支撑与留白
科研 201.8 ha | 公园绿地 291.6 ha
住宅 98.8 ha | 战略留白 79.2 ha


体量与拆改留

建筑基底 222 个 | 平均概念高度 24.4 m
保留占 44% | 改造 182.3 ha | 拆除限于低效危房
地上建筑面积 2154 万 m²（概念）
法定强度指标 status=unknown，见 metrics.json

三处重点区比较：发动机 · 原点 · 客厅

三区两翼回路：原点社区产出人才与原型 → 众智园完成中试与量产 → 大钟寺完成展示、消费与传播

各区均使用 provisional 边界：定位差异、空间联系、项目抓手与风险条件并列表达，灰色为概念建筑基底

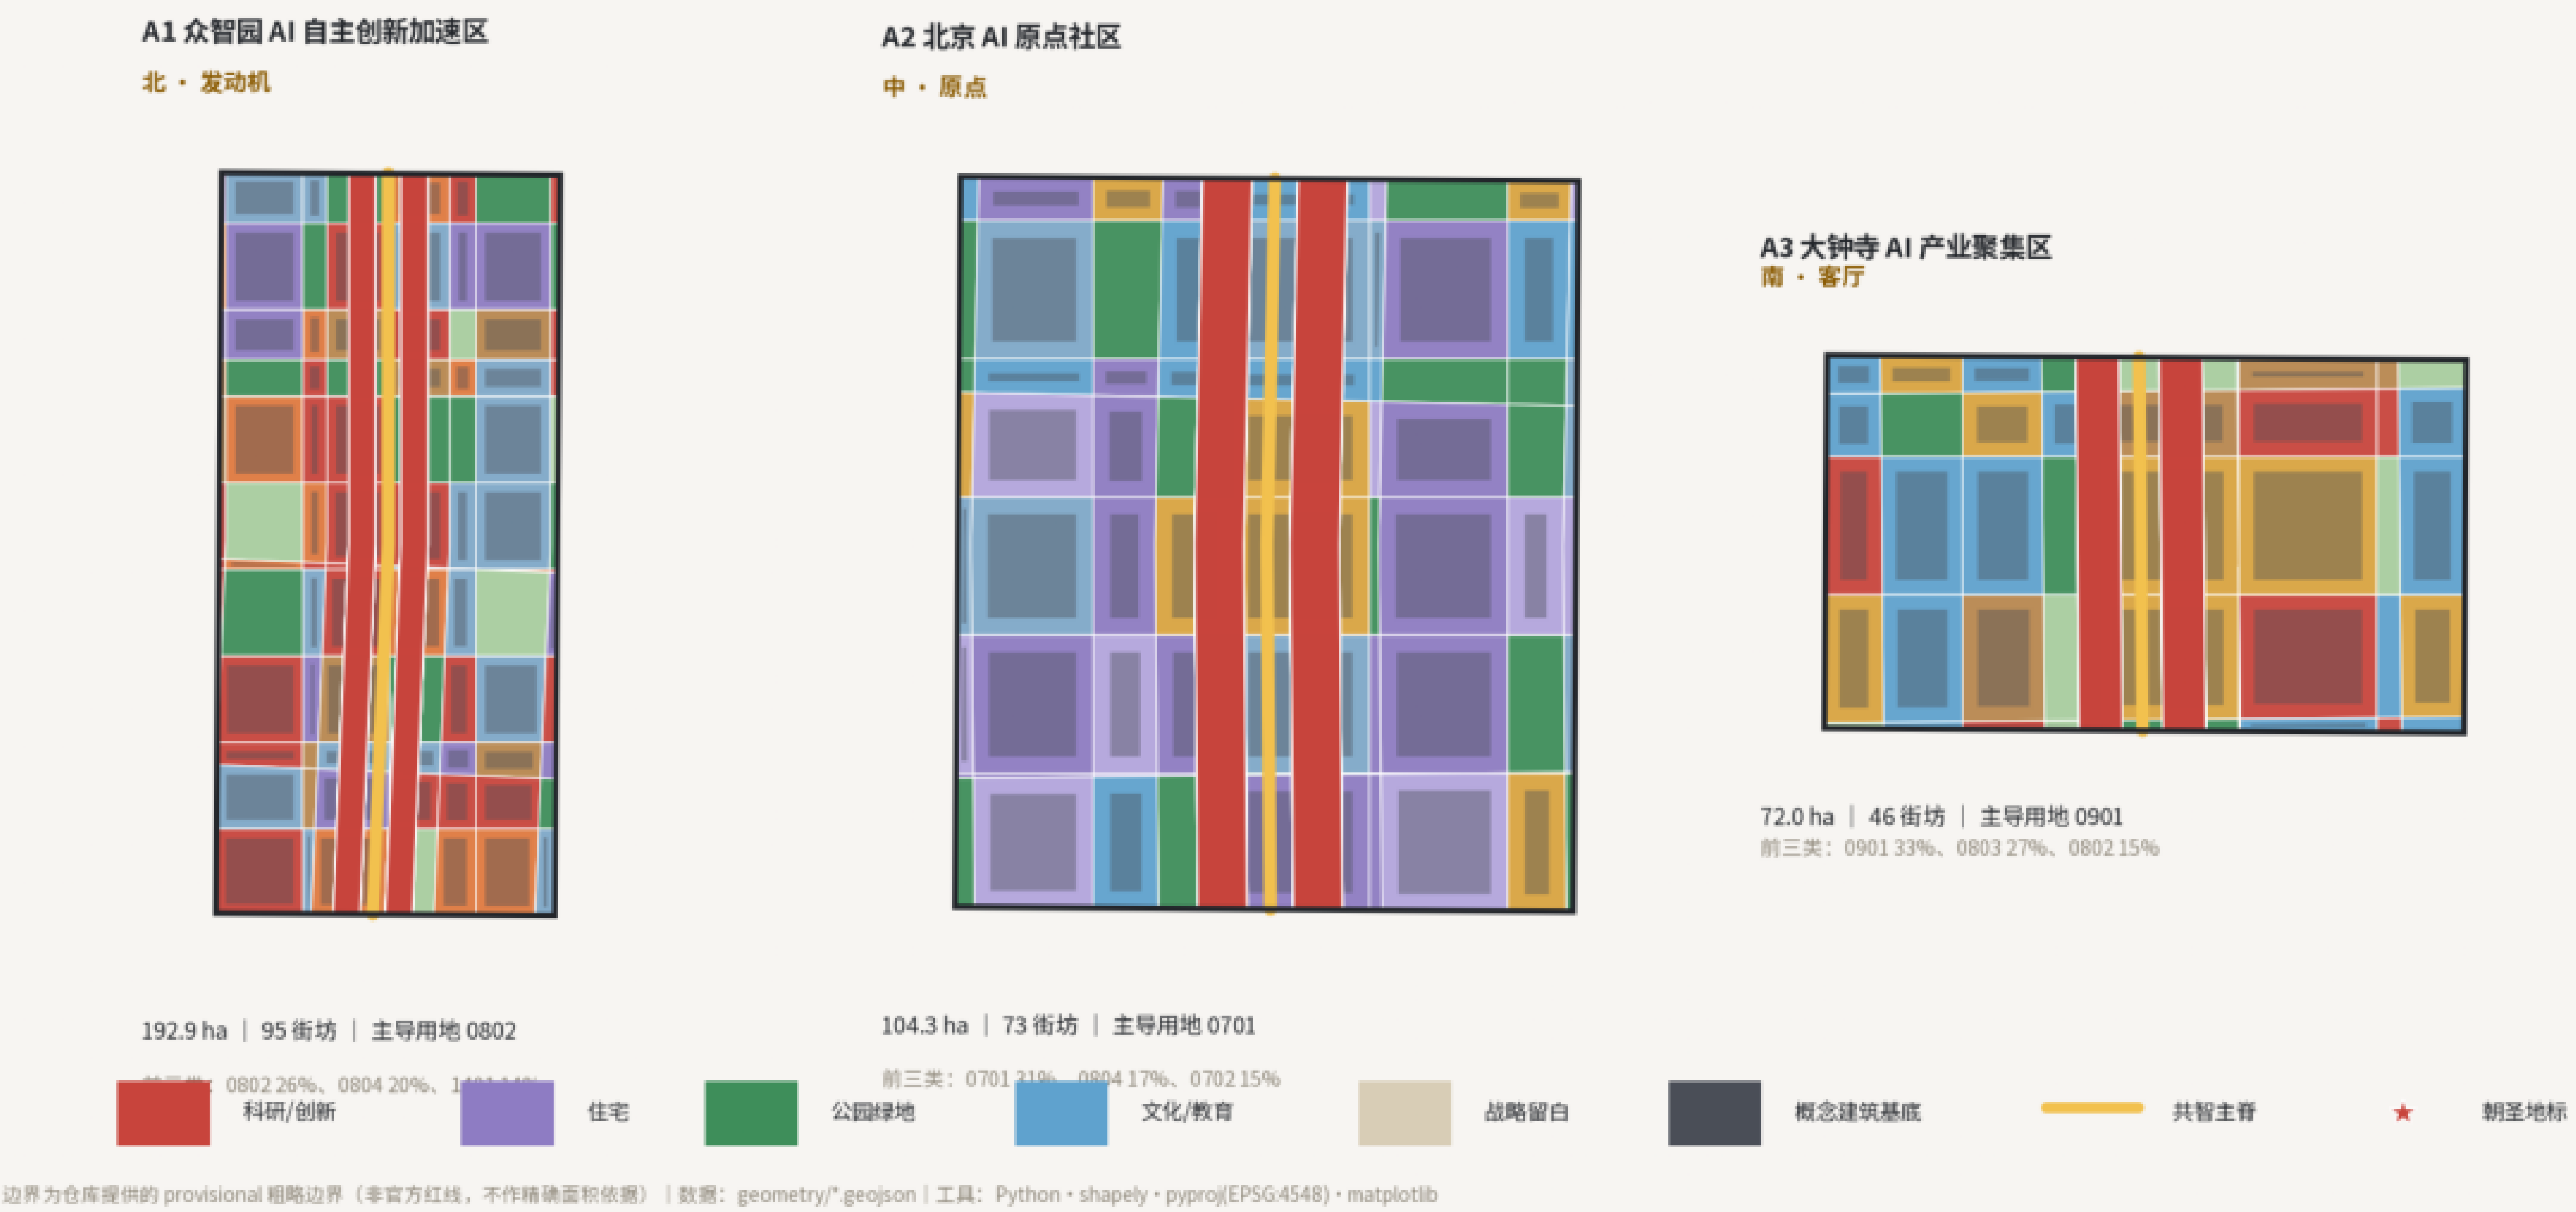

协同回路与风险条件

原点社区产出人才与原型 → 众智园完成中试与量产 → 大钟寺完成展示、消费与传播。


A1 192.9 ha（95 街坊） | A2 104.3 ha（73 街坊） | A3 72.0 ha（46 街坊）

风险：腾退时序、权属与一体化改造审批均未知，本板仅为空间组织建议。

交通慢行 · 蓝绿连续 · 场景节点

先通慢行与换乘，再谈商业增量 | 主脊 9.72 km | 中心线合计 29,846 m | 300 m 公共空间可达 91.0%

车行只承诺微循环与断面预留，不承诺道路红线（红线资料缺失，见 A-CONTROLS-001）

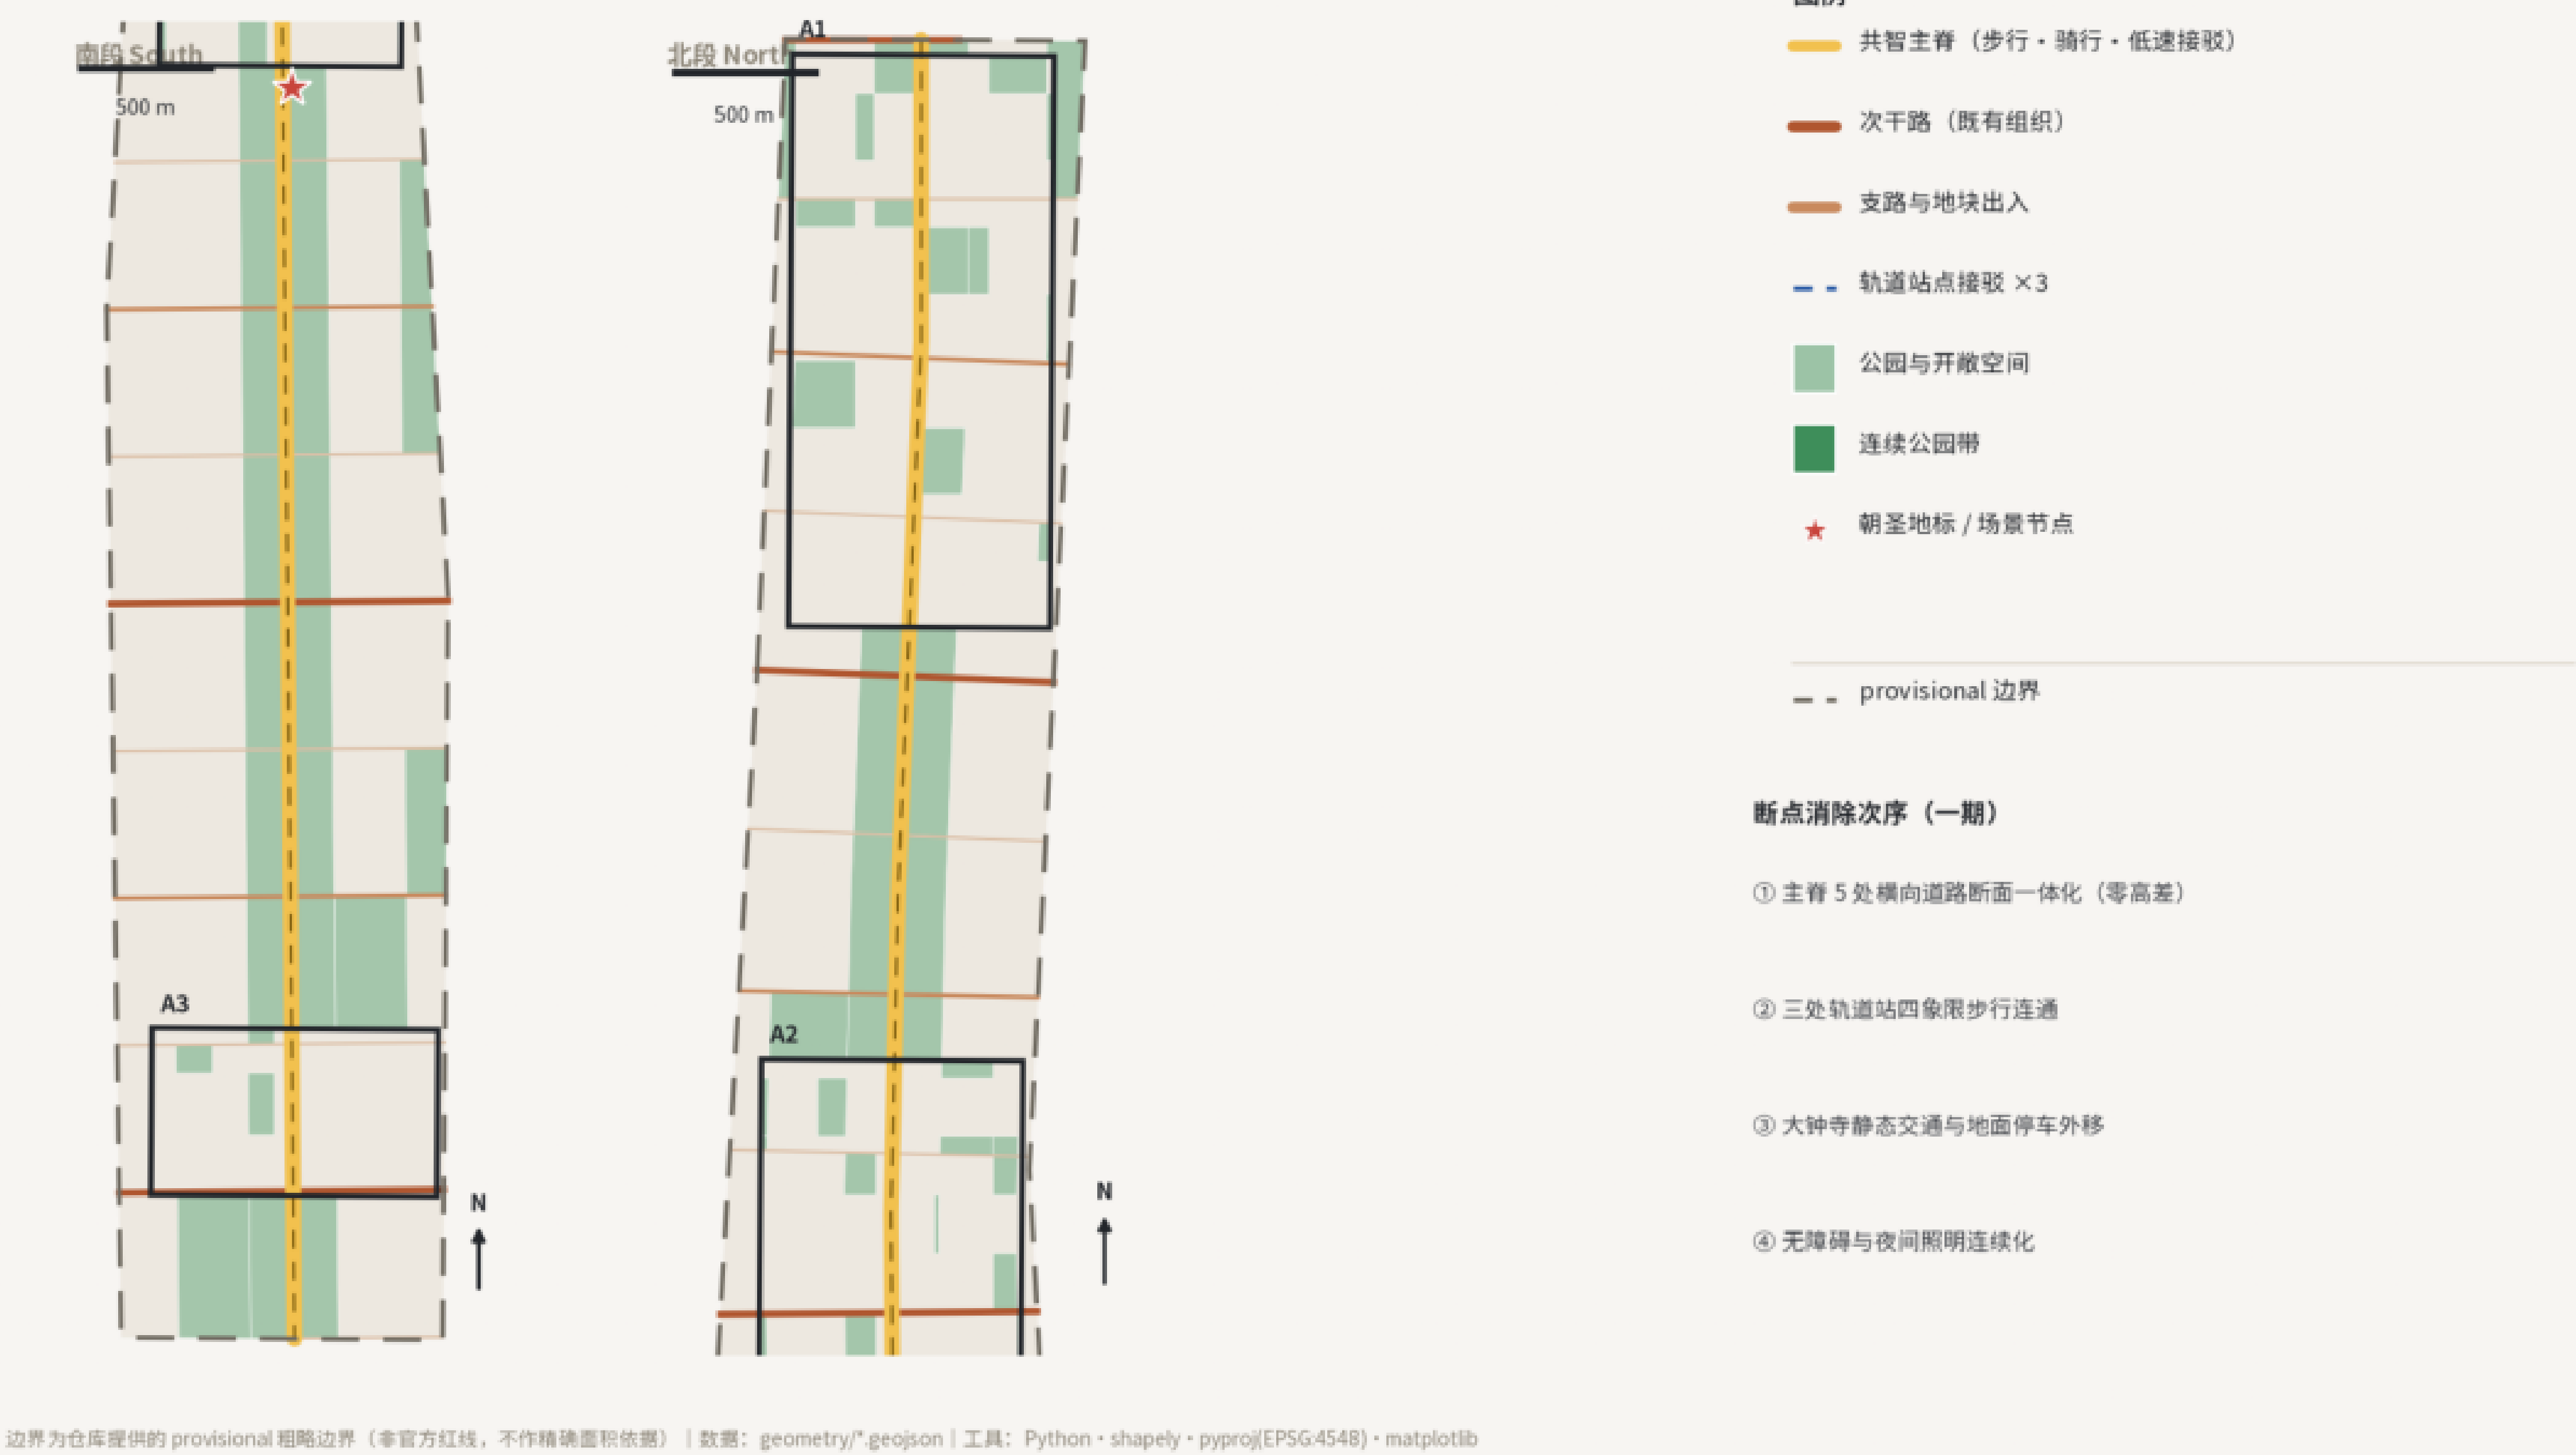

一期断点消除次序

- ① 主脊横向道路断面一体化（零高差）
- ② 三处轨道站四象限步行连通
- ③ 大钟寺静态交通与地面停车外移
- ④ 无障碍与夜间照明连续化

市政与数据设施

综合管廊沿主脊两侧预留（概念线位）
算力与储能随轨道站点分级布置
城市数据中枢落众智园并对接区级平台
海绵：下沉绿地+透水铺装组织面源径流

场景卡（节选）

- SC-01 绿道慢行连续性与断点识别
- SC-03 自动驾驶无人接驳环线（测试）
- SC-04 末端无人配送与夜间货运窗（测试）
- SC-07 具身智能中试共享工厂（测试）
- SC-09 铁路遗址数字再现与 AI 导览
- SC-10 街区级社区共治议事平台

画像与运营（agent.6）

科学家 · 开发者 · 机器人工程师 · 创业者 · 居民与老年人
年度开发者大会+季度开放日+月度社区工作坊
贡献铭牌：数据集 · 模型卡 · 评测结果 · 人工复核记录
三条半日公共体验路线与国际双语口径


数据治理三边界

禁用人脸、健康、居住与未成年人可识别数据
自动判断仅产出候选建议，处置权在人并留痕
合成数据不得冒充实测，铭牌需可核查
合规参照生成式 AI 暂行办法与无障碍法

指标证据链：可复算、留空白、不编造

四项闸门 DETERMINISTIC / SPATIAL / VISUAL / PROFESSIONAL 结果写入 self_check.json | 绿地 314.6 ha | 公共空间 402.5 ha

法定控制指标（容积率、高度、退线、绿地率控制）一律 status=unknown，并注明所需来源与复算前提

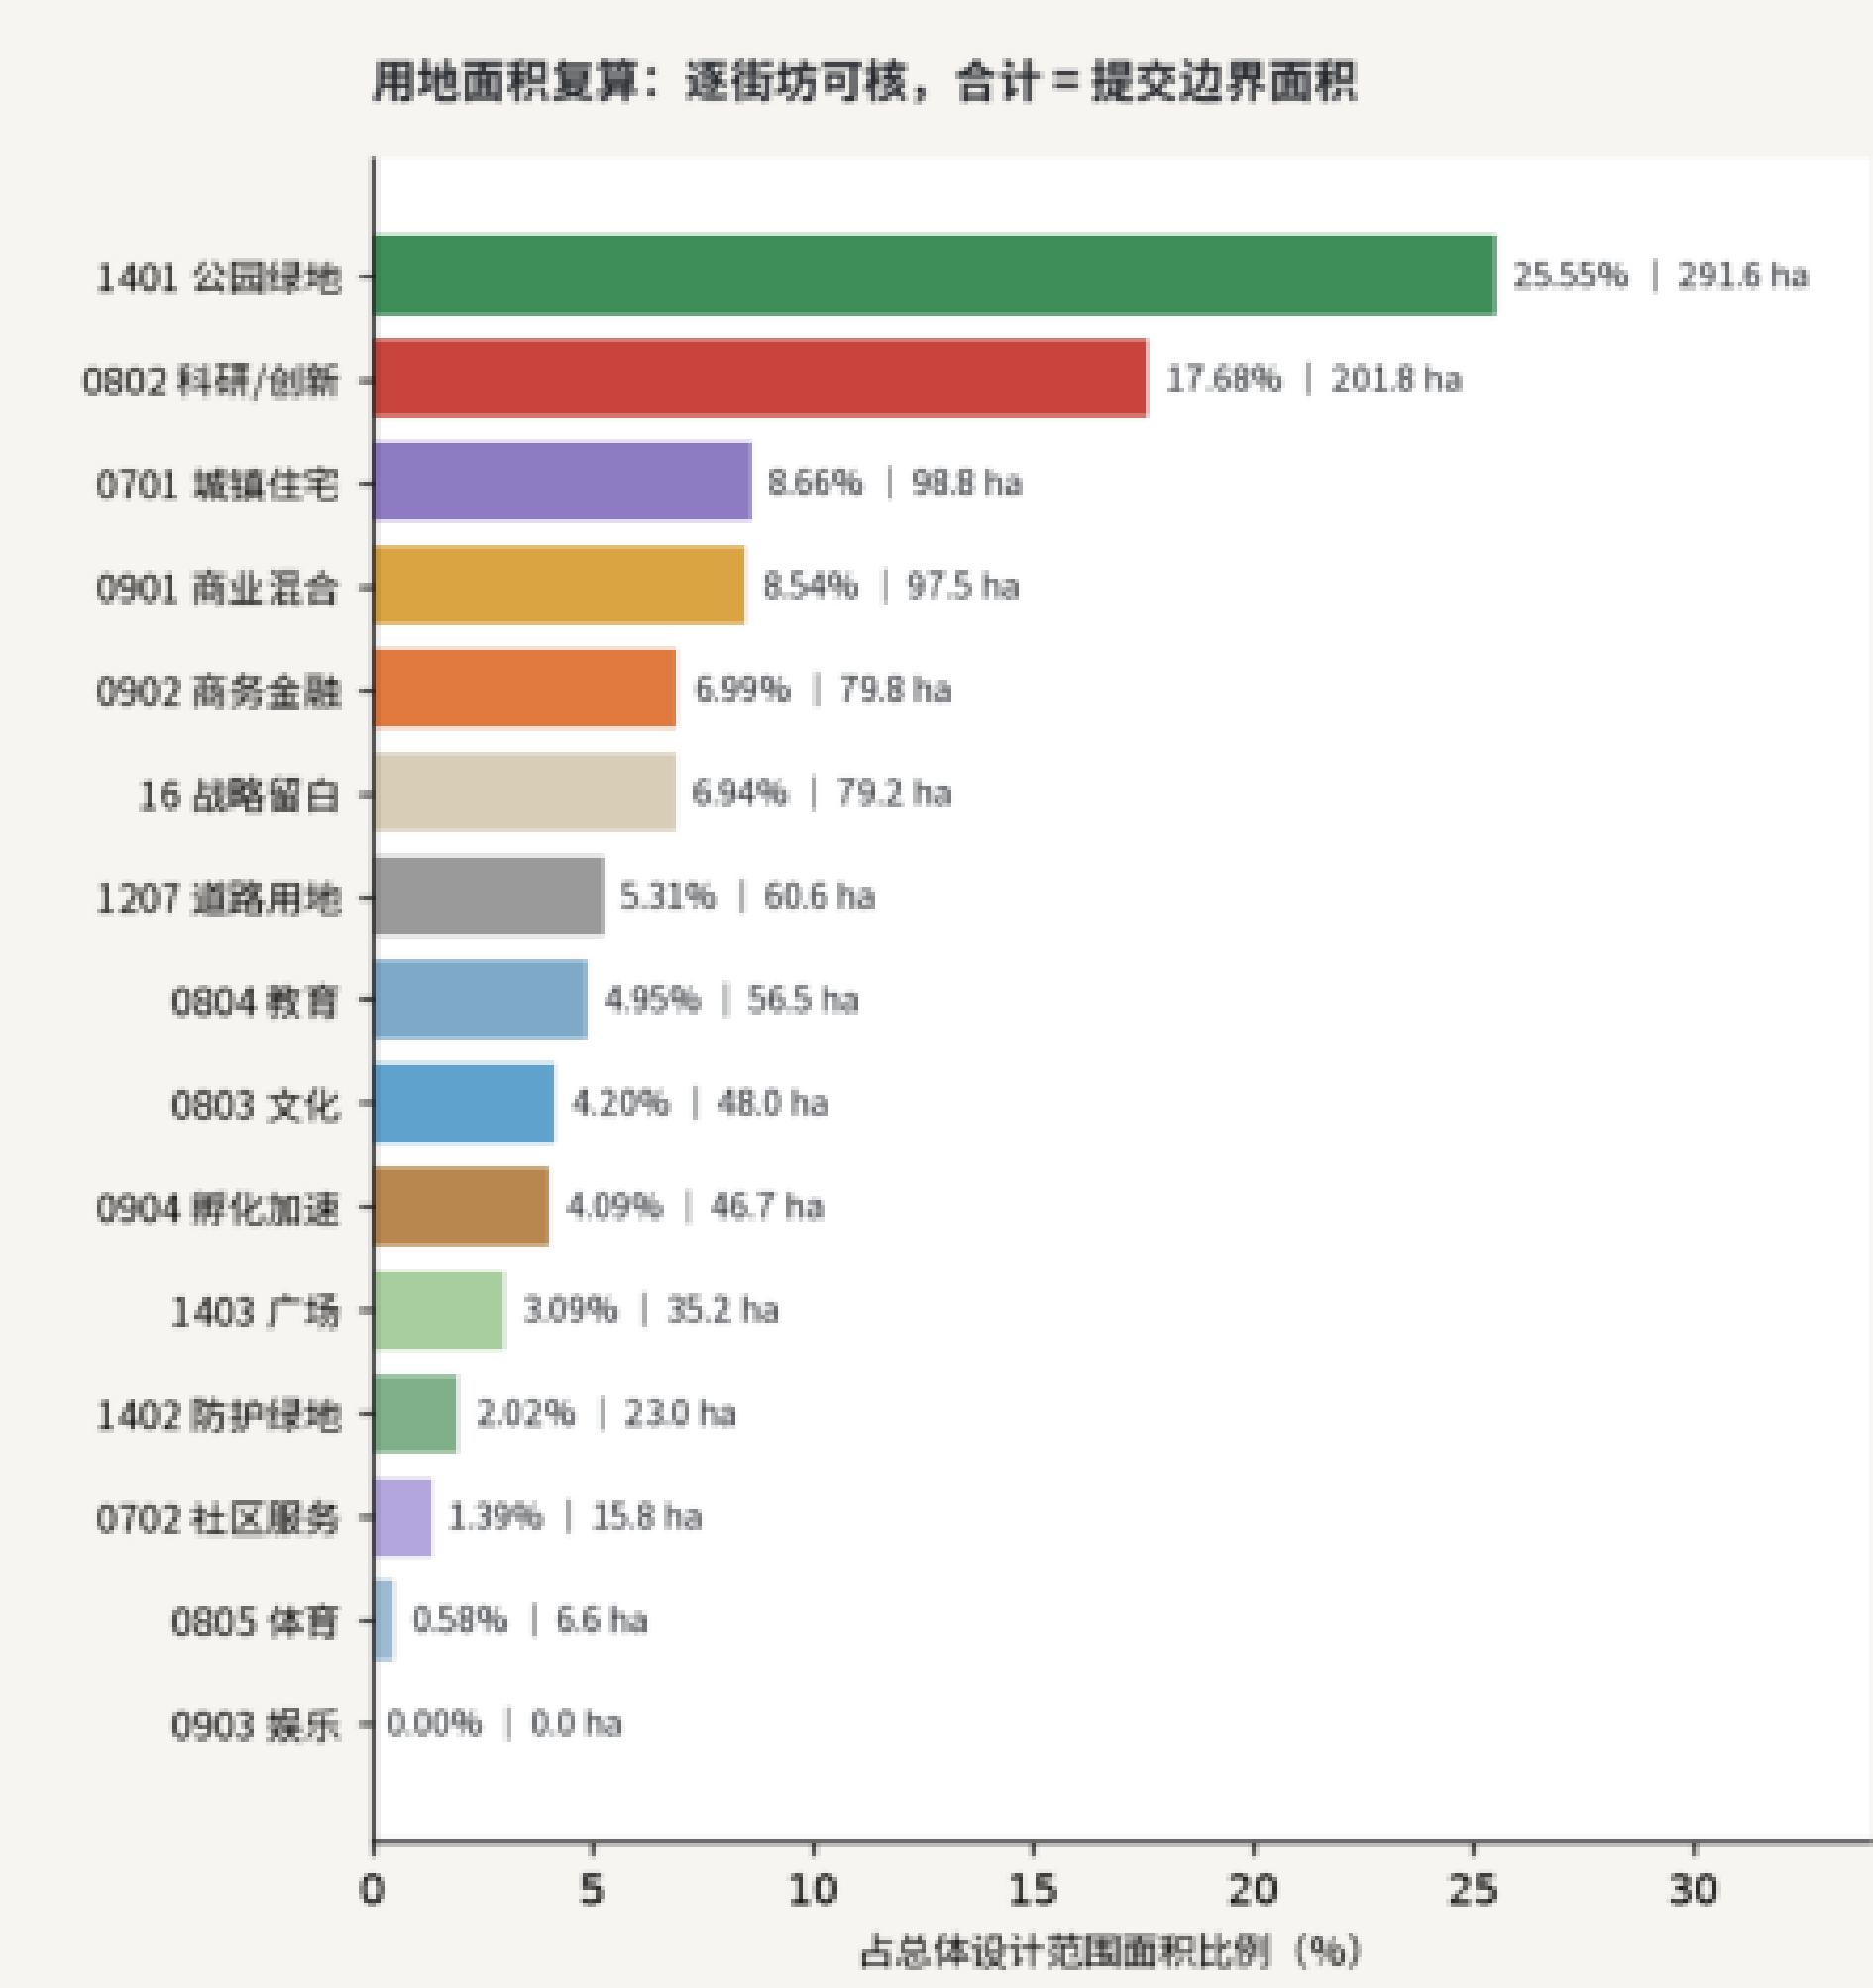

边界为仓库提供的 provisional 粗略边界（非官方红线，不作精确面积依据） | 数据： geometry/" .geojson | 工具： Python + shapely + pyproj(EPSG:4548) + matplotlib

指标—公式—来源文件—状态

site_area_sqm	11.41 km² polygon_area(site_boundary) @EPSG:4548 geometry/site_boundary.geojson	known
green_ratio	27.6% green_area / site_area green_space + site_boundary	known
public_space_ratio	35.3% public_area / site_area public_space + site_boundary	known
building_density	28.5% union(footprint) / site_area buildings.geojson	known
design_floor_area_ratio	1.89 sum(fp x floors) / site_area buldings.geojson	known (概念值)
park_within_300m_share	91.0% area within 300 m of public space / site_area public_space.geojson	known
floor_area_ratio	unknown 需官方控规条件 planning_limits.json	unknown
official_building_height_control_m	unknown 需官方高度控制 planning_limits.json	unknown
setback_m	unknown 需道路红线与建筑控制线 planning_limits.json	unknown

复算顺序：边界 → 用地切分 → 绿地与公共空间 → 建筑与强度 → 分期 → 图面与 HTML 数值。

任何变更须重跑 self_check_submission.py 并刷新 manifest 哈希；街坊数判图 count(LAND_USE)，重点区街坊数分母不同。

分期与实施

- 一期 386.8 ha（34%）公园与起步区
- 二期 308.4 ha（27%）众智园与界面成网
- 三期 446.1 ha（39%）组团更新与留白深化
- 12 项示范项目库+四项实施政策机制

声明

本方案为概念建议，不构成官方结论、审批或实施承诺
全部几何与指标可复算；法定控制项 status=unknown
AI agent 生成（Codex/OpenAI），人类指令与复核参与
许可 COMMUNITY-DISPLAY-ONLY；无商业底图与授权字体