


图 A0-1-1 场地总览·总体空间结构图 (核心图 1)

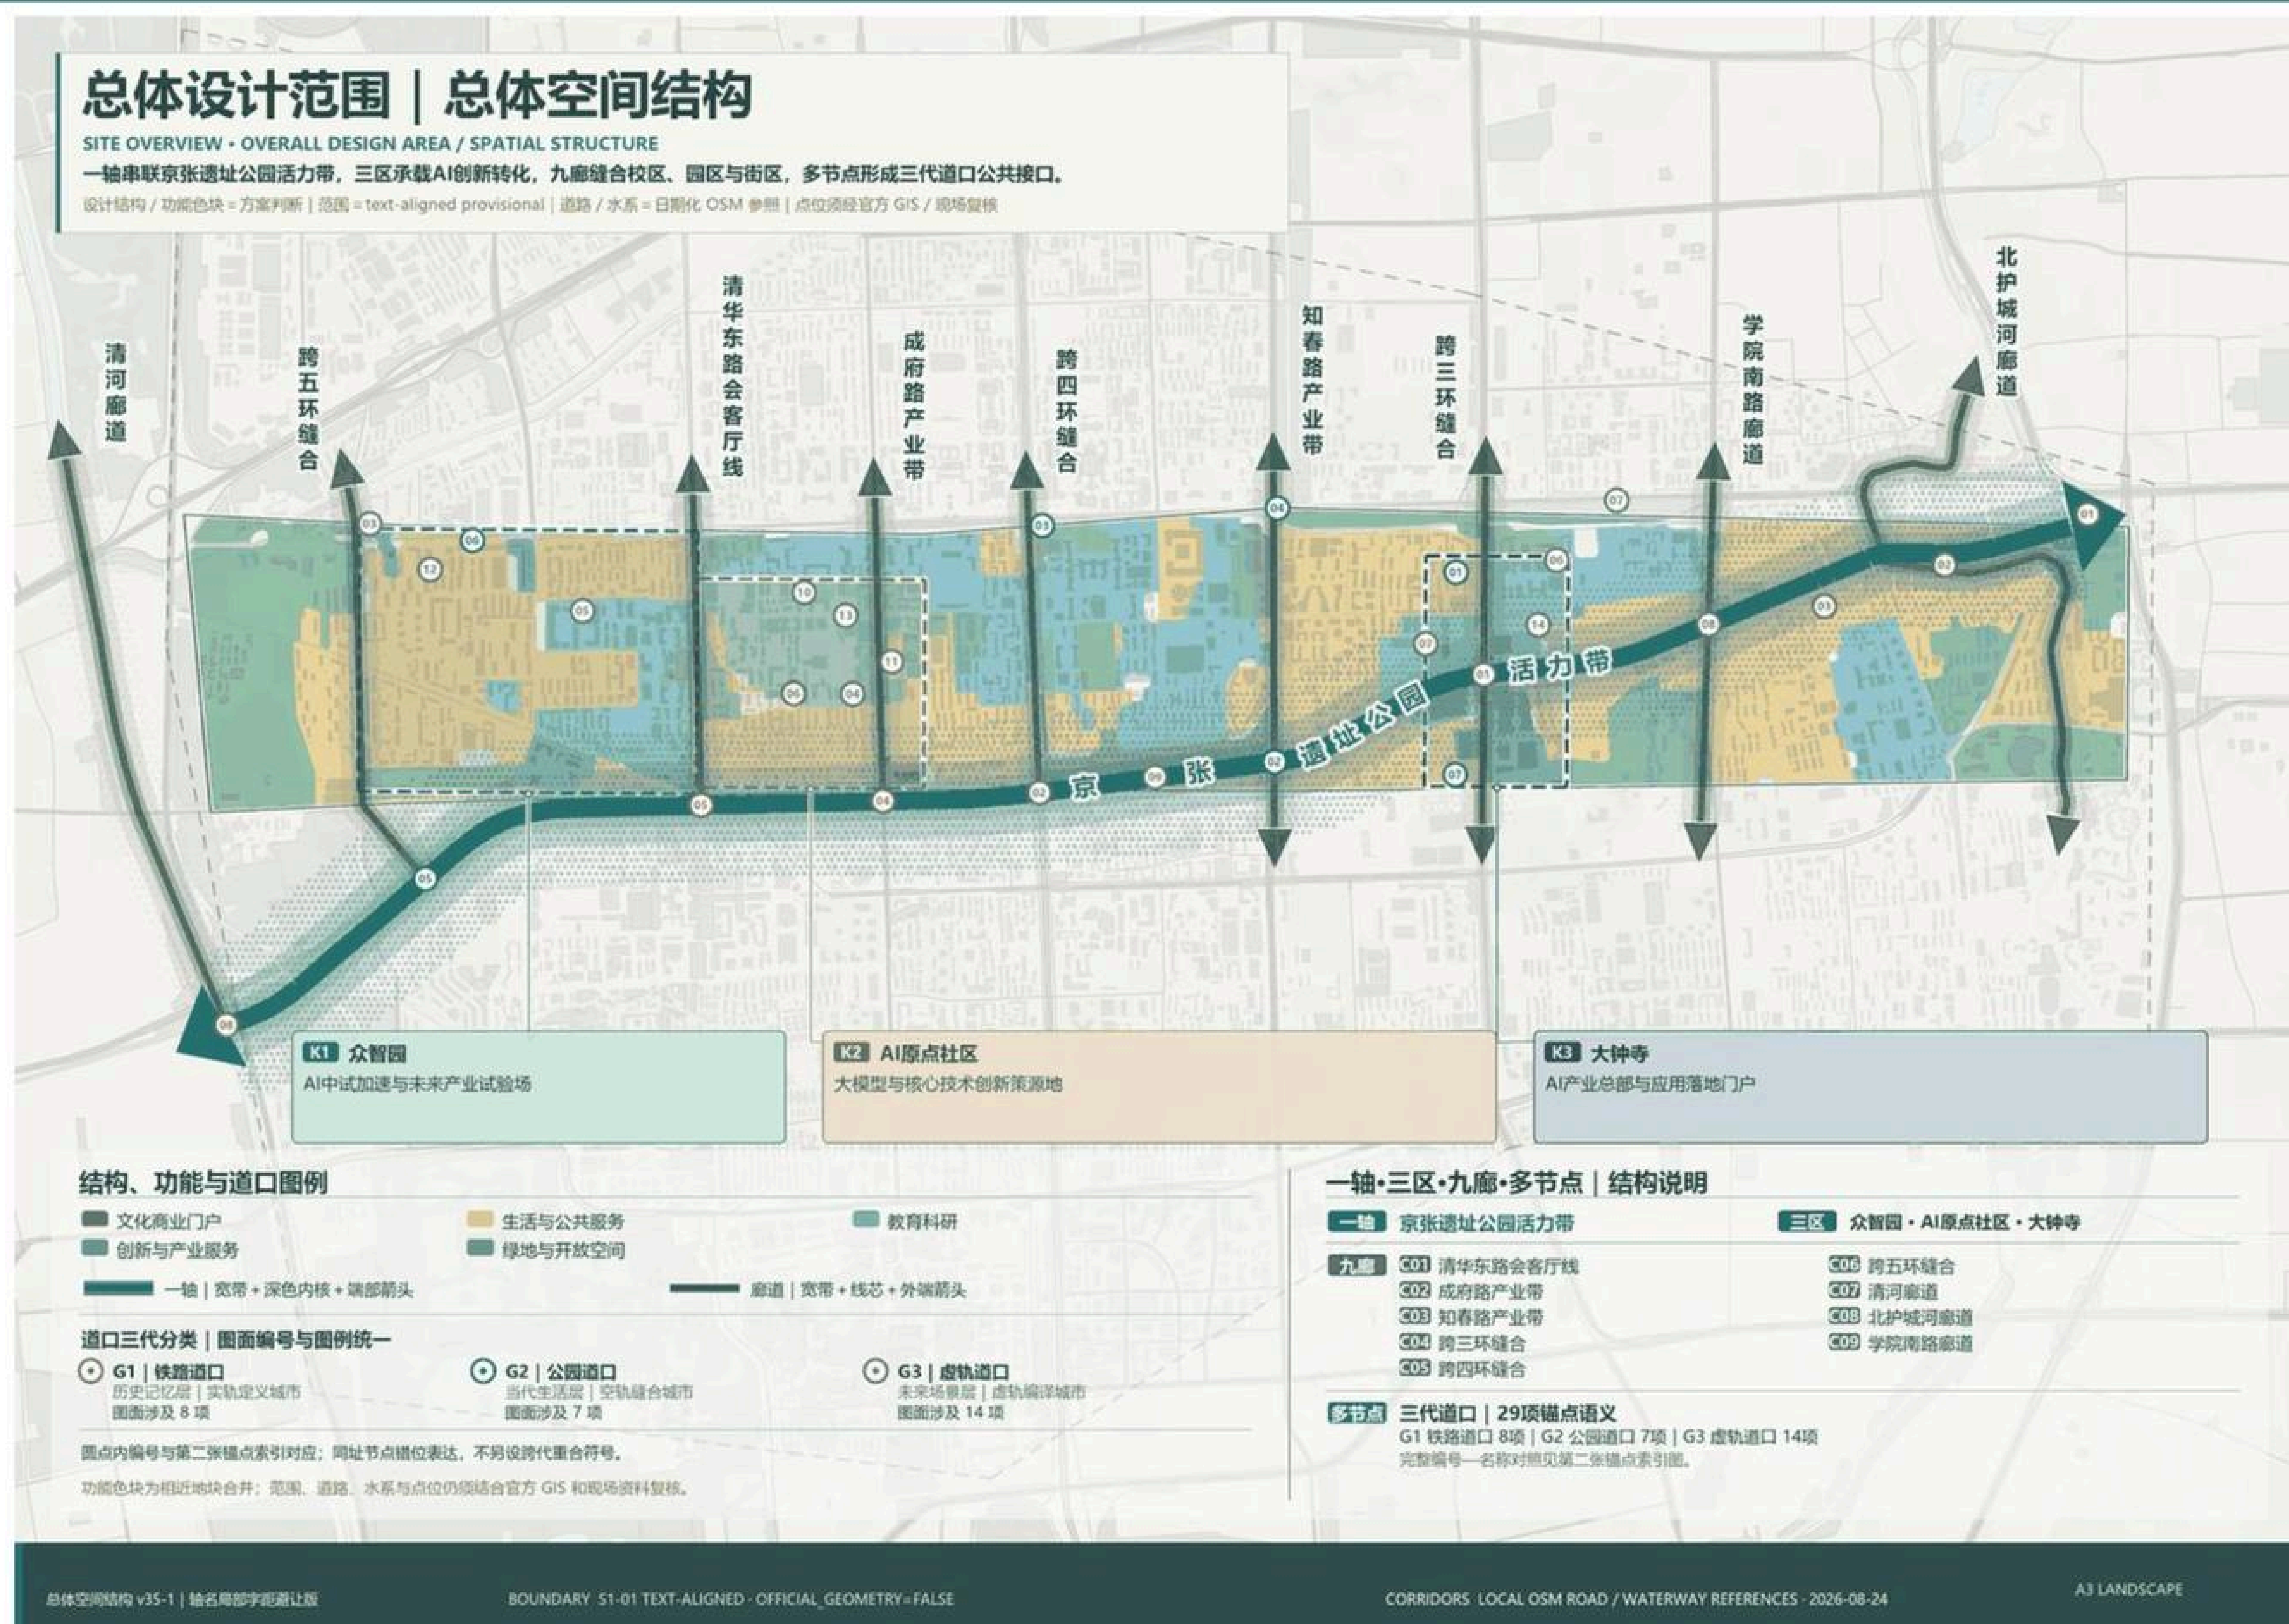

区域结构与创新协同总图

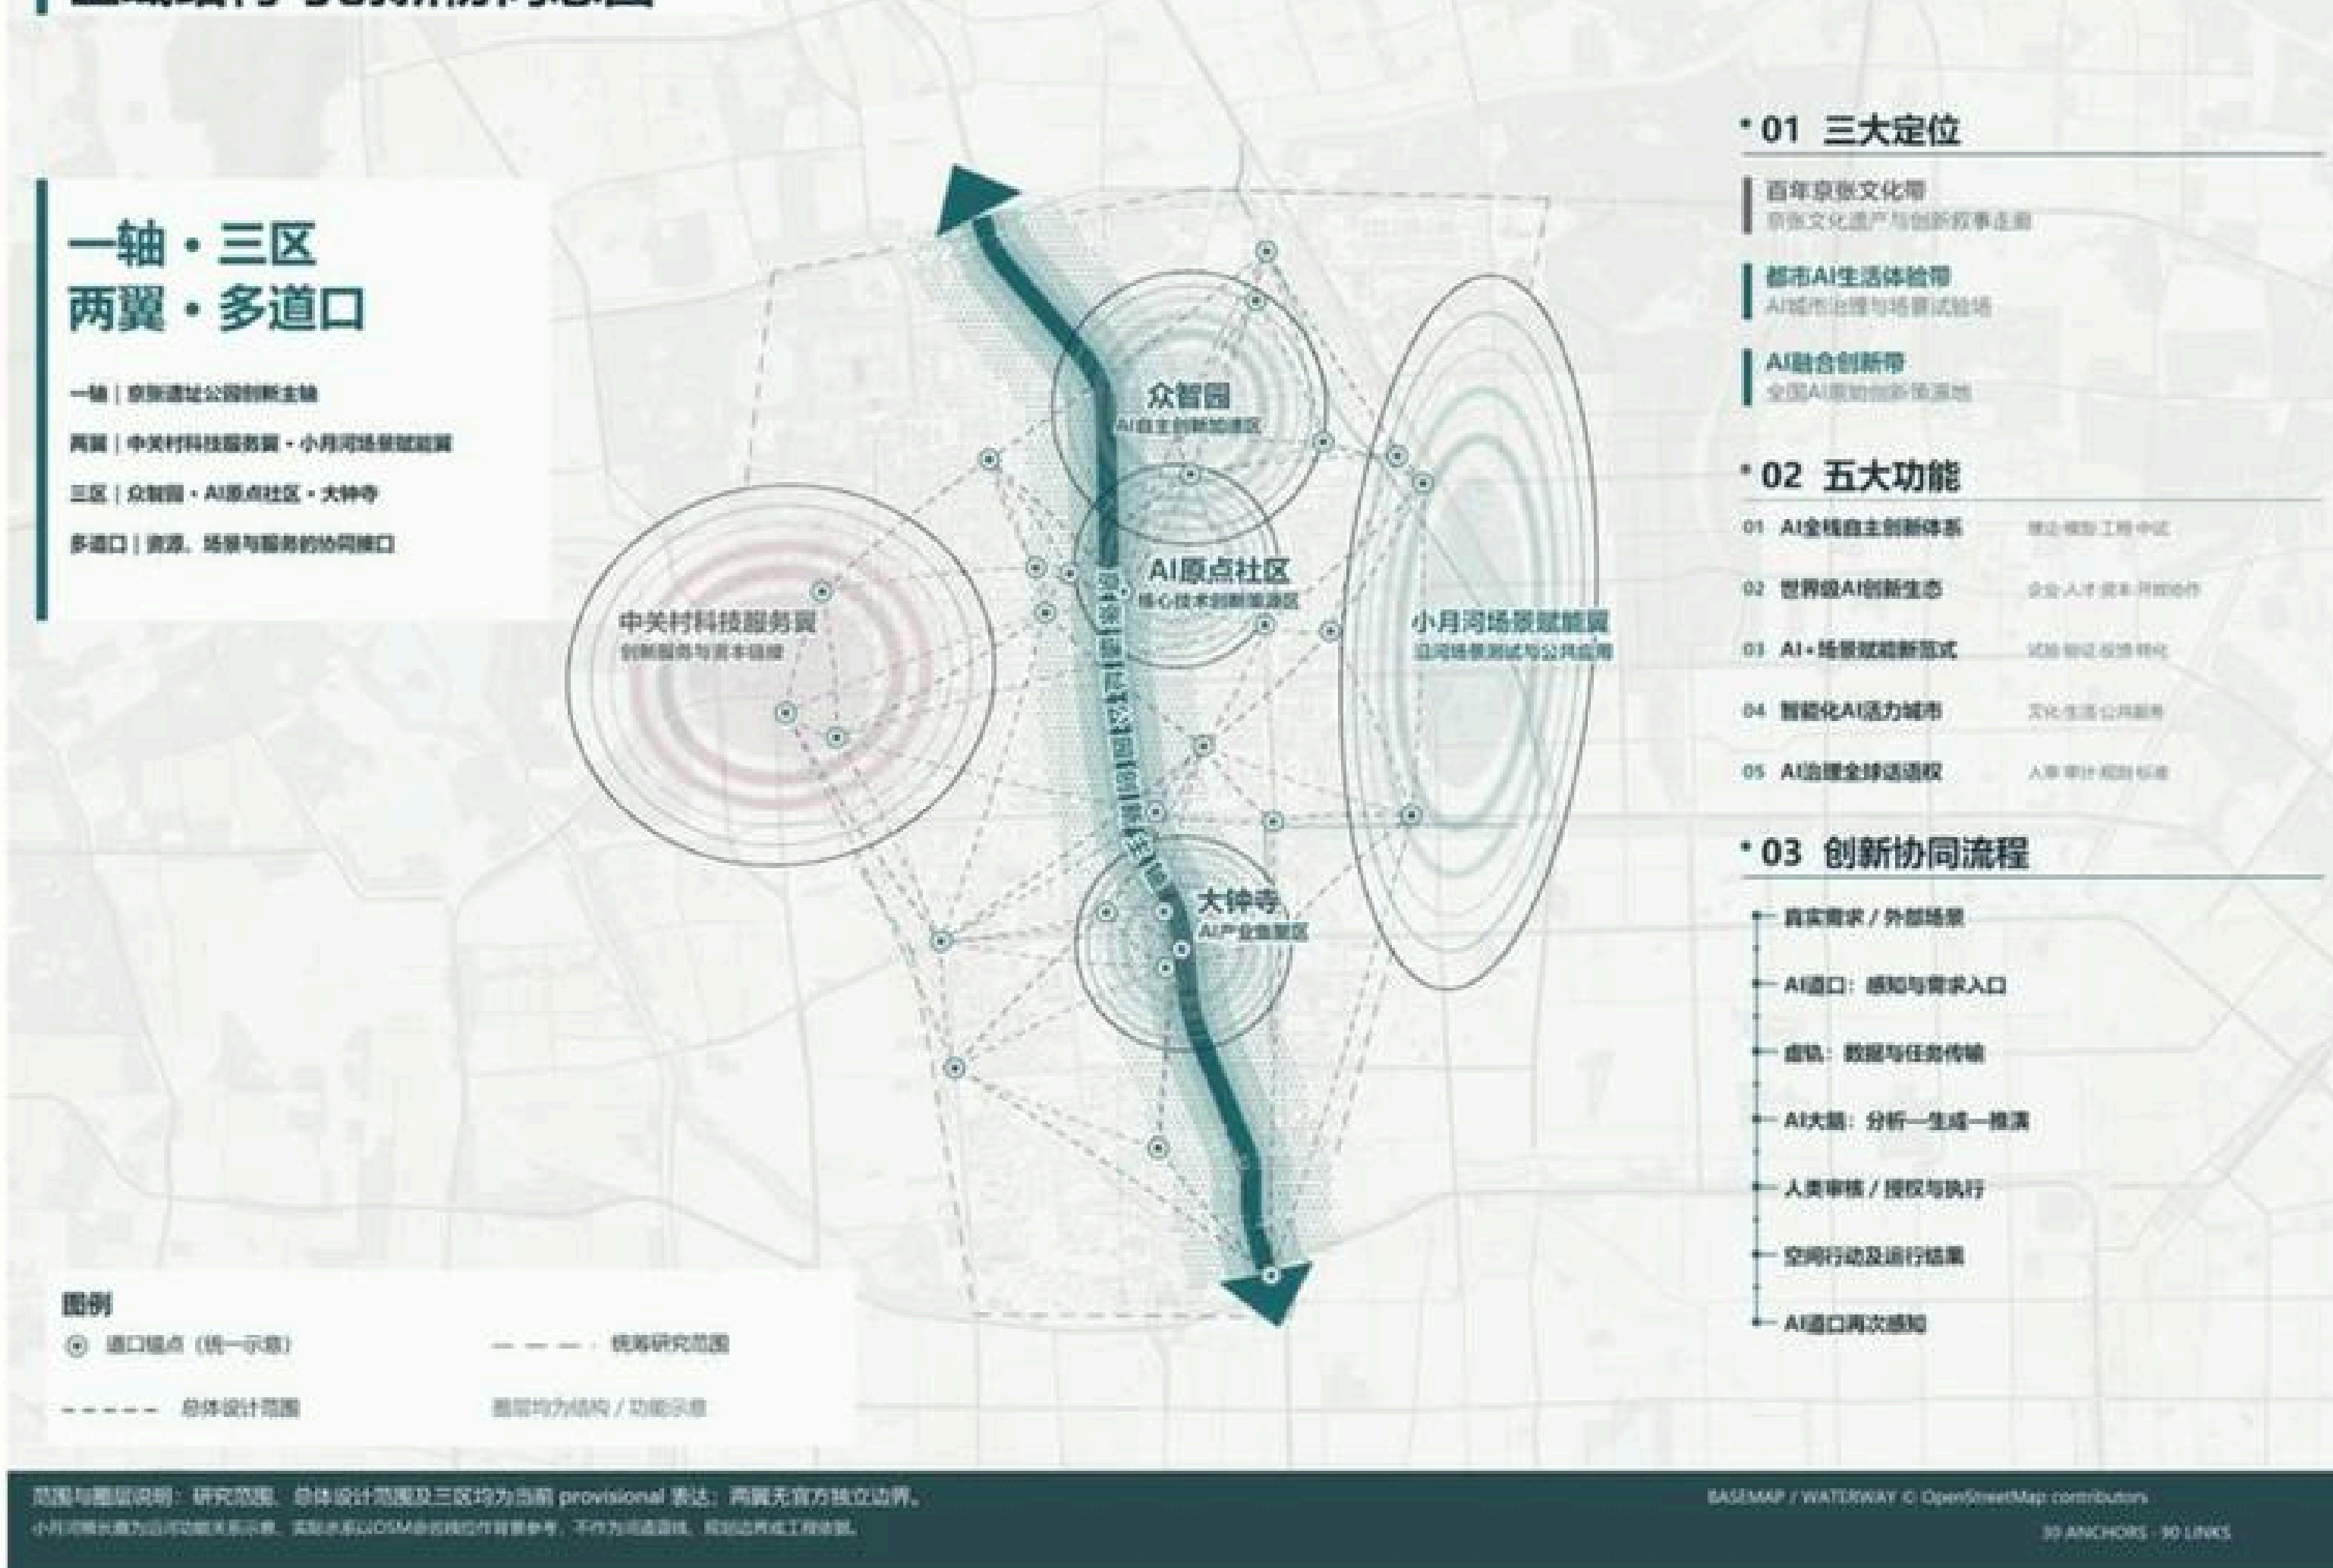


图 A0-1-2 区域结构与创新协同·AI道口

核心判断

- 以京张铁路遗产为时间轴，以三区两翼和 AI 道口为创新网络
- 一轴三区两翼、多道口；三大定位沿“实轨—空轨—虚轨”三代轨转译
- 三级范围：统筹研究范围 / 总体设计范围 / 三处重点区域

关键指标

11.4	km ² 总体设计范围 (公告约值) 官方公告约 11.4 km ² ; 临时几何复算 11.4925 km ² 见 A0-6-2
368.4	ha 三处重点区域合计 官方公告约面积 / metric:key_areas_announced_total_sqm
3+2	三区两翼场内组织 第03章 / 任务书三大定位五大功能



图 A0-1-3 三层范围工作框架图

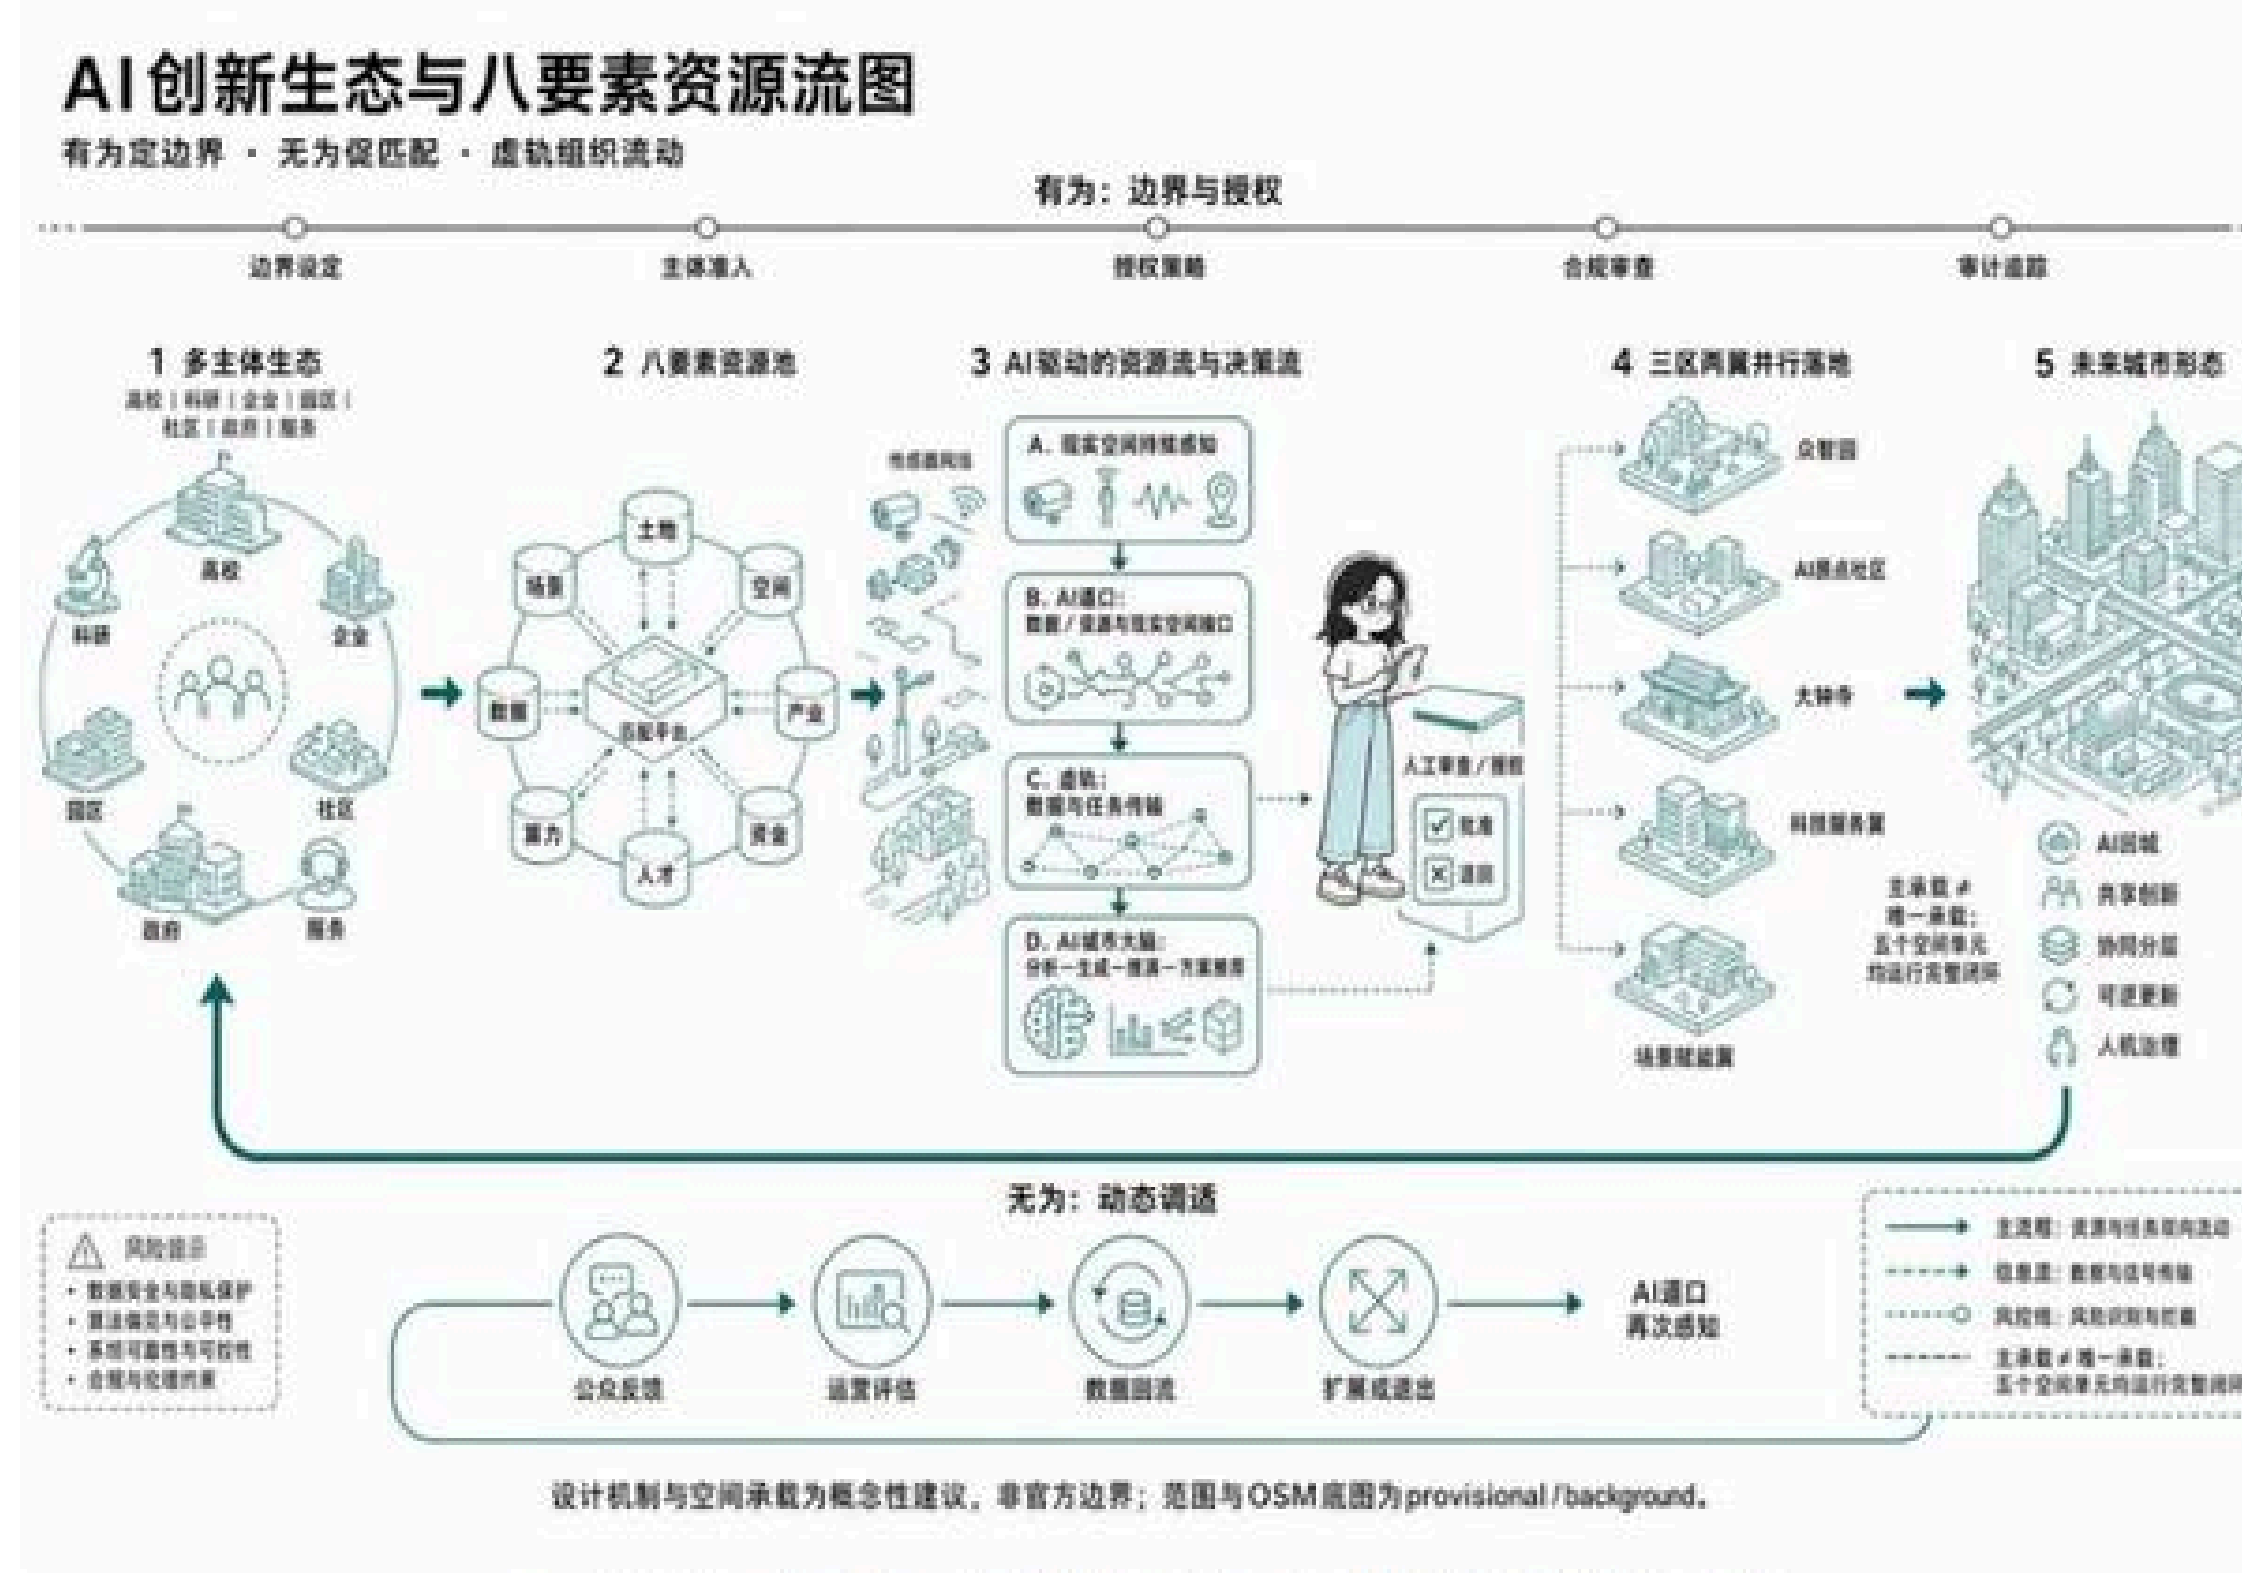


图 A0-1-4 AI创新生态八要素资源流

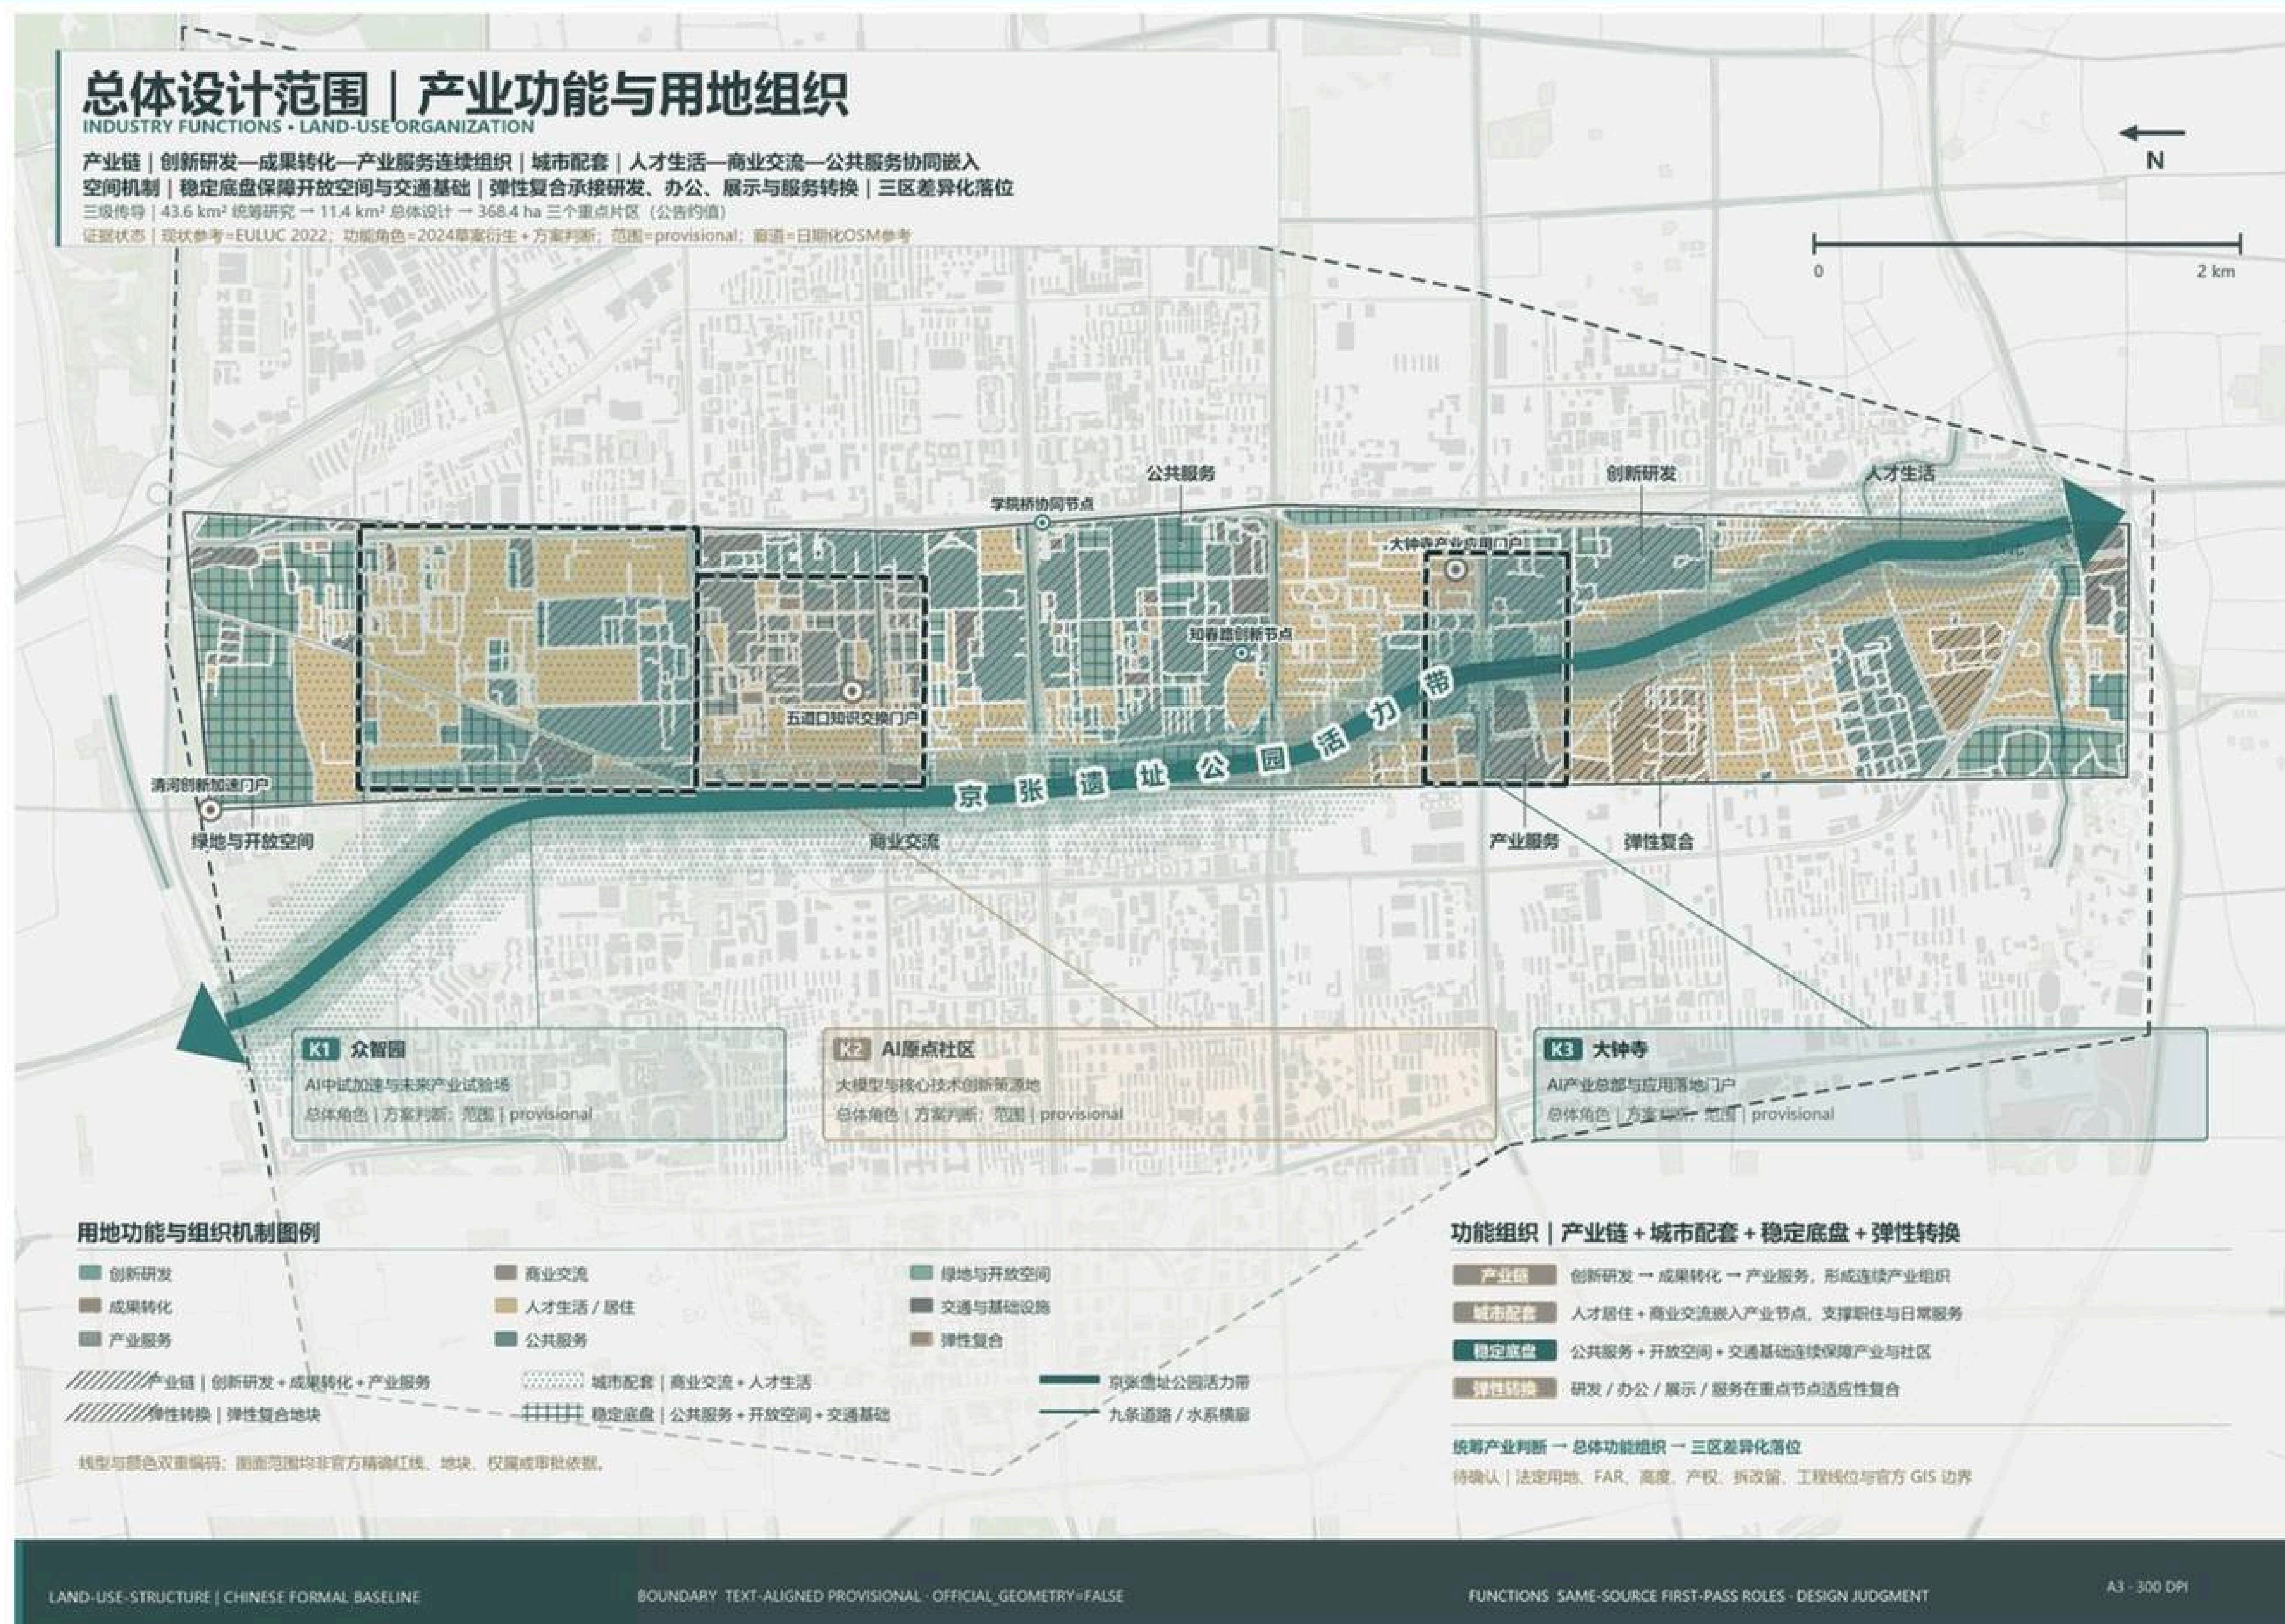


图 A0-1-5 统筹研究范围全景鸟瞰

边界声明：总体设计范围及重点片区边界采用临时约束范围，只用于方案阶段空间组织与测算，不作为官方精确红线、权属边界或审批依据。

图面数值回溯 geometry / metrics.json (G-11)

图 A0-2-1 总体用地与功能结构图 (核心图 2)



第07章 | 拆改留分类与空间对象方向

对象 / 项目组团级方案

不替代地块、权属、审批或实施结论



图 A0-2-2 拆改留分类与空间对象方向图

核心判断

■ 以城市更新为主要空间路径，在京张遗址公园沿线街区控规框架内统筹用地与开发强度

拆改留由单一“保留/拆除”调整为六类方向，现阶段只达对象/项目组团级深度

开发强度与建筑高度无正式依据时明确待确认，不得伪造控规结论

关键指标

6 类	拆改留方向 第07章 7.4 / source:CH7-RENEWAL
29 项	道口锚点 第04章 图4-2 / source:CH7-CHAINS
待确认	建设规模与拆改留（远期校准） 第07章 / 不作实施承诺

总体设计范围 | 开发强度分区与总体形态控制

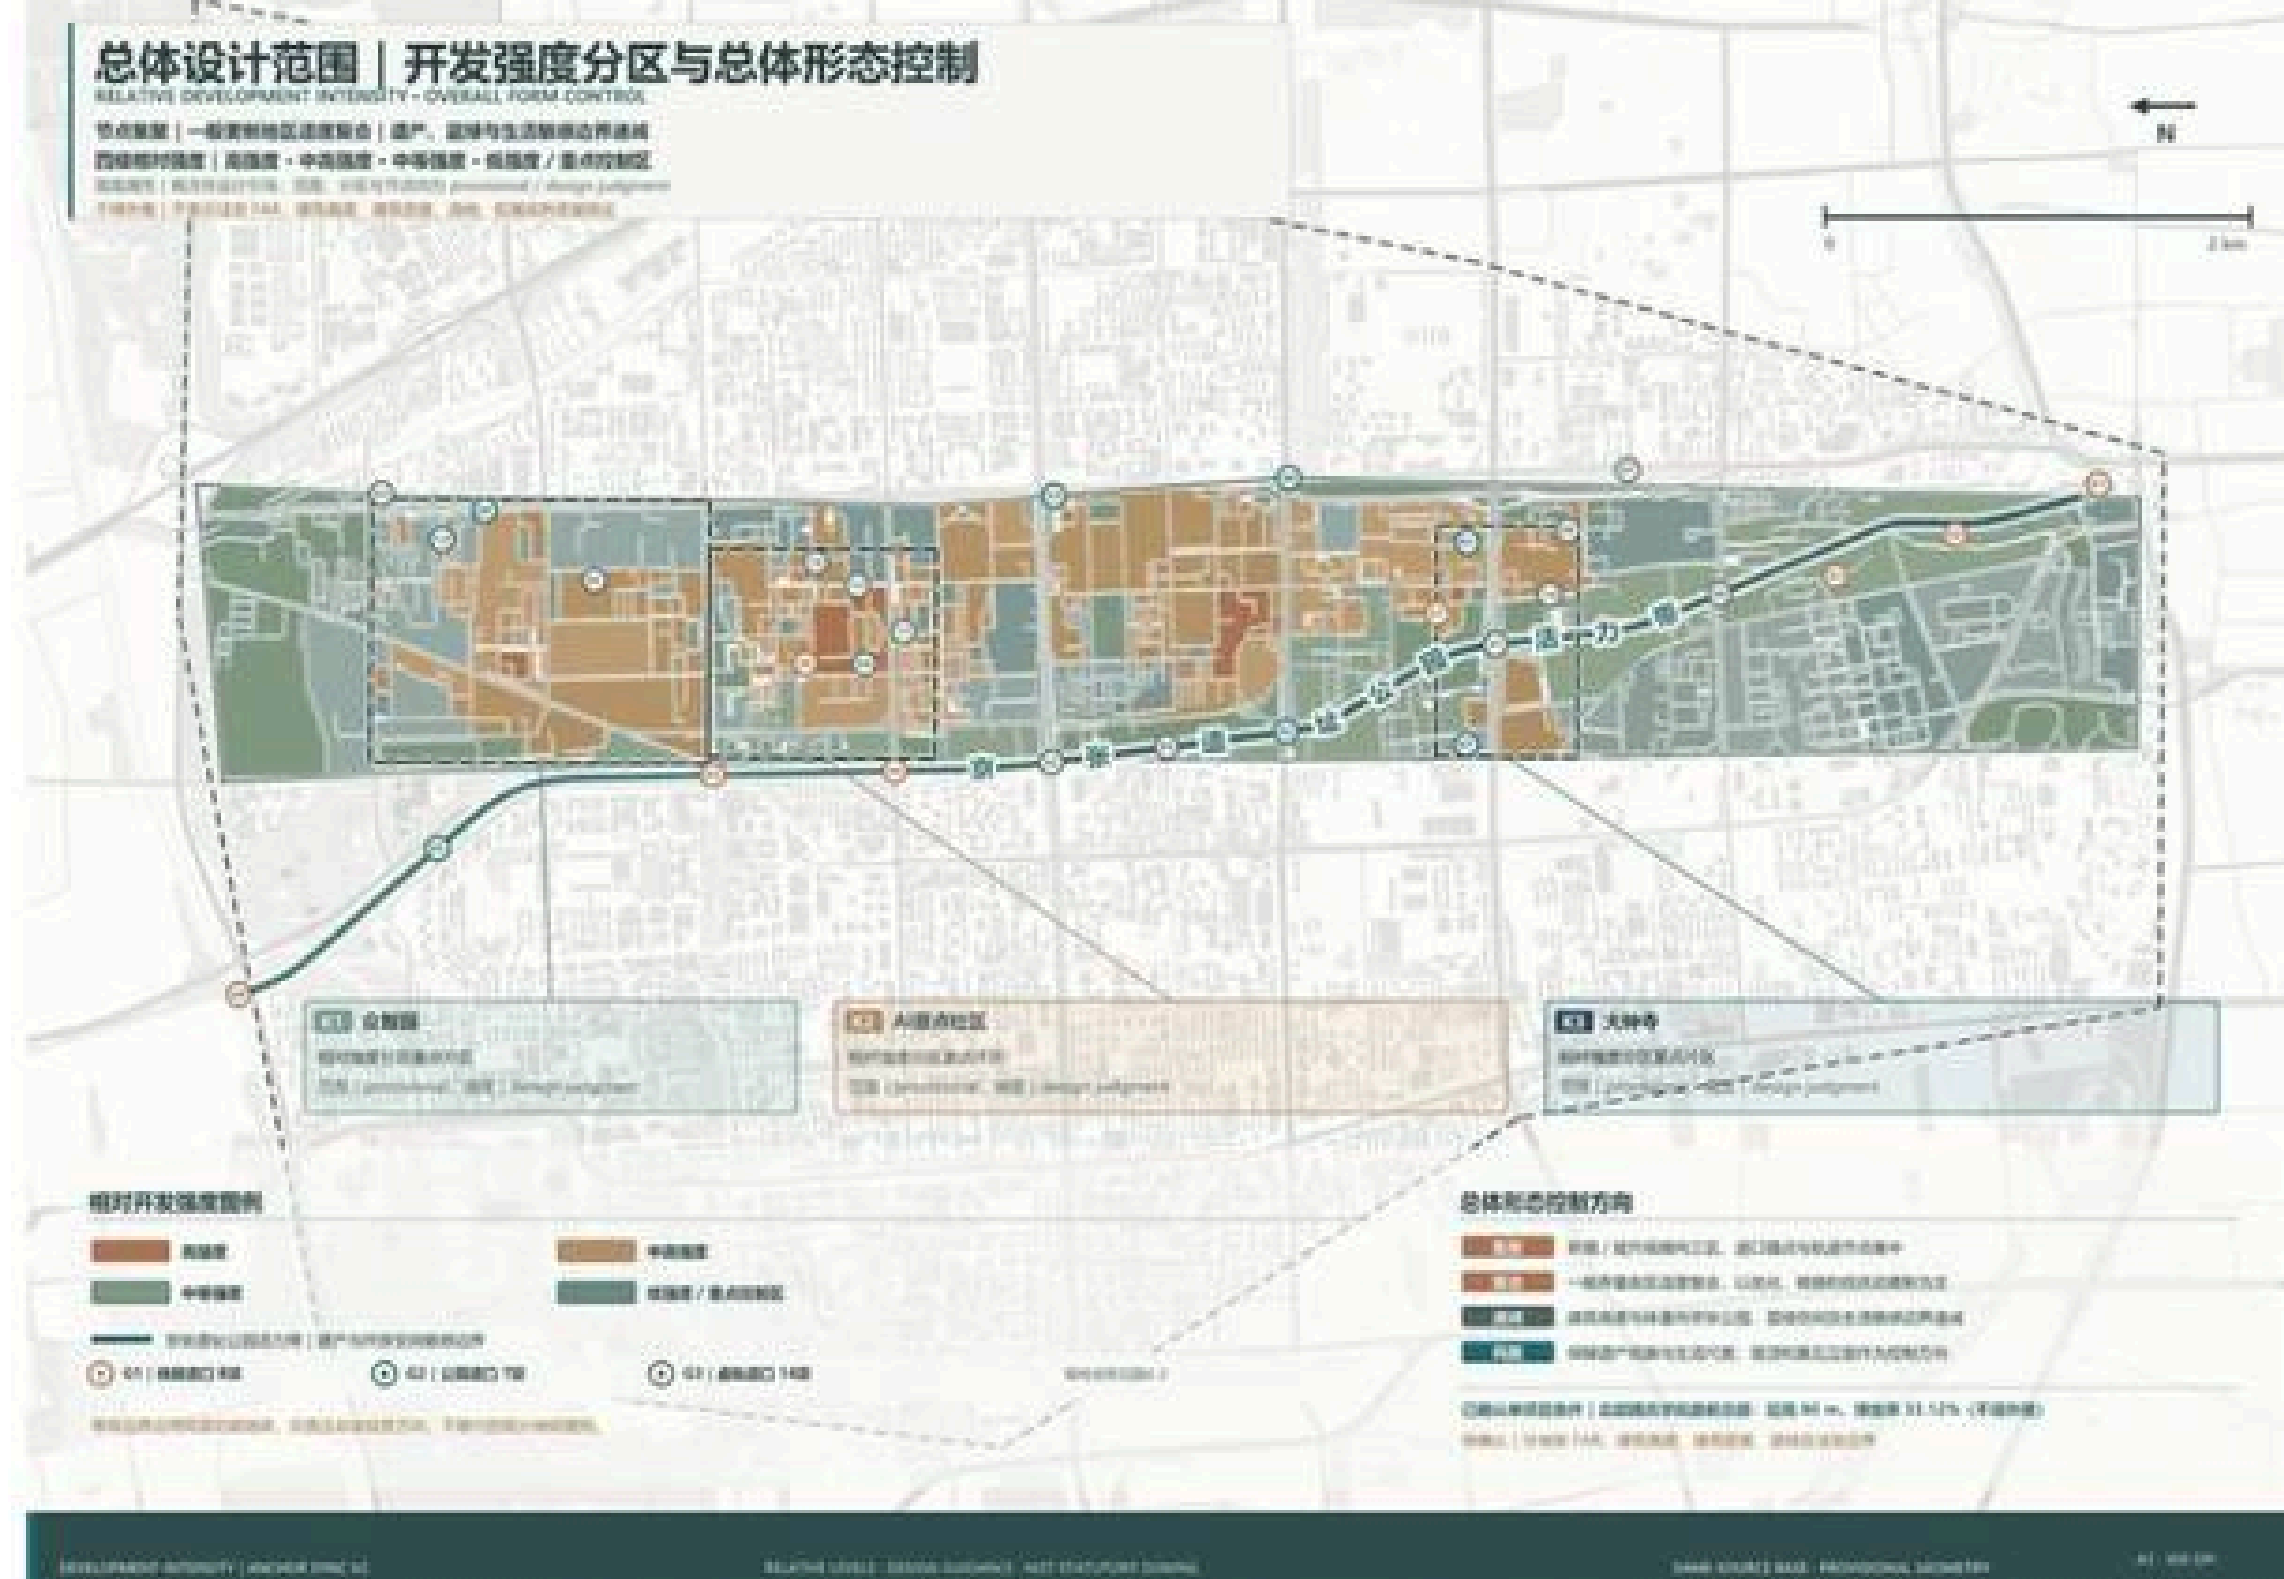


图 A0-2-3 开发强度分区图·图4-5

总体设计范围 | 道口锚点分布



图 A0-2-4 道口锚点分布图·图4-2

总体设计范围 | 城市更新总体框架

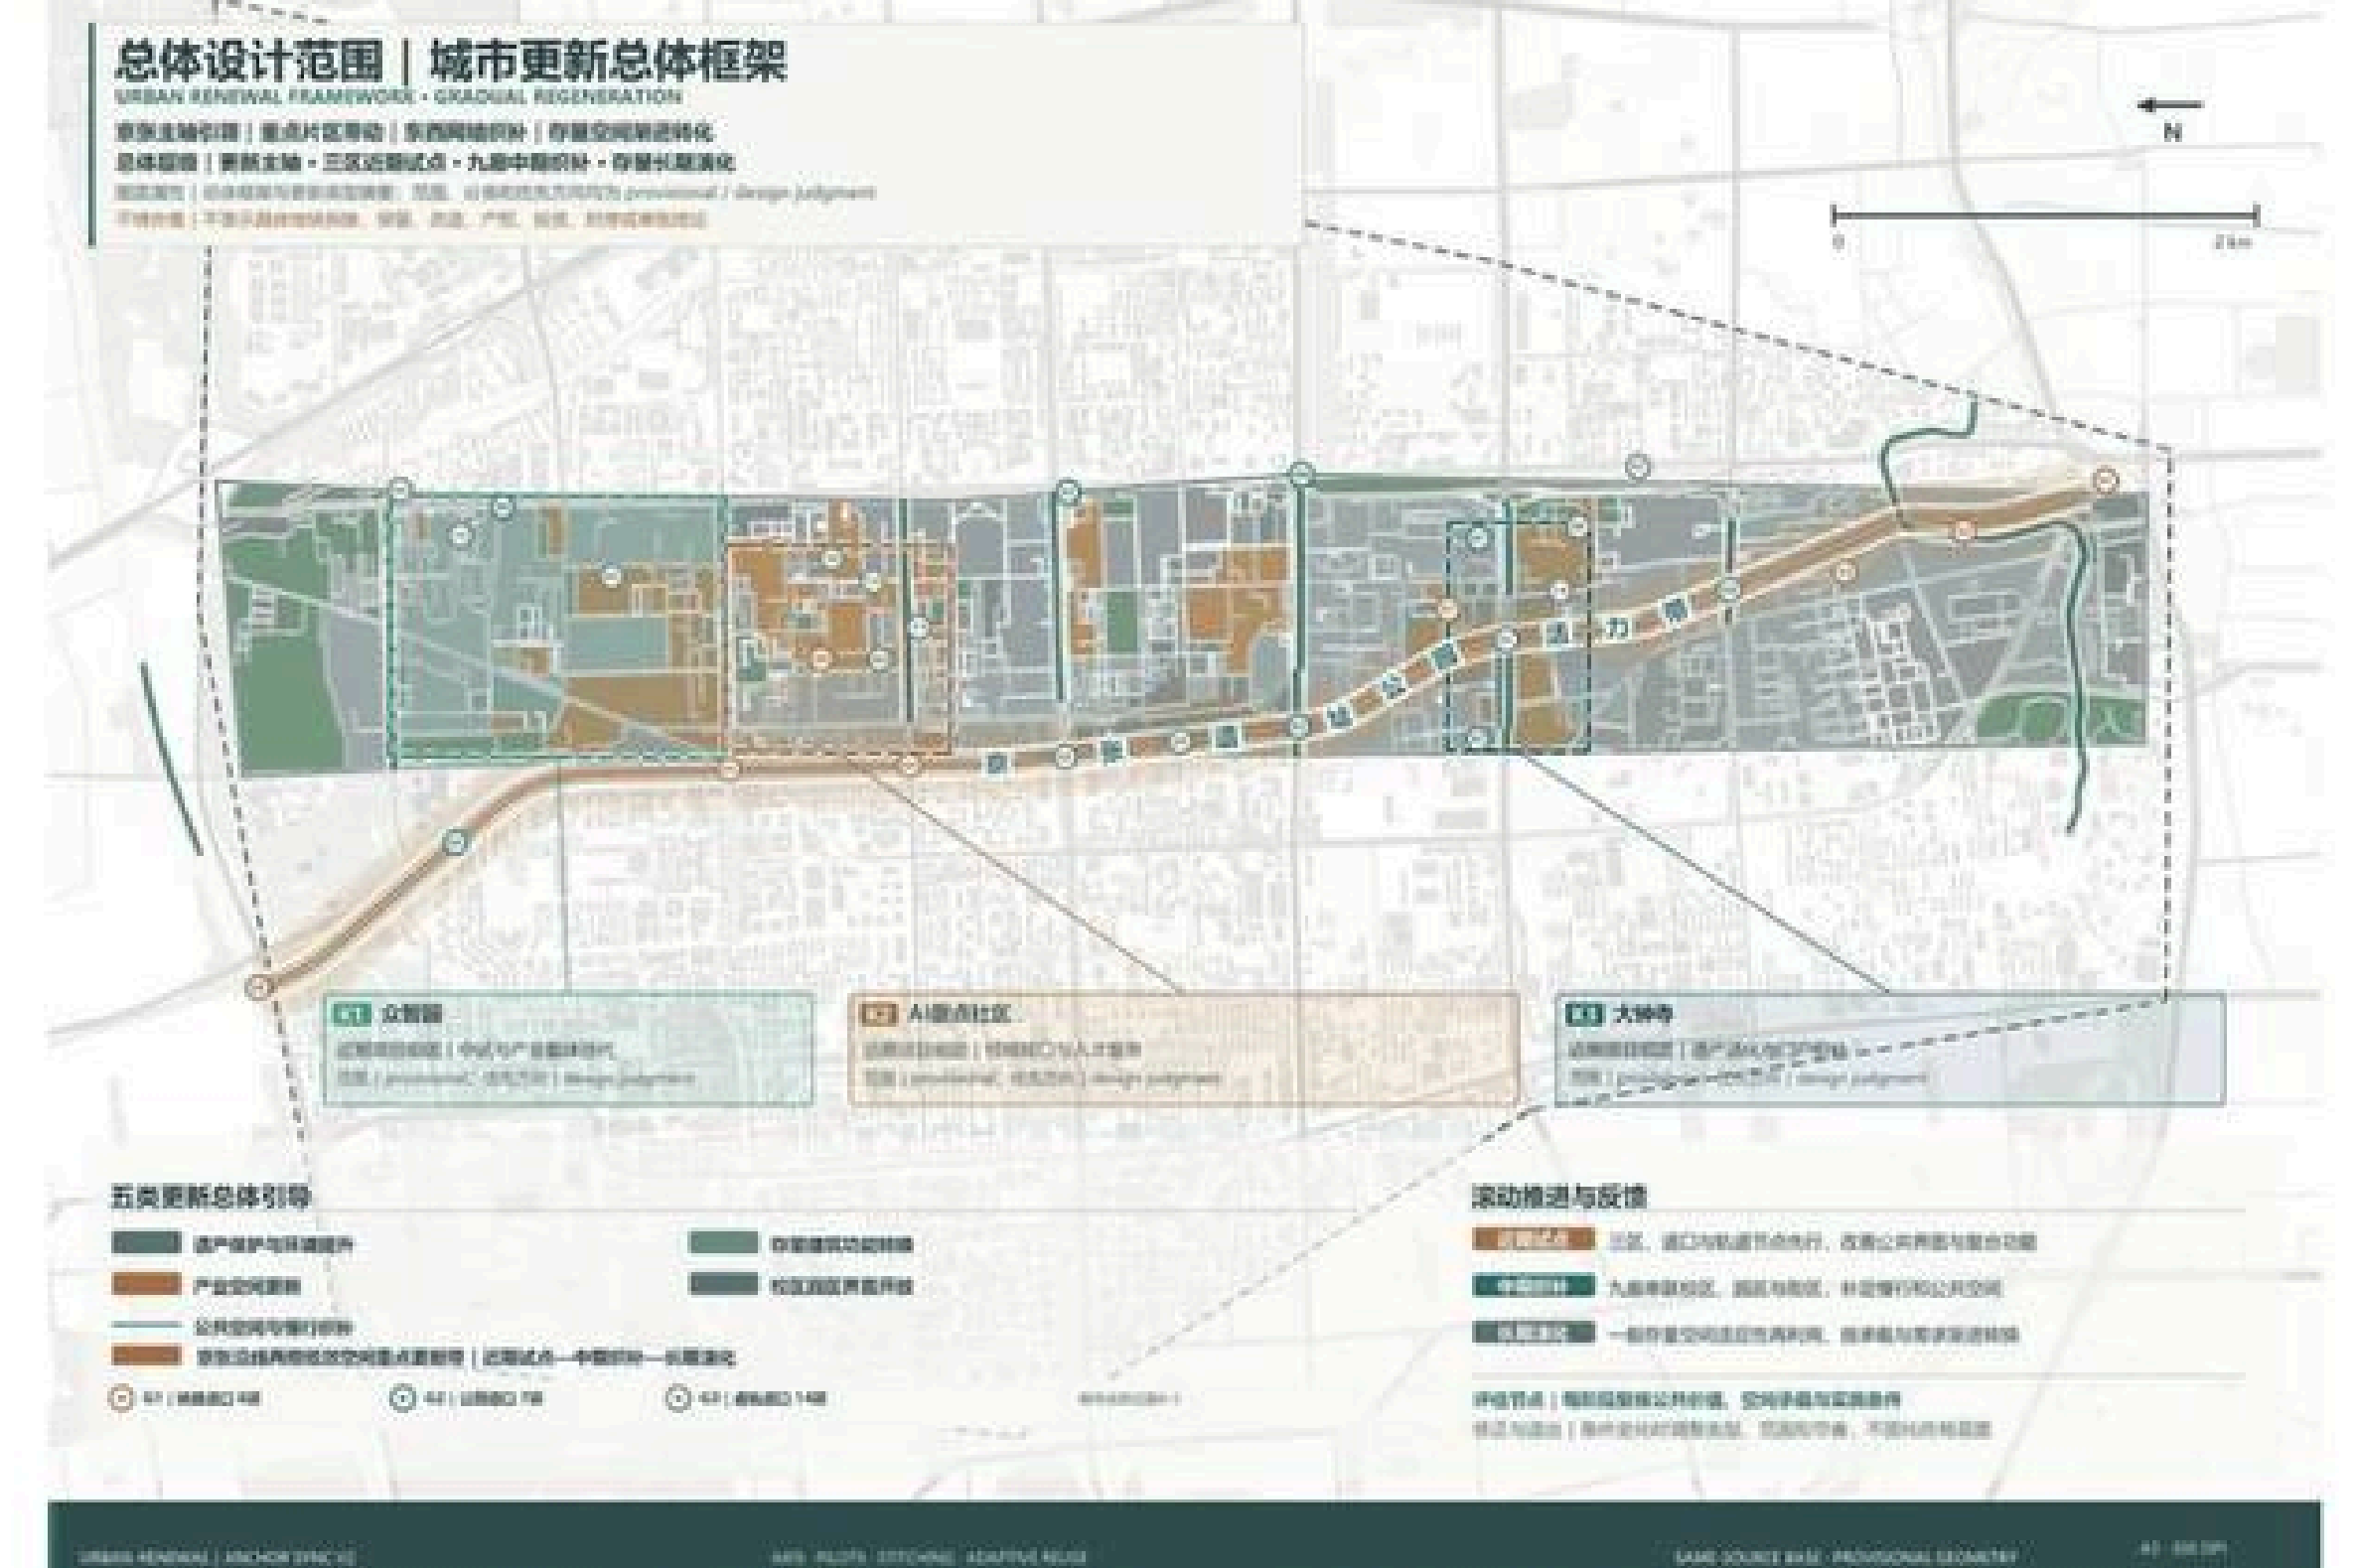


图 A0-2-5 城市更新总体框架图·图4-6

图 A0-3-1 交通—蓝绿公共空间复合系统图（核心图 3）



SC-10 京张铁路记忆导览

开放遗产空间 | 多终端沉浸导览 | 现场即时问答

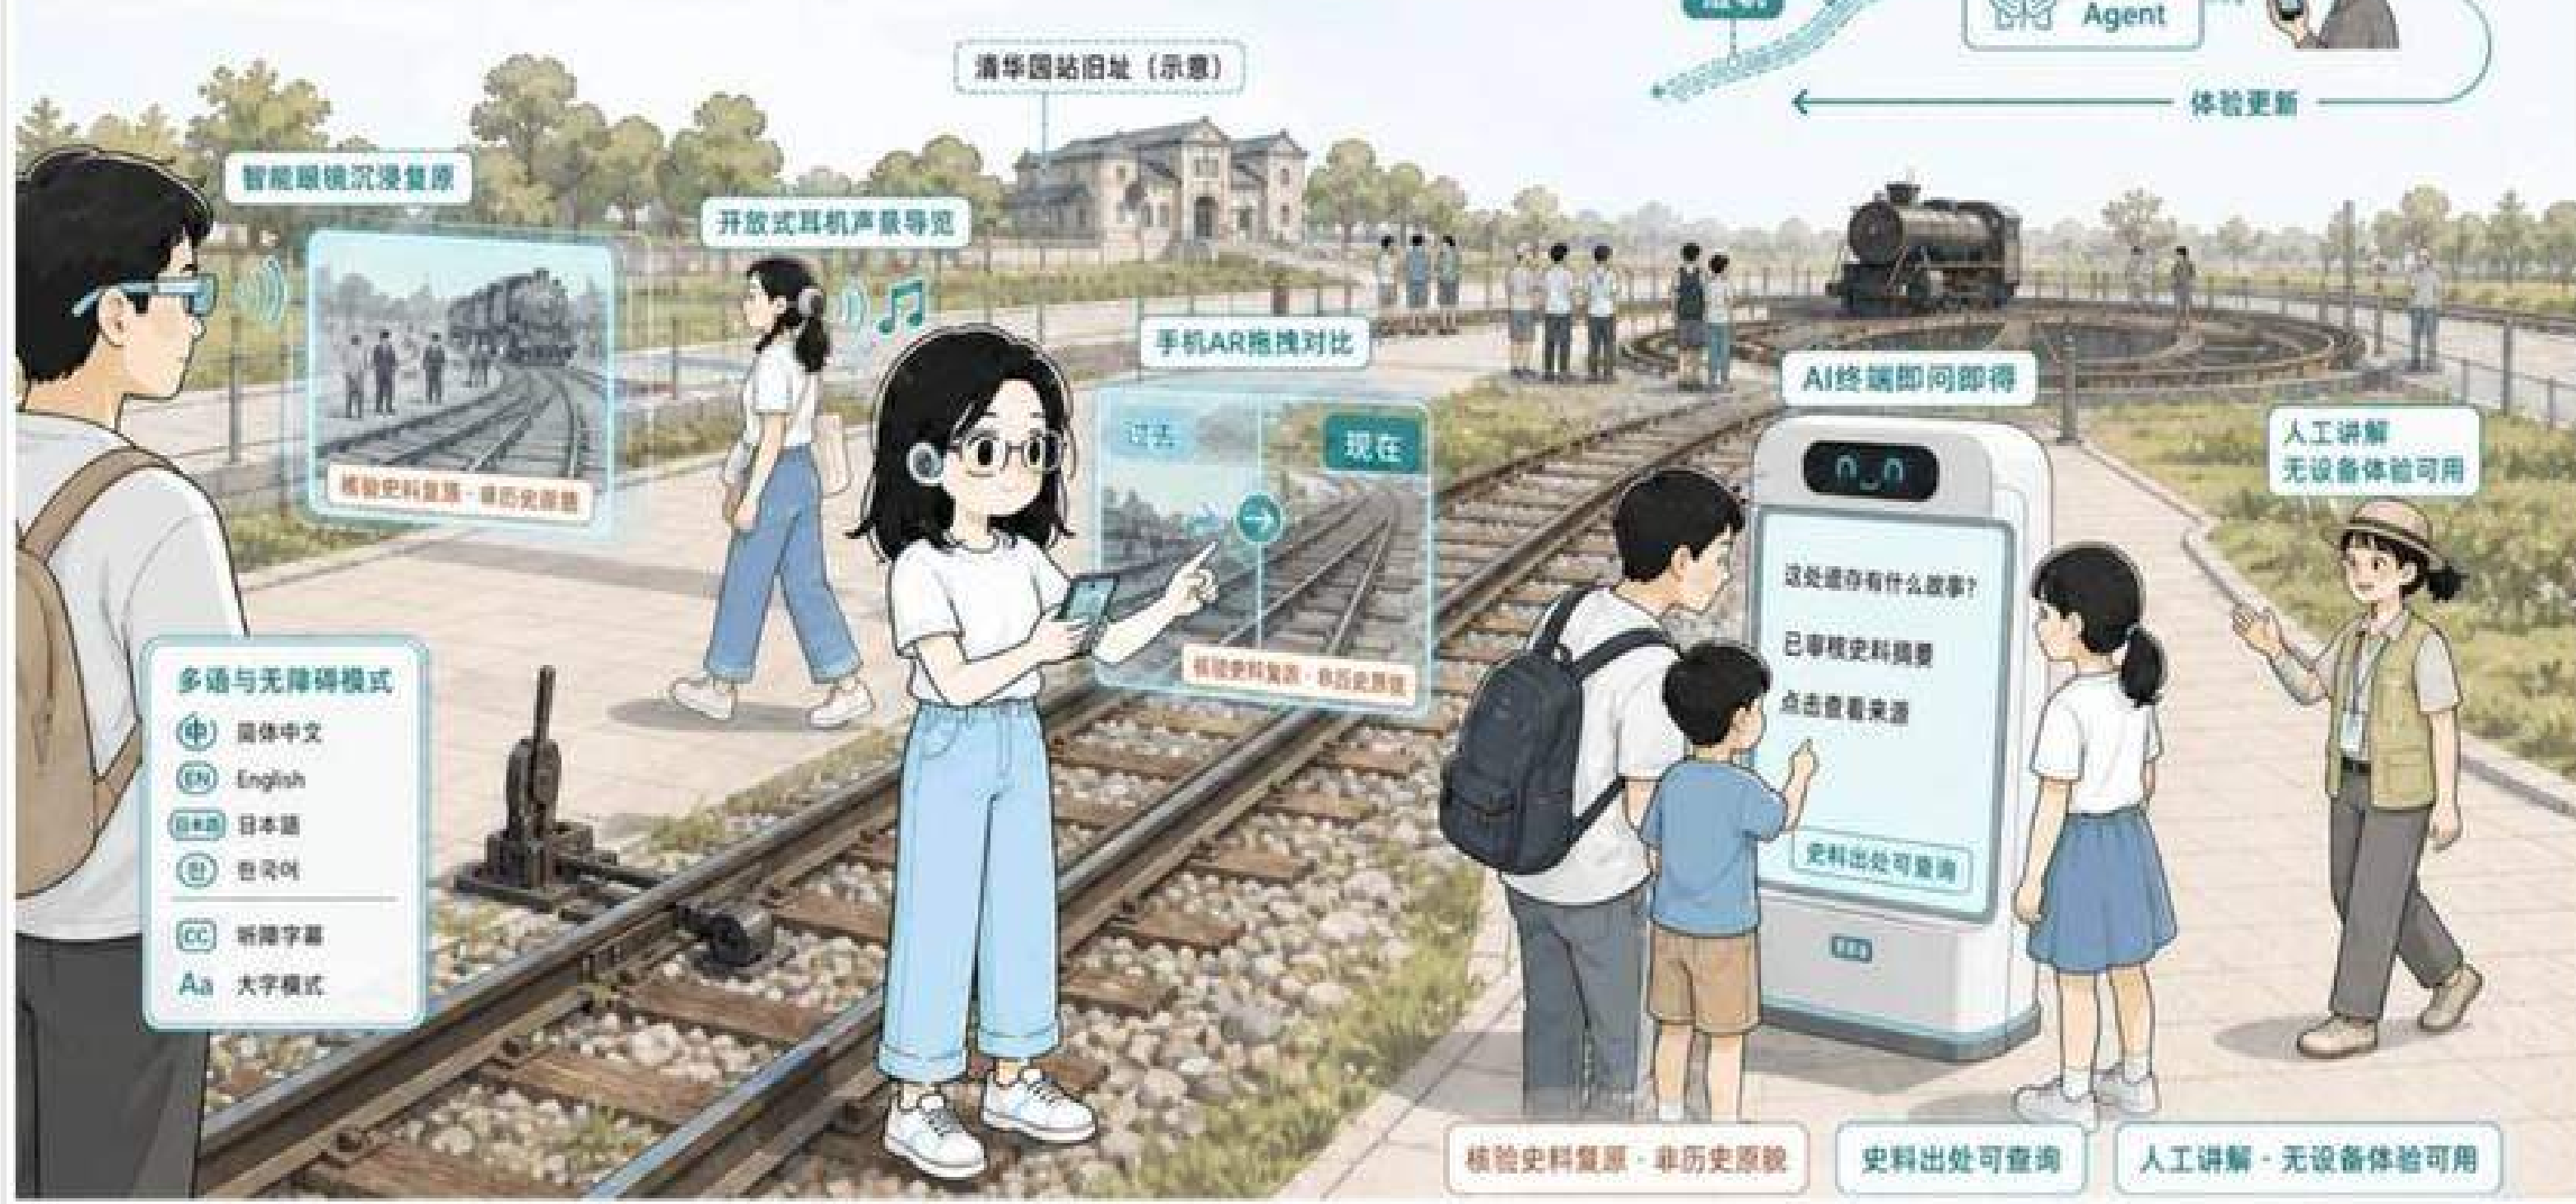


图 A0-3-2 SC-10 京张铁路记忆导览

核心判断

- 南北是连续性问题，东西是可达性问题——京张公园与双轨道走廊已形成南北骨架
- 京张遗址公园承担南北贯通与东西缝合的复合公共空间任务，优先修复慢行断点
- 市政、新型基础设施与端侧算力仅表达概念性空间接口，不下工程可行性结论

关键指标

4 项	最低空间行动（南北连续 / 东西缝合 / 节点强化 / 断点修复） 第08、09章 / source:CH8-TRANSPORT
9 条	九廊横向缝合（跨三至五环、清河、北护城河、学院南路等） 第08章 / depth:traffic_rail_slow_parking
3 处	AI 朝圣地标（可核验贡献·公众参与·可撤回更新） 第06章 表6-4 / data:geometry/public_space



图 A0-3-3 原点社区五道口与京张公园中段活动



图 A0-3-4 众智园学知园站城融合剖面



图 A0-3-5 LM-03 大钟寺“古今共鸣门户”

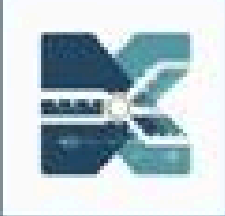


图 A0-4-1 三处重点区域索引与设计任务图（核心图 4）



图 A0-4-2 众智园“AI共试灯塔”共享中试与公众观察

核心判断

- 三区自北向南差异化：众智园中试加速 / 原点社区策源转化 / 大钟寺产业集聚，合计约 368.4 ha
- 众智园“高校核+企业核+共享中试第三极”；原点社区“成果转化网络+低扰动更新”；大钟寺“文化先导→AI 导入”
- 九廊按片区形成三组横向联系：北部园区·郊野·滨水 / 中部高校·园区·社区·站点 / 南部总部·文保·商业·门户

关键指标

192.1	ha 众智园 AI 自主创新加速区 (DK-07) 官方公告约面积 / key_areas.geojson#PROV-KEY-001
104.3	ha 北京 AI 原点社区 (DK-05) 官方公告约面积 / key_areas.geojson#PROV-KEY-002
72.0	ha 大钟寺 AI 产业聚集区 (DK-04) 官方公告约面积 / key_areas.geojson#PROV-KEY-003

A-05-02 | 众智园 AI 自主创新加速区综合详细设计



图 A0-4-3 众智园重点区域综合详细设计

A-05-03 | 北京 AI 原点社区综合详细设计



图 A0-4-4 AI原点社区重点区域综合详细设计

A-05-04 | 大钟寺 AI 产业聚集区综合详细设计



图 A0-4-5 大钟寺重点区域综合详细设计

图 A0-5-1 AI 创新生态与场景闭环 (第06章主图)

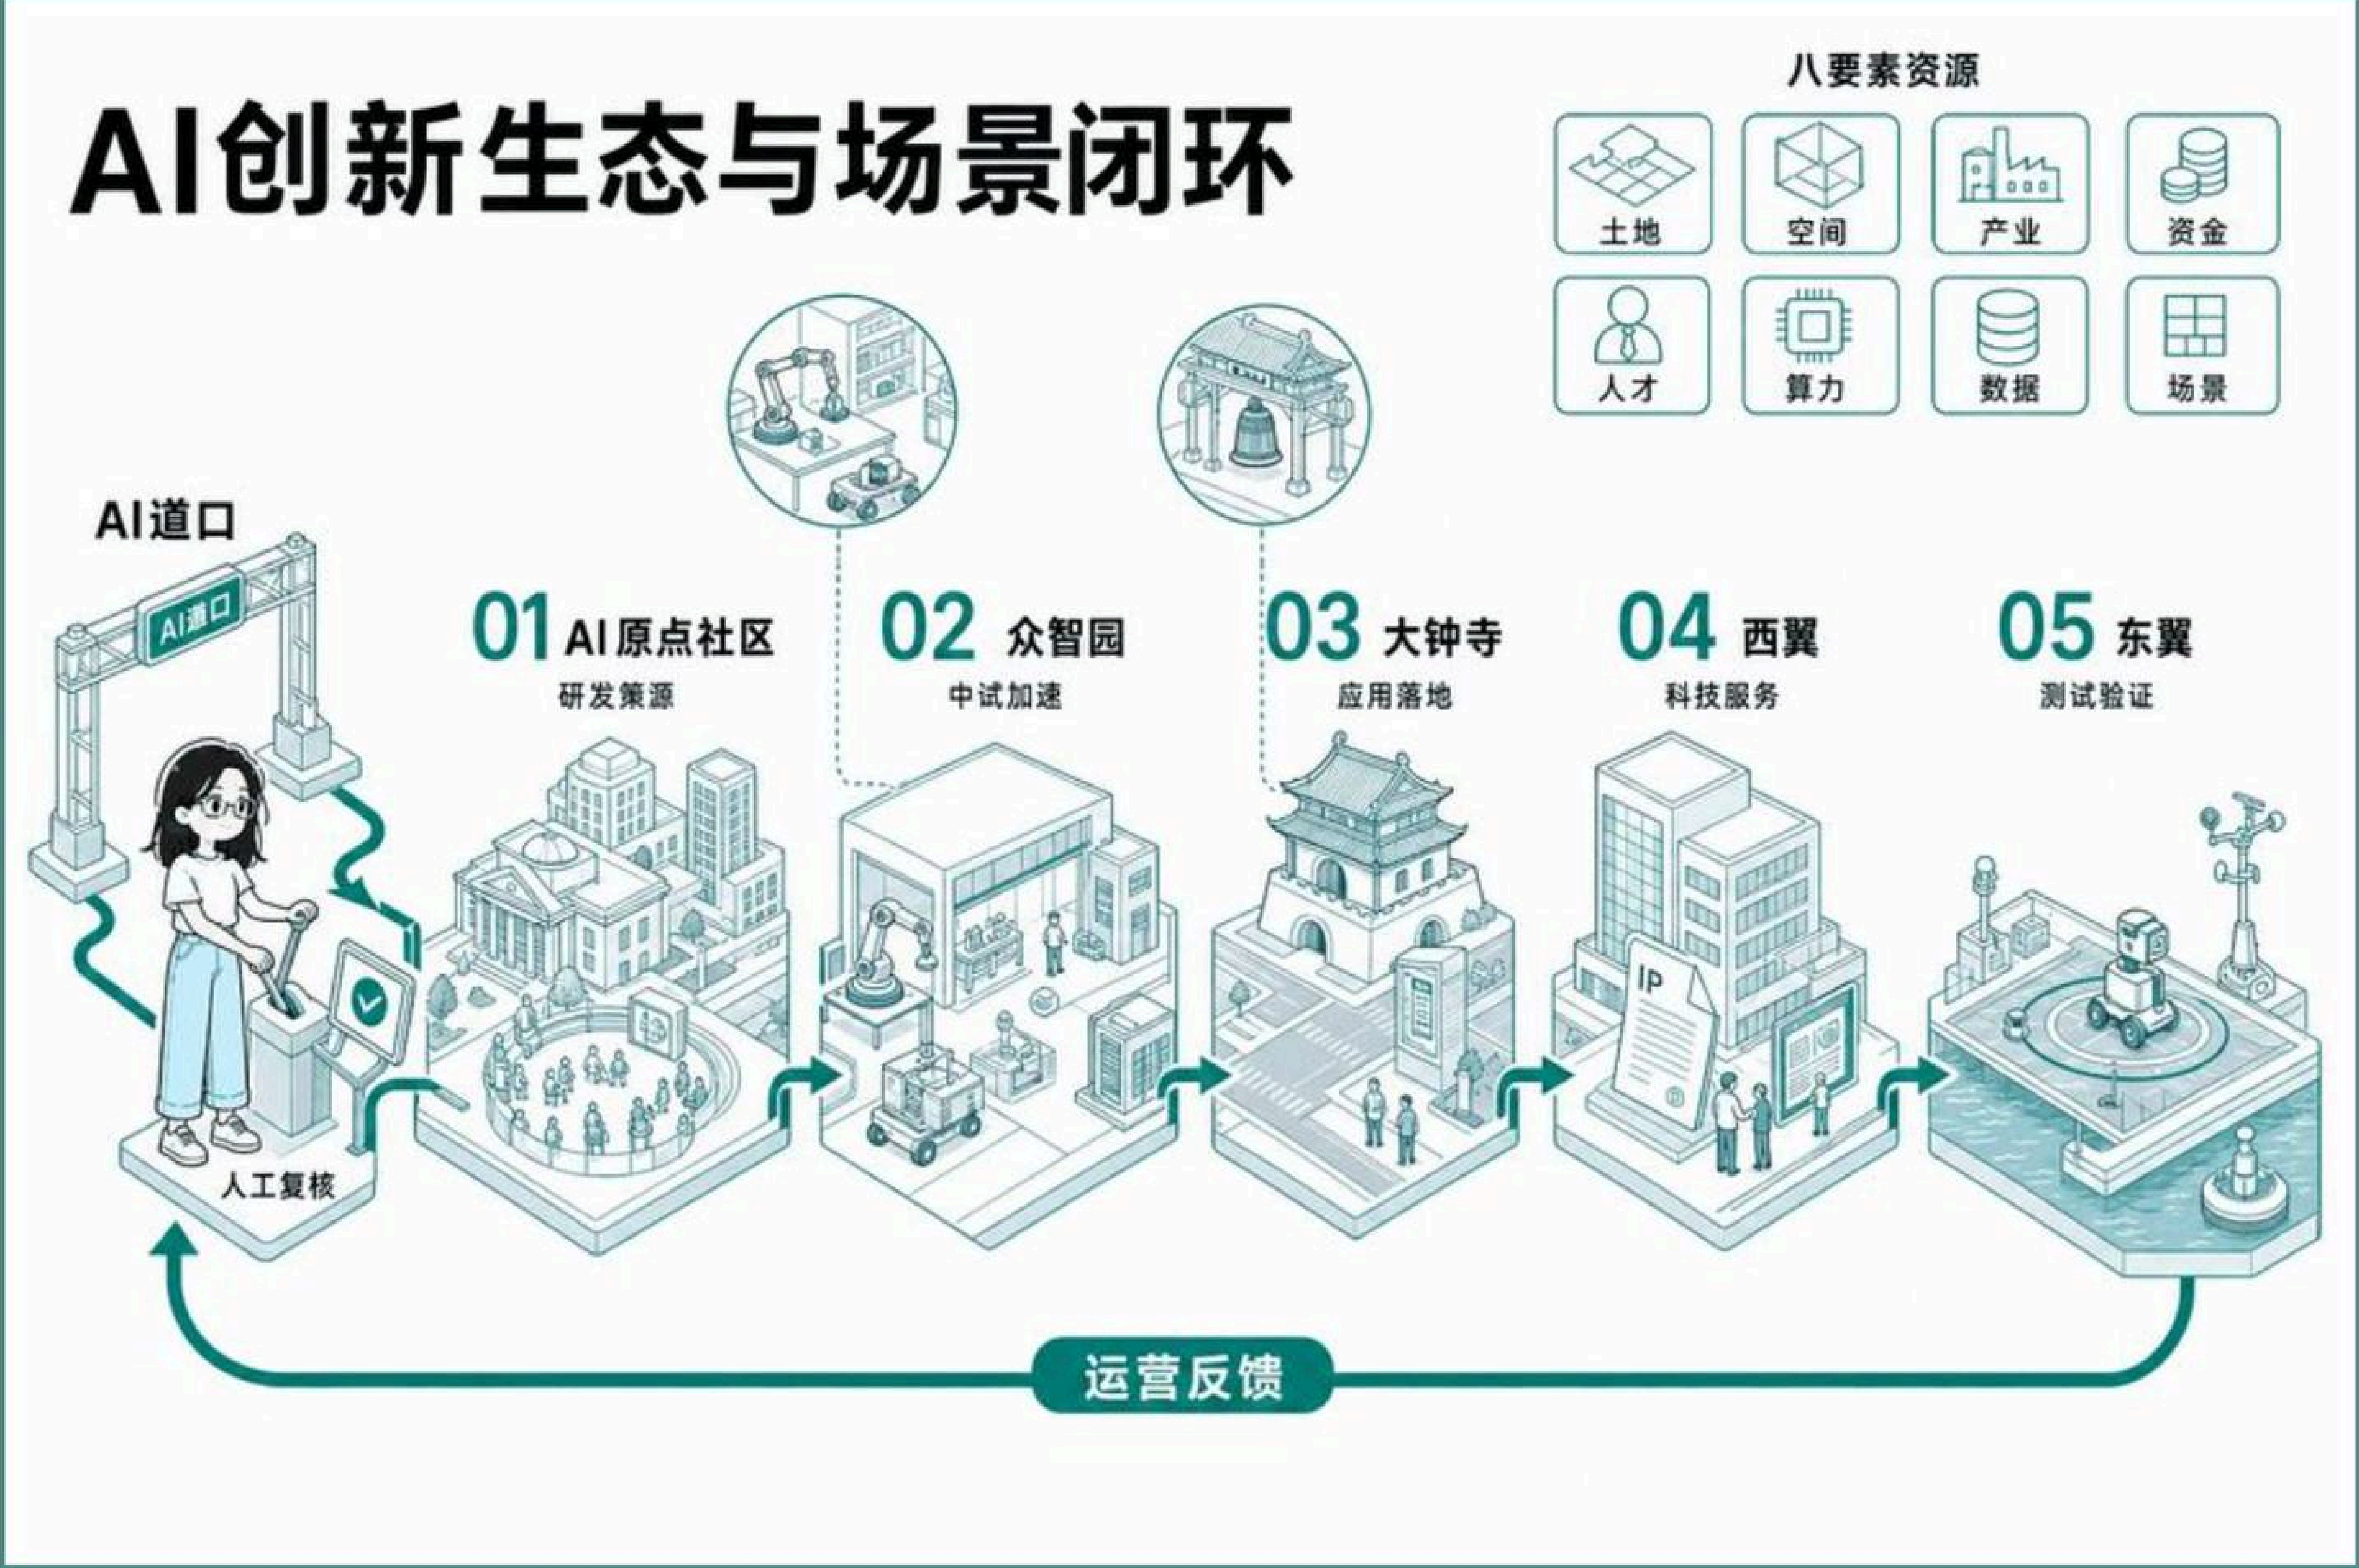


图 A0-5-2 AI原点“开源共创星图”开放共创与公共议事

核心判断

- 以五类空间角色承接八类创新资源，形成 AI 创新生态与场景闭环
- 人工复核、非数字替代与退出复原是场景开放的共同底线
- 分期按证据与治理成熟度排序而非日历，无证据的成功叙事不触发扩展

关键指标

12 张	AI 场景卡 (SC-01 ~ SC-12) 第06章 / source:CH6-SCENARIO-ASSETS
5 类	空间角色与用户节律 第06章 图6-2 / source:CH6-SCENARIO-BASELINE
3 处	AI 朝圣地标 (LM-01 ~ LM-03) 第06章 表6-4



图 A0-5-3 SC-01 AI 创新客厅场景卡

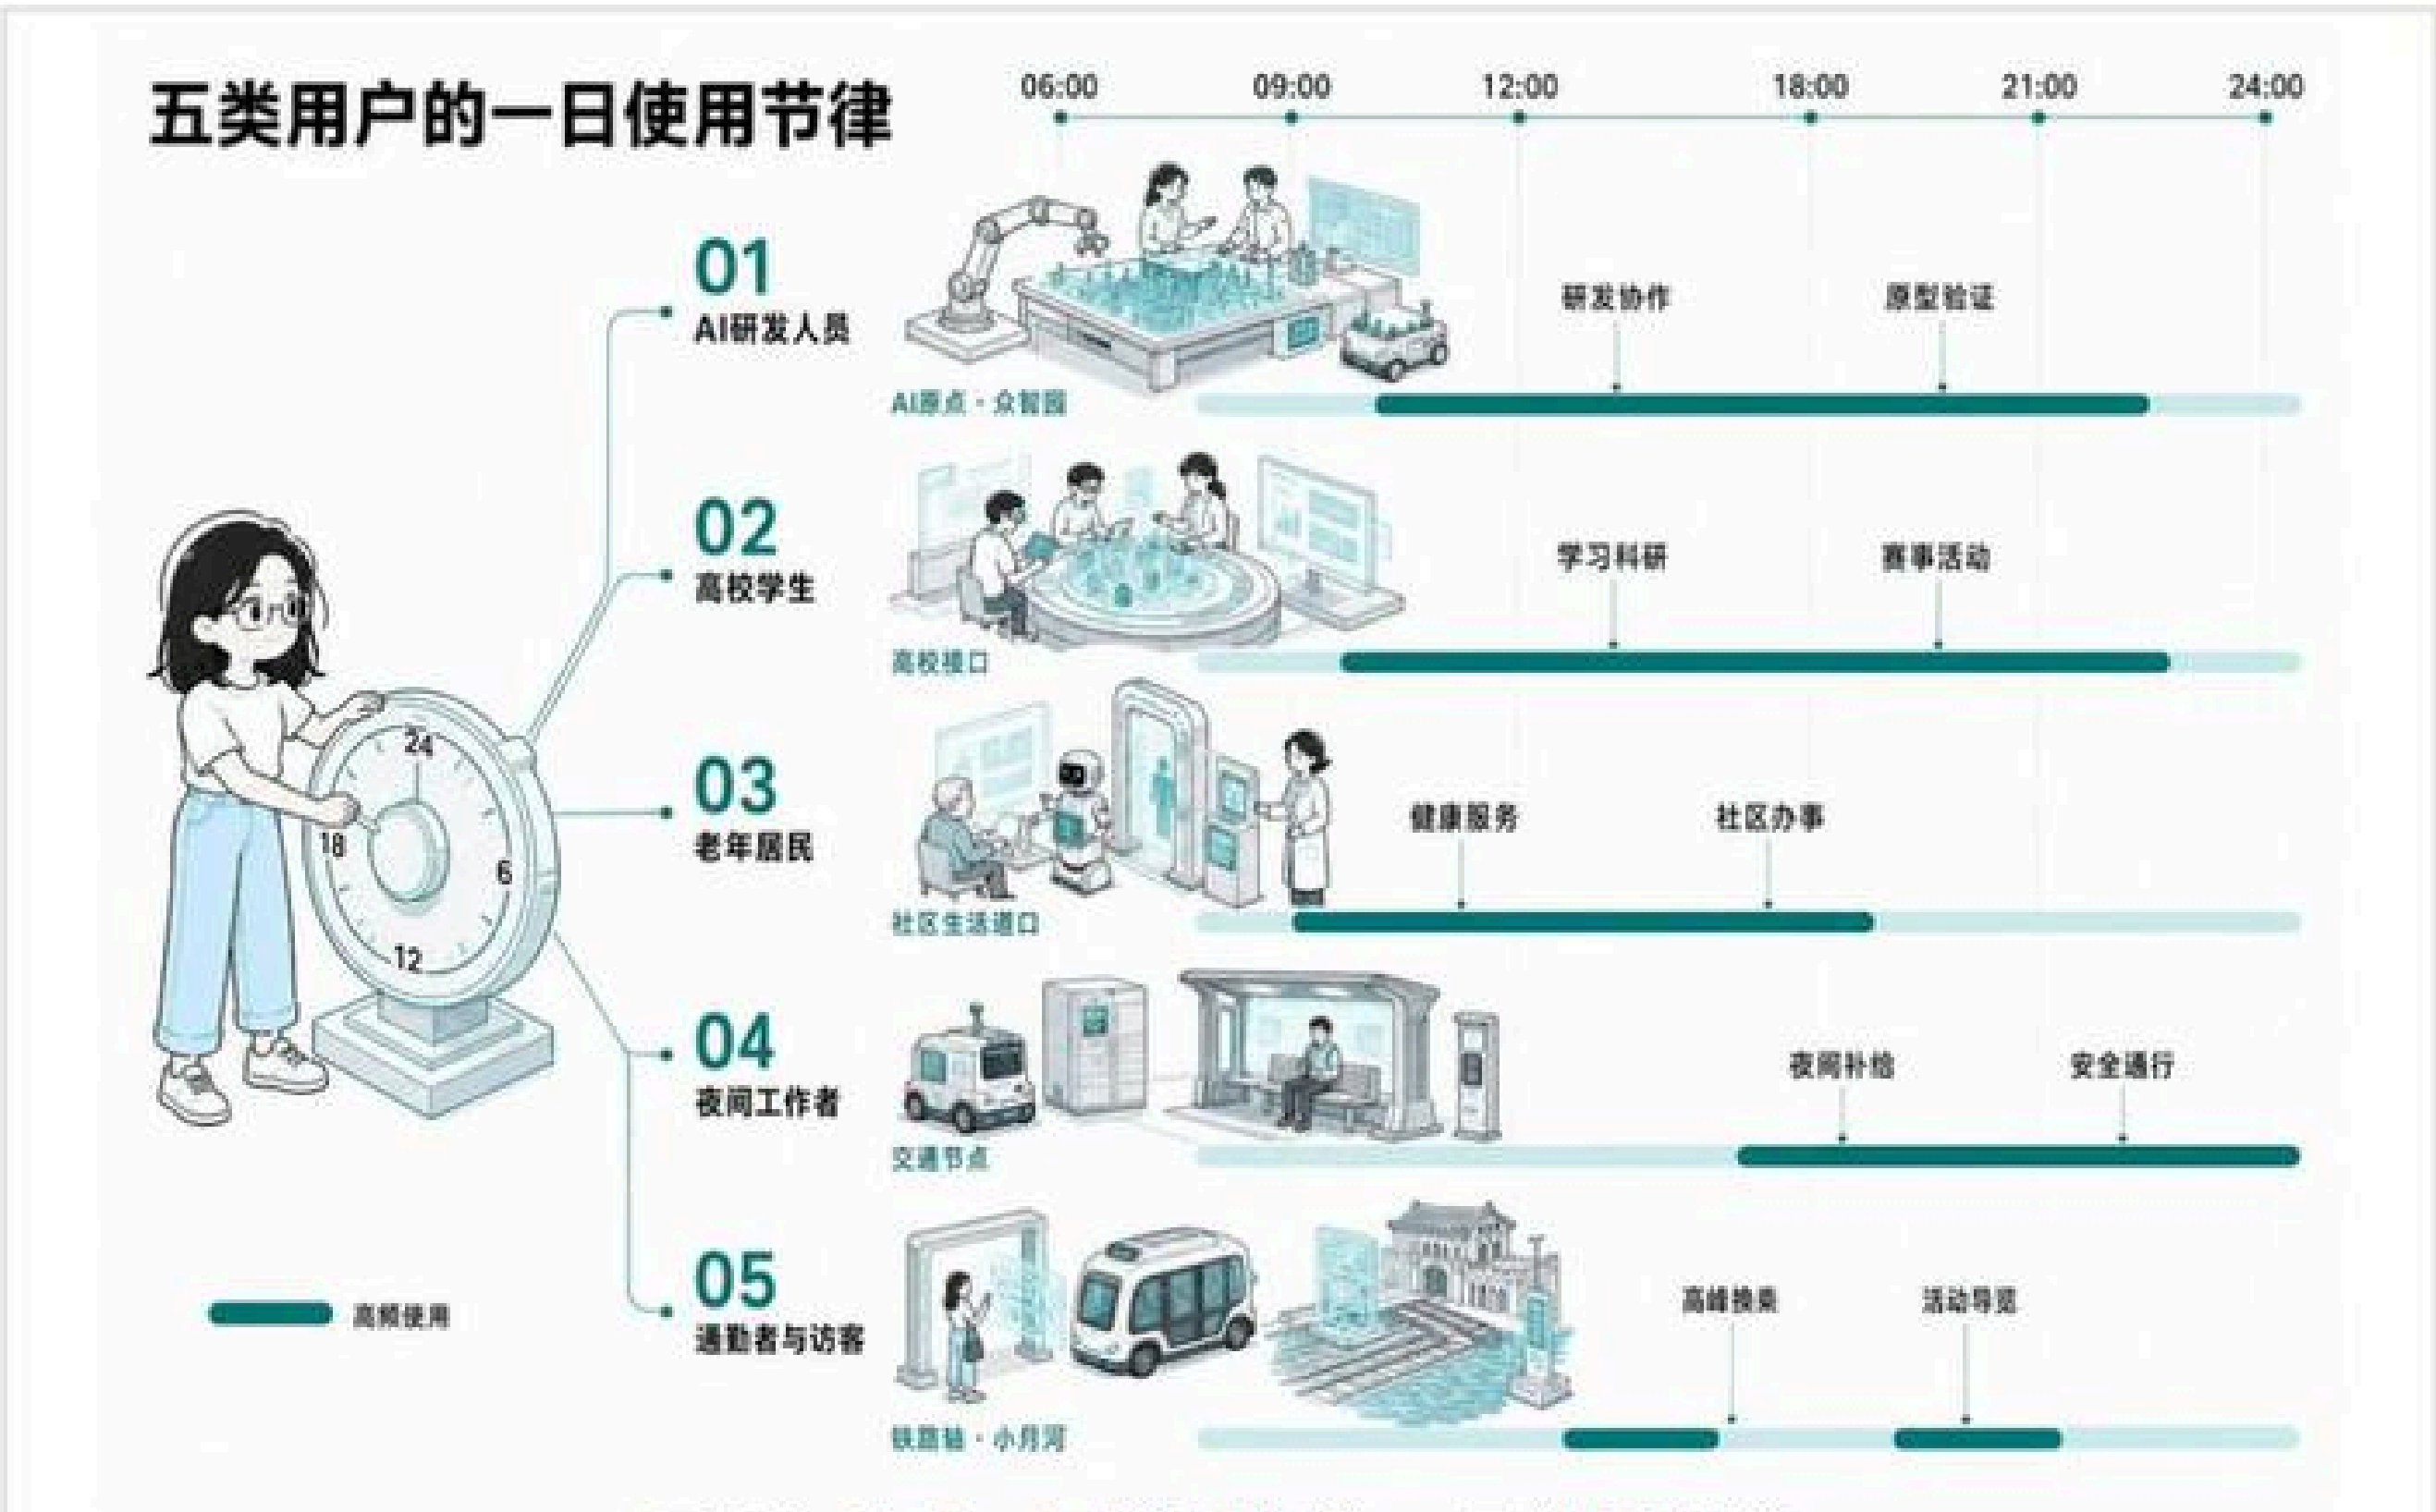


图 A0-5-4 五类用户的一日使用节律



图 A0-5-5 分期逻辑三段式：证据成熟度排序

图 A0-6-1 核心指标复算与任务证据链 (核心图 5)

核心指标复算与任务证据链

来源—几何—复算—指标—审查

任一环节变化，均按同一证据链重置；
临时模型不替代官方红线与法定指标。



企业·人才·产值三阶段方案目标 (T0=100)			
	近期试点	中期织补	长期演化
企业有效聚集	110	125	140
人才空间密度	108	120	130
场地AI产值	115	140	170

- 方案目标为参赛情景阈值，不是官方预测或政府承诺；取得统一T0台账后换算绝对值。
- 当前边界与核心空间指标为 provisional 低置信度设计模型；正式数据变化后全链路重置。



分层自检状态
中文内容自检：通过

四道本地闸门：
全部通过

设计深度：15/15

图 A0-6-2 来源—主张—空间—指标—成果证据链

来源—主张—空间—指标—成果
证据链

任一环节缺失时降为 provisional / unknown，
不用来源数量替代证据链质量



缺口与复核 ASSUMPTION / GAP
数据不确定性·专业核验条件与替换触发器；缺失值保持 unknown，不以推测填充。

核心判断

- 建立“公告任务指标—空间模型指标—产业运营指标—合规审查指标”四层体系
- 复算由提交 GeoJSON 在 EPSG:4548 下得出，属低置信度方案模型值
- 任务矩阵覆盖 23 项必选要求与 agent.1—agent.6；标准矩阵共 7 项（强制 6 项），强制项 6/6 已响应

关键指标

11.49	km² 总体范围几何复算 metric:site_area_sqm / known-low confidence
368.79	ha 三处重点区合计复算 第11章 / 临时约束范围
6 / 6	项 强制标准已响应 (总 7-强制 6) 第11章 / 23项必选 + agent.1—6

区域创新协同流程

从真实需求进入，到空间行动反馈回流



图 A0-6-3 区域创新协同流程

SC-04 公共算力服务窗口

AI原点·众智圈 | 算力服务 | 近期可试点



图 A0-6-4 SC-04 公共算力服务窗口

SC-09 小月河生态感知与滨水预警站

小月河滨水空间 | 生态感知与预警 | 规划测试

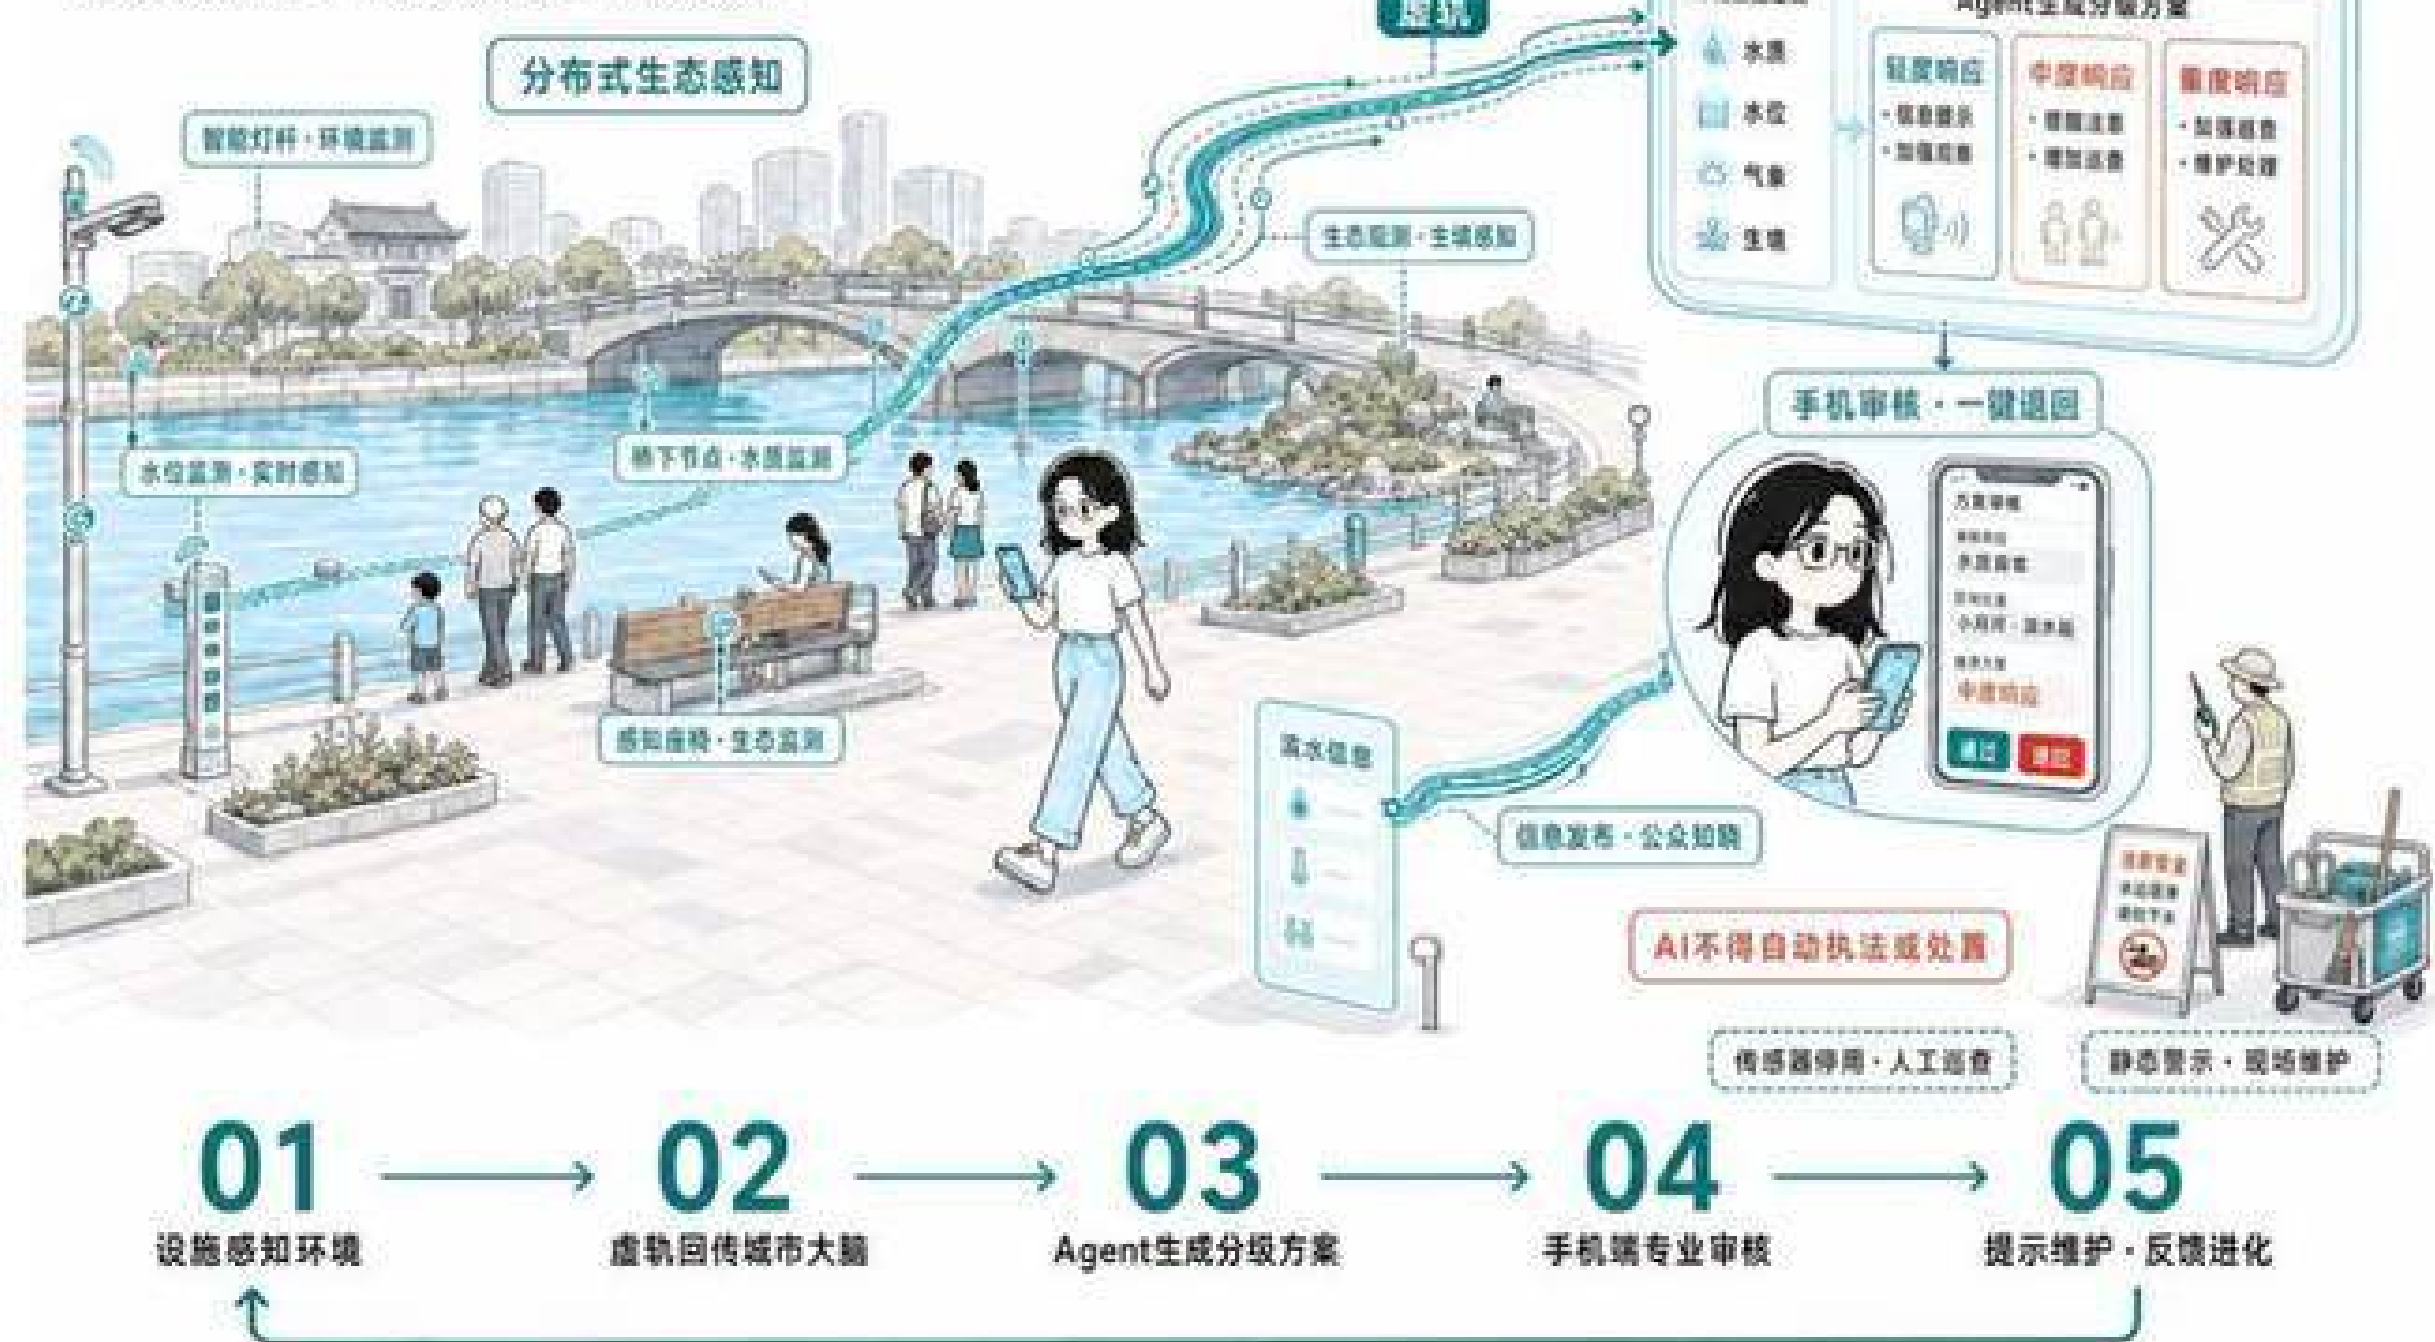


图 A0-6-5 SC-09 小月河生态感知与滨水预警站