



# 总览地图 · 智轨走廊城市设计提案

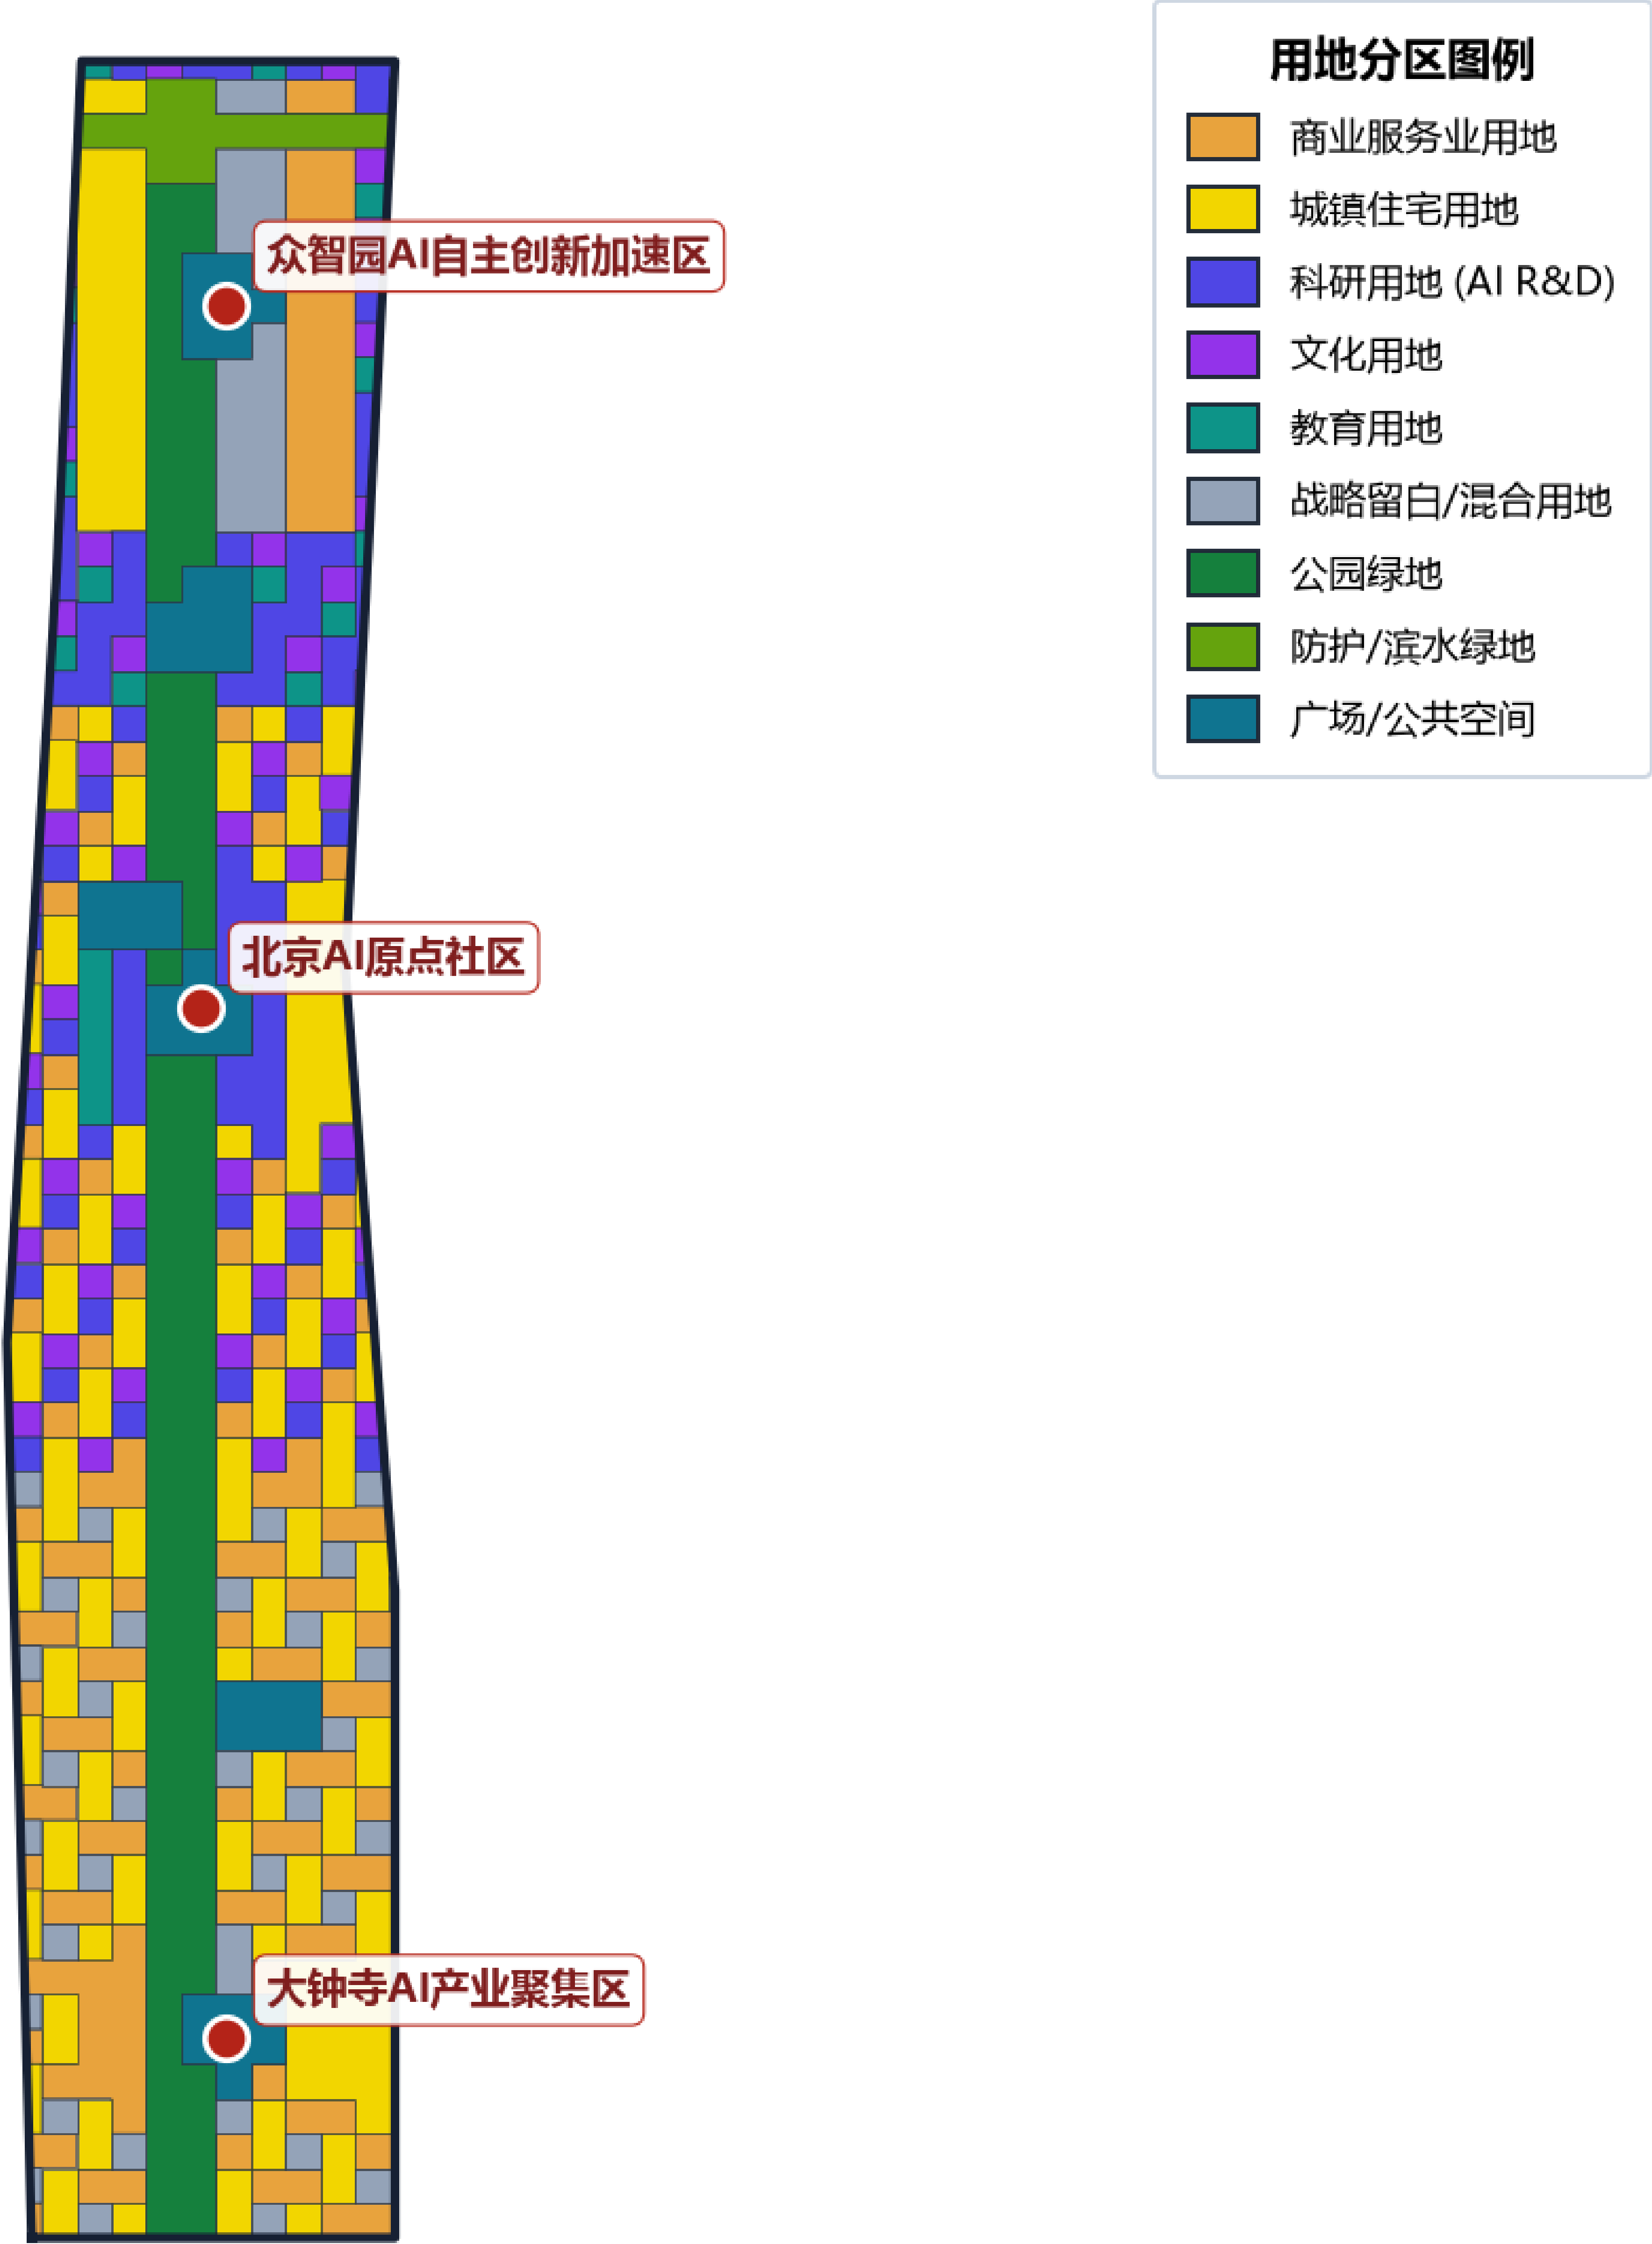

用地分区结构

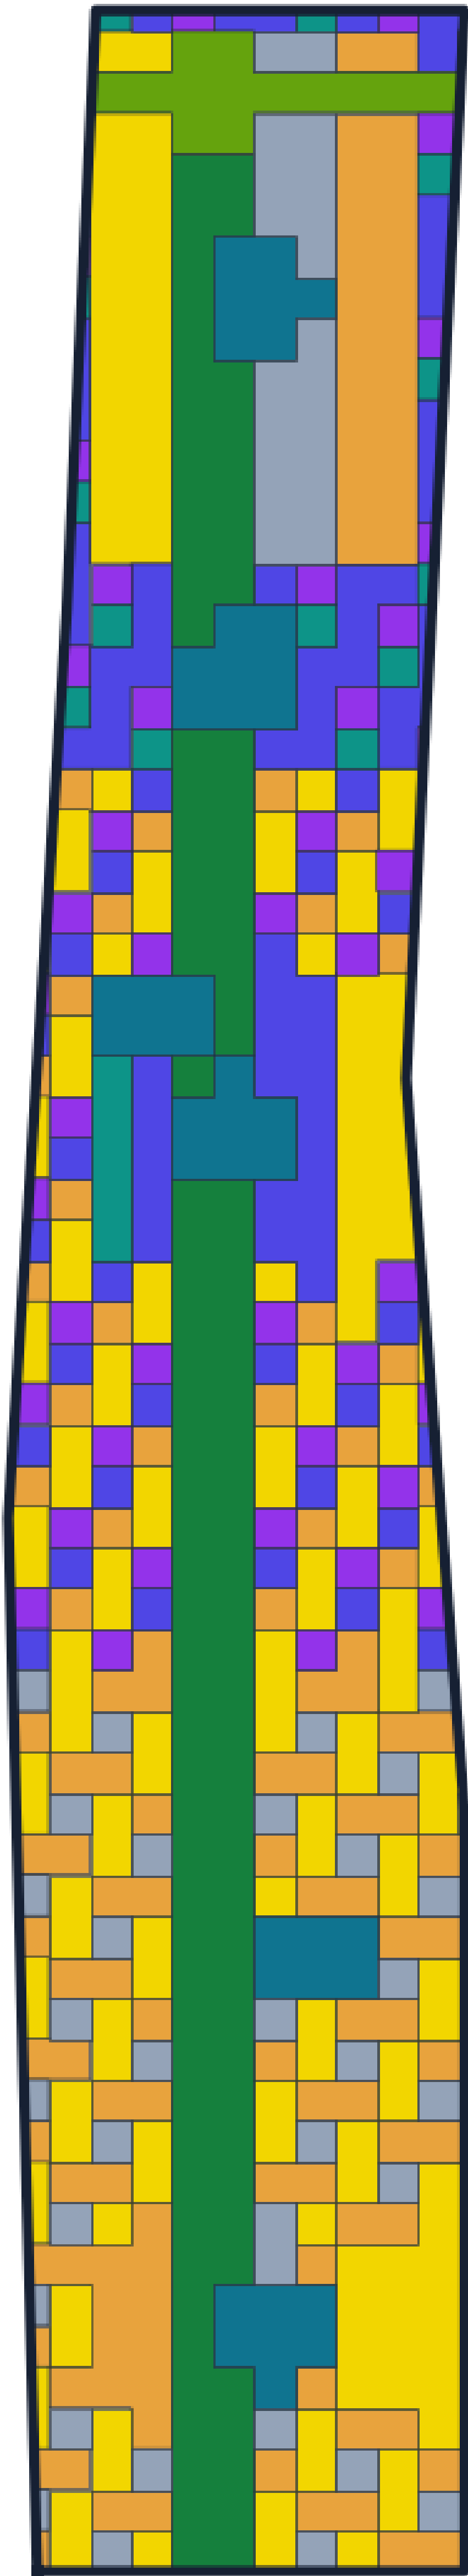

用地结构（按单元数排序）

- 商业服务业用地（75 单元）
- 城镇住宅用地（70 单元）
- 科研用地 (AI R&D)（44 单元）
- 文化用地（43 单元）
- 教育用地（14 单元）
- 战略留白/混合用地（40 单元）
- 公园绿地（4 单元）
- 防护/滨水绿地（1 单元）
- 广场/公共空间（6 单元）


三处重点区域详细设计




注：重点区域边界为 provisional\_constraint，非组织方法定红线。

图例说明

交通慢行·蓝绿公共空间复合系统

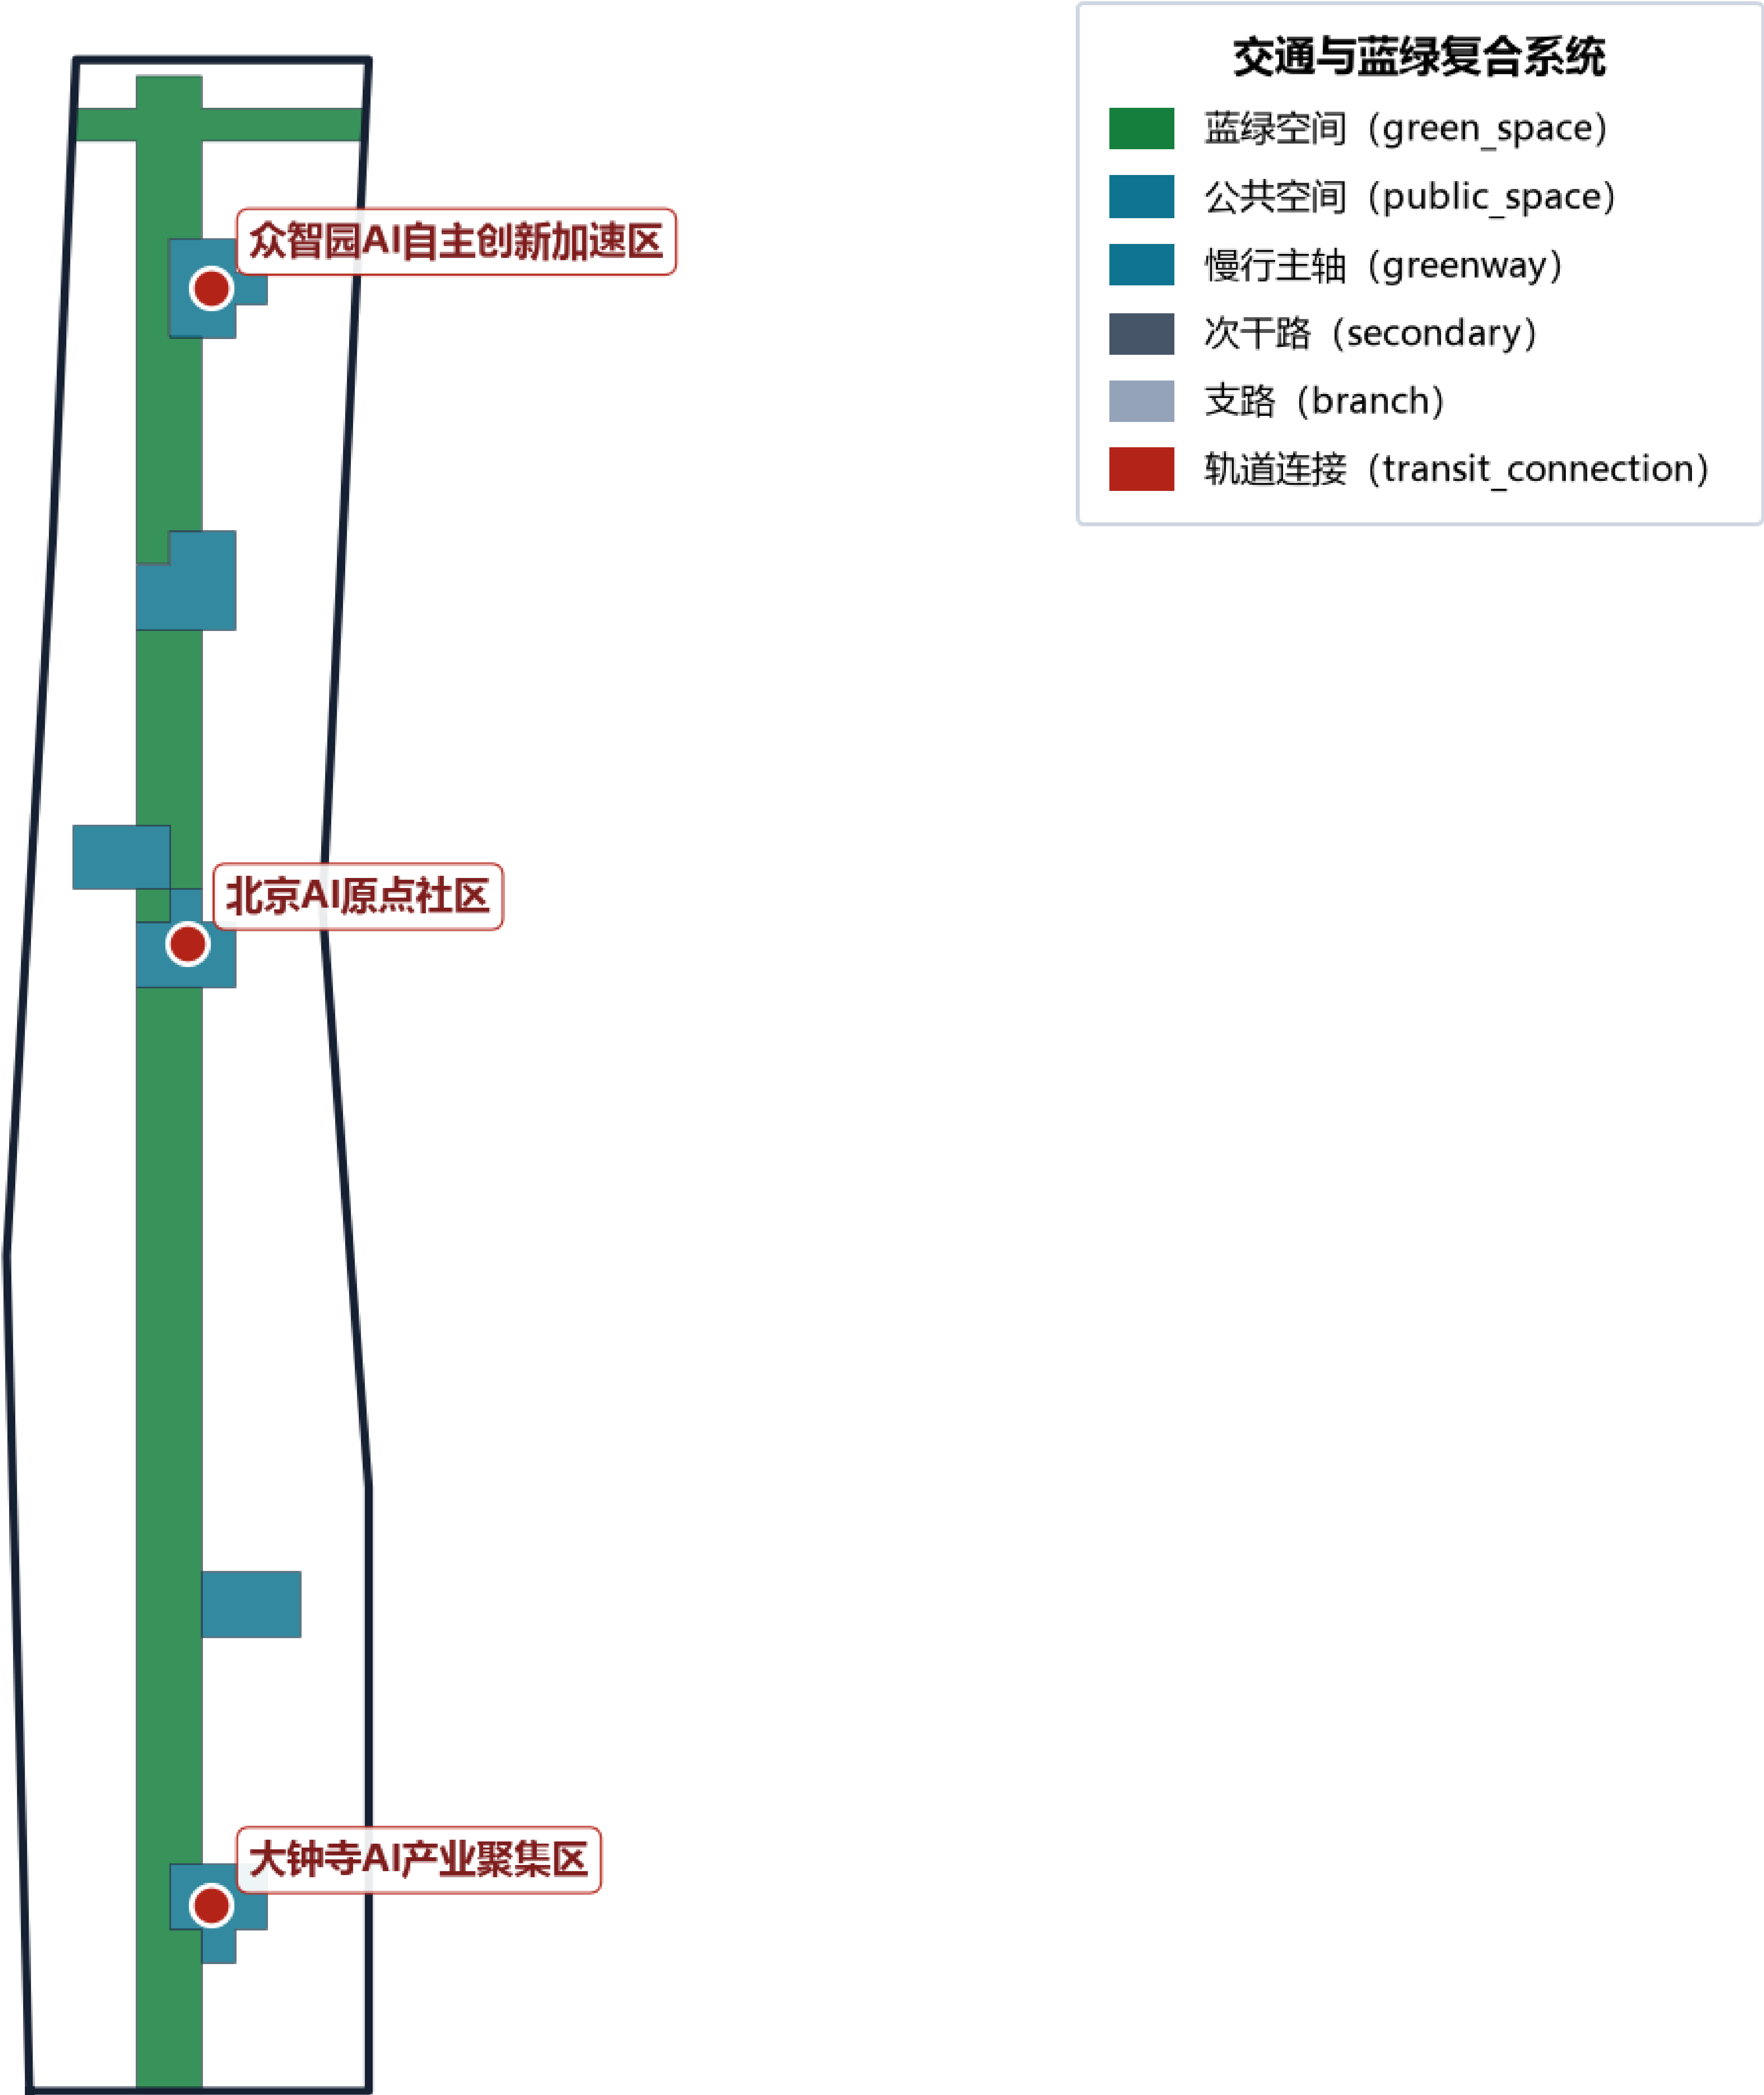

## 核心指标复算证据

 

绿地率 18.6% 公共空间占比 6.7% 建筑密度 27.2%

比例指标由 GeoJSON 投影面积 (EPSG:4548) 复算; 精度受 provisional boundary 限制。

|                                                |   |         |
|------------------------------------------------|---|---------|
| GeoJSON EPSG:4548                              |   |         |
|                                                |   | ( )     |
|                                                |   | 1141.3  |
|                                                |   | 211.9   |
|                                                |   | 76.2    |
|                                                |   | 310.6   |
|                                                | % | 18.6    |
|                                                | % | 6.7     |
|                                                | % | 27.2    |
|                                                |   | 3       |
|                                                |   | 369.3   |
|                                                |   | 1141.3  |
| floor_area_ratio / /                           | — | unknown |
| provisional_constraint=official_boundary=false |   | unknown |