

百年京张AI创新带城市设计开源征集

京张智脉共生带


JingZhang AI Symbiosis Belt

一带一链 · 三核两翼 · 多点场景 | 专业城市设计方案 (formal professional design package)

边界状态：provisional_constraint (intake only) — official 边界发布后需复算全部图层与指标


总览地图：一带一链·三核两翼·多点场景

证据来源：geometry/*.geojson + metrics.json + proposal.md

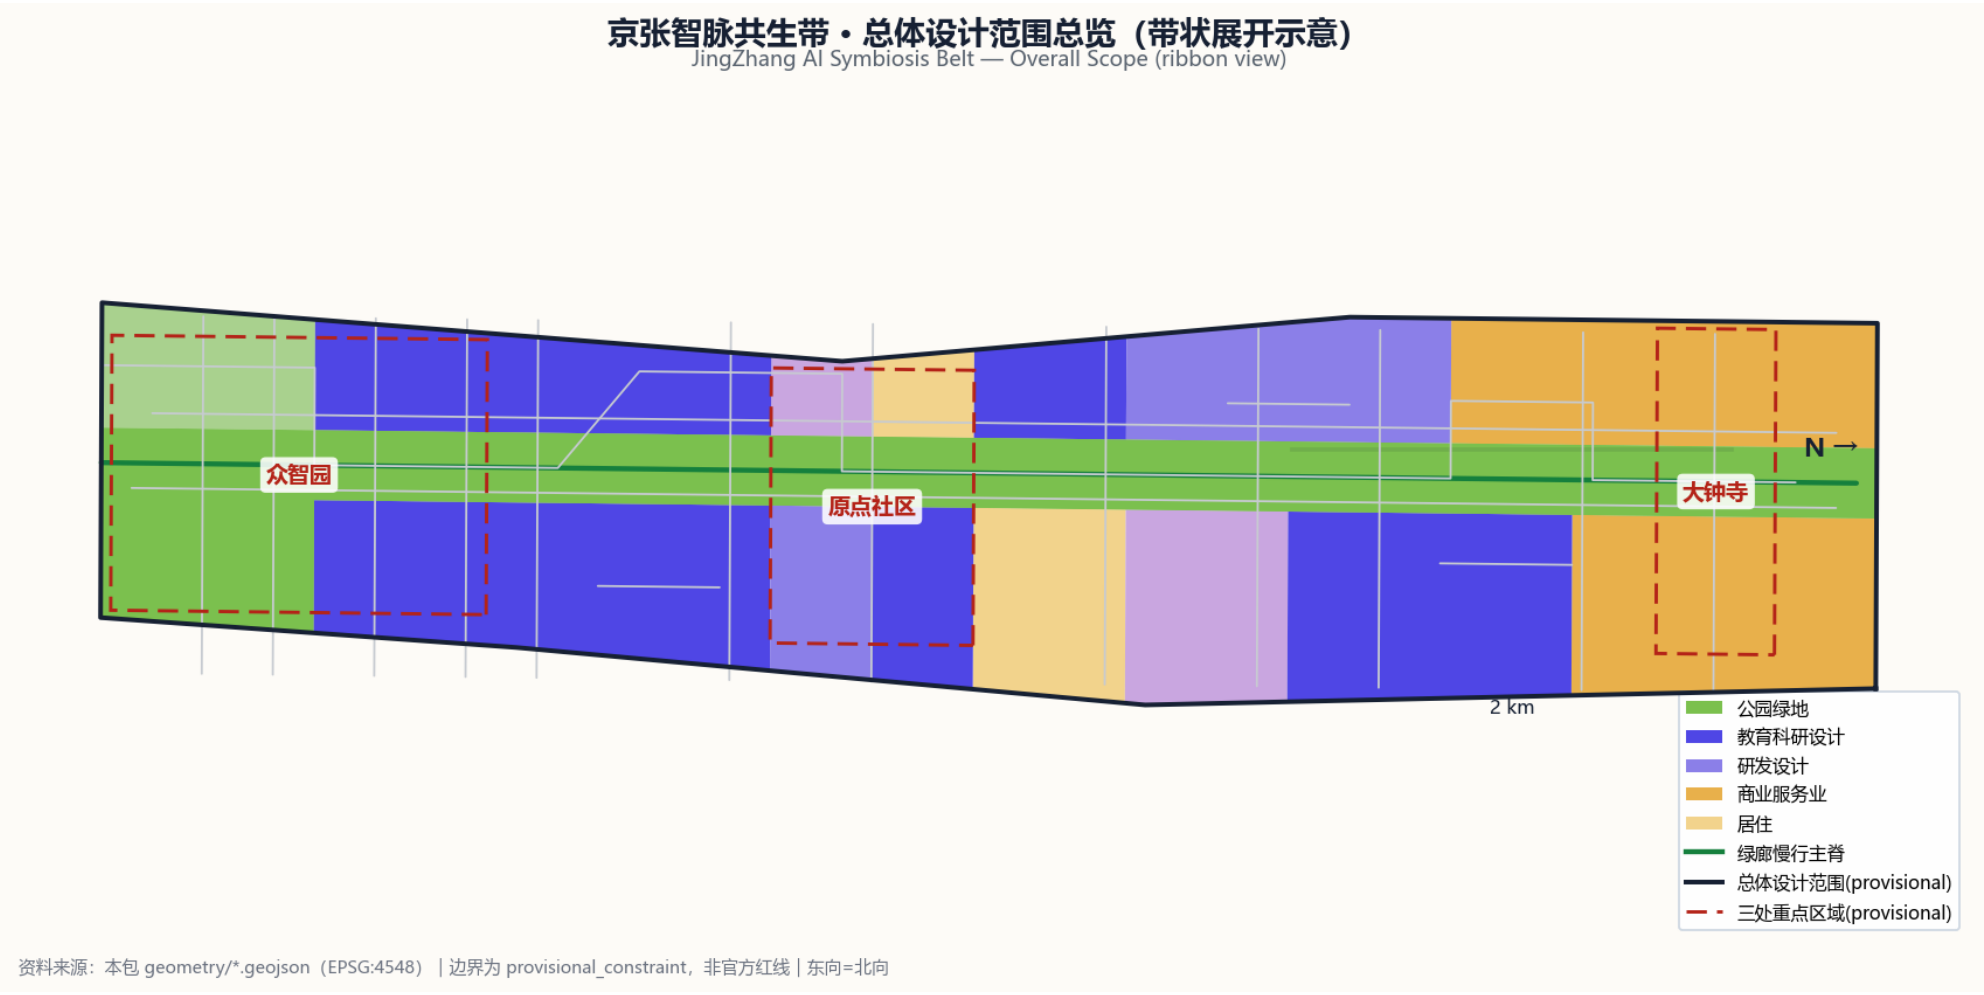

用地结构：产业功能比例与用地分区




证据来源：geometry/*.geojson + metrics.json + proposal.md

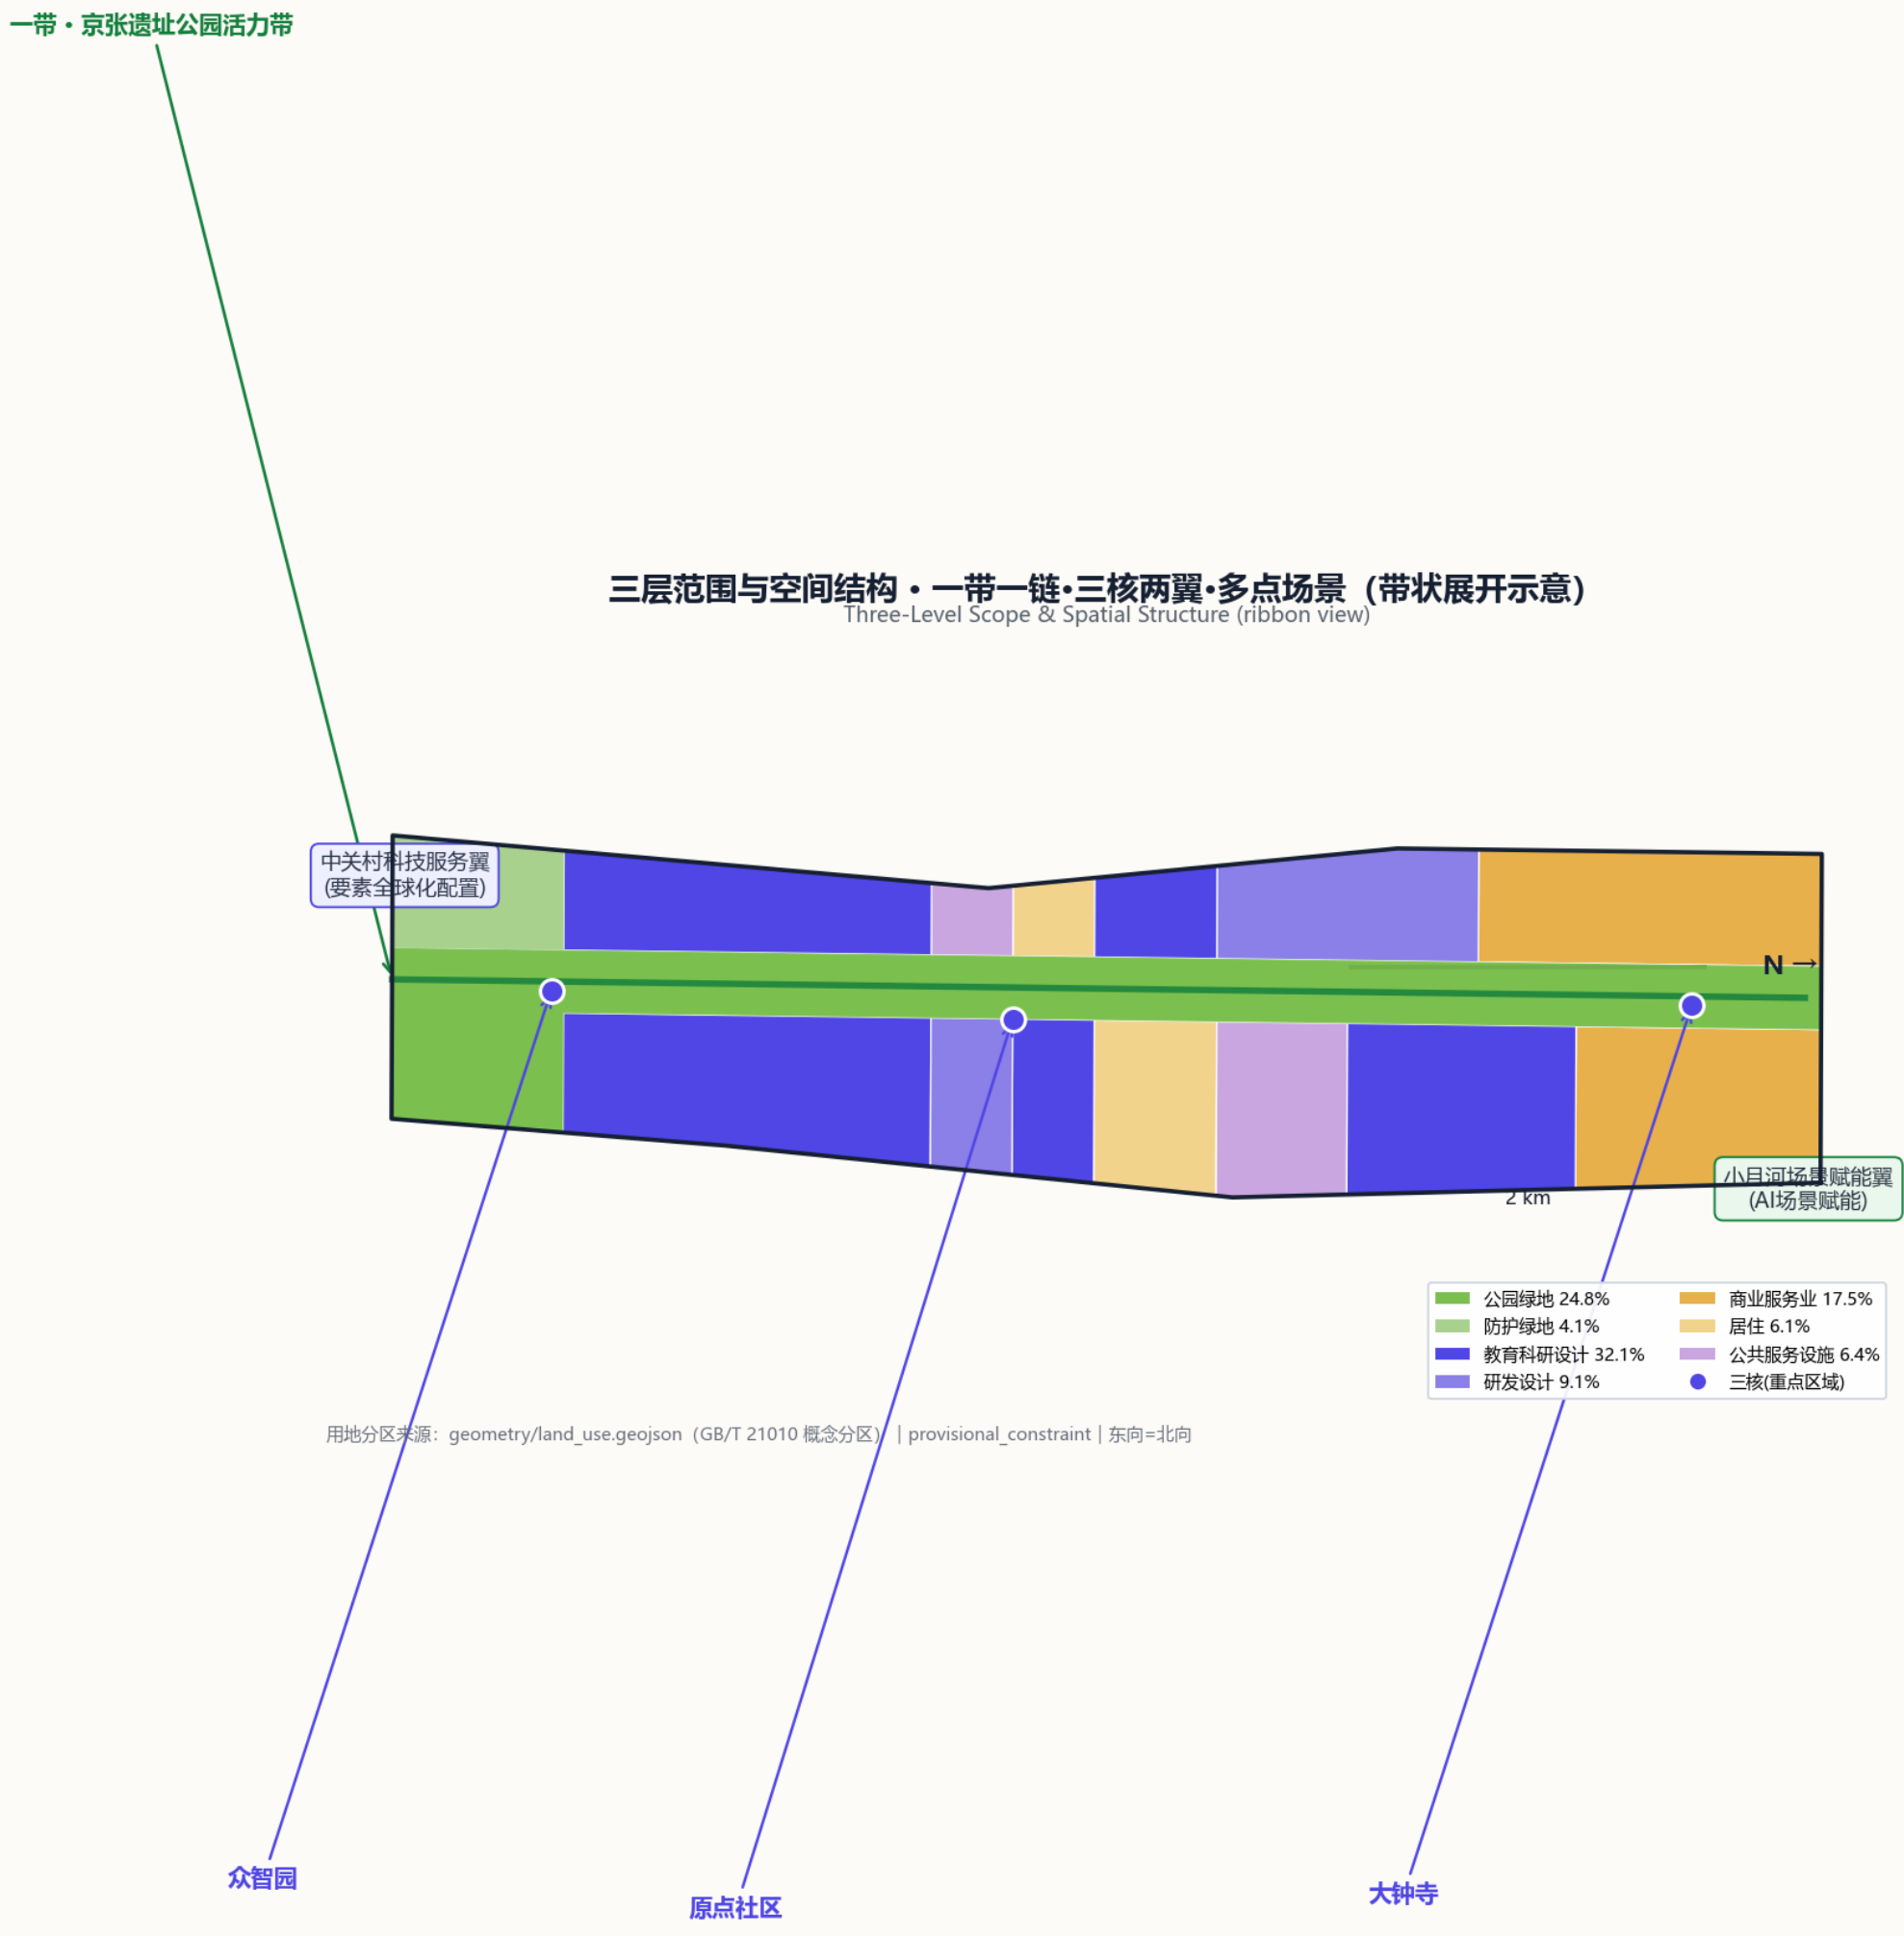

重点区域：众智园 / 原点社区 / 大钟寺详细设计

证据来源：geometry/*.geojson + metrics.json + proposal.md


三处重点区域·索引与设计任务 (KA-001 / KA-002 / KA-003)

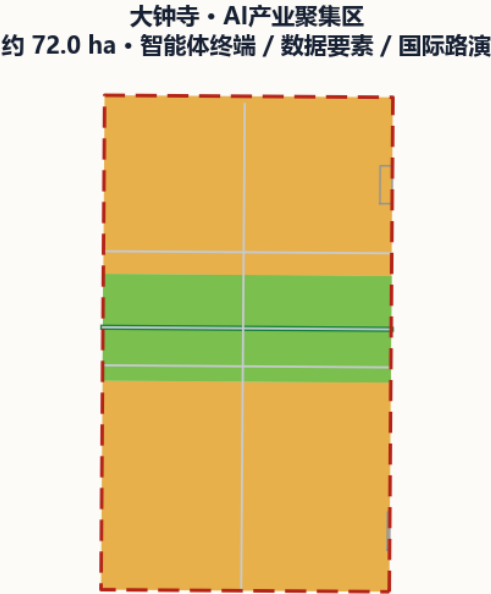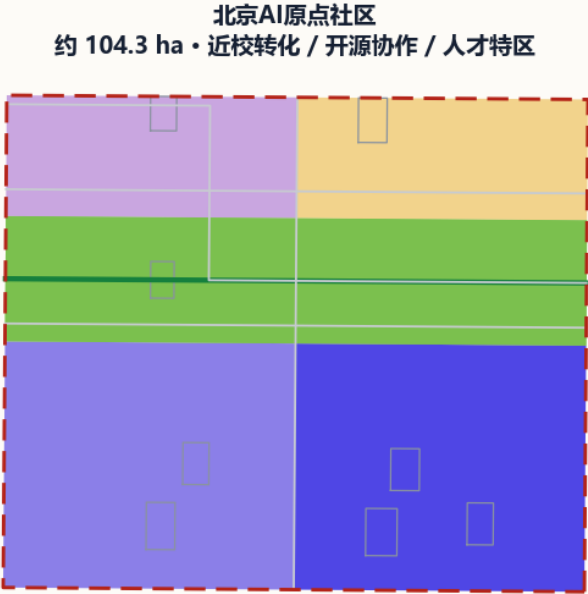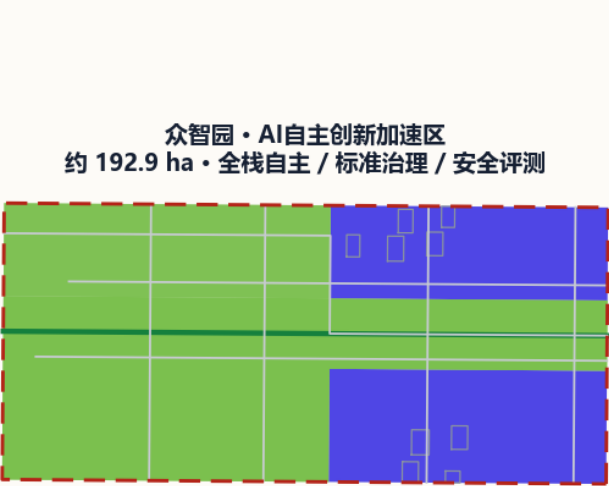

资料来源：geometry/key_areas.geojson + land_use/buildings/roads/green_space | provisional_constraint, 地块级结论待正式数据复核


交通慢行与蓝绿公共空间复合系统

证据来源：geometry/*.geojson + metrics.json + proposal.md

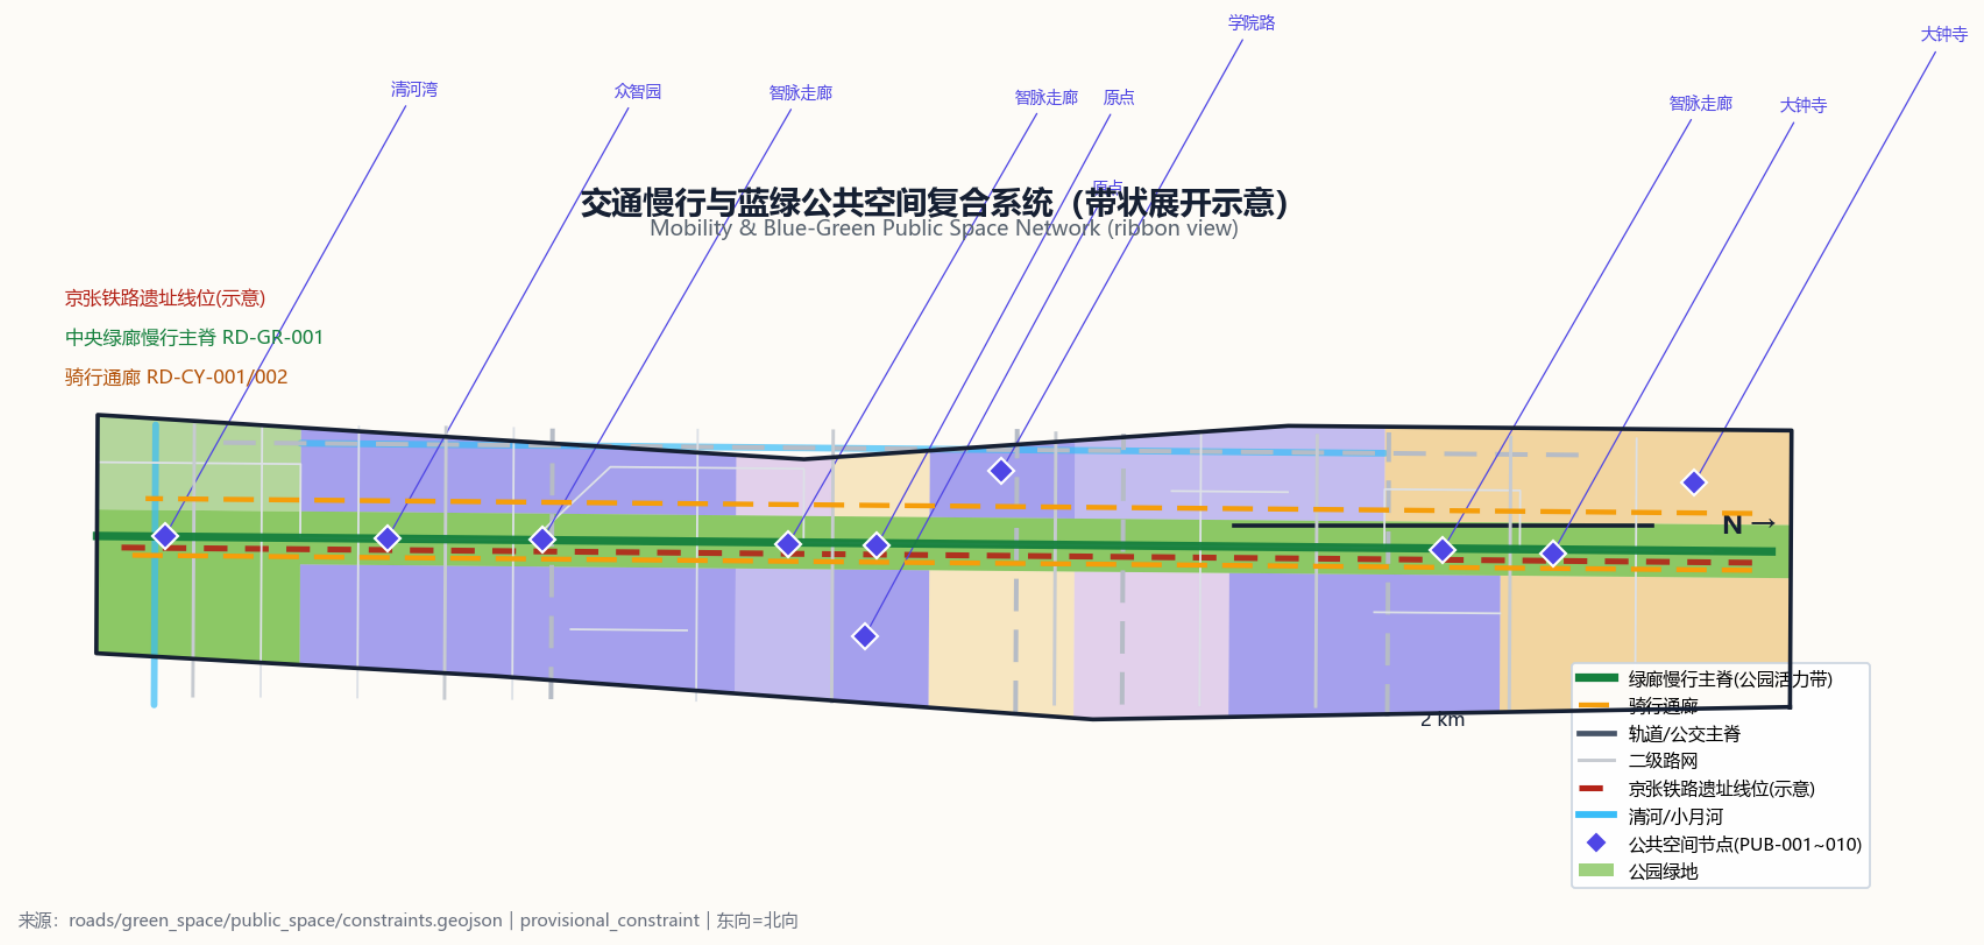

核心指标复算与证据链

证据来源：geometry/*.geojson + metrics.json + proposal.md

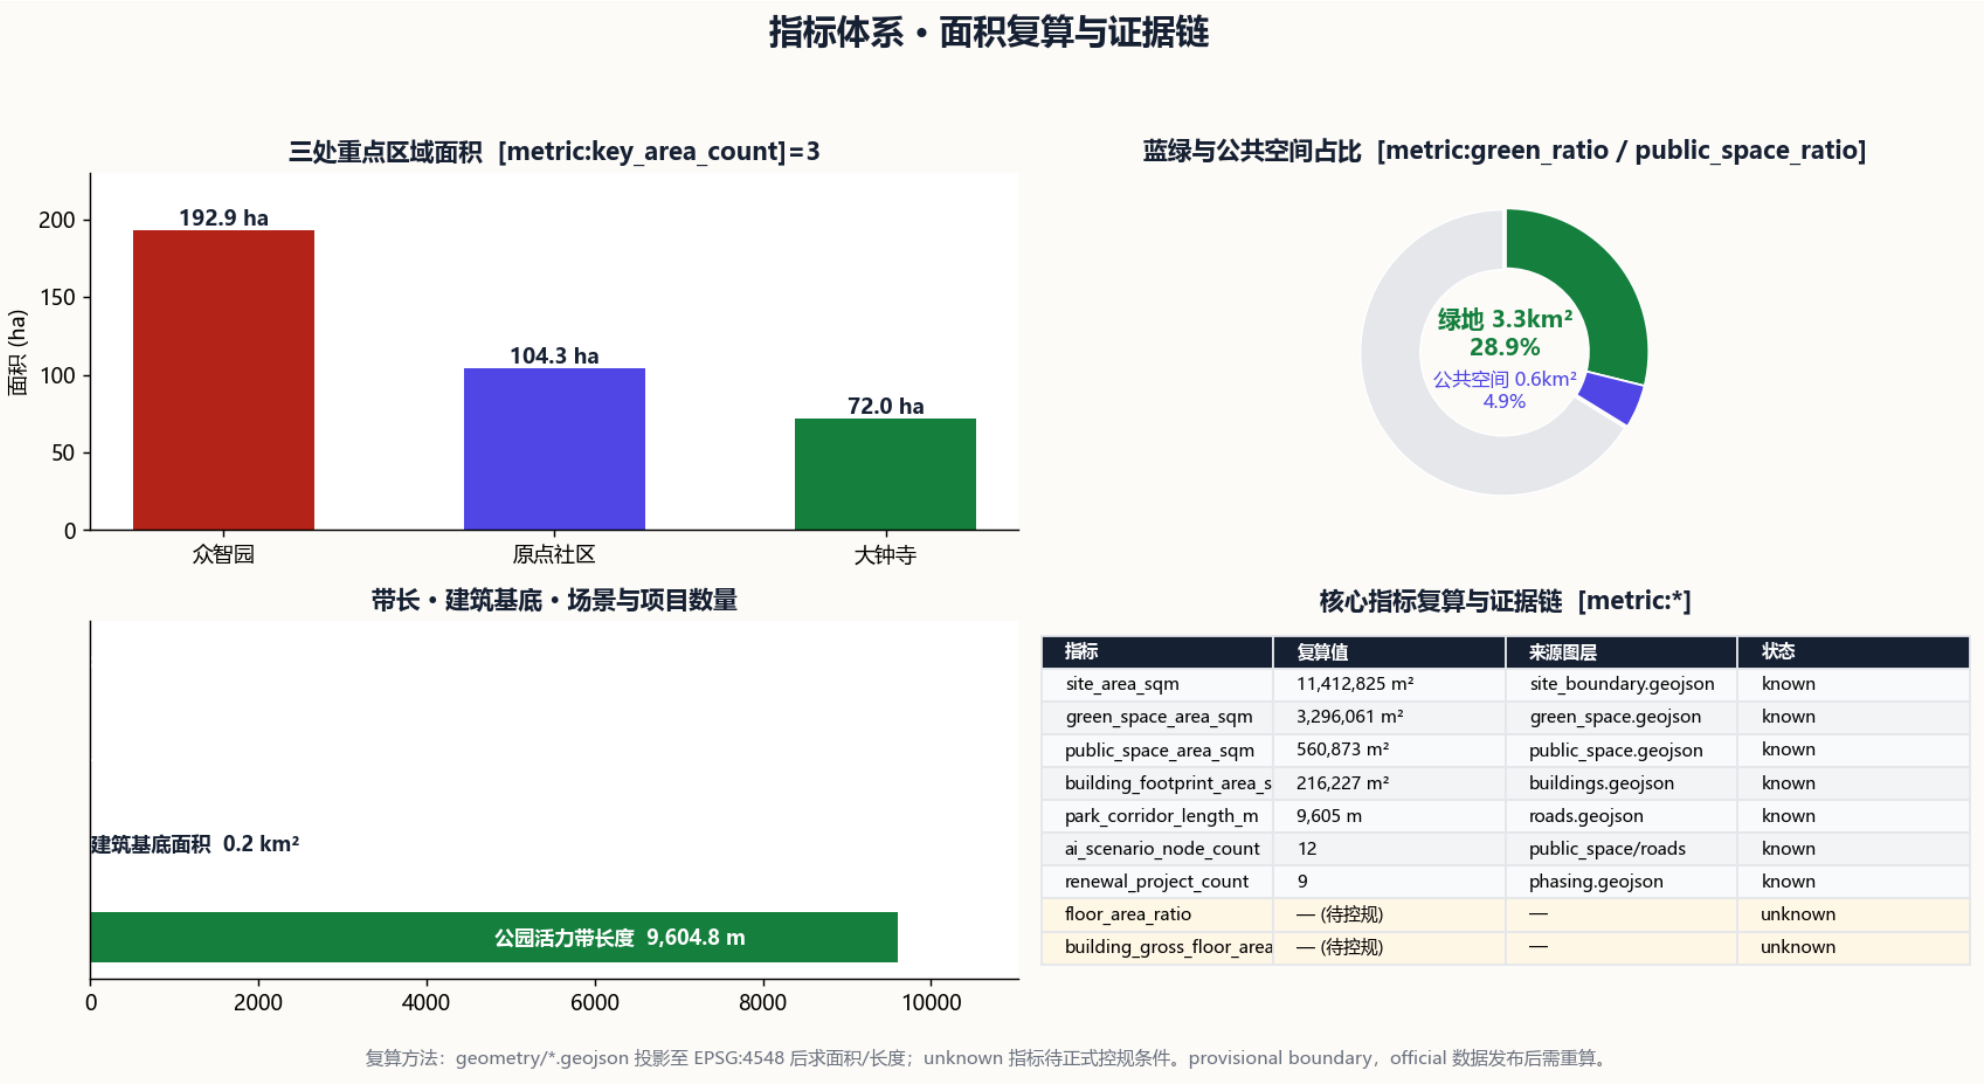

核心指标复算与合规说明

site_area_sqm	11412825.386	总体设计范围面积（m ² ）
green_ratio	0.288803	绿地率（绿廊+公园/总体范围）
public_space_ratio	0.049144	公共空间占比（十处节点）
green_space_area_sqm	3296061.431	绿地面积（m ² ）
public_space_area_sqm	560873.208	公共空间面积（m ² ）
building_footprint_area_sqm	216226.892	概念建筑基底面积（m ² ）
park_corridor_length_m	9604.8	京张遗址公园活力带主轴长度（m）
ai_scenario_node_count	12	AI 场景节点（含 4 张产业测试验证）
renewal_project_count	9	概念更新项目（分期挂接 phasing）
key_area_count	3	重点区域（众智园/原点/大钟寺）

合规与边界声明

- 本方案全部图层与指标基于 provisional 边界生成，标注 provisional_constraint、official_boundary=false、boundary_precision=provisional_rough。
- 坐标系：GeoJSON 为 EPSG:4326；面积复算投影至 EPSG:4548（CGCS2000 3 度带 CM117E）。
- 用地分区依据 GB/T 21010 概念分类；建筑为概念方向表达，非审定开发强度。
- 缺失项（容积率/建筑规模/高度）标注 unknown，待官方控规条件与 official 边界发布后复算。
- 本页为离线静态 PDF，无远程资源；素材来源见 sources.json 与 report/copyright_statement.md。