


JING-ZHANG LOCAL URBAN UNITS

A north-south civic datum plus wide, fine-grain and thick cross-corridor cities

OVERALL STRUCTURE / 01

ONE DATUM · NINE COMPLETE CITIES

The unit of design crosses Jing-Zhang and contains the real city on both sides.

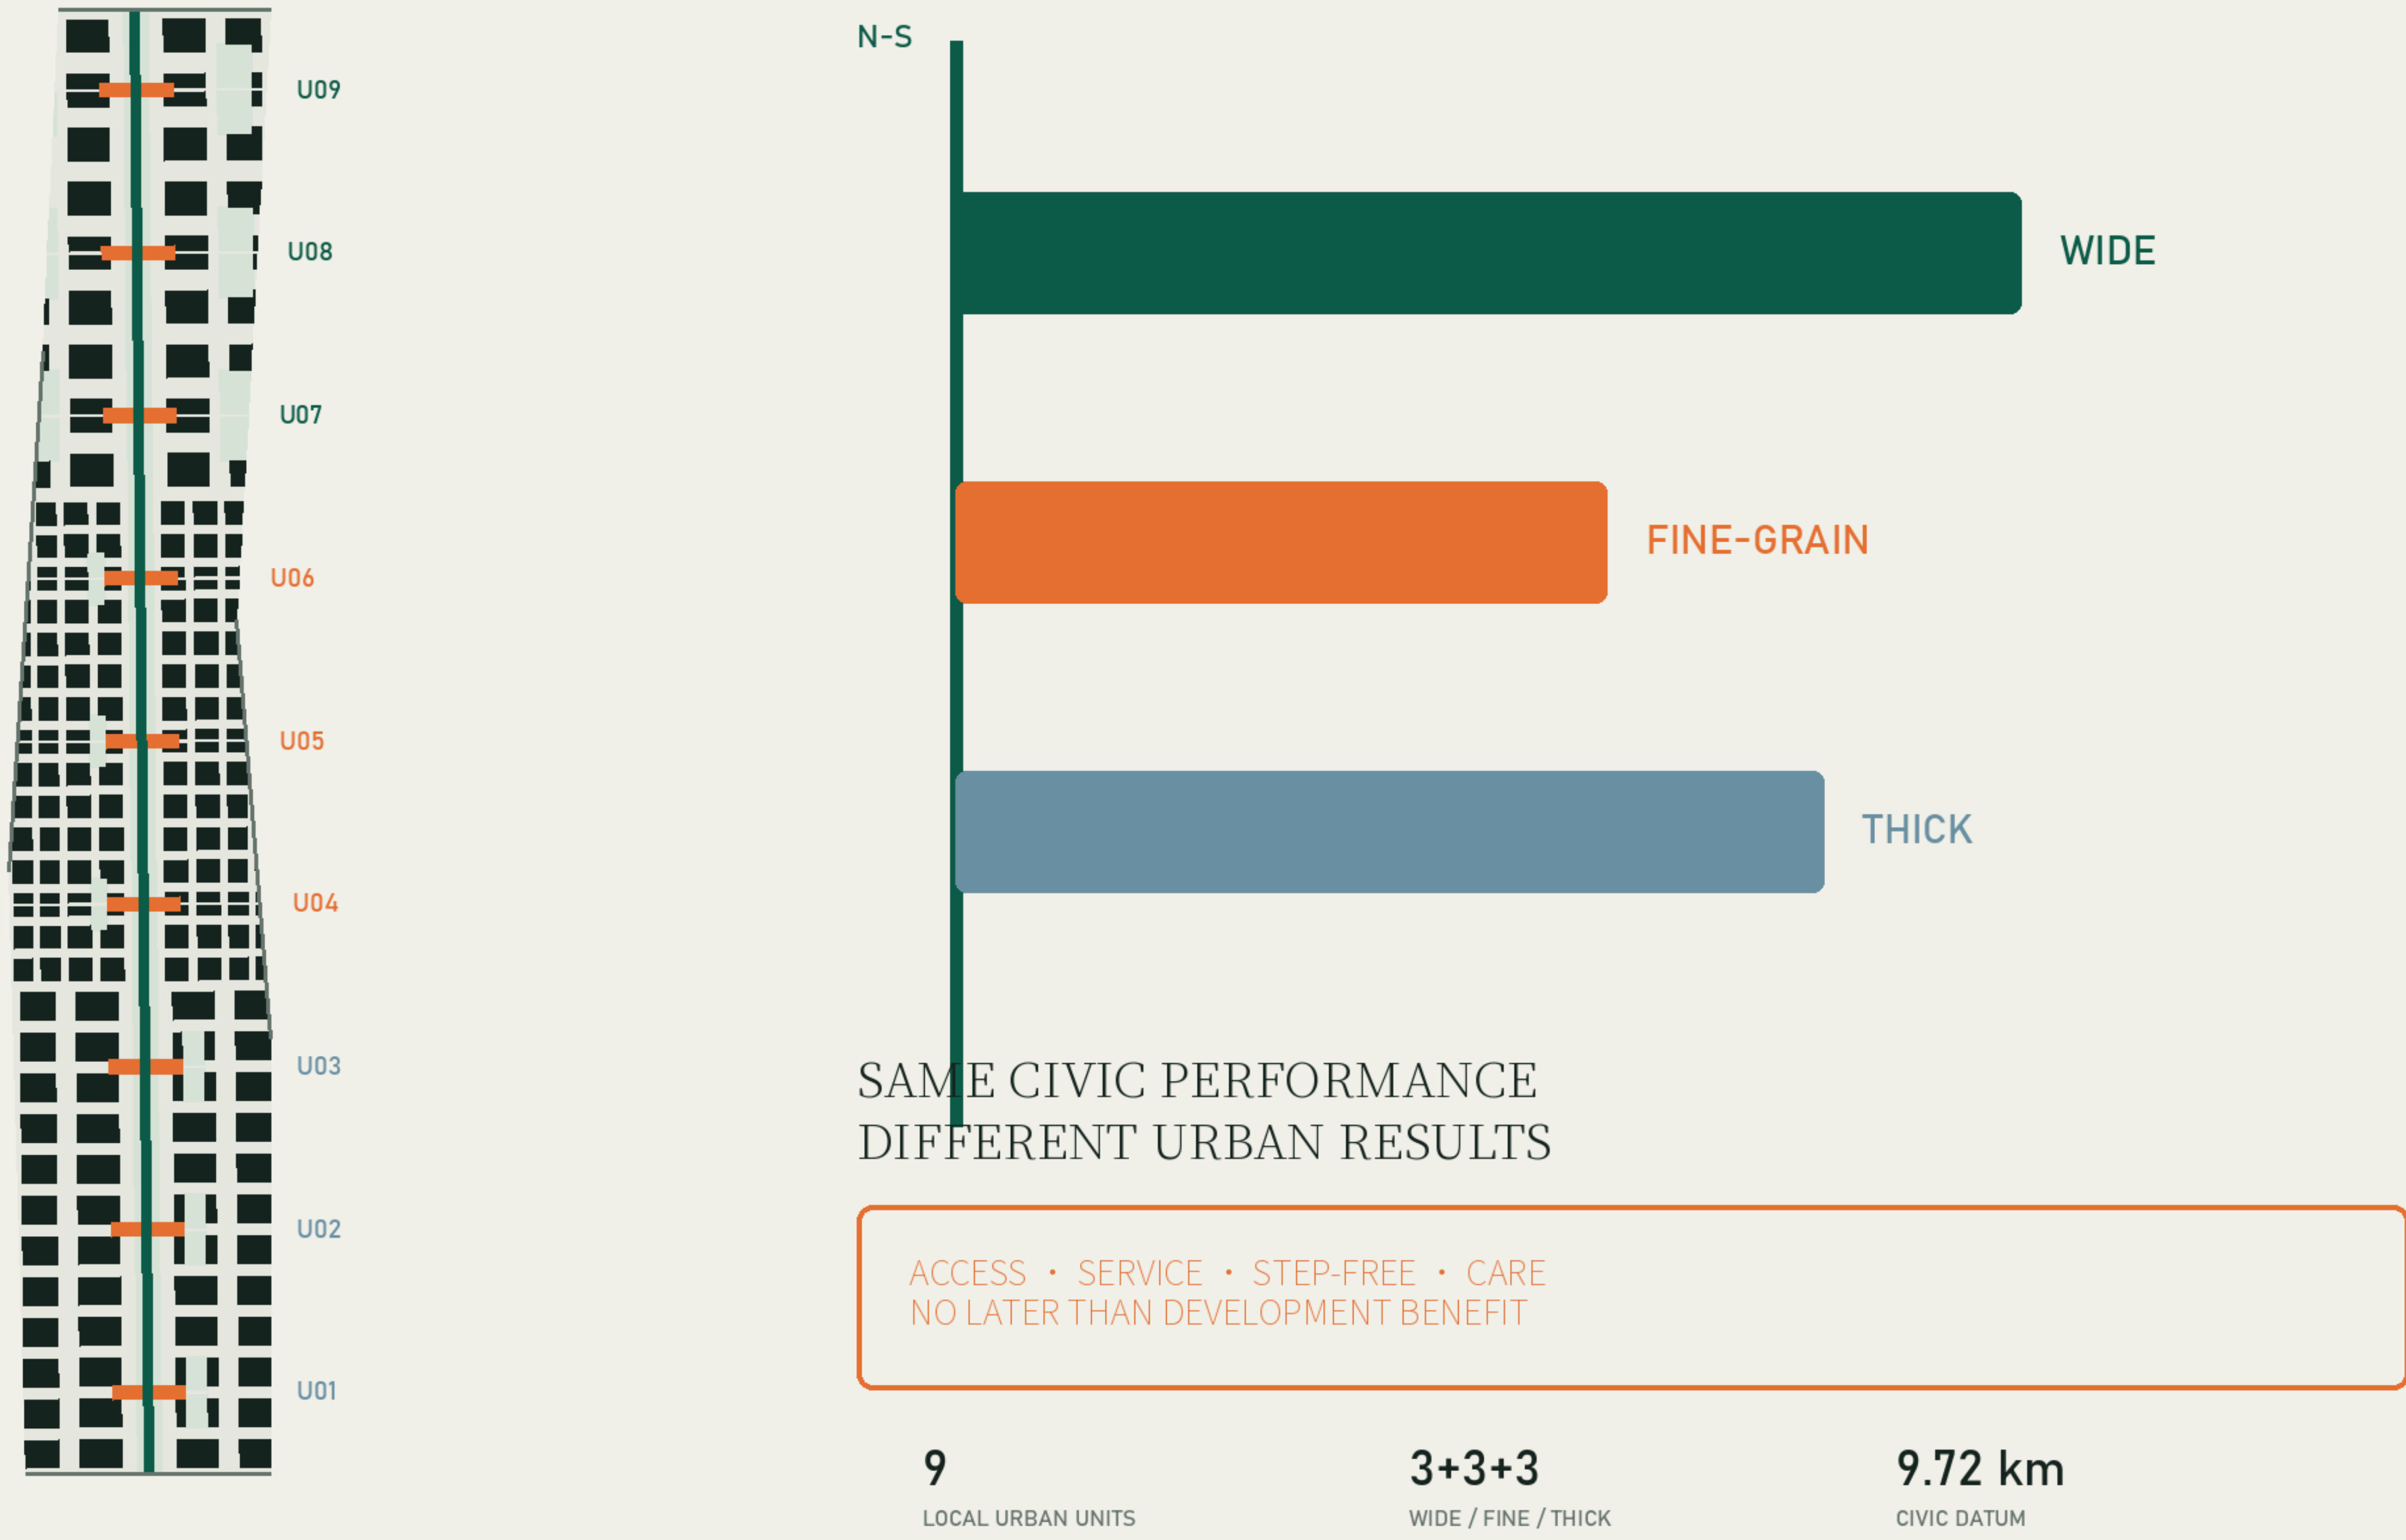


PROVISIONAL BOUNDARY · CONCEPT DESIGN · REBUILD ON OFFICIAL POLYGONS

01

CORE JUDGEMENT

The masterplan unit is not a node on the corridor.

It is a complete piece of local city crossing Jing-Zhang.

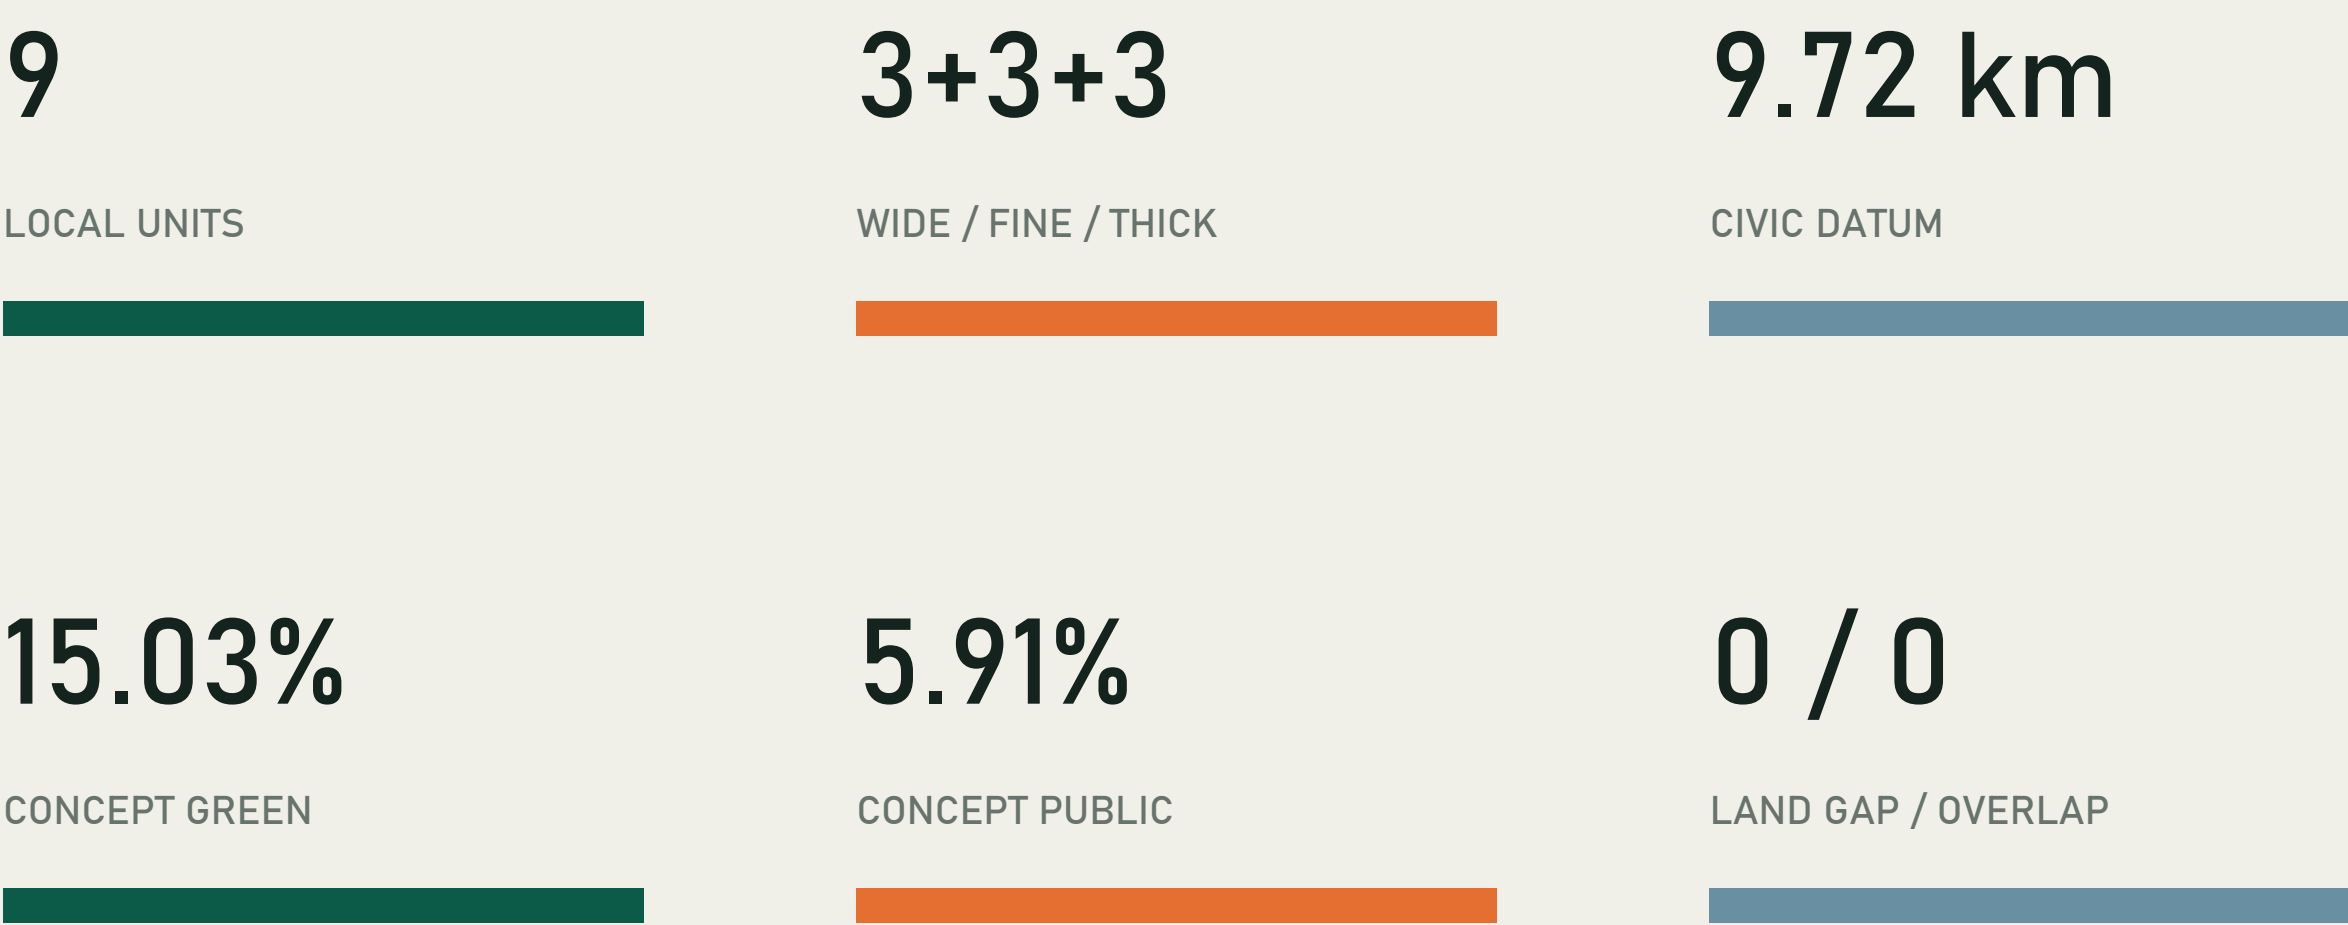

PUBLIC OUTCOMES NO LATER THAN THE MAIN DEVELOPMENT BENEFIT


NORTH WIDE / MIDDLE FINE / SOUTH THICK

The same civic datum and delivery gate use different land, ground-floor, mobility and implementation tools

THREE KEY AREAS / 03


NORTH WIDE · MIDDLE FINE · SOUTH THICK

One civic datum and one gate produce three different urban-design instruments.

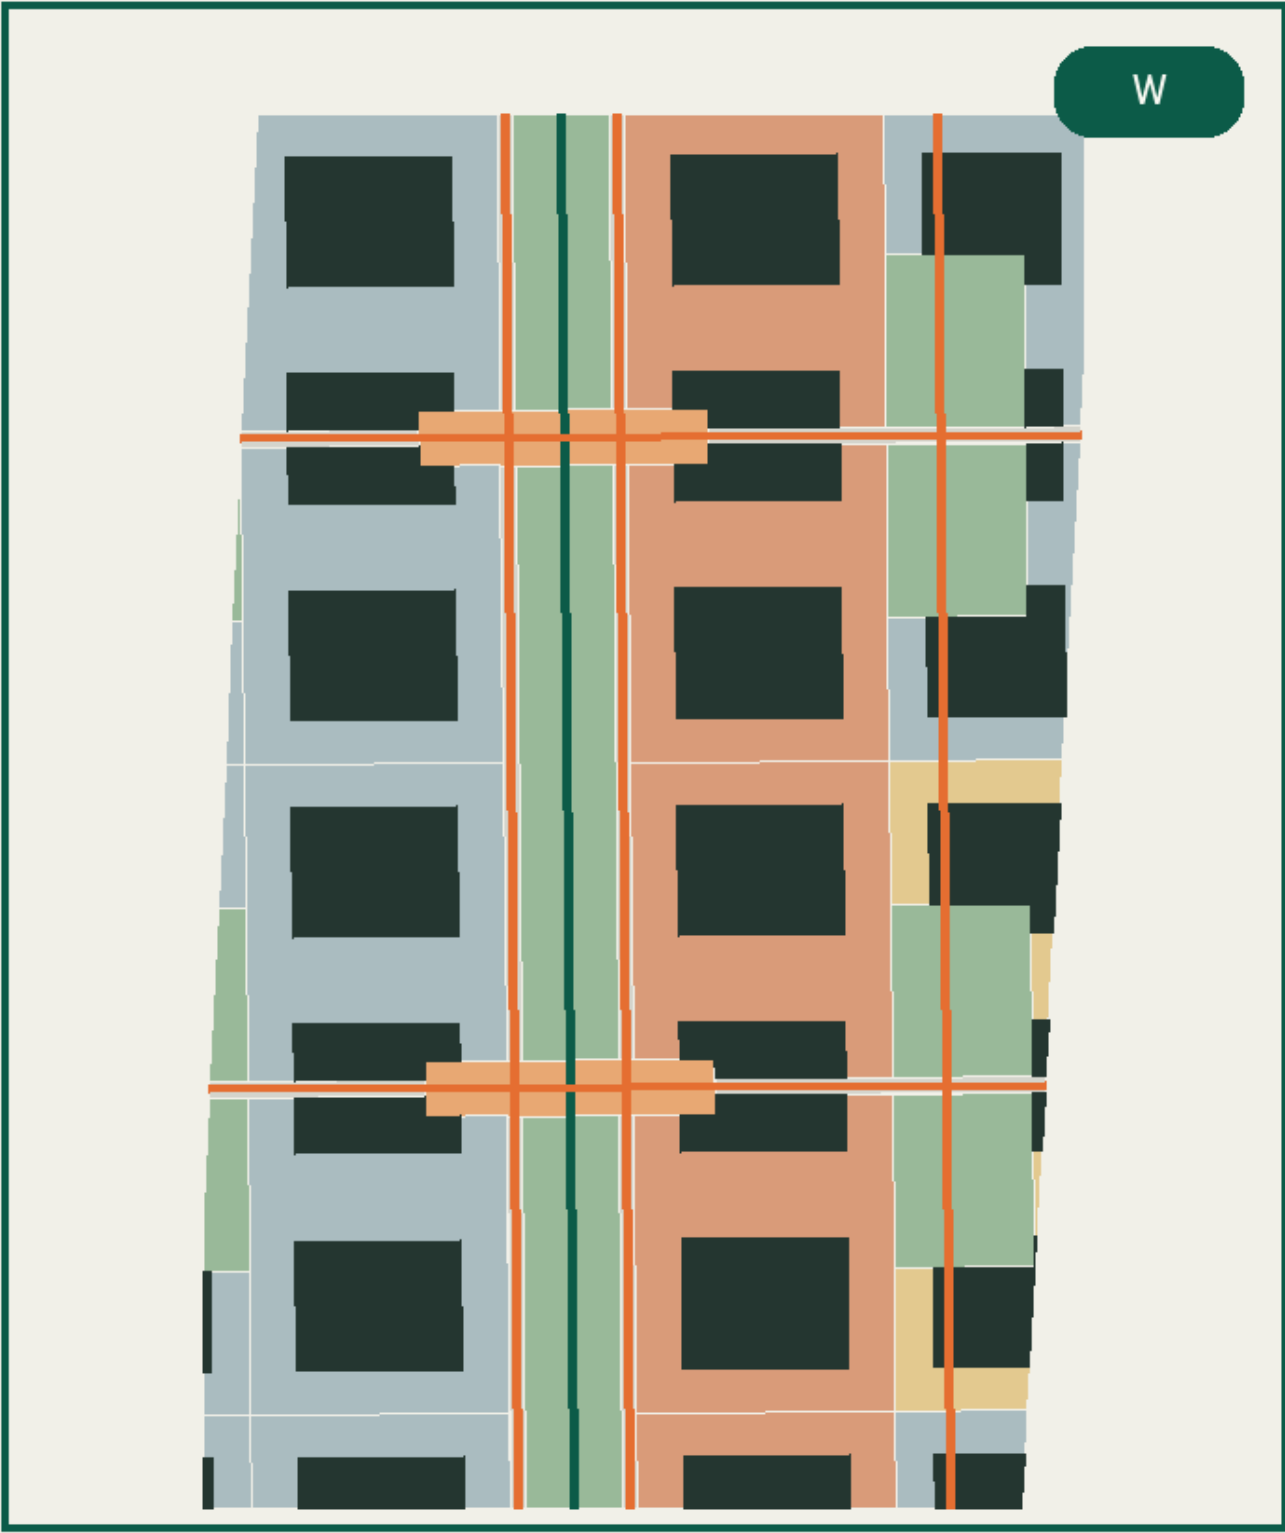


ZHONGZHIYUAN / WIDE

PUBLIC STREETS SUBDIVIDE LARGE PROJECTS
SECURE R&D CORE + CIVIC OUTER RING
LAND AND INFRASTRUCTURE CONDITIONS

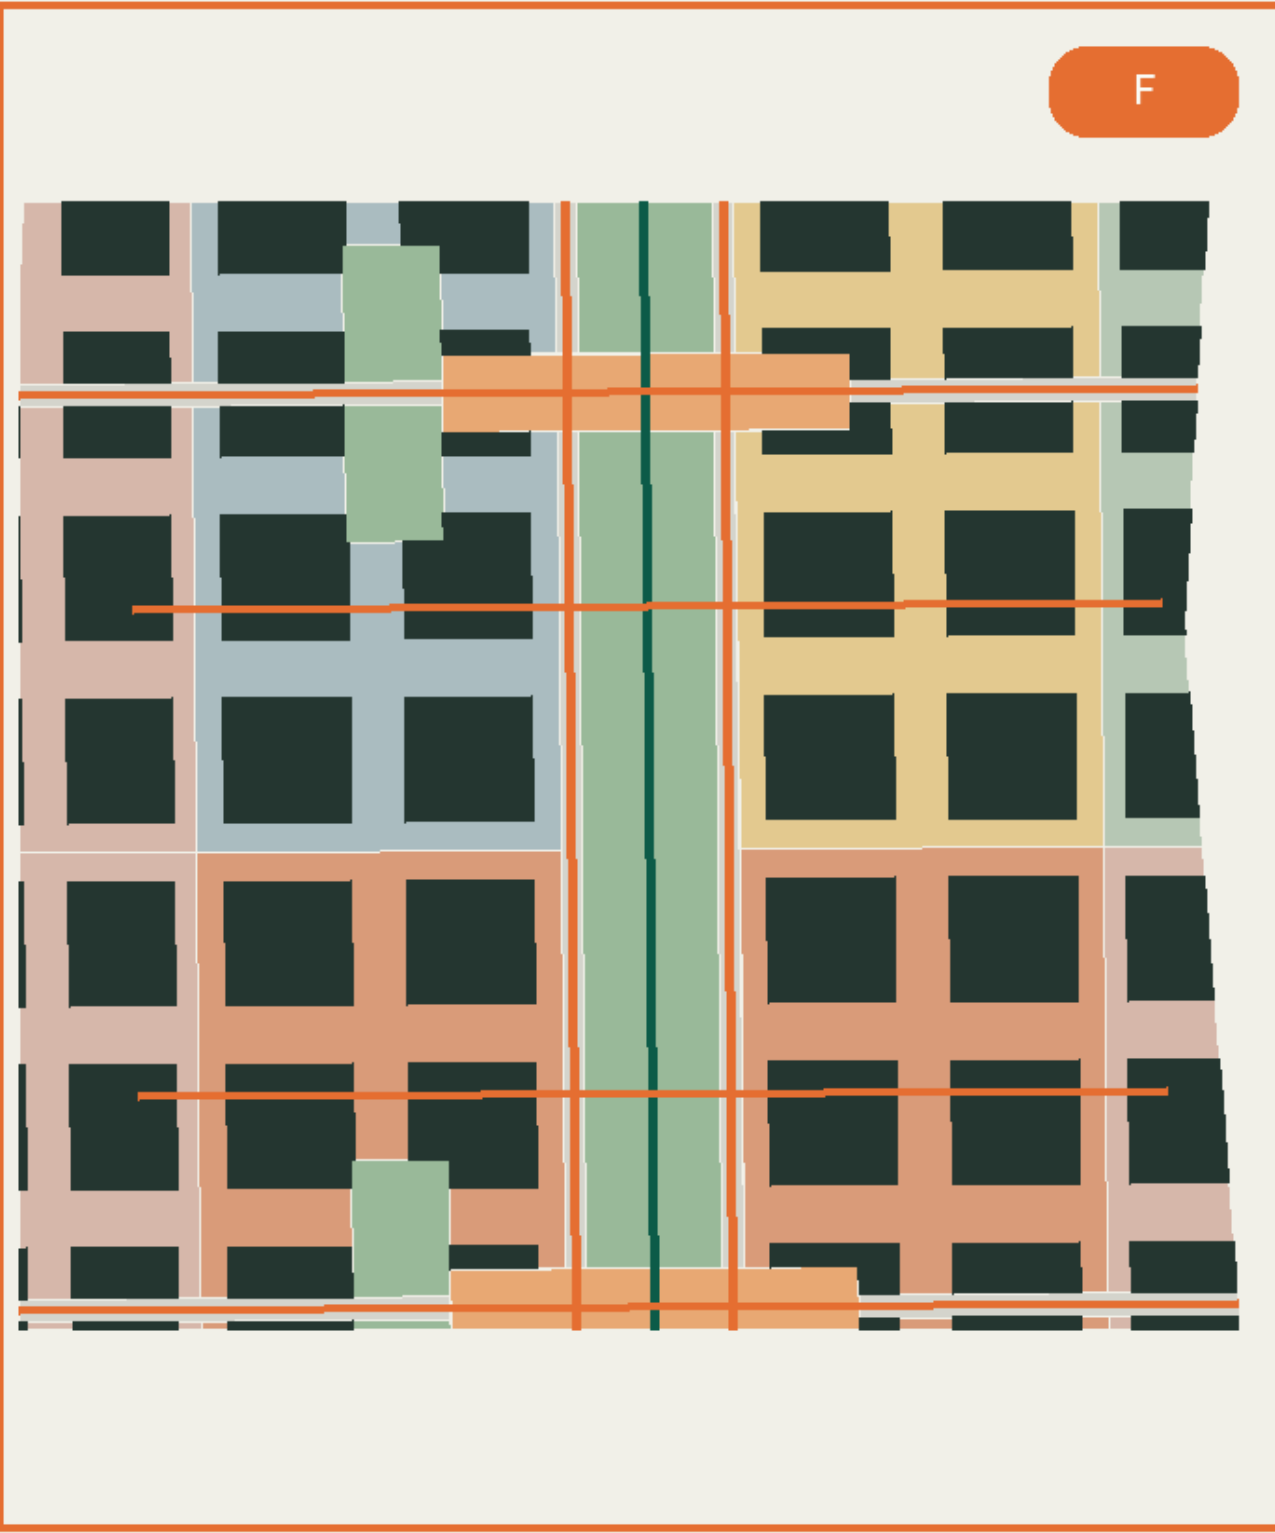

AI ORIGIN / FINE

RETAIN GRAIN
GROUND FLOOR + FORECOURT + ALLEY + COURT
PERMIT AND ACCESS AGREEMENTS

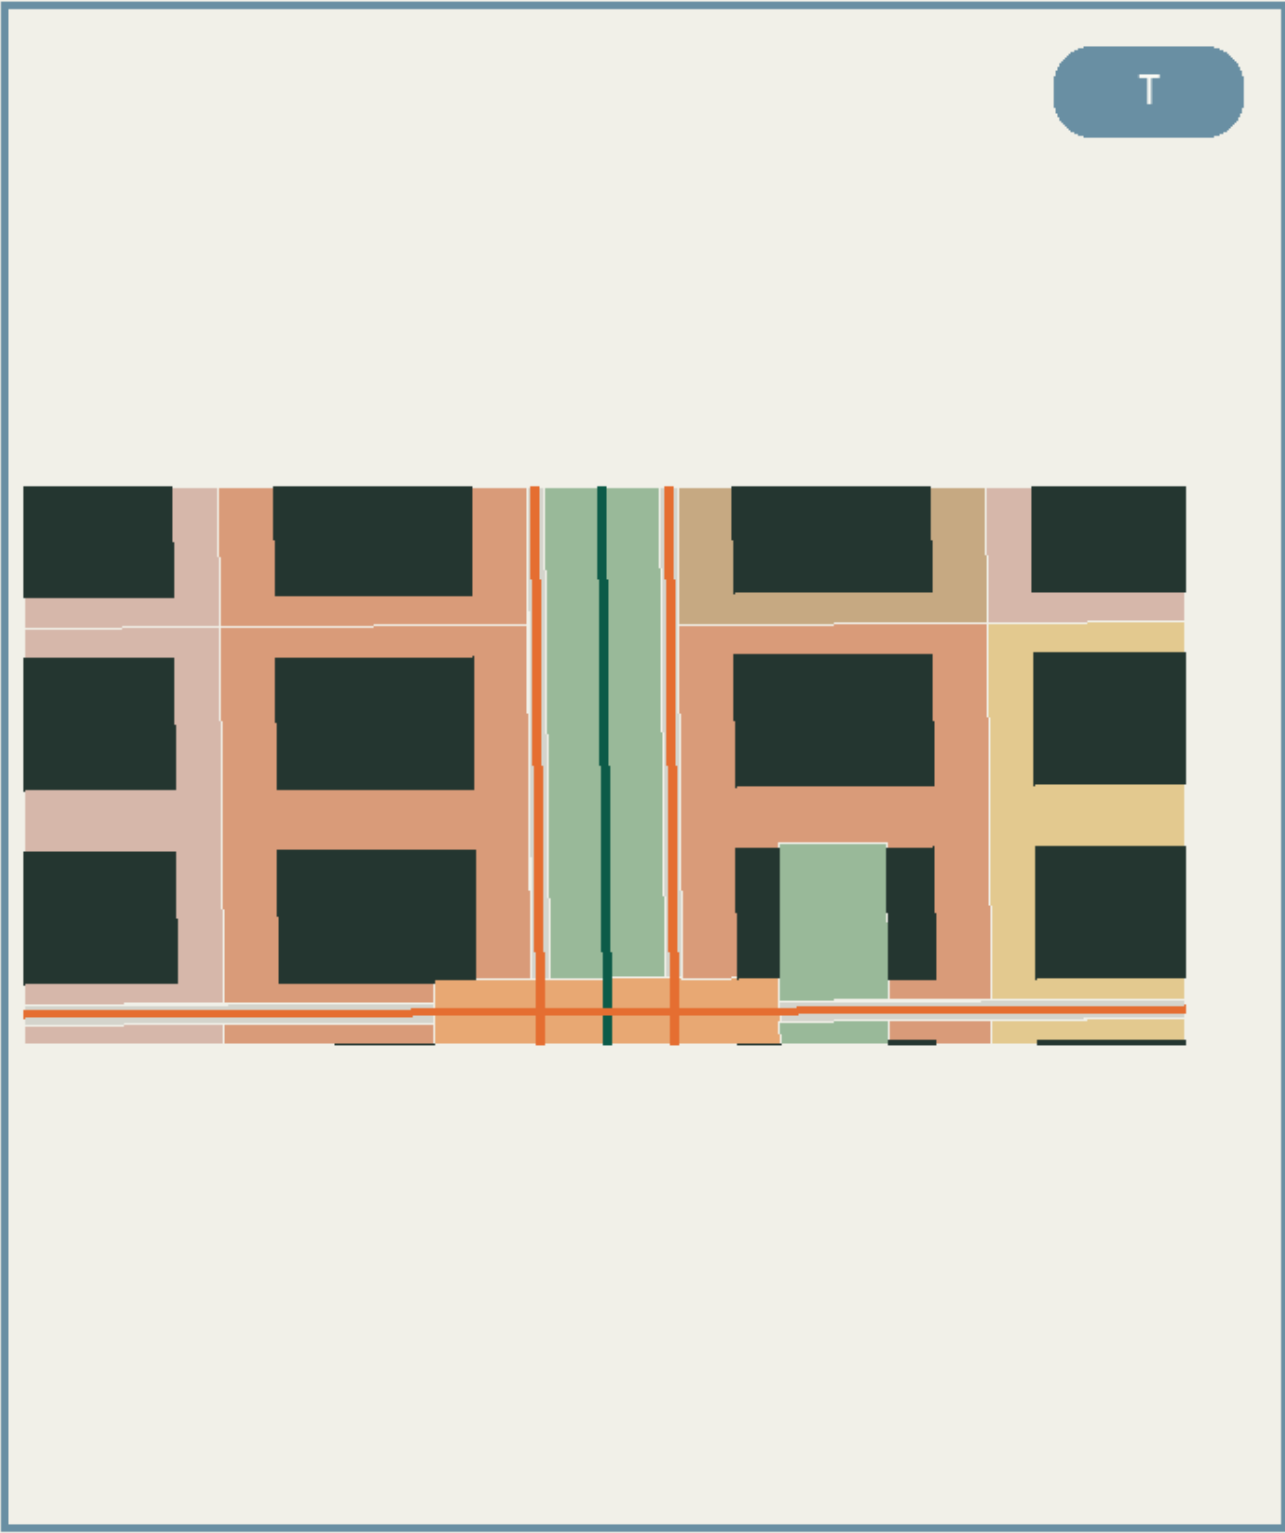

DAZHONGSI / THICK

GROUND-LEVEL FOUR QUADRANTS FIRST
STATION + COMMUNITY + CULTURE + PODIUM
JOINT-DEVELOPMENT GATE

KEY-AREA POLYGONS REMAIN PROVISIONAL; CONCEPT DETAILED DESIGN, NOT ENGINEERING OR OWNERSHIP

03

ZHONGZHIYUAN / WIDE

- 01 Public streets subdivide large projects
- 02 Civic outer ring plus secure core
- 03 Freight on outer edges
- 04 Land and infrastructure conditions

GATE-U08 / two routes and an R&D commons first

AI ORIGIN / FINE

- 01 Retain fine grain
- 02 Ground floor plus court plus alley
- 03 Never assume campus access
- 04 Permits and access agreements

GATE-U06 / routes and essential ground-floor services first

DAZHONGSI / THICK

- 01 Four-quadrant ground first
- 02 Station plus community plus cultural podium
- 03 Massing steps down to heritage
- 04 Station-city joint-development gate

GATE-U01 / step-free ground and community service first

COMPLETE SPACE / CLOSED RESPONSIBILITY LOOP

Six spatial systems, twelve scenarios, nine public delivery gates and honest unknowns

MOBILITY + BLUE-GREEN / 04

CONTINUOUS NORTH-SOUTH · COMPLETE EAST-WEST

One datum, nine complete streets and three locally different mobility/landscape sections.

PUBLIC SPACE / PUBLIC SPACE OUTSIDE

GROUND-FLOOR MESH / NO ASSUMED CAMPUS PASSAGE

FOUR QUADRANTS / HIGH FLOOR / STEPPED MASS

公共基座 / DATUM

横向城市街 / CROSS-CITY STREET

局部链接 / LOCAL CONNECTION

CONCEPT ALIGNMENTS AND WIDTHS REQUIRE ROAD, RAIL, UTILITY AND OWNERSHIP REVIEW

04

METRICS + DELIVERY / 05

RECALCULABLE SPACE · ENFORCEABLE GATES

Known means computable from current design geometry; statutory and existing data gaps remain unknown.

9

LOCAL UNITS

3+3+3

WIDE / FINE / THICK

9.72 km

CIVIC DATUM

15.03%

CONCEPT GREEN

5.91%

CONCEPT PUBLIC

12 / 7

AI / TEST SCENARIOS

0 / 0

LAND GAP / OVERLAP

9

PUBLIC GATES

UNKNOWN / DATA GAPS

FAR · FLOOR AREA · HEIGHT · ROAD REDLINES · RETAIN/RENOVATE/DEMOLISH

VERIFY

SECURE

DELIVER


ACCEPT

BENEFIT

PUBLIC OUTCOMES NO LATER THAN MAIN DEVELOPMENT BENEFIT

AREAS RECALCULATED IN EPSG:4548; REBUILD THE CHAIN WHEN OFFICIAL DATA ARRIVE

05

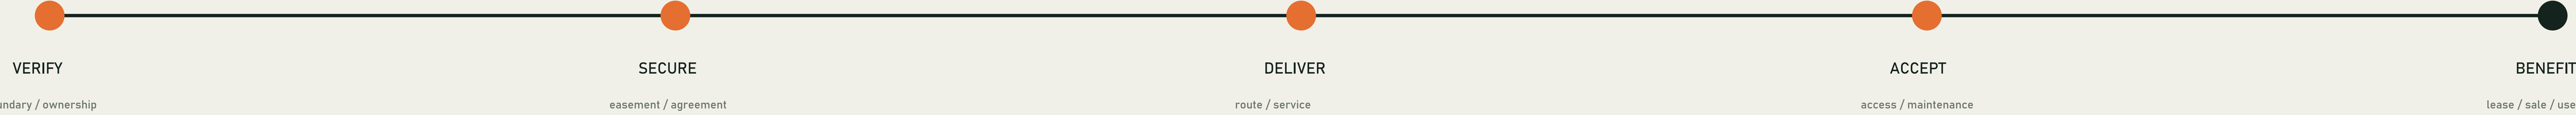

A USABLE, REACHABLE AND MAINTAINED CITY COMES BEFORE THE MAIN DEVELOPMENT BENEFIT

UNKNOWN / DATA GAPS

FAR / floor area / numeric height

road redlines / real building actions

rebuild the evidence chain when official data arrive