

NORTH OF ZERO

零公里以北

Open-source urban design proposal · Centennial Jing-Zhang AI Innovation Belt · A3 booklet

One spine, three hubs · two wings, six loops · AI begins from the human origin

OPEN CO-CREATION EXPRESS


Beijing North (K0) → the Future (K9)

Passengers: sofizhang × Claude Agent · Gate: GitHub PR · 2026-08-10 · v1.3

FORMAL

bilingual
recomputable

Presentation booklet; structured data is authoritative. All spatial content is conceptual, for professional deepening; provisional rough boundaries only; no government approval or commitment implied.

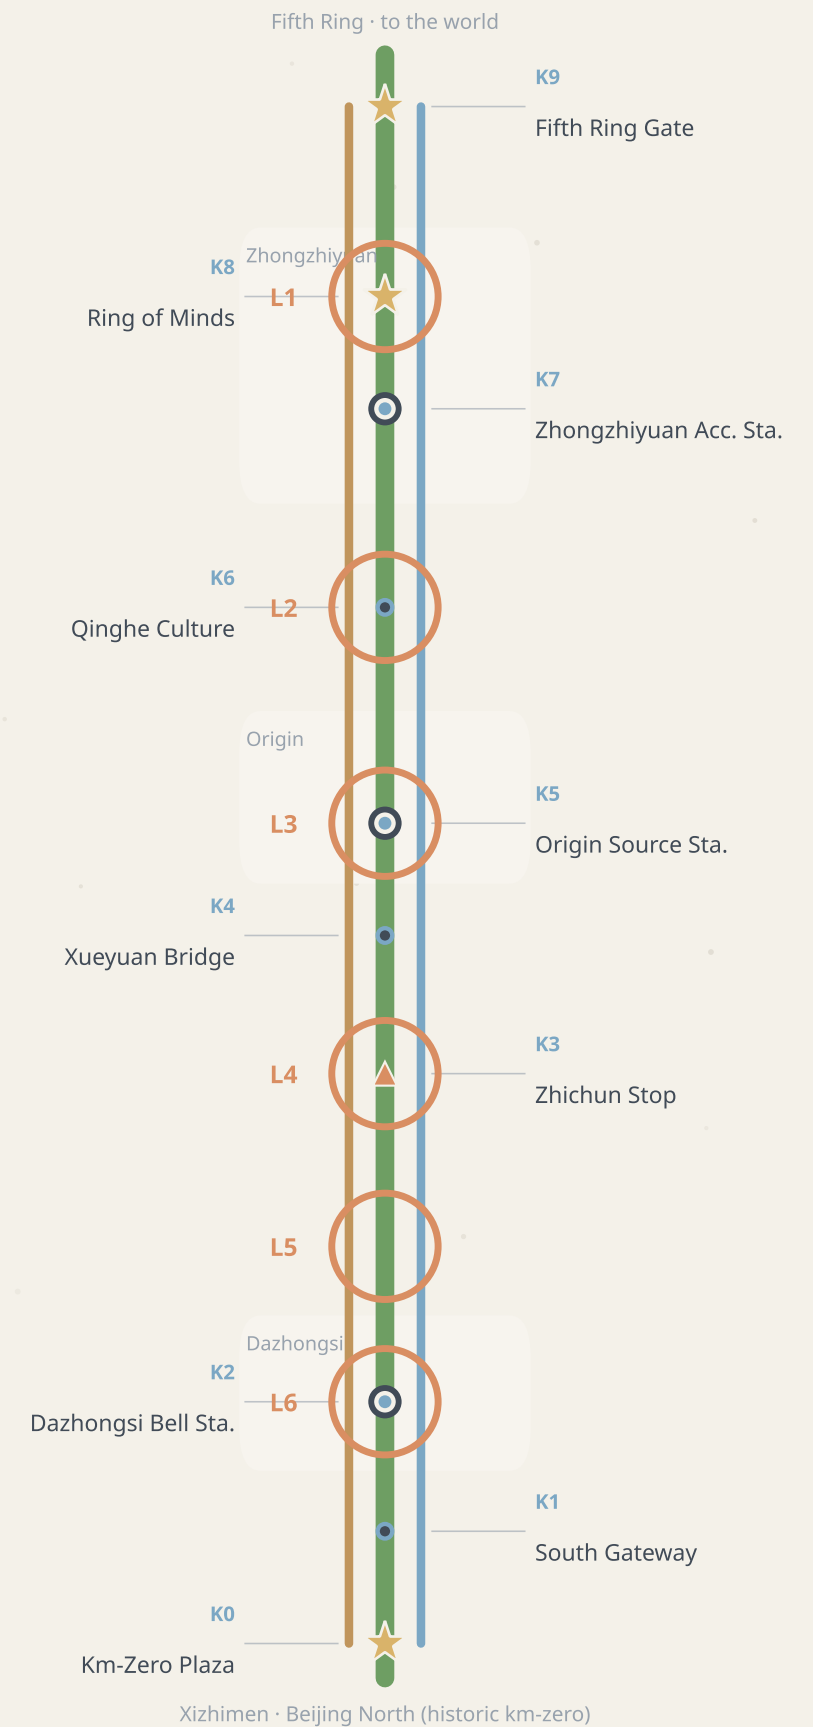

One-page read: three moves for one corridor

01

RE-STITCH

Six east-west suture loops re-stitch the two halves of a city divided for decades into one everyday walking system.

02


LIGHT UP

North of kilometre zero, the 9.7 km spine becomes a double-track artery: heritage on one track, AI scenarios on the other, ten stations K0-K9.

03

CO-CREATE

Three hubs, a scenario-access list and a contributors honor system run the city as a living open-source project.

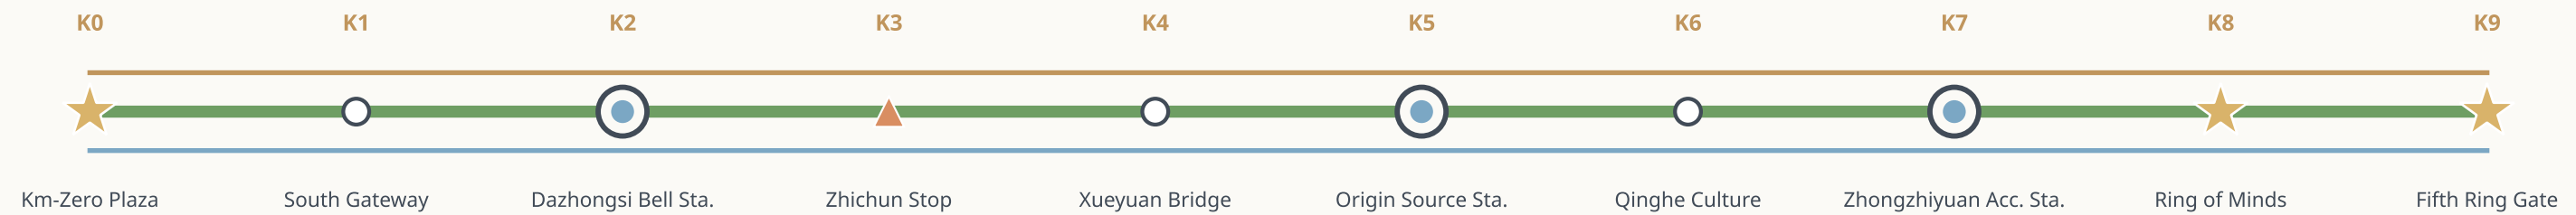

11.41 km²

Overall Design Area (Δ0.11%)

27.6%

green ratio

28.1%

composite public space

25.8 km

slow network

12+6+4

cards + personas + landmarks

23/23

tasks covered

The NORTH OF ZERO diagram: the proposal as a transit map

Line information

Zero-North green spine (heritage park)

Heritage track (railway narrative)

Intelligence track (AI scenarios & compute)


Suture loops L1-L6

Three hub stations

AI pilgrimage landmarks

Testing & validation

Two wings (indicative)

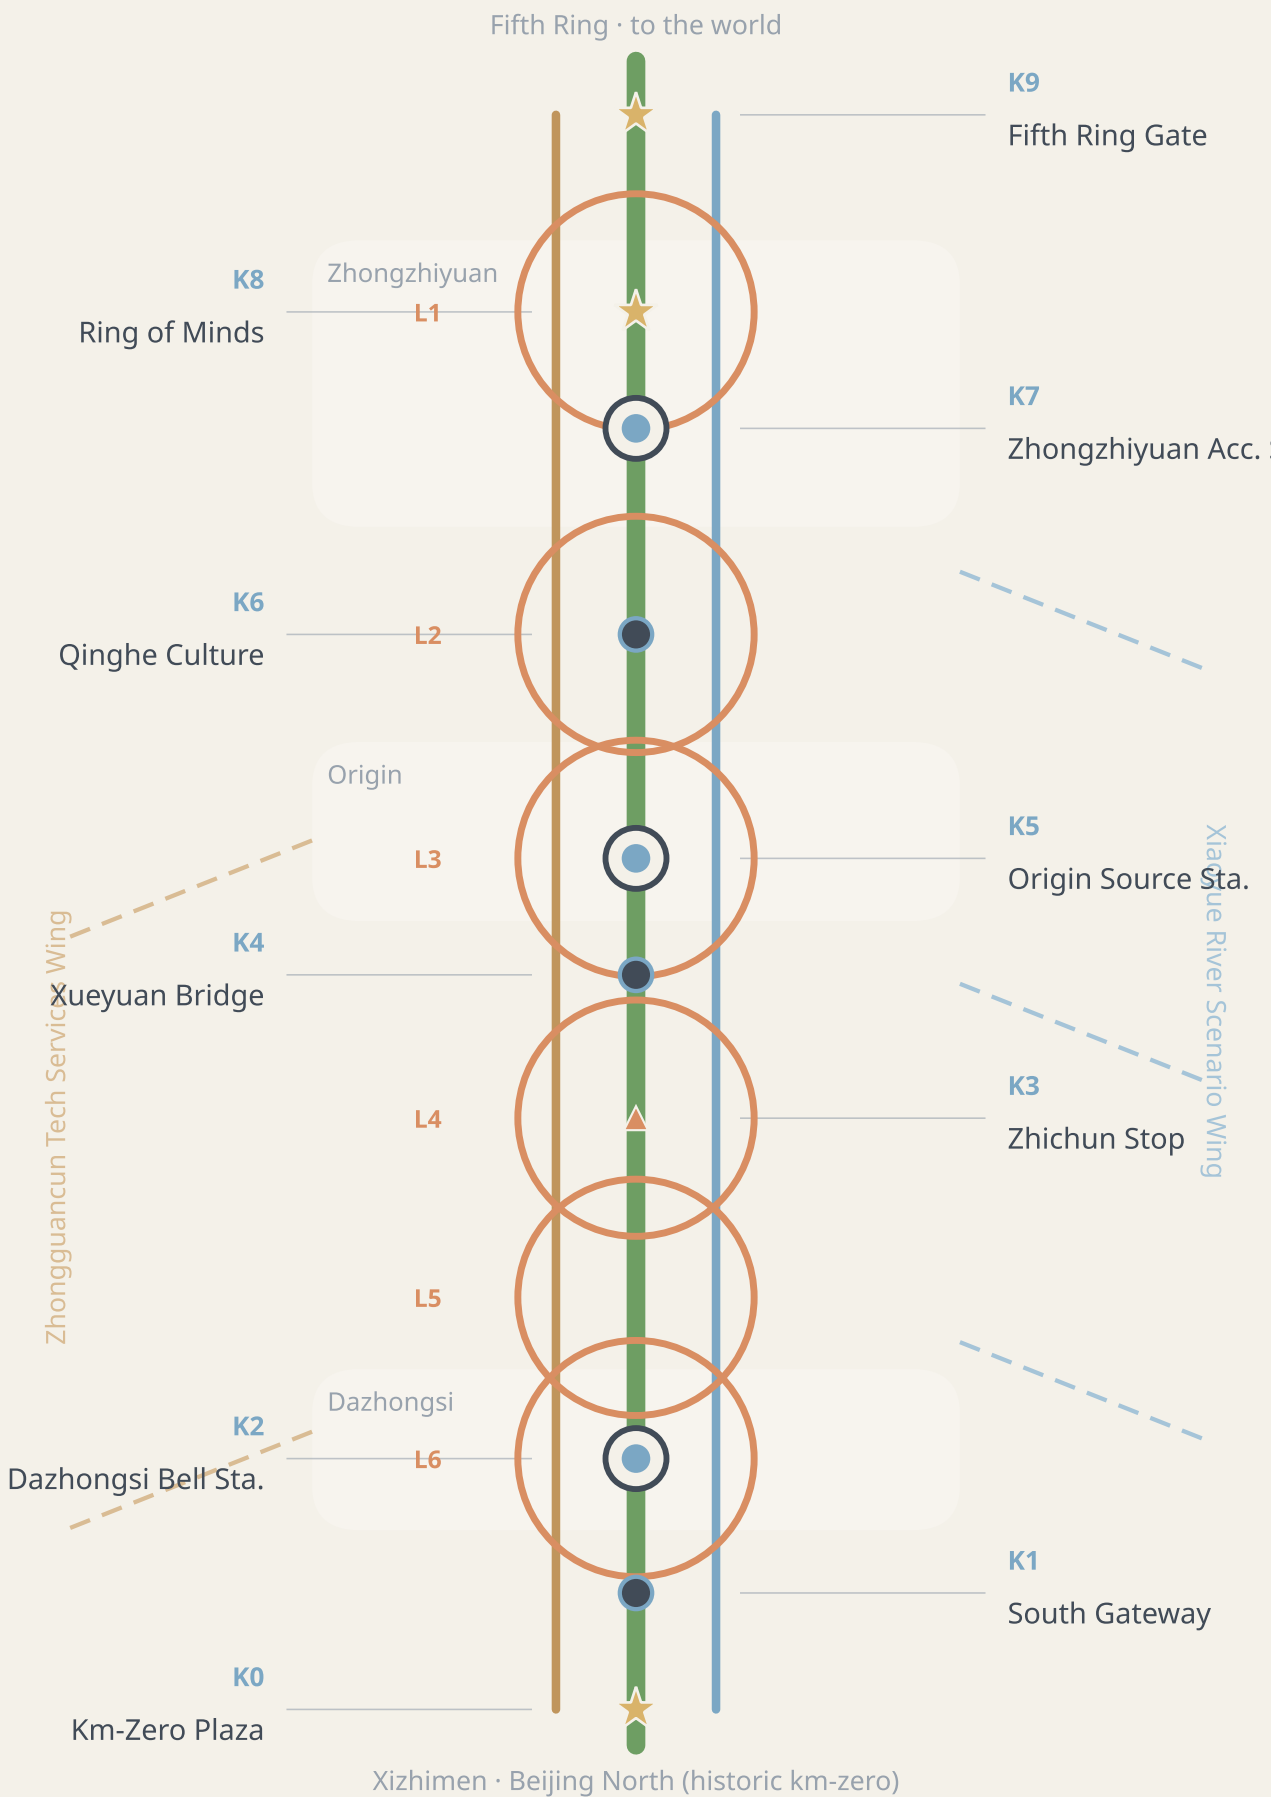

Six loop packages

- L1

Zhongzhiyuan: forum + grid
- L2

Qinghe: gallery + water
- L3

Herringbone: campus suture
- L4

Zhichun: delivery + health
- L5

Jimen: renewal + elderly
- L6

Dazhongsi: quadrants + AV

Ten stations are ten renewal catalysts — see the P11 schedule.


How to read

Every station is a buildable concept node; every loop a suture project package; the two tracks are belt-wide narrative & scenario systems. Topological diagram, not to scale.

Structure & land use: a recomputable spatial chassis

Fig.1 Concept & evidence overview: one meridian, three hubs, two wings, six loops


NORTH OF ZERO · Conceptual recommendation, for professional deepening

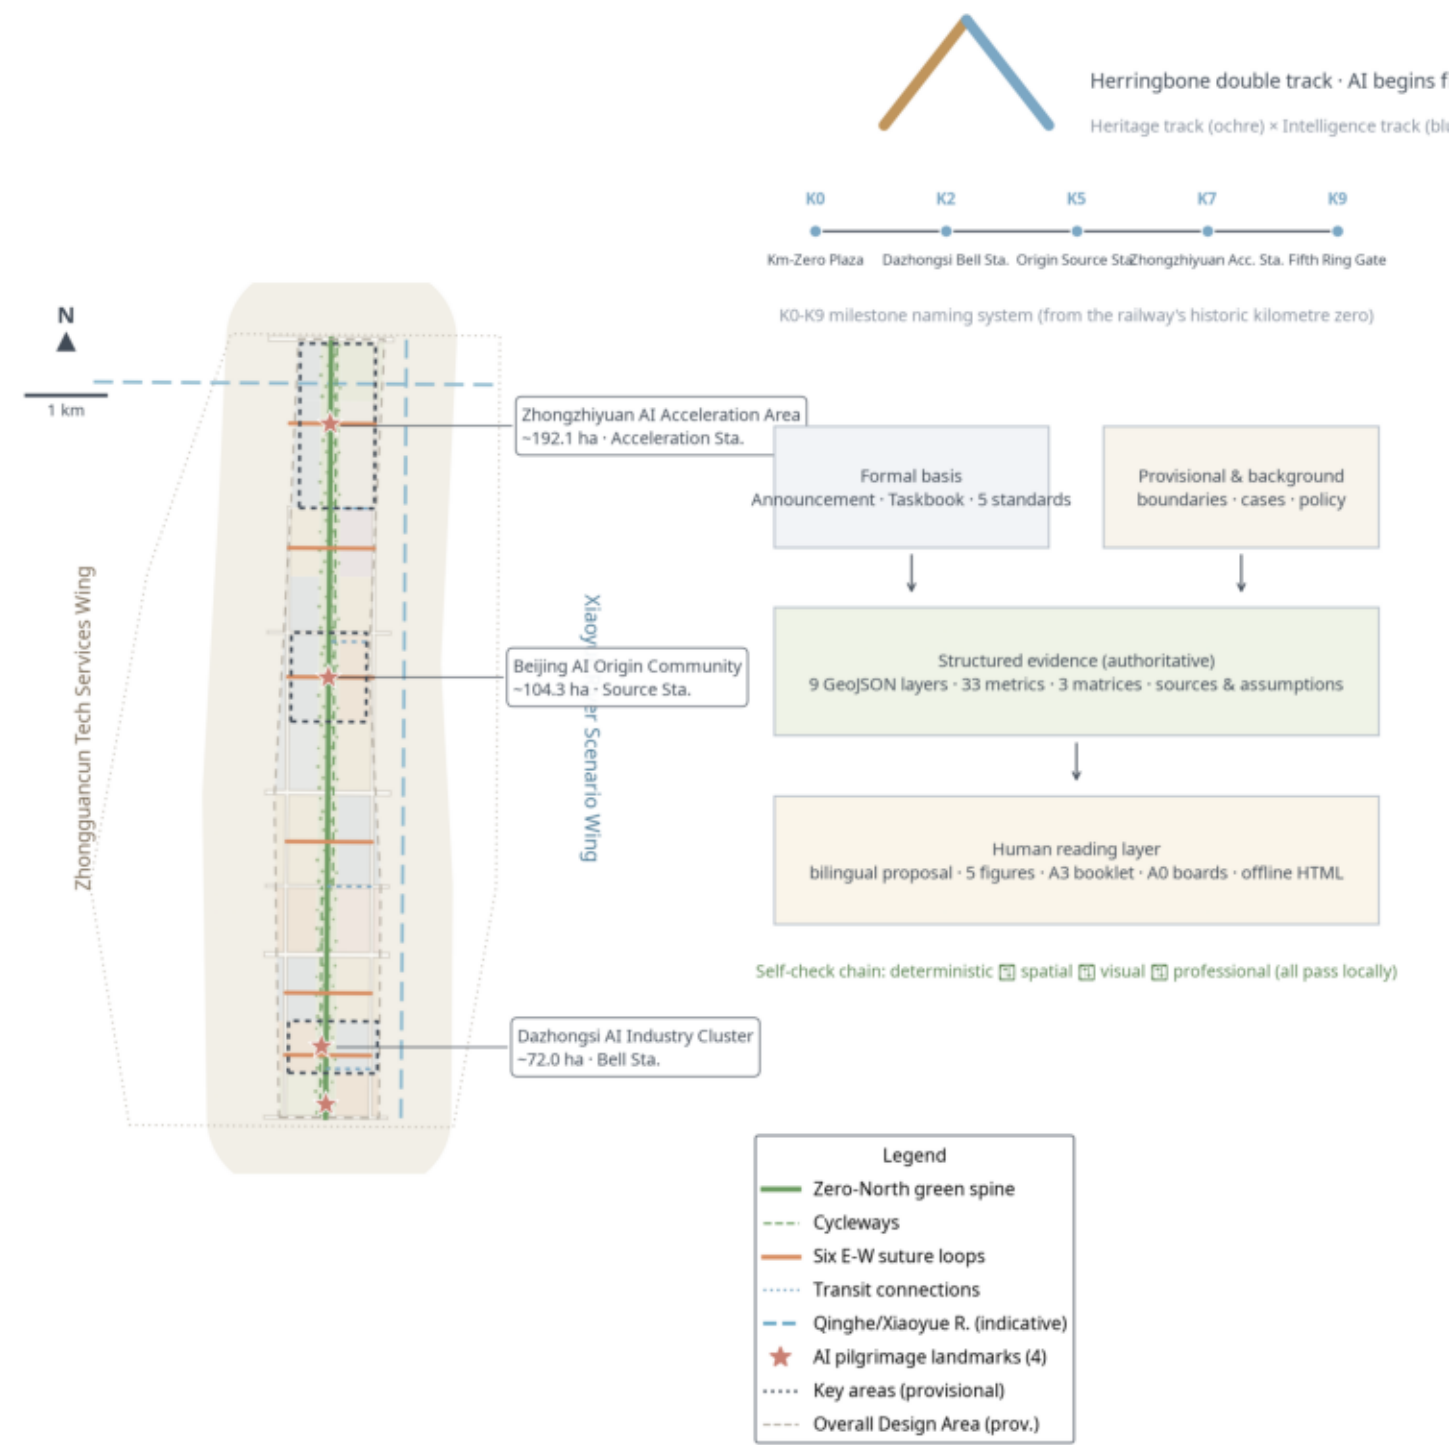

Data: package geometry/*.geojson + metrics.json (recomputed in EPSG:4548) · self-drawn basemap, no external map data
Provisional rough boundary (dashed): not an official redline, not for precise areas; full recalculation once official data arrives

Fig.2 Three-level scope & land-use structure (33 conceptual units, full partition)


Conceptual land-use recommendation, not a statutory approval · areas in EPSG:4548

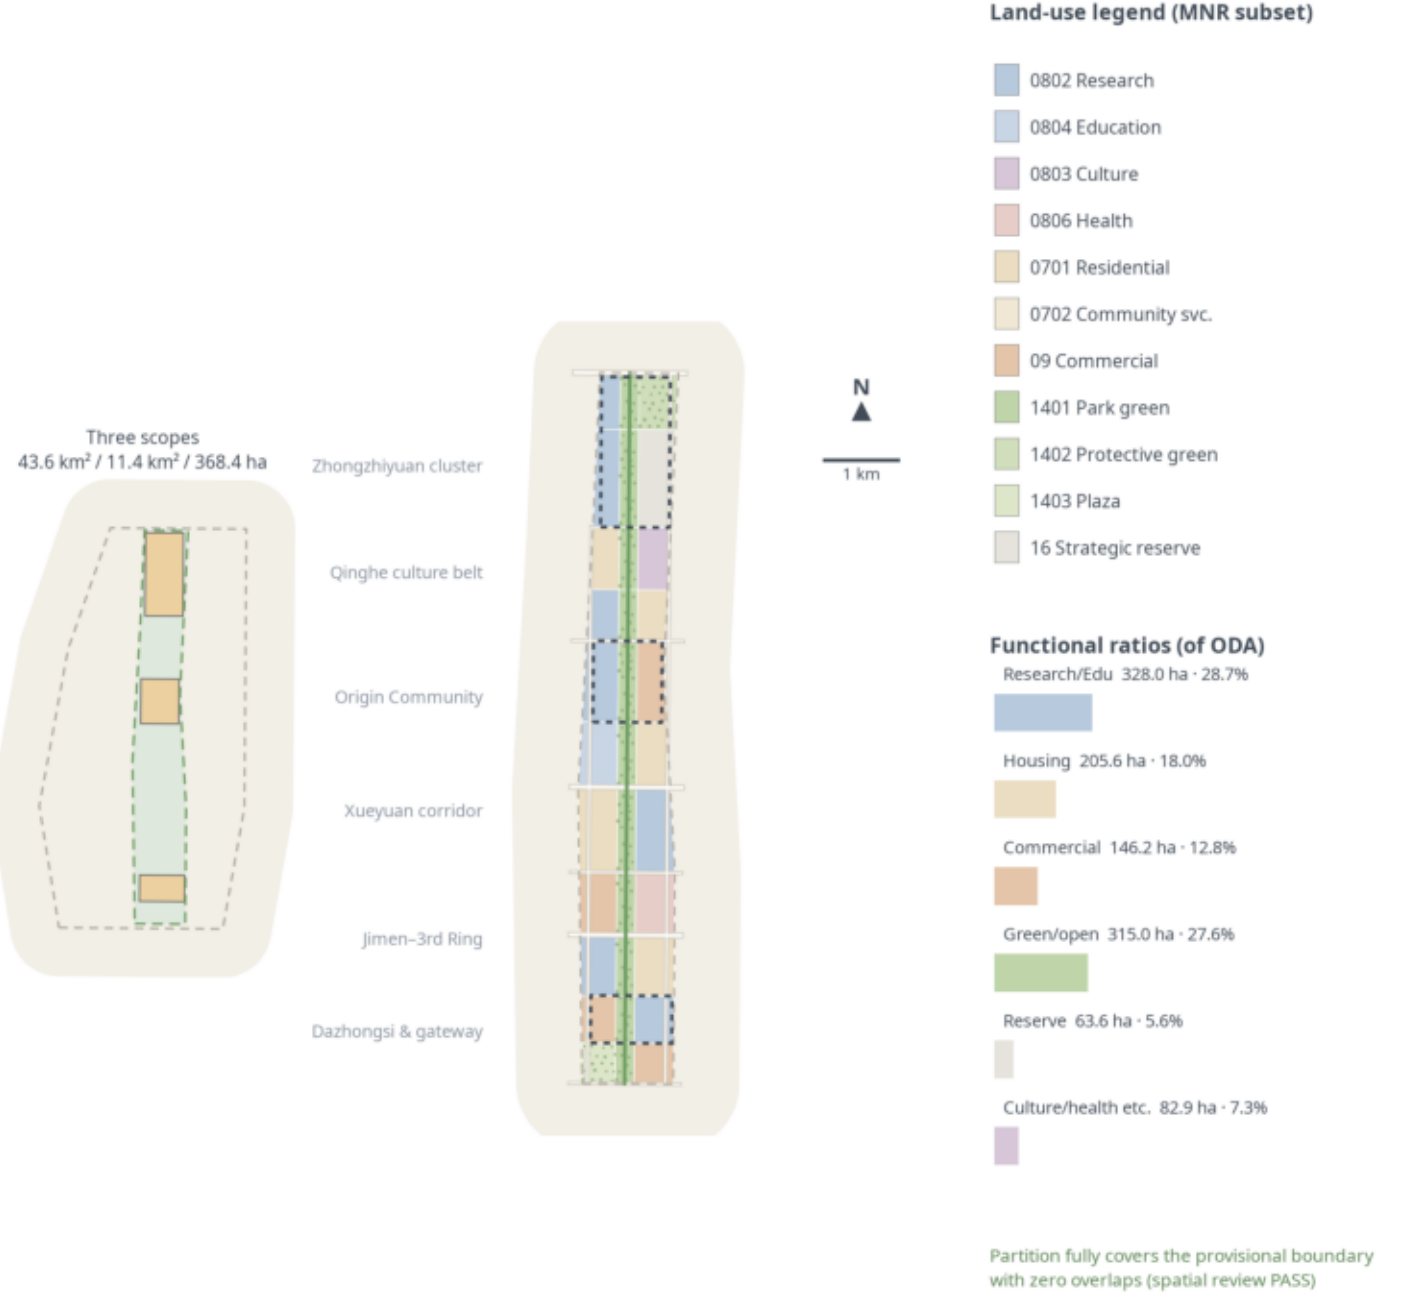


Data: package geometry/*.geojson + metrics.json (recomputed in EPSG:4548) · self-drawn basemap, no external map data
Provisional rough boundary (dashed): not an official redline, not for precise areas; full recalculation once official data arrives

Section studies: three urban characters of one green spine


Section A-A · Zhongzhiyuan (K7-K8): low-rise R&D courts × 240 m green spine × reserve units

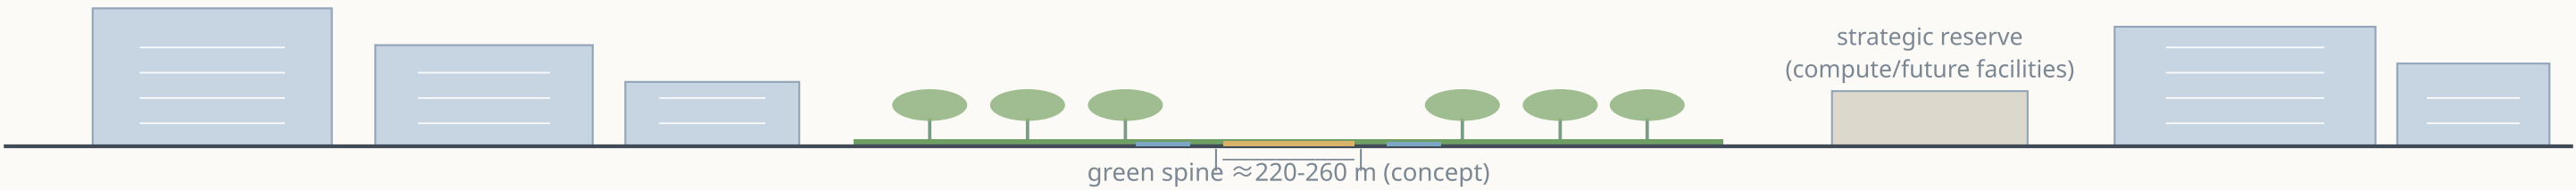

Section B-B · Origin Community (K5): fine-grain courts × Herringbone suture × station integration

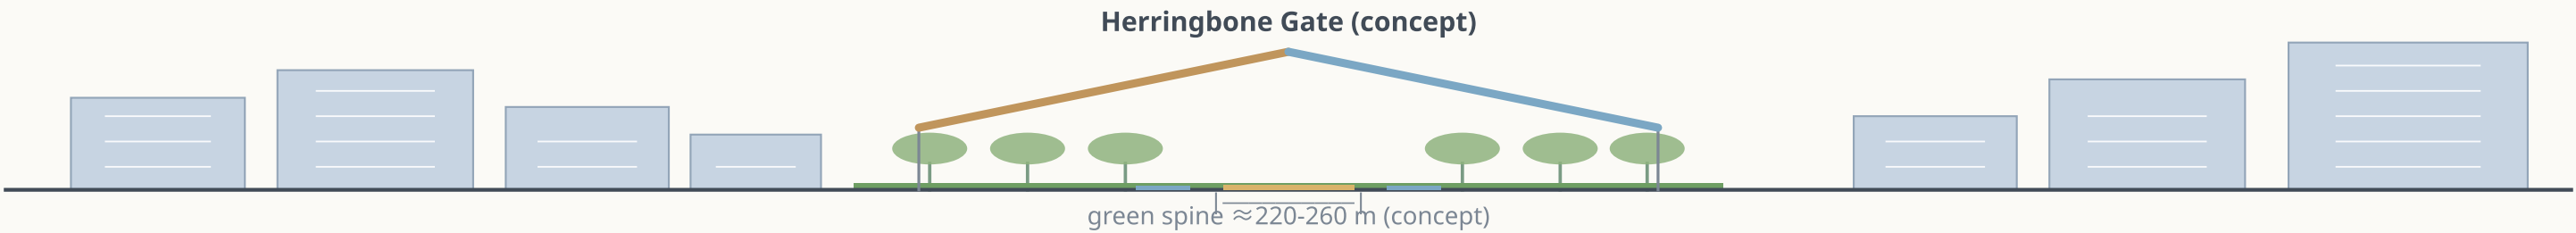

Section C-C · Dazhongsi (K2): retrofitted stock × four-quadrant station links

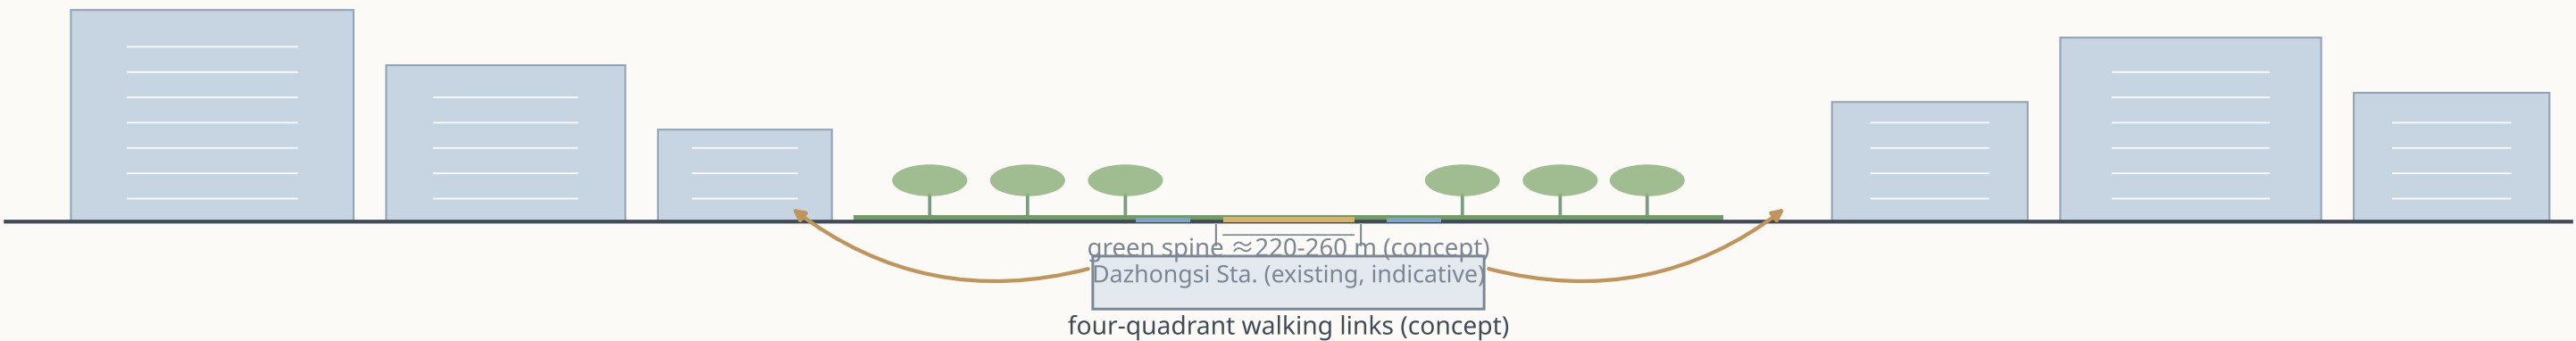

Sections are conceptual: spine width, building heights and the bridge form are morphological studies, not engineering; no feasibility conclusions on bridges/underground — for professional deepening.


Three hubs: the Ring, the Herringbone, the Quadrants

Fig.3 Detailed-design index of the three key areas (concepts within provisional boundaries)


Seven-part depth: positioning · structure · renewal · mobility · public space · AI scenarios · risk

NORTH OF ZERO

Zhongzhiyuan · Acceleration
Garden-type full-stack district: the Ring, reserve units, micro-grid pilot

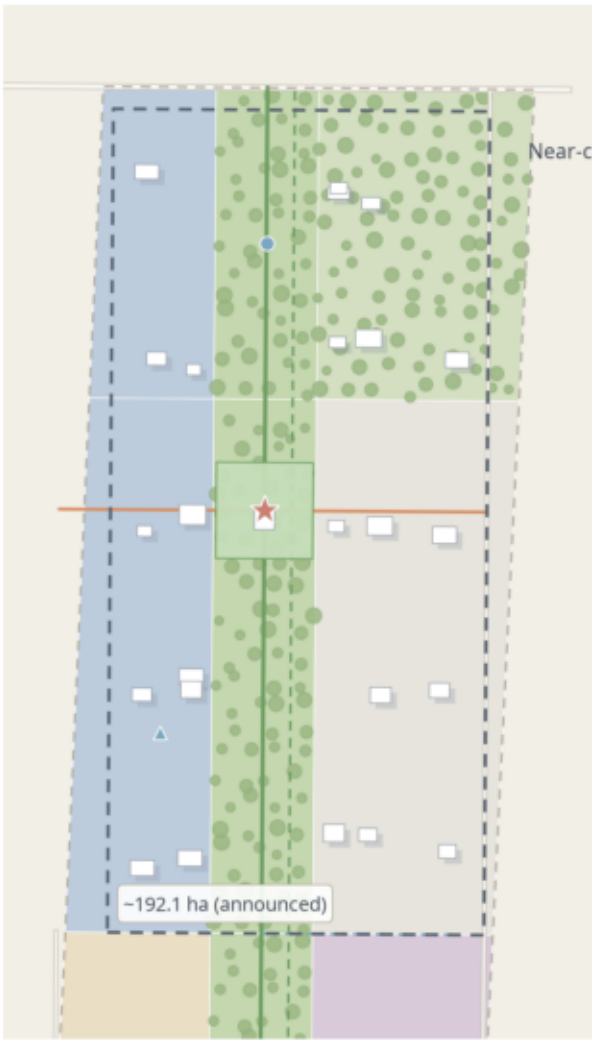

Origin Community · Source
Near-campus district: Herringbone Gate, low-disturbance renewal, station integration

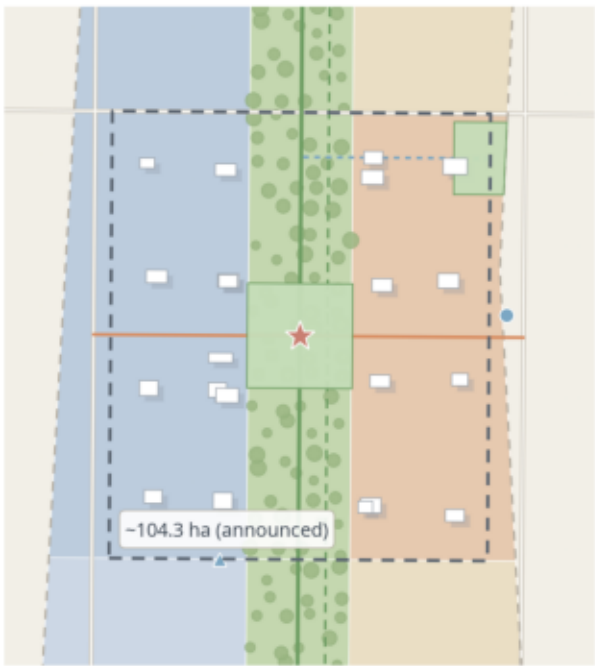

Dazhongsi · Bell
Urban district: four-quadrant links, AI-native formats, AV pilot



- Concept massing (64, not architecture)

Node plazas & forecourts

Suture loops

Green spine

★

Landmarks


▲

Testing scenarios

.....

Provisional key-area boundary

Data: package geometry/*.geojson + metrics.json (recomputed in EPSG:4548) · self-drawn basemap, no external map data
Provisional rough boundary (dashed): not an official redline, not for precise areas; full recalculation once official data arrives

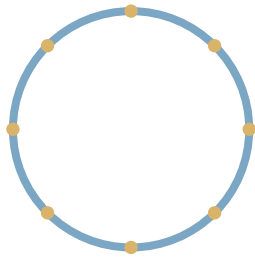

Zhongzhiyuan · Acceleration

K7-K8 · 192.1 ha

The Ring organizes full-stack clusters and reserve units; micro-grid pilot first.

Seven parts: positioning→risk




Origin · Source

K5 · 104.3 ha

The Herringbone Gate sutures campus, park and community; low-disturbance renewal keeps the grain.

Seven parts: positioning→risk

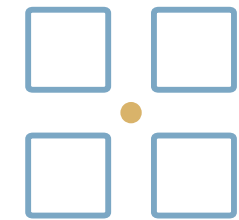


Dazhongsi · Bell

K2 · 72.0 ha

Four-quadrant links dissolve severance; AI-native formats take the street level.

Seven parts: positioning→risk

The Herringbone Gate: axonometric view of the Origin Community (concept)

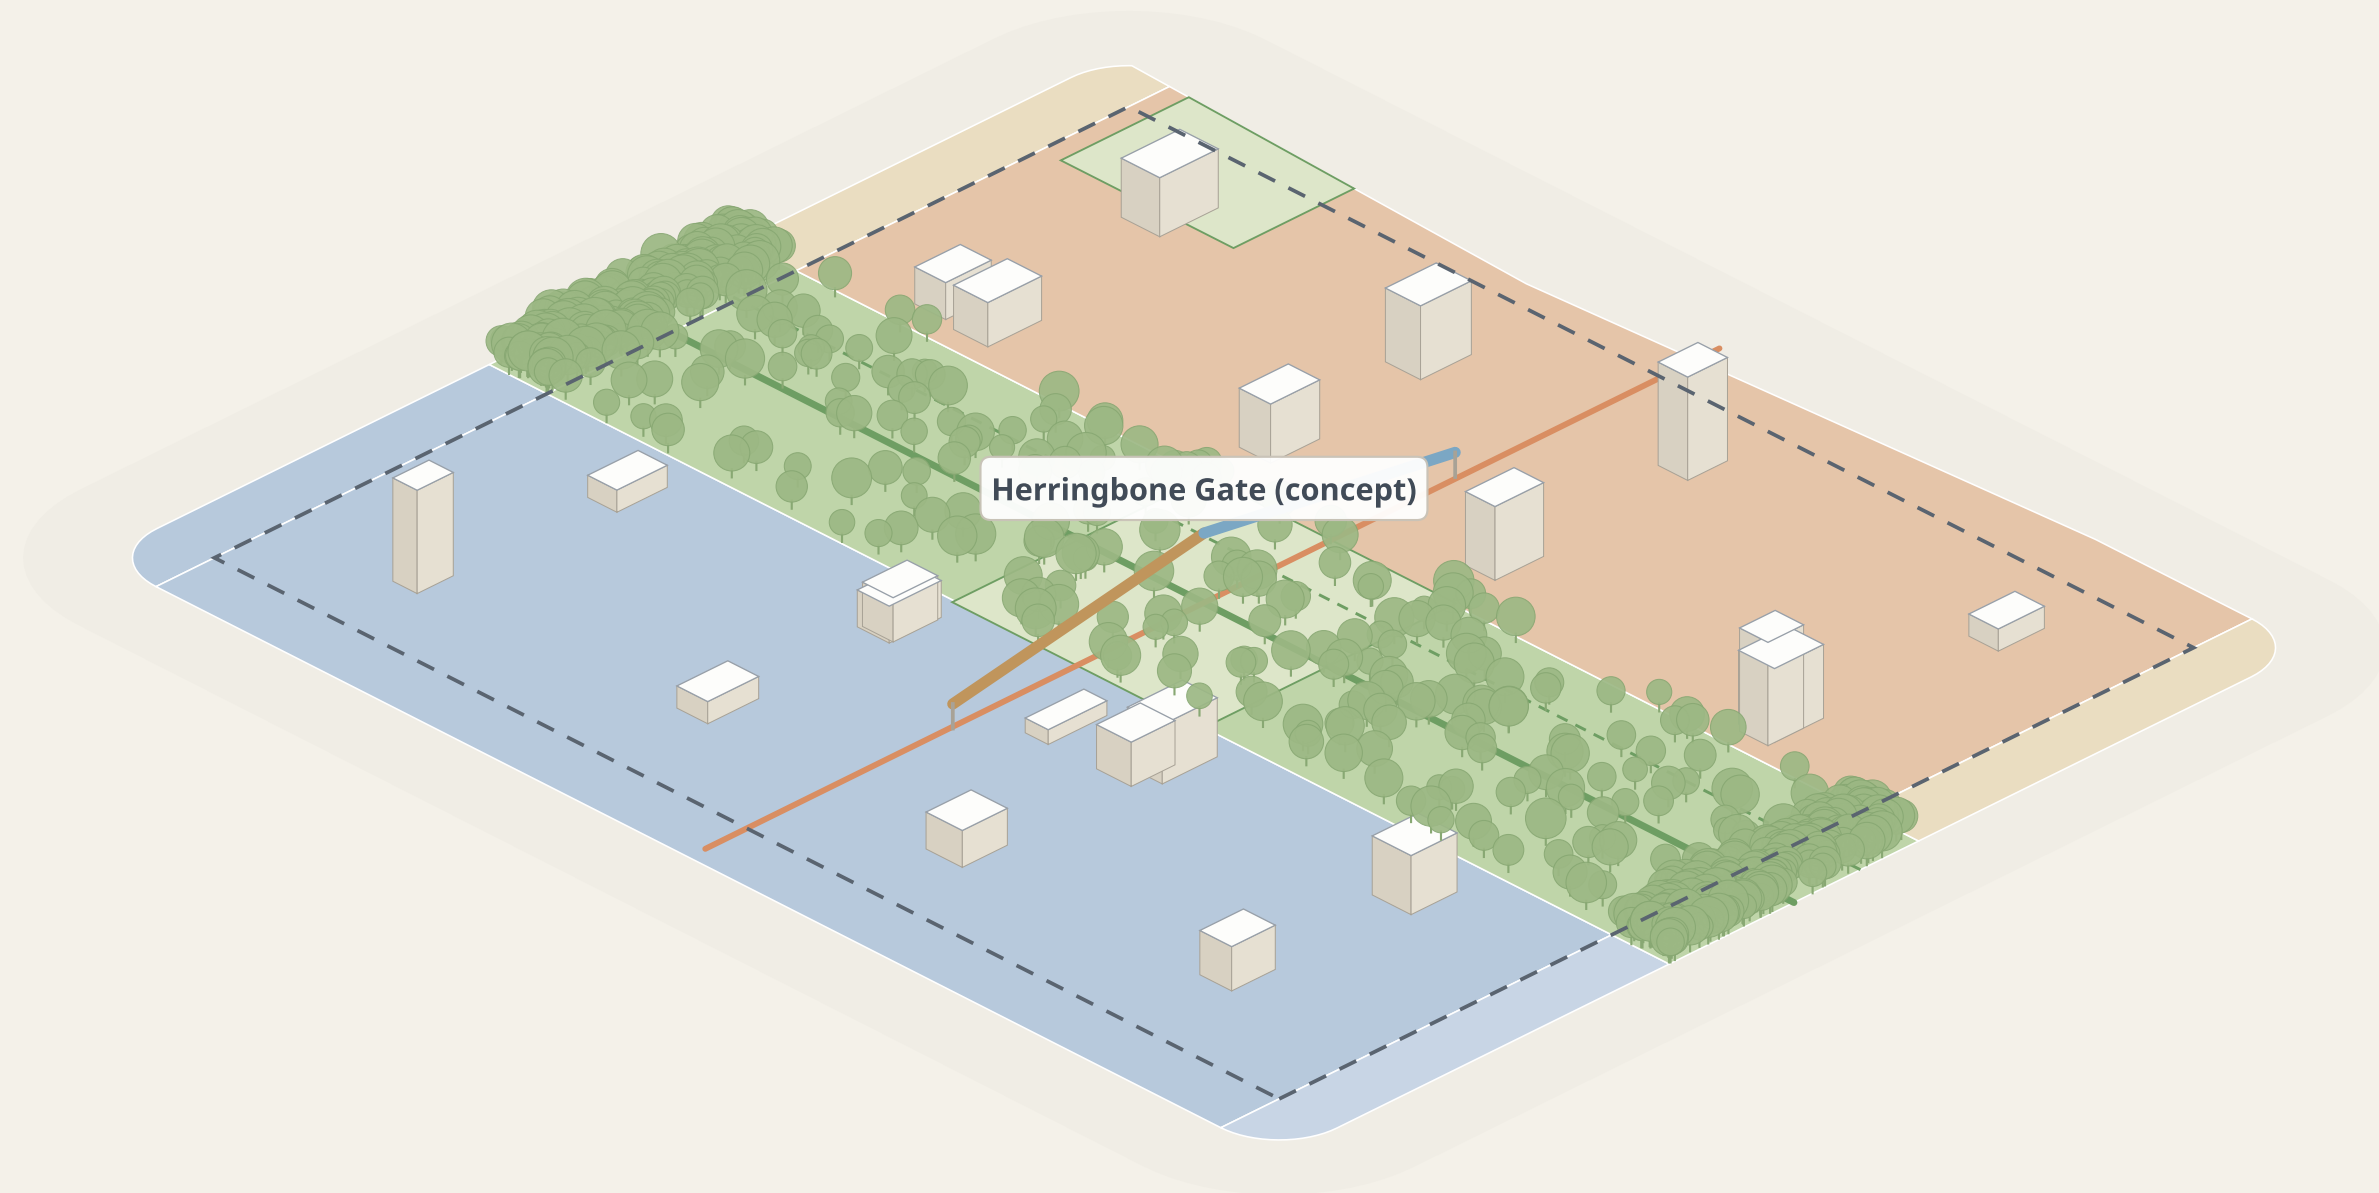

Why 人


In 1909 Zhan Tianyou beat the grade with a herringbone alignment; today two tracks merge into 人 — AI begins from the human origin.

What it does

The crossing of loop L3: transfer
cluster west, Wudaokou street east;
the heritage gallery sits beneath.

Boundary

The axon is conceptual massing, not architecture; heritage exhibition subject to approval; no engineering conclusions.

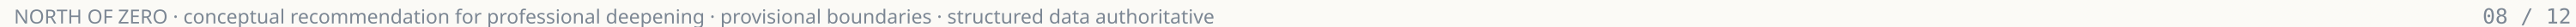

Twelve scenario tickets — stamped ones are testing & validation

S01 K0-K9	Greenway AI companion P4·P5	S02 L3	Suture smart crossing P4 T	S03 L4	Robot delivery hub P2·P4 T
S04 HT line	AI cultural guide P5	S05 K2	Enterprise copilot P3	S06 L4	Health navigation P4
S07 L1-L6	Ops-review agent P6	S08 K5-E	Agent-native retail P2·P5	S09 K5-W	Transfer matchmaking P1·P2
S10 K8	Edge compute grid P2·P6 T	S11 K2	AV shuttle loop P3·P4 T	S12 K0	Honor & memory P1·P5

One rule for every ride: public/authorized data only · no identification or profiling · on-site anonymized aggregation · human review of key decisions · testing ≠ approved operation

Six riders and one day on North of Zero

P1

Researcher

home station K5

near-campus transfer space

P2

Startup engineer

home station K7

flexible desks · compute quota

P3

Industry operator

home station K2

one-stop services · roadshows

P4

Resident family

home station K4

human channels · accessibility

P5

Intl. visitor

home station K0

bilingual wayfinding · pilgrimage

P6


City operator

home station L1-L6


reviewable tools · clear duty

One day (a startup engineer, narrative concept)




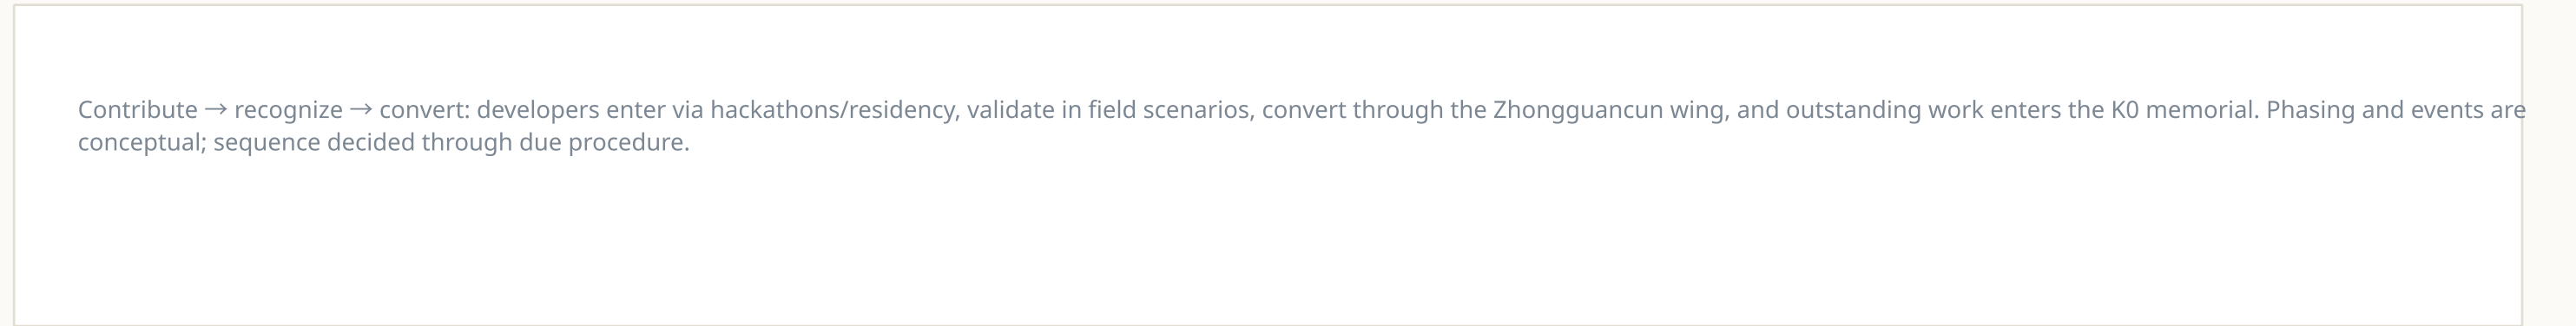


Dashboard & compliance: every number recomputes

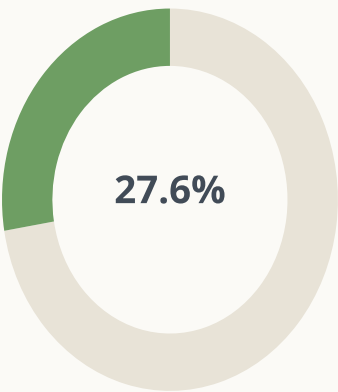


green ratio

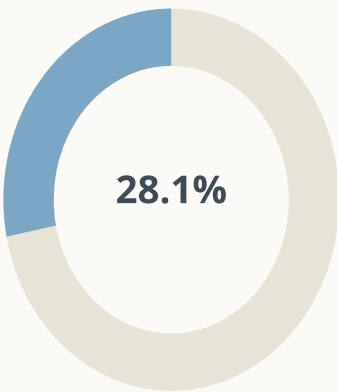

composite public space

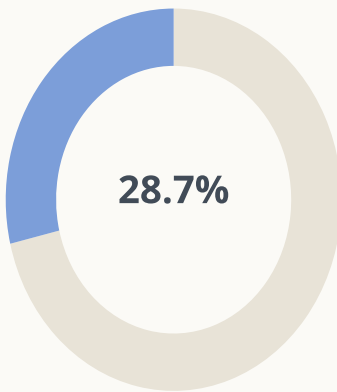

research/education land

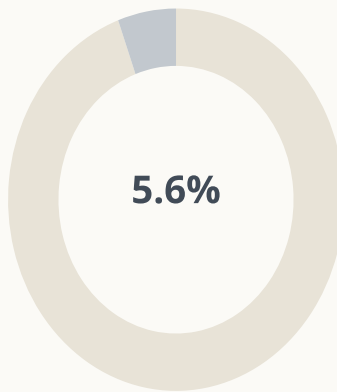

strategic reserve



tasks covered



four local reviews

Recomputation (EPSG:4548)

Overall Design Area	11,412,825 m²	~11.4 km² announced · Δ0.11%
Key areas total	3,692,893 m²	368.4 ha announced · Δ0.24%
Slow network	25,838 m	greenway + cycle + loops
Concept floor area	942,008 m²	low conf. · FAR pending

Compliance & rights

- 23 tasks / 5 standards / 15 depth items in three matrices
- 22 sources with licenses; cases marked "not verified offline"
- AI-generation disclosed: Anthropic Claude × Claude Code; open toolchain
- Font: WQY Zen Hei (GPL + exception) · no external map/imagery
- Privacy: anonymized aggregation + human review; testing ≠operation

The largest uncertainty is the official data gap: precise boundaries, regulatory conditions, building inventory, heritage lines and municipal capacity all pending. Everything is downgraded to conceptual recommendations with registered recalculation triggers; once official polygons arrive, the whole package regenerates.