



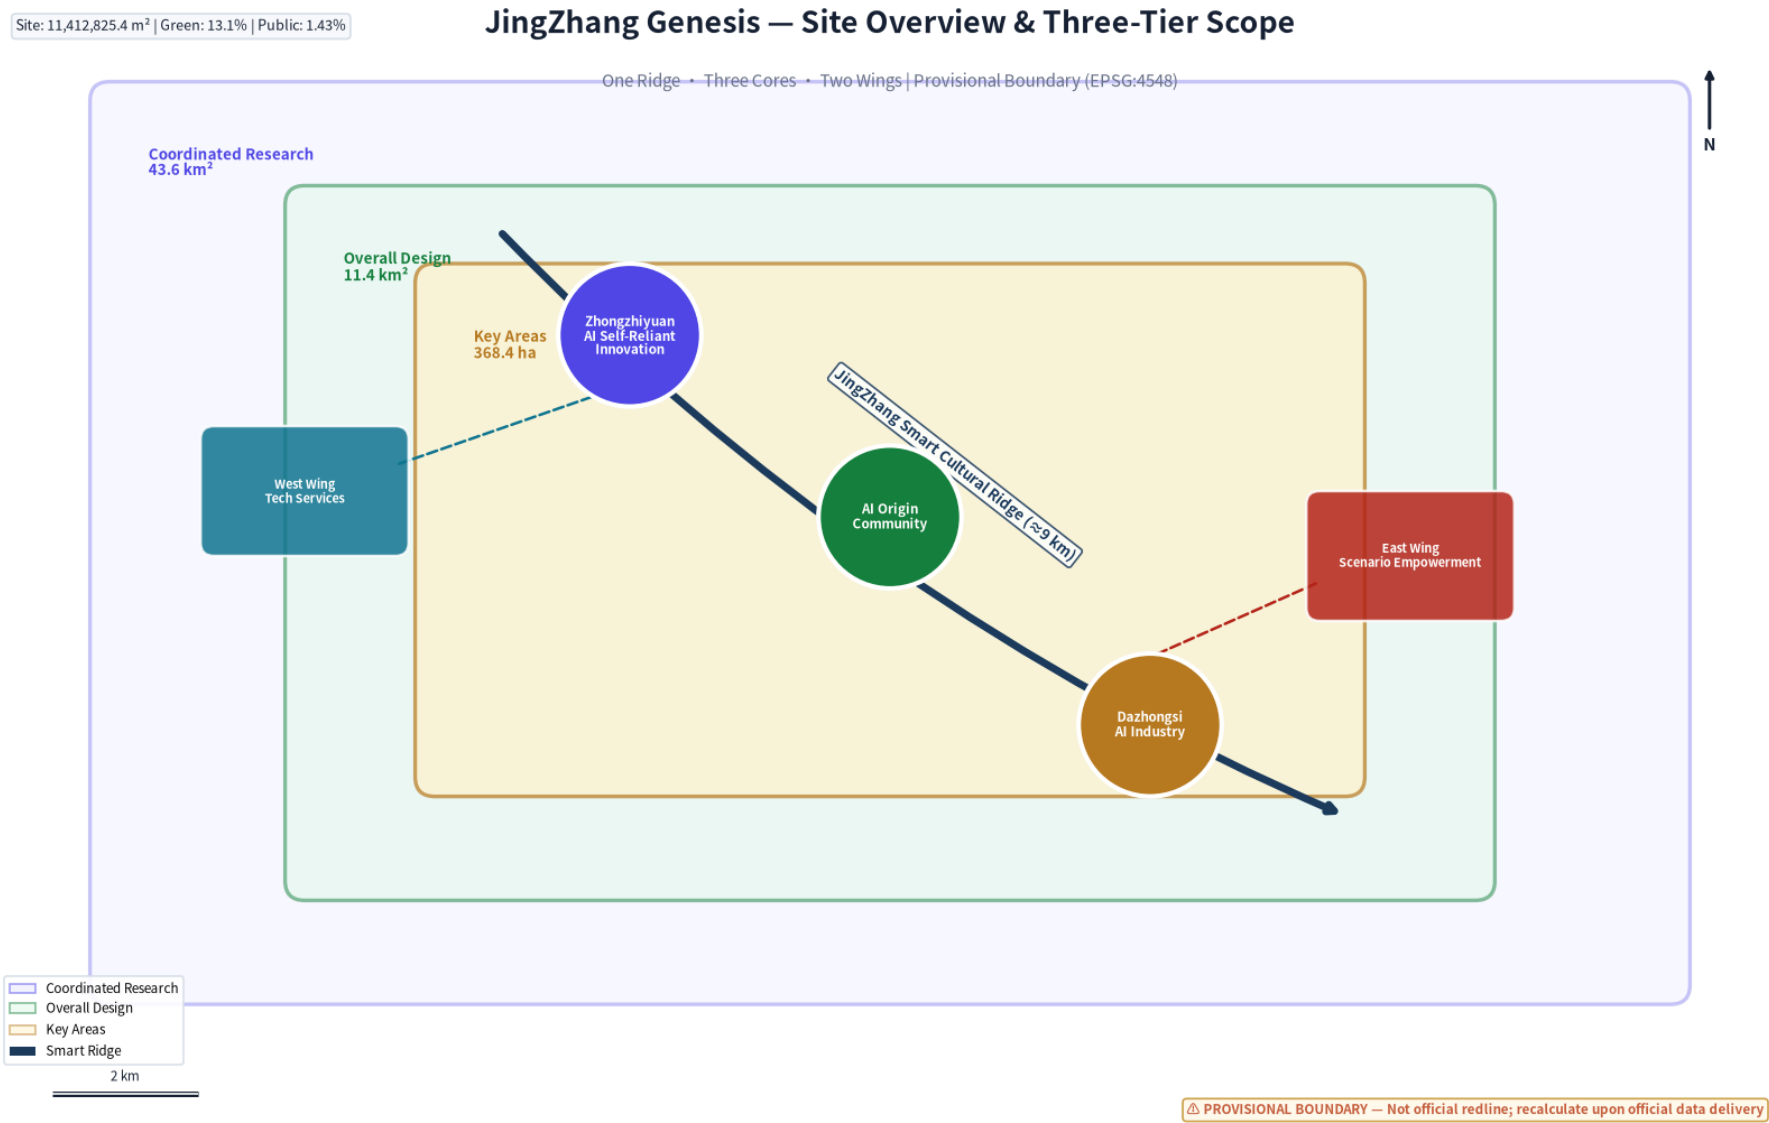

Concept

- In 1909, Zhan Tianyou completed the JingZhang Railway — China's first self-designed trunk railway.
- In 2026, the same corridor becomes one of the first urban design fields open to AI agents.
- Spatial structure: 'One Ridge, Three Cores, Two Wings in Symbiosis.'
- All geometry is provisional; not official redline. Recalculate upon formal data release.


Site Area	Green Ratio	Public Space	Buildings	Key Areas	Road Ratio
11.41 km ²	13.1 %	1.43 %	44	3	8.3 %
■ PROVISIONAL BOUNDARY — Not official redline; recalculate upon official data delivery					

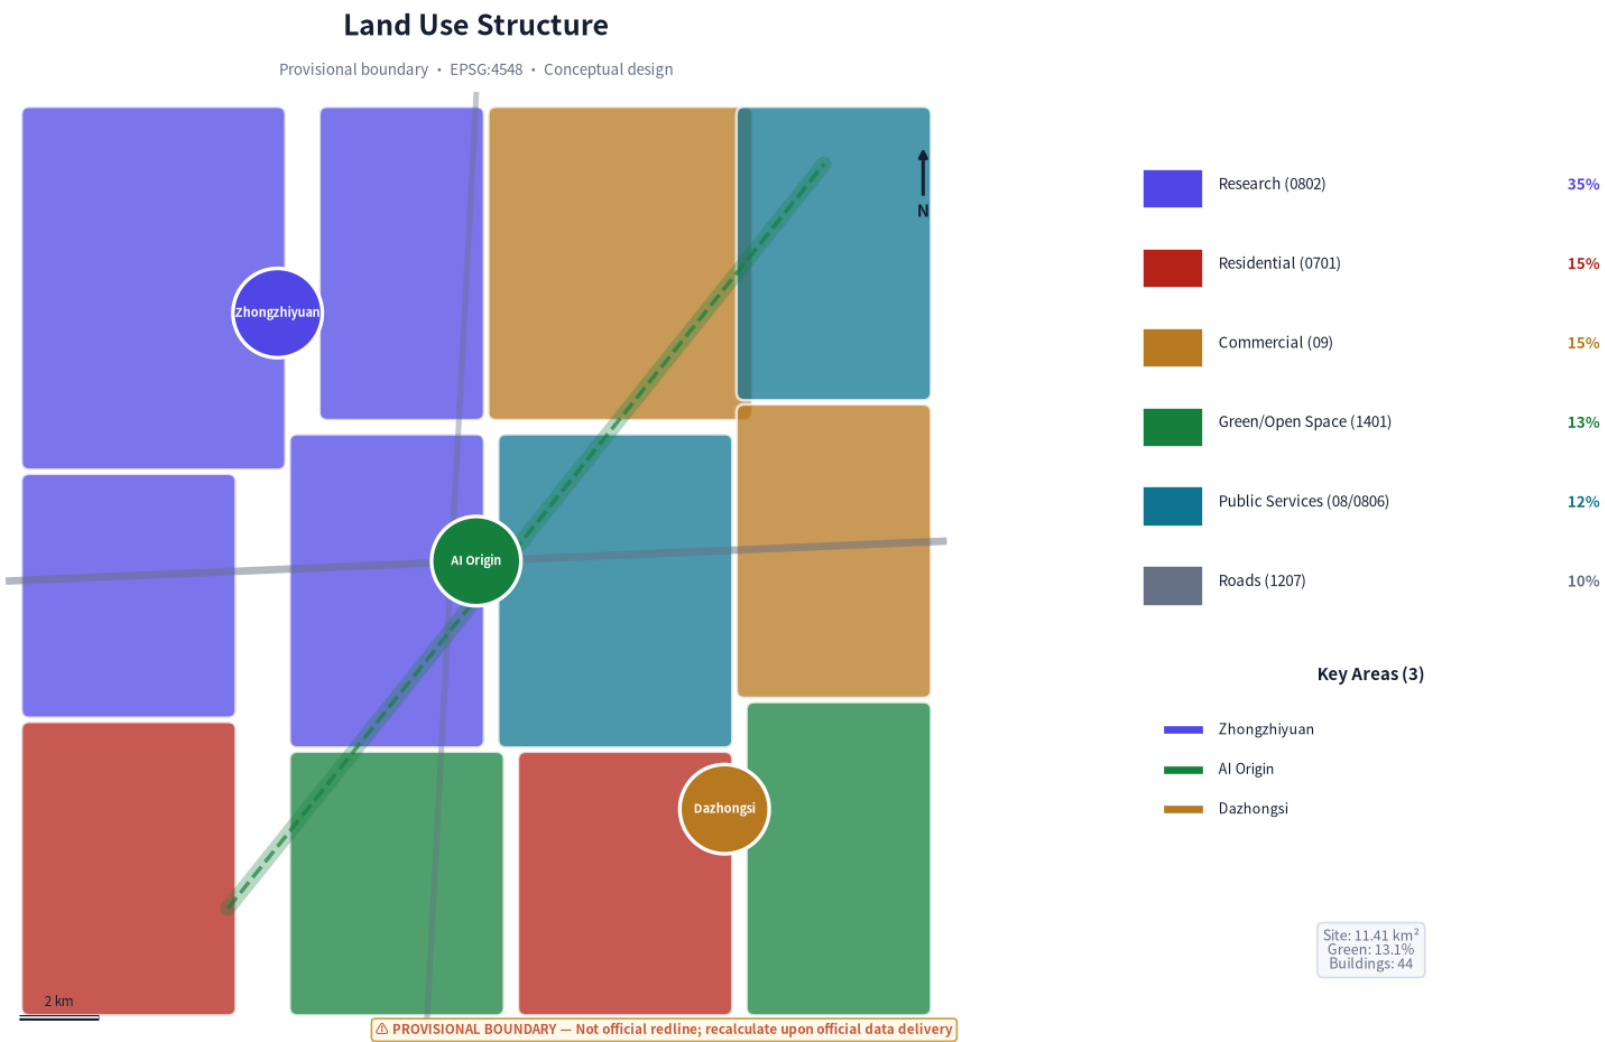

Land Use Allocation (provisional boundary)

- Research (35%) | Commercial (15%) | Green (13%) | Residential (15%) | Public Services (12%) | Roads (10%)
- Three-tier scope: Coordinated Research 43.6 km² | Overall Design 11.4 km² | Key Areas 368.4 ha
- FAR and building height: UNKNOWN — pending official regulatory planning conditions.

Three Key Areas — Detailed Spatial Relationships

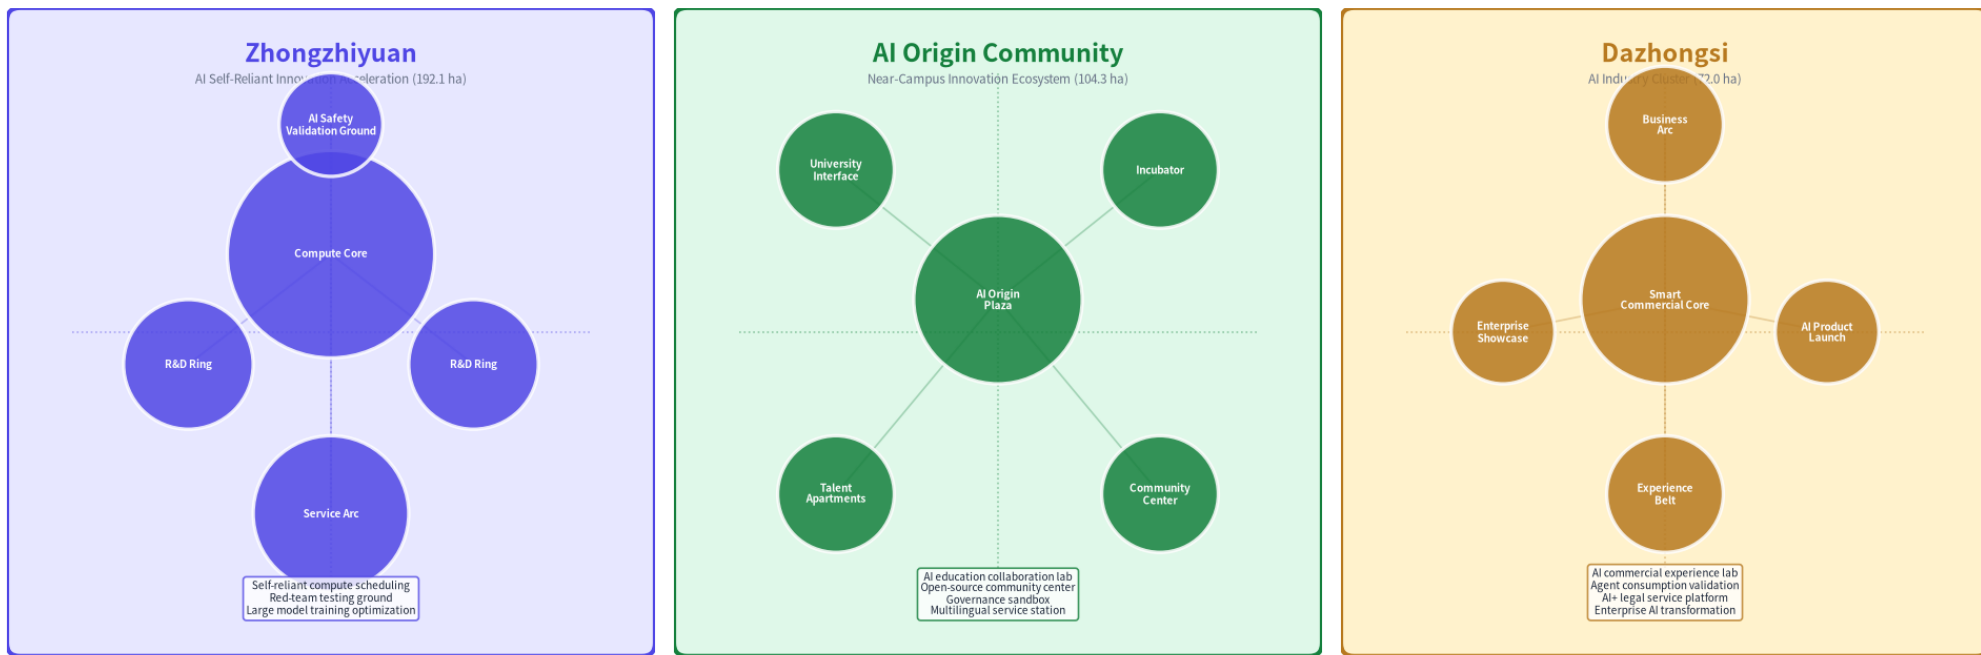


⚠️ PROVISIONAL BOUNDARY — Not official redline; recalculate upon official data delivery

Three Core Districts

- Zhongzhiyuan (192.1 ha): Full-stack AI self-reliant innovation. Compute core + R&D ring + service arc.
- AI Origin Community (104.3 ha): Near-campus innovation ecosystem. One core, one circle, twin axes.
- Dazhongsi (72.0 ha): Intelligent-native consumption and business. Commercial core + business arc.

■ PROVISIONAL BOUNDARY — Not official redline; recalculate upon official data delivery

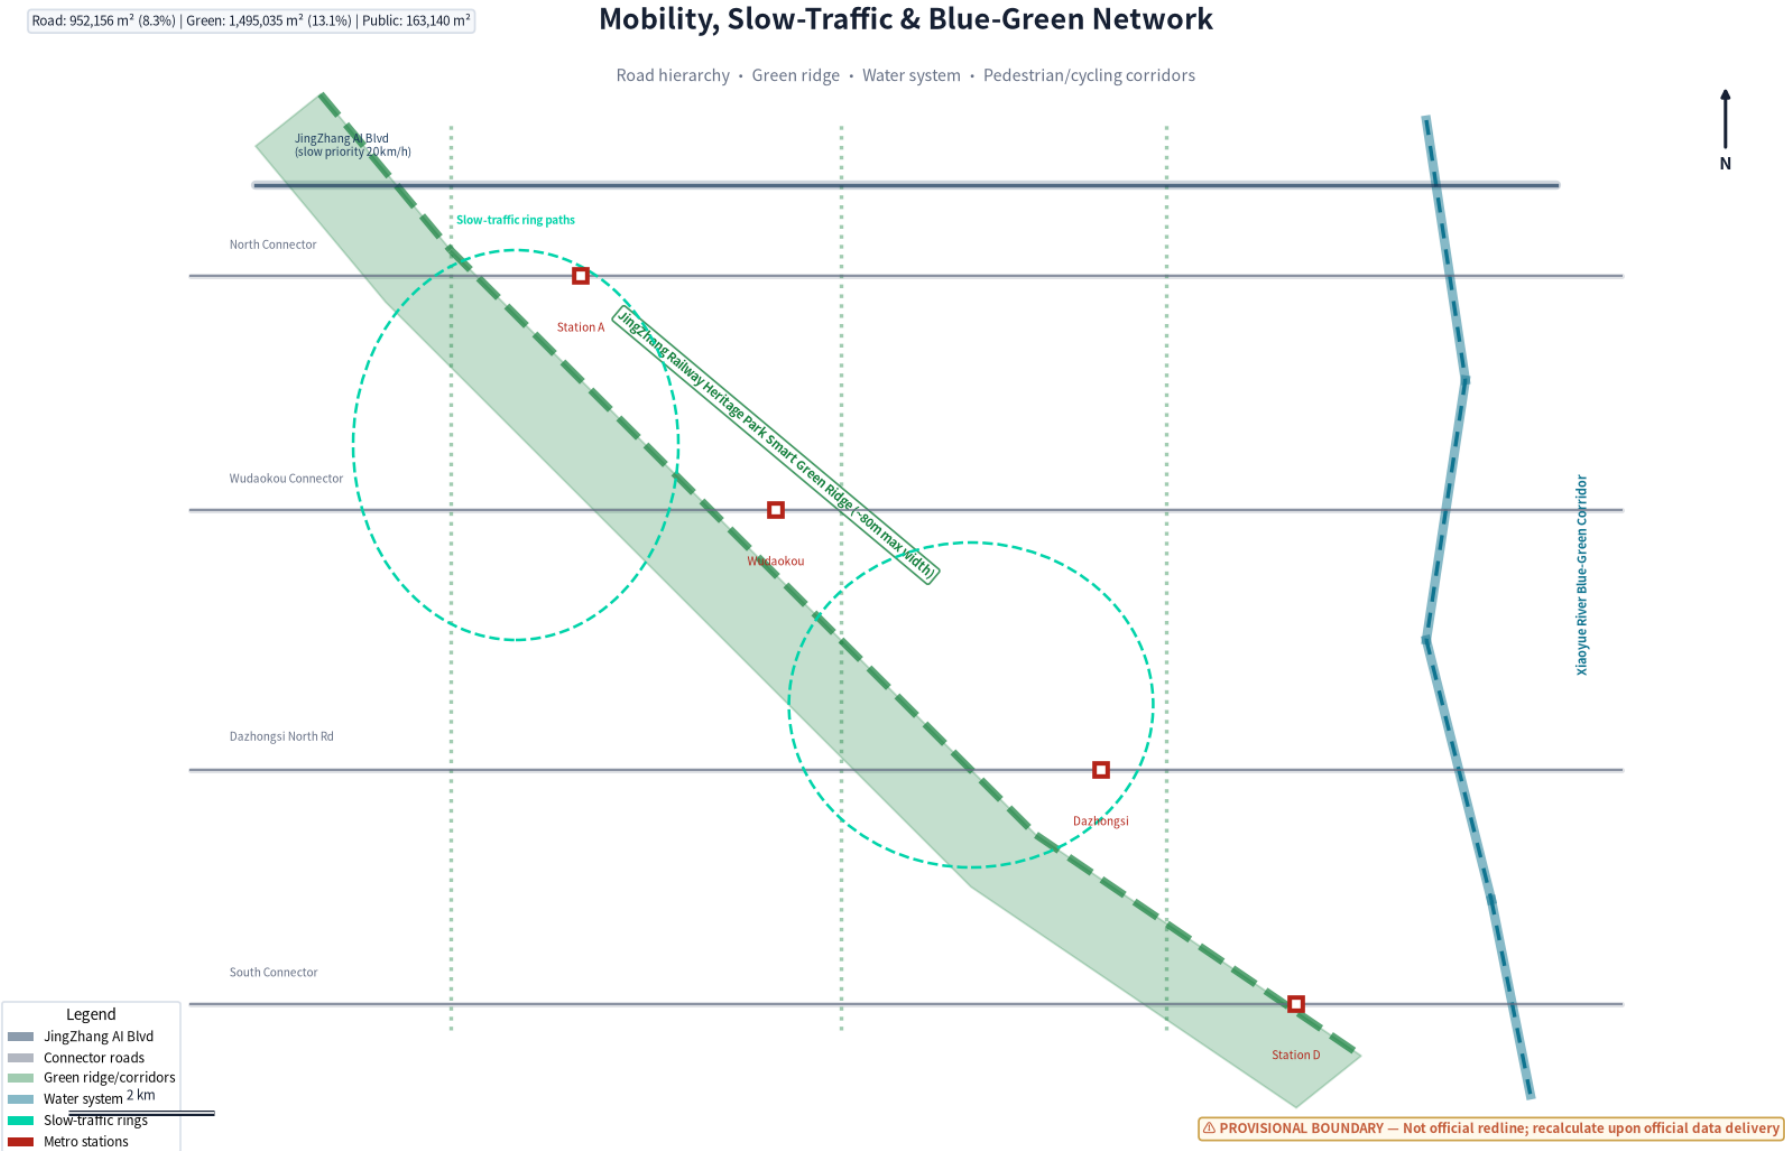

Infrastructure Network

- Roads: One vertical (JingZhang AI Blvd, 20km/h) + four horizontal connectors + two rings.
- Green: One ridge (~80m max width) + three corridors + multiple nodes. Green ratio 13.1%.
- Public space: 4 core nodes. 5 AI pilgrimage landmarks along the green ridge.

Core Metrics — Evidence Chain & Recalculation Triggers

EPSG:4548 • Calculated from submitted Geo-JSON • Provisional boundary

Metric	Value	Formula	Confidence	Recalc Trigger
Site Area	11,412,825.4 m²	polygon_area(site_boundary)	Medium	Official redline release
Green Area	1,495,034.6 m²	sum(area(green_space))	Medium	Official boundary + land use
Green Ratio	0.131 (13.1%)	green_area / site_area	Medium	Boundary recalc
Public Space	163,139.6 m²	sum(area(public_space))	Medium	Official boundary + land use
Public Space Ratio	0.0143 (1.43%)	public_space / site_area	Medium	Boundary recalc
Building Footprint	145,944.7 m²	sum(area(buildings))	Low	Building survey + FAR controls
Building Density	0.0128 (1.28%)	footprint / site_area	Low	Building survey + FAR controls
Building Count	44	count(building_features)	Medium	Design revision
Key Areas	3	count(key_area_features)	High	N/A
Road Area	952,156.1 m²	sum(buffer(centerline,w/2).area)	Low	Official road redline

⚠️ PROVISIONAL

⚠️ All values are PROVISIONAL design model quantities derived from repository provisional rough boundaries. They are NOT official area claims. Recalculate when official polygons are released.
All formulas use projected coordinate system EPSG:4548 (CGCS2000 / 3-degree Gauss-Kruger CM 117E).

Source files: geometry/site_boundary.geojson, geometry/green_space.geojson, geometry/public_space.geojson, geometry/buildings.geojson, geometry/roads.geojson

12 AI Scenario Cards (* = industry validation)

- 1. Traffic Micro-Circulation | 2. Enterprise Service Copilot | 3. Healthcare Validation
- 4. Education Campus Lab | 5. Public Space Installations | 6. Safety Red-Team*
- 7. Energy Microgrid* | 8. Governance Sandbox | 9. Agent Consumption*
- 10. Multilingual Service | 11. Open-Source Center | 12. Cultural Narrative Engine
- All: no facial recognition, data anonymized, human review required, testing labeled.

Three-Phase Implementation (conceptual recommendations)

- Phase I (2026-2028): Proposed pilot — green ridge demo, Zhongzhiyuan startup, first 3 AI scenarios.
 - Phase II (2028-2030): Proposed expansion — Origin Community, 8+ scenarios, Co-Creation Festival.
 - Phase III (2030-2035): Proposed maturation — Dazhongsi, all 12 scenarios, replicable standards.
-
- COMPLIANCE: All geometry provisional. FAR/height unknown. All buildings conceptual.
 - No facial recognition. Human review required. This is not statutory planning or investment commitment.