

我，百年京张铁路，今天觉醒了感知系统——第二次测量：

可感京张感知基线带

京张铁路遗址公园感知提升与智慧慢行系统规划 · 十三章规划纪事

- 一百一十九年前测量的是这条铁路能通向多远，这一次测量的是人走在它上面是否好走、好停、好用。
- 全篇十三章，每章先讲故事再讲规划，各配一张规划图与一张概念效果图。
- 成果：13 张规划图、13 张概念效果图、1 张文化主视觉、9 个空间图层、21 项可复算指标。



图说：文化主视觉：确立“测量对象由线路转为人”的规划立意；本方案自制图像，非实景。

本方案以京张铁路遗址公园为规划对象，回答一个具体问题：沿线公共空间是否好走、好停、好用。规划把遮阴、绿视、驻留与夜间安全四类使用者感受转化为可复算、可复测的指标，据此确定更新顺序；把人工智能与低速智能设备安置在明确的空间位置与运行规则之内，使技术服务于日常通行而不占用通行；并把居民与青年研究人员的判断写进评估与整改流程，形成可以被重新测量、被修改的更新方法。

对应正文：卷首与全篇导读

数据与口径：范围面积、主轴长度与断面数量由空间数据在 EPSG:4548 下复算

使用边界：暂定研究边界；感知类指标为模型估算；低速设备线路与驿站为概念性建议，实施前须完成审批。

图 01 醒来：设计依据与资料清单

第一章 · 规划图

- 工作先建立资料分级再动笔：公告与任务书、国家与行业规范、公开地图与遗产资料、自建空间数据依次递减可信度。
- 据此形成“可直接使用、可概念推定、必须标注待明确、本次不采集”四张清单。
- 现状诊断的结论是这条线缺三样具体的东西——连续树荫、可坐的位置、敢走的照明，以及一样制度性的东西：把使用者判断写回规划的接口。



图说：图 01 区位与规划依据。外层虚线为暂定统筹研究范围（约 43.6 平方公里），内层为总体设计范围（11.41 平方公里），右侧两栏是本章实质内容：所依据的资料层级与各自能走多远。范围为暂定研究边界，非法定规划边界。

五月的清晨五点四十，青年规划师林深站在大钟寺北侧的路基上。护养工老陈推着车过来，伸出手指往南点了三下——那儿夏天晒得站不住，那儿有个轮椅上不去，再往南晚上灯是断的。这三根手指，成了整份规划要回答的问题。

对应正文：	第一章（醒来）
数据与口径：	图面由本方案空间数据直绘，面积与长度在 EPSG:4548 下复算
使用边界：	暂定研究边界；感知类指标为模型估算；低速设备线路与驿站为概念性建议，实施前须完成审批。

景 01 清晨的公共空间主轴

第一章 · 概念效果图

- 五月的清晨五点四十，青年规划师林深站在大钟寺北侧的路基上。
- 护养工老陈推着车过来，伸出手指往南点了三下——那儿夏天晒得站不住，那儿有个坎轮椅上不去，再往南晚上灯是断的。
- 概念效果图用于说明空间关系与使用方式，不表达建筑形式、层数与高度。



图说：景 01 清晨的主轴。钢轨留在铺装里当作记忆，树荫连续，坐处成组，路面平到轮椅可以自己走。概念效果图，非实景，不表达建筑形式与高度。

工作先建立资料分级再动笔：公告与任务书、国家与行业规范、公开地图与遗产资料、自建空间数据依次递减可信度；据此形成“可直接使用、可概念推定、必须标注待明确、本次不采集”四张清单。现状诊断的结论是这条线缺三样具体的东西——连续树荫、可坐的位置、敢走的照明，以及一样制度性的东西：把使用者判断写回规划的接口。

对应正文：第一章（醒来）

数据与口径：画面按主轴与重点地区相对位置绘制，不含强度与高度数据

使用边界：概念效果图非实景，不作为现状或建成状况证明；相关设施须经审批后实施。

第二章 · 规划图

景 02 全带鸟瞰

第二章 · 概念效果图

- 六月的评审会吵得不太客气：做产业的说范围太窄，做详细设计的说范围太宽。
- 主持会议的老工程师放下笔说：“那就准备三把尺子。”
- 概念效果图用于说明空间关系与使用方式，不表达建筑形式、层数与高度。



图说：景 02 全带鸟瞰。一条连续绿脊、两侧向它打开的首层、沿线三处分工不同的地区：北端接住到达的人，中段接住留下的人，南端接住来试验的人。概念效果图，非实景。


统筹研究层约 43.6 平方公里，只回答产业与人群趋势，不用用地方案；总体设计层 11.41 平方公里，做面向控规深化的概念性城市设计；重点地区层 3 处、369.2 公顷，做详细设计与断面整治标准做法。传导按五步固定：研究结论、空间结构、详细设计、现场复测、下一轮清单——后两步是自下而上的。

对应正文：	第二章（尺子的三种长度）
数据与口径：	画面按主轴与重点地区相对位置绘制，不含强度与高度数据
使用边界：	概念效果图非实景，不作为现状或建成状况证明；相关设施须经审批后实施。

图 03 实验室的门开向街道：产业与未来城市研究

第三章 · 规划图

- 创新功能确定三种公共面：门户服务面（大钟寺）、社区创新面（AI 原点社区）、验证展示面（众智园），共同要求首层开放、可步行到达、不设门禁式围合。
- 使用者分六类并落为空间需求。
- 国际经验按“可借鉴机制”与“须警惕教训”分列共 7 例，其中一例智慧社区因数据治理边界不清而终止，成为本方案数据条款的直接来源。

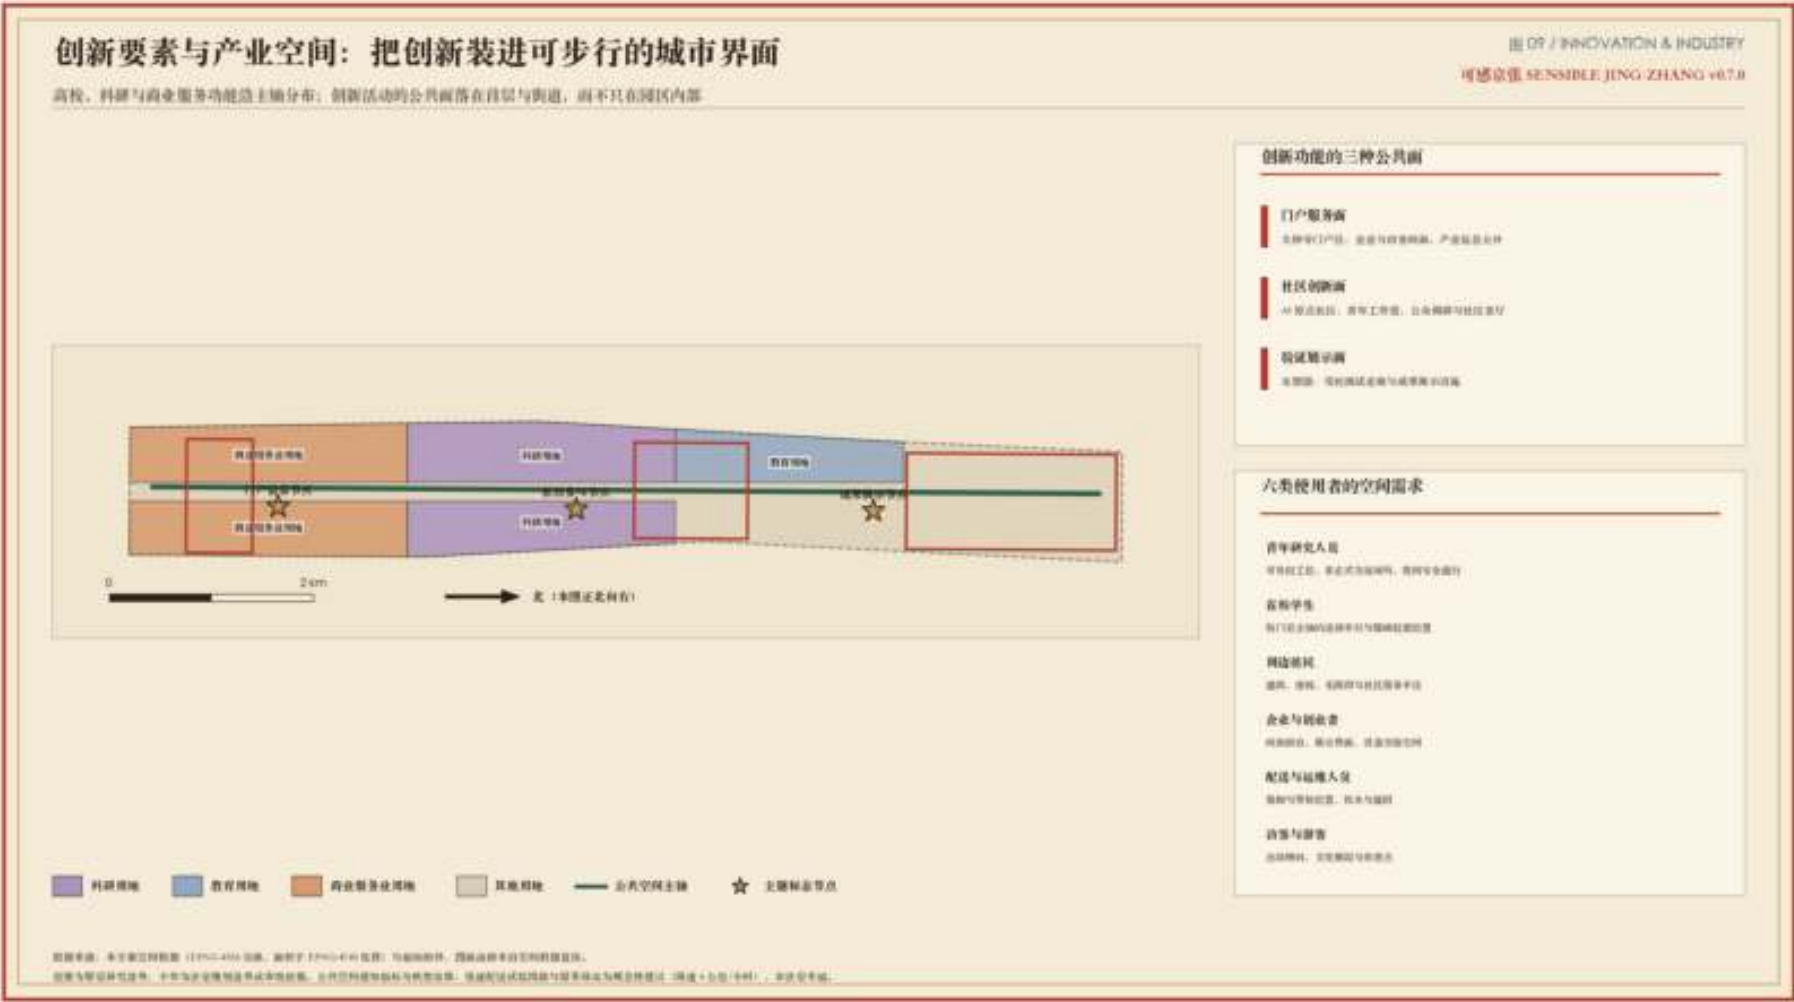

图说：图 03 创新要素与产业空间。科研、教育与商业服务用地几乎贴着主轴排列，说明创新功能与公共空间是一条界面的两面；右下表列出六类使用者各自需要的空间。

走访一家具身智能公司时，林深问机器人能走多远，工程师说楼里没问题，出了门情况就复杂了。另一处旧厂房的二楼，一位博士生边吃盒饭边说：需要一个不用消费也能坐两小时的地方。那天她在笔记上写下：把实验室的门开向街道。

对应正文：	第三章（实验室的门开向街道）
数据与口径：	图面由本方案空间数据直绘，面积与长度在 EPSG:4548 下复算
使用边界：	暂定研究边界；感知类指标为模型估算；低速设备线路与驿站为概念性建议，实施前须完成审批。

景 03 校园与园区创新界面

第三章 · 概念效果图

- 走访一家具身智能公司时，林深问机器人能走多远，工程师说楼里没问题，出了门情况就复杂了。
- 另一处旧厂房的二楼，一位博士生边吃盒饭边说：需要一个不用消费也能坐两小时的地方。
- 概念效果图用于说明空间关系与使用方式，不表达建筑形式、层数与高度。



图说：景 03 创新界面。首层是可以看进去的工坊，台阶就是座位，红砖车间改为入口，低速配送设备停在绿化带外侧、不进入人的通行带。概念效果图，非实景。


创新功能确定三种公共面：门户服务面（大钟寺）、社区创新面（AI 原点社区）、验证展示面（众智园），共同要求首层开放、可步行到达、不设门禁式围合。使用者分六类并落为空间需求。国际经验按“可借鉴机制”与“须警惕教训”分列共 7 例，其中一例智慧社区因数据治理边界不清而终止，成为本方案数据条款的直接来源。

对应正文：	第三章（实验室的门开向街道）
数据与口径：	画面按主轴与重点地区相对位置绘制，不含强度与高度数据
使用边界：	概念效果图非实景，不作为现状或建成状况证明；相关设施须经审批后实施。

图 04 一条脊、三个院、十八次停下：总体设计与城市更新

第四章 · 规划图

- 总体结构定为“一脊、三区、十八断面”。
- 评估维度四项合成短板指数，全线模型估算平均 0.416、最高 0.554，不低于 0.45 的 5 处构成一期对象。
- 十八断面按问题归为六族，各配一套标准做法。

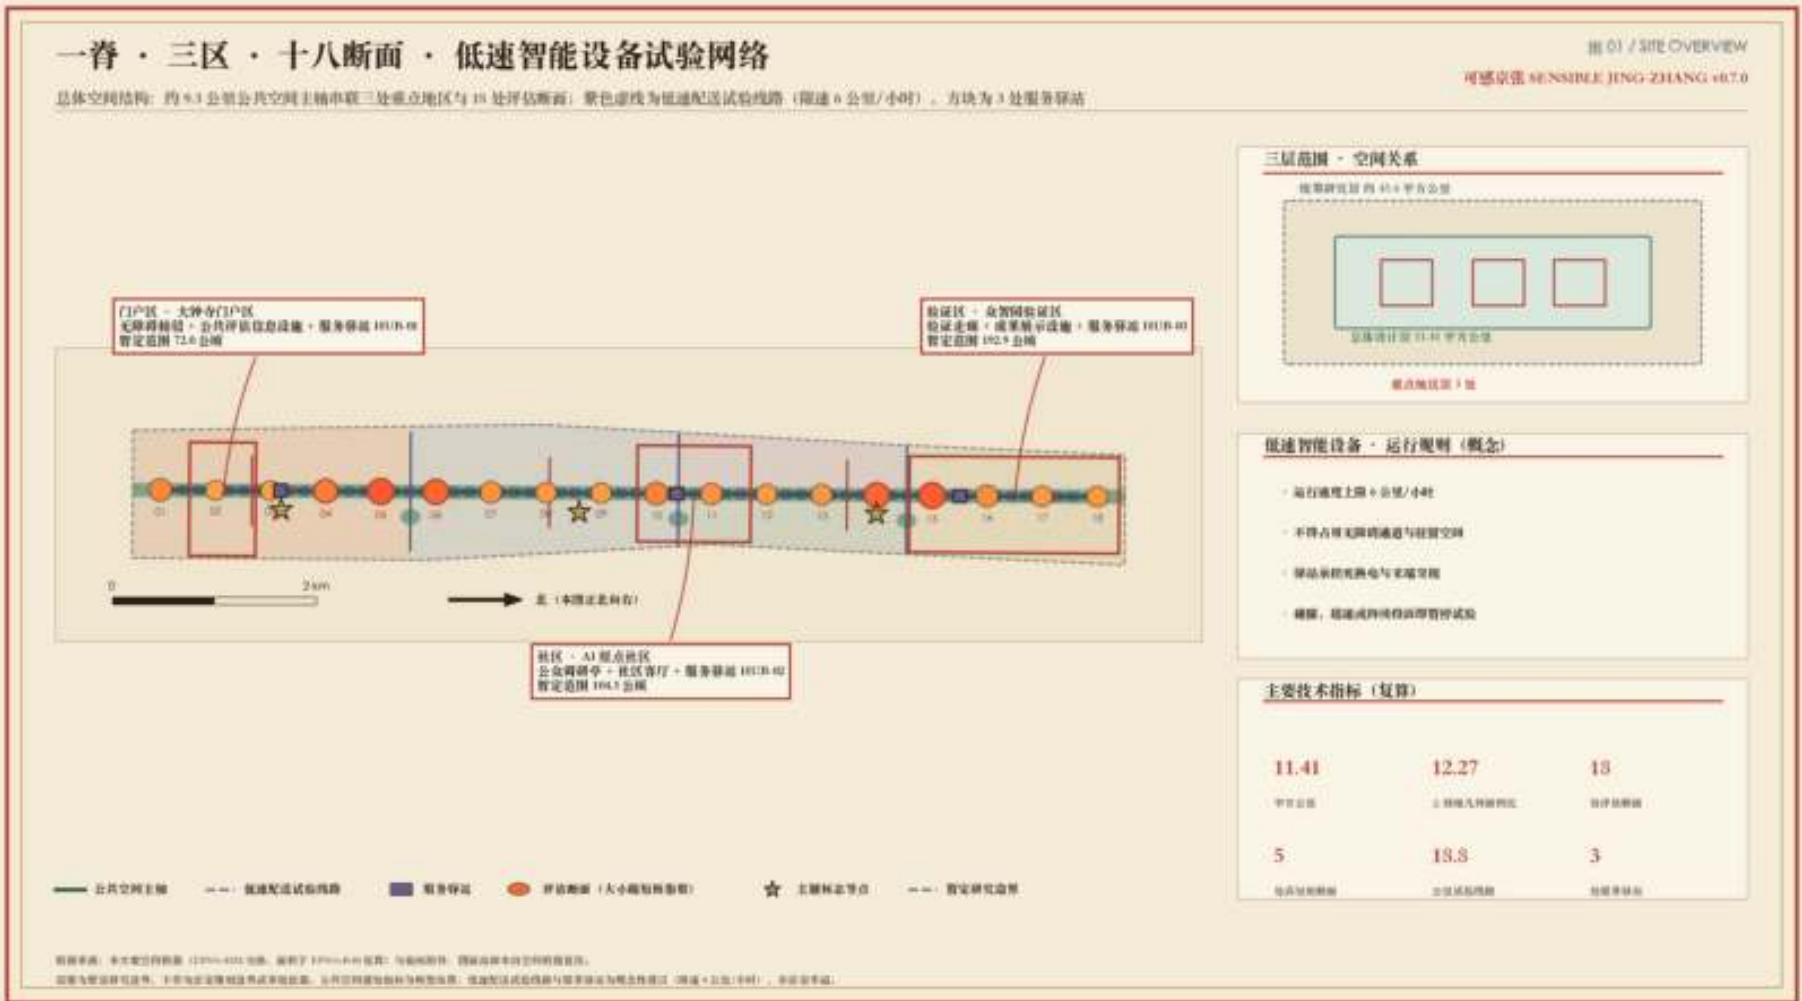

图说：图 04 总体空间结构（总览地图）。先看绿线是否连续，再看橙色圆点大小——越大表示模型估算短板越显著，五个最大的就是一期要动的地方；紫色虚线为低速配送试验线路，平行主轴而不占用主轴。

七月的第一周，工作组把九点三公里走了十八次，每隔约五百米停下来记四件事：头顶有没有树荫、眼前有多少绿、身边能不能坐下、晚上灯亮不亮。第九次停下时是三十六度，一个孩子把脸埋进母亲的裙子里躲太阳，老陈自己先受不了了：“行，这个真得记下来。”

对应正文：第四章（一条脊、三个院、十八次停下）

数据与口径：图面由本方案空间数据直绘，面积与长度在 EPSG:4548 下复算

使用边界：暂定研究边界；感知类指标为模型估算；低速设备线路与驿站为概念性建议，实施前须完成审批。

景 04 短板断面整治前后

第四章 · 概念效果图

- 七月的第一周，工作组把九点三公里走了十八次，每隔约五百米停下来记四件事：头顶有没有树荫、眼前有多少绿、身边能不能坐下、晚上灯亮不亮。
- 第九次停下时是三十六度，一个孩子把脸埋进母亲的裙子里躲太阳，老陈自己先受不了了：“行，这个真得记下来。
- 概念效果图用于说明空间关系与使用方式，不表达建筑形式、层数与高度。



图说：景 04 整治前后。右图新增的停留空间来自边界空间重组，没有压缩人行通道，信息牌置于通行带之外。效果须在建成 90 日后复测确认。

总体结构定为“一脊、三区、十八断面”。评估维度四项合成短板指数，全线模型估算平均 0.416、最高 0.554，不低于 0.45 的 5 处构成一期对象。十八断面按问题归为六族，各配一套标准做法。城市更新以整治提升为主，因为这条线缺的不是新建量，而是连续性。

对应正文：	第四章（一条脊、三个院、十八次停下）
数据与口径：	画面按主轴与重点地区相对位置绘制，不含强度与高度数据
使用边界：	概念效果图非实景，不作为现状或建成状况证明；相关设施须经审批后实施。

第五章 · 规划图

- 图 03 / KEY AREAS
- 可感知强 SENSIBLE JING-ZHANG v07.0
- ## 三处重点地区：门户区 · 社区 · 验证区
- 以模型估算短板断面为一期优先整治对象；公共评估信息设施与快速设备服务节点为智慧服务落点
- 门户区 · 大神寺门户区
- 北园街路口、公共评估信息设施、智慧驿站 H13-01、智慧驿站 H13-02
- The diagram illustrates the Shen Shou Portal Area. It features a horizontal road with various colored circles representing different types of nodes or facilities. A red dashed box highlights a specific section of the road. The background is divided into three color-coded zones: orange, grey, and blue.
- 社区 · AI 原点社区
- 公共图书馆、社区居民厅、智慧驿站 H13-03、智慧驿站 H13-04
- The diagram shows the AI Origin Community. It displays a horizontal road with various colored circles representing different types of nodes or facilities. A red dashed box highlights a specific section of the road. The background is divided into three color-coded zones: orange, grey, and blue.
- 验证区 · 众智园验证区
- 验证走廊、成果展示设施、智慧驿站 H13-05、智慧驿站 H13-06
- The diagram depicts the Zhongzhiyuan Verification Zone. It shows a horizontal road with various colored circles representing different types of nodes or facilities. A red dashed box highlights a specific section of the road. The background is divided into three color-coded zones: orange, grey, and blue.
- 数据来源：本方案空间数据（1:2500~1:500 比例，来源于 1:500~1:1000 地形图）与基础路网、道路等级来自公开的道路资源。
- 如需为特定研究应用，本项目会依据相应需求定制数据。公开资料经加工制作后使用。该图配适成色线路与要素标注为概念性表达（精度±公里/小时），非法定标准。
- 一期优先断面（短板指数 ≥ 0.45）
- | 断面 | 路段 | 短板 | 指标 | 得分 |
|-----------|----------|-------|------|------|
| PS-SEC-05 | ST-JZ-05 | 0.554 | 0.52 | 0.51 |
| PS-SEC-15 | ST-JZ-15 | 0.548 | 0.55 | 0.42 |
| PS-SEC-14 | ST-JZ-14 | 0.518 | 0.51 | 0.33 |
| PS-SEC-06 | ST-JZ-06 | 0.515 | 0.55 | 0.36 |
| PS-SEC-04 | ST-JZ-04 | 0.457 | 0.78 | 0.62 |
- 详细设计深化任务
- 01 大牌号、品牌识别系统建设、公共评估信息设施、H13-01 建设
 - 02 节点改造：公共图书馆、社区居民厅、H13-03 实施
 - 03 无源器：验证走廊、成果展示设施、H13-05 实施
 - 04 智能感知型：道路、建筑、照明与智慧标准建设
 - 05 运行策略：建设、建设与运营条件准入运营模式


书店店主苏禾坐轮椅，那天她卡在坡道上，摆手说不用帮忙，等了一会儿自己找角度上去了。“最难的不是坡，是有些地方只有一个台阶——你们觉得那是三厘米，对我是一堵墙。”同一天下午，一位访客在站口左右各走一趟，问了三个人，用了四分半钟才找到路。

对应正文:	第五章（三处必须成功的地方）
数据与口径:	图面由本方案空间数据直绘，面积与长度在 EPSG:4548 下复算
使用边界:	暂定研究边界；感知类指标为模型估算；低速设备线路与驿站为概念性建议，实施前须完成审批。

景 05 大钟寺门户人视

第五章 · 概念效果图

- 书店店主苏禾坐轮椅，那天她卡在坡道上，摆手说不用帮忙，等了一会儿自己找角度上去了。
- “最难的不是坡，是有些地方只有一个台阶——你们觉得那是三厘米，对我是一堵墙。
- 概念效果图用于说明空间关系与使用方式，不表达建筑形式、层数与高度。

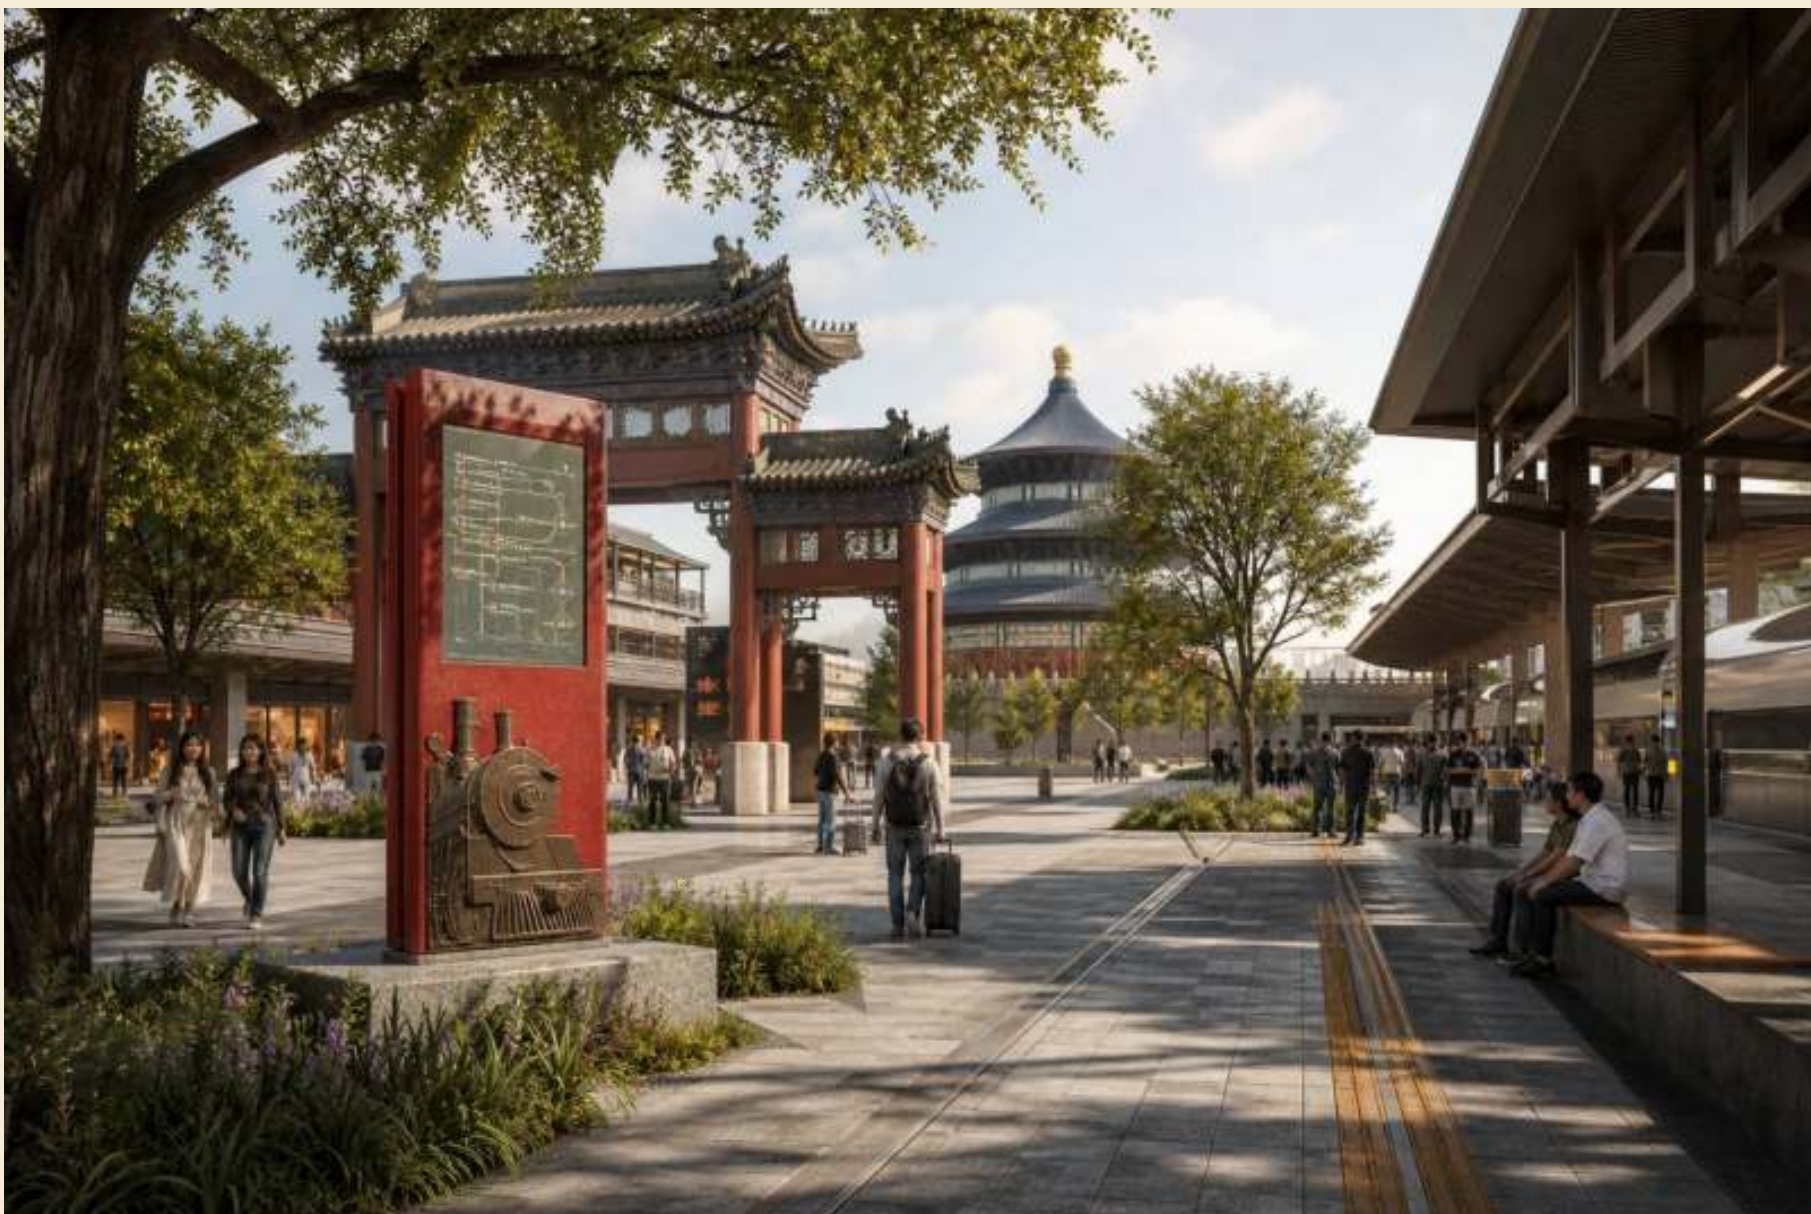

图说：景 05 门户人视。出站抬头能看见方向，走十几步有树荫，再走几步有座位；信息牌不比人高、也不闪烁。门户的成败不在气派，而在陌生人能否顺利进入城市。

门户区（72.0 公顷）做无障碍接驳连续体，出站 150 至 300 米内完成辨向、遮阴、坐憩与信息；AI

原点社区（104.3 公顷）把参与变成日常，调研亭与社区客厅设在居民日常动线上；众智园（192.9 公顷）做

到“可运行也可停止”，设备带、行人带与观看区平面分离。三处统一执行三条底线：驻留带在通行带之外且净宽不小于 1.5 米、不占用无障碍通道、一期完成本地区高短板断面整治。

对应正文：第五章（三处必须成功的地方）

数据与口径：画面按主轴与重点地区相对位置绘制，不含强度与高度数据

使用边界：概念效果图非实景，不作为现状或建成状况证明；相关设施须经审批后实施。

图 06 会思考的城市要先学会等人：AI 场景与创新生态

第六章 · 规划图

- 应用场景 16 项，按服务、测试、文化、运营、产业、治理、青年、健康八类布置，其中受控测试 6 项单独管理。
- 每项场景必须回答落点、责任与停止条件三个问题，答不出第三个就不进入试点。
- 共同停止条件五条：占用通行或无障碍空间、发生碰撞超速或持续投诉、采集越界或缺少知情同意、数据不可复核、文保消防交通前置未满足。



图说：图 06 AI 场景空间落点。每个编号都对应一个具体断面，而不是笼统覆盖全线；图右下的五条停止条件比左边的编号更重要，它们决定这些场景能不能被信任。

八月的第七次路测，设备在行人横穿时稳稳停住，随后比预期早半秒起步。没出事，工程师顾一鸣自己先出了一身汗，当场急停并改了两条规则。他后来在评审会上说：可以运行，也必须可以停止。同一个月，调研亭第一次开门，居民的问题都很具体：座椅能不能挪到有树的一侧、下午三点这段路能不能不走、路口提示音能不能小一点。

对应正文：第六章（会思考的城市要先学会等人）

数据与口径：图面由本方案空间数据直绘，面积与长度在 EPSG:4548 下复算

使用边界：暂定研究边界；感知类指标为模型估算；低速设备线路与驿站为概念性建议，实施前须完成审批。

景 06 公众调研亭

第六章 · 概念效果图

- 八月的第七次路测，设备在行人横穿时稳稳停住，随后比预期早半秒起步。
- 没出事，工程师顾一鸣自己先出了一身汗，当场急停并改了两条规则。
- 概念效果图用于说明空间关系与使用方式，不表达建筑形式、层数与高度。



图说：景 06 公众调研亭。它之所以要小、要普通，是因为必须出现在人们本来就会经过的地方。调研依知情同意协议开展，不采集生物特征。

应用场景 16 项，按服务、测试、文化、运营、产业、治理、青年、健康八类布置，其中受控测试 6 项单独管理。


每项场景必须回答落点、责任与停止条件三个问题，答不出第三个就不进入试点。共同停止条件五条：占用通行或无障碍空间、发生碰撞超速或持续投诉、采集越界或缺少知情同意、数据不可复核、文保消防交通前置未满足。感知设施仅采集环境量，机位随灯杆一体设置。

对应正文：	第六章（会思考的城市要先学会等人）
数据与口径：	画面按主轴与重点地区相对位置绘制，不含强度与高度数据
使用边界：	概念效果图非实景，不作为现状或建成状况证明；相关设施须经审批后实施。

图 07 留下来的墙：用地分区、建筑规模与拆改留

第七章 · 规划图

- 概念用地 9 个单元合计 1141.3 公顷，主轴为公园绿地，两翼依次布置商业服务业、科研、教育、公共管理与公共服务及住宅用地，北端留白。
- 建筑规模只给可复算的部分：概念基底 7.3 公顷。
- 容积率、限高与人口容量标注待明确。

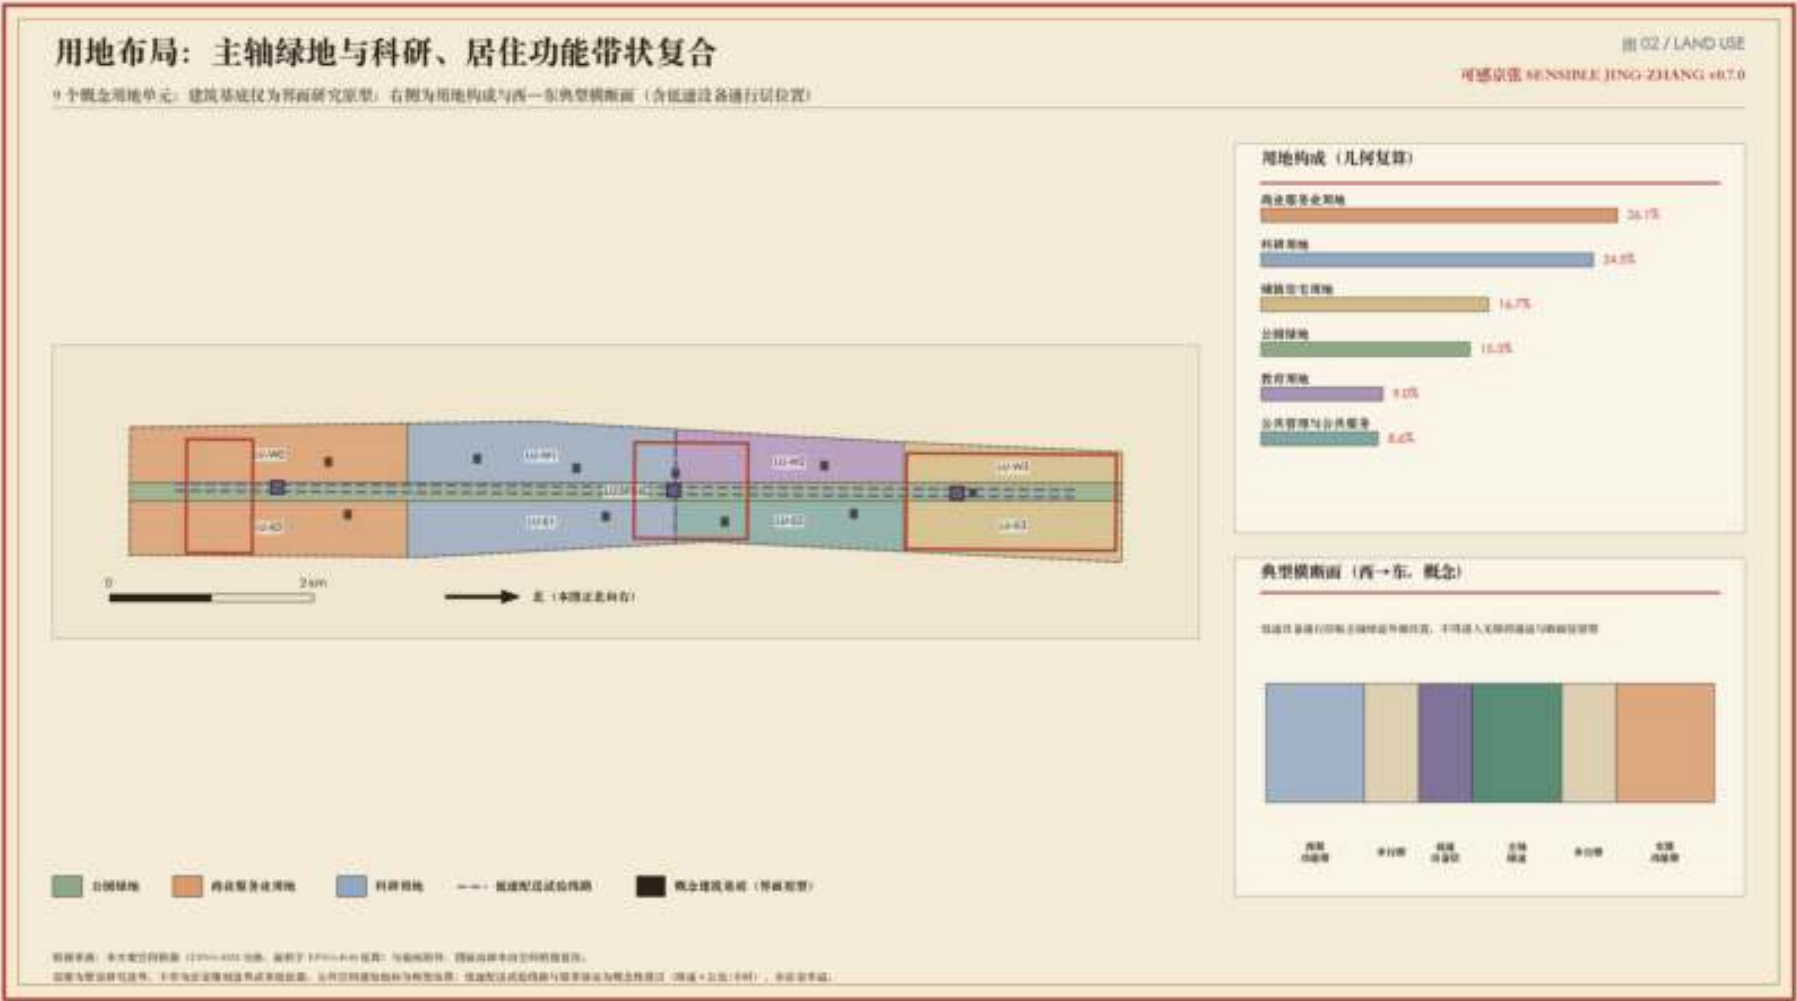

图说：图 07 用地分区与典型横断面。右下断面自西向东为功能带、步行带、低速设备层、主轴绿道、步行带、功能带——低速设备层在绿道外侧，不进入无障碍通道与驻留带，这是全案最不能让步的剖面关系。

九月的那场谈话最难。评价表上写着“建议拆除”，对应一排一九七几年的单层车间。王阿婆在这个院子里住了四十一年，她说：“那排房子的墙，是我小时候上学天天摸着走过去的。你们说它没人用——它当过食堂、托儿所、自行车棚，它一直有人用，只是现在没人管。”三周后，评价结果改为“保留改造”，并公开写明改变理由。

对应正文：	第七章（留下来的墙）
数据与口径：	图面由本方案空间数据直绘，面积与长度在 EPSG:4548 下复算
使用边界：	暂定研究边界；感知类指标为模型估算；低速设备线路与驿站为概念性建议，实施前须完成审批。

景 07 保留车间改造为社区客厅

第七章 · 概念效果图

- 九月的那场谈话最难。
- 评价表上写着“建议拆除”，对应一排一九七几年的单层车间。
- 概念效果图用于说明空间关系与使用方式，不表达建筑形式、层数与高度。



图说：景 07 保留改造。锯齿屋架与砖柱留下，柱间换成大面木框玻璃，檐下加雨棚与坡道，内部为社区客厅与公共卫生间。改造以结构安全评估与产权协商为前置条件。

概念用地 9 个单元合计 1141.3 公顷，主轴为公园绿地，两翼依次布置商业服务业、科研、教育、公共管理与公共服务及住宅用地，北端留白。建筑规模只给可复算的部分：概念基底 7.3 公顷；容积率、限高与人口容量标注待明确。风貌改用可执行的相对要求：临主轴首层通透率不低于 60%、新建体量退让压低、保留建筑材料作为区段基准。拆改留按八项评价打分，以保留修缮与保留改造为主。

对应正文：	第七章（留下来的墙）
数据与口径：	画面按主轴与重点地区相对位置绘制，不含强度与高度数据
使用边界：	概念效果图非实景，不作为现状或建成状况证明；相关设施须经审批后实施。

第八章 · 规划图

- [illegible]

十月的早高峰，一条不到四米宽的界面里有四种速度在插缝：自行车、快步的学生、推保温箱的骑手、拉行李和拄拐的人。

第十七次侧身避让时，骑手小满在她前面刹住了车。“不是我们想抢路，是这段路只有一条路。”老陈补了一句：清扫也得排时间，人多的时候我这车也是障碍。

对应正文:	第八章（先接住人）
数据与口径:	图面由本方案空间数据直绘，面积与长度在 EPSG:4548 下复算
使用边界:	暂定研究边界；感知类指标为模型估算；低速设备线路与驿站为概念性建议，实施前须完成审批。

景 08 共享断面分层

第八章 · 概念效果图

- 十月的早高峰，一条不到四米宽的界面里有四种速度在插缝：自行车、快步的学生、推保温箱的骑手、拉行李和拄拐的人。
- 第十七次侧身避让时，骑手小满在她前面刹住了车。
- 概念效果图用于说明空间关系与使用方式，不表达建筑形式、层数与高度。



图说：景 08 共享断面分层。共享不等于混行：设备带与行人带之间有连续绿化隔离，停留区在通行区之外，装卸有固定位置。


慢行网络四层次：主轴绿道、东西向联系廊与轨道接驳、口袋公园与驻留带、低速设备试验线路（中心线累计约 18.8 公里、限速 6 公里/小时）；概念路网密度 2.93 千米/平方千米。断面分配四条通则：行人优先连续、驻留带在通行带之外、装卸限时限时、设备带贴绿化隔离带外侧并连续分隔。市政与公共服务按专项登记要求，不预设工程规模。

对应正文：	第八章（先接住人）
数据与口径：	画面按主轴与重点地区相对位置绘制，不含强度与高度数据
使用边界：	概念效果图非实景，不作为现状或建成状况证明；相关设施须经审批后实施。

图 09 树荫是最便宜的科技：蓝绿公共空间与城市风貌

第九章 · 规划图

- 蓝绿与公共空间按带级、段级、邻里级三级组织，邻里级标准配置为连续遮阴、成组座椅、饮水点、可渗透铺装与小型雨水花园。
- 指标口径分列：绿地系统几何面积比 12.27%，公共空间节点面积比 1.34%，两者含义不同且都不等同于法定绿地率。
- 风貌以可执行的相对要求表达，铁路遗存保留为铺装线索，不作仿古复建。

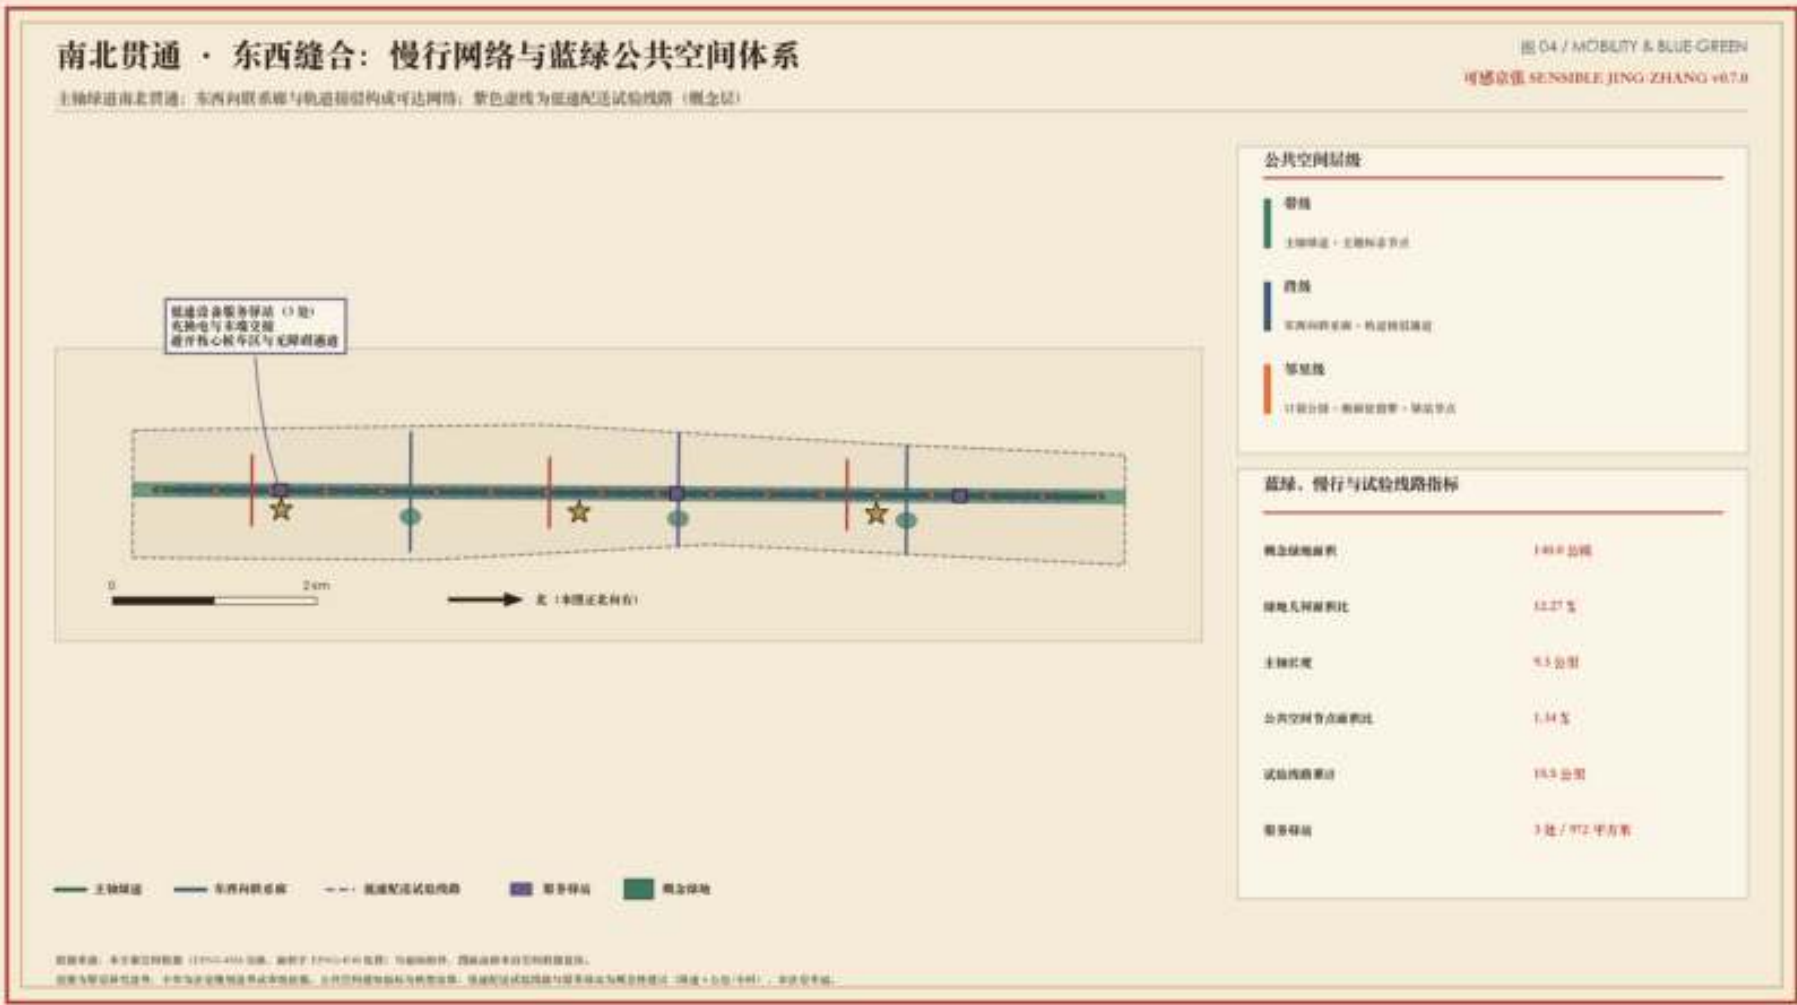

图说：图 09 慢行网络与蓝绿公共空间体系。上一章讲“怎么到”，这一章讲“到了之后是否舒服”；右侧两栏区分三个层级与四项指标口径。

第二年七月，同样的下午两点、同样三十六度，那个等候点已经有了一片树荫。苏禾把轮椅停在阴影边缘说：你们做了很多智慧的东西，但今天我最感谢这几棵树。那天工作组带了温度计，阴影里低了四度多。四度决定一个人愿不愿意在这里等十分钟。

对应正文：第九章（树荫是最便宜的科技）

数据与口径：图面由本方案空间数据直绘，面积与长度在 EPSG:4548 下复算

使用边界：暂定研究边界；感知类指标为模型估算；低速设备线路与驿站为概念性建议，实施前须完成审批。

景 09 夏日口袋公园

第九章 · 概念效果图

- 第二年七月，同样的下午两点、同样三十六度，那个等候点已经有了一片树荫。
- 苏禾把轮椅停在阴影边缘说：你们做了很多智慧的东西，但今天我最感谢这几棵树。
- 概念效果图用于说明空间关系与使用方式，不表达建筑形式、层数与高度。



图说：景 09 夏日口袋公园。台阶是座位，藤架补上乔木还不够高的那几年，饮水与雾化解决最热的两小时，边上的浅草沟是雨水花园。乔木成荫需要时间，一期先补植并以轻型构架过渡。


蓝绿与公共空间按带级、段级、邻里级三级组织，邻里级标准配置为连续遮阴、成组座椅、饮水点、可渗透铺装与小型雨水花园。指标口径分列：绿地系统几何面积比 12.27%，公共空间节点面积比 1.34%，两者含义不同且都不等同于法定绿地率。风貌以可执行的相对要求表达，铁路遗存保留为铺装线索，不作仿古复建。

对应正文：	第九章（树荫是最便宜的科技）
数据与口径：	画面按主轴与重点地区相对位置绘制，不含强度与高度数据
使用边界：	概念效果图非实景，不作为现状或建成状况证明；相关设施须经审批后实施。

图 10 把愿望排队：更新项目清单、实施政策与分期计划

第十章 · 规划图

- 更新项目 12 项、分三期。
- 分期判据：一期为短板指数不低于 0.45 且不依赖法定资料即可实施。
- 二期需产权协商或新建设施。

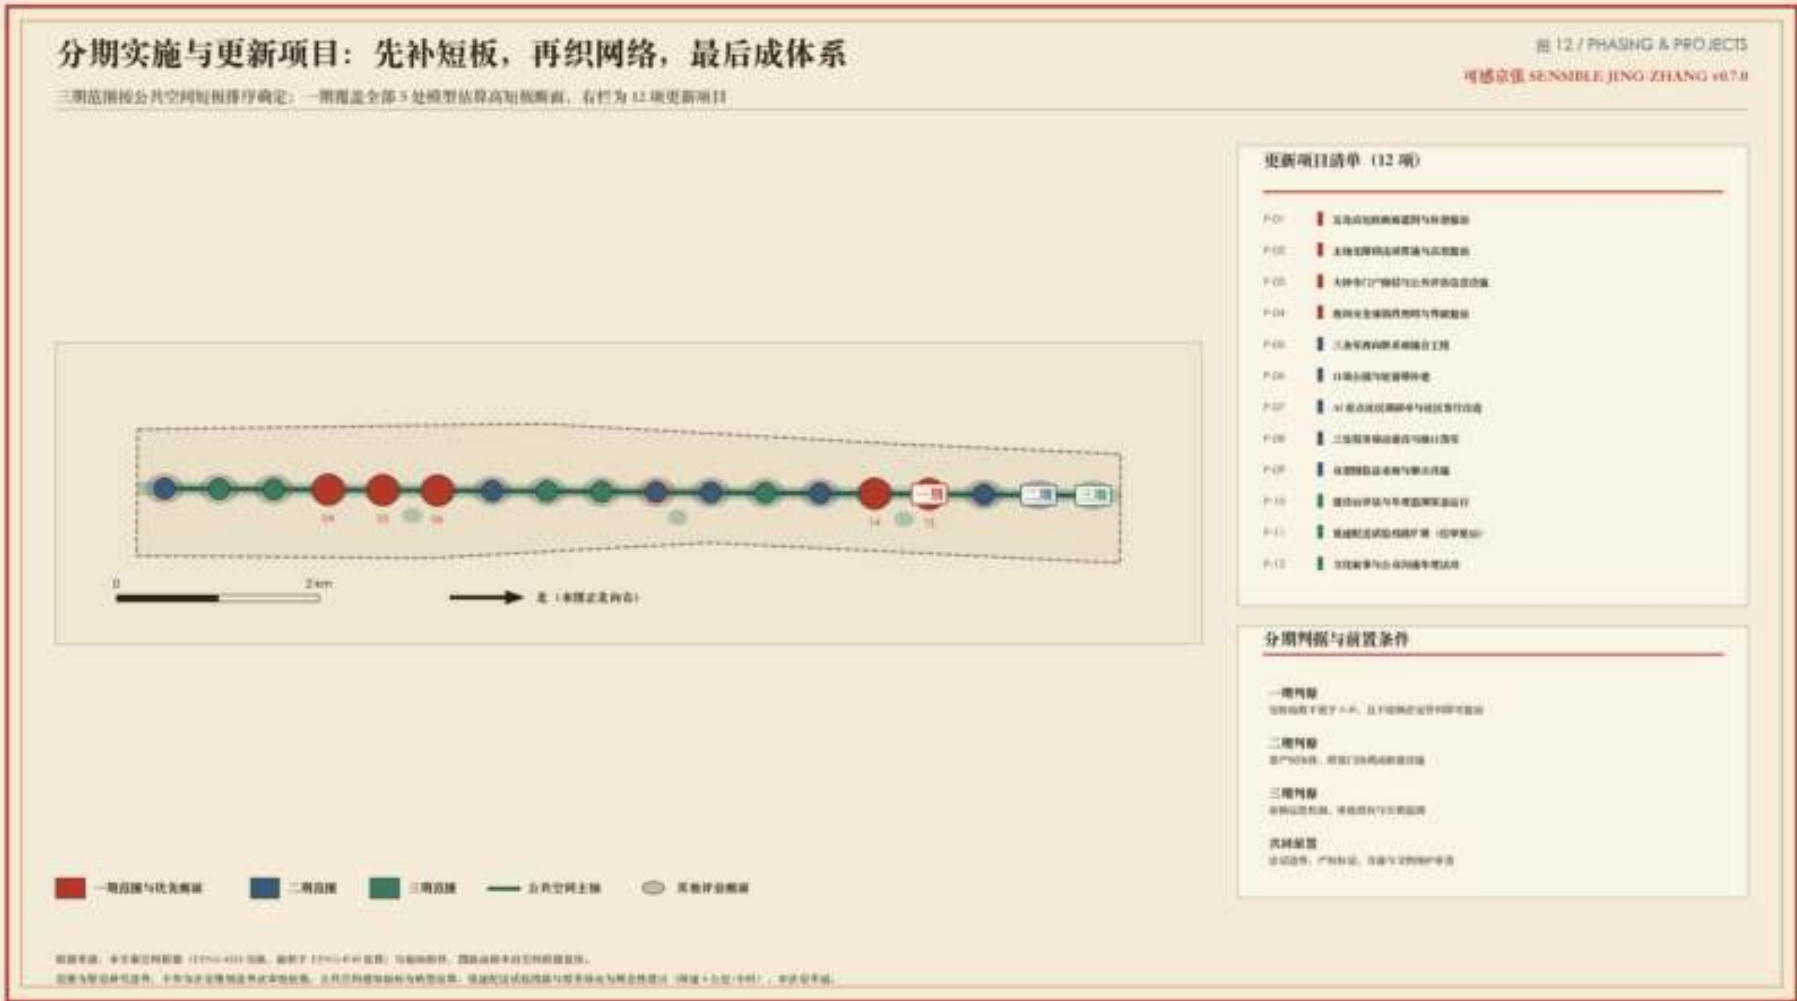

图说：图 10 分期实施与更新项目。红蓝青三块范围即三期，主轴上红点为一期优先断面，可直接检查一期是否覆盖全部五处高短板断面。

十二月的会议上，桌上摆着二十七条建议，钱只够做四五件事。有人提议按“见效快、拍照好看”排序。林深把十八张断面记录纸重新摊开：如果按好看排序，第一期会去修已经最好的那几段，可最差的五段明年夏天还是一样晒。

对应正文：第十章（把愿望排队）

数据与口径：图面由本方案空间数据直绘，面积与长度在 EPSG:4548 下复算

使用边界：暂定研究边界；感知类指标为模型估算；低速设备线路与驿站为概念性建议，实施前须完成审批。

景 10 众智园验证走廊

第十章 · 概念效果图

- 十二月的会议上，桌上摆着二十七条建议，钱只够做四五件事。
- 有人提议按“见效快、拍照好看”排序。
- 概念效果图用于说明空间关系与使用方式，不表达建筑形式、层数与高度。



图说：景 10 验证走廊。它的价值不在于设备能跑多快，而在于证明一套规则可以让设备在人多的地方安全地慢下来、停下来、把决定交回给人。

更新项目 12 项、分三期。分期判据：一期为短板指数不低于 0.45 且不依赖法定资料即可实施；二期需产权协商或新建设施；三期依赖运营机制与审批授权。实施政策四项：产权协商前置、共建共管、运营协议管住技术、公众复核决定下一轮。每个项目立项即登记基线、目标值、复测时间与责任主体，建成 90 日复测，达标结项、未达标整改。

对应正文：	第十章（把愿望排队）
数据与口径：	画面按主轴与重点地区相对位置绘制，不含强度与高度数据
使用边界：	概念效果图非实景，不作为现状或建成状况证明；相关设施须经审批后实施。

第十一章 · 规划图

- [illegible]

第二年一月自查时发现一个错误：两处都写“绿地比例”，数字却不一样——一处是绿地系统几何面积比，一处混入了公共空间节点。差别不大，性质很坏。处理方式并不浪漫：分开命名、写清计算范围、统一全部表述、在变更记录里写明改过这件事。

对应正文:	第十一章（一把可以被验算的尺子）
数据与口径:	图面由本方案空间数据直绘，面积与长度在 EPSG:4548 下复算
使用边界:	暂定研究边界；感知类指标为模型估算；低速设备线路与驿站为概念性建议，实施前须完成审批。

景 11 年度复测日

第十一章 · 概念效果图

- 第二年一月自查时发现一个错误：两处都写“绿地比例”，数字却不一样——一处是绿地系统几何面积比，一处混入了公共空间节点。
- 差别不大，性质很坏。
- 概念效果图用于说明空间关系与使用方式，不表达建筑形式、层数与高度。



图说：景 11 年度复测日。整治前基线、目标值与复测结果并排公布，未达标当场登记整改；下一期先修哪里，由公开结果与公众意见共同决定。

指标分三类：可由几何直接复算的空间指标 21 项，全部在 EPSG:4548 下复算；需法定资料支撑的管控指标（容积率、限高、人口容量）标注待明确；需运营与调研校准的绩效指标标注模型估算或待实测。合规矩阵按标准、成果深度与任务覆盖三类相互校核，共 6 项标准、15 项深度条目，正文每处结论都能追到一项矩阵条目。

对应正文：	第十一章（一把可以被验算的尺子）
数据与口径：	画面按主轴与重点地区相对位置绘制，不含强度与高度数据
使用边界：	概念效果图非实景，不作为现状或建成状况证明；相关设施须经审批后实施。

第十二章 · 规划图

- # 夜间安全与照明整治：让安全感看得见、复测得出来

图 13 / NIGHT SAFETY

按照模型估算夜间安全分项排序识别薄弱断面：整治以连续照明、活跃节点、可呼叫停靠点与日常维护为主，不以监控密度替代环境改善

可感知强度 SENSIBLE JING-ZHANG v07.0

夜间安全薄弱断面（模型估算）

断面	指标	夜间安全
P5-SEC-14	0.0-14	0.308
P5-SEC-04	0.0-04	0.304
P5-SEC-07	0.0-07	0.400
P5-SEC-18	0.0-18	0.426

整治措施与运行规则

- 连续照明**
通过照明设施、杆件的物理存在，避免物理断点
 - 活跃节点**
通过节点与照明设施的设置改善
 - 可呼叫停靠点**
通过设置物理呼叫点与物理设施与物理设施
 - 日常维护**
灯杆、设施与照明设施的日常维护
 - 夜间运行规则**
通过设置物理呼叫点与物理设施与物理设施
 - 物理设施**
通过设置物理呼叫点与物理设施与物理设施

数据来源：本方案数据来源于 2019-2021 年，来源于 1:50000 比例尺地形图、卫星影像图、道路设计图等公开数据；
数据为整理与计算，不作为法律依据或责任依据，仅供参考与决策支持，不作为法律依据或责任依据（误差 ± 0.5m），不作为法律依据。

三月的夜里十点半，程宁走到主轴南段，前面两百米灯是好的，再往前路灯间距忽然变大，留下一段黑。她算了一下绕路要多走七分钟，最后打开手机电筒快步走了过去。第二天她在调研亭留下一条意见：不要摄像头，要灯。

对应正文:	第十二章（夜里那一段路）
数据与口径:	图面由本方案空间数据直绘，面积与长度在 EPSG:4548 下复算
使用边界:	暂定研究边界；感知类指标为模型估算；低速设备线路与驿站为概念性建议，实施前须完成审批。

景 12 夜间安全整治

第十二章 · 概念效果图

- 三月的夜里十点半，程宁走到主轴南段，前面两百米灯是好的，再往前路灯间距忽然变大，留下一段黑。
- 她算了一下绕路要多走七分钟，最后打开手机手电筒快步走了过去。
- 概念效果图用于说明空间关系与使用方式，不表达建筑形式、层数与高度。



图说：景 12 夜间整治。亮度层级为路径最亮、界面其次、信息设施最暗。技术退到后面：它负责让人知道自己在哪里、可以向谁求助。

风险按资料、技术、数据隐私与越权四类登记。夜间安全采用连续照明、活跃首层界面、可呼叫停靠点与日常维护四件事，并明确巡检记录只用于判断设施状态、不用于识别个人。版权方面，正文、规划图、主视觉、效果图与图册均为本次提交原创生成，不引用未清权影像。合规底线：不声称获得官方批准、不构成法定规划、不代表资金或实施授权。

- | | |
|--------|------------------------------------|
| 对应正文： | 第十二章（夜里那一段路） |
| 数据与口径： | 画面按主轴与重点地区相对位置绘制，不含强度与高度数据 |
| 使用边界： | 概念效果图非实景，不作为现状或建成状况证明；相关设施须经审批后实施。 |

图 13 第二次测量之后：成果构成与公众沟通

第十三章 · 规划图

- 成果构成：十三章规划说明书、13 张规划图、13 张概念效果图、1 张文化主视觉、9 个空间图层、21 项可复算指标，以及 A0 图版与 A3 图册。
- 公众沟通以十三处叙事站点对应十三章内容，用于导览与年度复测活动。
- 文化叙事仅用于沟通，不作为现状事实、技术指标或规划依据。



图说：图 13 规划导图。八步闭环从核定资料开始、到建设后评估结束，而第八步的箭头回到第二步——这条回头的箭头是全篇的方法核心。导图为方法示意，不含空间比例关系。

第二年五月的复测日，老陈提前退休了三个月还是来了。信息牌上并排放着五处断面的基线、目标与复测结果：两处达标、两处接近、一处没达到，没达到的当场登记整改。轮到他说话时，他只说了一句：我扫了十九年，第一回有人把我说的话写在牌子上。苏禾那天第一次把这条路走完，用了两小时零六分。

对应正文：	第十三章（第二次测量之后）
数据与口径：	图面由本方案空间数据直绘，面积与长度在 EPSG:4548 下复算
使用边界：	暂定研究边界；感知类指标为模型估算；低速设备线路与驿站为概念性建议，实施前须完成审批。

景 13 十三章叙事分镜长卷

第十三章 · 概念效果图

- 第二年五月的复测日，老陈提前退休了三个月还是来了。
- 信息牌上并排放着五处断面的基线、目标与复测结果：两处达标、两处接近、一处没达到，没达到的当场登记整改。
- 概念效果图用于说明空间关系与使用方式，不表达建筑形式、层数与高度。



图说：景 13 叙事分镜长卷。十二格对应本篇故事在空间上的落点，也是公众沟通的站点：从清晨的通勤者，到坡道上的三类使用者，到暗段里的照度记录，到复测日的公众确认。

成果构成：十三章规划说明书、13 张规划图、13 张概念效果图、1 张文化主视觉、9 个空间图层、21 项可复算指标，以及 A0 图版与 A3 图册。公众沟通以十三处叙事站点对应十三章内容，用于导览与年度复测活动；文化叙事仅用于沟通，不作为现状事实、技术指标或规划依据。规划留下的不是结论，而是一把尺子和一套规矩：谁都可以重量一遍，量出不同结果就按规矩改。

对应正文：	第十三章（第二次测量之后）
数据与口径：	画面按主轴与重点地区相对位置绘制，不含强度与高度数据
使用边界：	概念效果图非实景，不作为现状或建成状况证明；相关设施须经审批后实施。