

# 京张·新轨 JingZhang NewTrack —— 百年京张AI创新带概念城市设计


百年京张AI创新带概念城市设计 · Concept Urban Design, Centennial Jing-Zhang AI Innovation Belt 「三轨同脉」Three Tracks, One Pulse · 一带三核 / 双翼七轴 · 人字回退 Switchback Fallback (JZ-SWITCHBACK-001) NT-6 服务契约 · 四态回退 normal/degraded/paused/retired · 折返试验段 SW-001/002/003 (v0.6) 概念建议(非审定结论) · 边界为临时粗略范围 (provisional\_constraint) · 面积由 geometry 按 EPSG:4548 复算

【临时边界与非官方红线警示 / provisional\_constraint · official\_boundary=false】本方案所有范围均为临时工作假定，不作为法定规划红线或政府审批依据；指标均基于临时几何复算，待官方正式边界及审定控规发布后整体重算。

| 总体设计范围    | 科研用地             | 绿地率              | 公共空间占比          | 道路总长                | AI场景卡      | 桌面演练           |
|-----------|------------------|------------------|-----------------|---------------------|------------|----------------|
| 11.41 km² | 4.82 km² (42.2%) | 21.7% (约2.48km²) | 1.2% (约13.7万m²) | 40.7 km (EPSG:4548) | 12张 (3类测试) | 24组 (8接受/16拒绝) |

## 01 总体概念与空间结构总览 / Master Concept & Spatial Structure

### 京张·新轨 JingZhang NewTrack —— 总体概念与空间结构总览 Three Tracks, One Pulse · 一带三核 / 双翼七轴

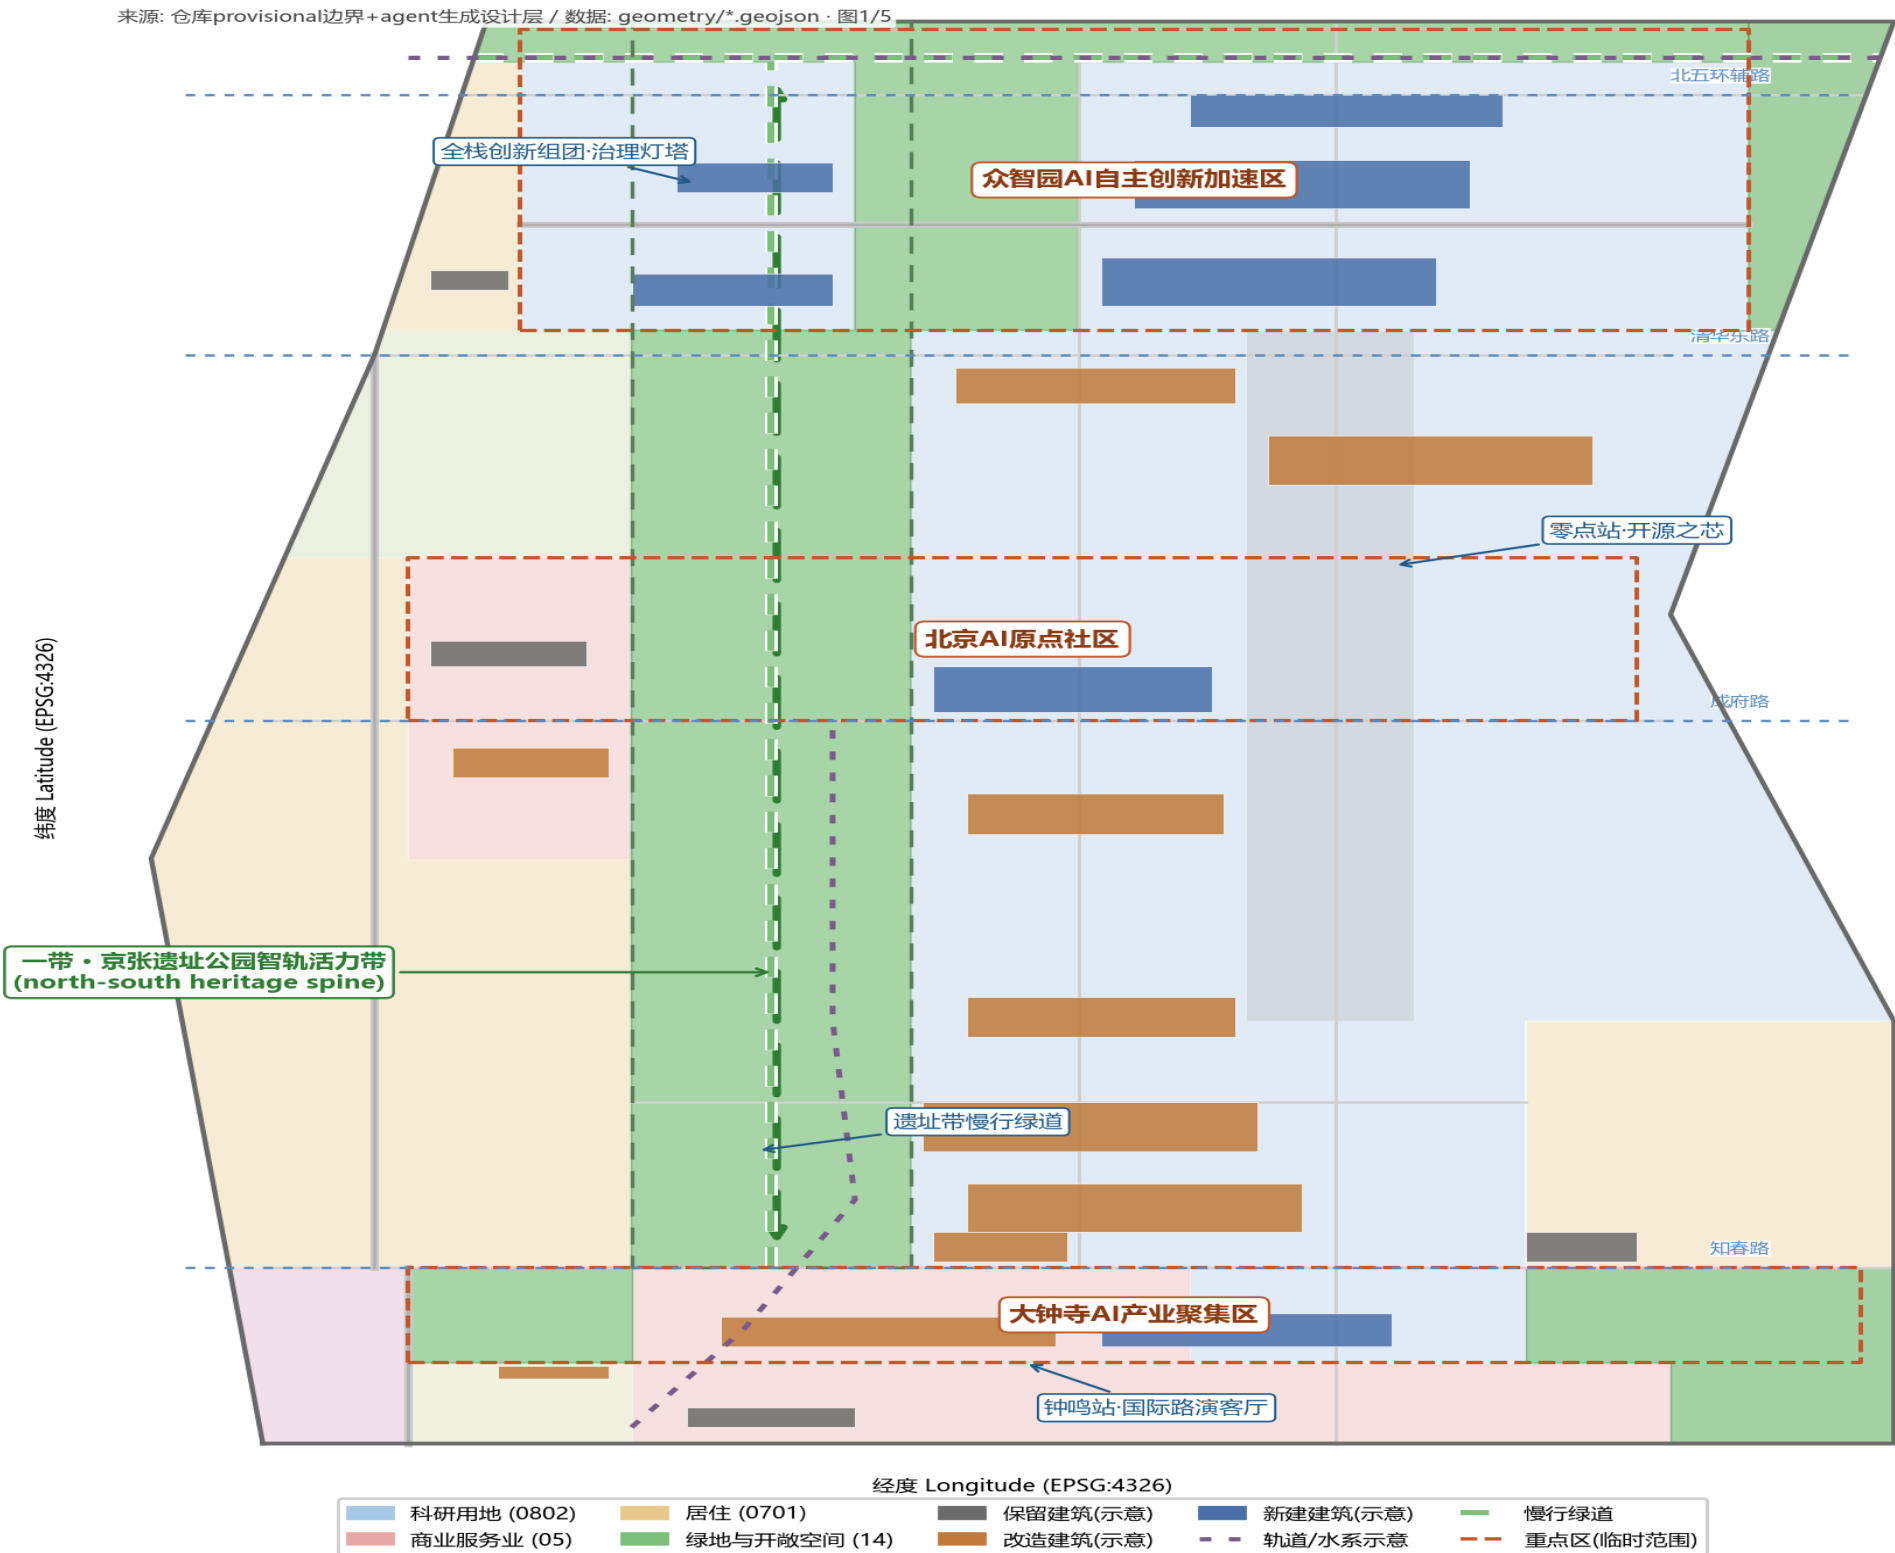

【临时边界与非官方红线警示 / provisional\_constraint · official\_boundary=false】  
本方案范围为临时工作假定，不作为法定红线或审批依据；指标均基于临时几何复算，待官方正式边界发布后整体重算。

图1：一带三核、双翼七轴；绿色主轴为京张遗址公园智轨活力带，三处重点区沿带分布，七条功能轴组织东西缝合与南北贯通。边界为临时粗略范围 (provisional\_constraint)。

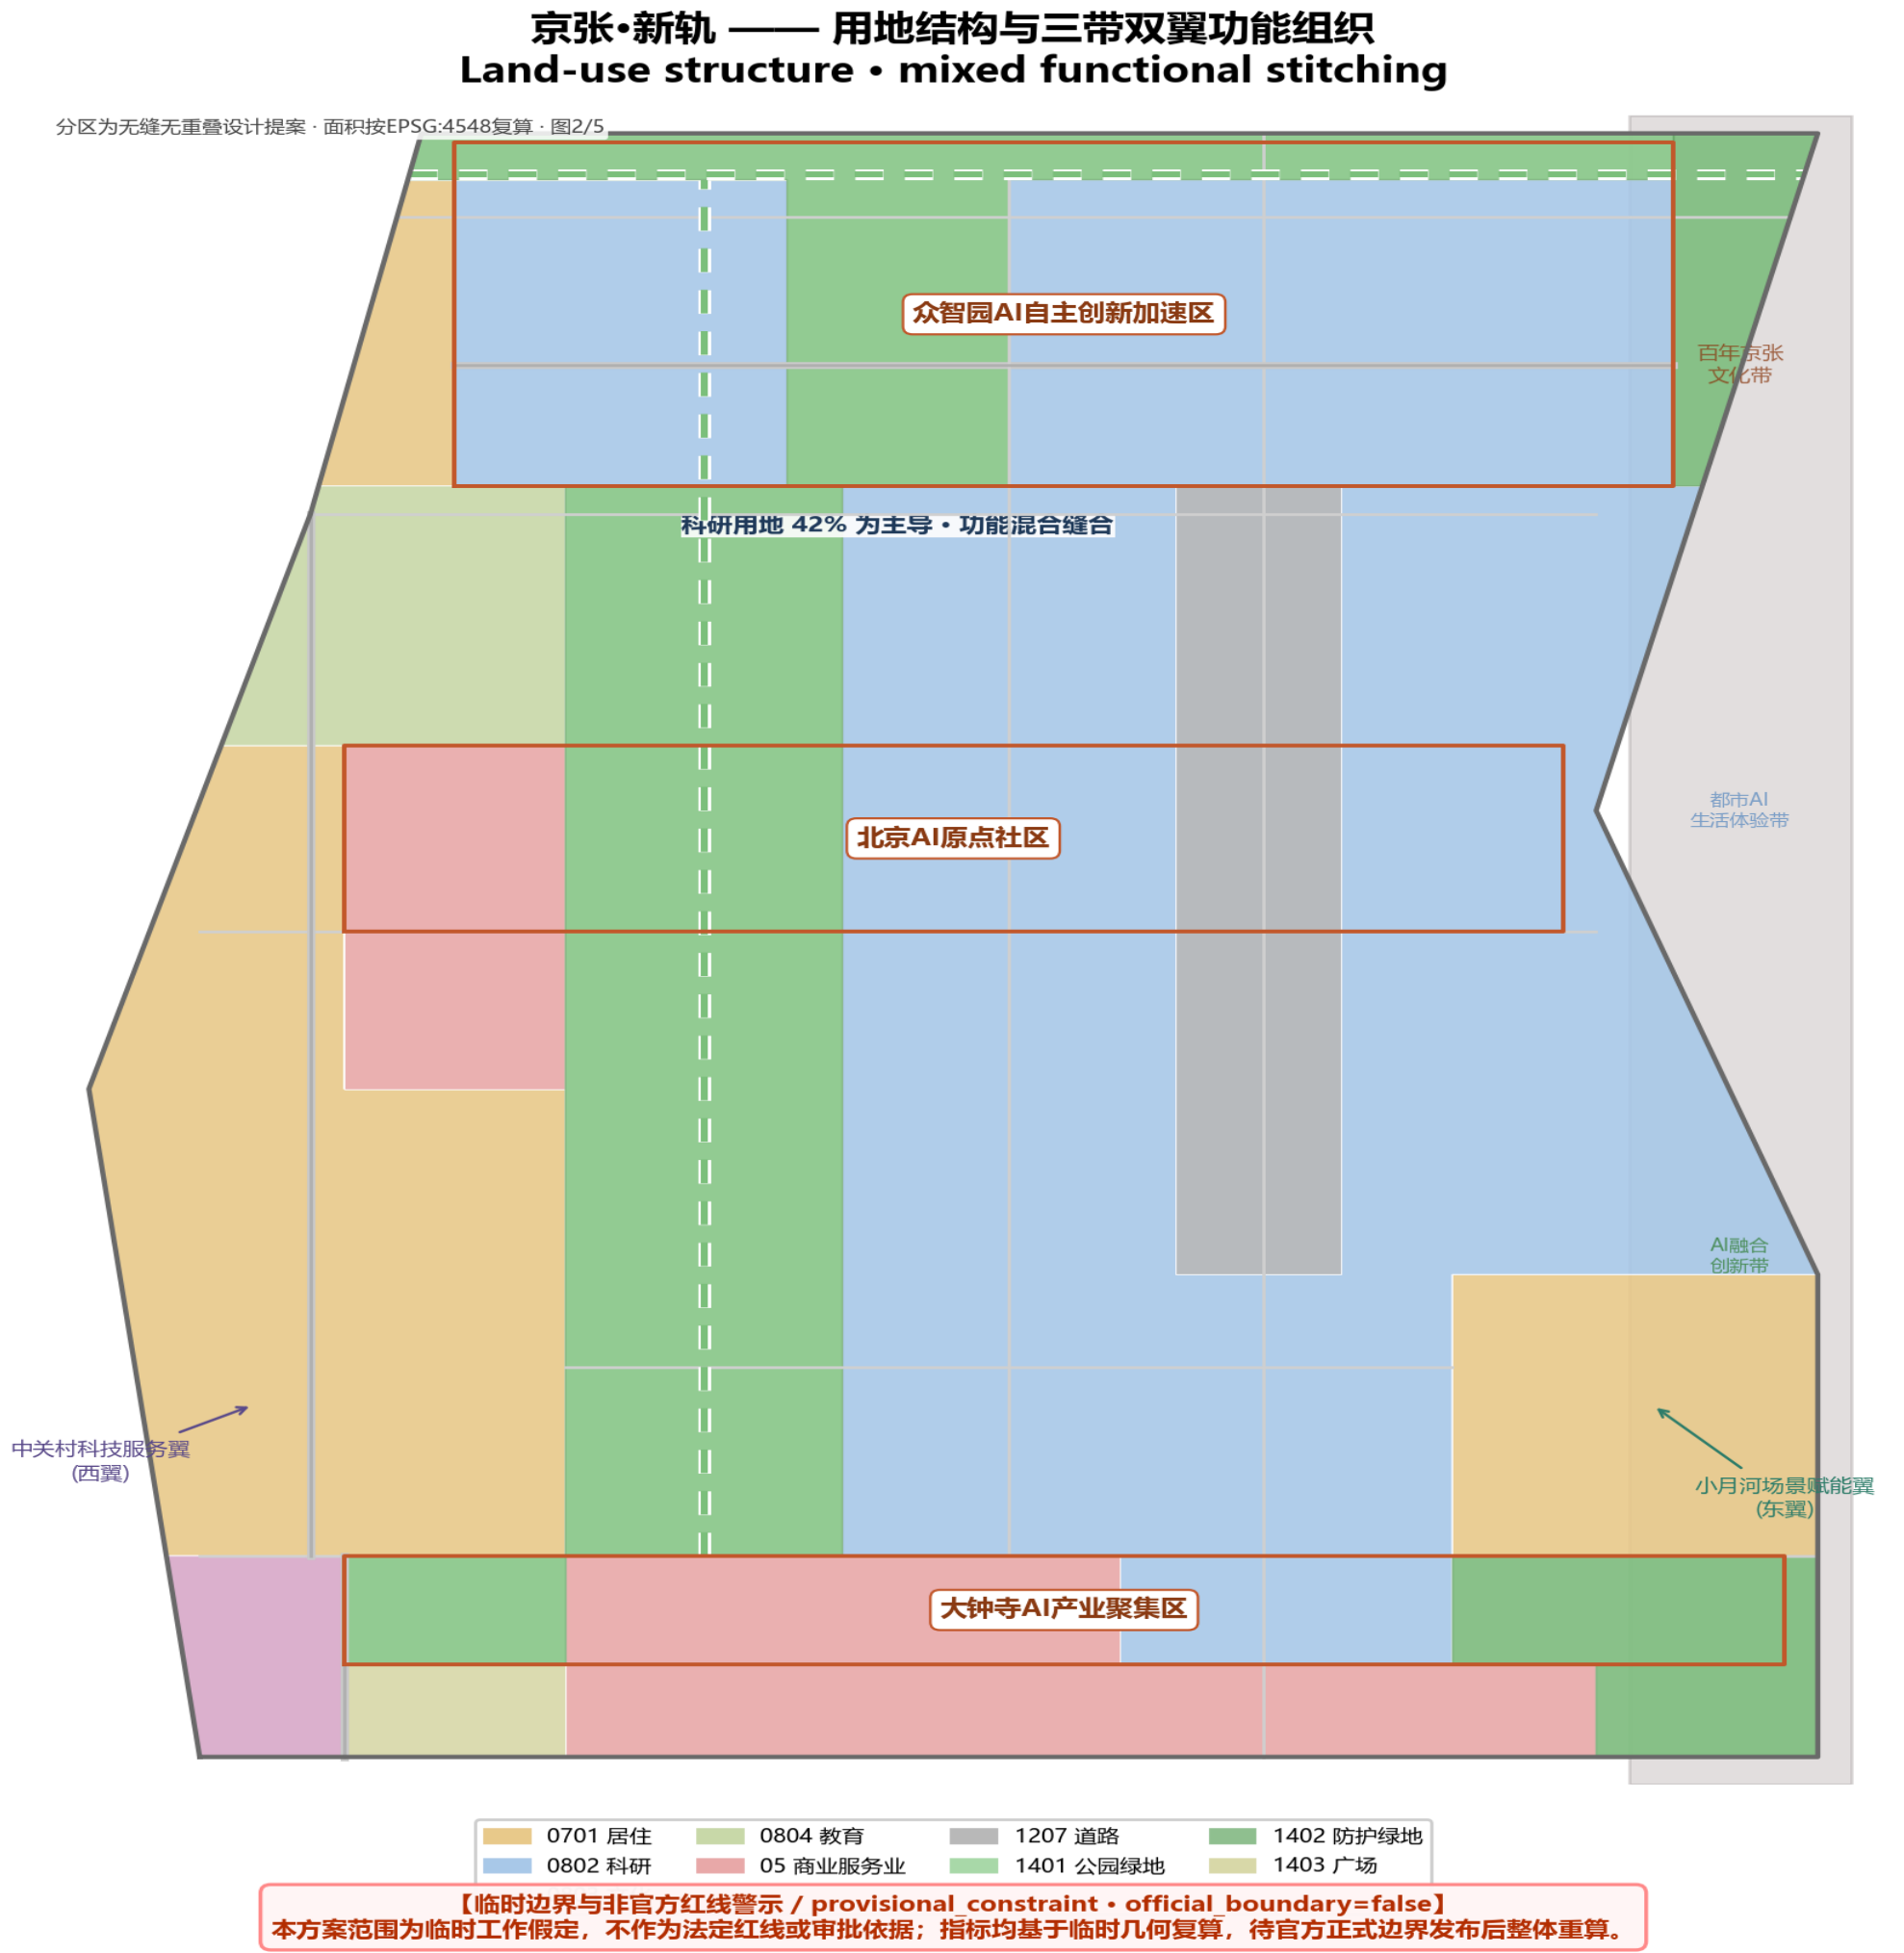


图2：无缝无重叠用地分区，科研用地 (0802) 占 42.2% 为主导；右侧三带身份覆盖示意，双翼机制支撑三核。全部面积由 geometry/land\_use.geojson 按 EPSG:4548 复算闭合。

京张·新轨 —— 三处重点区域详细设计任务索引  
Three key areas • position + space + AI scenarios + risks

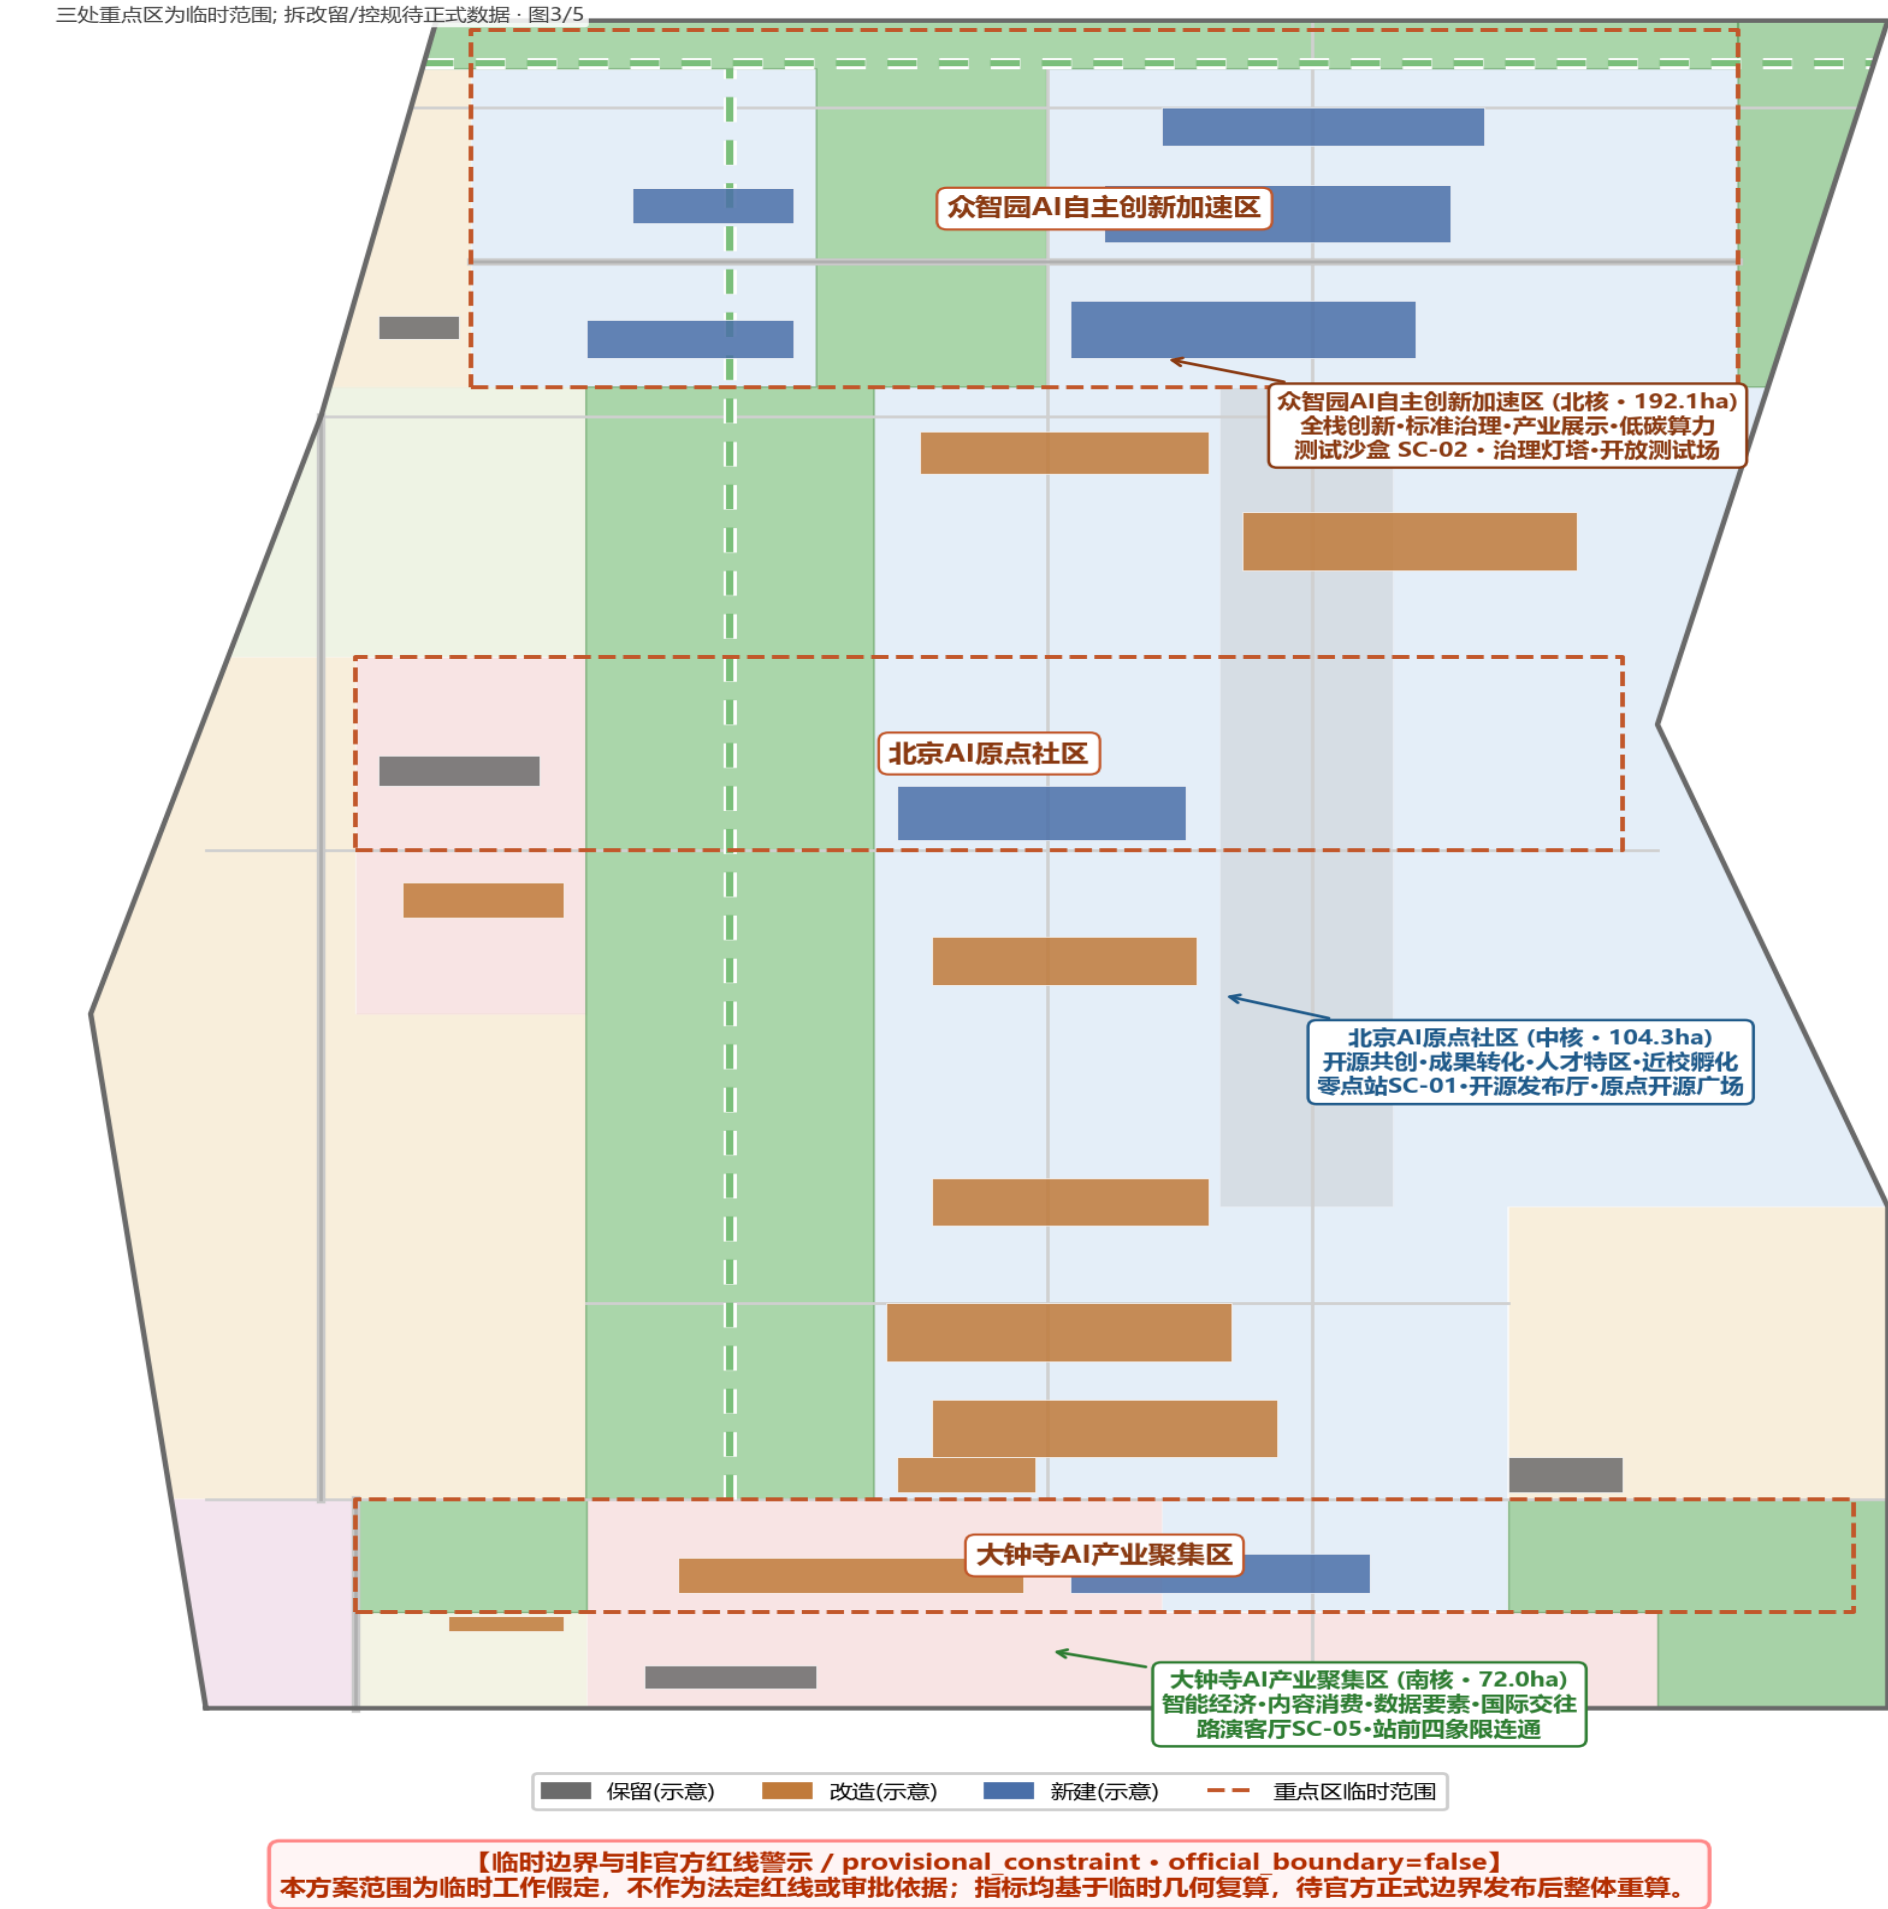


图3：众智园（北核:192.1ha）、原点社区（中核:104.3ha）、大钟寺（南核:72.0ha）的定位、空间动作、AI场景、折返试验段 (JZ-SW1/2/3) 与实施风险。

京张·新轨 —— 交通慢行与蓝绿公共空间复合系统  
Mobility • slow-mobility stitching • blue-green network

道路/轨道线位均为 provisional\_alignment 示意, 红线与工程以官方为准 · 图4/5

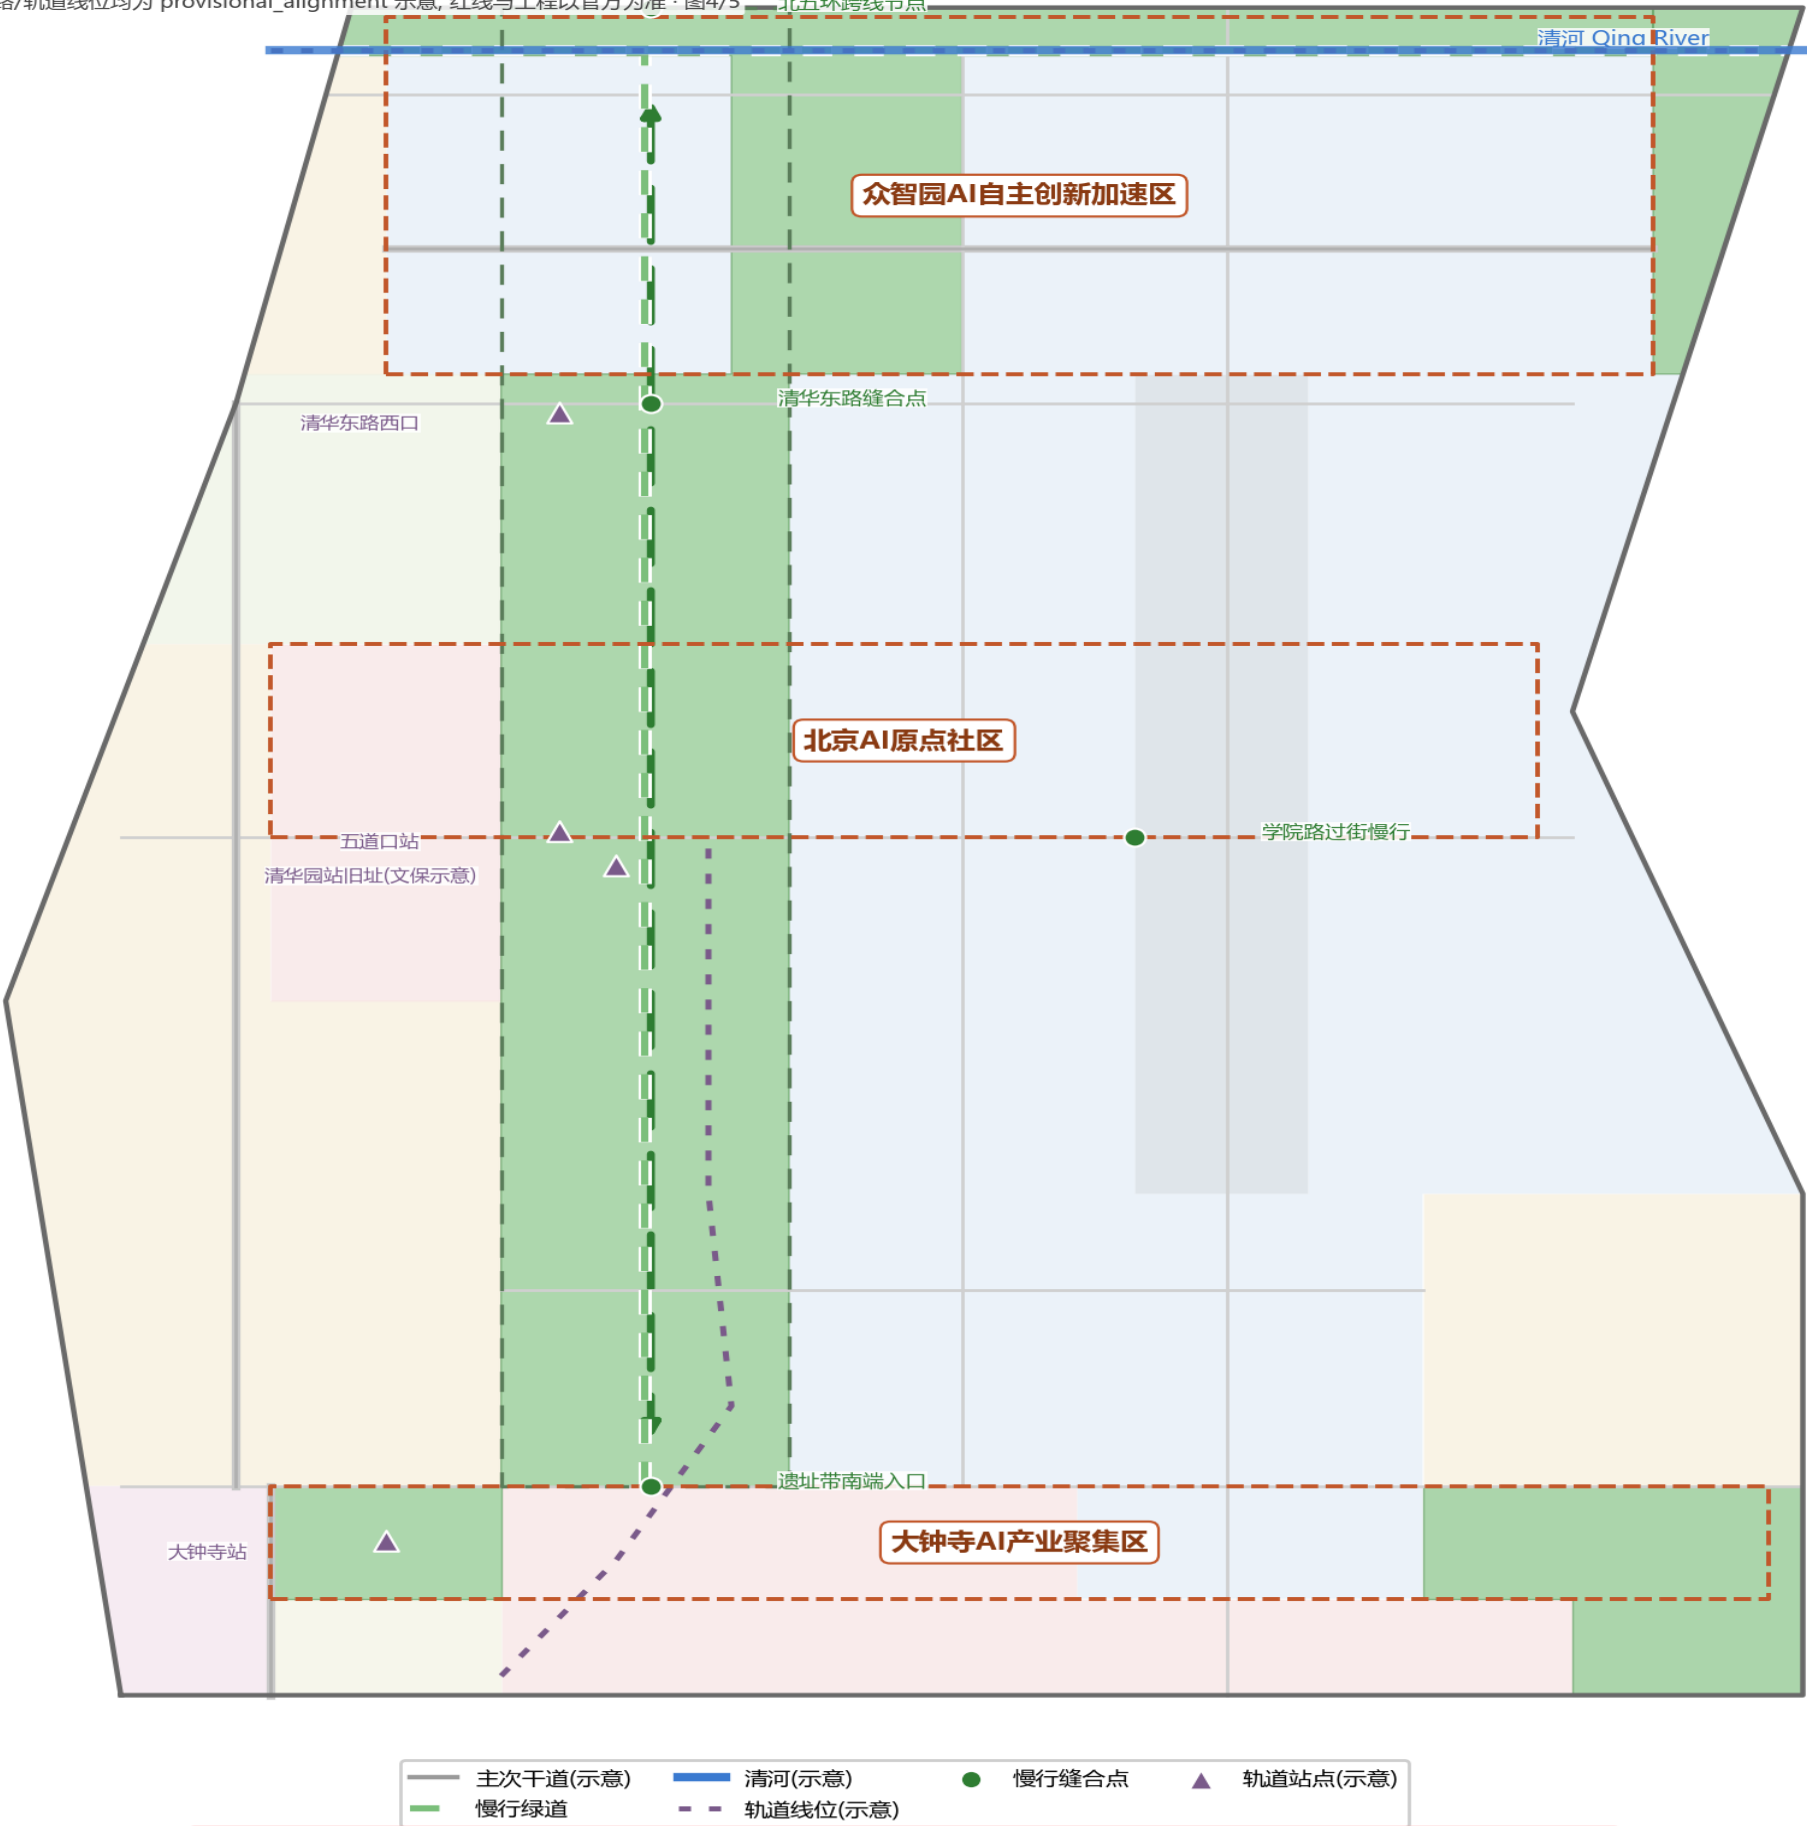



图4：慢行绿道、清河界面、慢行缝合点与轨道站点一体化示意；道路示意总长 40.7 km (EPSG:4548 复算)；线位均为 provisional\_alignment 概念示意。

京张·新轨 —— 核心指标复算与证据链 Core metrics & evidence chain  
(全部数值与 geometry/metrics.json 一致)


核心指标 Core Metrics  
(由 geometry/\*.geojson 按 EPSG:4548 复算)

|                                                |              |
|------------------------------------------------|--------------|
| 场地面积 site_area<br>provisional · EPSG:4548      | 11.41 km²    |
| 绿地率 green_ratio<br>支撑人才生活与创新交往                 | 21.7%        |
| 公共空间比 pub_ratio<br>广场+庭院 · 支撑日常停留              | 1.2%         |
| 建筑基底 bld_footprint<br>21处代表性图斑(非审定)            | 0.98 km²     |
| 道路示意长度 road_len<br>12条 · provisional_alignment | 40.7 km      |
| 科研用地 research<br>占场地主导功能                       | 4.82 km²     |
| 三期分期 sum<br>无缝闭合                               | 11.41 km²    |
| 待官方控规<br>unknown · 待正式条件                       | FAR/高度/密度/退线 |

用地构成 (km², 临时边界内复算)

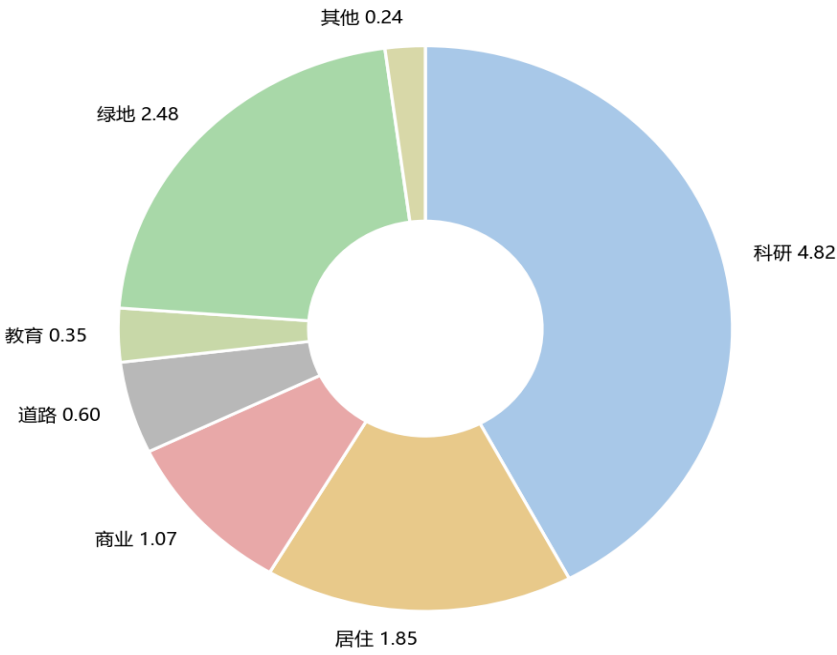

分期推进 Phasing (无缝分区与时序)

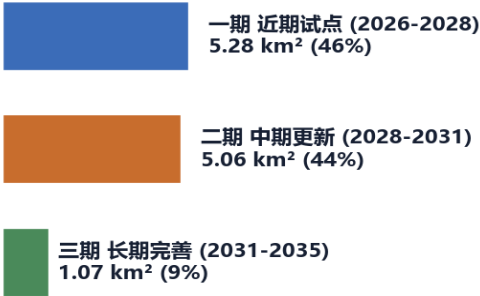

概念分期, 非实施承诺 · 支撑三阶段渐进更新

证据链 Evidence Chain (可复算/待控规/运营校准)



机制证据: NT-6 六步服务契约 · 四态 normal/degraded/paused/retired · 折返试验段 SW-001/002/003

最小试点 SC-04: G0=not\_run · G1=pending\_authorization · G2=sandbox\_only

待正式数据: 官方红线 · 控规(FAR/高度/密度/退线) · 现状建筑/权属 · 市政工程

→ 官方 polygon 发布后整体重算全部图层/指标/图件 (见 assumptions.json A-RECALC-001)

边界为临时粗略范围 (provisional\_constraint) · 不可作官方红线/精确面积依据 · 图5/5

图5：指标由 geometry/\*.geojson 按 EPSG:4548 复算；FAR/高度/密度/退线等法定控制指标保持 unknown，待正式控规条件发布后整体重算。