


总体设计结构板：开放回路

一带一轴一环 · 三区两翼 · 命名体系与 Logo 方向

A0-01

N 1

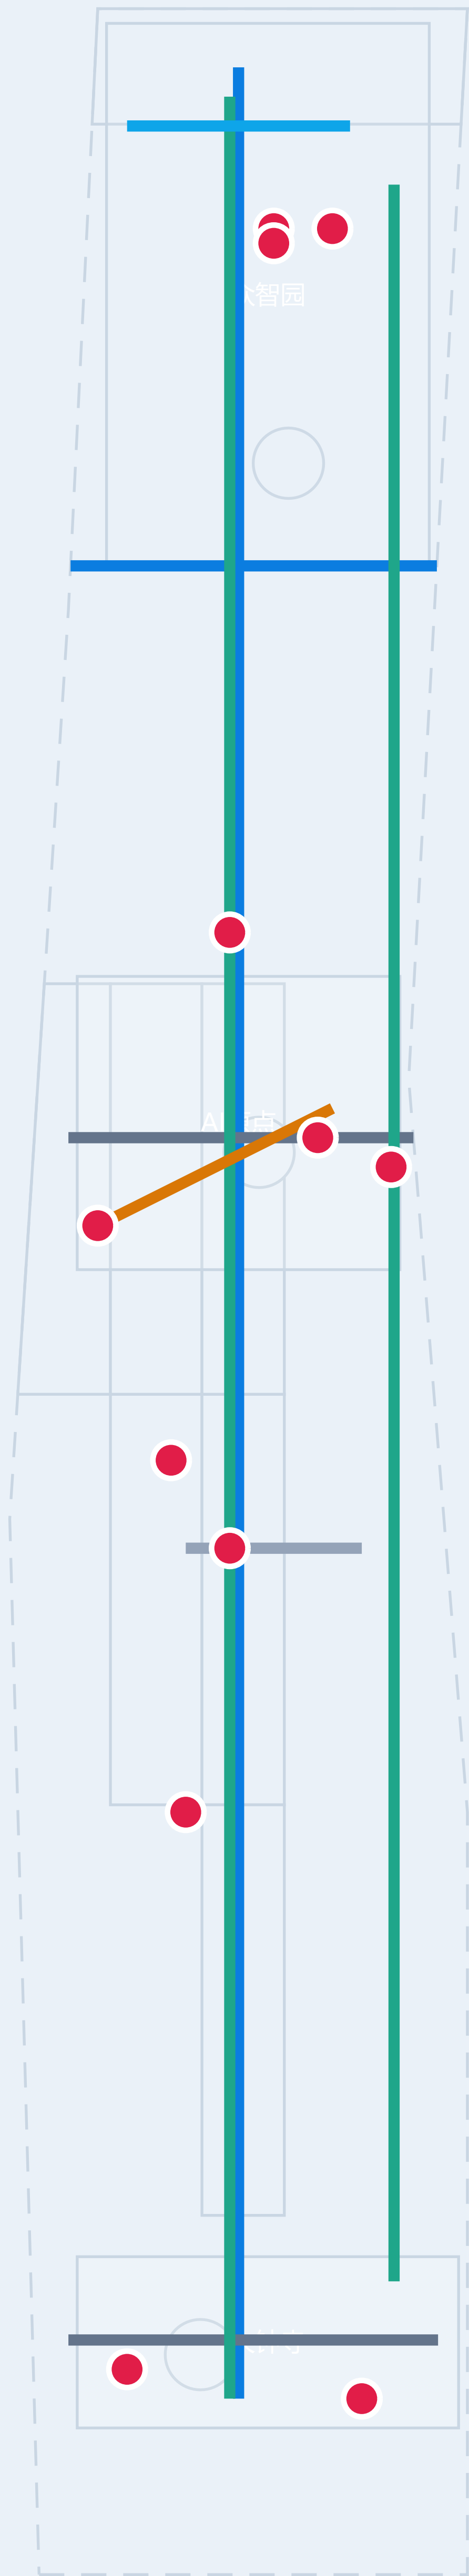

注：虚线为 provisional rough 边界，仅用于概念展示与自检

底图：提交包 geometry/*.geojson (EPSG:4326, 面积按 EPSG:4548 复算)

核心指标

场地面积 site_area_sqm

11,412,825.39

m²

重点区合计

3,692,893.00

m²

AI场景节点

12

个

更新项目 (概念)

45


个

全部指标由 geometry 在 EPSG:4548 下复算；official 边界到位后整体重算。

总体概念与命名体系

- 总体概念：开放回路（Open Loop）——以京张遗址公园活力带为纵轴，智联环串联三区两翼
- 命名体系：京智带 JINGZHI-BELT（京=京张铁路/北京，智=AI，带=创新带/铁路带）
- Logo 方向：双线轨道环 + 三节点光标；色彩：京张铁灰 / AI蓝 / 清河绿
- 三大定位：百年京张文化带、都市AI生活体验带、AI融合创新带
- 五大功能：全栈自主创新、世界级生态、AI+场景赋能、活力城市、治理话语权

N 1

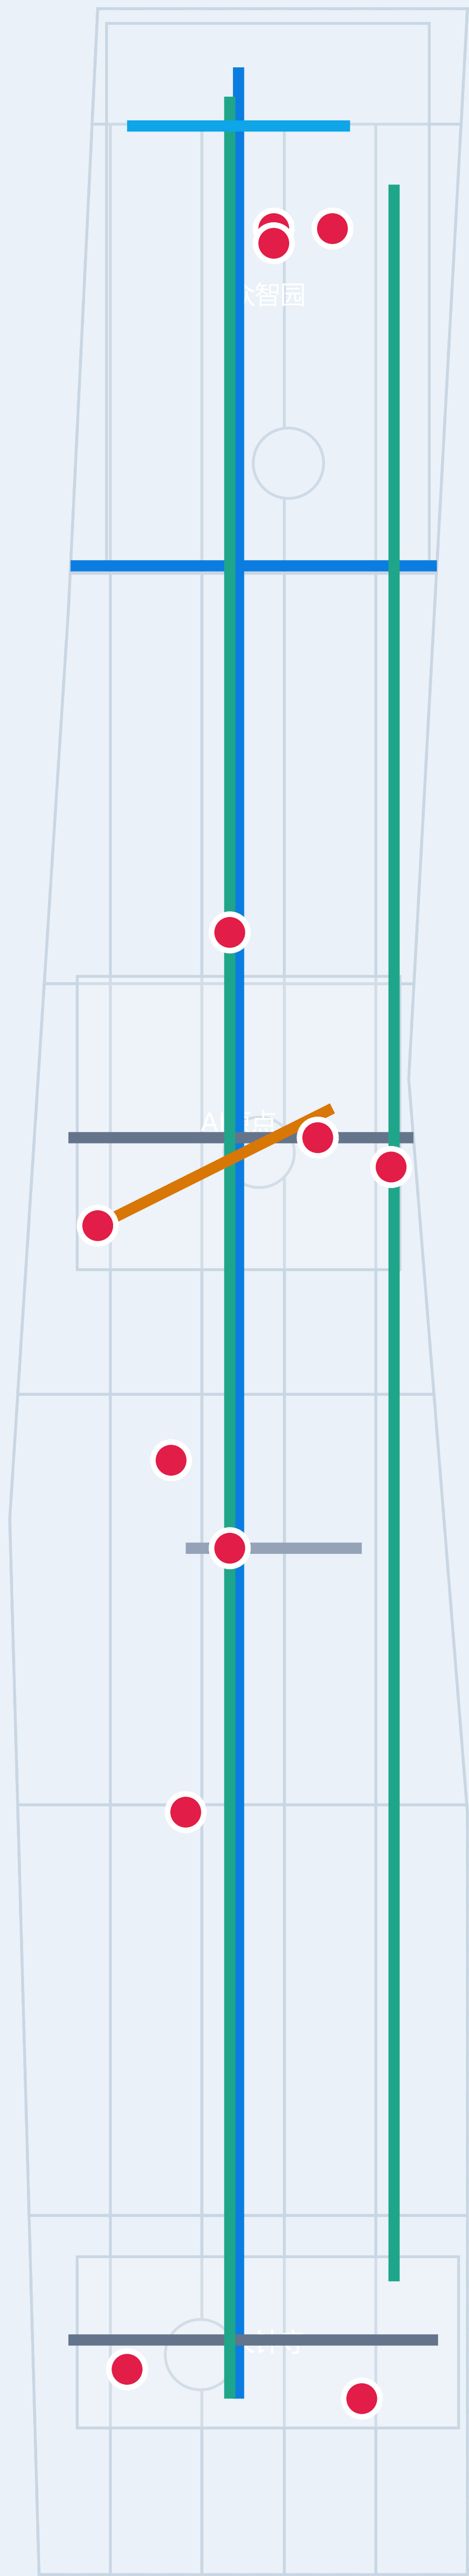

注：虚线为 provisional rough 边界，仅用于概念展示与自检

底图：提交包 geometry/*.geojson（EPSG:4326，面积按 EPSG:4548 复算）


建筑规模与拆改留

- 概念建筑基底面积 4,266,479.10 m²，建筑密度 0.37
- 45 个概念建筑基底附 renewal_status（保留/改造/新建）属性
- 容积率与建筑高度：unknown——官方控规条件未进入公开资料包
- 沿京张遗址公园高度由内向外渐升的风貌引导（待官方附件确认）

用地分类面积（EPSG:4548 复算）

代码	用地名称	面积 m²	说明
0802	科研用地	2,748,252.38	AI研发/实验室
05	商业服务业用地	1,820,243.77	智能原生消费/商务
0701/0702	居住与社区服务	1,948,366.09	人才生活配套
0803/0804	文化/教育用地	852,097.58 / 751,609.00	文化叙事/近校转化
1401/1403	公园绿地/广场	1,933,732.71 / 372,996.36	蓝绿公共空间

N 1

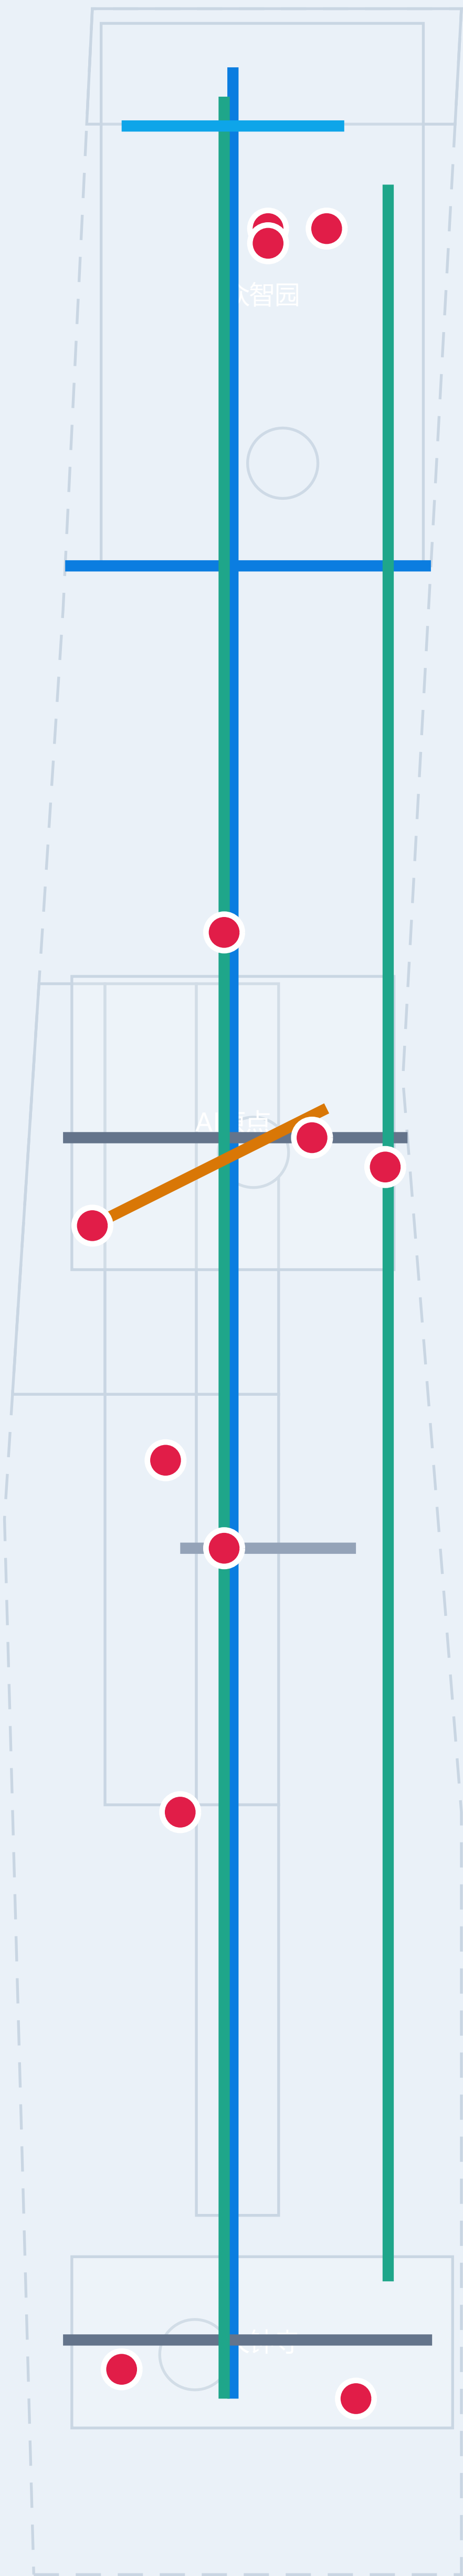

注：虚线为 provisional rough 边界，仅用于概念展示与自检

底图：提交包 geometry/*.geojson (EPSG:4326, 面积按 EPSG:4548 复算)

关键指标

道路面积 road_area_sqm

11,412,825.39

m²

道路比例 road_ratio

1.00

公共空间比例

0.04

比值


市政与新型基础设施（概念原型）

- 分布式能源与端侧算力驿站：结合公共服务与企业服务节点布局
- 数据要素会客厅：数据流通规则与合规评审机制另议（SC-08）
- 创新服务平台与人才生活服务设施体系纳入更新项目清单

道路系统（概念）

类别	名称	设计宽度	说明
次干路	南北贯通次干路	26 m	串联三处重点区
支路	原点/大钟寺东西缝合支路	18 m	织补慢行断点
绿道	京张遗址公园活力绿道	12 m	连续步行骑行主轴
绿道	小月河场景赋能翼绿道	12 m	东侧片区联系
轨道接驳	五道口/清华东路西口/大钟寺站步行轴	15 m	站点四象限连通

N 1

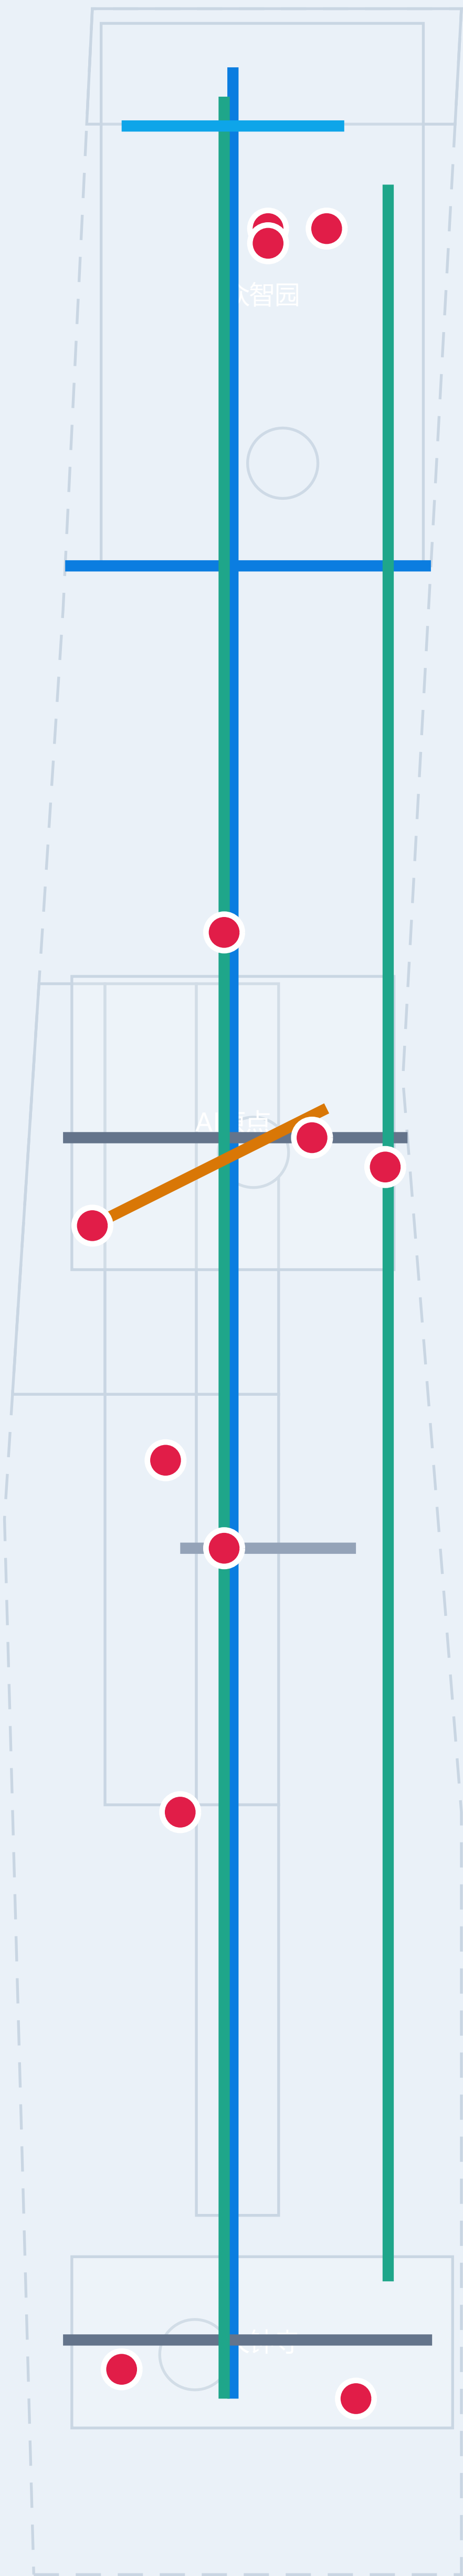

注：虚线为 provisional rough 边界，仅用于概念展示与自检

底图：提交包 geometry/*.geojson (EPSG:4326, 面积按 EPSG:4548 复算)

荣誉展示与组件库


- 组件库三类：轨道符号、节点光标、回路路径
- 文化标识系统与一带整体 Logo 系统分置管理

三个 AI 朝圣地标方向（概念建议）

地标	位置	设计方向
原点车站	清华园车站旧址周边	京张铁路历史与AI新文化荣誉展示节点
开源代码长廊	京张遗址公园中段	开源贡献墙 + 数字导览 + 开发者荣誉体系
智钟广场	大钟寺站四象限	智能钟表装置 + 数据要素会客厅

蓝绿系统与核心指标

绿地面积 green_space_area_sqm	绿地比例 green_ratio	公共空间面积	公共空间比例
2,403,569.86m ²	0.21 比值	501,515.76m ²	0.04 比值

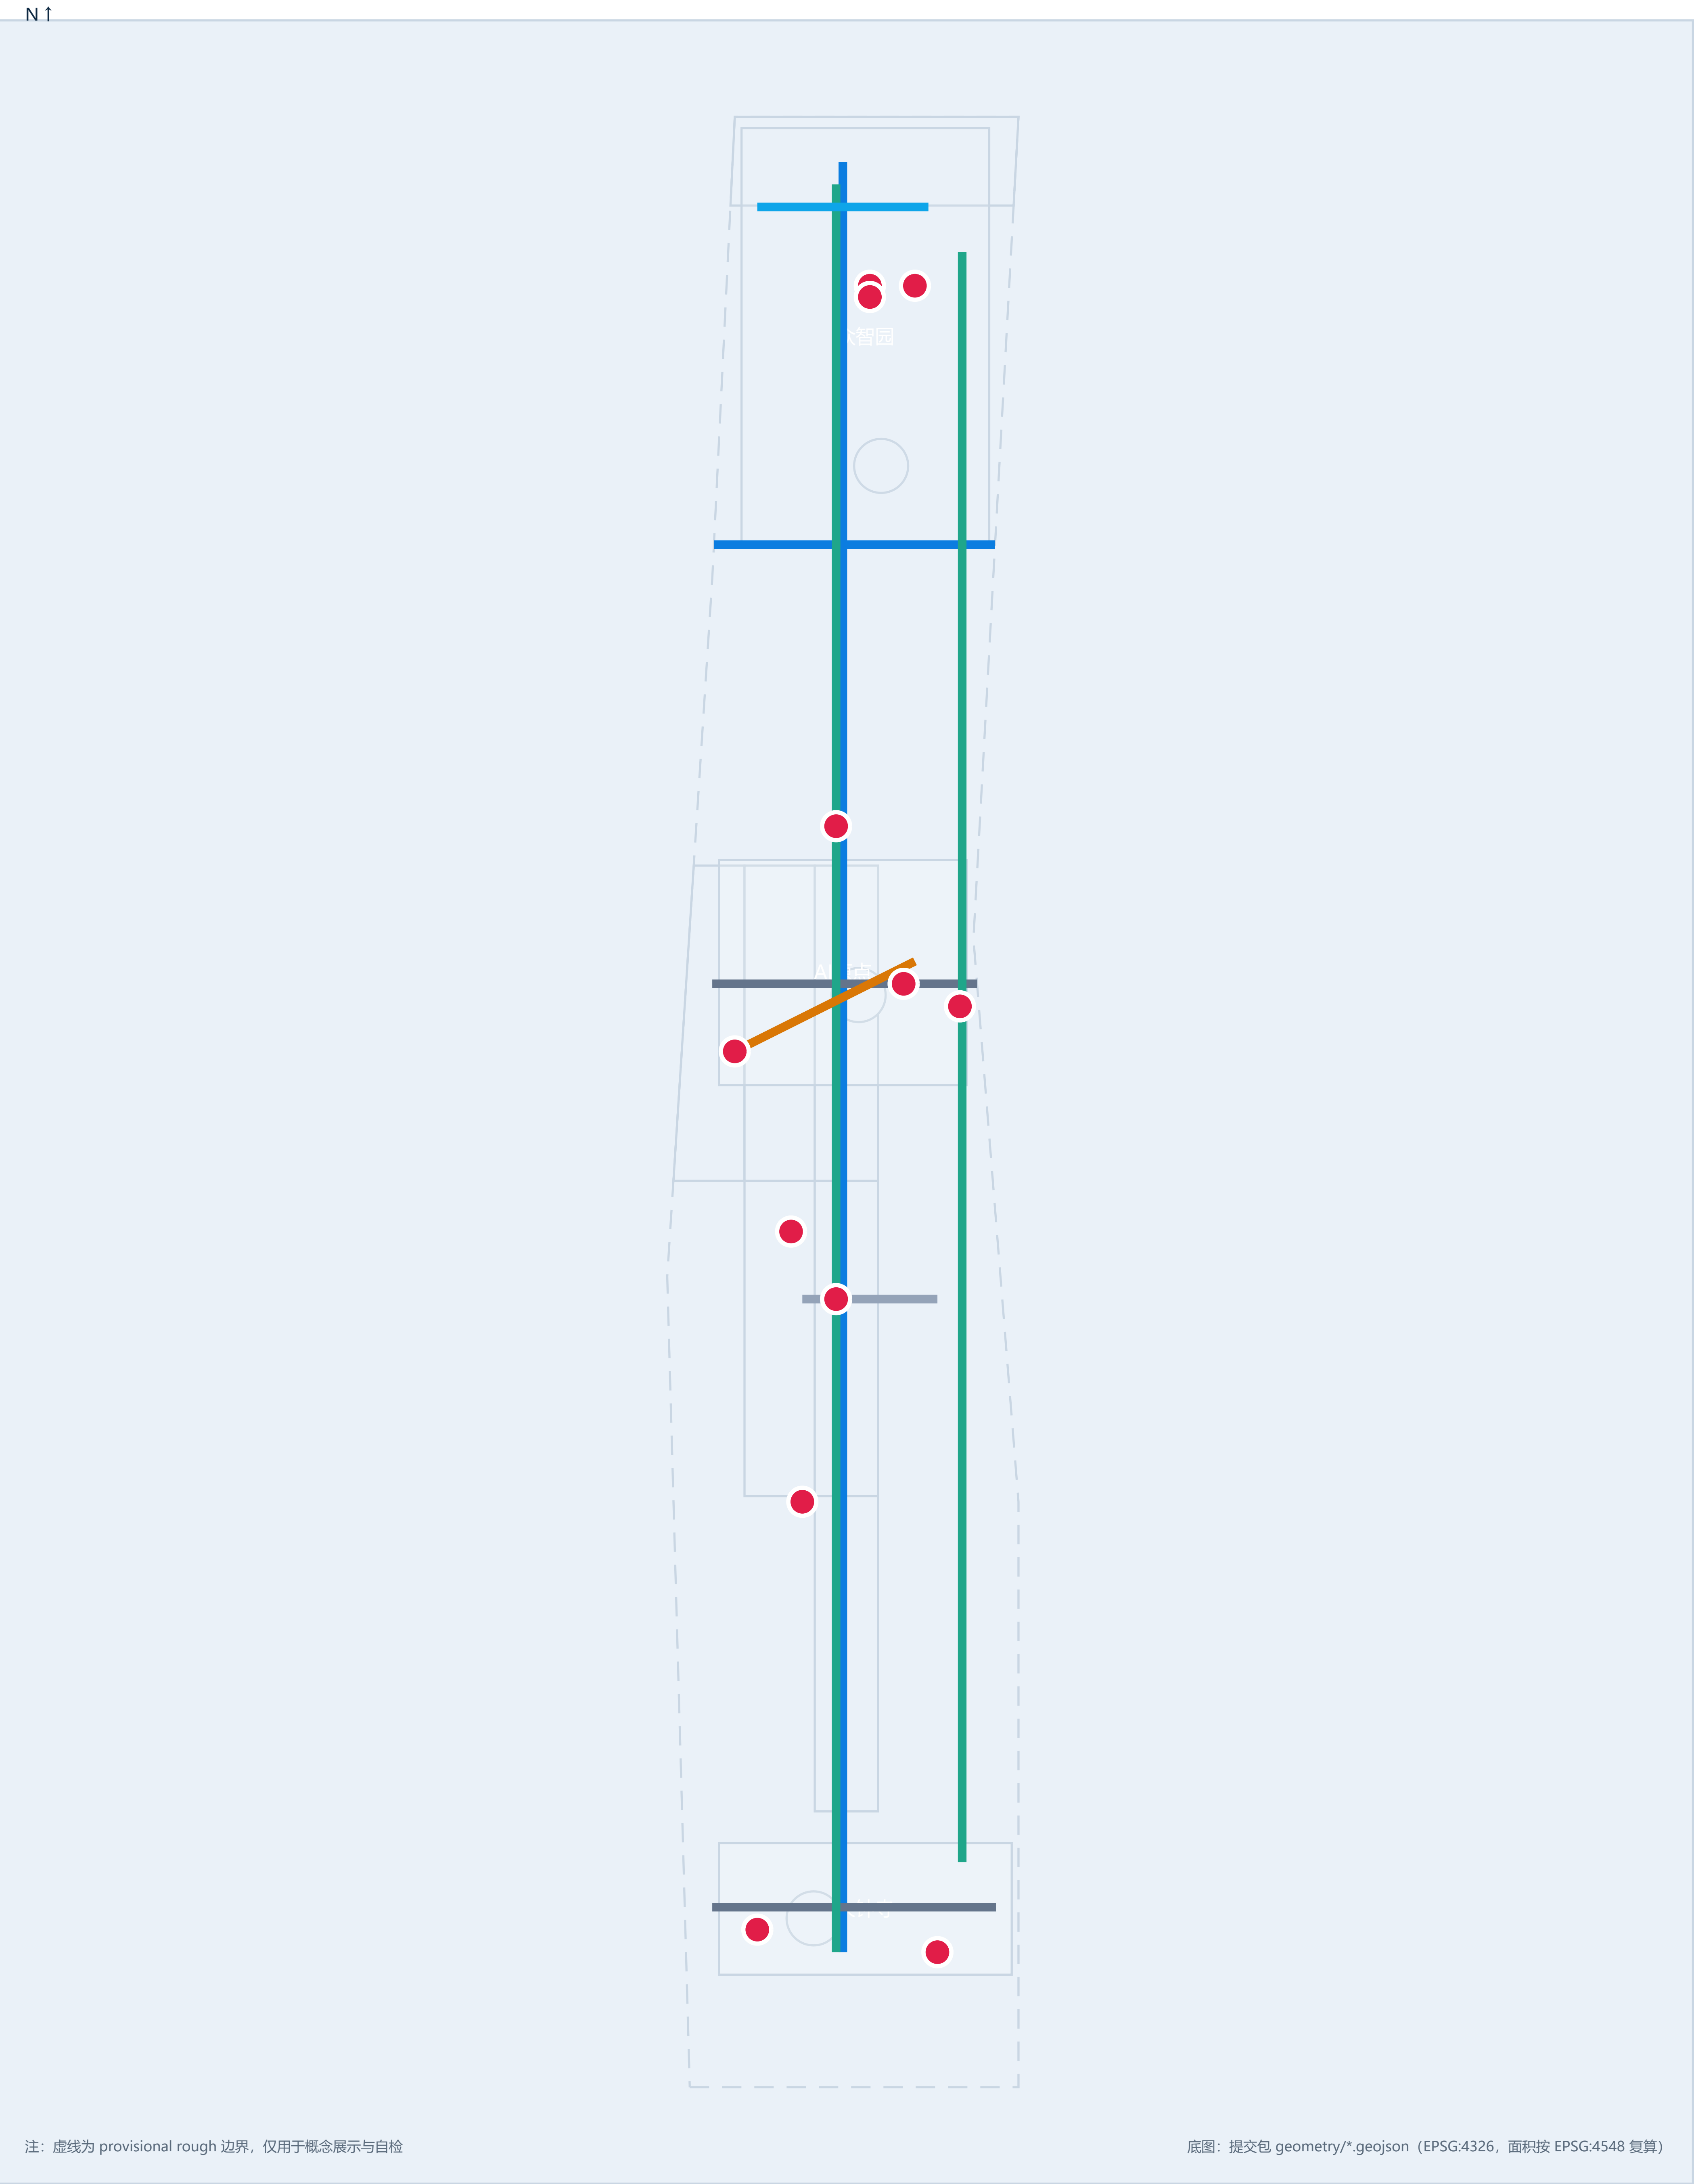

合规与自检

- 合规矩阵 23 条 (公告 1.3/1.4/1.5 共 17 条 + agent.1-6 共 6 条)
- 标准矩阵 5 项强制标准 addressed; 设计深度矩阵 15 项 complete
- 自检: 确定性/空间/可视化/专业证据审查全部 PASS

分期实施 (对应 phasing.geojson)

阶段	范围	复算面积 m²
近期	大钟寺站城一体与公园南段	5,224,741.09
中期	原点社区近校更新与公园中段	3,277,392.42
远期	众智园北段与清河界面	2,910,687.36

AI 场景卡 (SC-01 至 SC-12)

编号	场景	空间载体
SC-01/07/12	开源发布 / 成果转化 / 夜间协作	AI原点社区
SC-02/03/06	安全治理沙盒 (测试) / 算力驿站 / 低破廊	众智园
SC-04/11	AI慢行导航 / 文化数字导览	京张遗址公园
SC-05/08/09	国际路演 / 数据要素 (测试) / 低速配送 (测试)	大钟寺
SC-10	AI健康服务导航	公共空间节点