



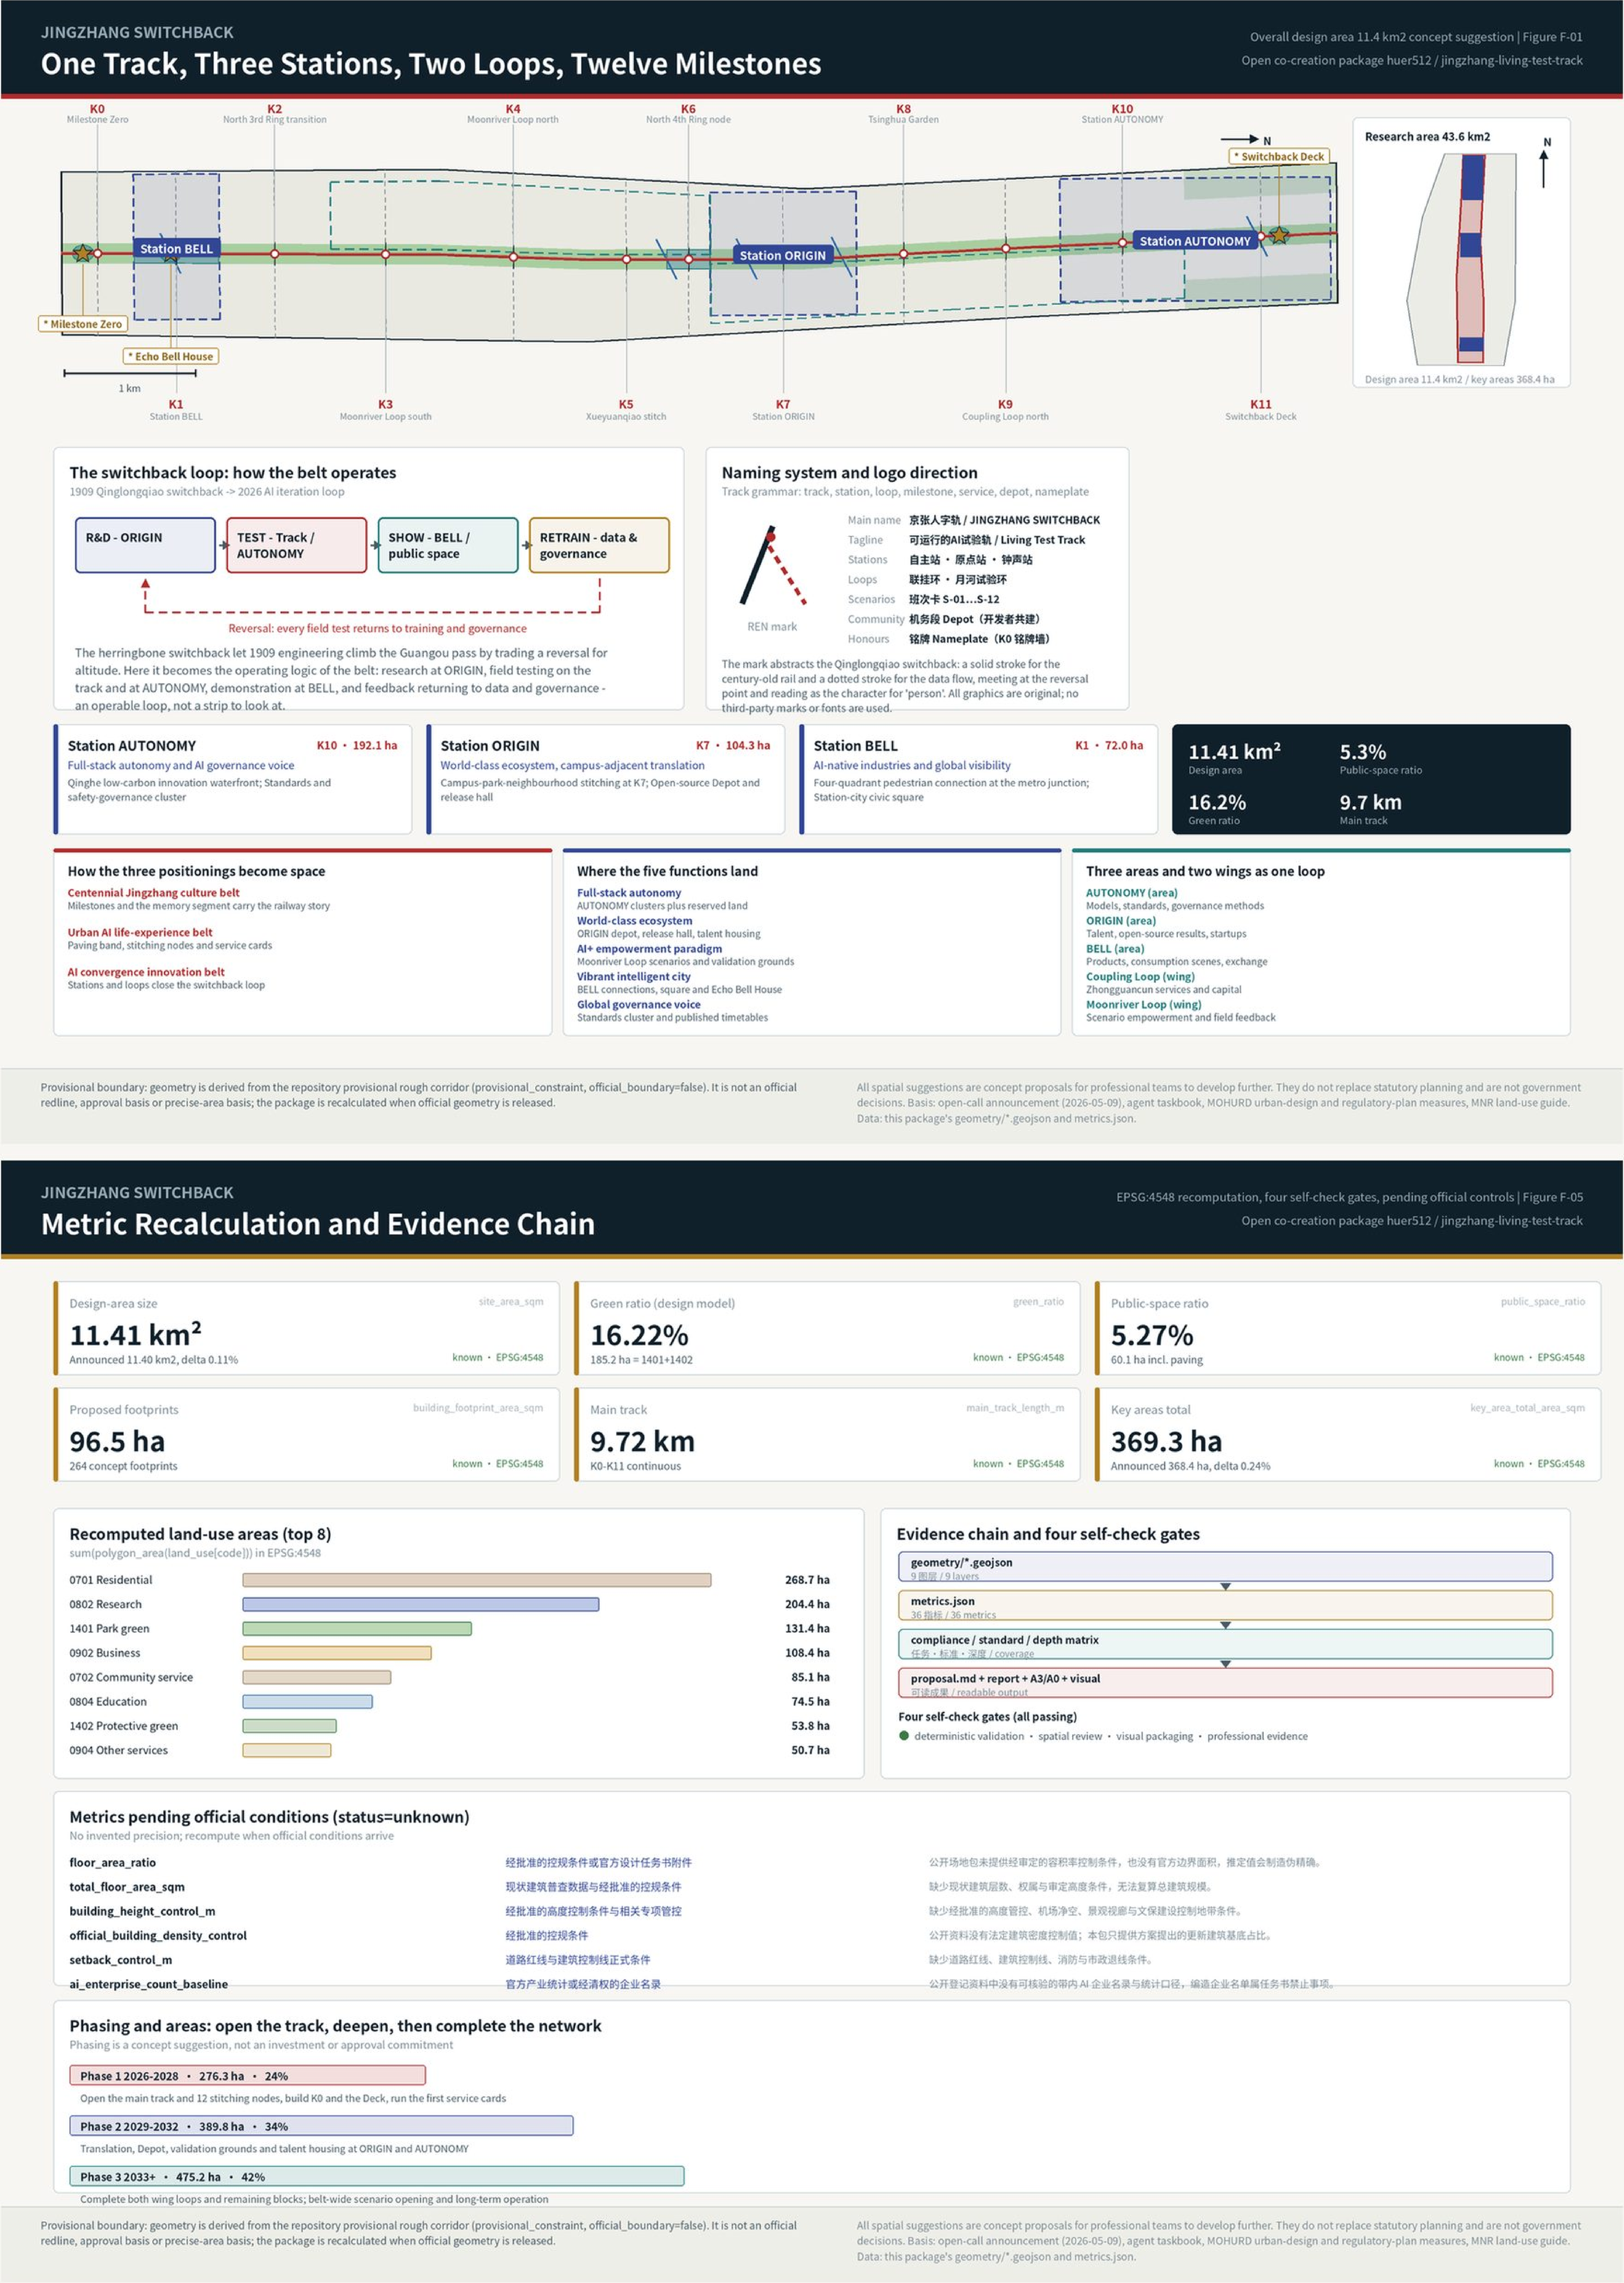

JINGZHANG SWITCHBACK

Three Stations in Detail: AUTONOMY, ORIGIN, BELL

Key detailed-design area 368.4 ha concept suggestion | Figure F-03
Open co-creation package huer512 / jingzhang-living-test-track

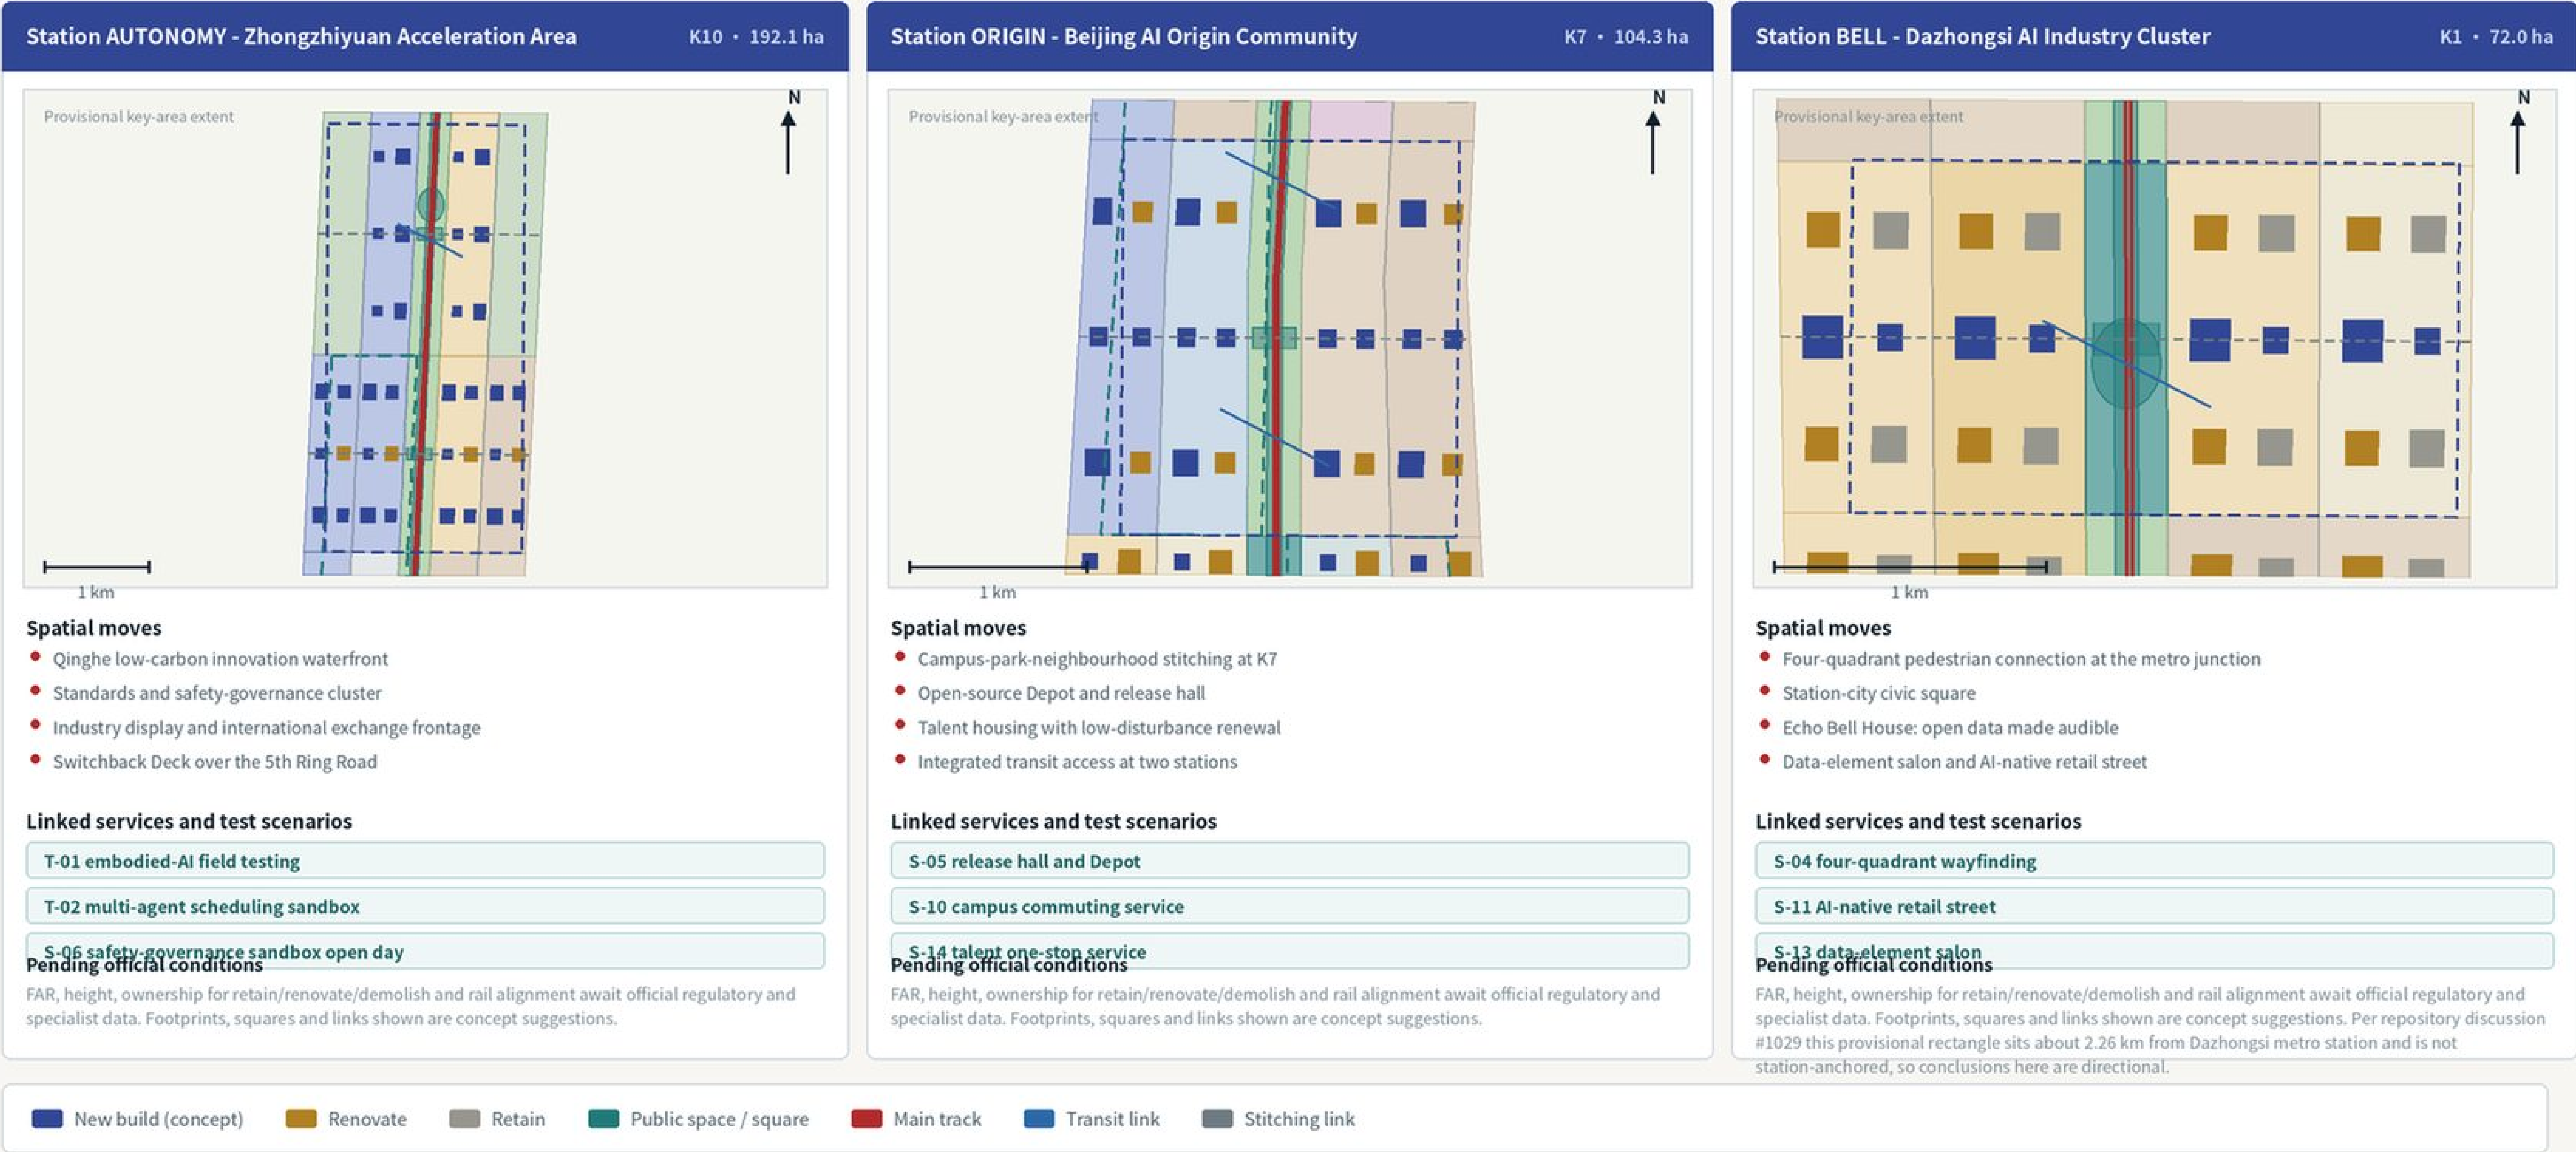

Three stations compared: role, mechanism, evidence

Station	Announced area	Role	Core mechanism	Evidence
Station AUTONOMY	192.1 ha	Full-stack autonomy and AI governance voice	Co-locating open testing with standards governance	PROV-KEY-001 / depth:three_key_area_detailed_design
Station ORIGIN	104.3 ha	World-class ecosystem, campus-adjacent translation	Open-source Depot plus release hall	PROV-KEY-002 / metric:key_area_count
Station BELL	72.0 ha	AI-native industries and global visibility	Four-quadrant connection plus Echo Bell House	PROV-KEY-003 / data:public_space.geojson


Provisional boundary: geometry is derived from the repository provisional rough corridor (provisional_constraint, official_boundary=false). It is not an official redline, approval basis or precise-area basis; the package is recalculated when official geometry is released.

All spatial suggestions are concept proposals for professional teams to develop further. They do not replace statutory planning and are not government decisions. Basis: open-call announcement (2026-05-09), agent taskbook, MOHURD urban-design and regulatory-plan measures, MNR land-use guide. Data: this package's geometry/"_.geojson and metrics.json.

JINGZHANG SWITCHBACK

Land-use Structure and Reserved-Land Strategy: a 60-face seamless partition

Coded with the MNR land-use classification guide | Figure F-02
Open co-creation package huer512 / jingzhang-living-test-track

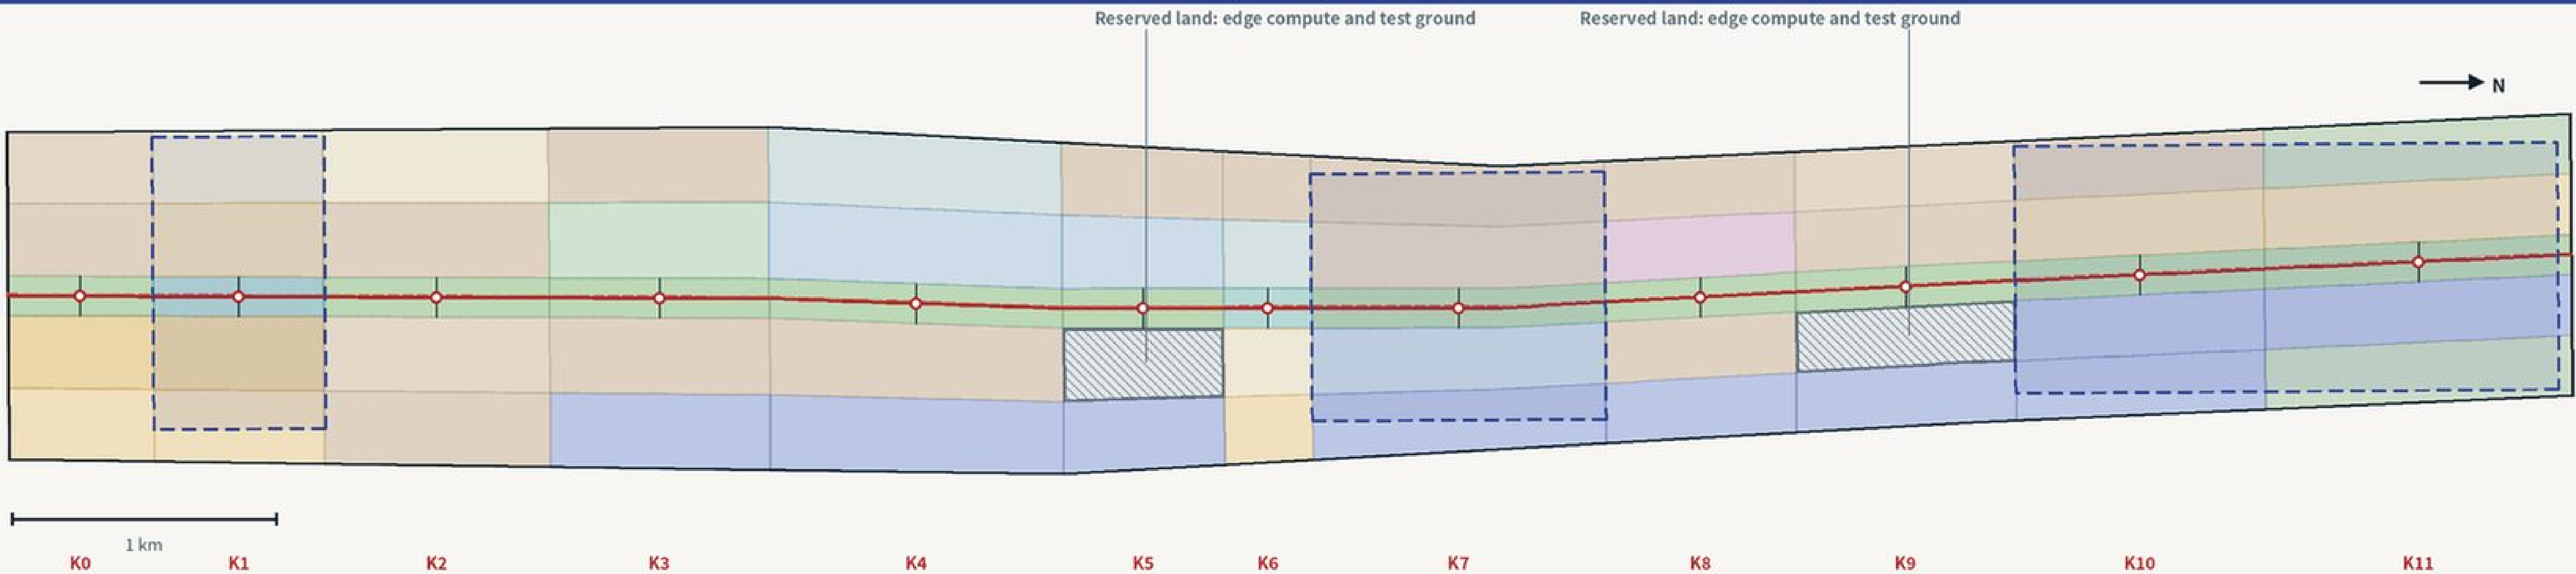

Land-use codes, areas and design intent

0701 Residential	268.7 ha	23.5%	0904 Other services	50.7 ha	4.4%
0802 Research	204.4 ha	17.9%	0806 Health	40.1 ha	3.5%
1401 Park green	131.4 ha	11.5%	16 Reserved	35.6 ha	3.1%
0902 Business	108.4 ha	9.5%	0901 Commercial	33.3 ha	2.9%
0702 Community service	85.1 ha	7.5%	0805 Sports	23.9 ha	2.1%
0804 Education	74.5 ha	6.5%	0803 Culture	16.7 ha	1.5%
1402 Protective green	53.8 ha	4.7%	1403 Civic square	14.7 ha	1.3%

Partition topology and recomputation

Faces	60
Coverage gap	50.8 m²
Overlaps	0
Tolerance	1,141 m² (0.01%)
Park green	131.4 ha
Research	204.4 ha
Reserved	35.6 ha

The partition is generated, not hand-drawn: the provisional boundary, twelve segment lines and longitudinal control lines are polygonized together, so adjacent faces share vertices and the result is seamless and overlap-free in EPSG:4548, recomputable by scripts/spatial_review.py. Reserved land keeps the uncertainty of compute, energy and test grounds in space instead of in false-precision indicators.

Twelve segments: dominant land use, renewal tendency, projects

Retain/renovate/demolish is a concept suggestion pending ownership and survey data

Seg/Milestone	Area	Dominant land use	Renewal tendency	Key renewal projects
B01 • K0	69.6 ha	Business + commercial	Renovate-led	Milestone Zero and gateway frontage
B02 • K1	81.6 ha	Business + civic square	Renovate + selective new build	Four-quadrant link, square, Echo Bell House
B03 • K2	109.6 ha	Residential + community	Retain-led	AI life-service street, embedded services
B04 • K3	108.3 ha	Research + sports	Renovate + new build	Moonriver Loop south, trackside sports
B05 • K4	142.9 ha	Research + health	New-build-led	AI+health validation ground, rental housing
B06 • K5	75.1 ha	Research + reserved	Renovate + reserve	Translation street, compute/energy reserve

Seg/Milestone	Area	Dominant land use	Renewal tendency	Key renewal projects
B07 • K6	39.2 ha	Business + civic square	Renovate-led	Stitching square, talent one-stop service
B08 • K7	122.6 ha	Research + education + community	Low-disturbance renewal	Depot, release hall, talent housing
B09 • K8	77.5 ha	Residential + culture	Retain + restore	Memory gallery, open-source units
B10 • K9	88.9 ha	Research + reserved	Renovate + reserve	Coupling Loop services, test reserve
B11 • K10	100.8 ha	Research + business	New-build-led	Autonomy clusters, standards, display
B12 • K11	125.1 ha	Protective green + research	Ecology-first	Switchback Deck, Qinghe waterfront

Provisional boundary: geometry is derived from the repository provisional rough corridor (provisional_constraint, official_boundary=false). It is not an official redline, approval basis or precise-area basis; the package is recalculated when official geometry is released.

All spatial suggestions are concept proposals for professional teams to develop further. They do not replace statutory planning and are not government decisions. Basis: open-call announcement (2026-05-09), agent taskbook, MOHURD urban-design and regulatory-plan measures, MNR land-use guide. Data: this package's geometry/"_.geojson and metrics.json.


Stitching, blue-green public space and implementation

JINGZHANG SWITCHBACK

12 stitching nodes, 5 transit links, 44 m public paving | Figure F-04

Stitching, Blue-Green Network and the Programmable Lane Section

Open co-creation package huer512 / jingzhang-living-test-track

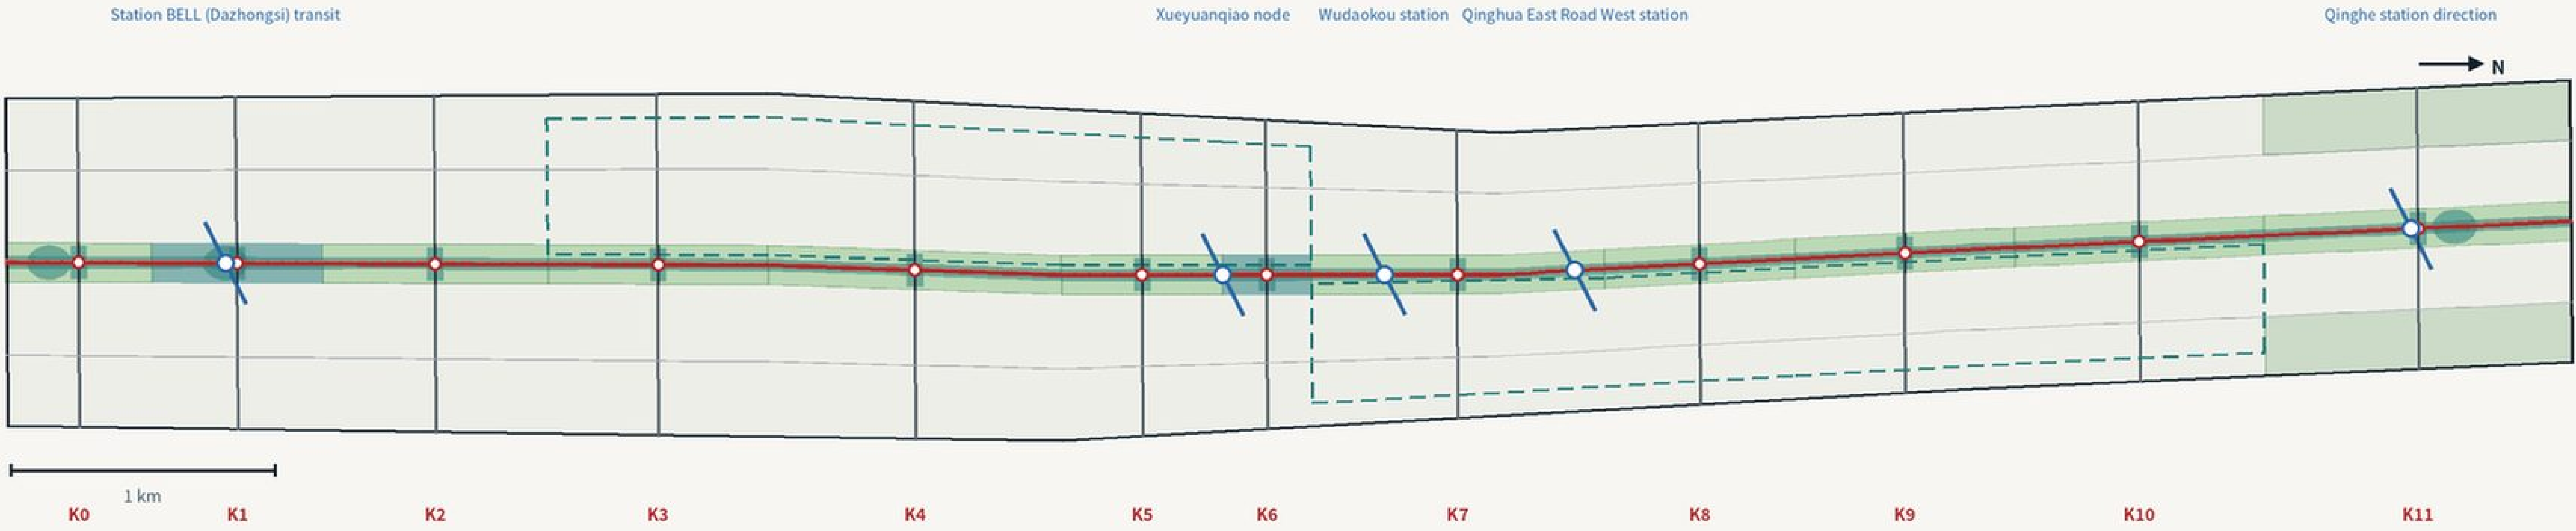

Section of the switchback public paving band (concept, 44 m)

Heritage strip | 4.5 m slow lane | 2.5 m programmable lane | buffer | community edge

Heritage strip 6m

Slow lane 4.5m

Programmable lane 2.5m

Buffer green 3m

Trees and seating 6m

44 m

The section is about time, not width. The programmable lane shares material and level with the slow lane: by default it is walking and resting space, opened by published timetable for delivery, cleaning and wheelchair-companion trials, with on-site human override and stop controls, and no night-time testing.

Gap stitching and the blue-green network

- 12 stitching nodes K0-K11, total stitching length 14,177 m
- Continuous main track 9.72 km; proposed slow-mobility network 69.6 km
- Green space 185.2 ha (park + protective), ratio 16.2%
- Public space 60.1 ha, ratio 5.3%
- 5 transit links: BELL four-quadrant, Xueyuanqiao, Wudaokou, Qinghua East Road West, Qinghe direction
- Two ring-road crossings: K11 Switchback Deck (5th Ring) and K0 gateway

Green and public-space ratios overlap by design (paving sits inside the park) and must not be added; see assumptions.json A-OVERLAP-001.

Twelve stitching nodes: gap, stitching action, linked services			
Stitching actions are concept suggestions; ring-road and under-bridge cases need specialist review			
Node	Gap observed	Stitching action (concept)	Services
K0	South gateway meets an arterial; the slow route simply ends	Milestone Zero plaza and nameplate wall with accessible entries	S-02 S-08
K1	Car-dominated metro junction, disorderly bicycle parking	Four-quadrant pedestrian link, station square, parking order	S-04 S-11
K2	Communities split by the 3rd Ring, long detours	Stitching link with local crossing and embedded services	S-03 S-09
K3	Gaps along Xiaoyue river, no continuous cycling	Close the Moonriver Loop south, trackside sports	S-09 T-03
K4	No direct walking link between campus and riverside	Stitching link, campus frontage opening, shaded seating	S-10
K5	Mixed traffic at Xueyuanqiao, dead space under the bridge	Stitching square, under-bridge services and lighting tiers	S-03 S-07

Node	Gap observed	Stitching action (concept)	Services
K6	Hard to cross the 4th Ring, service gap	Stitching square with talent one-stop and health services	S-14 S-02
K7	Three-way gap between campus, park and neighbourhood	Triple stitching with Depot and release-hall forecourt	S-05 S-10
K8	Railway remains unexplained to the neighbourhood	Memory gallery, platform narrative, low-impact lighting	S-06 S-12
K9	Weak link between Coupling Loop north and Heqing Road	Close the loop, add embedded community service points	S-13 S-14
K10	Walls cut AUTONOMY off from the main track	Stitching link, display forecourt, open-test entrance	T-01 T-02
K11	No place to pause at the 5th Ring crossing	Switchback Deck viewing and narrative, Qinghe continuity	S-06 S-08

Provisional boundary: geometry is derived from the repository provisional rough corridor (provisional_constraint, official_boundary=false). It is not an official redline, approval basis or precise-area basis; the package is recalculated when official geometry is released.

All spatial suggestions are concept proposals for professional teams to develop further. They do not replace statutory planning and are not government decisions. Basis: open-call announcement (2026-05-09), agent taskbook, MOHURD urban-design and regulatory-plan measures, MNR land-use guide. Data: this package's geometry/"'.geojson and metrics.json.

Implementation, operation, risk and boundary

- Near term 2026-2028 (276.3 ha): open the track and twelve stitching nodes, build K0 and the Deck, run the first service cards.
- Medium term 2029-2032 (389.8 ha): translation, Depot, validation grounds and talent housing at ORIGIN and AUTONOMY.
- Long term 2033+ (475.2 ha): both wing loops and remaining blocks complete renewal, belt-wide scenario opening.
- Twelve renewal projects each state their dependencies; unresolved conditions keep a project researchable.

- Track Week: spring opening, summer test season, autumn results week, winter review.
- Depot community: fixed hours, public task board, contribution records, nameplate honours.
- Scenario opening in four steps: apply, assess, publish, review.
- Boundary: concept proposals only; not statutory planning and not a government decision.

Risk and mitigation

- Data privacy (4): aggregate statistics, no person recognition, publication and human review.
- Technology maturity (4): shadow mode first, exit-capable installations, reserved land.
- Implementation complexity (4): ring-road and station projects listed with preconditions.
- Public acceptance (3): pedestrian priority, published windows, on-site stop controls.

Boundary and verifiability

- No FAR, height, plot-level renewal, road or rail alignment, or feasibility conclusions.
- No non-public or personal data; no claim of official approval, endorsement or commitment.
- All graphics original, typefaces open-licensed; case citations carry source, date and limits.
- All four self-check gates pass; 36 metrics recomputable from this package in EPSG:4548.