


JING-ZHANG CIVIC FOUNDRY | THE SITE IS NOT A STRAIGHT STRIP

One provisional base model aligns the official text extent, announced areas and four public background anchors—without pretending to be a statutory boundary.

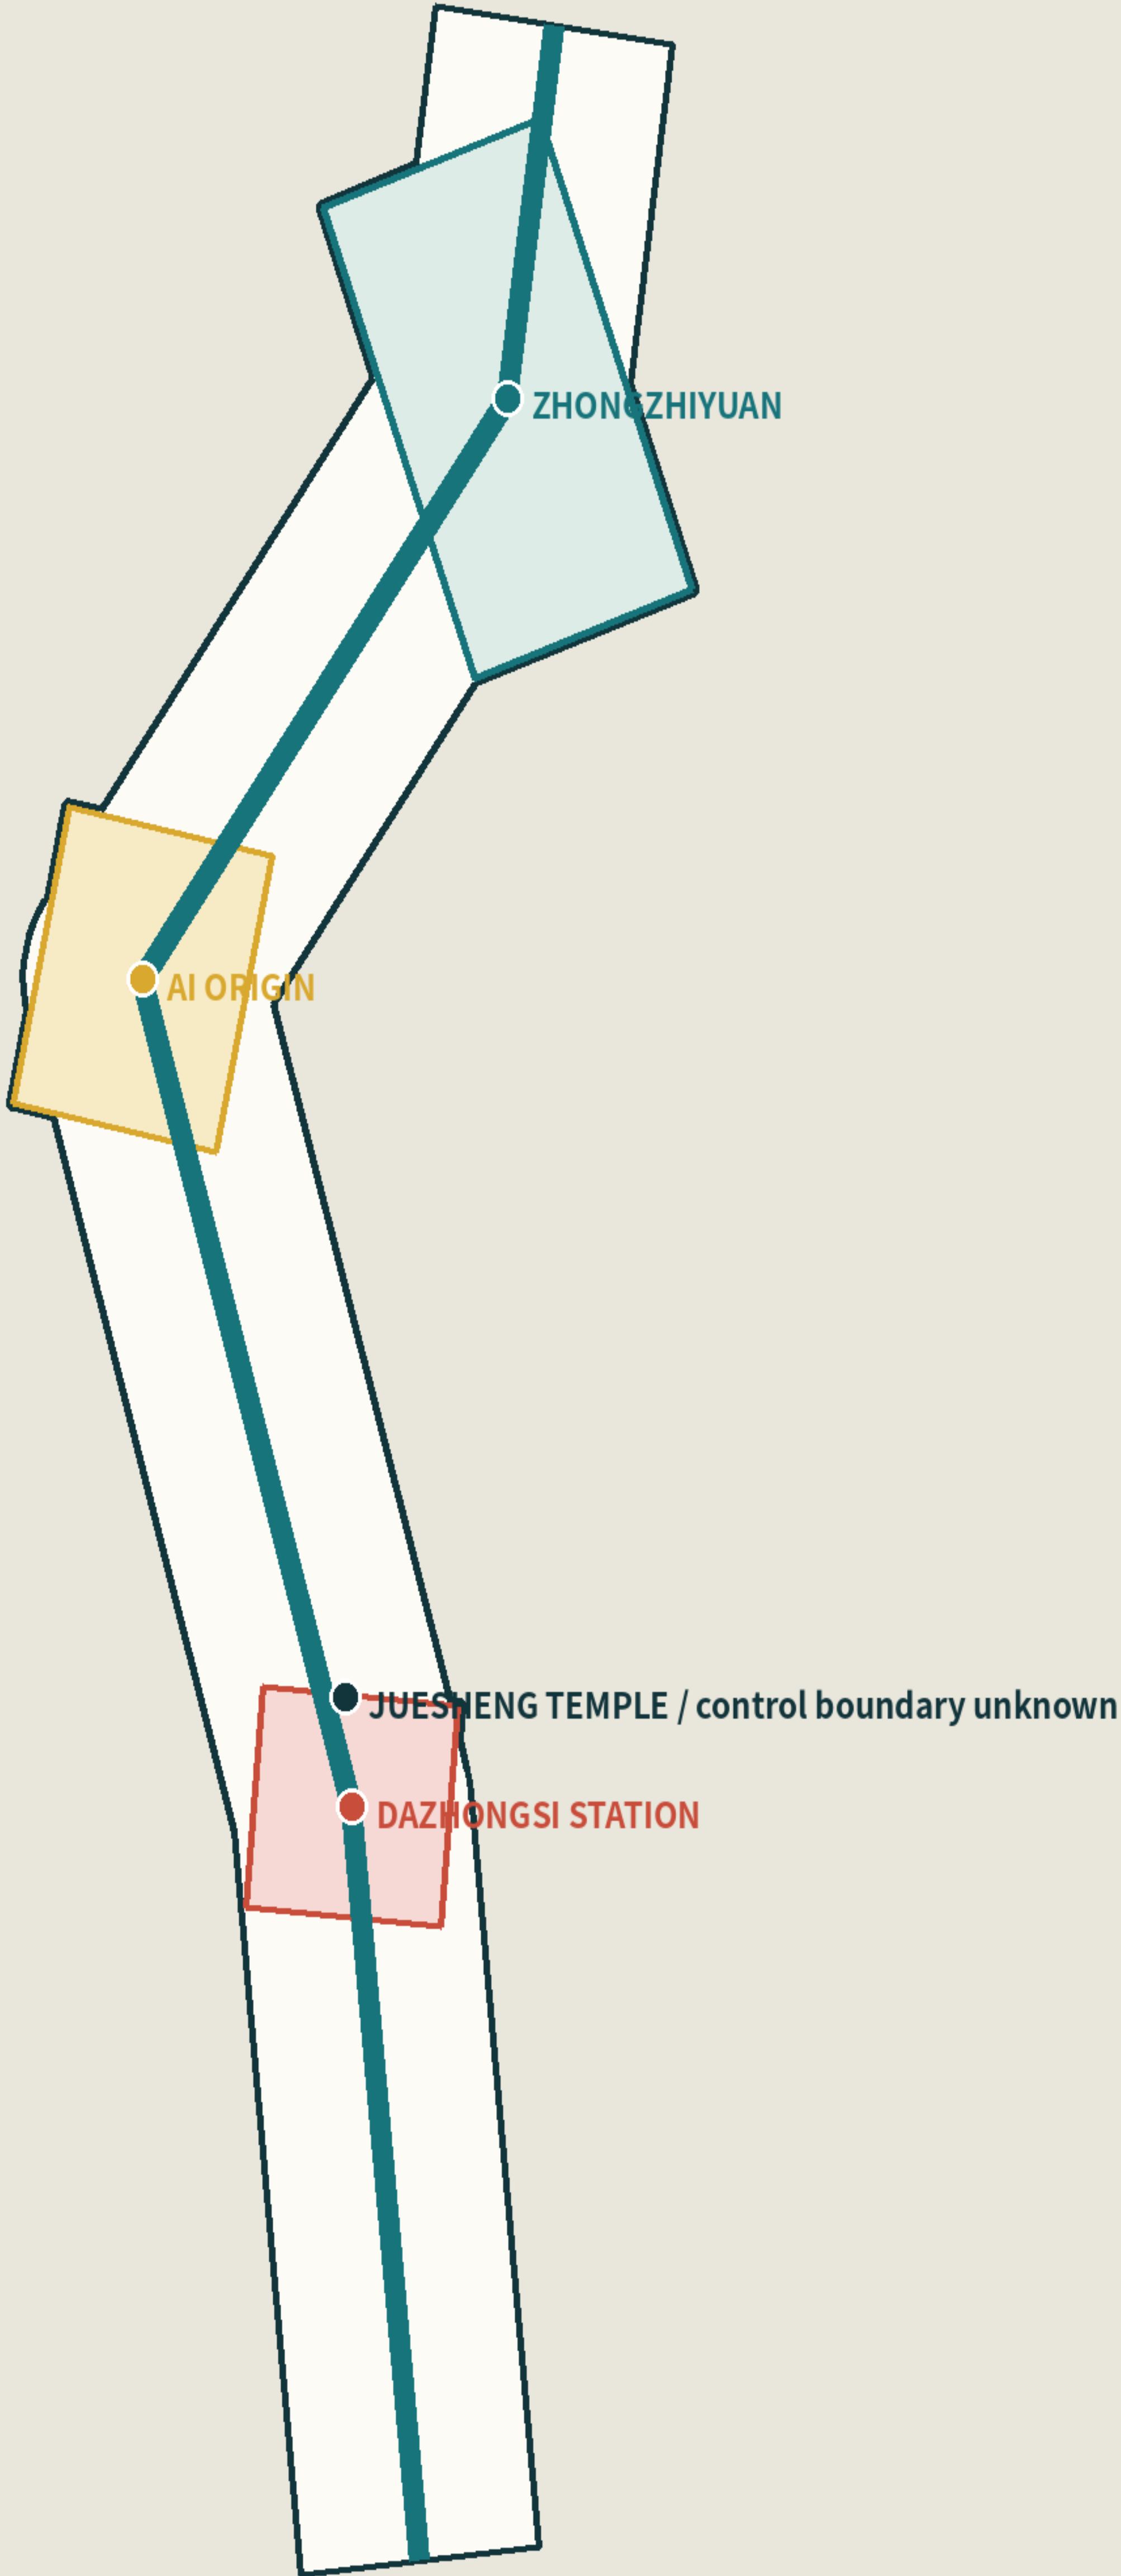

PROVISIONAL / anchor-aligned, not an official redline

DO NOT MIX SCALES

43.6 km² coordinated research / 11.4 km² overall design / 368.4 ha across three key areas. The 16 ha existing AI Origin core and ~3 km² influence range are background only.

FOUR ANCHORS

Xuezhiyuan–Zhongzhiyuan, Origin Building, Dazhongsi Station and Juesheng Temple. Coordinates support orientation only; statutory polygons remain missing.

ONE SPATIAL PROPOSITION

Embed cultural evidence, civic commissions, public prototypes and one-year adopt-or-exit decisions into actual ground floors and public-space sequences.

RECALCULATION CONTRACT


When official polygons arrive, regenerate all nine GeoJSON layers, metrics, five figures, A3/A0 and offline HTML—not just the basemap.

THE THREE KEY AREAS ARE NOT ONE GENERIC AI DISTRICT

Street–block–plot–building logic gives each area a different five-minute sequence, ground-floor contract and acceptance focus.

ZHONGZHIYUAN | GARDEN SUPERBLOCK

192.1 ha provisional

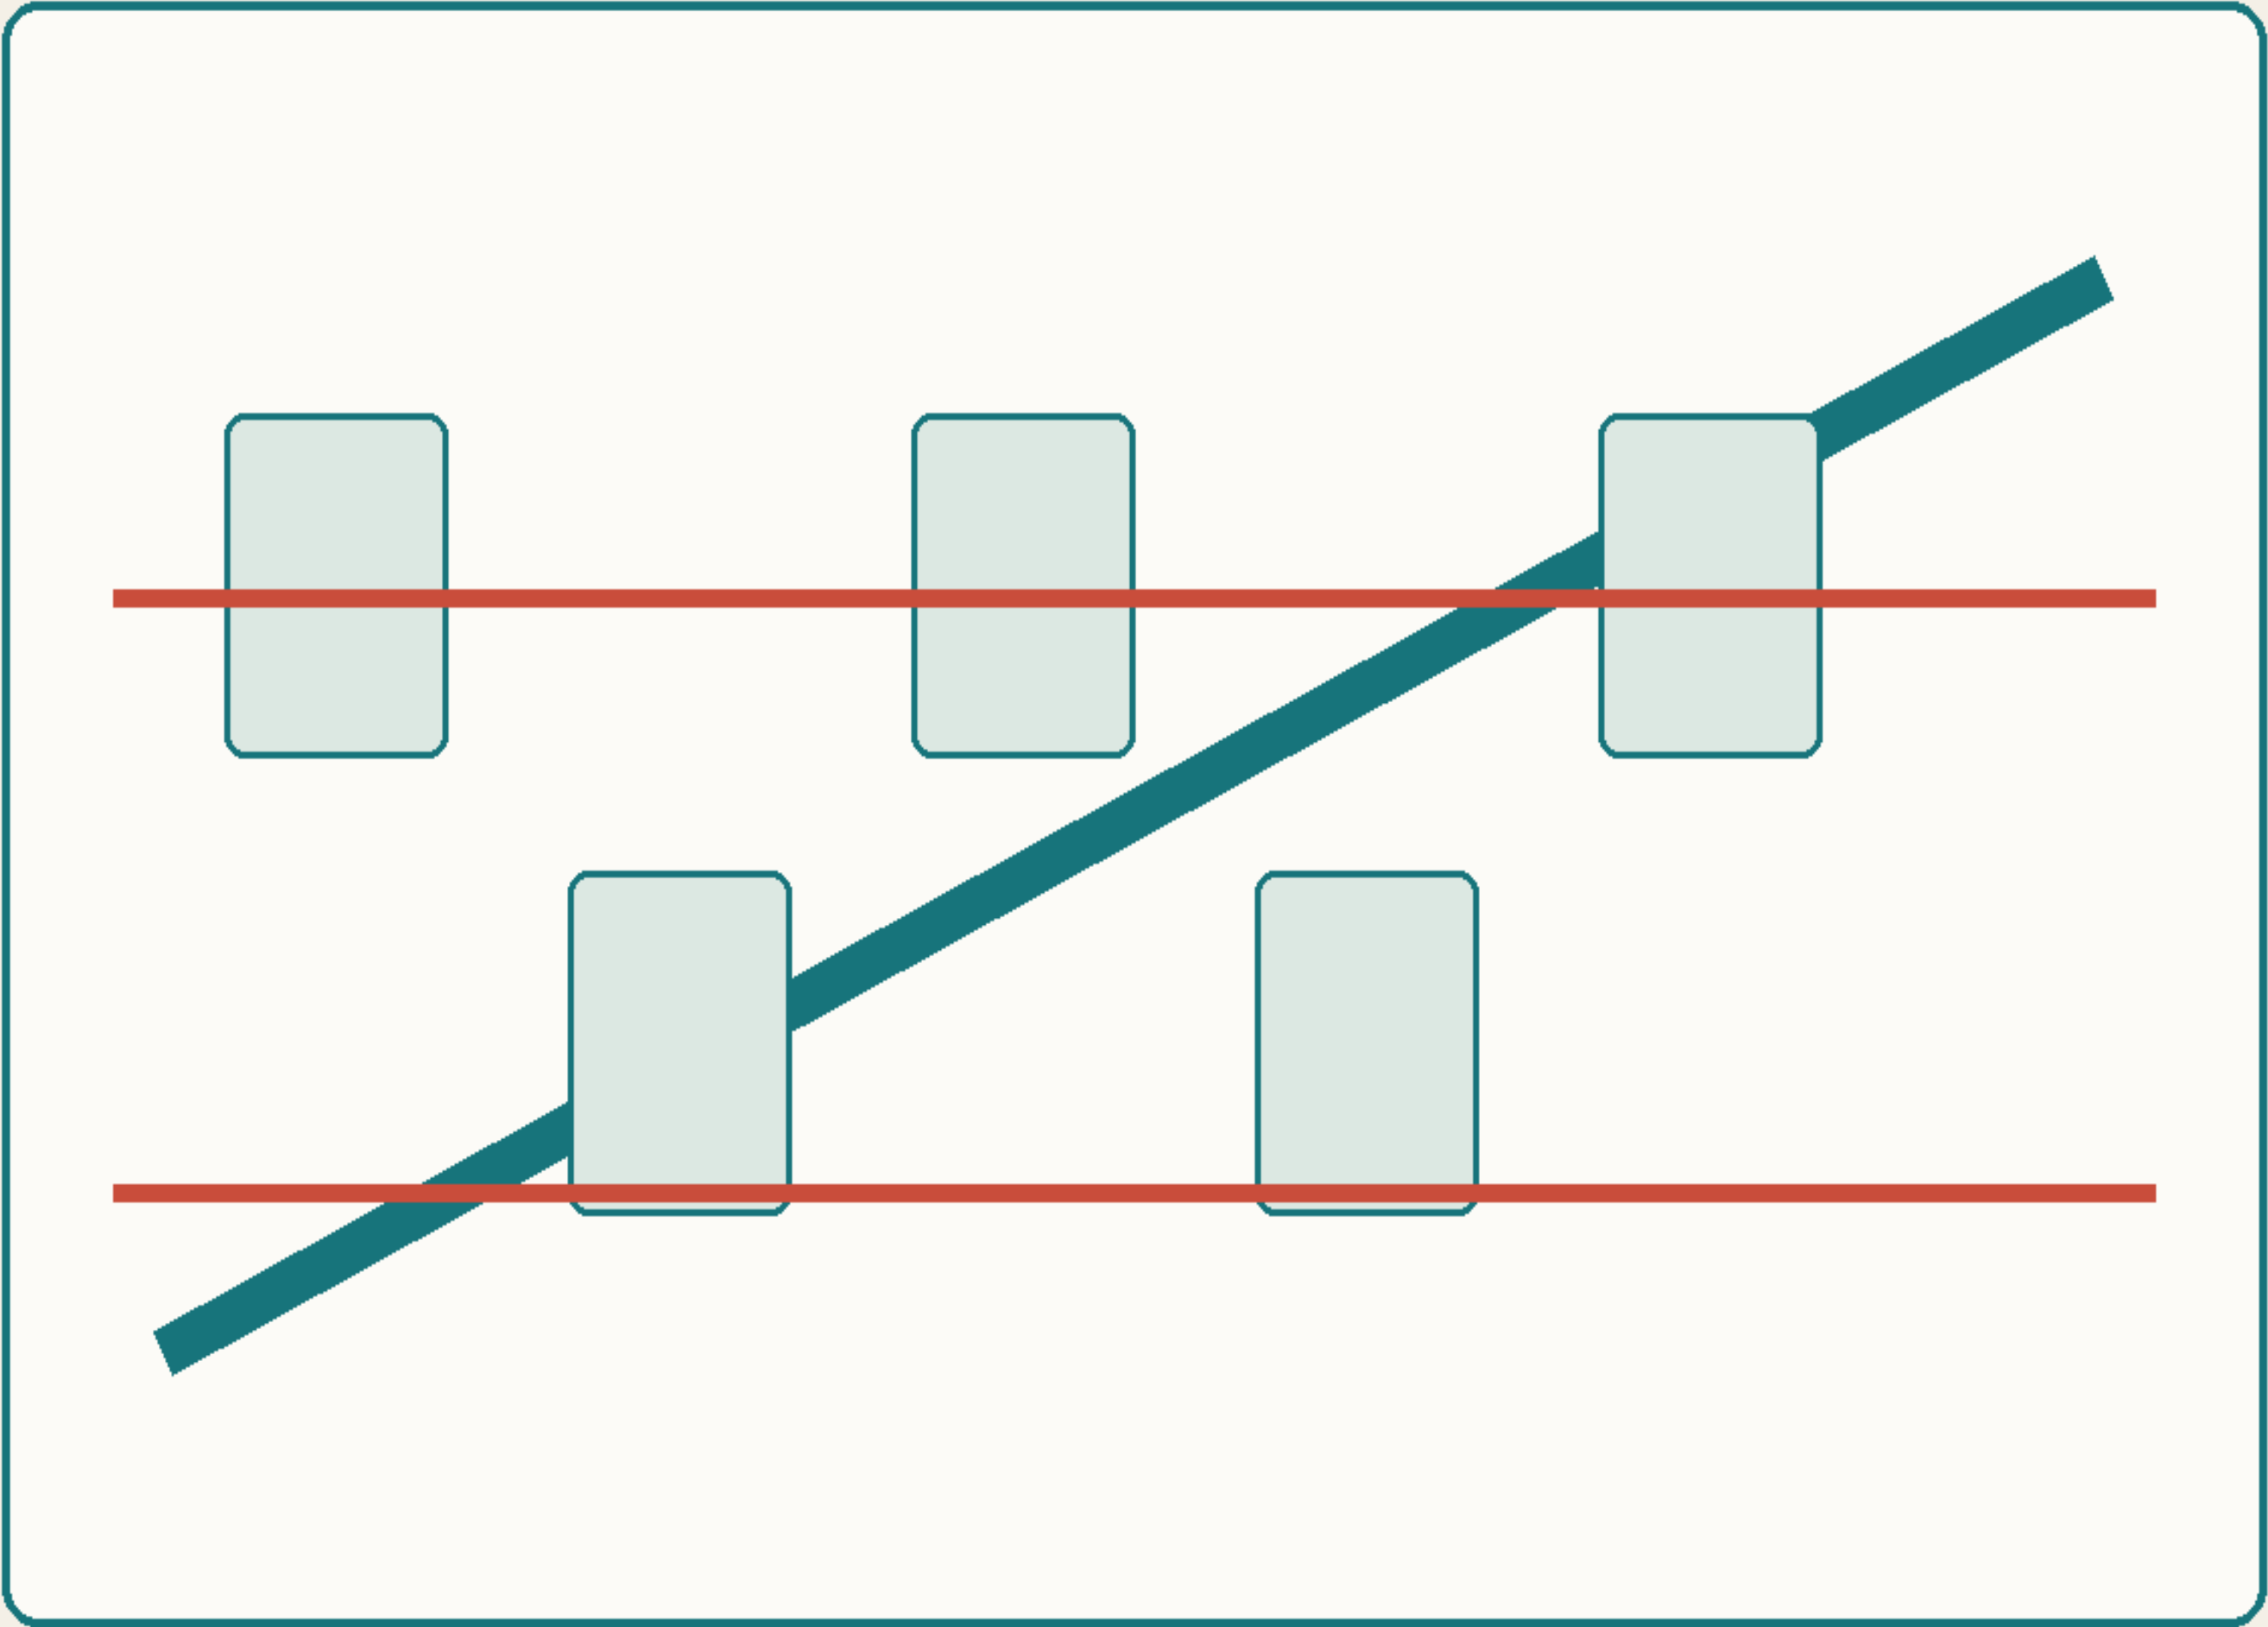

QUIET → TEST → OBSERVE → GARDEN → EXIT

Open long blocks: station–sunken forecourt–controlled test edge–garden/water–quiet exit. Separate logistics from public observation; reject blank compound walls.

BLOCK OPENINGS


ACTIVE GROUND FLOOR

SEPARATE LOGISTICS

REVERSIBLE PROTOTYPE

AI ORIGIN | NEAR-CAMPUS COURTYARDS

104.3 ha provisional

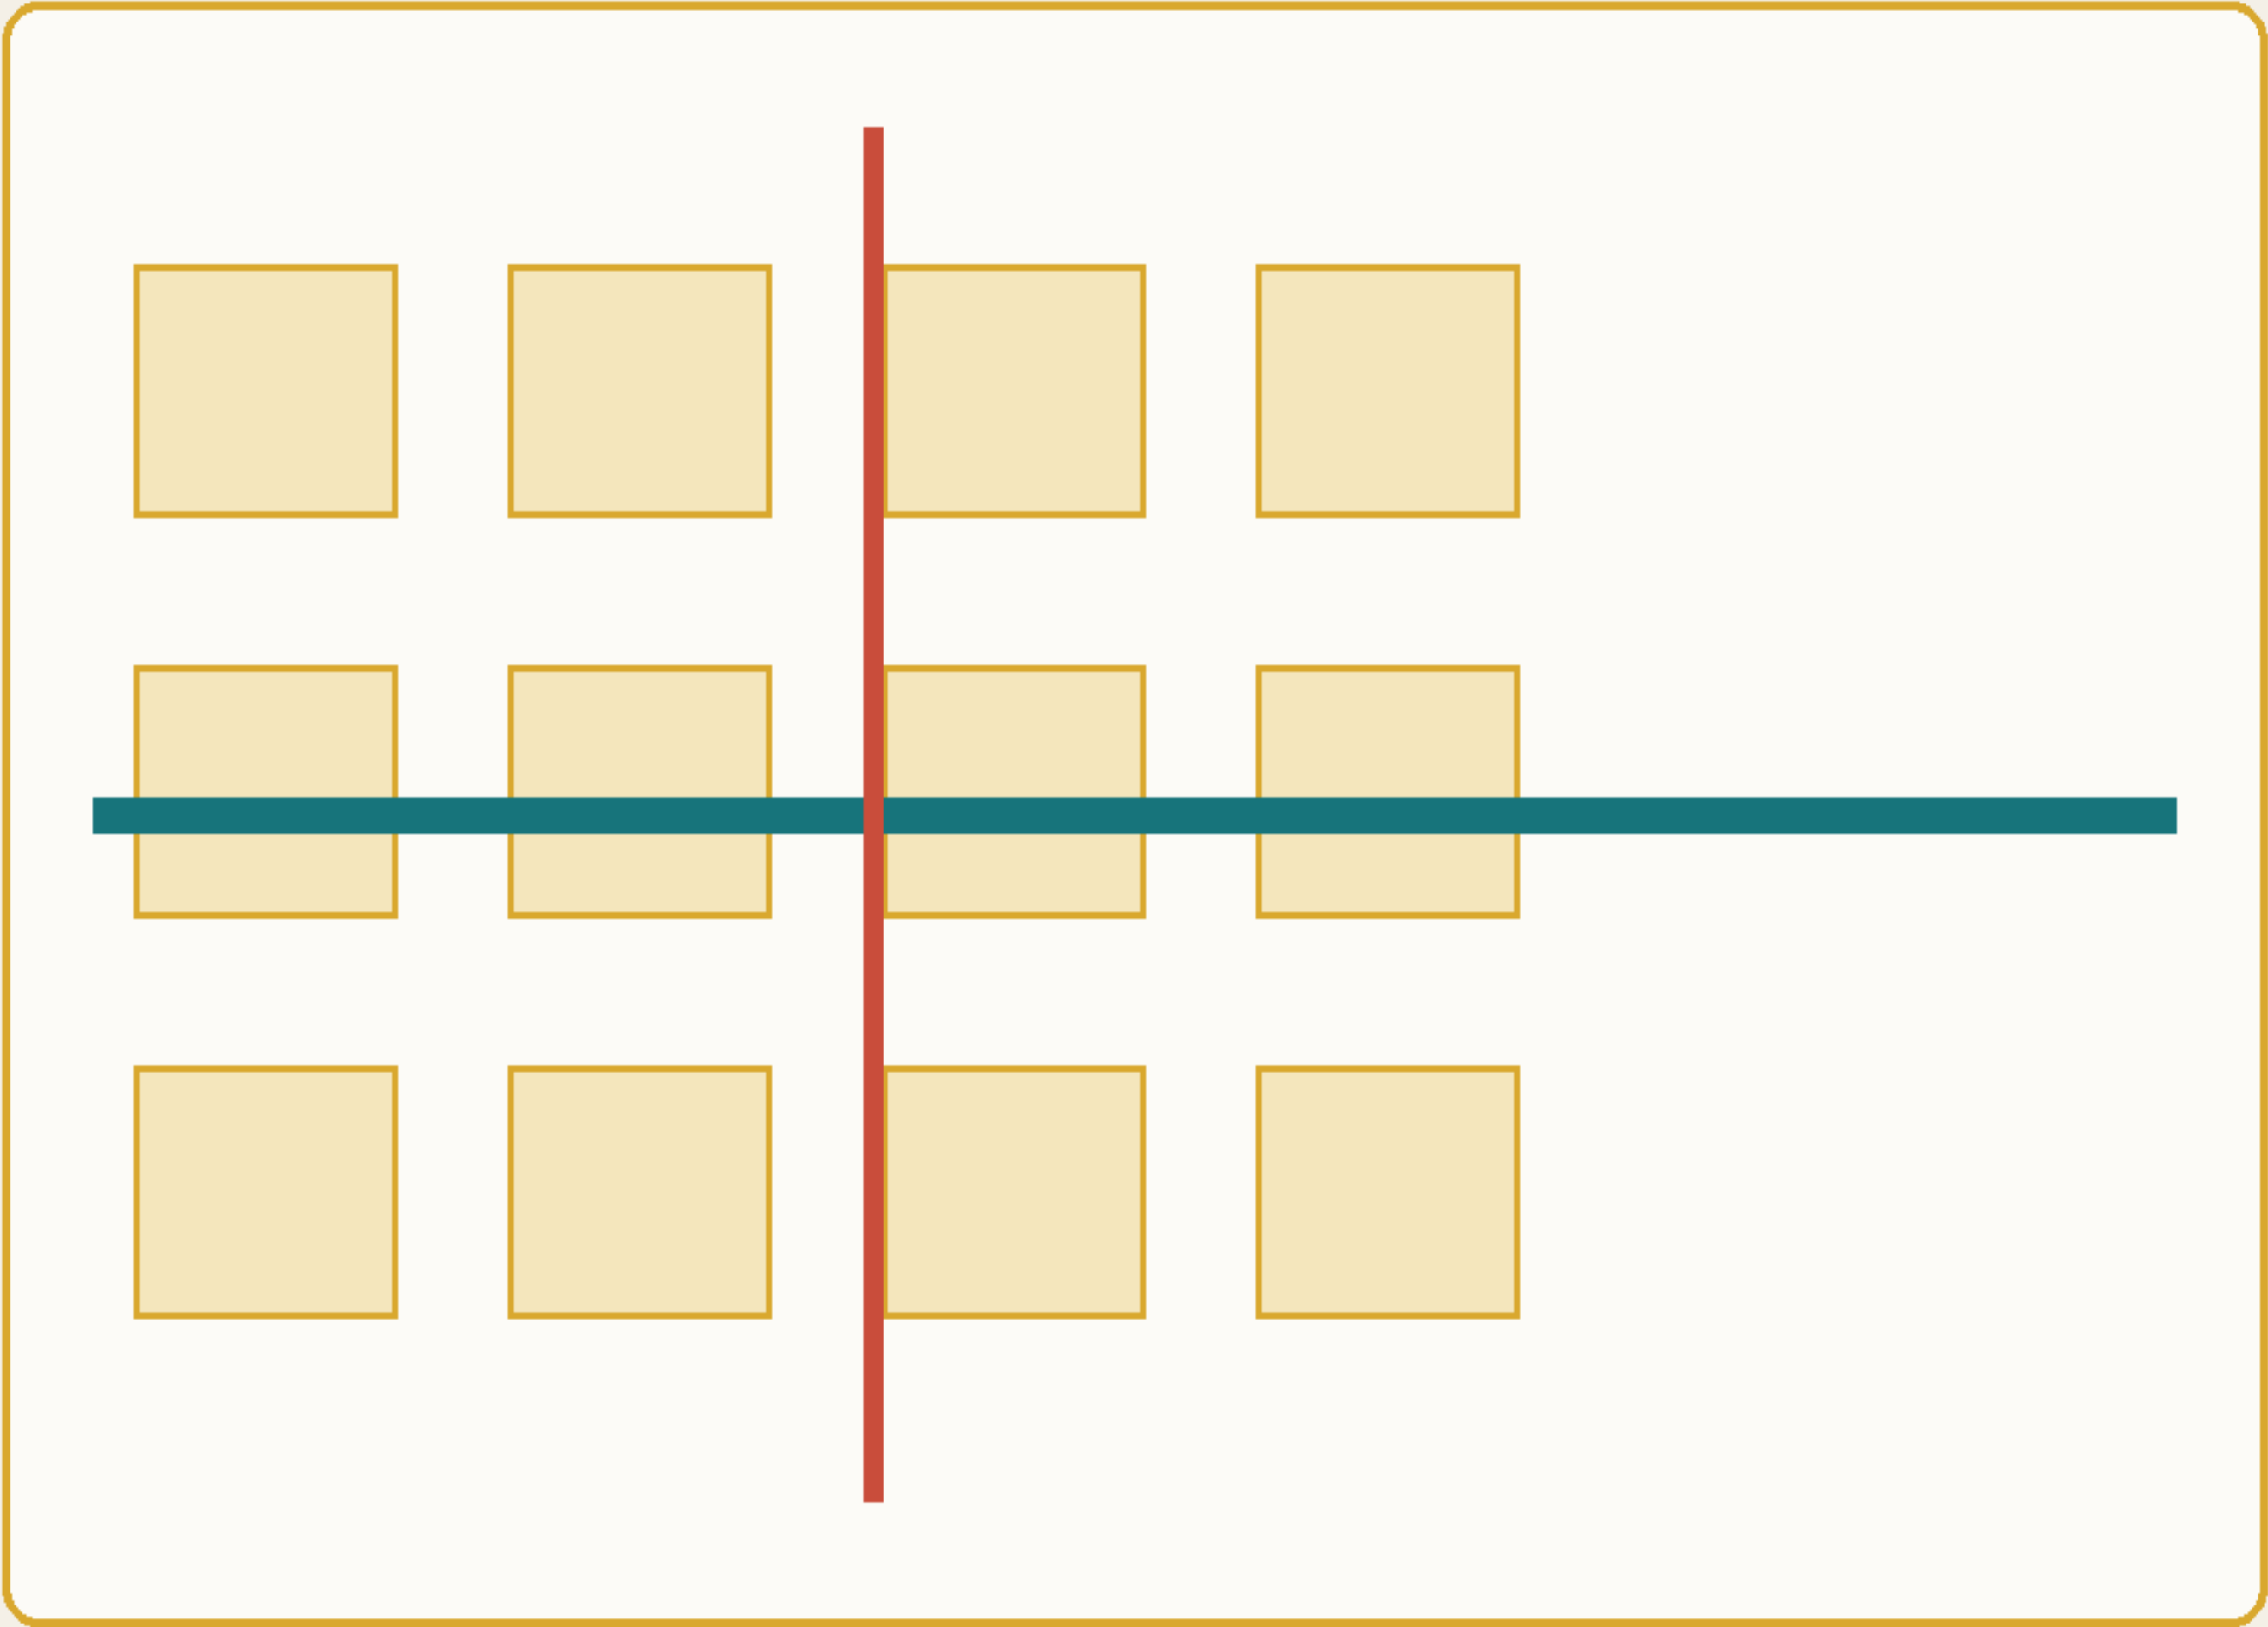

STREET → ARCADE → COURT → WORKSHOP → CAMPUS

Retain–repair–reuse the street–lane–court–workshop sequence. Daily retail, learning, care and human service precede programmed events.

BLOCK OPENINGS


ACTIVE GROUND FLOOR

SEPARATE LOGISTICS

REVERSIBLE PROTOTYPE

DAZHONGSI | STATION–CITY–HERITAGE

72.0 ha provisional

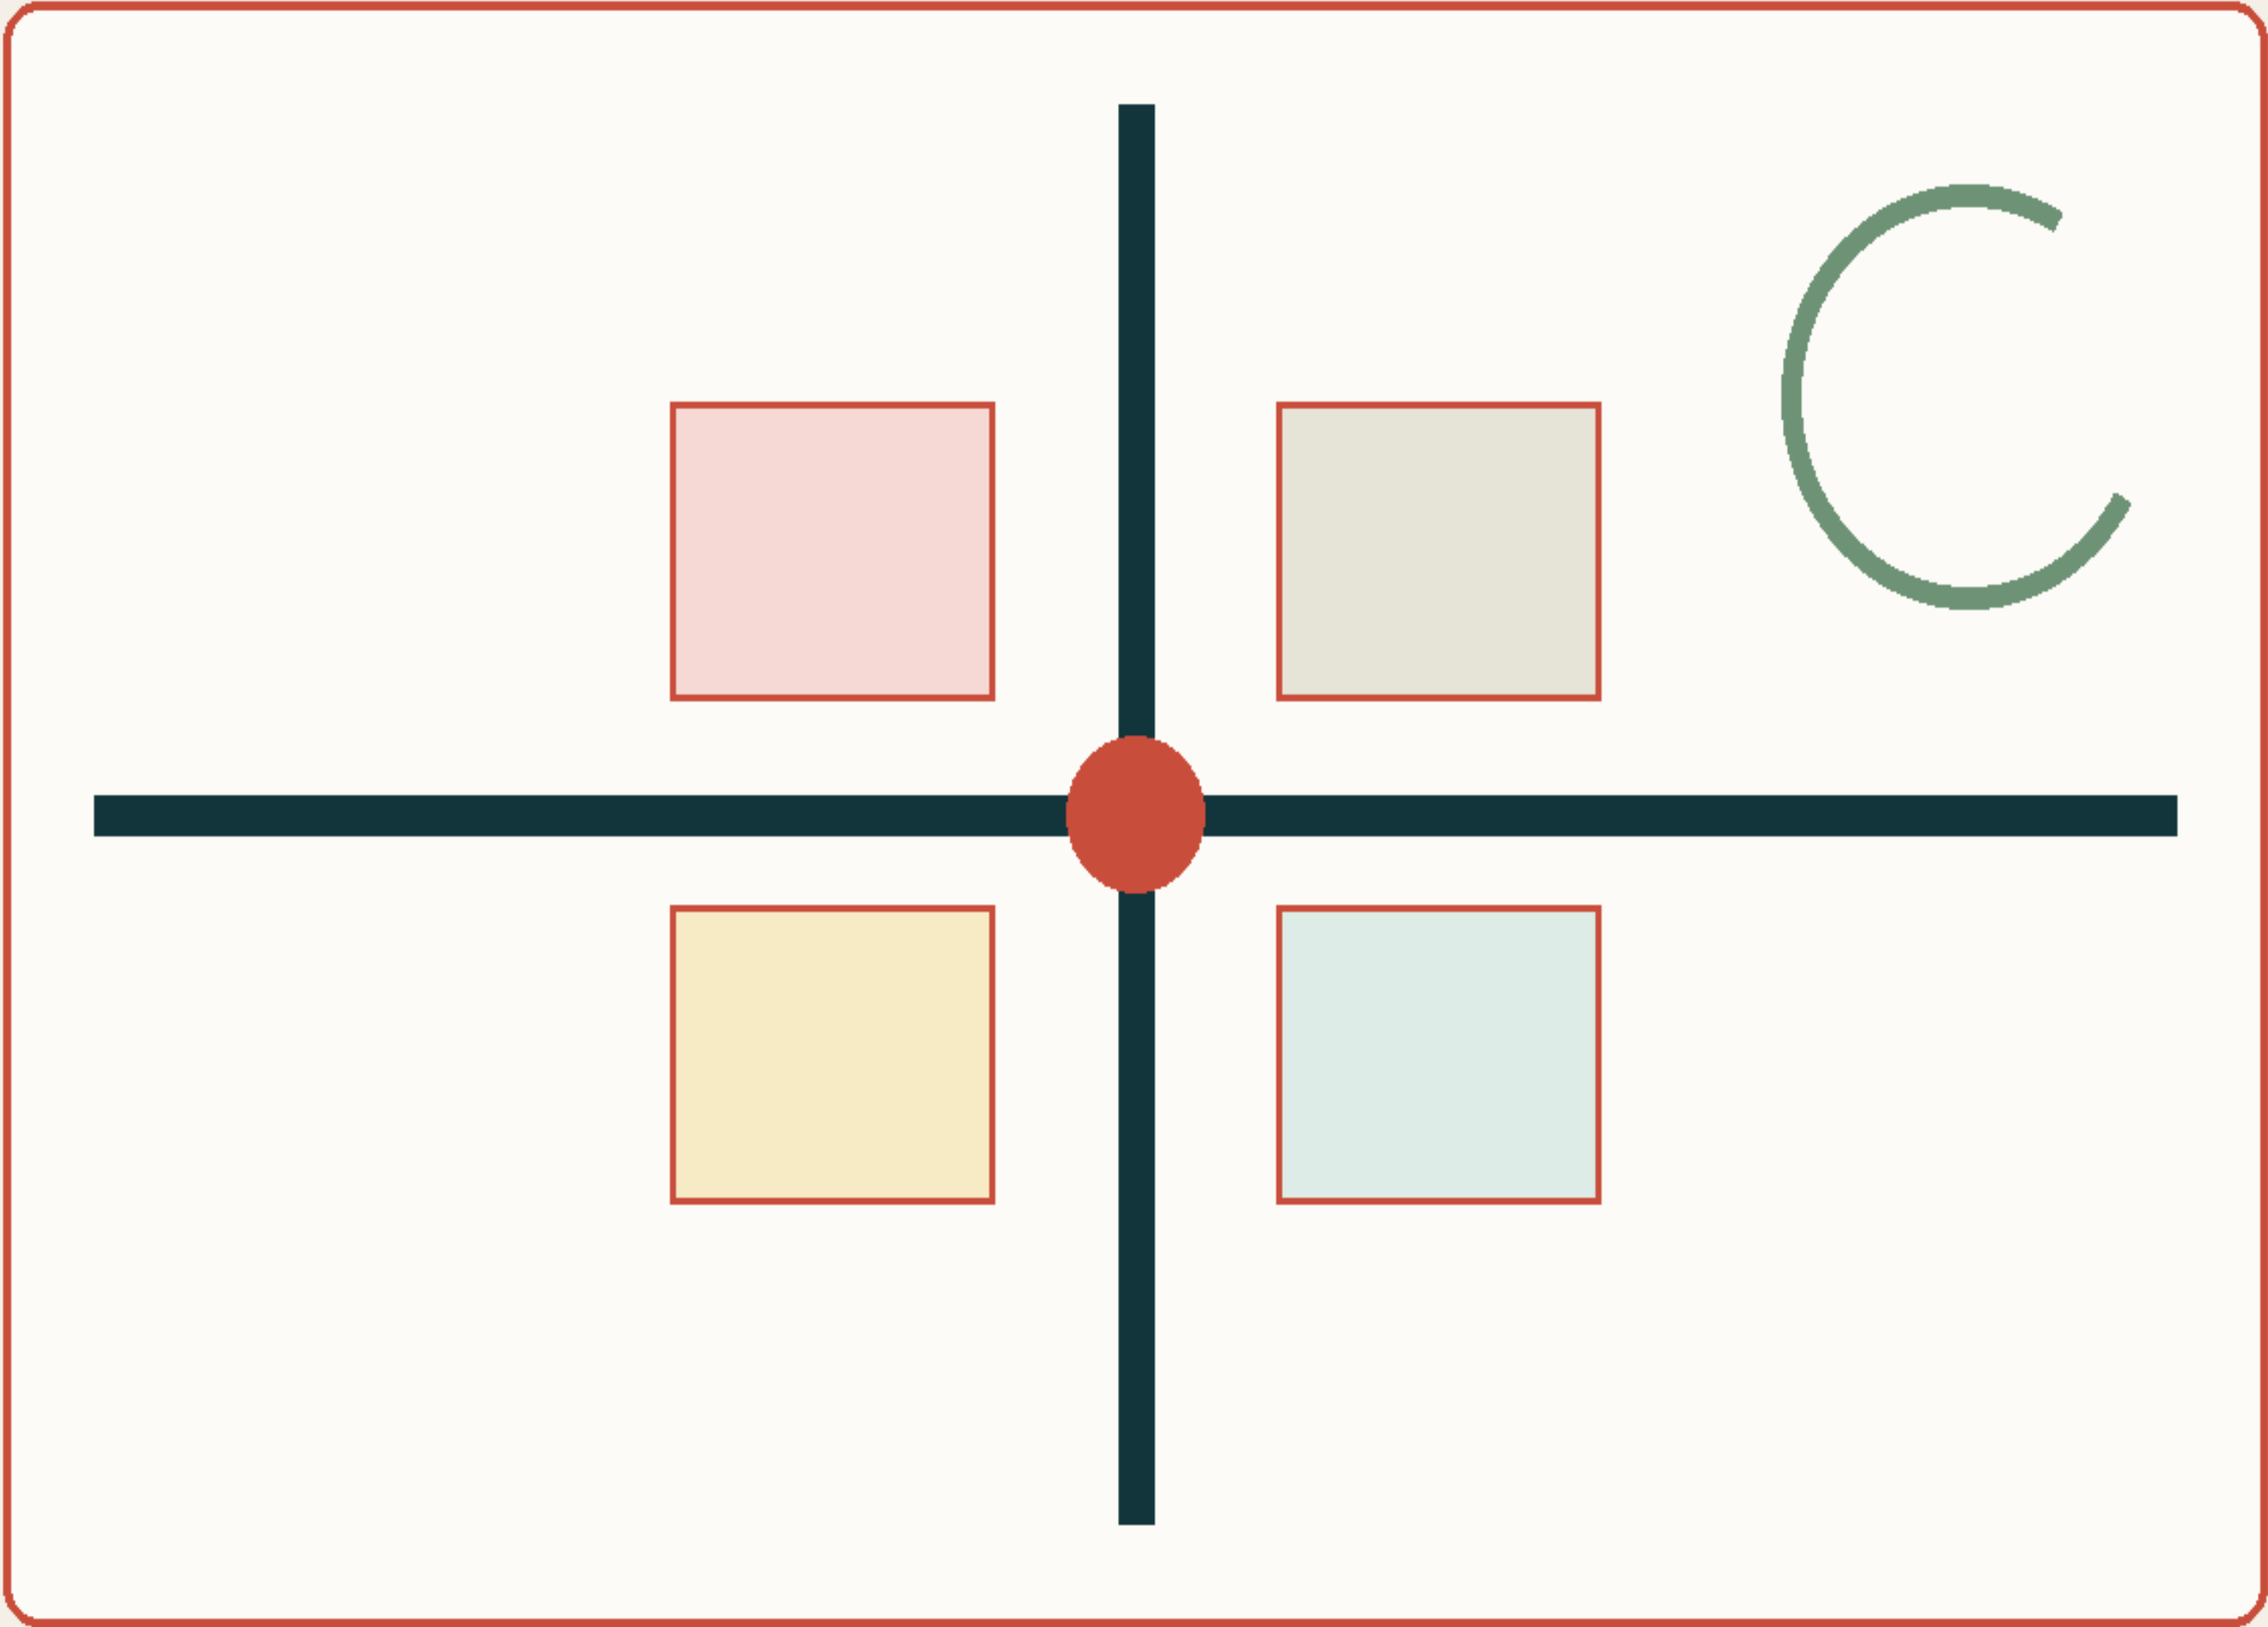

STATION → STREET → SQUARE → HALL → QUIET

Link all four station quadrants and cycle parking to active ground floors and civic-premiere space; form a quiet relationship to Juesheng Temple without inventing its control line.

BLOCK OPENINGS

ACTIVE GROUND FLOOR

SEPARATE LOGISTICS

REVERSIBLE PROTOTYPE

TURN CLASSIC METHODS INTO REQUIRED DELIVERABLES

These books are not decorative references: every method produces a reviewable drawing or control sheet.

KROPF / PANERAI

STREET-BLOCK-PLOT-BUILDING

Existing/proposed tissue matrices for all three key areas: retain, repair, open or replace.

SPACEMATRIX

FAR × GSI × OSR × LAYERS

Parcel intensity sheets only after statutory inputs arrive; no invented regulatory values.

ALLAN B. JACOBS

MEASURE THE STREET

Five existing/proposed sections: walking, cycling, traffic, shade, frontage, loading and access.


GORDON CULLEN

SERIAL VISION

One five-minute sequence per key area tests arrival, reveal, enclosure, turn, quiet and exit.


5 张必须成对的断面 / FIVE PAIRED SECTIONS

01 Xuezhiyuan-forecourt-garden/water

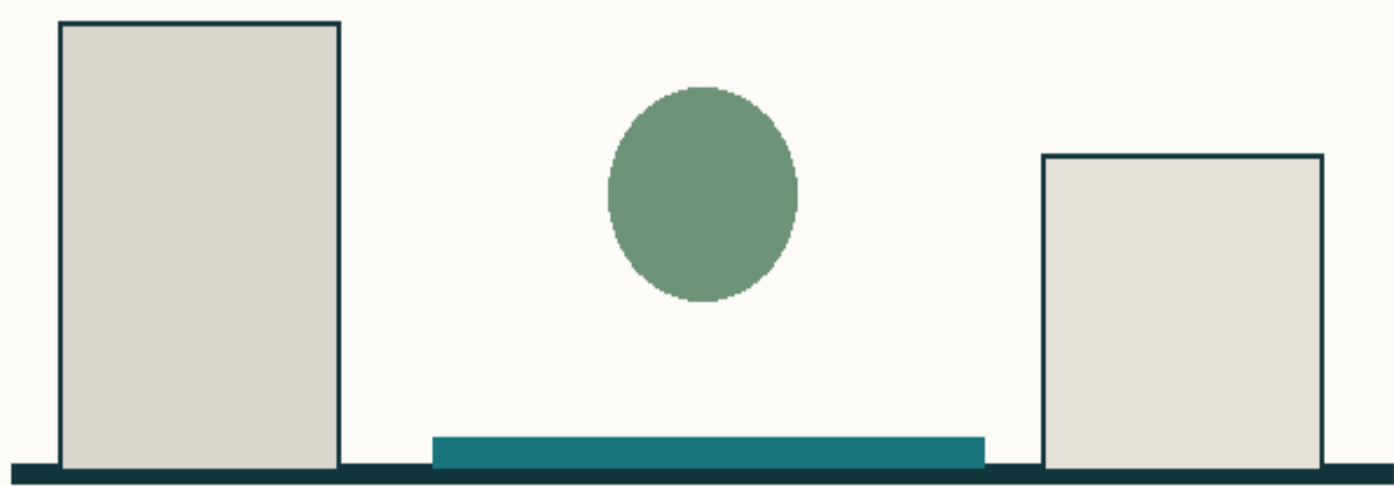


WIDTH / REDLINE TO SURVEY

02 Chengfu Rd-Origin-AI lane/campus

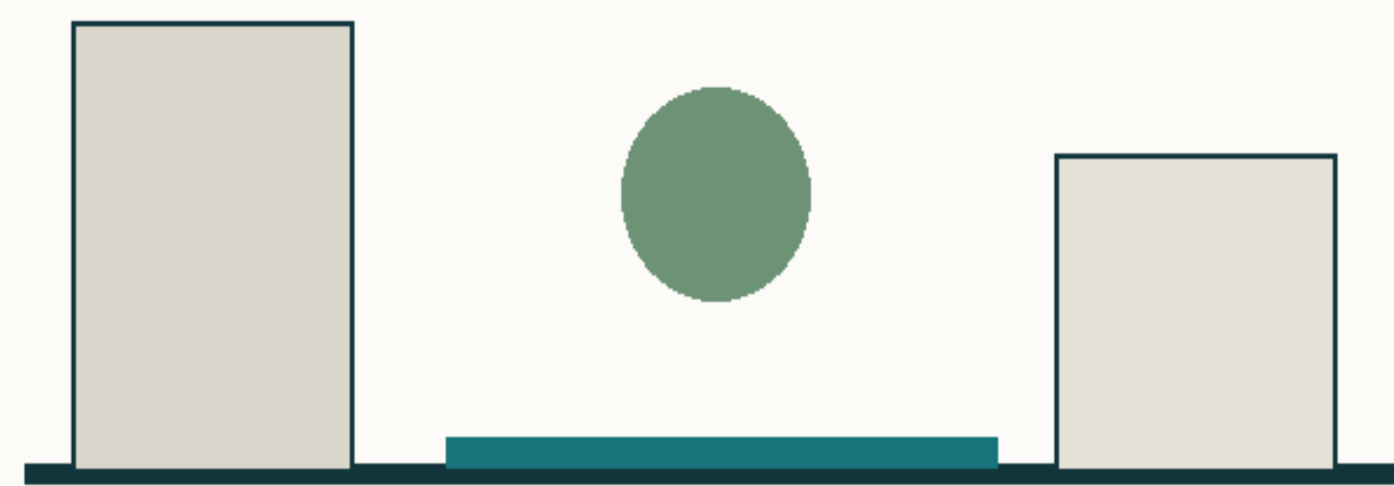


WIDTH / REDLINE TO SURVEY

03 Dazhongsi quadrants-Bluejing/Fangheng

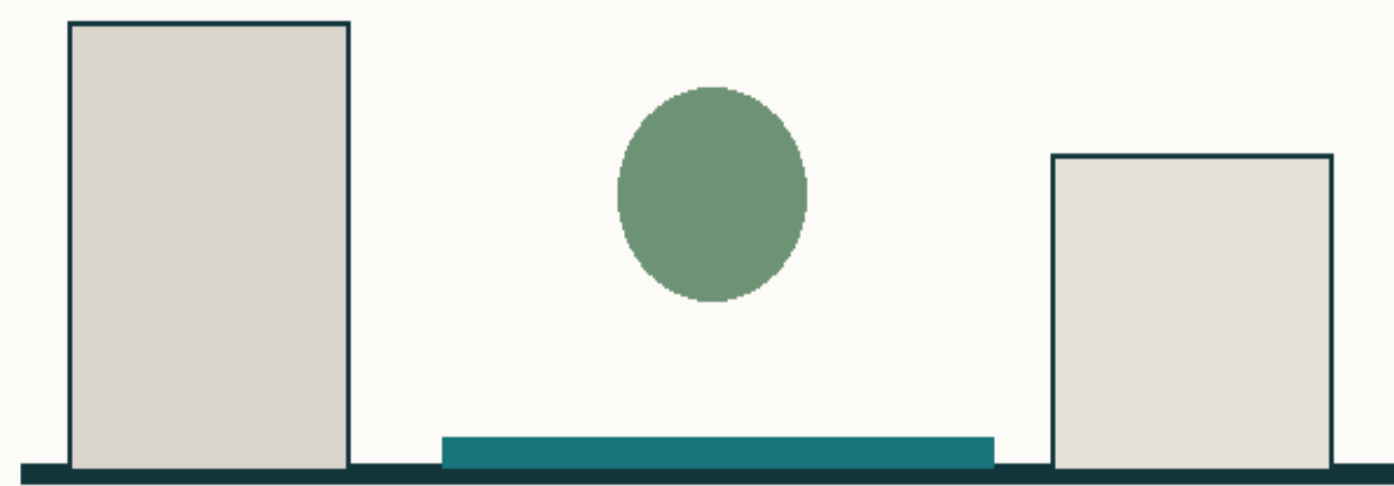


WIDTH / REDLINE TO SURVEY

04 Jing-Zhang spine-east/west stitch

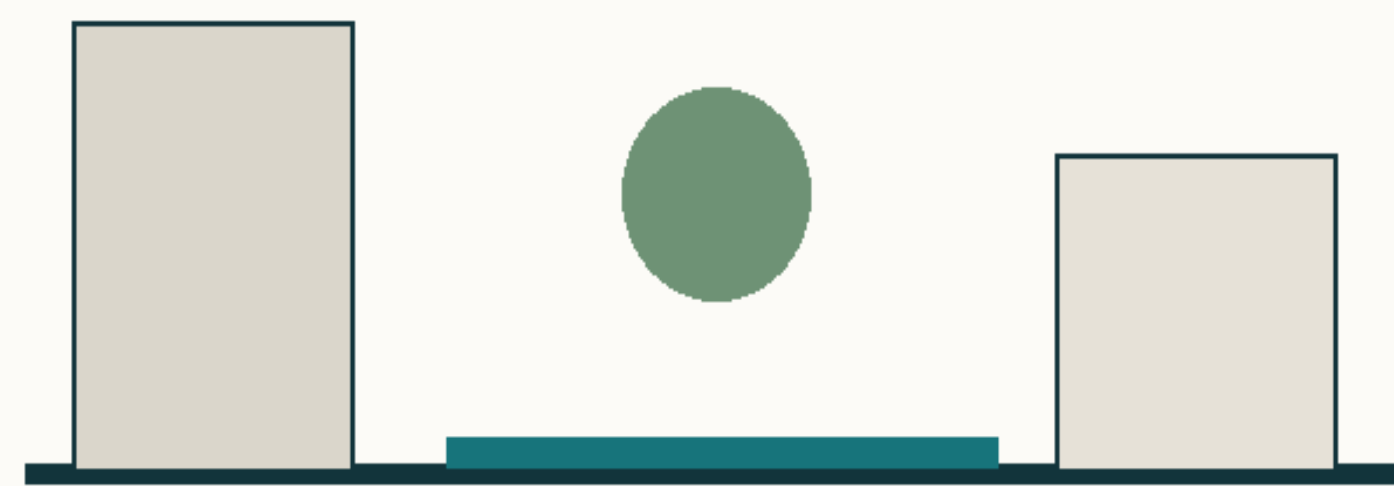

WIDTH / REDLINE TO SURVEY

05 Qinghe/Xiaoyue blue-green edge

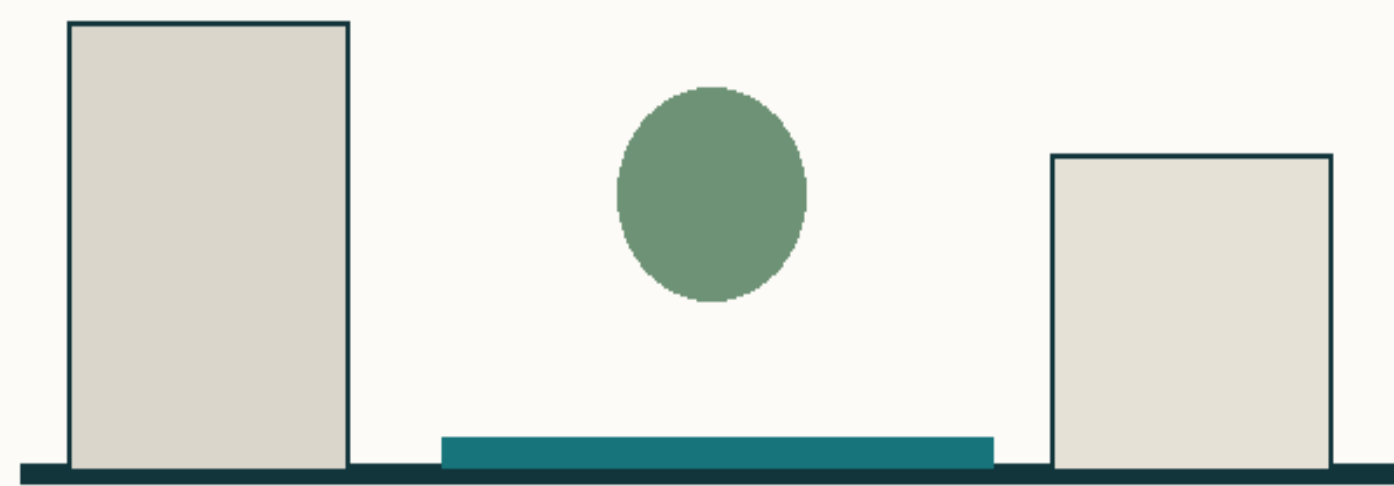

WIDTH / REDLINE TO SURVEY

SCORING COMES FROM CLOSED CONTROL LOOPS, NOT MORE WORDS

Separate official facts, design commitments and acceptance evidence. Unknown is a managed status with a data request, professional owner and hold point.

CONTROL	OFFICIAL	DESIGN COMMITMENT	ACCEPTANCE EVIDENCE	GATE
Boundary / parcel	UNKNOWN	Do not cross formal redlines	Official polygons + parcel IDs	G0
Land-use compatibility	UNKNOWN	Cultural overlay never replaces statutory use	Approved use and compatibility table	G1
GFA / FAR / height / GSI	UNKNOWN	No invented concept values	Approved values + parcel recalc	G1
Public facilities	UNKNOWN	Daily services cannot be displaced by events	Type / scale / location / handover	G1
Road / public passage	UNKNOWN	Five sections + nine stitches	Position / width / opening mechanism	G2
Rail / heritage	UNKNOWN	Four quadrants + quiet relationship	Formal polygons + professional opinions	G3
Fire / sun / wind / heat / noise	UNKNOWN	Technical proof precedes imagery	Current-standard professional reports	G3
Access / municipal	UNKNOWN	Field tasks + offline baseline	Field acceptance + capacity confirmation	G3
Form / fifth facade	UNKNOWN	Block-plot-building interface controls	Control drawings + building review	G2

G0

DATA FREEZE

SOURCE / CRS / RIGHTS

G1

STATUTORY

ZERO CRITICAL UNKNOWN

G2

SPATIAL

100% BUILDINGS + SECTIONS

G3

TECHNICAL

EIGHT TECHNICAL CHECKS

G4

AS-BUILT + USE

HANDOVER + 12-MONTH REVIEW

CONSTRUCTION ISSUE CONDITION: every applicable statutory field has an official value, source, approval and effective date; construction-critical unknowns = 0.