


三层范围：统筹研究范围约 43.6 km²（区域战略与协同）、总体设计范围约 11.4 km²（城市更新与控规深度设计）、重点区域范围约 368.4 ha（三座档案站详细设计）。三层不是孤立图纸：研究层回答一带为什么成立，设计层落为可复算用地与项目，重点区验证可实施性。

京张档案带 · 总体概念总览

记忆主脊 · 三座档案站 · 两翼记录器

中关村科技服务翼（要素记录翼）

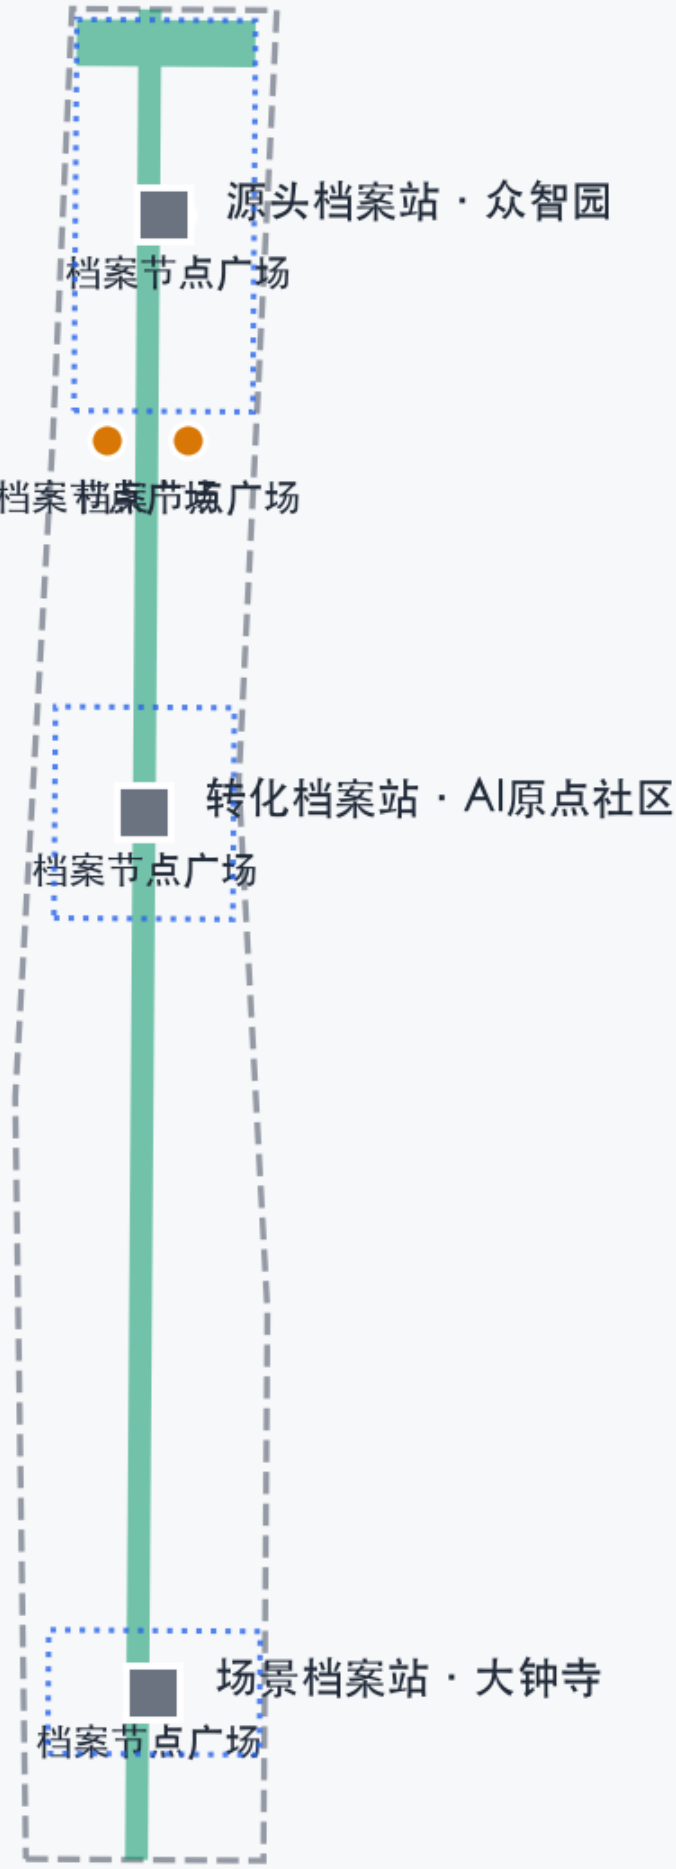

小月河场景赋能翼（场景记录翼）

风险与合规：provisional 边界整包重算；控规/红线/权属/文保缺口列入假设；档案设施不采集个人轨迹；荣誉人类终审；不声称官方批准与实施承诺。

边界为 provisional 临时边界，非官方红线；官方数据发布后整体复算

把开放共创写进城市档案：贡献即入档、服务即留档、纠错即补档、荣誉即档案

三层范围


- 统筹研究范围 43.6 km²
- 总体设计范围 11.4 km²
- 重点区域范围 368.4 ha

Zhongzhiyuan / Origin / Dazhongsi

空间结构：一带（记忆主脊）· 三站（源头/转化/场景档案站）· 两翼（中关村要素记录翼、小月河场景记录翼）· 多点（留名墙/荣誉年鉴/提交碑）· 双网（蓝绿慢行网与档案检索网）。城市更新采用档案化更新单元：档案锚点+主脊缝合+低扰动微更新。

京张档案带 · 用地结构与空间结构

科研 · 教育 · 商业 · 居住 · 蓝绿 · 留白

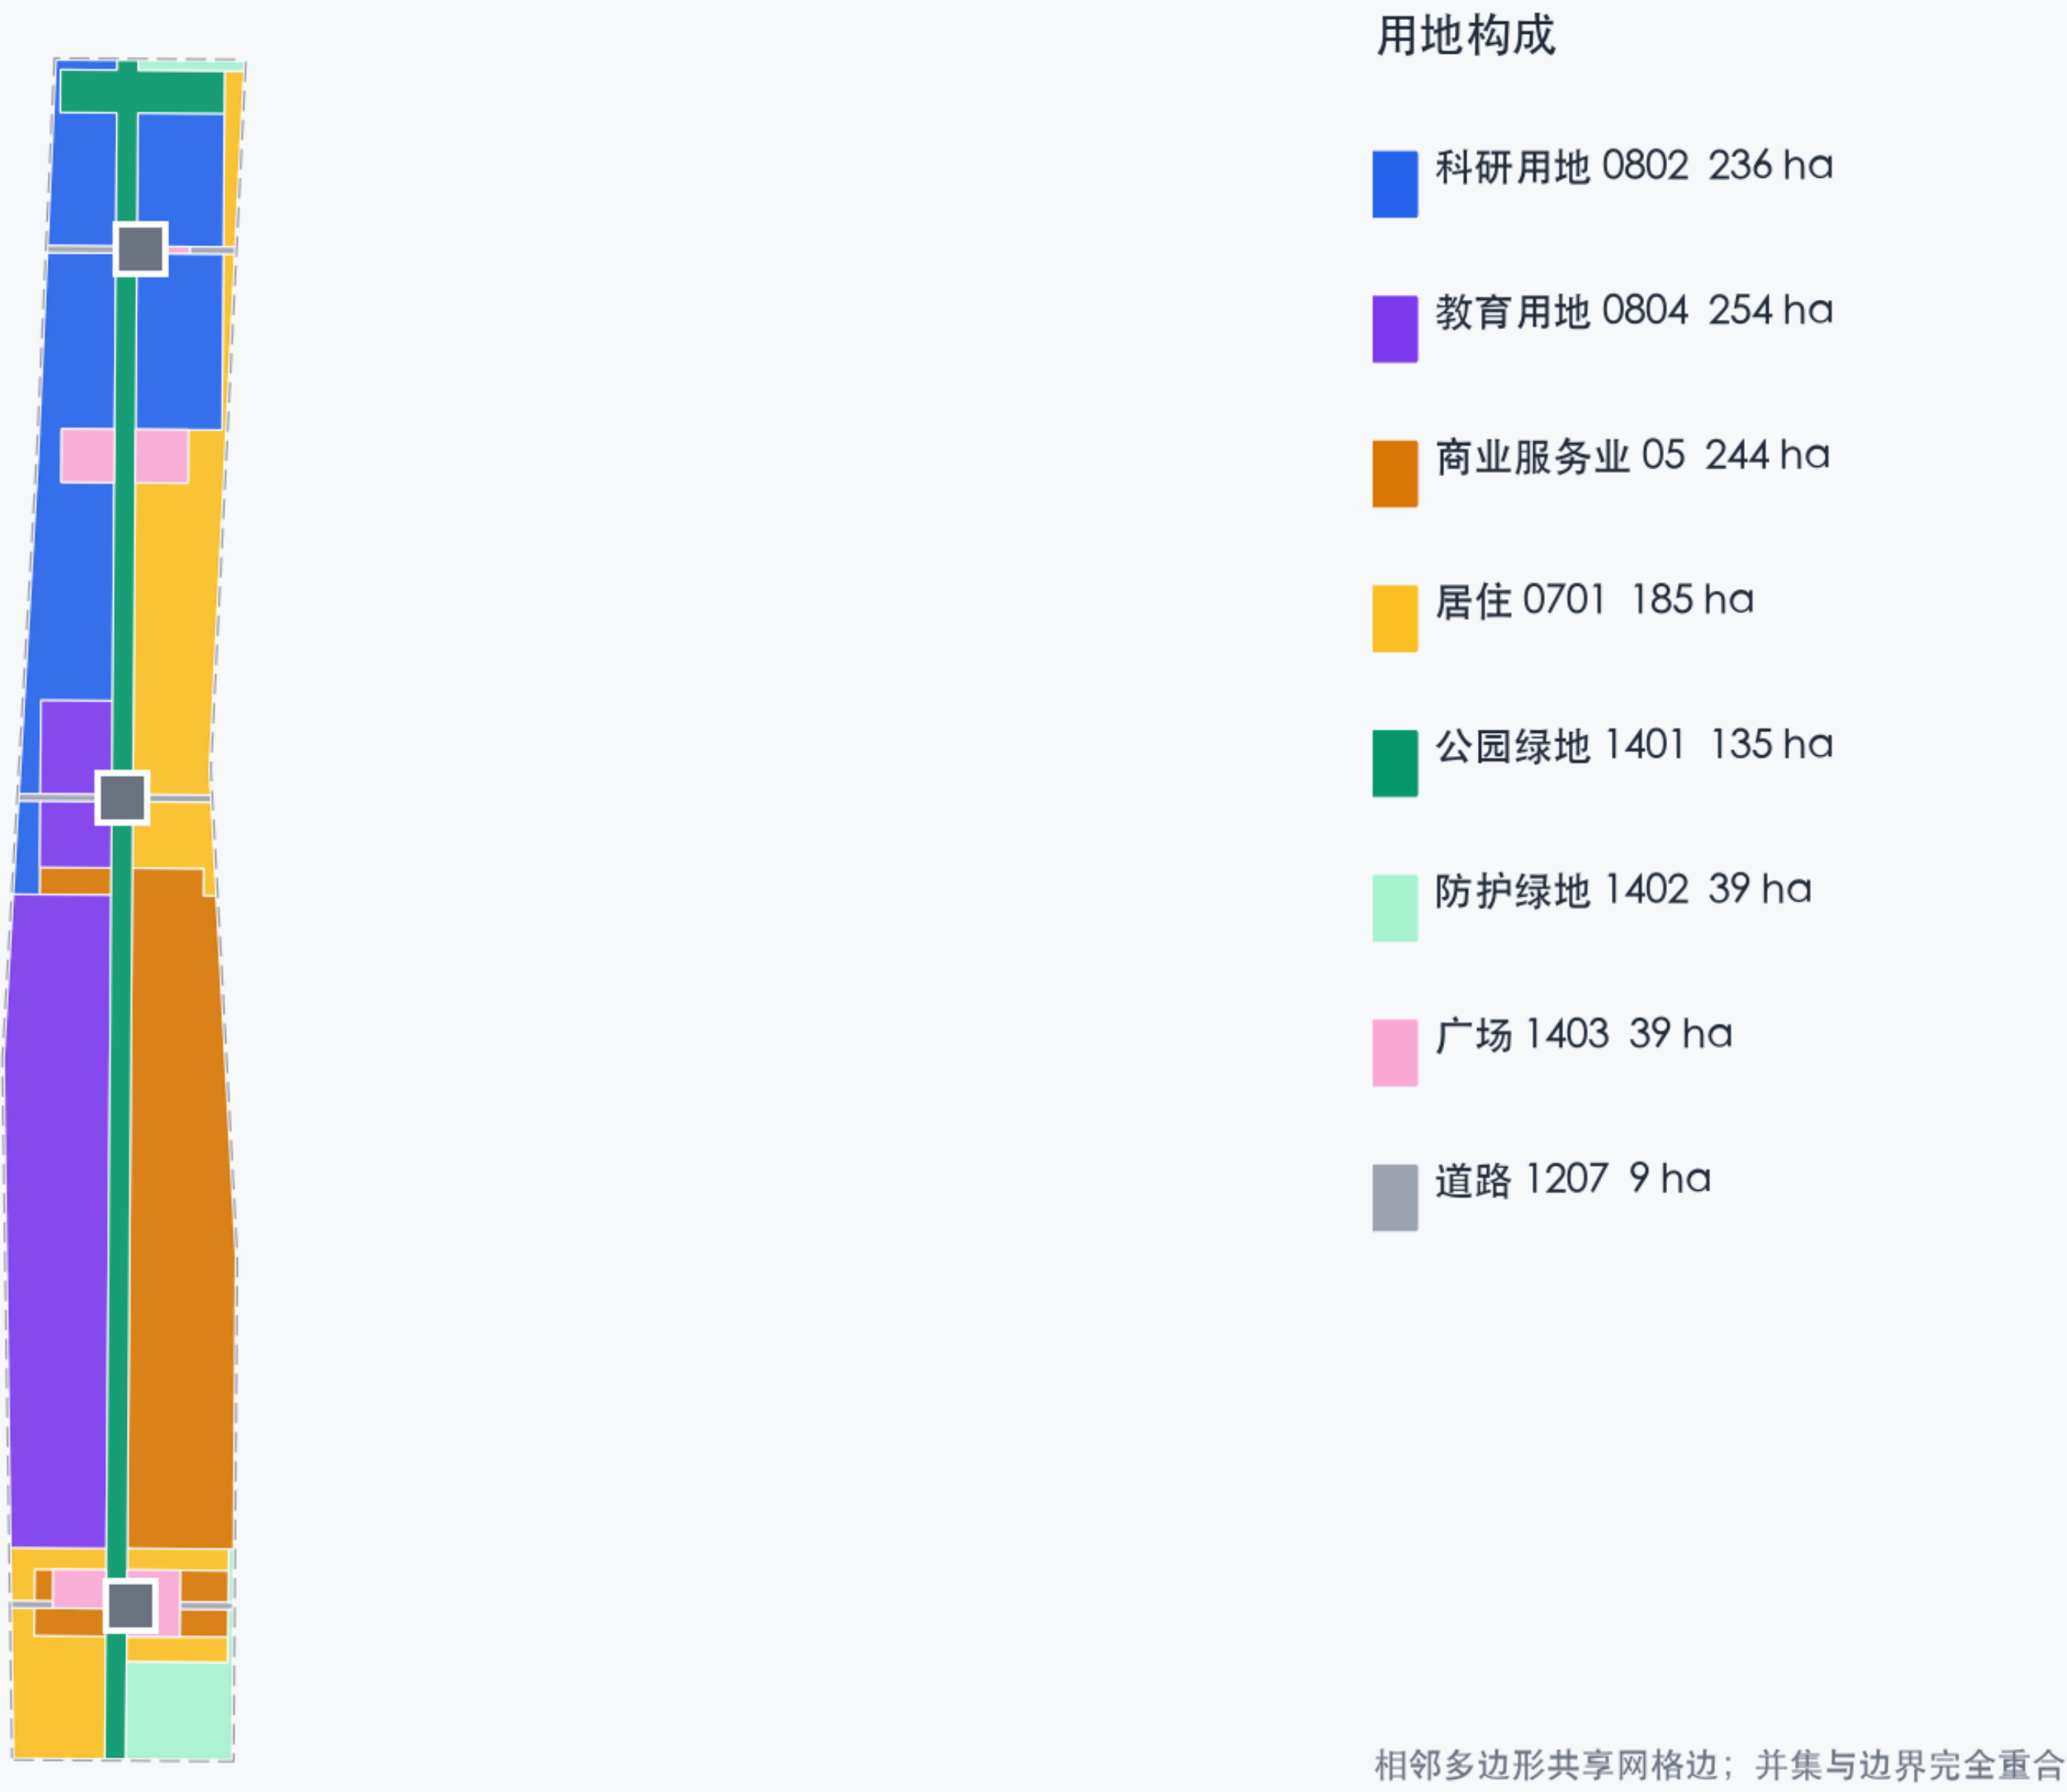

风险与合规：provisional 边界整包重算；控规/红线/权属/文保缺口列入假设；档案设施不采集个人轨迹；荣誉人类终审；不声称官方批准与实施承诺。


边界为 provisional 临时边界，非官方红线；官方数据发布后整体复算

13

项概念更新项目分三期：一期主脊缝合与档案锚点、二期测试街区与数据平台、三期两座档案站；每项带前置条件、成本量级、验收指标与回滚触发器（安全/隐私/文保/生态/经济）。

京张档案带 · 交通慢行与蓝绿公共空间

主脊绿道 · 三条缝合带 · 档案节点

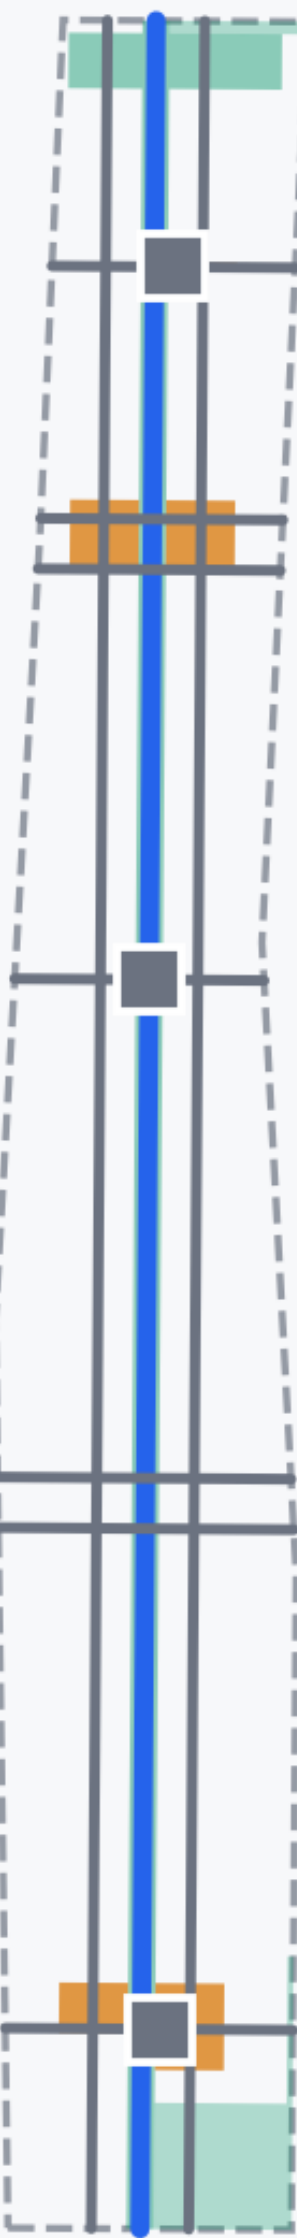

交通与蓝绿

- 主脊绿道 (greenway)

1 条 南北贯通

- 东西缝合带 (branch)

3 条 对应三座档案站

- 道路中心线总长

37.3 km

- 绿地面积 / 占比

174 ha / 15.23%

- 公共空间面积

394801 m²

- 轨道接驳

大钟寺 / 五道口 / 清华东路西口（概念）

道路红线/轨道线位为概念组织，工程结论待官方资料补齐


风险与合规：provisional 边界整包重算；控规/红线/权属/文保缺口列入假设；档案设施不采集个人轨迹；荣誉人类终审；不声称官方批准与实施承诺。

边界为 provisional 临时边界，非官方红线；官方数据发布后整体复算

三座档案站：源头站 · 众智园（全栈自主创新，模型评测与标准研讨场）；转化站 · AI原点社区（成果转化，开源提交碑与荣誉年鉴）；场景站 · 大钟寺（智能原生新业态，四象限步行连通）。三区全部为方向性概念设计。

京张档案带 · 三座档案站重点设计

源头 · 转化 · 场景

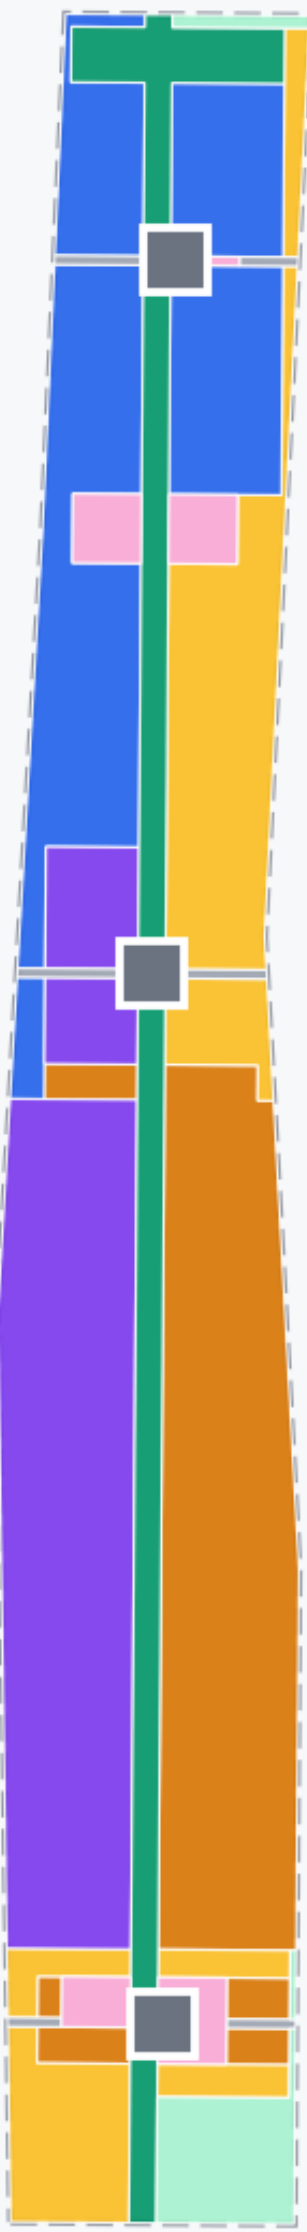

源 SOURCE	众智园 · 全栈自主创新
档案：算力 / 模型 / 标准 / 测试档案	
动作：模型评测与标准研讨场（测试验证）	

转 TRANSFORM	AI原点社区 · 成果转化
档案：成果 / 人才 / 企业档案	
动作：开源提交碑 · 荣誉年鉴 · 原点会客厅	

场 SCENARIO	大钟寺 · 智能原生新业态
档案：场景 / 运营 / 纠错档案	
动作：四象限步行连通 · 智能终端体验街	

风险与合规：provisional 边界整包重算；控规/红线/权属/文保缺口列入假设；档案设施不采集个人轨迹；荣誉人类终审；不声称官方批准与实施承诺。

三区空间结论为概念建议，官方 polygon 到位前保持方向性表达

边界为 provisional 临时边界，非官方红线；官方数据发布后整体复算

空间复算指标（EPSG:4548）：总体范围 11,412,825 m²、绿地率 15.2%、公共空间占比 3.46%、建筑基底 89,569 m²、道路 37.3 km。法定管控指标（容积率/高度/密度/退线）待正式数据补齐；运营绩效指标只定义口径。

京张档案带 · 指标复算与证据

EPSG:4548 复算 · 指标三分类

空间复算指标（status=known）

总体设计范围 11,412,825 [data-metric=site_area_sqm]	绿地率 0.1523 [data-metric=green_ratio]	公共空间占比 0.03459 [data-metric=public_space_ratio]
建筑基底面积 89,569 [data-metric=building_footprint_area_sqm]	道路中心线总长 37,308 [data-metric=road_centerline_total_length_m]	重点区数量 3 [data-metric=key_area_count]

Sources & state

- OFFICIAL-ANNOUNCEMENT (formal)
- AGENT-TASKBOOK (formal)
- SITE-PACKAGE / SOURCE-REGISTRY
- PROVISIONAL-BOUNDARIES (provisional_only)
- 本地标准快照 ×5 (formal)

自检状态

Spatial review: PASS

Professional evidence: PASS

Visual packaging: PASS

Deterministic validation: PASS

法定管控指标（FAR/高度/密度/退线）→ 待正式数据补齐，不填伪值

运营绩效指标（档案条目/留名/纠错回应率）→ 只定义口径，不填伪值

风险与合规：provisional 边界整包重算；控规/红线/权属/文保缺口列入假设；档案设施不采集个人轨迹；荣誉人类终审；不声称官方批准与实施承诺。

边界为 provisional 临时边界，非官方红线；官方数据发布后整体复算