



Key areas

Detailed design of the three key areas (comprehensive implementation-plan-depth concept)



Zhongzhiyuan AI Acceleration Zone

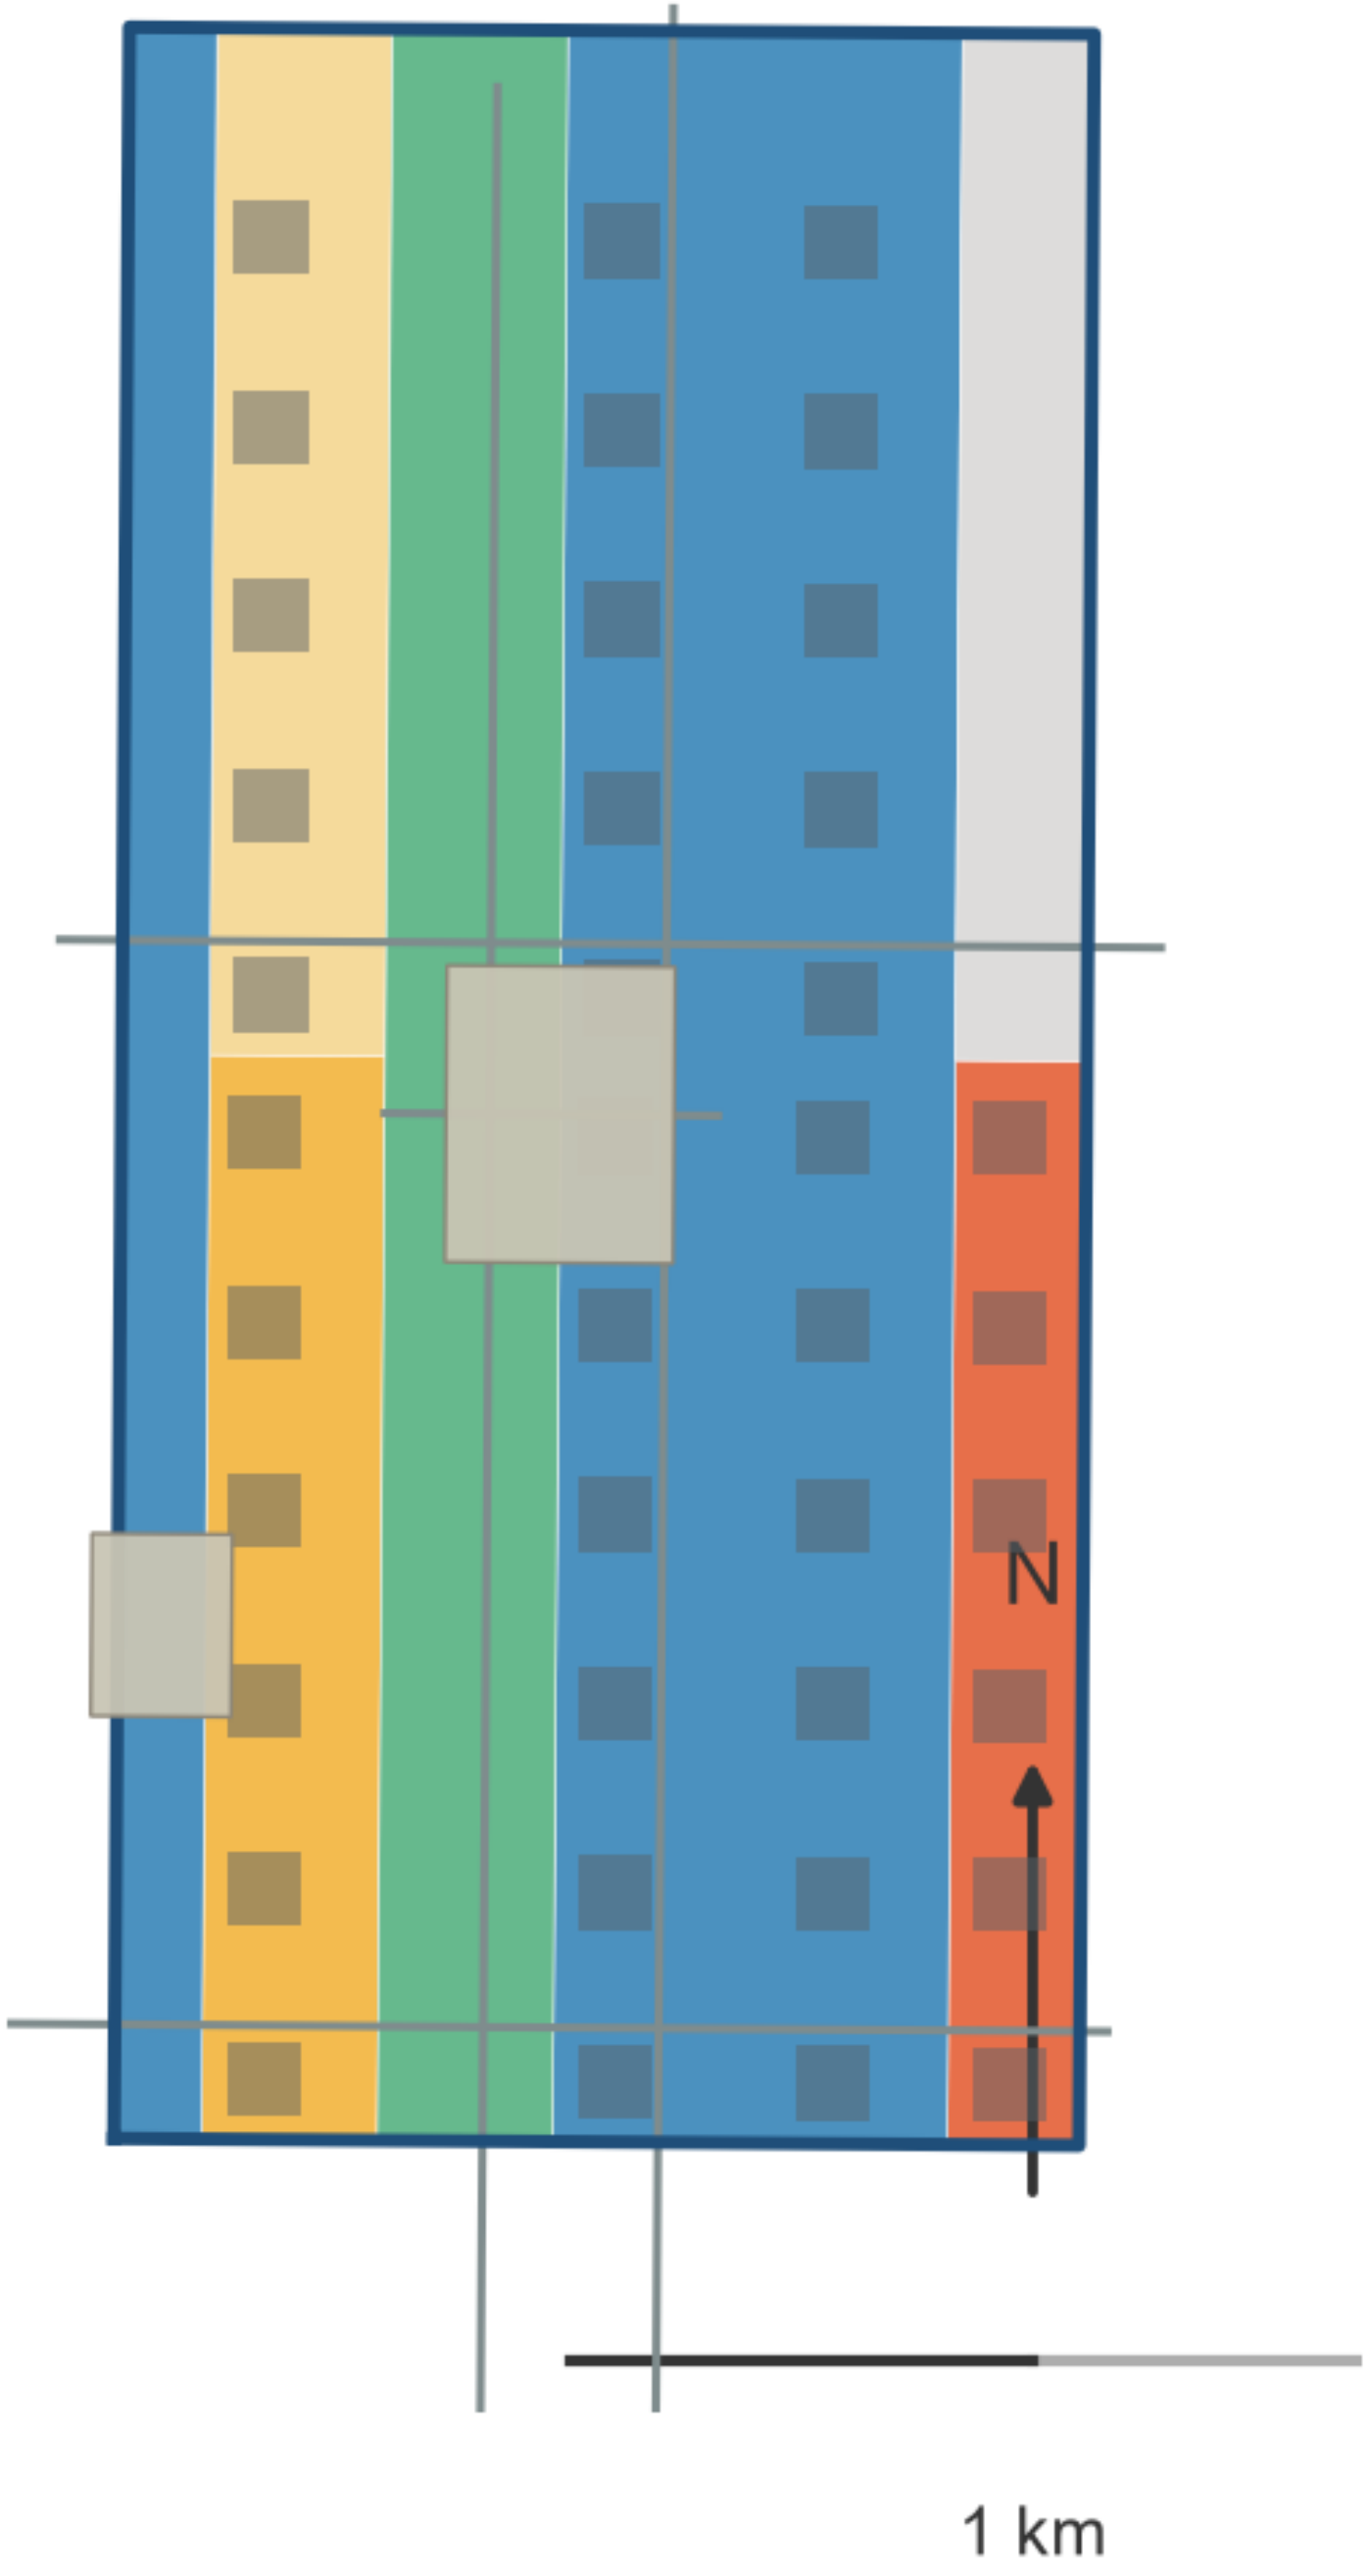


Beijing AI Origin Community

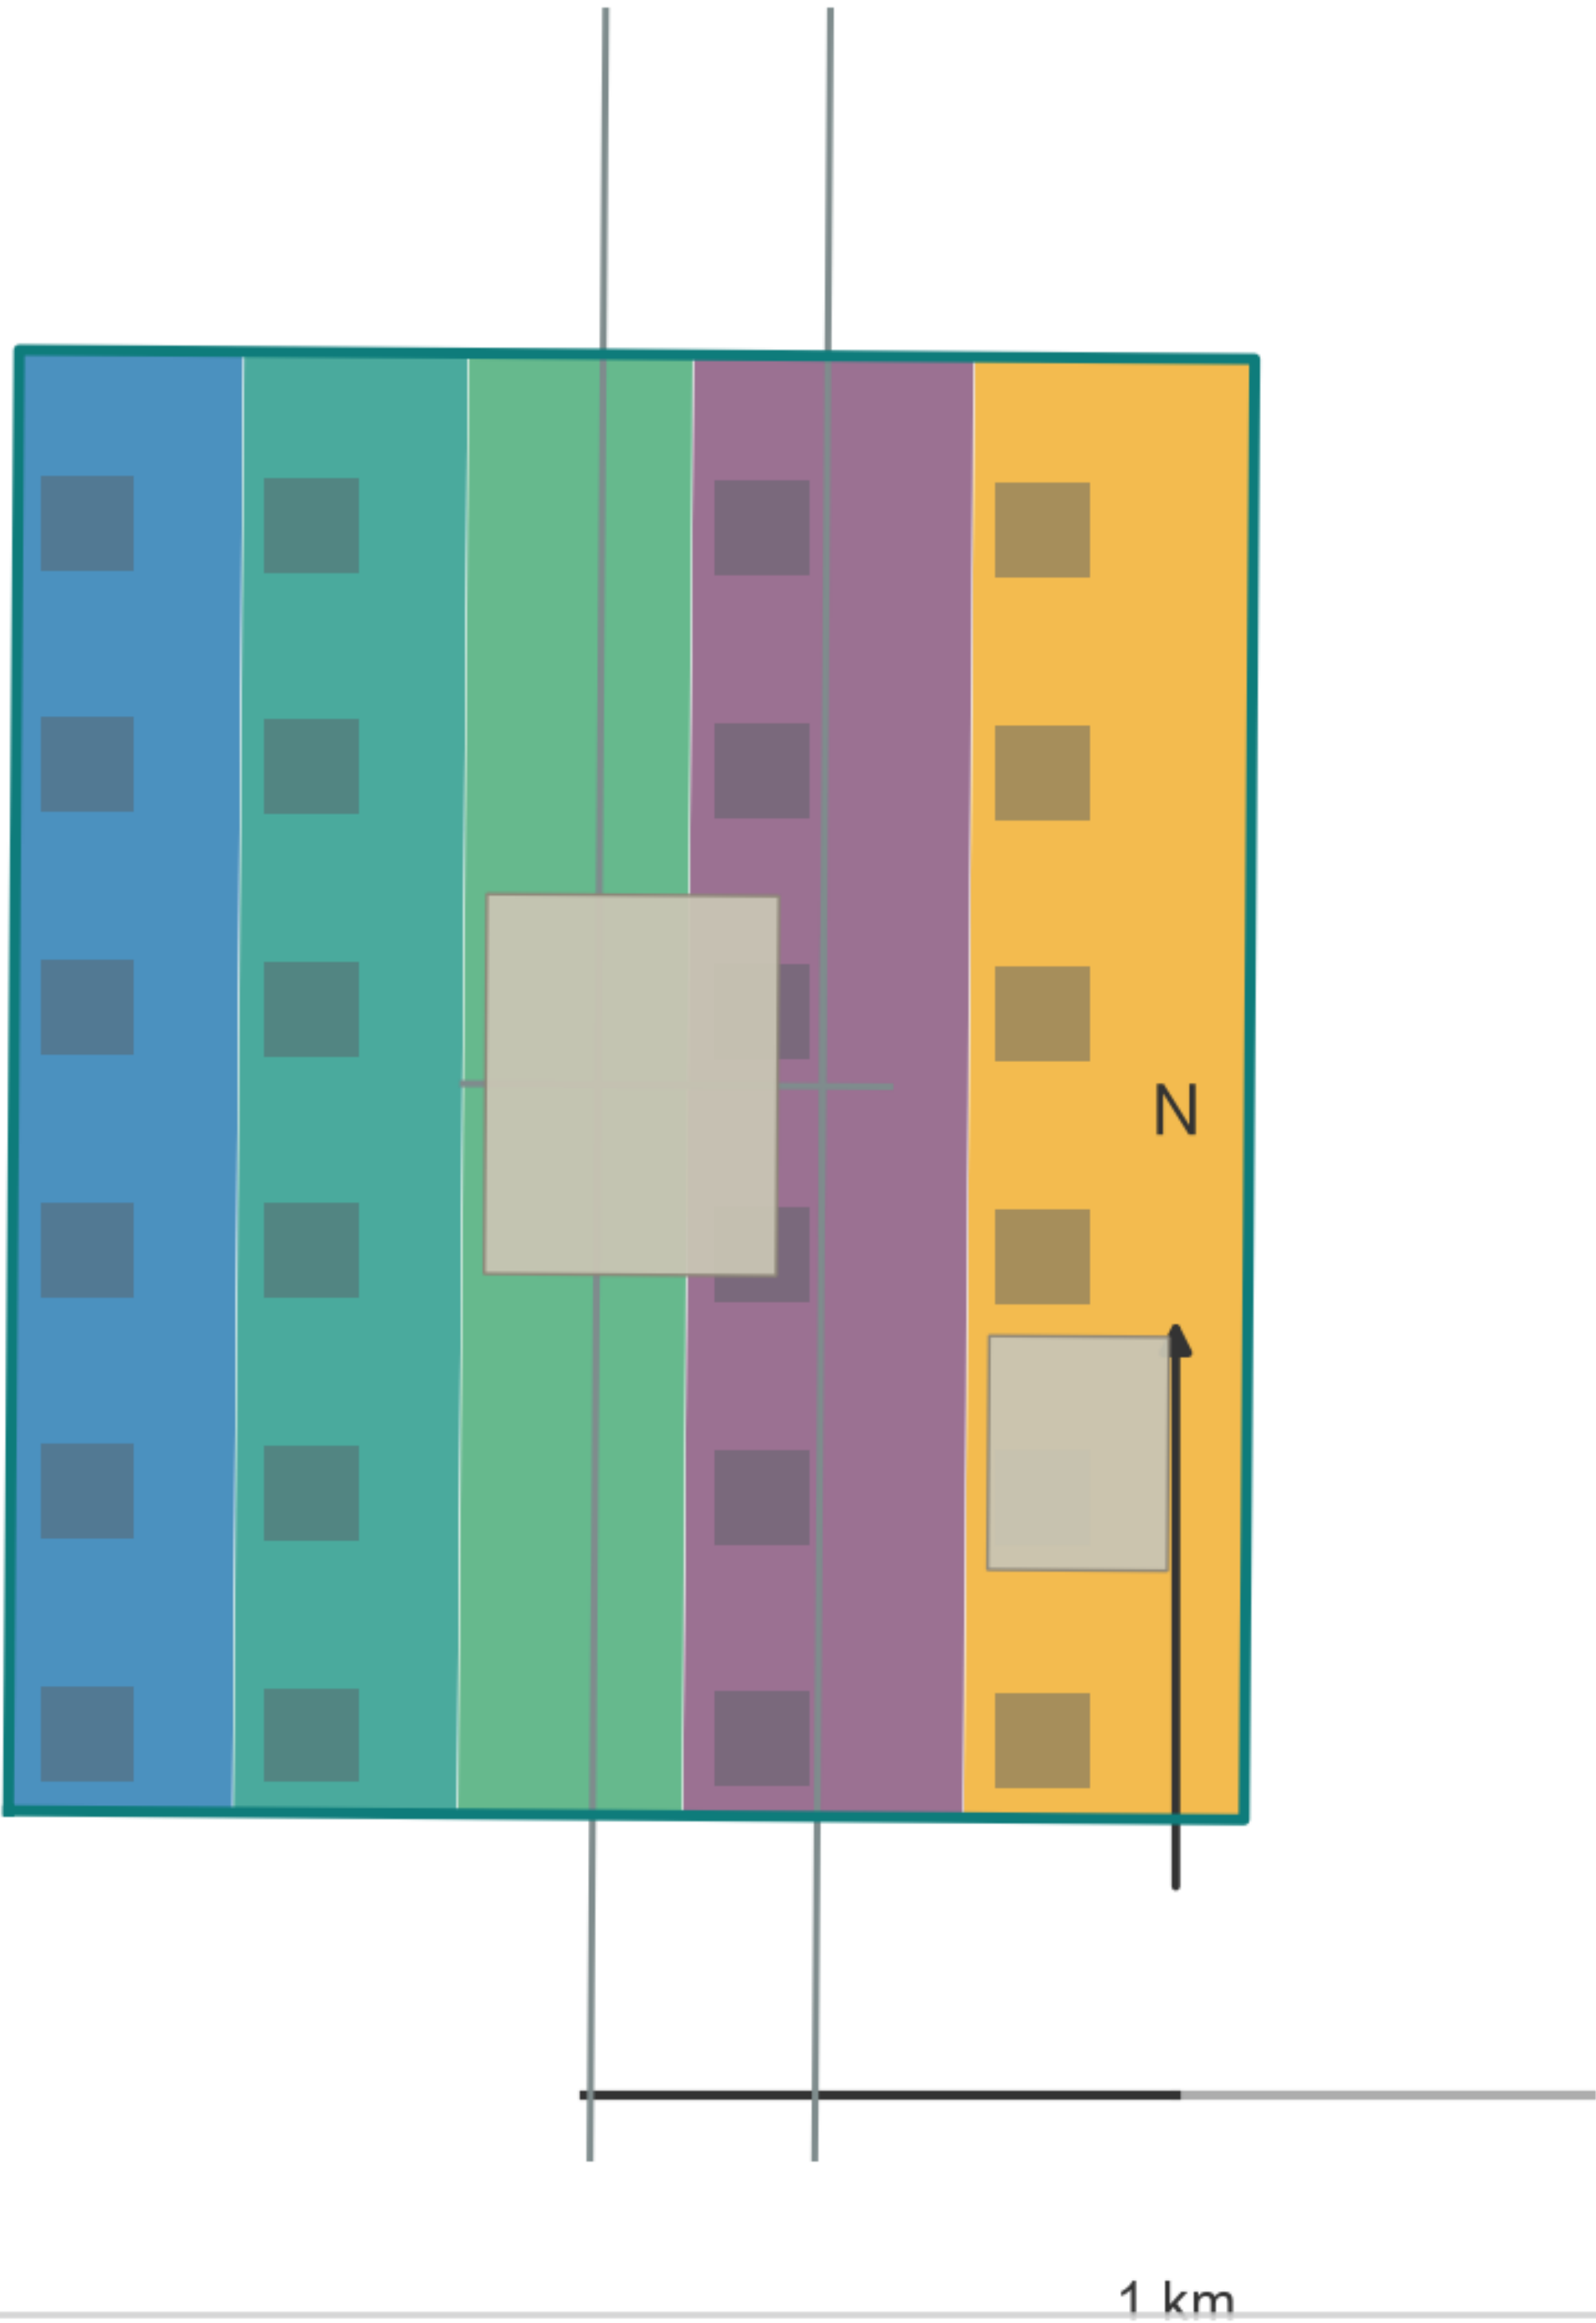

Dazhongsi AI Industry Cluster

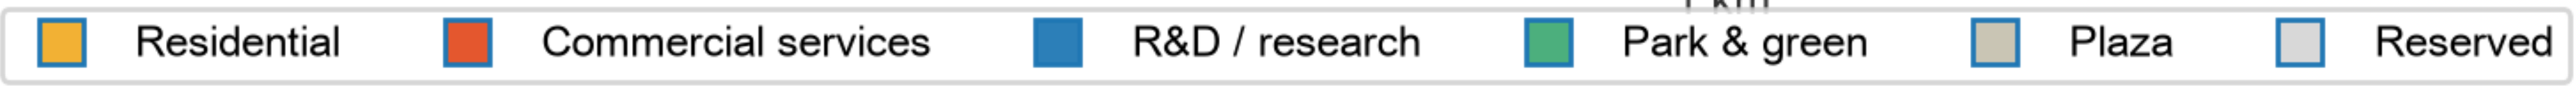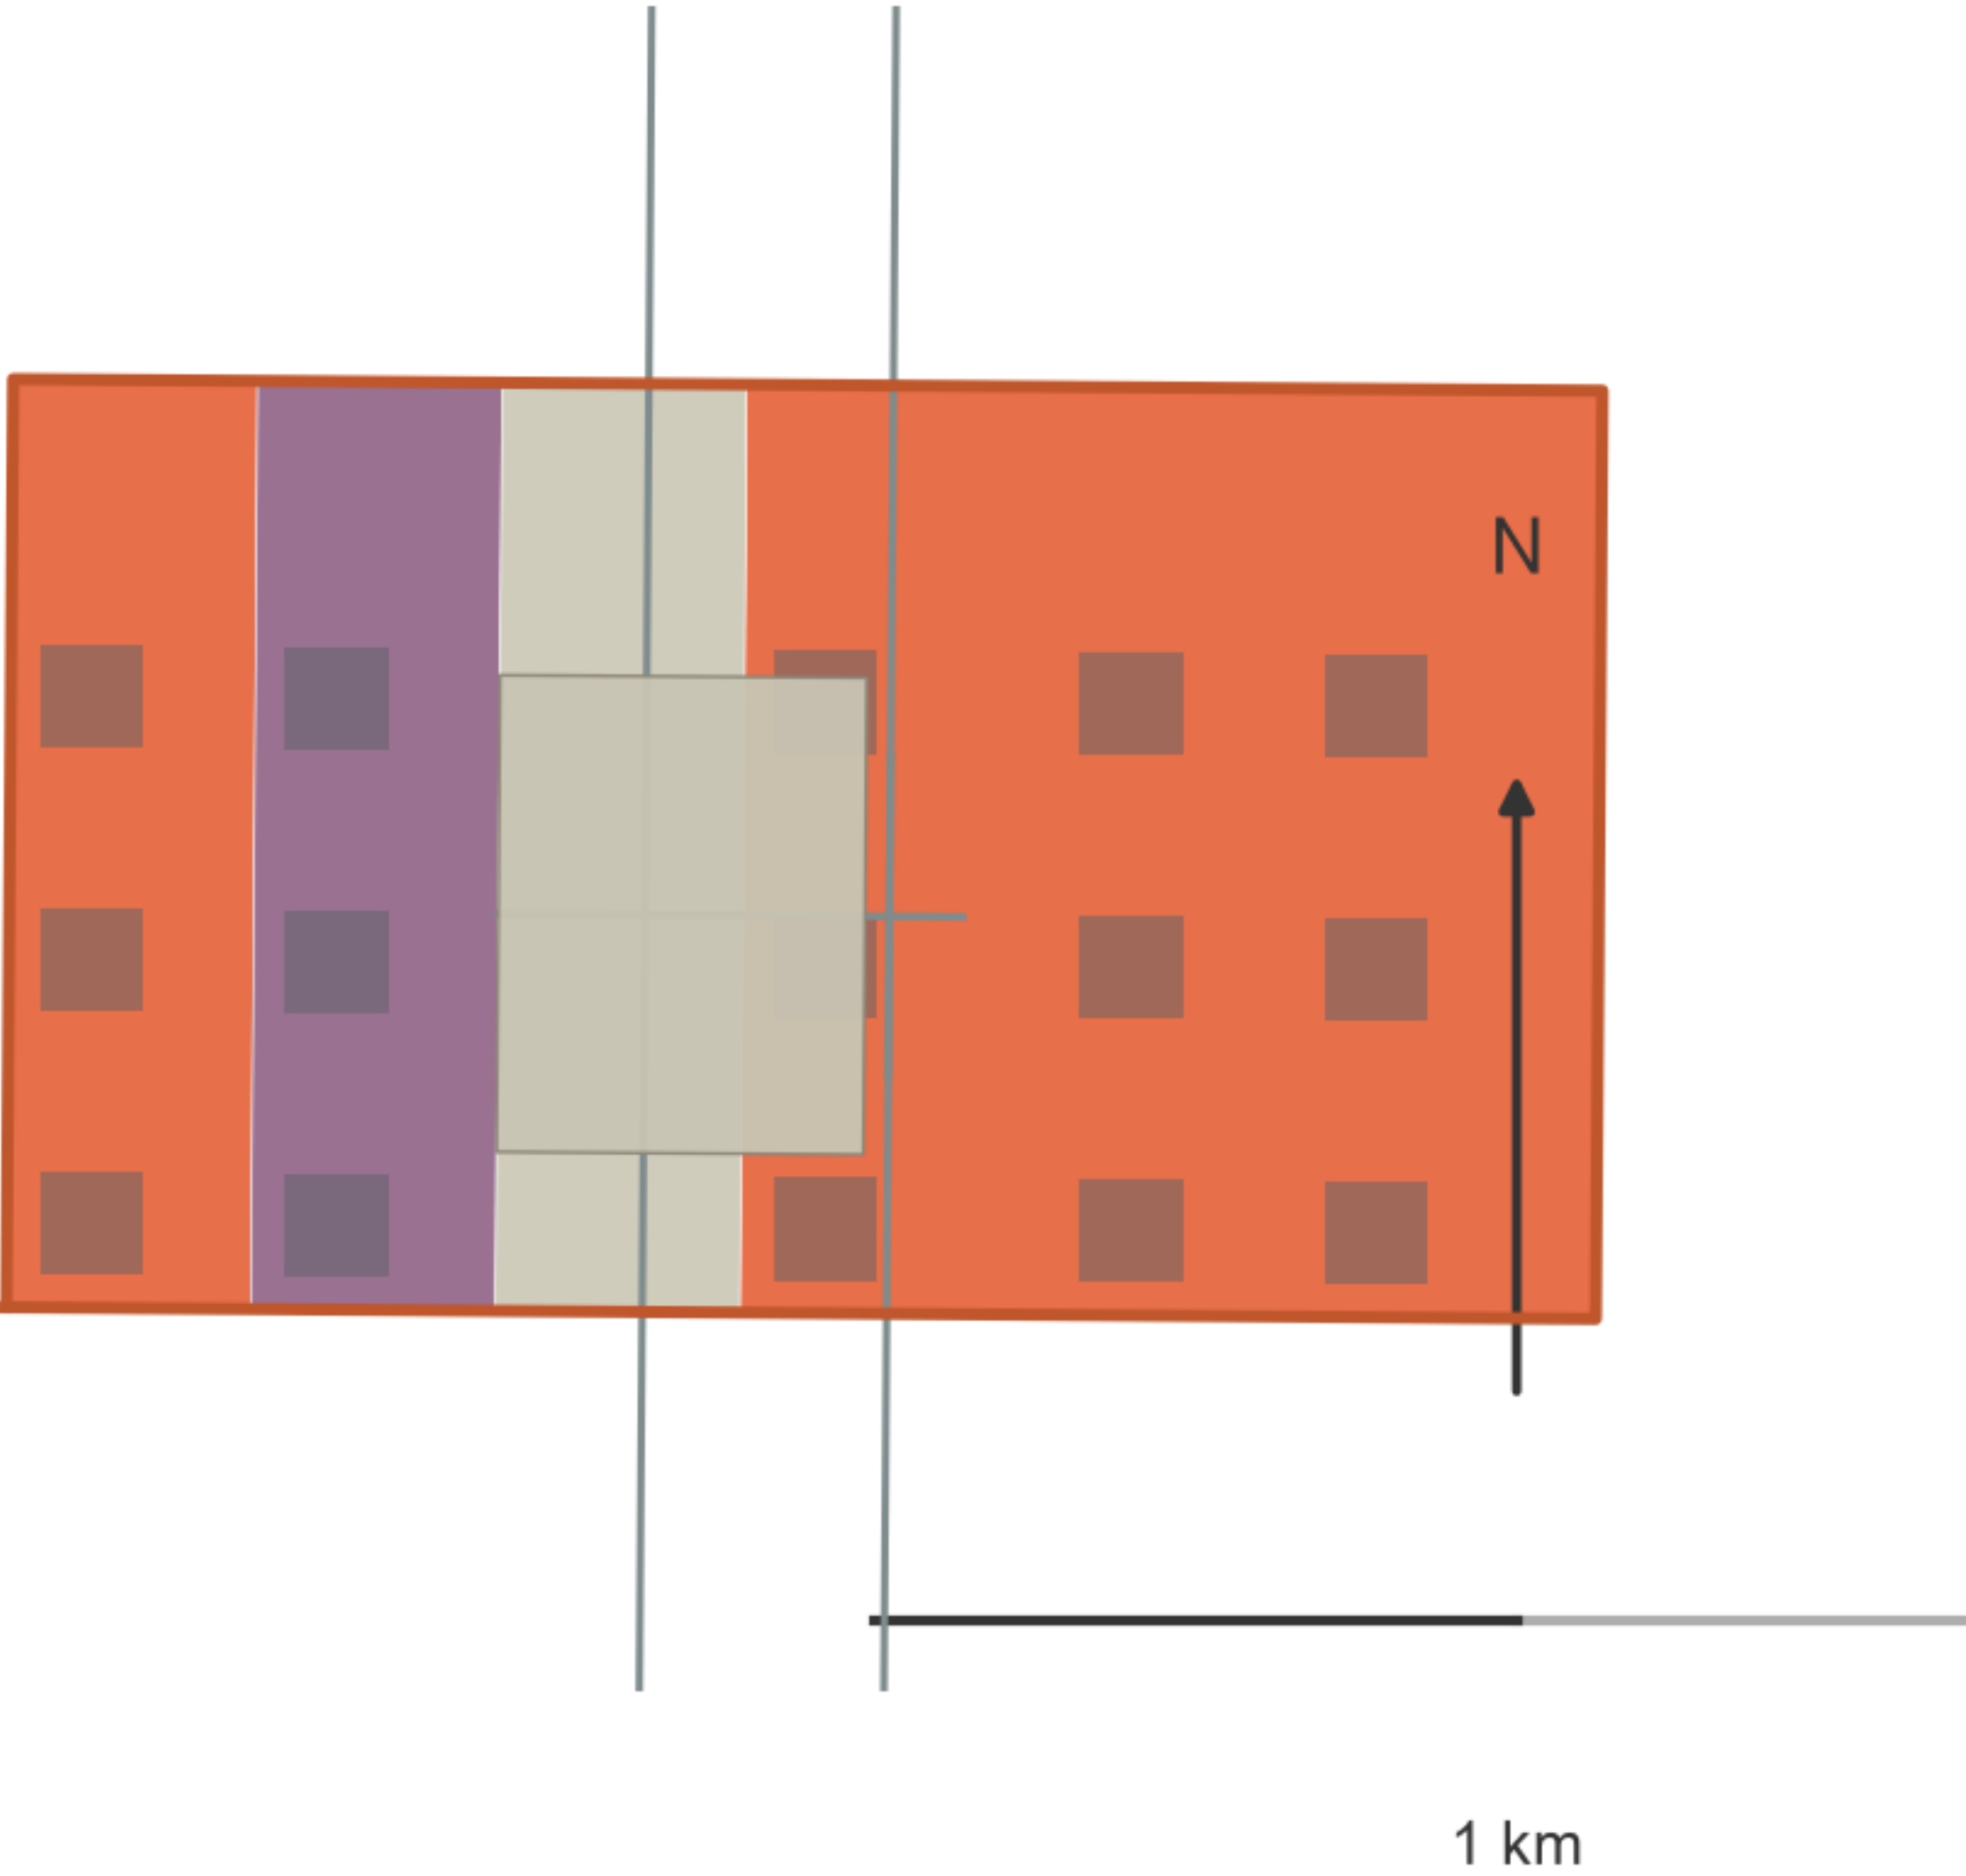

Land-use structure of the overall design area (regulatory-depth urban design concept)

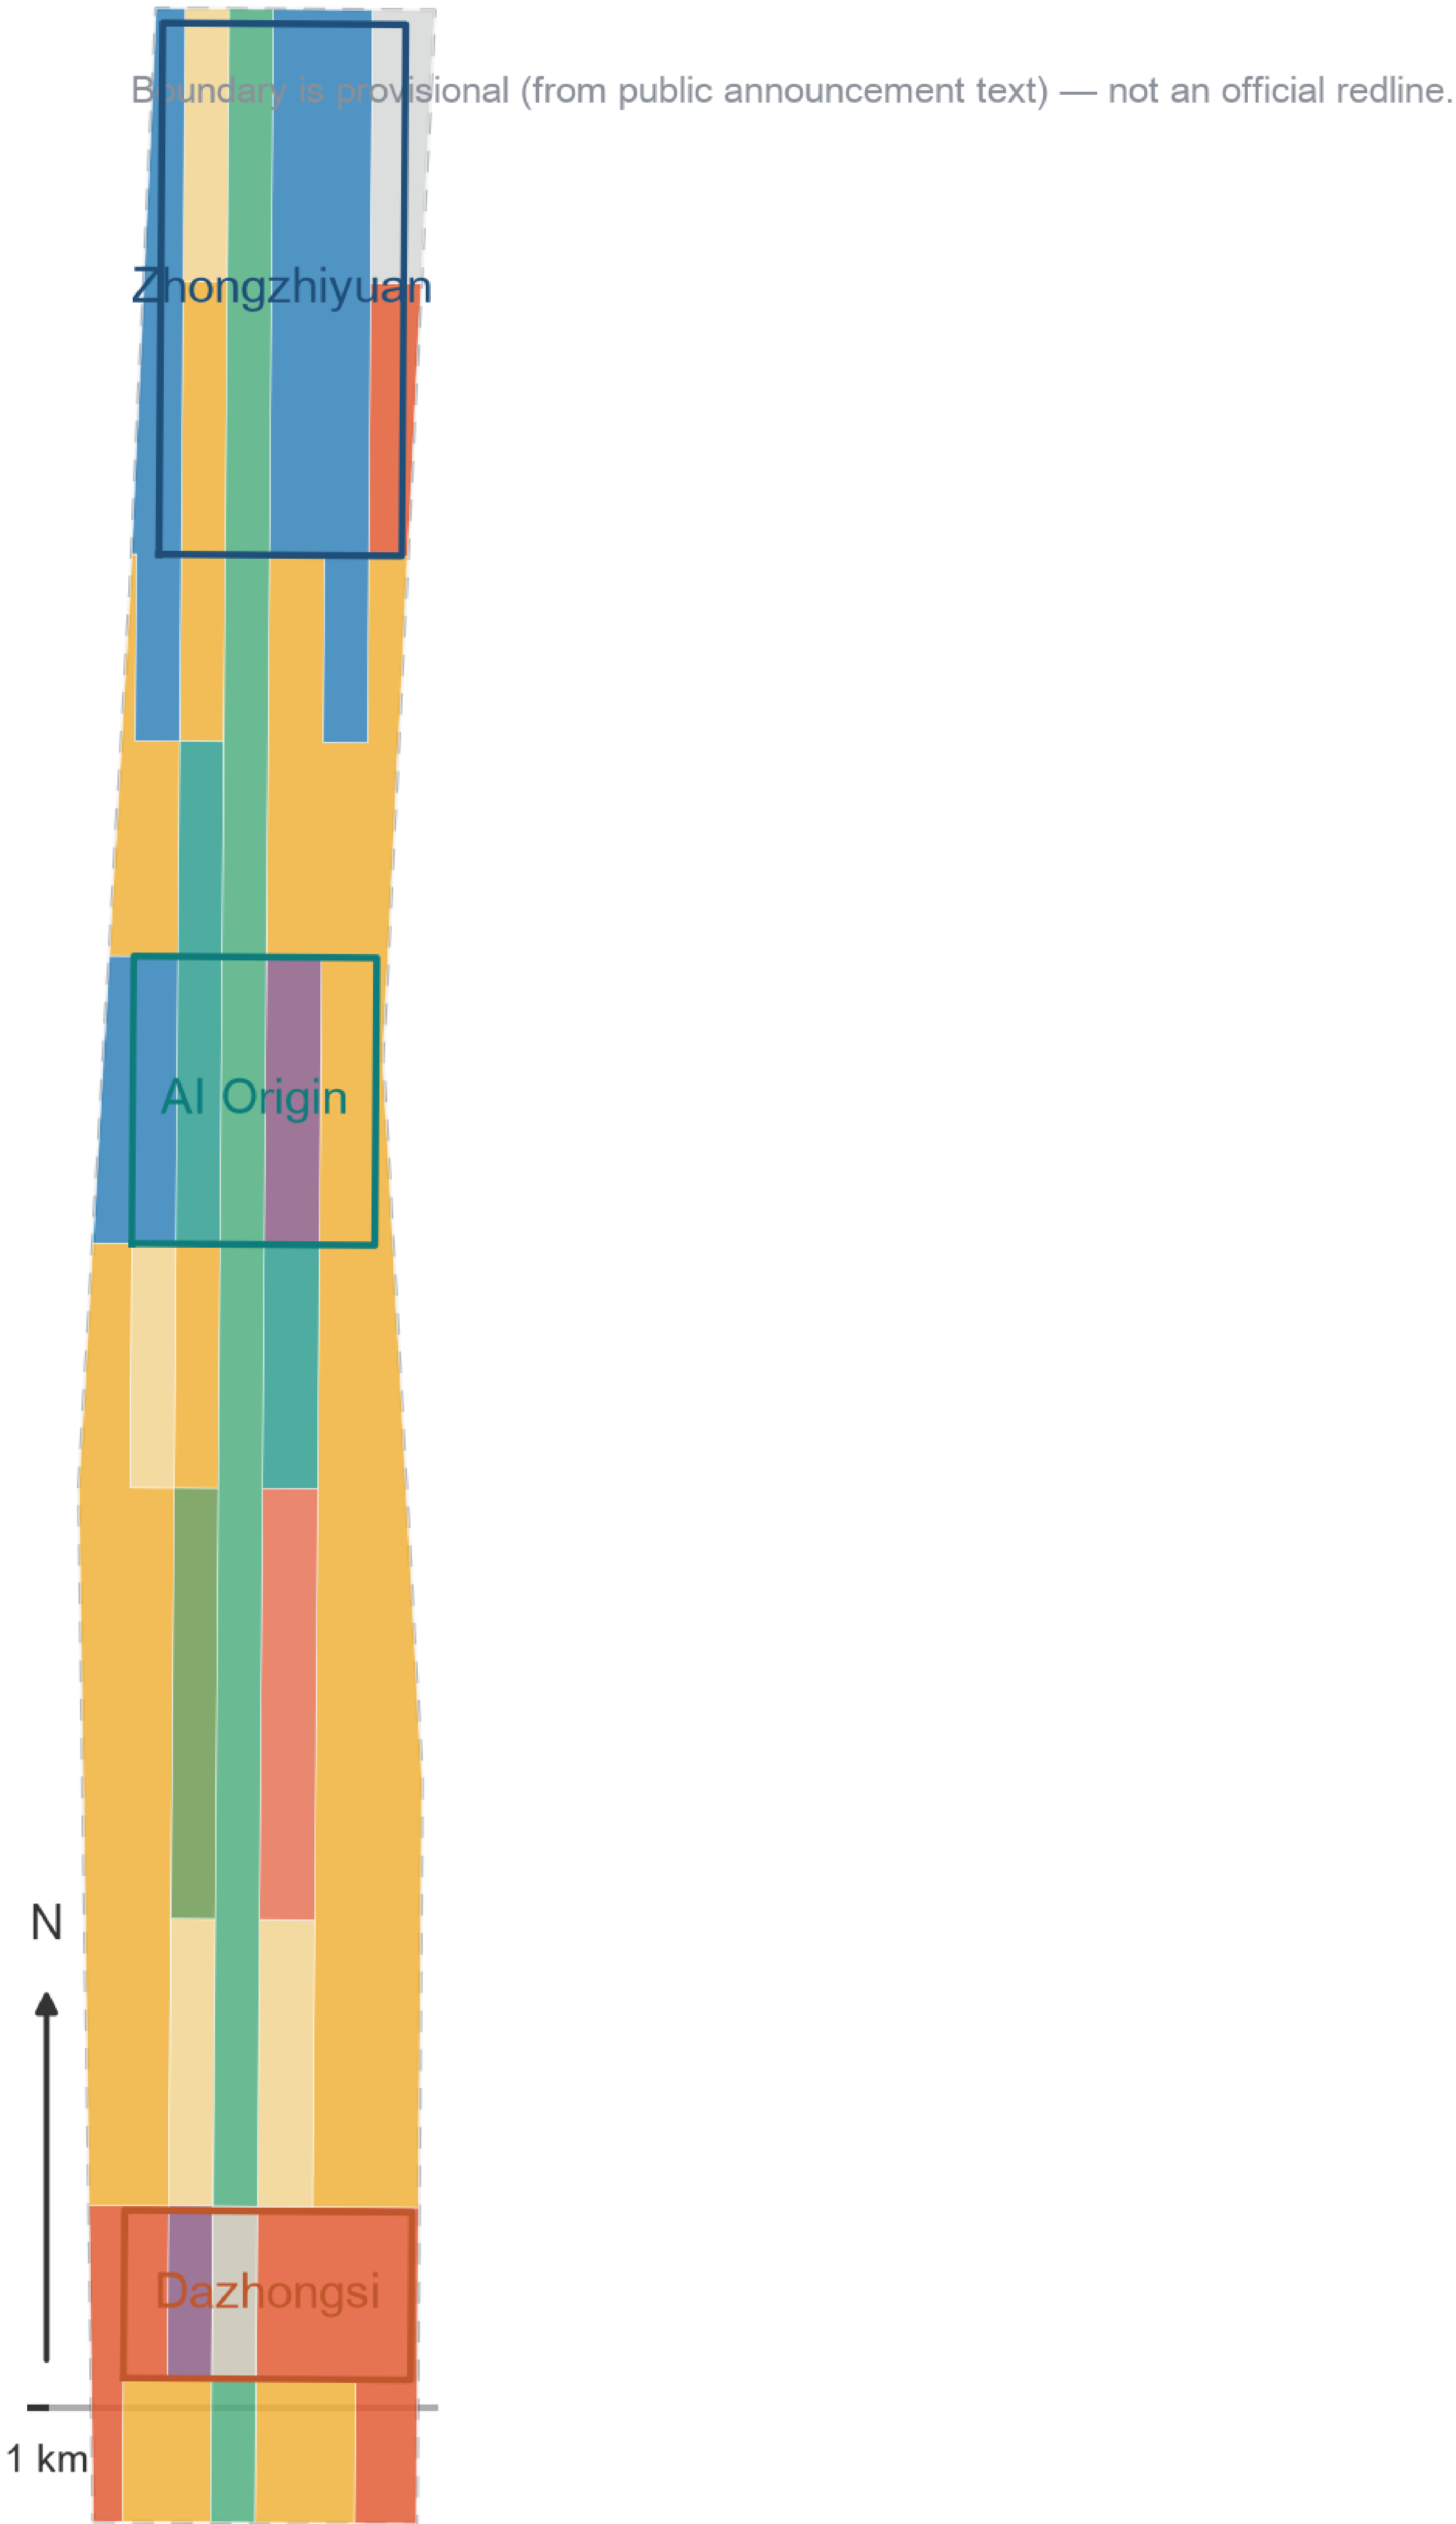


Land-use legend

- 0802 R&D / research
- 05 Commercial services
- 0701 Residential
- 0702 Community facilities
- 0803 Culture
- 0804 Education
- 0805 Sports
- 0806 Health
- 1401 Park & green
- 1403 Plaza
- 16 Reserved


Per MNR land-use classification guide subset;
areas recomputed in EPSG:4548, see metrics.json.

Metric recomputation and evidence chain (from geometry / metrics.json)


Land-use distribution (overall design area)

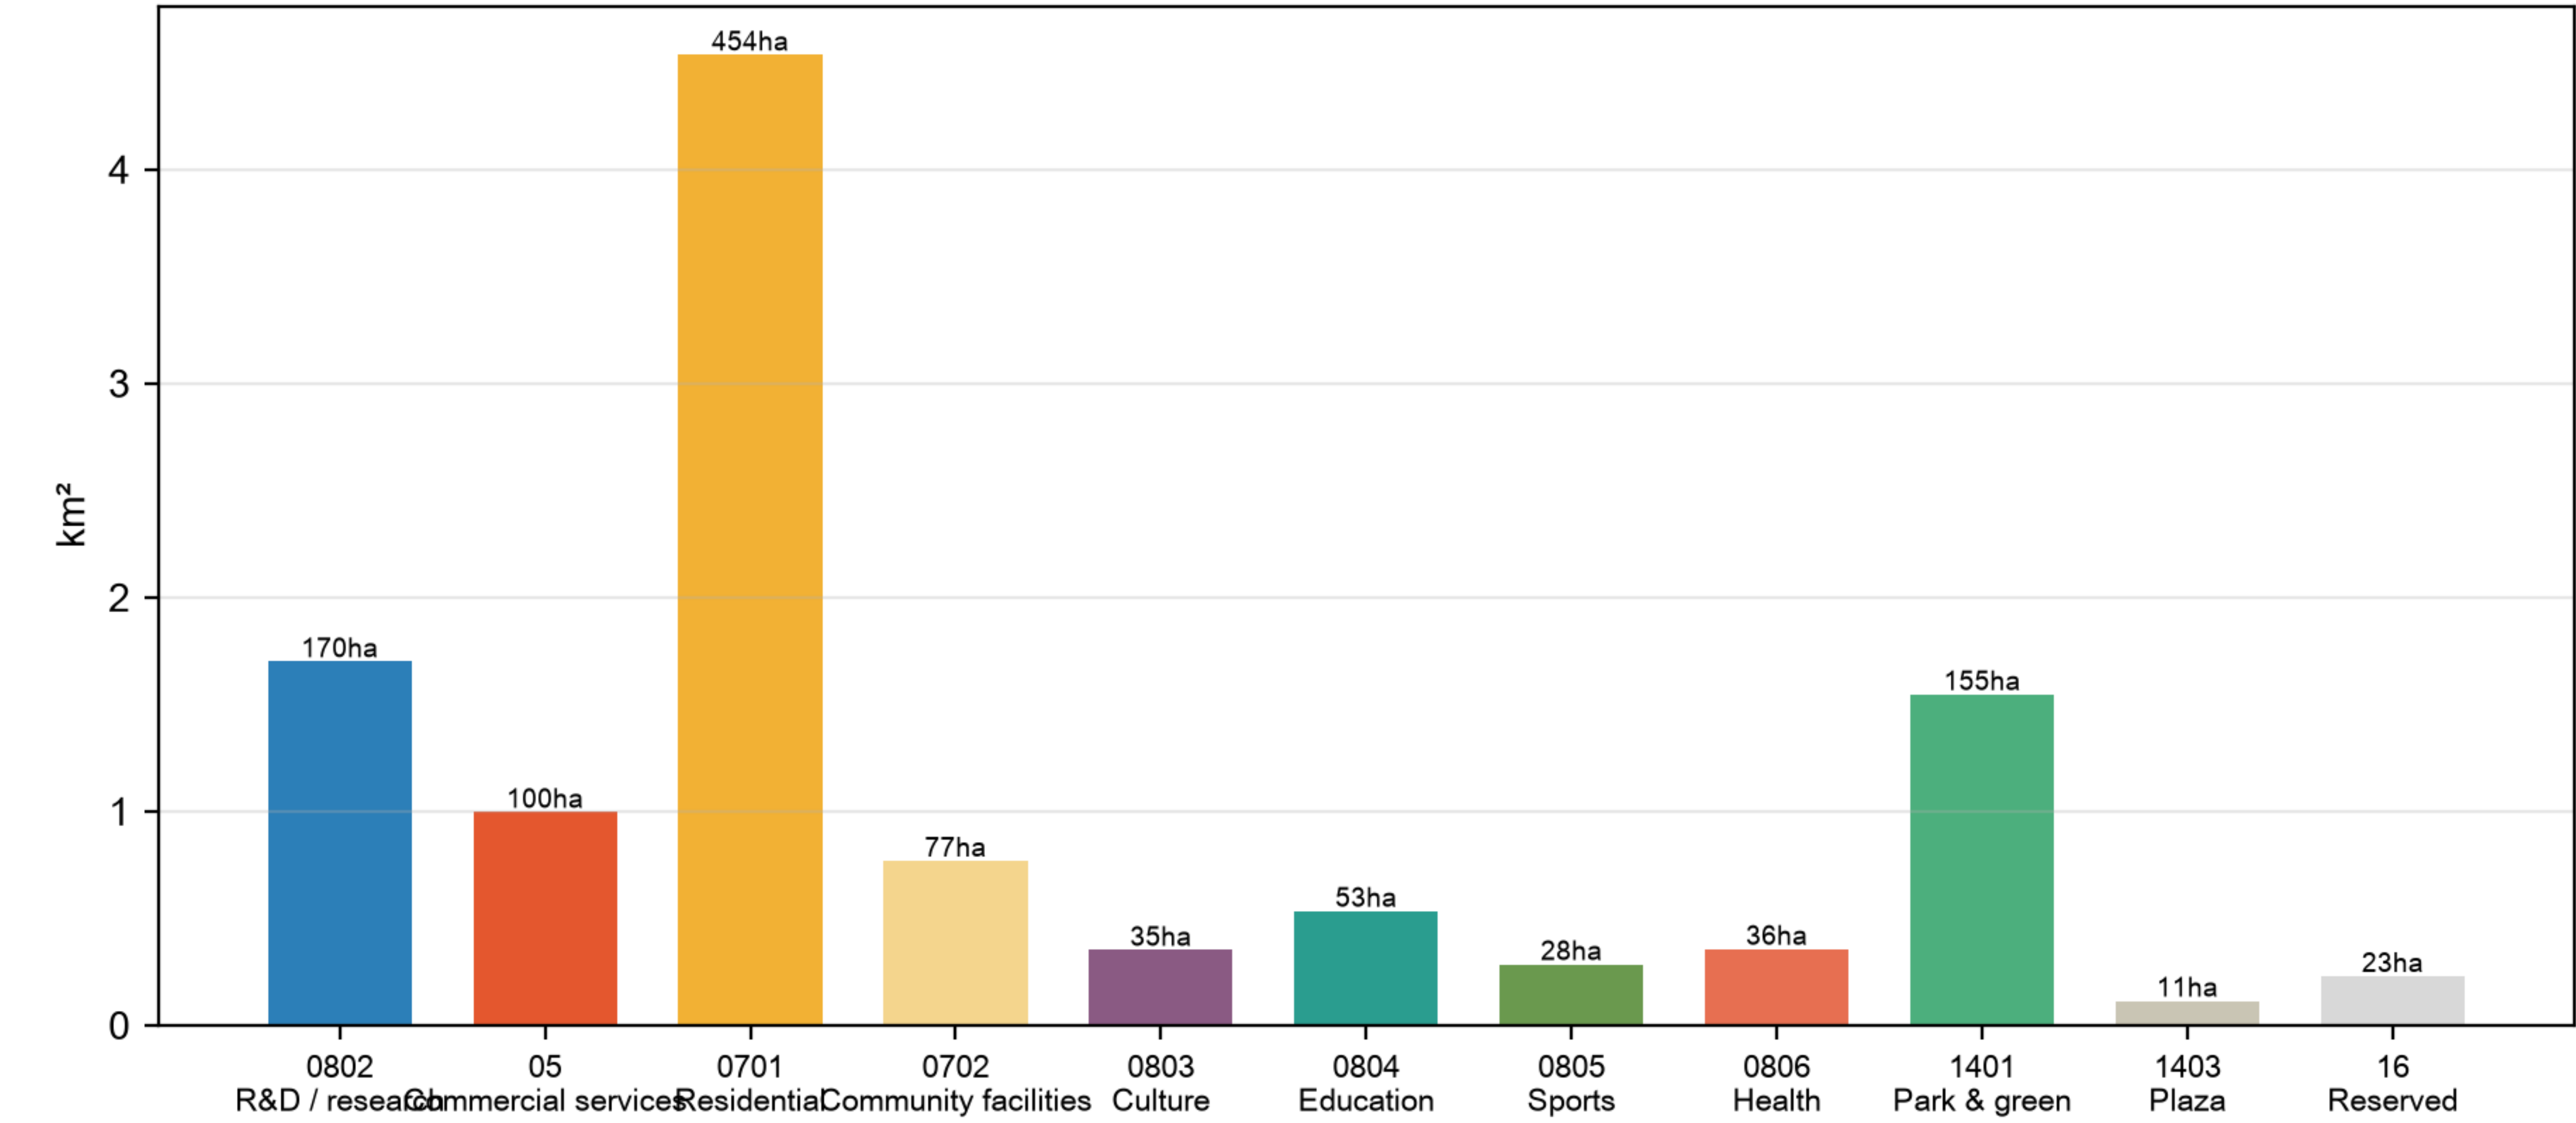


Core spatial ratio metrics

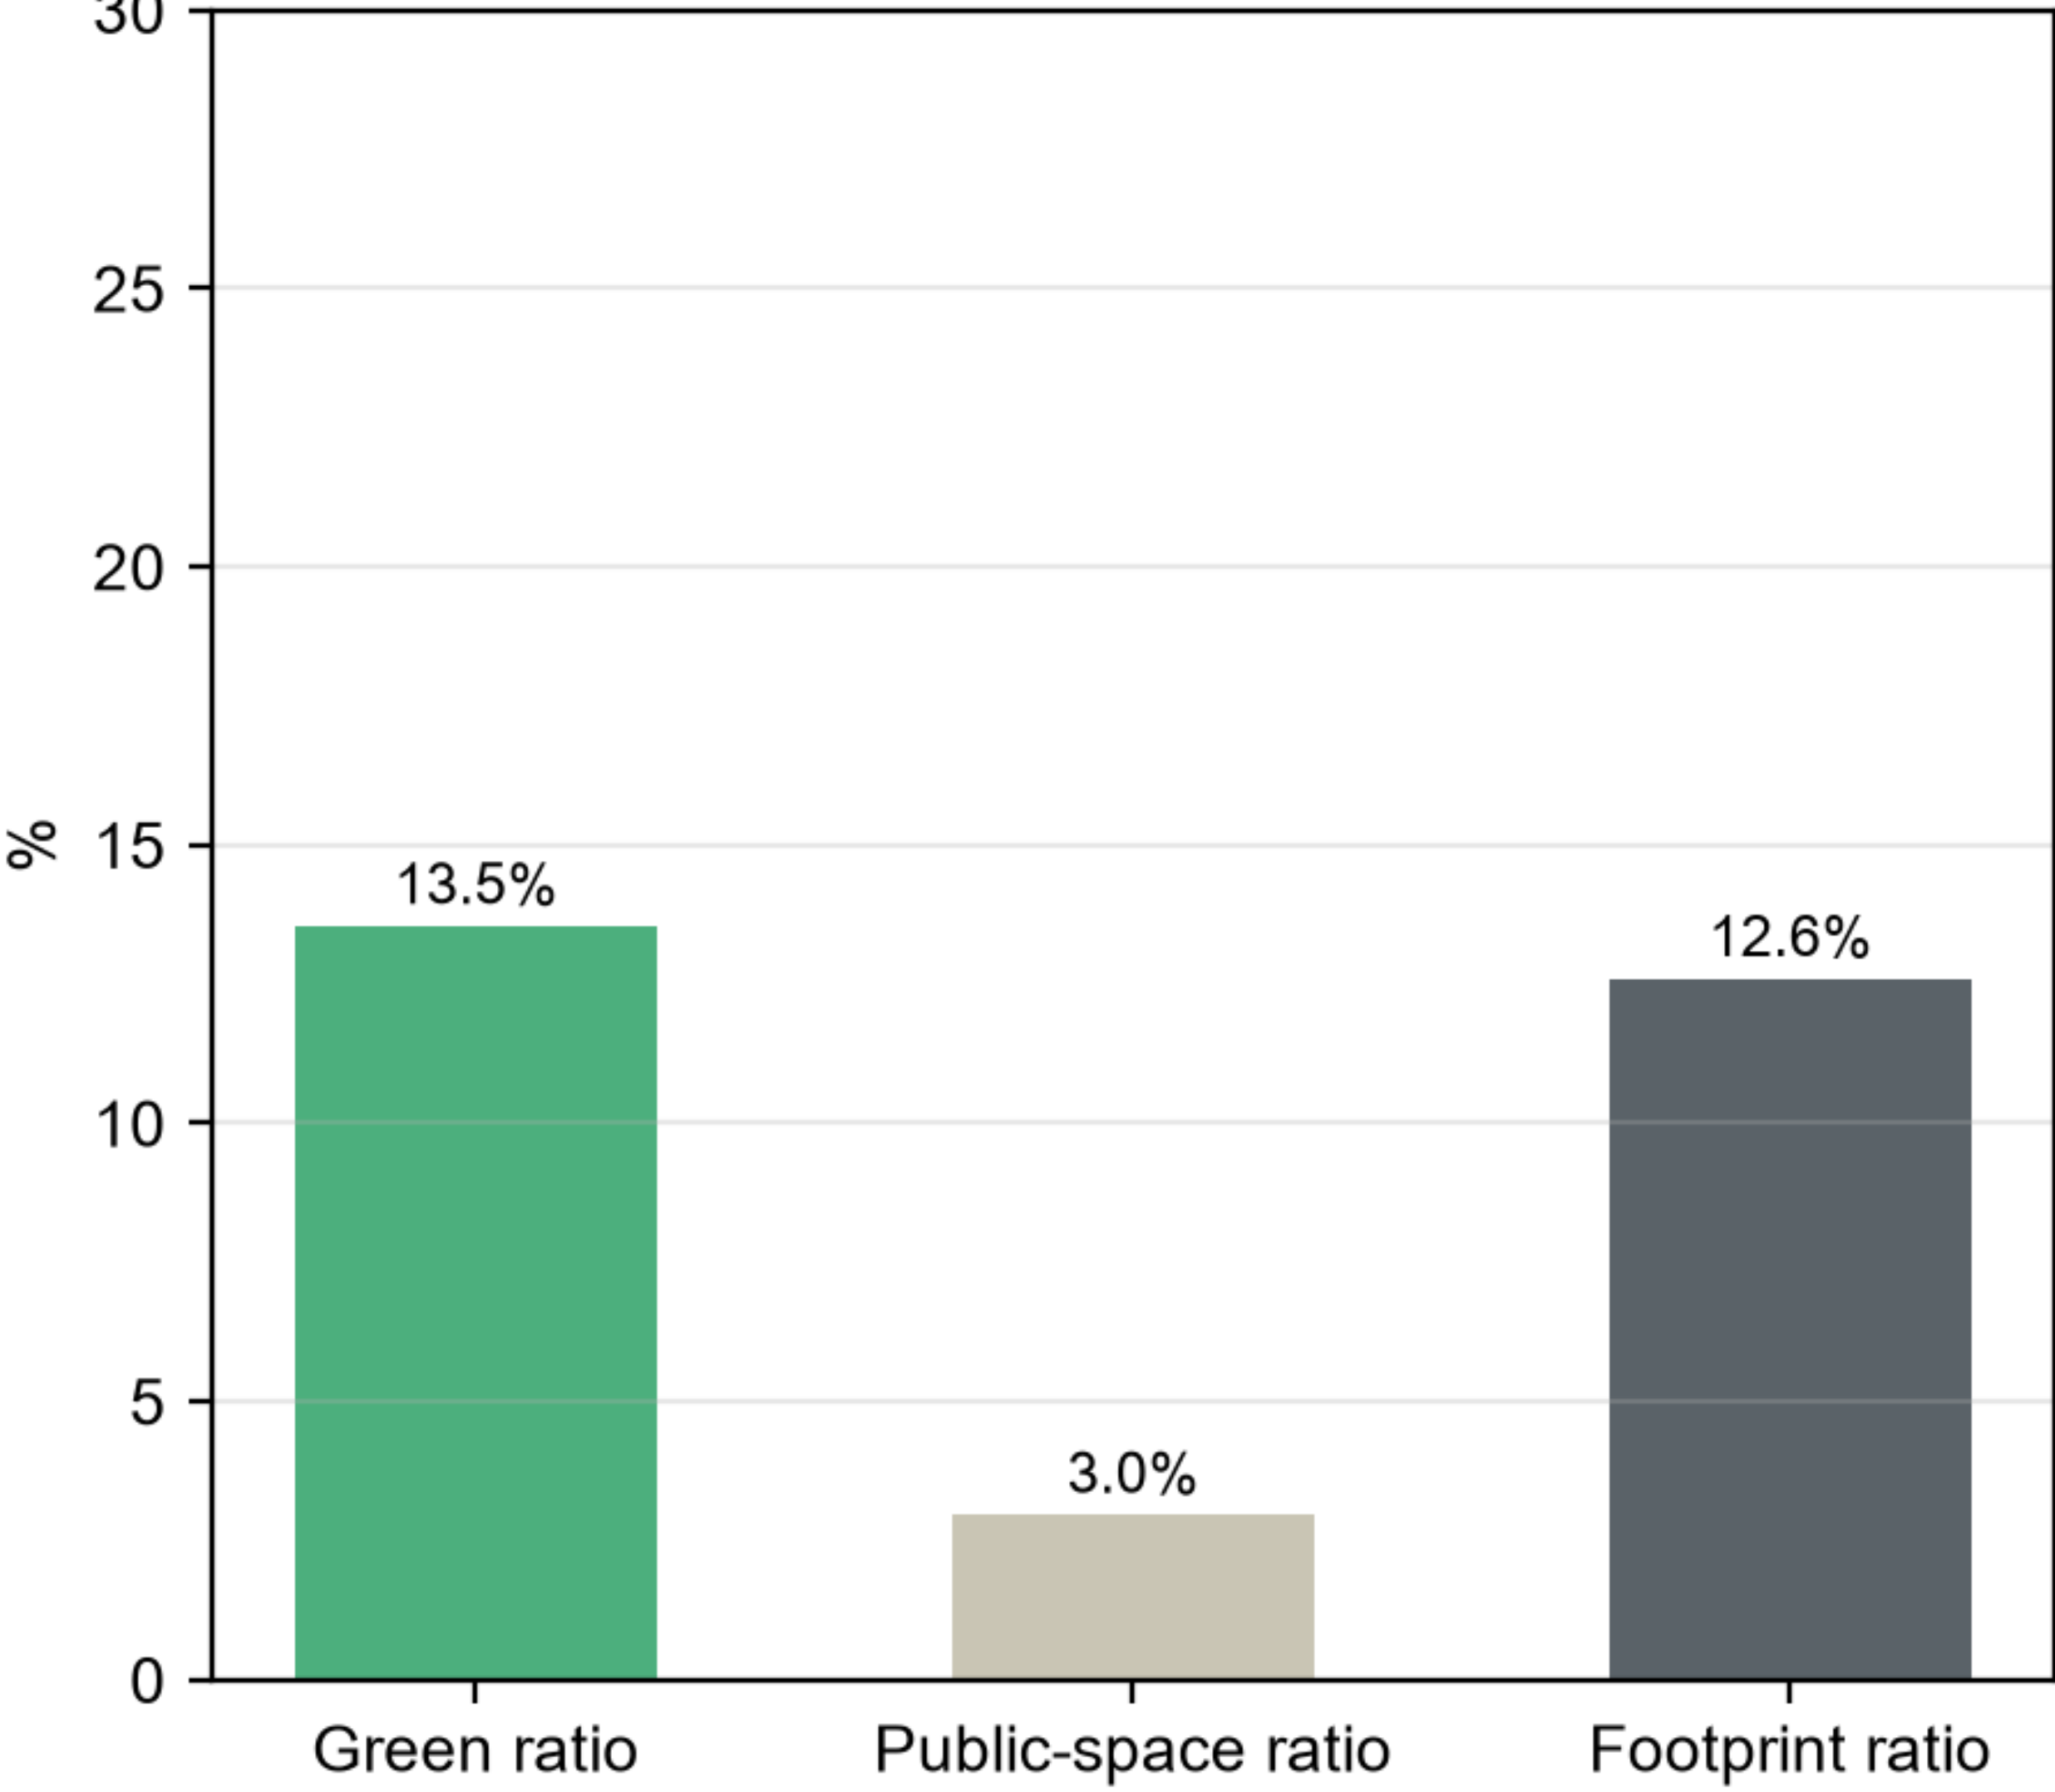

Key-area footprints (ha)

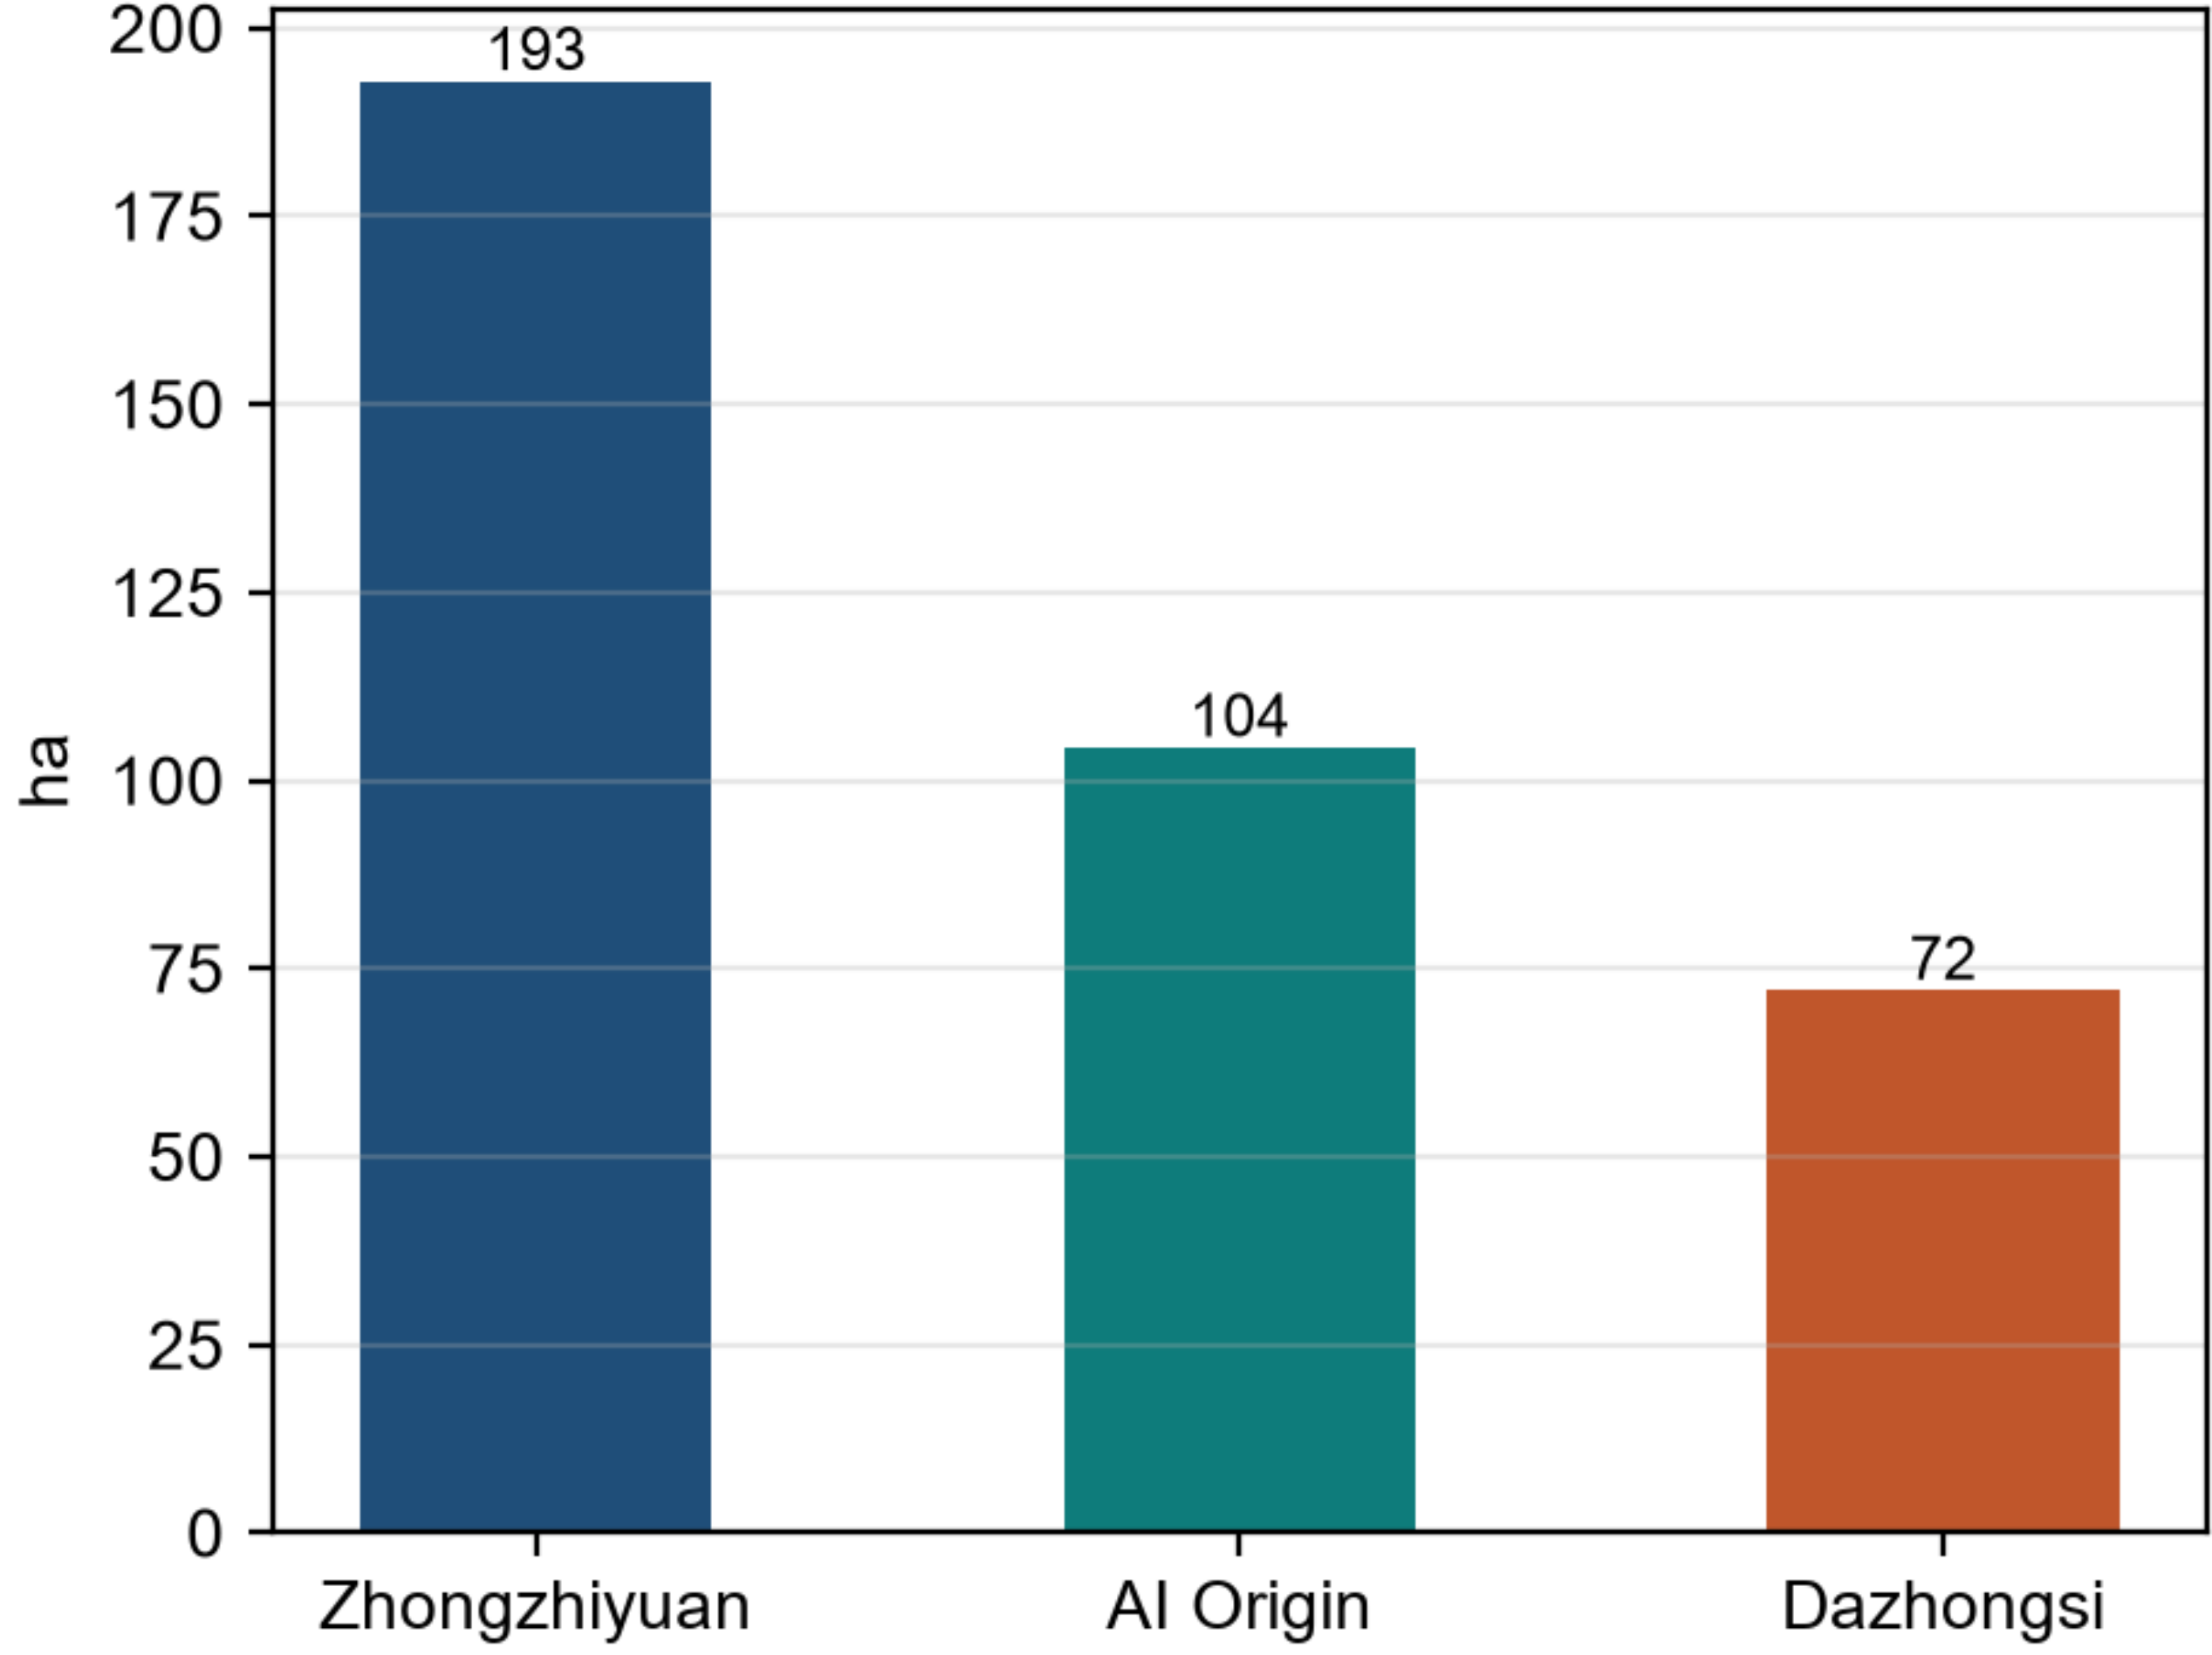

Area totals

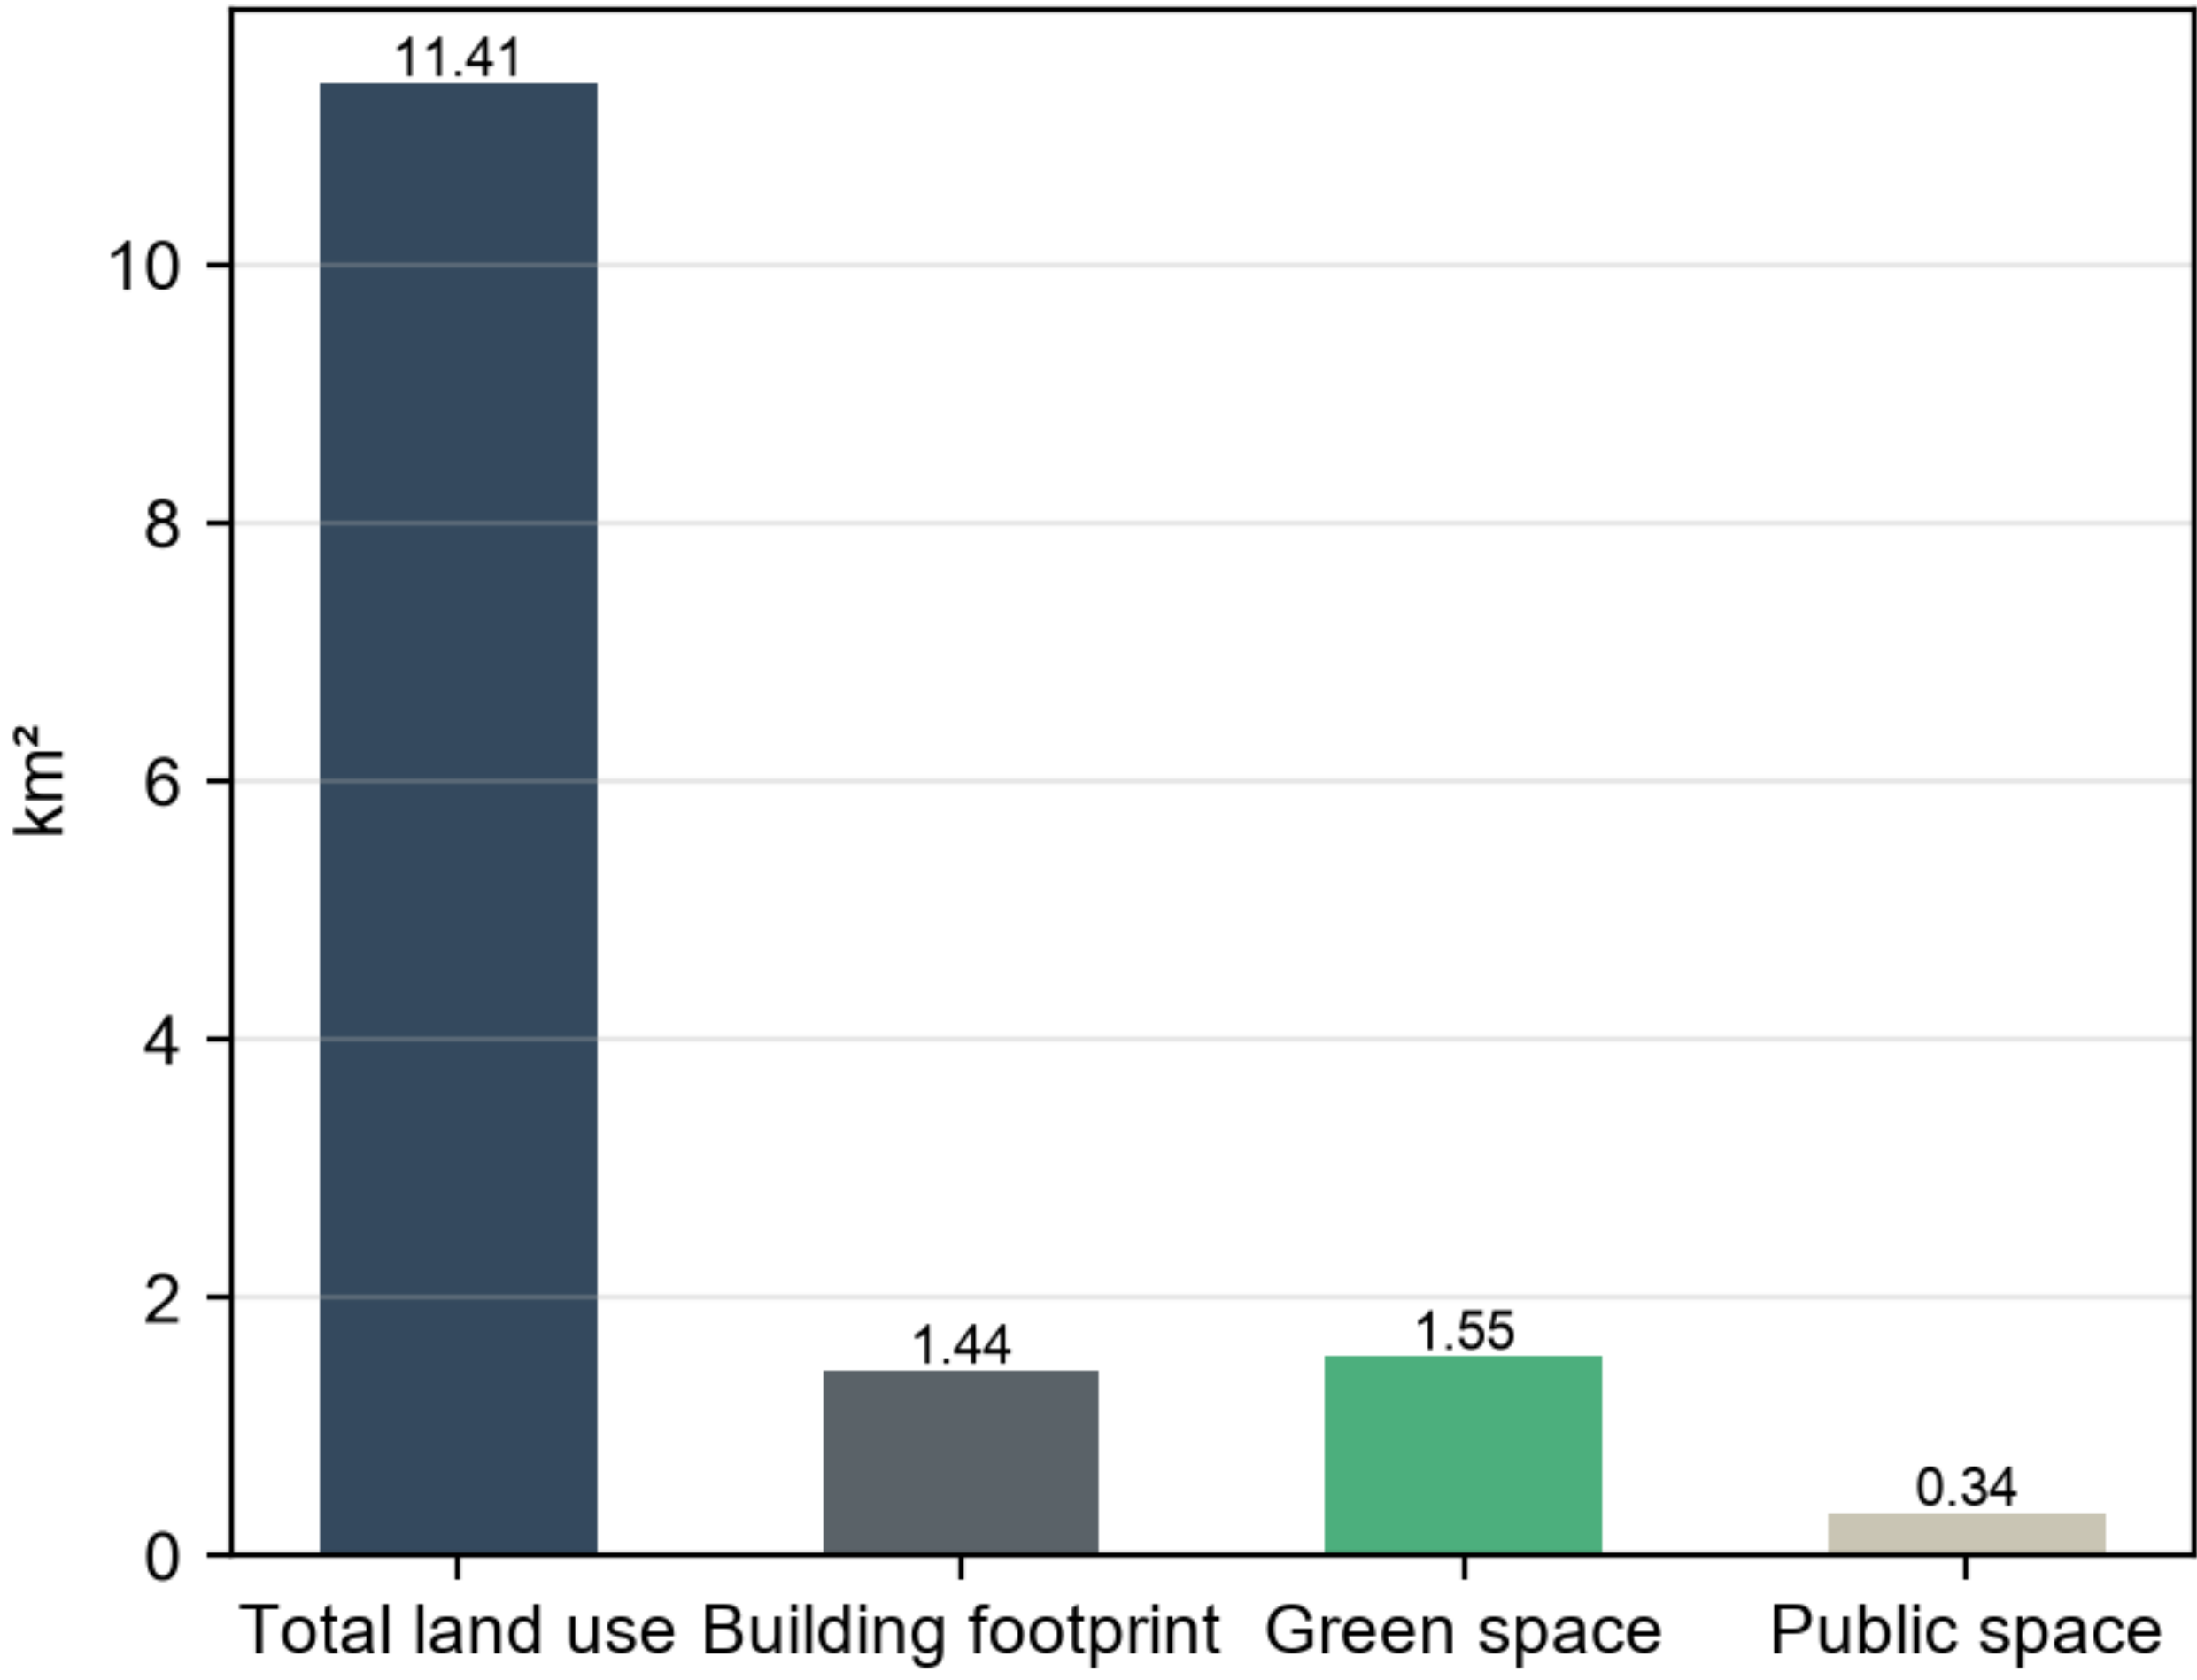


Additional metrics

- Road centerline length: 28,797 m
- Key-area count: 3 areas
- Near-term pilot (P1): 230 ha

All areas/ratios recomputed from submitted GeoJSON in EPSG:4548 (see metrics.json). Boundary is provisional.

Mobility, slow-traffic and blue-green public-space composite system

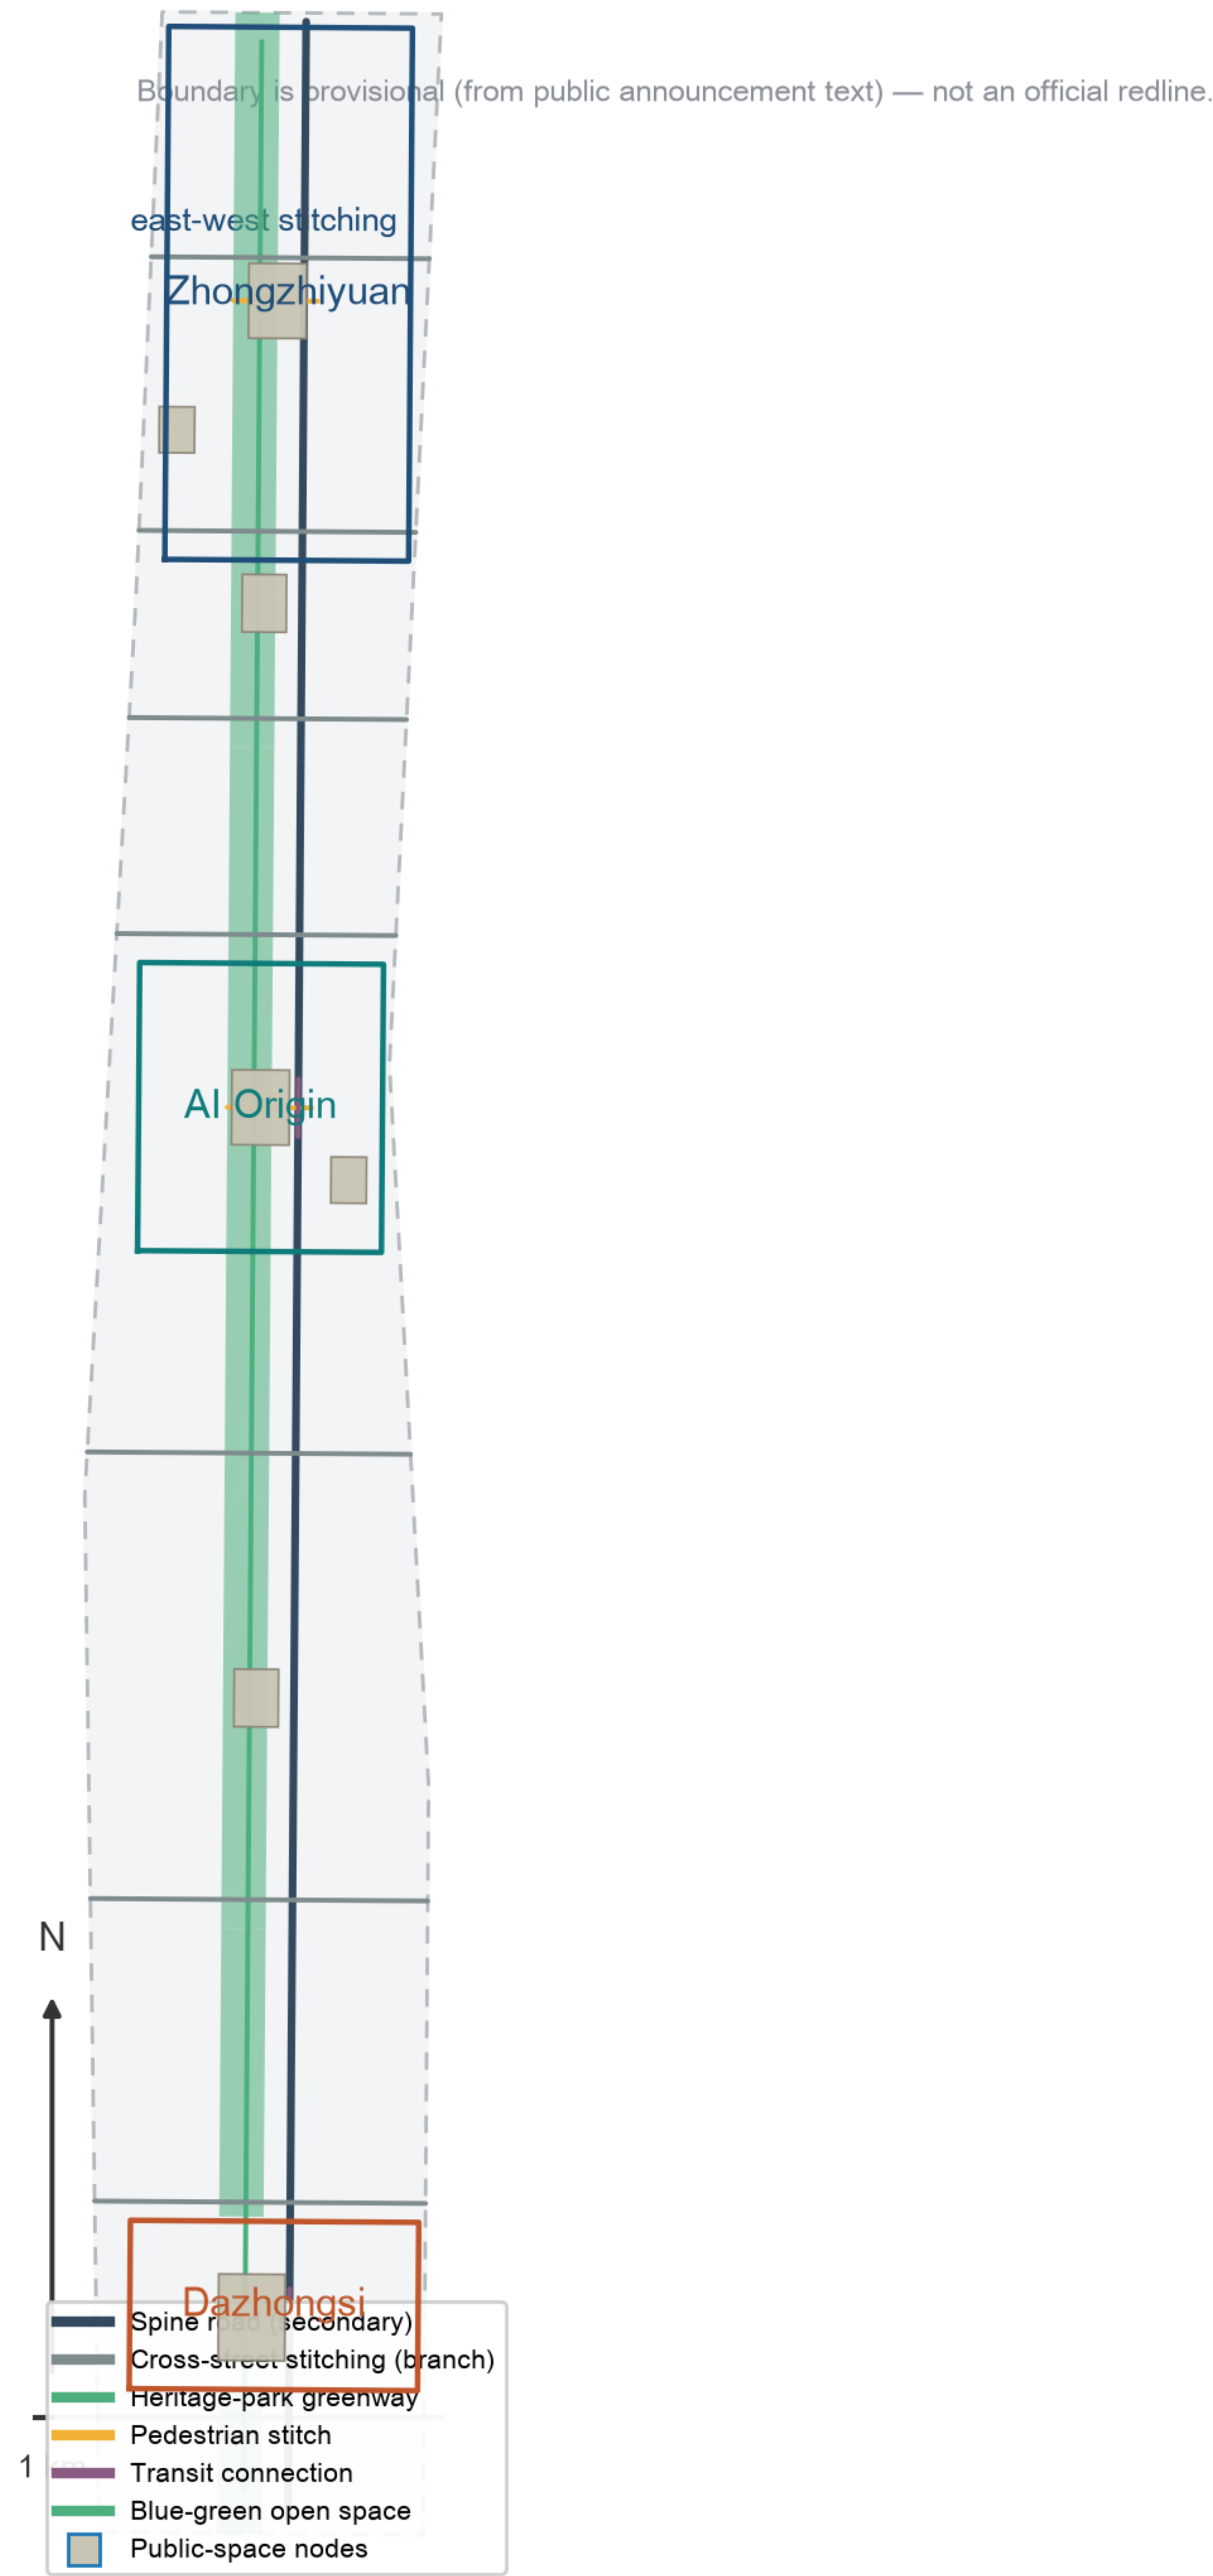

Jing-Zhang AI Pulse — Overall Concept
The Belt · Three Cores · Two Wings

