


总览地图 · 三层范围 · 重点区域 · 蓝绿骨架

Site overview · three-tier scope · key areas · blue-green frame | 总用地 1 141.28 ha · 重点区域 369.29 ha (3 处) · 主脊绿道 9.72 km

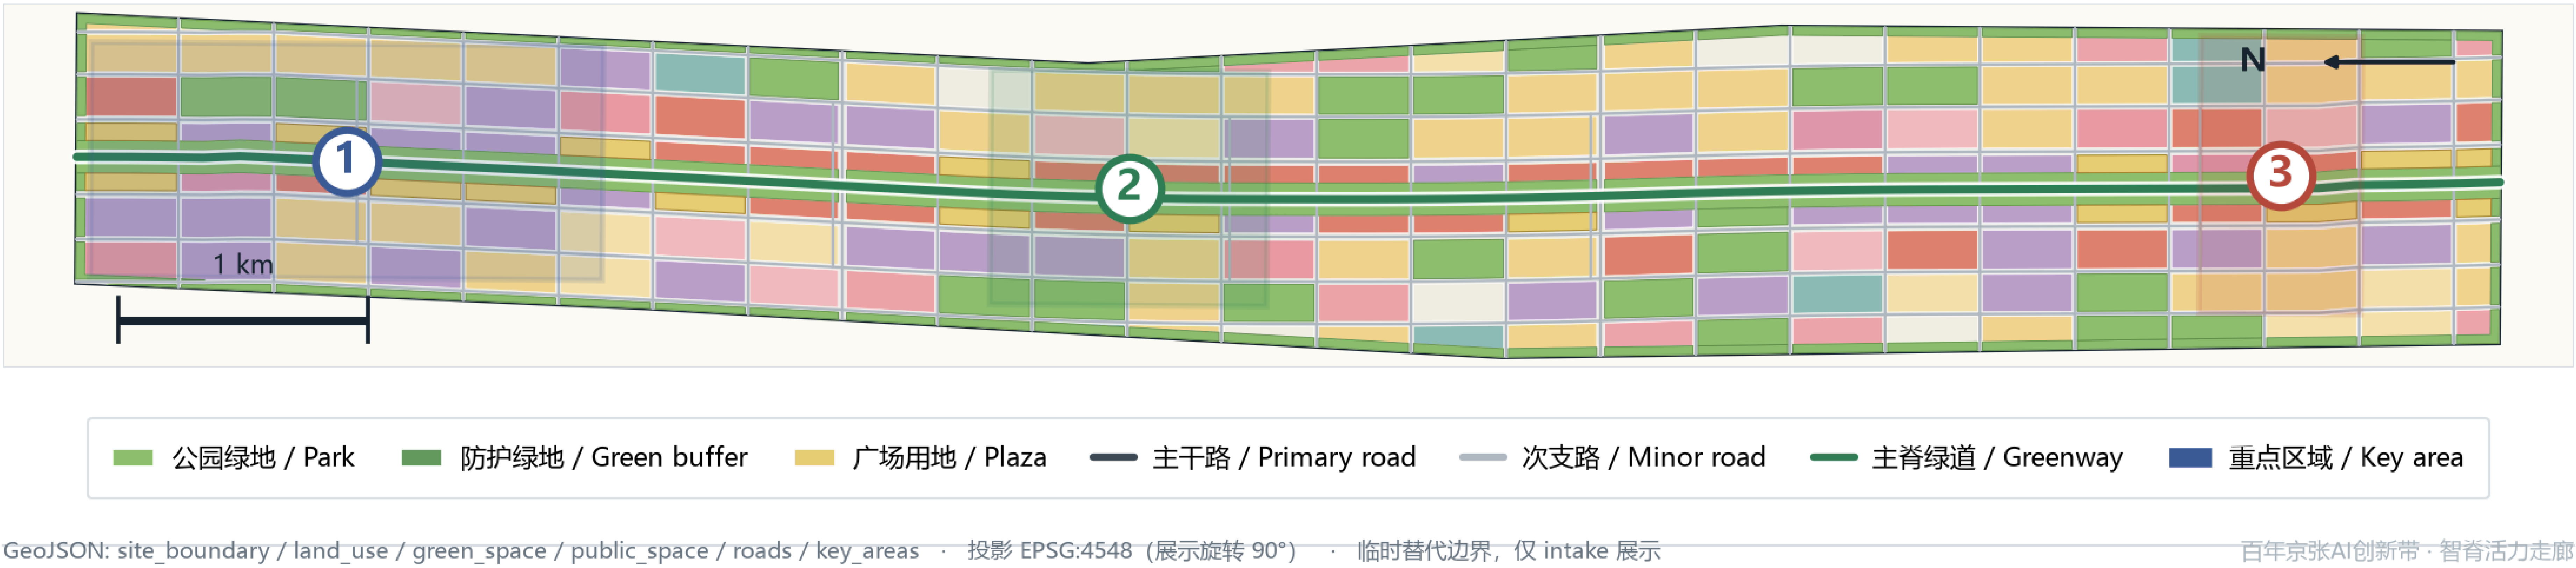


总体设计范围 1 141.28 ha · 重点区域 369.29 ha (3)

主脊绿道 9.72 km · 300 m 步行圈覆盖 51.10%

用地结构 · 258 地块无缝覆盖

Land-use structure · 258 parcels seamless coverage | 复算缺口 2.87 m² · 最大重叠 0.0607 m² · 容差 1141.28 m²

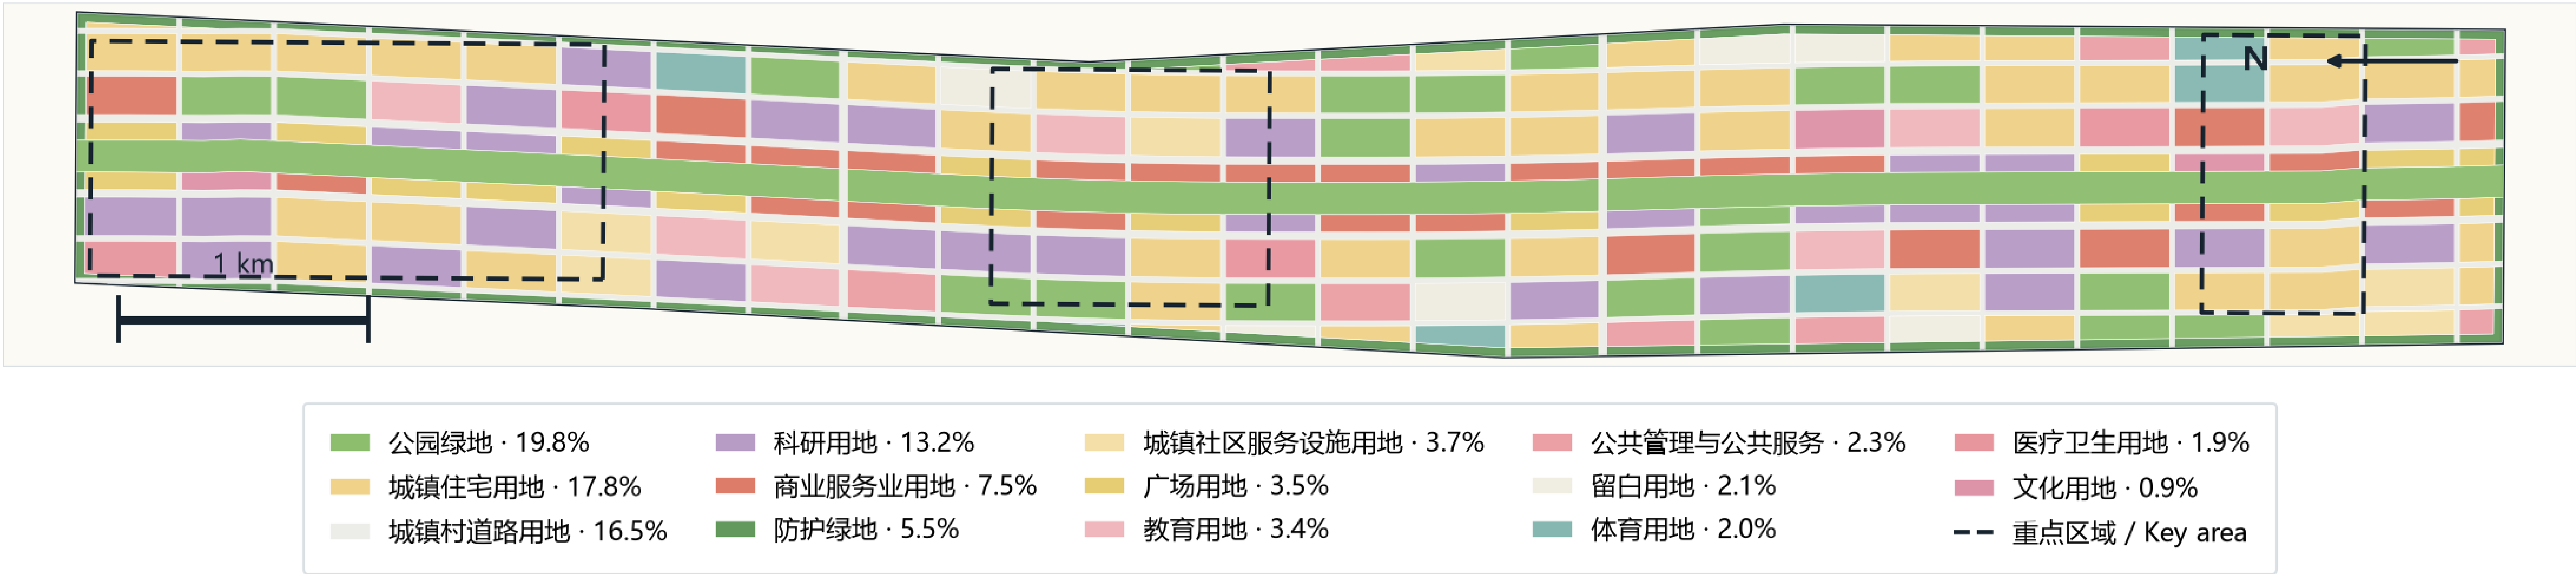

GeoJSON: land_use.geojson + key_areas.geojson · 投影 EPSG:4548 (展示旋转 90°) · 临时替代边界, 仅 intake 展示


百年京张AI创新带 · 智脊活力走廊

缺口 2.87 m² · 最大重叠 0.0607 m² · 容差 1141.28 m²

公园 19.77% · 居住 17.83% · 道路 16.48% · 工业研发 13.20% · 商业 7.49%

重点区域 · 三处详细设计片区

Key areas · three detailed-design districts | 重点区域 369.29 ha (3 处) · 概念建筑 164 栋

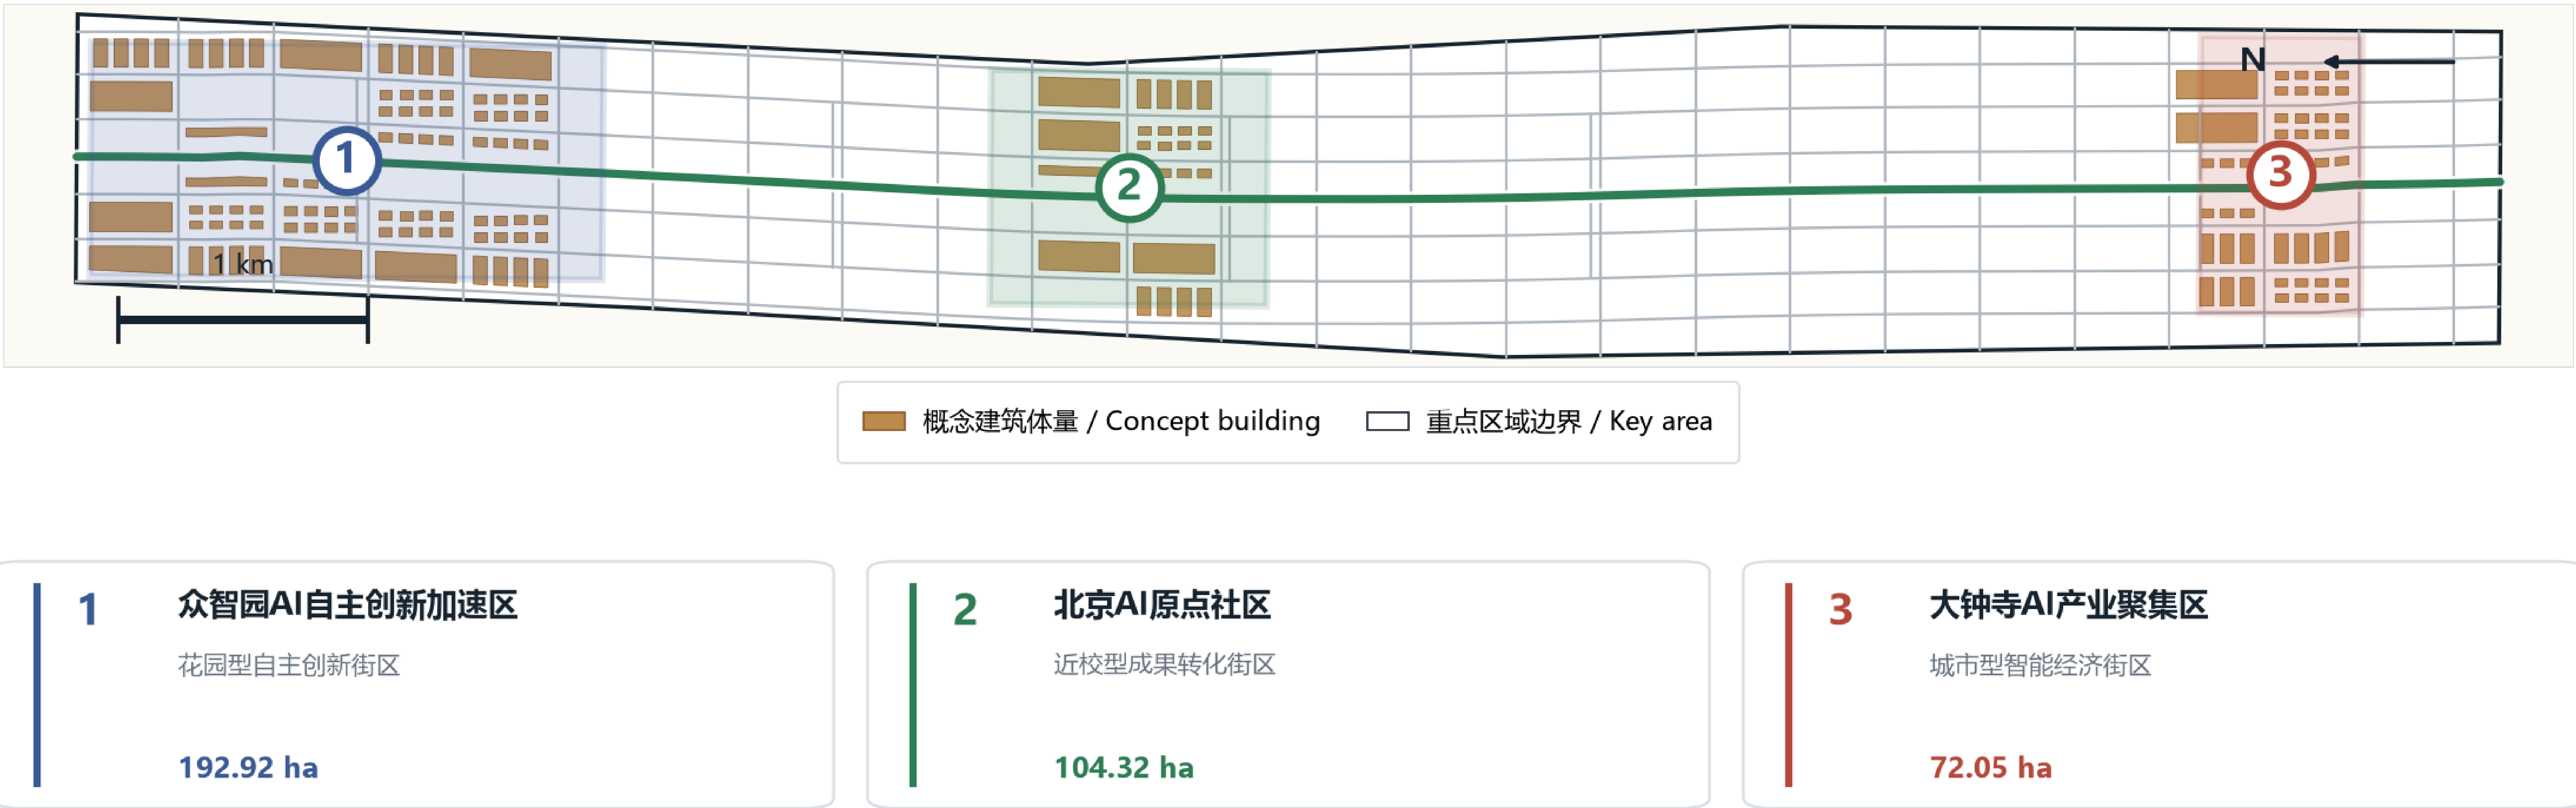

GeoJSON: key_areas / buildings / roads · 投影 EPSG:4548 (展示旋转 90°) · 临时替代边界, 仅 intake 展示

百年京张AI创新带 · 智脊活力走廊


重点区域共 369.29 ha (3 处) · 概念建筑 164 栋

平均建筑高度 34.08 m · 最高 60.00 m

毛容积率 1.427 · 概念总建筑面积 5 271 411 m²

分期实施 · 核心指标证据

Phasing PH-01 / 02 / 03 | 启动 369.29 ha · 拓展 425.19 ha · 收官 346.81 ha

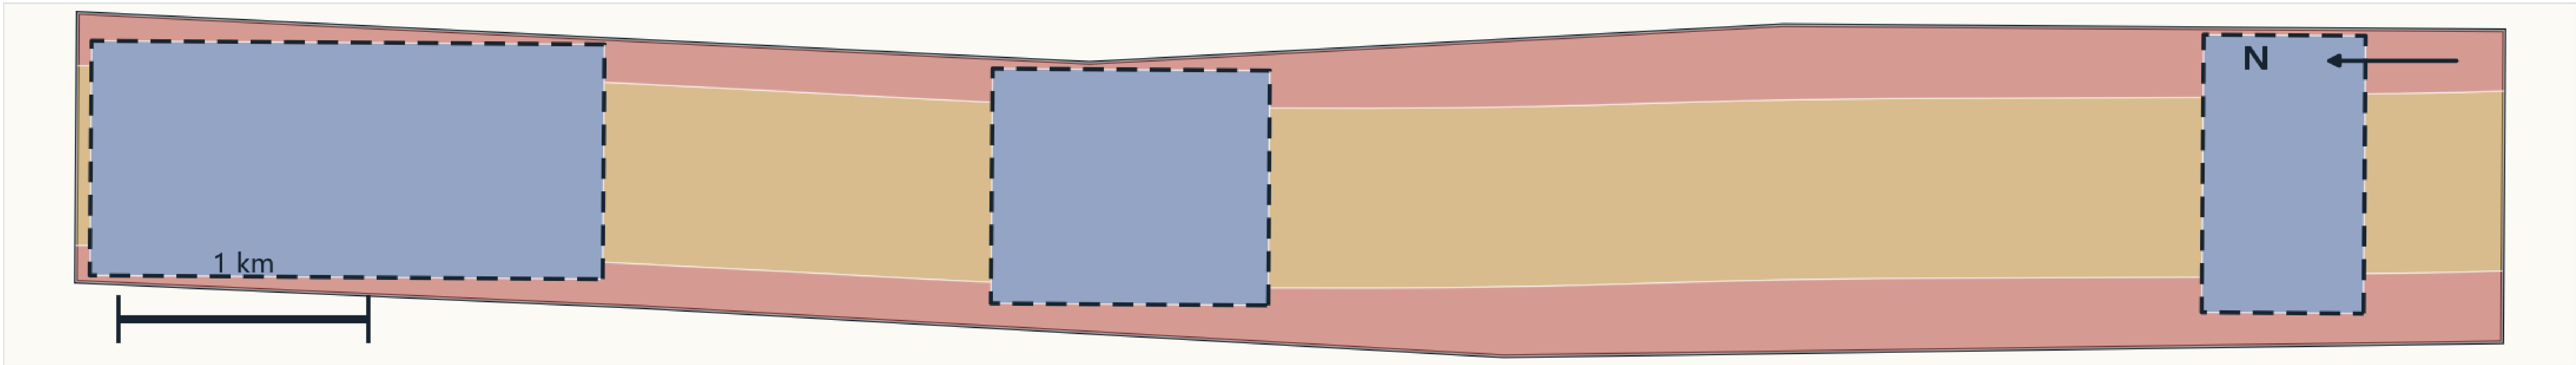

PH-01 启动 / Launch PH-02 拓展 / Expand PH-03 收官 / Consolidate -- 重点区域 / Key area

总用地 Site area 1 141.28 ha	重点区域 Key areas 369.29 ha (3 处)	主脊绿道 Spine greenway 9.72 km
300 m 步行圈覆盖 Walkshed 51.10 % (583.24 ha)	概念建筑 Buildings 164 栋	用地地块 Parcels 258 块

GeoJSON: phasing + key_areas · 指标来源 metrics.json (EPSG:4548 独立复算, 展示旋转 90°) · 8 项 unknown 诚实标注

百年京张AI创新带 · 智脊活力走廊

PH-01 启动 369.29 ha · PH-02 拓展 425.19 ha · PH-03 收官 346.81 ha

路网密度 8.83 km/km² · 主脊步行圈覆盖 51.10%